

A801 EXISTING CONCRETE TEE - TYPICAL
A804 CUSTOM WALL COVERING PROVIDED BY OWNER. OCCI

05/04/2021

A7.1.3

GENERAL SHEET NOTES

- A. REFER TO THE A0 X SERIES SHEETS FOR ARCHITECTURAL GENERAL NOTES, DRAWING, REFERENCE AND MATERIAL SYMBOLS, ABBREVIATIONS, AS WELL AS DIMENSIONING CONVENTIONS USED ON THIS SHEET.
- B. REFER TO AND COORDINATE WITH MECHANICAL, PLUMBING, AND ELECTRICAL FOR ADDITIONAL INFORMATION NOT SHOWN ON THIS SHEET.
- C. THE PURPOSE OF THE DRAWINGS ON THIS SHEET IS TO ILLUSTRATE THE OVERALL CONFIGURATION OF ALL ITEMS OF ALL TRADES OCCURRING ON THE INTERIOR ELEVATIONS. LOCATIONS OF ELEMENTS SHOWN ON ELECTRICAL, MECHANICAL, AND PLUMBING DRAWINGS ARE SCHEMATIC AND THE DIMENSIONS SHOWN HERE TAKE PRECEDENCE.
- D. REFER TO THE A0 X SERIES SHEETS FOR TYPICAL MOUNTING HEIGHTS FOR DIMENSIONS NOT SHOWN ON THIS SHEET.
- E. REFER TO THE 'AF' SERIES SHEETS FOR INTERIOR FINISH INFORMATION.
- F. SOLE PRODUCT OR MANUFACTURER/SOURCE: WHERE A SINGLE PRODUCT OR MANUFACTURER/SOURCE IS NAMED, SUBJECT TO COMPLIANCE WITH REQUIREMENTS, COMPARABLE PRODUCTS WILL BE CONSIDERED.

UCCS**UCCS CYBERSECURITY AND SPACE ECOSYSTEM EXPANSION**3650 NORTH NEVADA AVE
COLORADO SPRINGS, CO, 80907

REFERENCE KEYNOTES

- 084113.A02 INTERIOR ALUMINUM-FRAMED ENTRANCES AND STOREFRONT
- 084113.A03 INTERIOR ALUMINUM-FRAMED STOREFRONT WITH DOOR SYSTEM TO MATCH SPECIFICATION 084123
- 084123.A01 1-HR FIRE-RATED ALUMINUM-FRAMED STOREFRONT SYSTEM WITH 3/4" LAMINATED FIRE-RATED GLAZING

SMITHGROUP899 LOGAN STREET
SUITE 508
DENVER, CO 80203
303.832.3272
smithgroup.com

RIDER LEVETT BUCKNALL

COST ESTIMATOR
1675 LARIMER STREET
DENVER, CO 80202
720.904.1480NVS
ACOUSTICS, IT/TELECOM & SECURITY, AUDIOVISUAL
2650 18TH STREET, SUITE 201-203
DENVER, CO 80211
720.213.7550MARTIN/MARTIN, INC.
STRUCTURAL ENGINEER
1249 WEST COLFAX AVENUE
LAKEWOOD, CO, 80215
303.431.6100


SHEET KEYNOTES

- A201 BASIS OF DESIGN R.O. SIZE: 36"X72" SKYLIGHT OPENINGS ABOVE IN STRUCTURAL TEES, RE. STRUCTURAL. VERIFY WITH SKYLIGHT MANUFACTURER.
- A801 EXISTING CONCRETE TEE - TYPICAL

ISSUED FOR REV DATE

BID SET 04MAY2021
CONSTRUCTION DOCUMENTS 15APR2021
DESIGN DEVELOPMENT 23DEC2020
SCHEMATIC DESIGN 19OCT2020

SEALS AND SIGNATURES

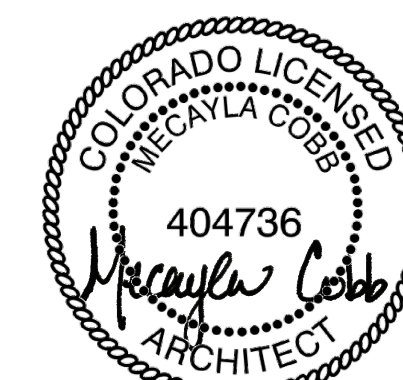

05/04/2021

GLASS TYPES

TYPES SHOWN ON ELEVATIONS, AND IN THE "GLASS TYPES" COLUMNS UNDER THE "OPENING" AND "FRAME" COLUMNS OF THE DOOR SCHEDULE.

SOLE PRODUCT OR MANUFACTURER/SOURCE: WHERE A SINGLE PRODUCT OR MANUFACTURER/SOURCE IS NAMED, SUBJECT TO COMPLIANCE WITH REQUIREMENTS, COMPARABLE PRODUCTS WILL BE CONSIDERED.

- GL-1 1" INSULATED GLAZING UNIT - CLEAR TEMPERED LOW-IRON
LOCATION: INTERIOR ENTRY VESTIBULE
BASIS OF DESIGN:
MANUFACTURER: VITRO
TYPE: SOLARBAN ACUTY
- GL-2 TYPE: 1" INSULATED GLAZING UNIT - CLEAR LOW-E
LOCATION: EXTERIOR STOREFRONT
BASIS OF DESIGN:
MANUFACTURER: VITRO
TYPE: SOLARBAN 90 CLEAR
- GL-3 1" INSULATED GLAZING UNIT - CLEAR TEMPERED LOW-E
LOCATION: INTERIOR STOREFRONT
BASIS OF DESIGN:
MANUFACTURER: VITRO
TYPE: SOLARBAN 90 CLEAR
- GL-4 1" INSULATED GLAZING UNIT - SPANDREL TEMPERED
LOCATION: EXTERIOR STOREFRONT
BASIS OF DESIGN:
MANUFACTURER: VITRO
TYPE: SOLARBAN ACUTY
SPANDREL COLOR: #E-070 WARM GRAY
- GL-5 3/8" CLEAR GLASS - TEMPERED
LOCATION: INTERIOR WINDOWS AND DOORS, UNRATED
- GL-6 5/16" FIRE-RATED GLASS
LOCATION: INTERIOR FIRE-RATED GLASS DOORS
RATING: 45-MIN.
- GL-7 3/4" FIRE-RATED GLASS
LOCATION: INTERIOR FIRE-RATED WINDOWS
RATING: 45-MIN.

SHEET TITLE

INTERIOR ELEVATIONS

PROJECT NUMBER


CD
SHEET NUMBER

12654.000

A8.1.1


66 EXECUTIVE CONFERENCE ROOM - WEST ELEVATION

SCALE: 1/4" = 1'-0"

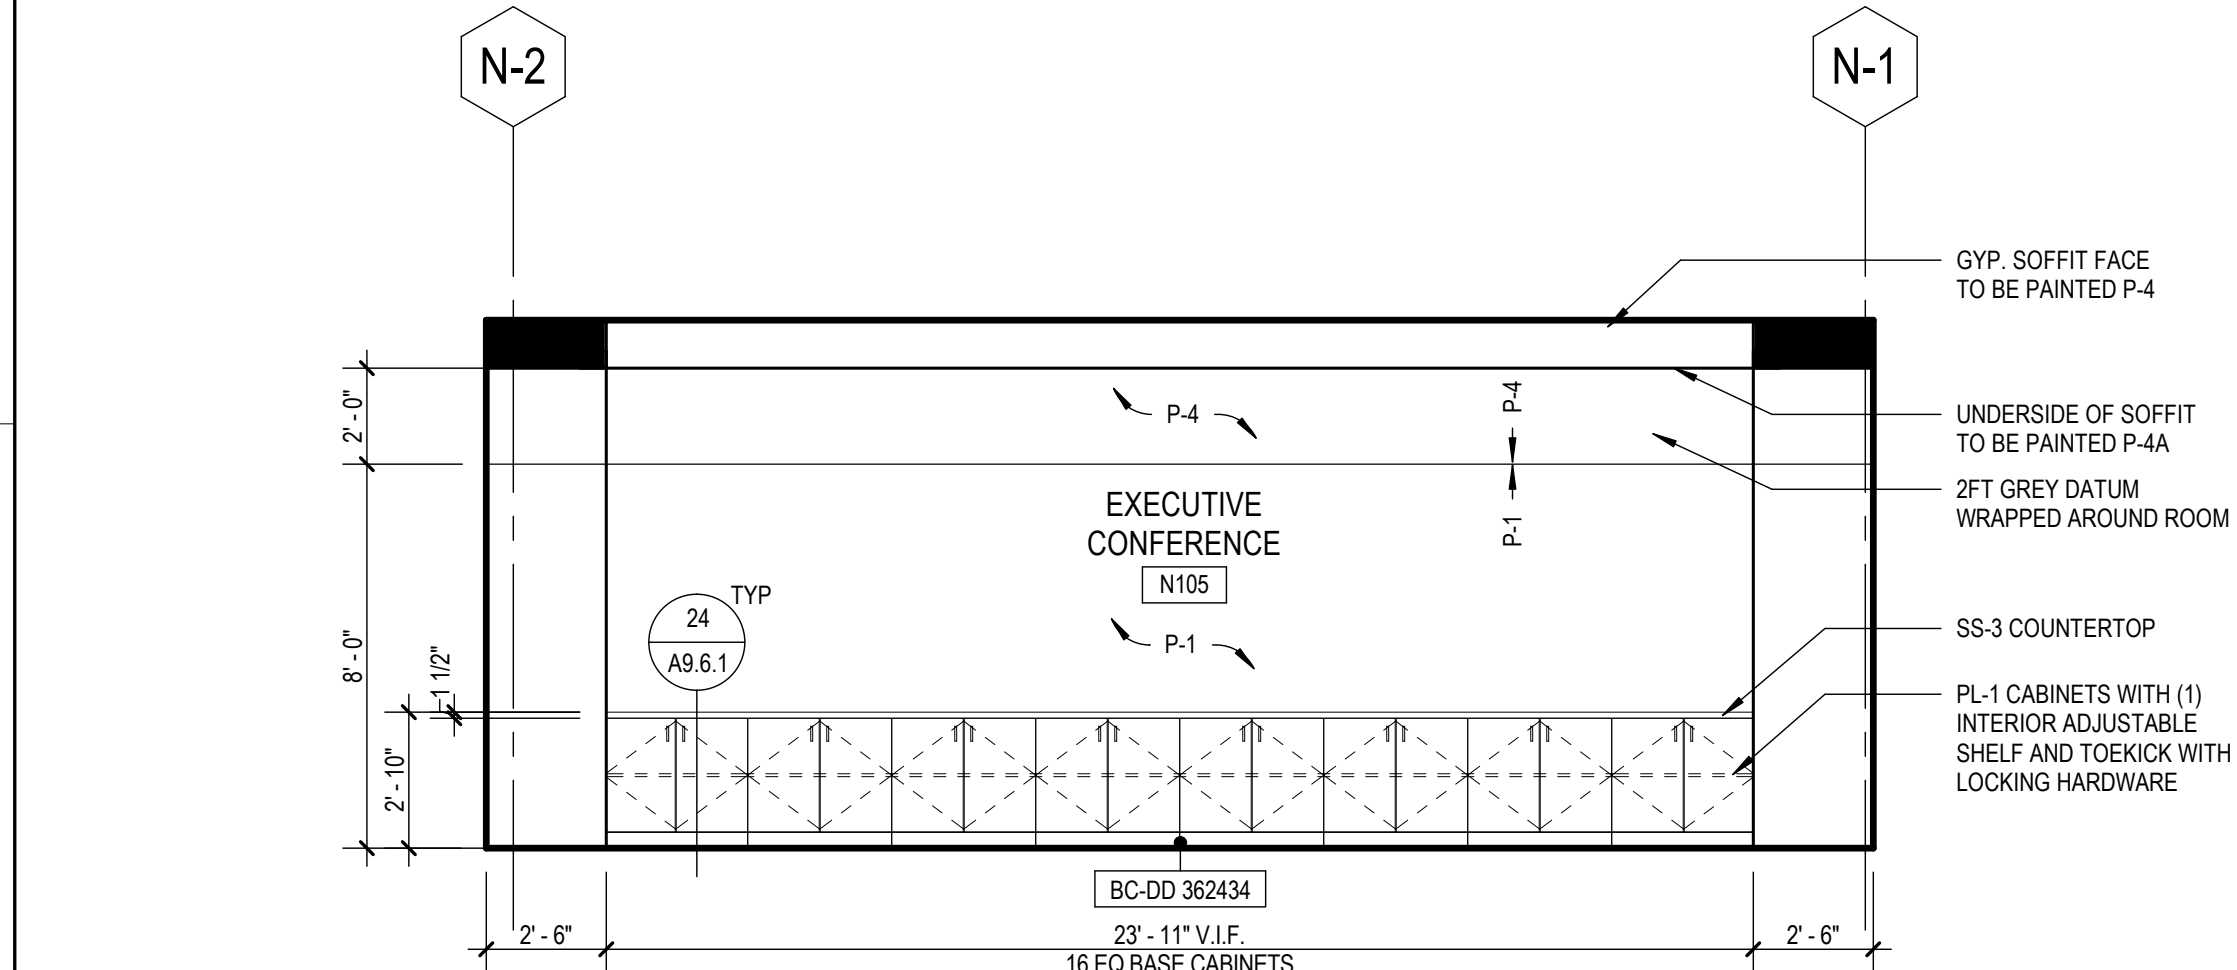


68 EXECUTIVE CONFERENCE ROOM - EAST ELEVATION

SCALE: 1/4" = 1'-0"

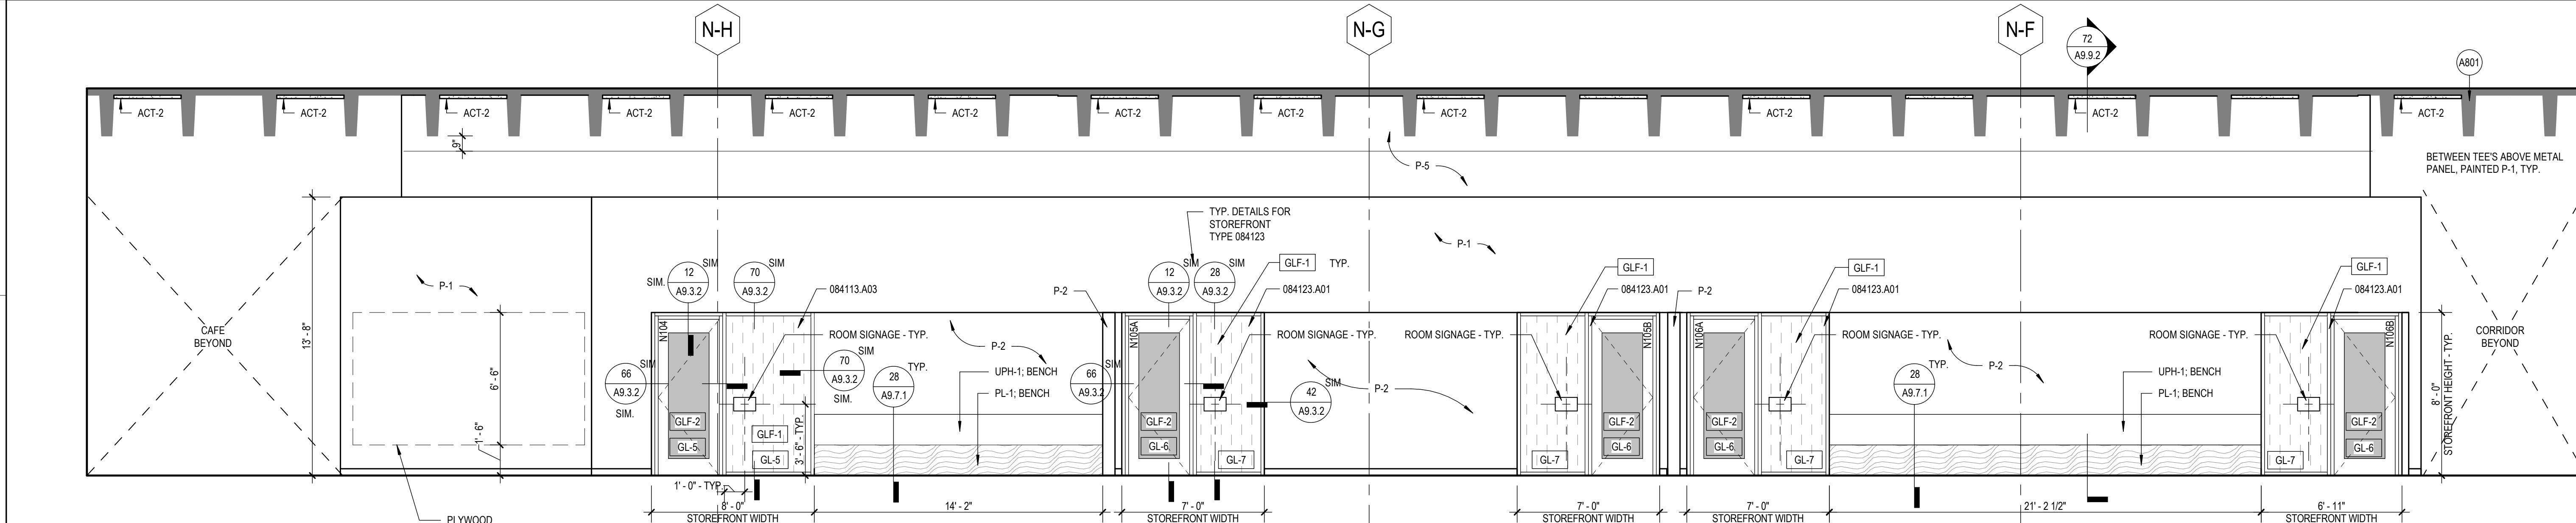

70 MAIN STREET - SOUTH ELEVATION

SCALE: 1/4" = 1'-0"

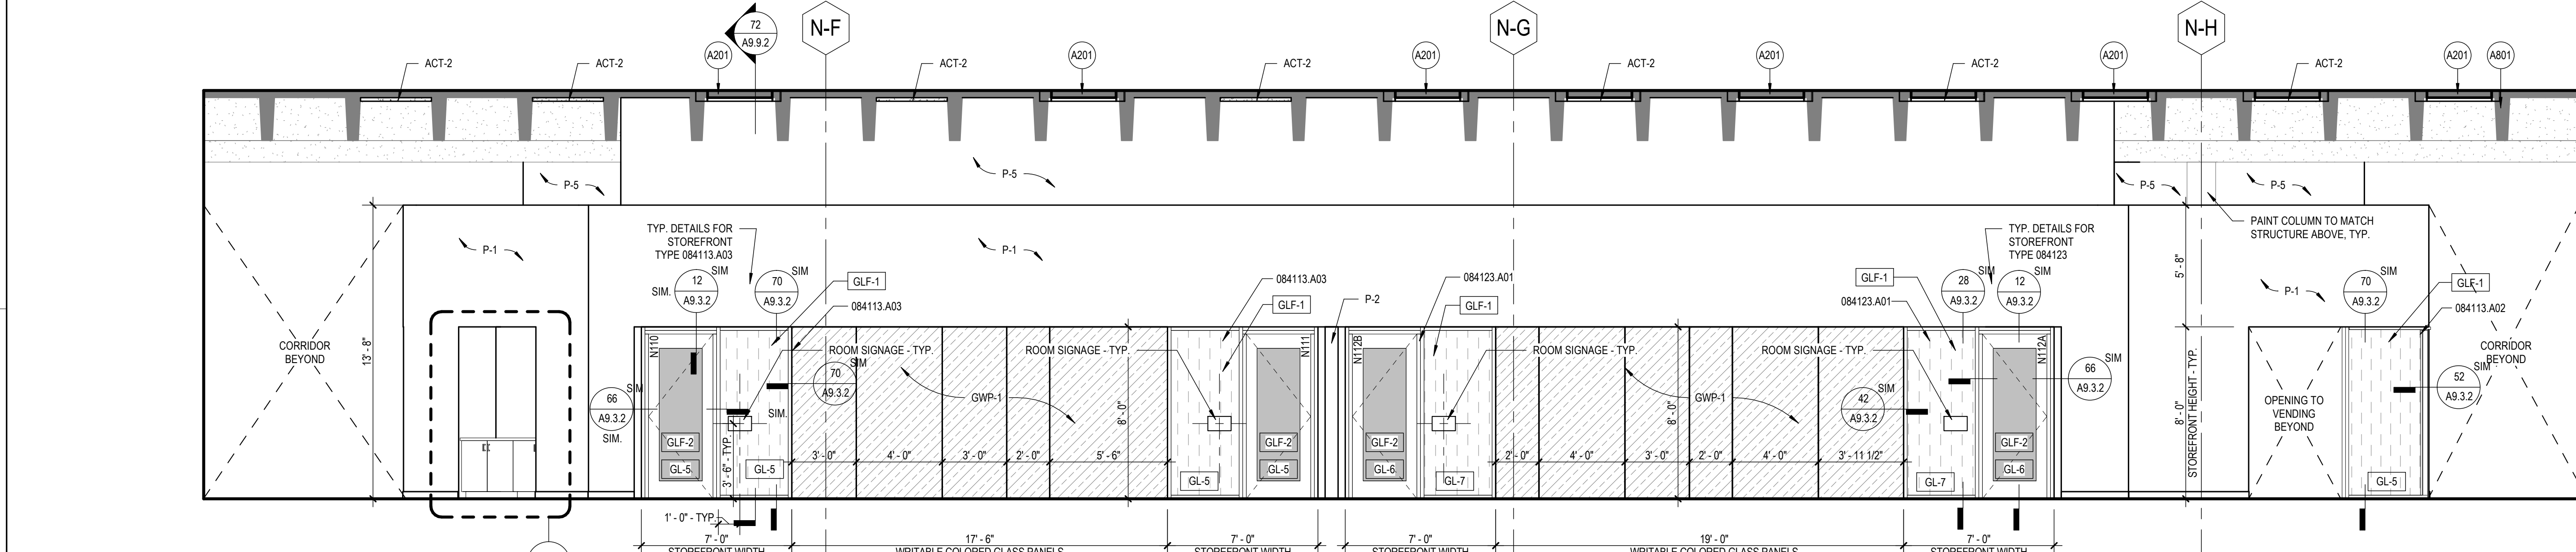


72 MAIN STREET - NORTH ELEVATION

SCALE: 1/4" = 1'-0"


42 CIRCULATION - EAST ELEVATION

SCALE: 1/4" = 1'-0"

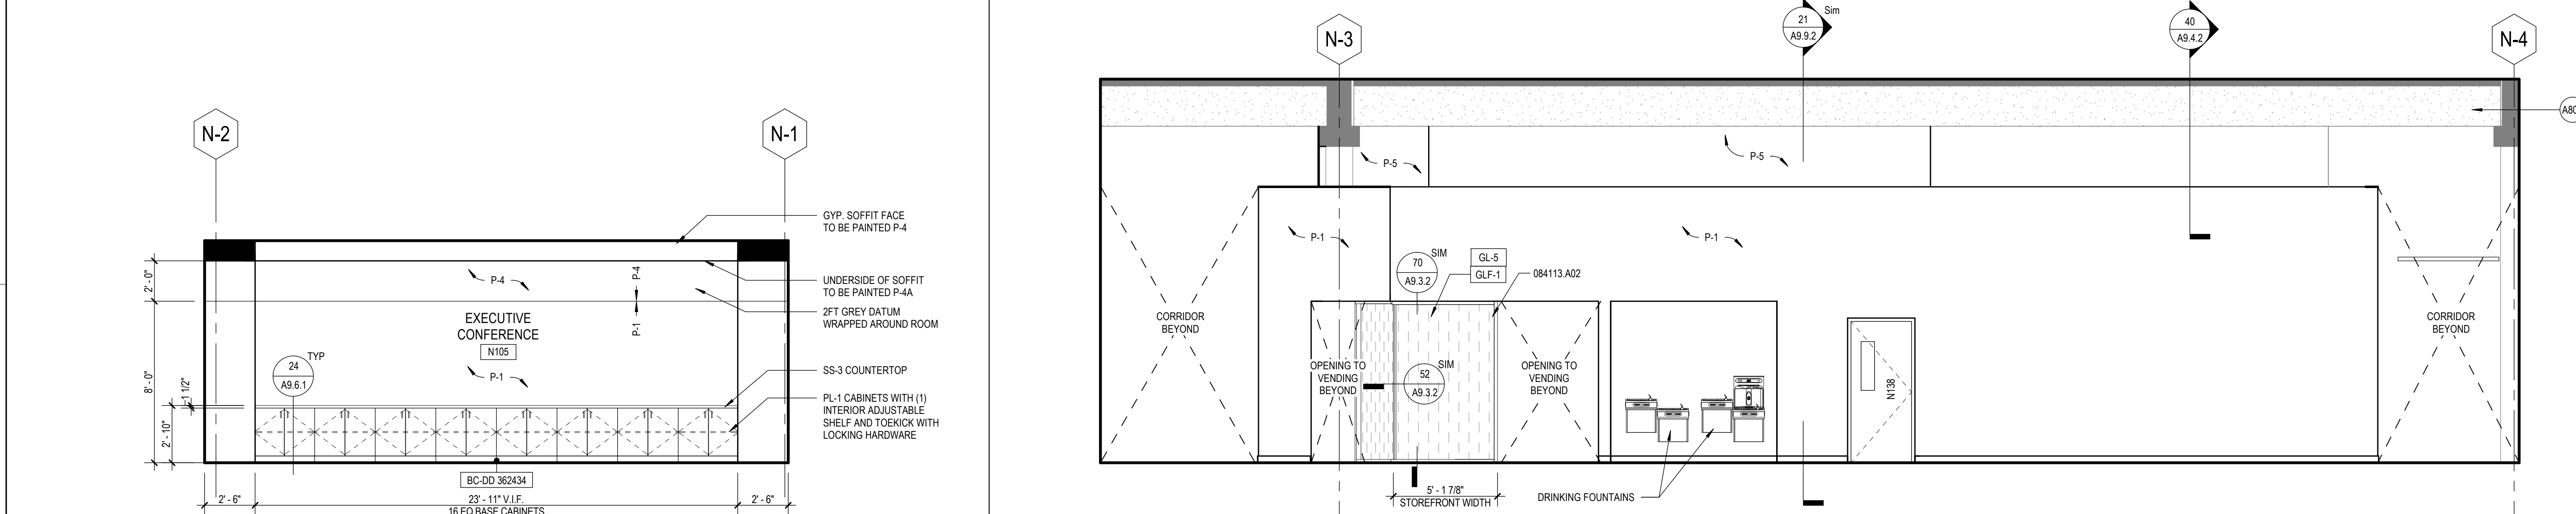


44 CIRCULATION - WEST ELEVATION

SCALE: 1/4" = 1'-0"

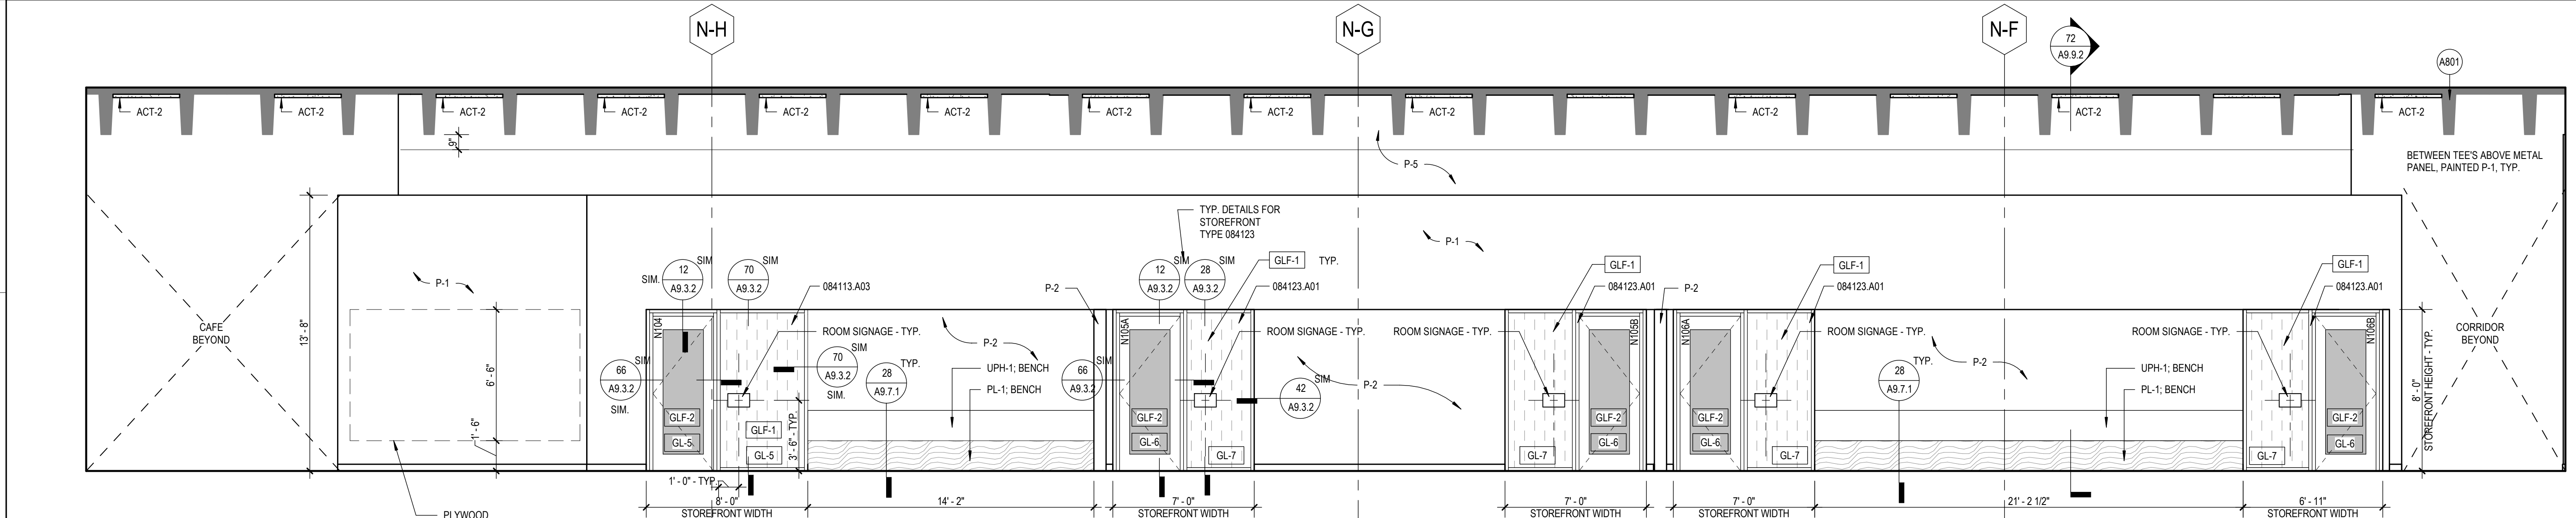

46 CIRCULATION - EAST ELEVATION

SCALE: 1/4" = 1'-0"

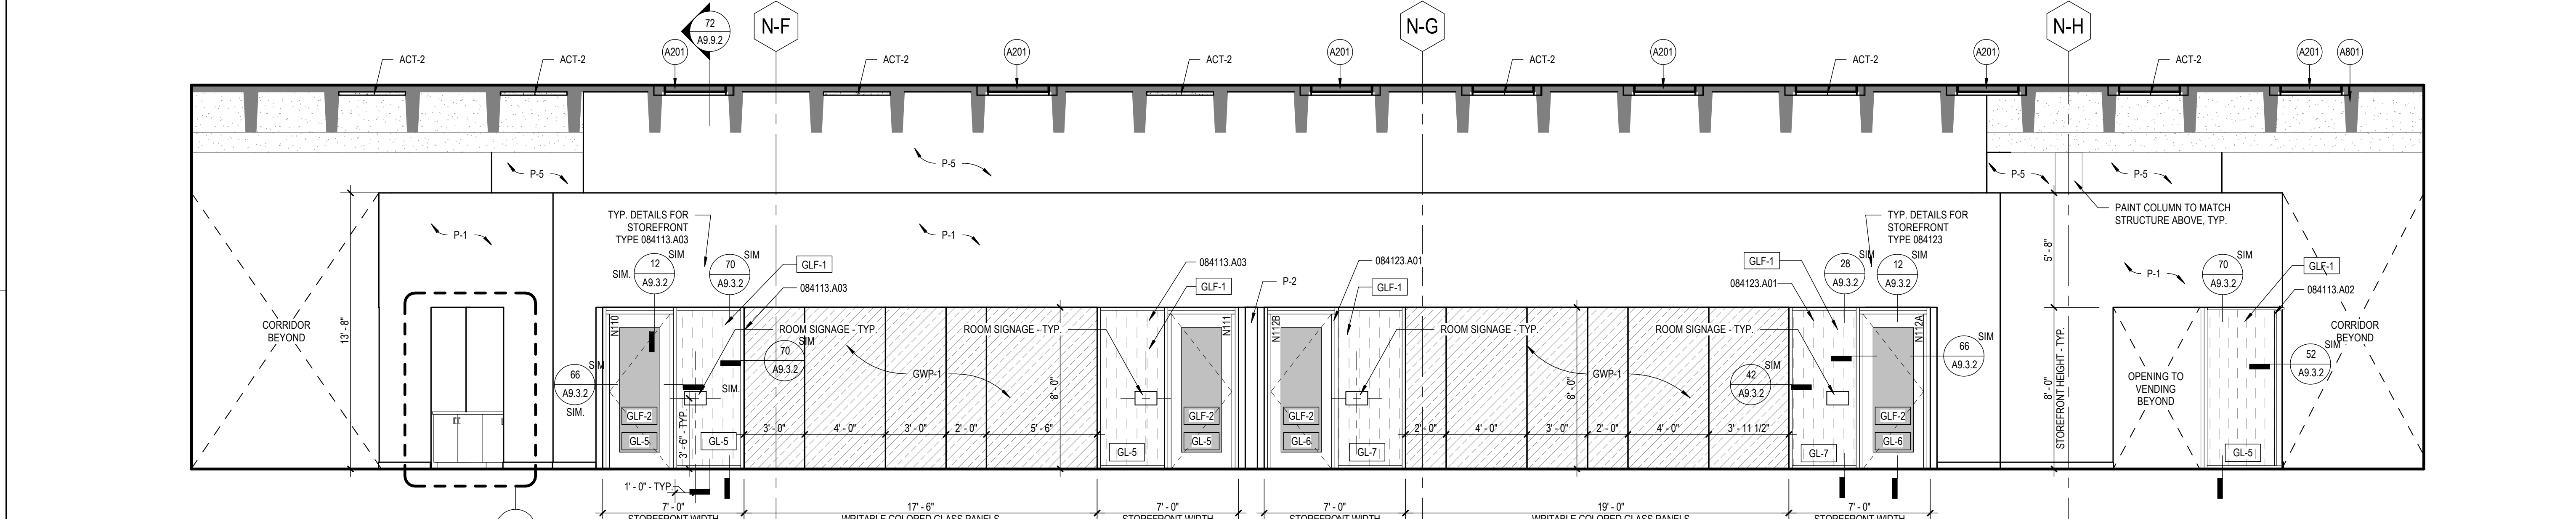


48 CIRCULATION - WEST ELEVATION

SCALE: 1/4" = 1'-0"


Author

5/4/2021 10:17:13 AM

Plot Date

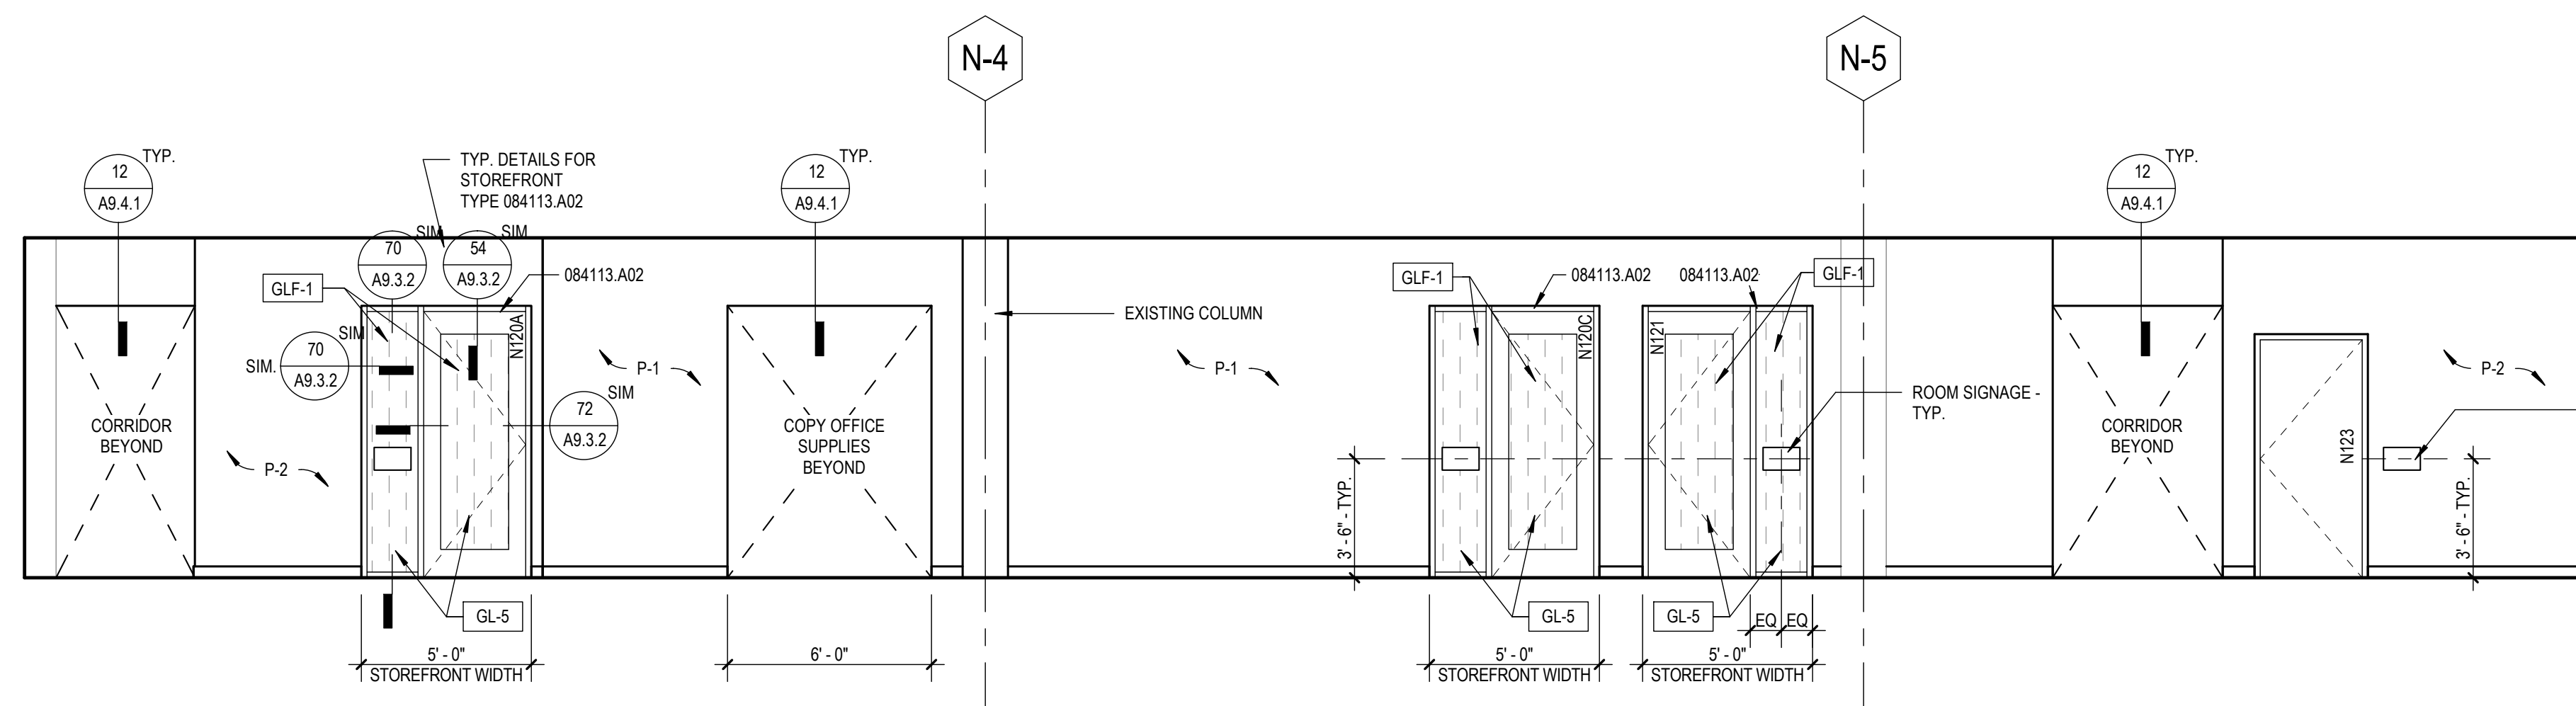

66 UCCS OFFICES - WEST ELEVATION
SCALE: 1/4" = 1'-0"

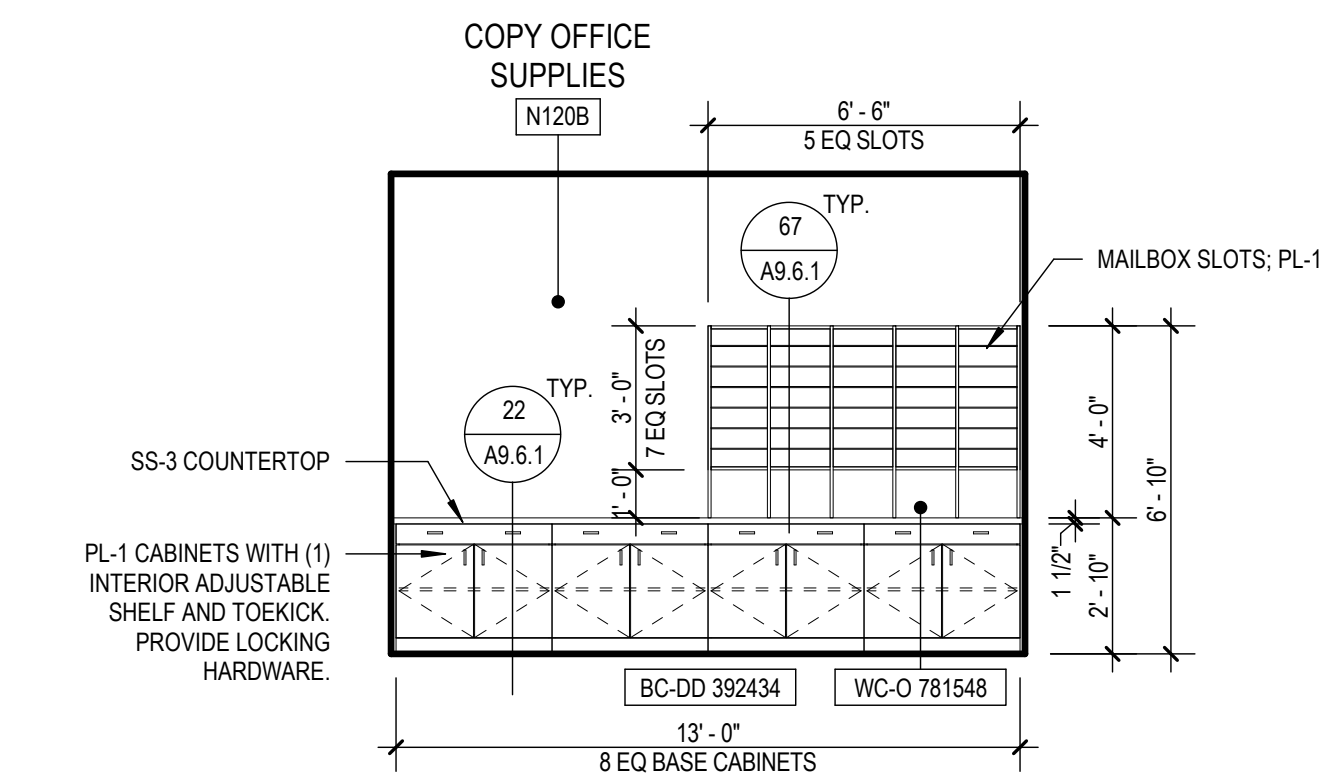

18 COPY OFFICE SUPPLIES - SOUTH ELEVATION
SCALE: 1/4" = 1'-0"


GENERAL SHEET NOTES

- A. REFLECT TO THE AO X SERIES SHEETS FOR ARCHITECTURAL GENERAL NOTES, DRAWING, REFERENCE AND MATERIAL SYMBOLS, ABBREVIATIONS, AS WELL AS DIMENSIONING CONVENTIONS USED ON THIS SHEET.
- B. REFLECT TO AND COORDINATE WITH MECHANICAL, PLUMBING AND ELECTRICAL FOR ADDITIONAL INFORMATION NOT SHOWN ON THIS SHEET.
- C. THE PURPOSE OF THE DRAWINGS ON THIS SHEET IS TO ILLUSTRATE THE OVERALL CONFIGURATION OF ALL ITEMS OF ALL TRADES OCCURRING ON THE INTERIOR ELEVATIONS. LOCATIONS OF ELEMENTS SHOWN ON ELECTRICAL, MECHANICAL, AND PLUMBING DRAWINGS ARE SCHEMATIC AND THE DIMENSIONS SHOWN HERE TAKE PRECEDENCE.
- D. REFLECT TO THE AO X SERIES SHEETS FOR TYPICAL MOUNTING HANGERS FOR DIMENSIONS NOT SHOWN ON THIS SHEET.
- E. REFLECT TO THE AF* SERIES SHEETS FOR INTERIOR FINISH INFORMATION.
- F. SILE PRODUCT OR MANUFACTURER/SOURCE. WHERE A SINGLE PRODUCT OR MANUFACTURER/SOURCE IS NAMED, SUBJECT TO COMPLIANCE WITH REQUIREMENTS, ALL COMPARABLE PRODUCTS WILL BE CONSIDERED.




UCCS CYBERSECURITY AND SPACE ECOSYSTEM EXPANSION

3650 NORTH NEVADA AVE
COLORADO SPRINGS, CO, 80907

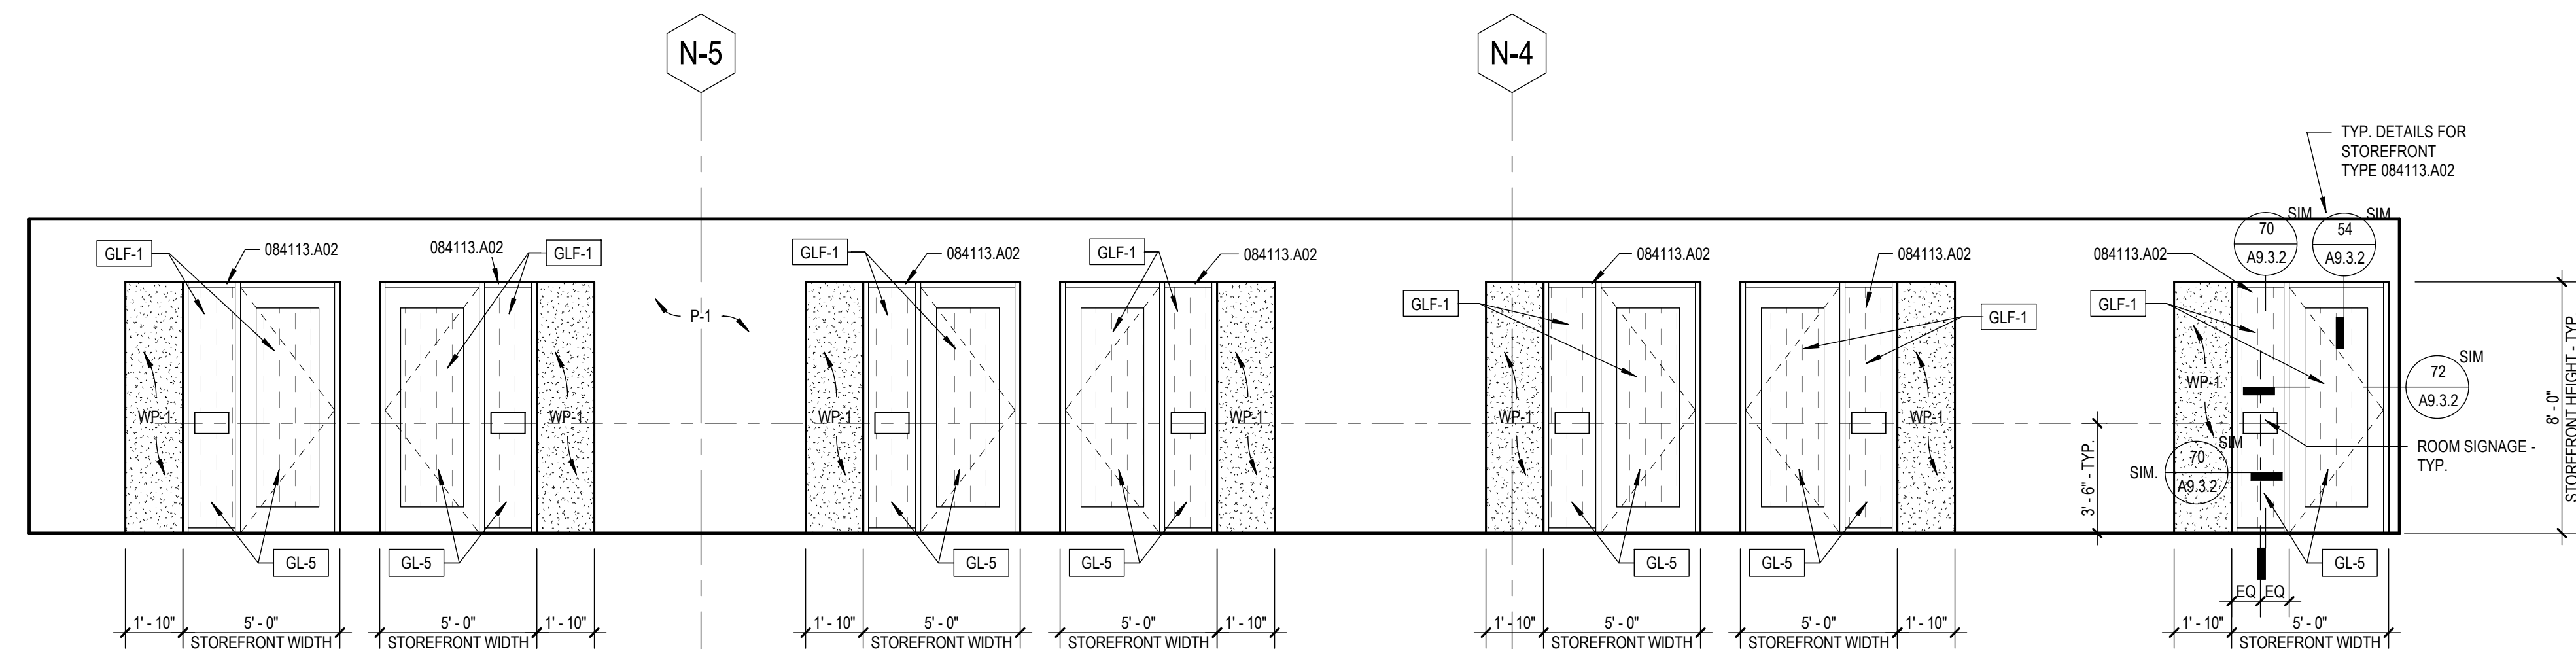

68 UCCS OFFICES - EAST ELEVATION
SCALE: 1/4" = 1'-0"

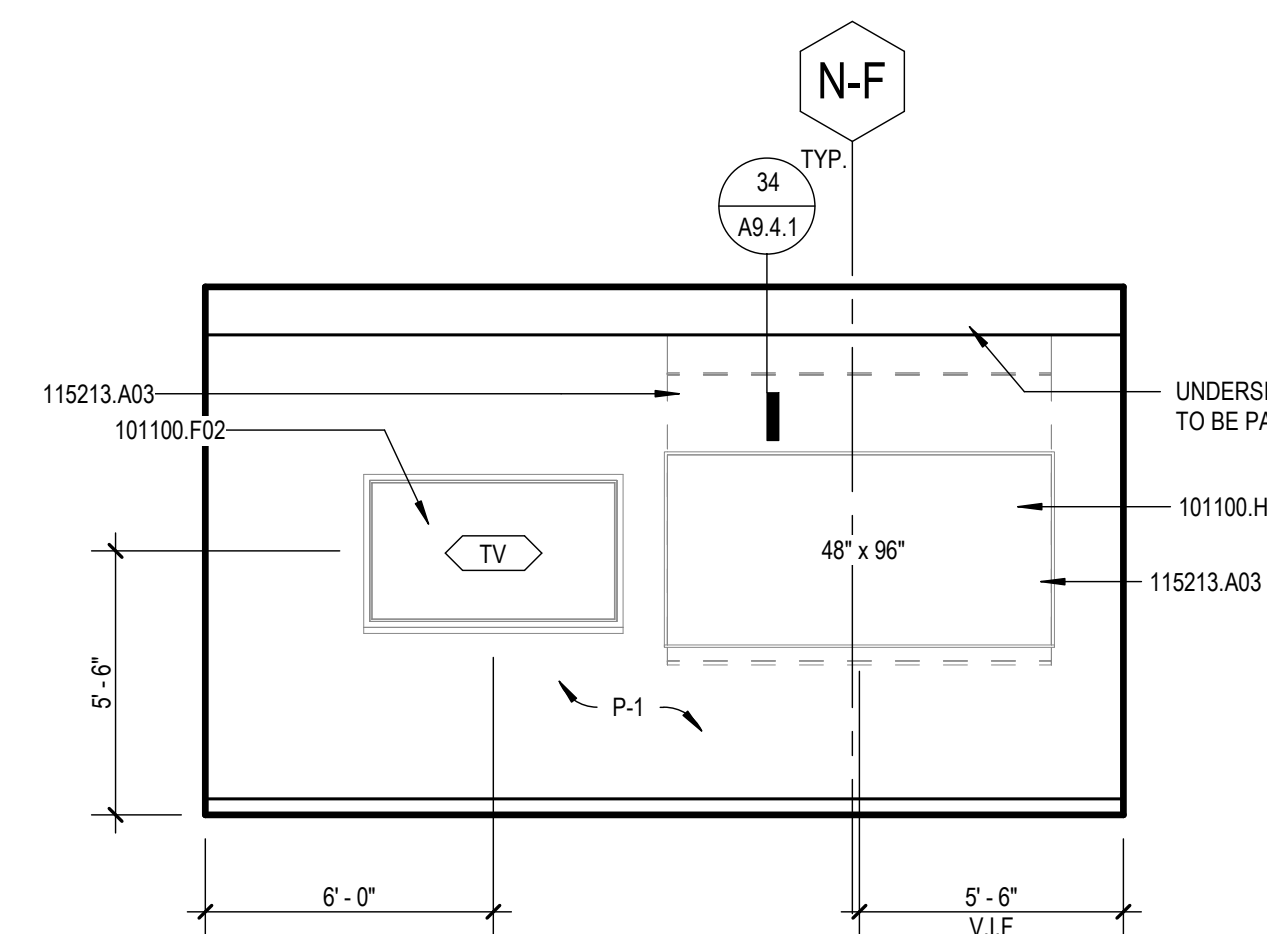

20 LARGE RESEARCH GRAD LABS - TEACHING WALL ELEVATION
SCALE: 1/4" = 1'-0"

REFERENCE KEYNOTES

- | | |
|------------|---|
| 084113.A02 | INTERIOR ALUMINUM-FRAMED ENTRANCES AND STOREFRONT |
| 101100.F02 | WALL MOUNTED DISPLAY UNIT (NIC) |
| 101100.H01 | MARKERBOARD |
| 115213.A03 | FRONT PROJECTION SCREEN |


SMITHGROUP

899 LOGAN STREET
SUITE 508
DENVER, CO 80203
303.832.3272
smithgroup.com


RIDER LEVETT BUCKNALL
COST ESTIMATOR
1675 LARIMER STREET
DENVER, CO, 80202
720-904-1480

NV5
ACOUSTICS, IT/TELECOM & SECURITY, AUDIOVISUAL
2650 18TH STREET, SUITES 201-203
DENVER, CO 80211
720-213-7550

MARTIN/MARTIN, INC.
STRUCTURAL ENGINEER
12499 WEST COLFAX AVENUE
LAKEWOOD, CO. 80215
303-431-6100

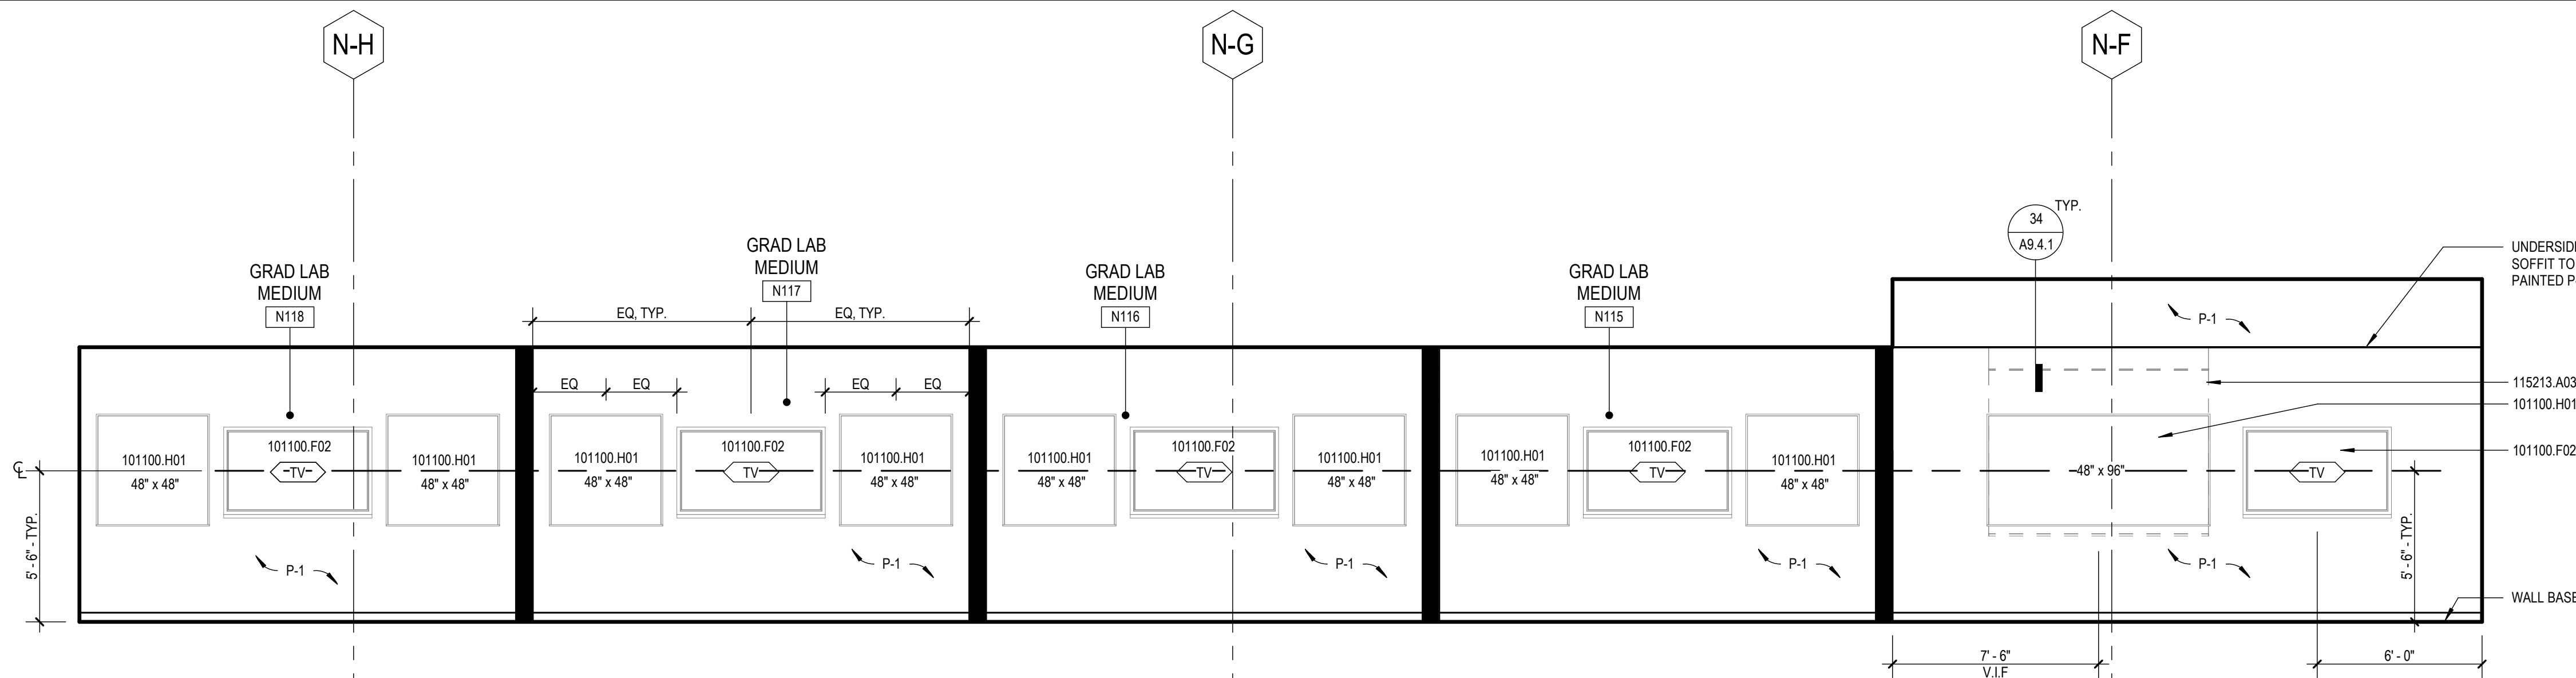

70 RESEARCH GRAD LABS - SOUTH ELEVATION
SCALE: 1/4" = 1'-0"

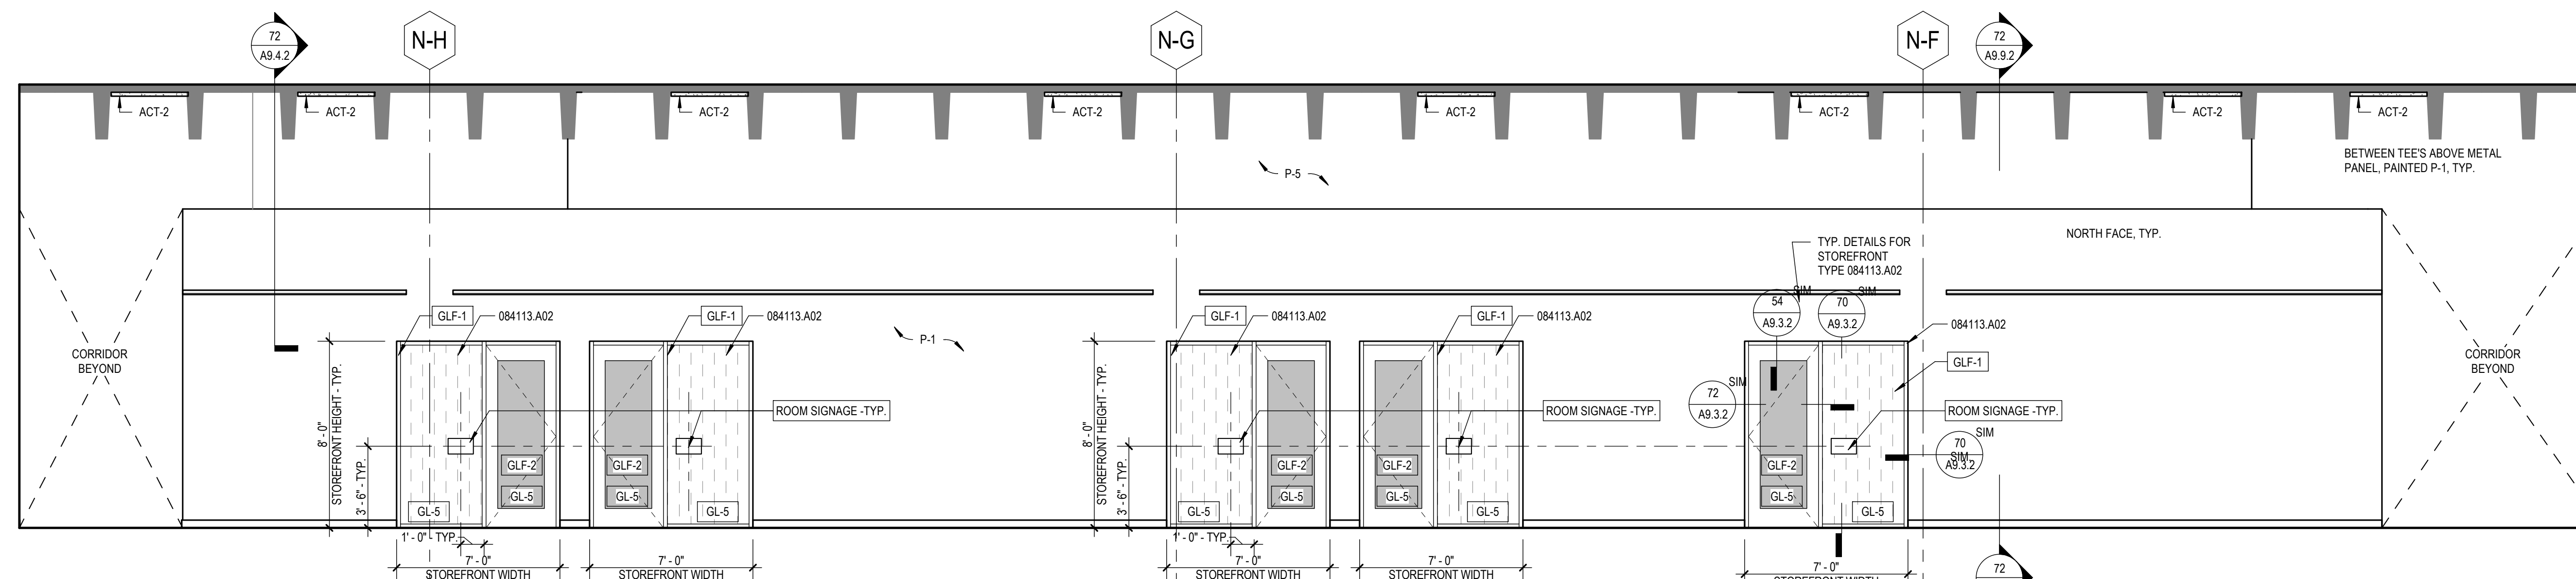

72 RESEARCH GRAD LAB CORRIDOR - SOUTH ELEVATION
SCALE: 1/4" = 1'-0"

○ SHEET KEYNOTES

GLASS TYPES

TYPES SHOWN ON ELEVATIONS, AND IN THE "GLASS TYPES" COLUMNS UNDER THE "OPENING" AND "FRAME" COLUMNS OF THE DOOR SCHEDULE.

SOLE PRODUCT OR MANUFACTURER/SOURCE: WHERE A SINGLE PRODUCT OR MANUFACTURER/SOURCE IS NAMED, SUBJECT TO COMPLIANCE WITH REQUIREMENTS, COMPARABLE PRODUCTS WILL BE CONSIDERED.

- | | |
|------|--|
| GL-1 | 1" INSULATED GLAZING UNIT - CLEAR TEMPERED LOW IR
LOCATION: INTERIOR ENTRY VESTIBULE
BASIS OF DESIGN:
MANUFACTURER VITRO
TYPE: SOLARBAN ACUTY |
| GL-2 | 1" INSULATED GLAZING UNIT - CLEAR LOW E
LOCATION: EXTERIOR STOREFRONT
BASIS OF DESIGN:
MANUFACTURER VITRO
TYPE: SOLARBAN 90 CLEAR |
| GL-3 | 1" INSULATED GLAZING UNIT - CLEAR TEMPERED LOW E
LOCATION: EXTERIOR STOREFRONT
BASIS OF DESIGN:
MANUFACTURER VITRO
TYPE: SOLARBAN 90 CLEAR |
| GL-4 | 1" INSULATED GLAZING UNIT - SPANDREL TEMPERED
LOCATION: EXTERIOR STOREFRONT
BASIS OF DESIGN:
MANUFACTURER ACUTY
TYPE: SOLARBAN ACUTY
SPANDREL COLOR: 83-0770 WARM GRAY |
| GL-5 | 3/8" CLEAR GLASS - TEMPERED
LOCATION: INTERIOR WINDOWS AND DOORS, UNRATED |
| GL-6 | 5/16" FIRE-RATED GLASS
LOCATION: INTERIOR FIRE-RATED GLASS DOORS
RATING: 45-MIN |
| GL-7 | 3/4" FIRE-RATED GLASS
LOCATION: INTERIOR FIRE-RATED WINDOWS
RATING: 45-MIN |

ISSUED FOR	REV	DATE
------------	-----	------

BID SET		04MAY2021
CONSTRUCTION DOCUMENTS		15APR2021
DESIGN DEVELOPMENT		23DEC2020
SCHEMATIC DESIGN		19OCT2020

SEALS AND SIGNATURES



05/04/2021

SHEET TITLE


INTERIOR ELEVATIONS

PROJECT NUMBER

CD

12654.000

A8 1 3

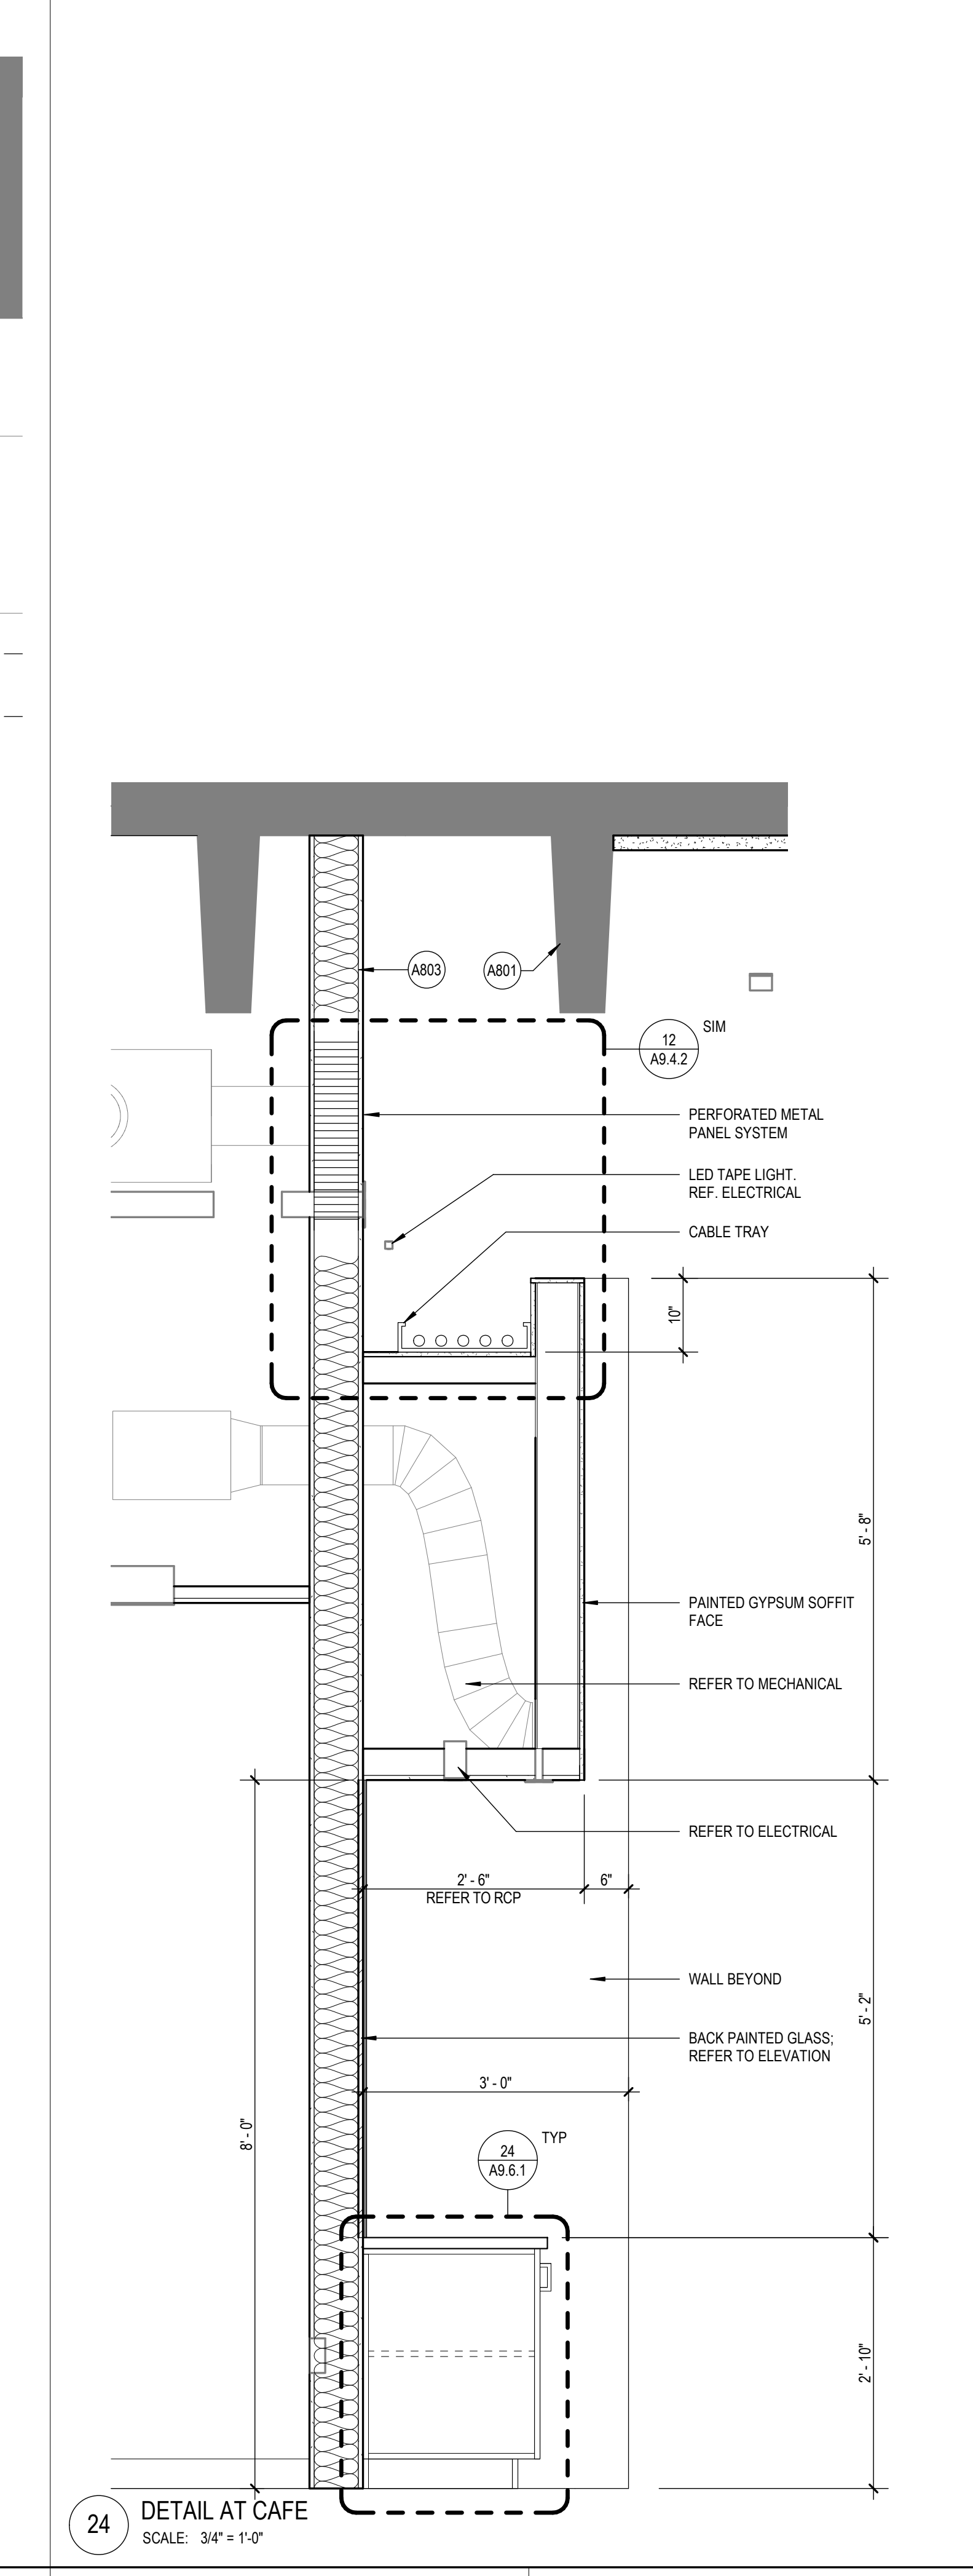

PROJECT NUMBER 12654.000

CD **A9.9.1**

SHEET NUMBER