



Replace RTU & Cabinetry - CT Area

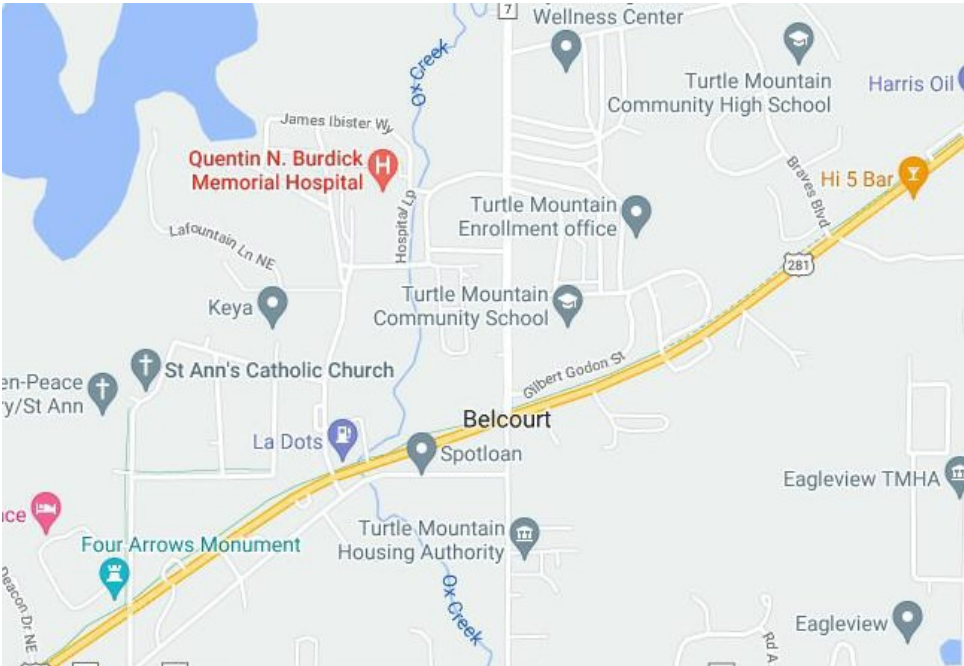

Project Vicinty



Site Map

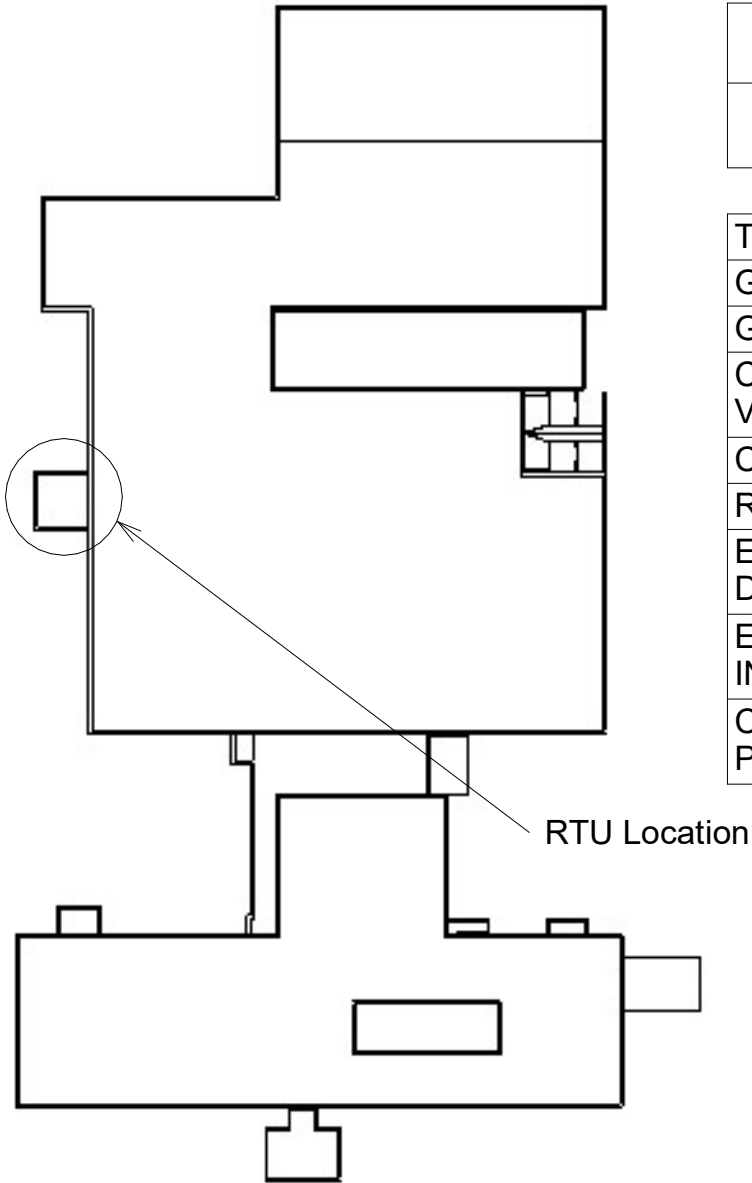

Sheets	
Sheet Name	Sheet Number
TITLE SHEET	T.1
GENERAL DEMOLITION	A.1
GENERAL INSTALL	A.2
CASEWORK SECTION VIEWS	A.3
CONCRETE	A.4
ROOM FINISH	A.5
ELECTRICAL DEMOLITION	E.1
ELECTRICAL INSTALLATION	E.2
CRAWL SPACE STEAM PIPE TIE IN	M.1

General Notes:
These design sheets are produced for the convenience of the offeror. Values and dimensions should be field verified by the offeror prior to award.



GREAT PLAINS AREA INDIAN HEALTH SERVICE
OFFICE OF ENVIRONMENTAL
HEALTH & ENGINEERING

DIVISION OF FACILITIES MANAGEMENT
115 4TH AVENUE SE, RM 309
ABERDEEN, SD 57401
(605) 226-7451 FAX (605) 226-7580
www.ihs.gov


Quentin N. Burdick
Memorial Health Facility

Replace RTU &
Cabinetry - CT Area

CONTRACT NO:	
TASK ORDER NO:	
PROJECT NUMBER:	GP22TM300H10
DATE:	08/26/2025
DRAWN BY:	Taylor Strand
CHECKED BY:	Brad Weekley
LAST REVISION DATE:	


TITLE SHEET

T.1

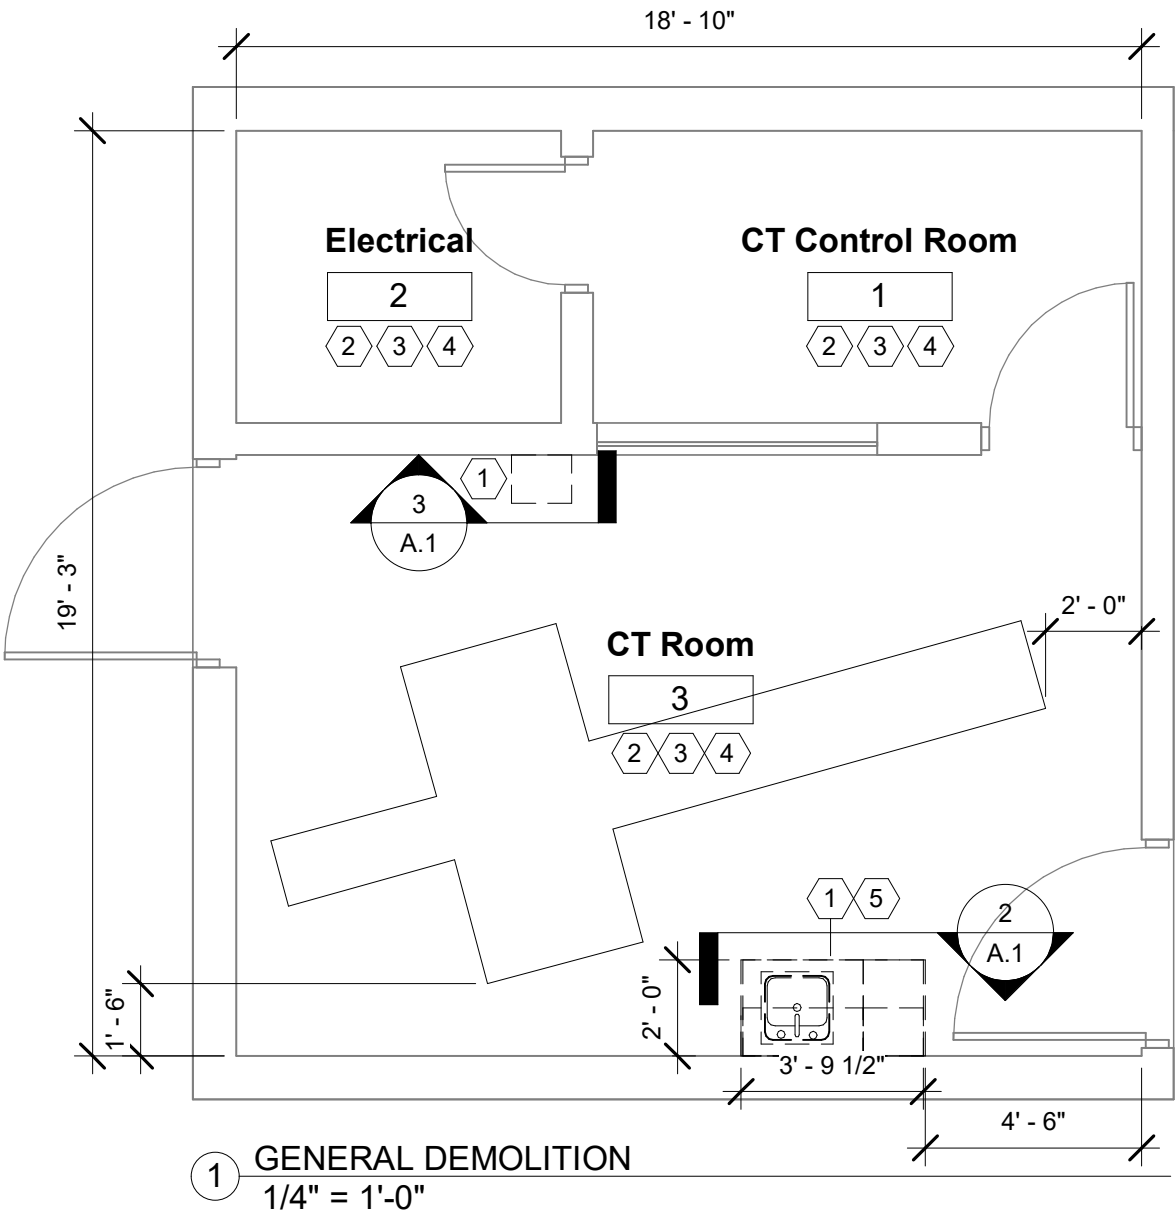

MASTER KEYNOTE	
Note Number	Note Content
1	Demolition Existing Cabinets as Per Base Bid
2	Demolish Existing VCT Flooring & Rubber Wall Base
3	Demolish Existing 2'x4' Ceiling Tile
4	Demolish Existing Ceiling Grid
5	Demolish Existing PVC Sewer Line 1' Below Floor & Cap. Demolish Water Line & Cap Above Ceiling Grid.

General Notes:
1. The contractor shall demolish throughout the following: flooring, ceiling tile, and ceiling grid. See SOW

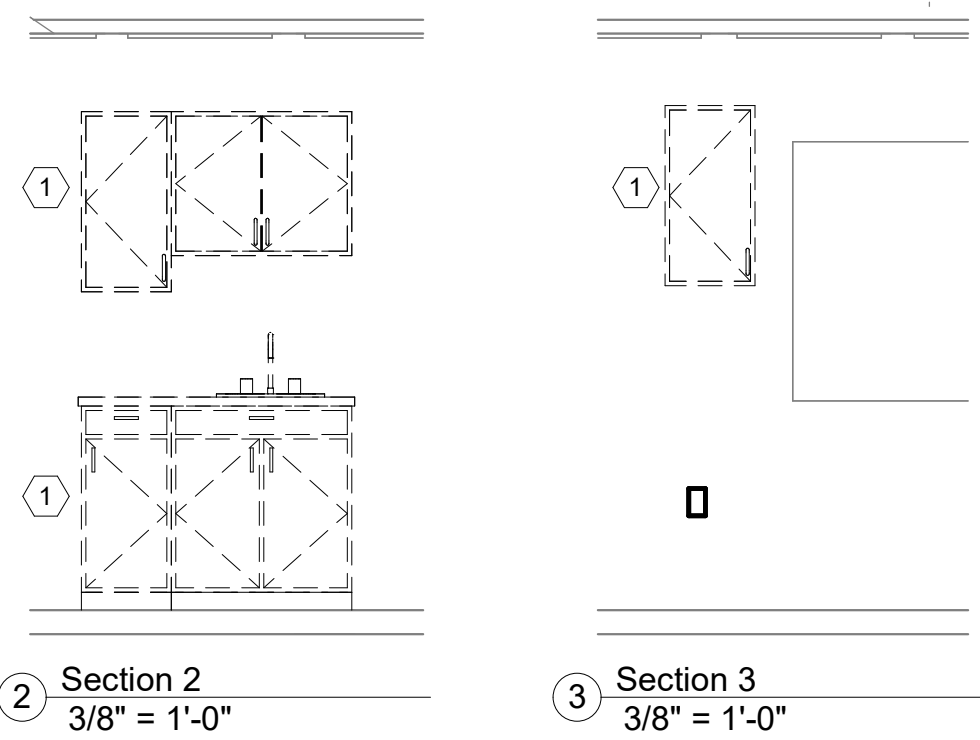

GREAT PLAINS AREA INDIAN HEALTH SERVICE
OFFICE OF ENVIRONMENTAL
HEALTH & ENGINEERING

DIVISION OF FACILITIES MANAGEMENT
115 4TH AVENUE SE, RM 309
ABERDEEN, SD 57401
(605) 226-7451 FAX (605) 226-7580
www.ihs.gov


Quentin N. Burdick
Memorial Health Facility

Replace RTU &
Cabinetry - CT Area


CONTRACT NO:	
TASK ORDER NO:	
PROJECT NUMBER:	GP22TM300H10
DATE:	08/26/2025
DRAWN BY:	Taylor Strand
CHECKED BY:	Brad Weekley
LAST REVISION DATE:	

GENERAL DEMOLITION


A.1

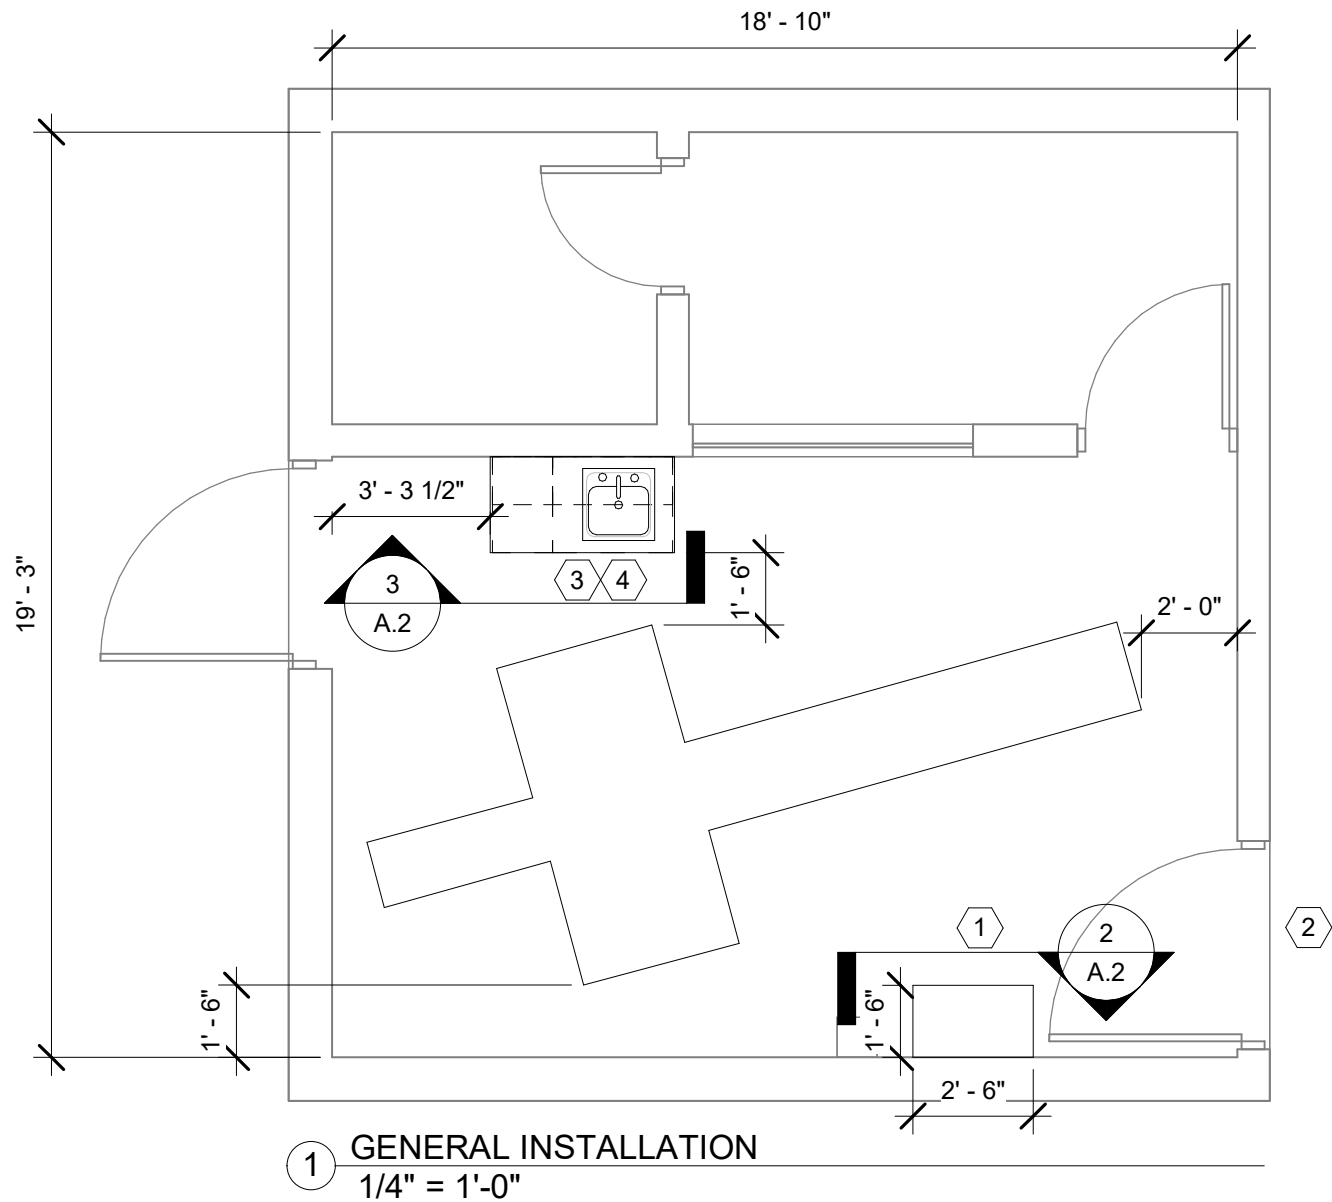

MASTER KEYNOTE	
Note Number	Note Content
1	Base Bid Cabinetry. MOD#1 Updates the Installation Location Only. See Base Bid for Further Details
2	Install New 4' Steel Door. See SOW
3	Base Bid Cabinetry. MOD#1 Updates the Installation Location Only. See Base Bid for Further Details
4	Install New 1/2" Copper Hot & Cold Water Lines. Tie Into Existing Water Lines Above Previous Sink. Install New 2" PVC Sewer & P-Trap. Tie Into Existing Sewer Line Below Previous Sink

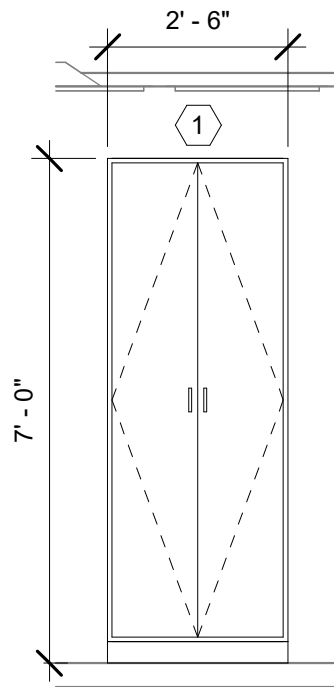

2 Section 4
3/8" = 1'-0"

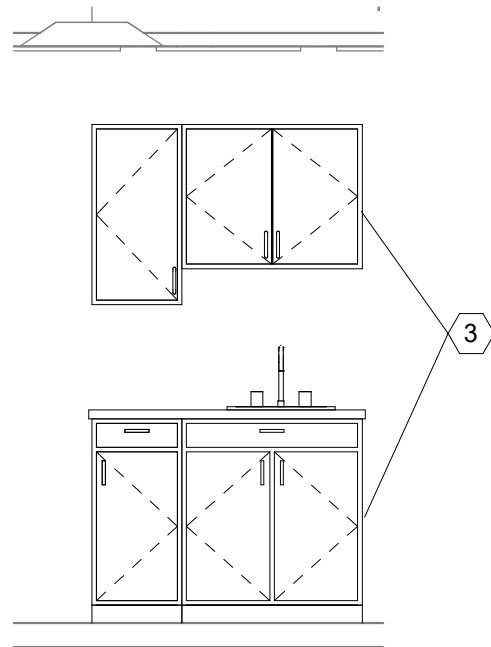

3 Section 5
3/8" = 1'-0"



GREAT PLAINS AREA INDIAN HEALTH SERVICE
OFFICE OF ENVIRONMENTAL
HEALTH & ENGINEERING

DIVISION OF FACILITIES MANAGEMENT
115 4TH AVENUE SE, RM 309
ABERDEEN, SD 57401
(605) 226-7451 FAX (605) 226-7580

www.ihs.gov

Quentin N. Burdick
Memorial Health Facility

Replace RTU & Cabinetry - CT Area

CONTRACT NO:	
TASK ORDER NO:	
PROJECT NUMBER:	GP22TM300H10
DATE:	08/26/2025
DRAWN BY:	Taylor Strand
CHECKED BY:	Brad Weekley
LAST REVISION DATE:	

GENERAL INSTALL

A.2



GREAT PLAINS AREA INDIAN HEALTH SERVICE
OFFICE OF ENVIRONMENTAL
HEALTH & ENGINEERING

DIVISION OF FACILITIES MANAGEMENT
115 4TH AVENUE SE, RM 309
ABERDEEN, SD 57401
(605) 226-7451 FAX (605) 226-7580

www.ihs.gov


Quentin N. Burdick
Memorial Health Facility

Replace RTU &
Cabinetry - CT Area


CONTRACT NO:	
TASK ORDER NO:	
PROJECT NUMBER:	GP22TM300H10
DATE:	08/26/2025
DRAWN BY:	Taylor Strand
CHECKED BY:	Brad Weekley
LAST REVISION DATE:	

CASEWORK SECTION
VIEWS


A.3

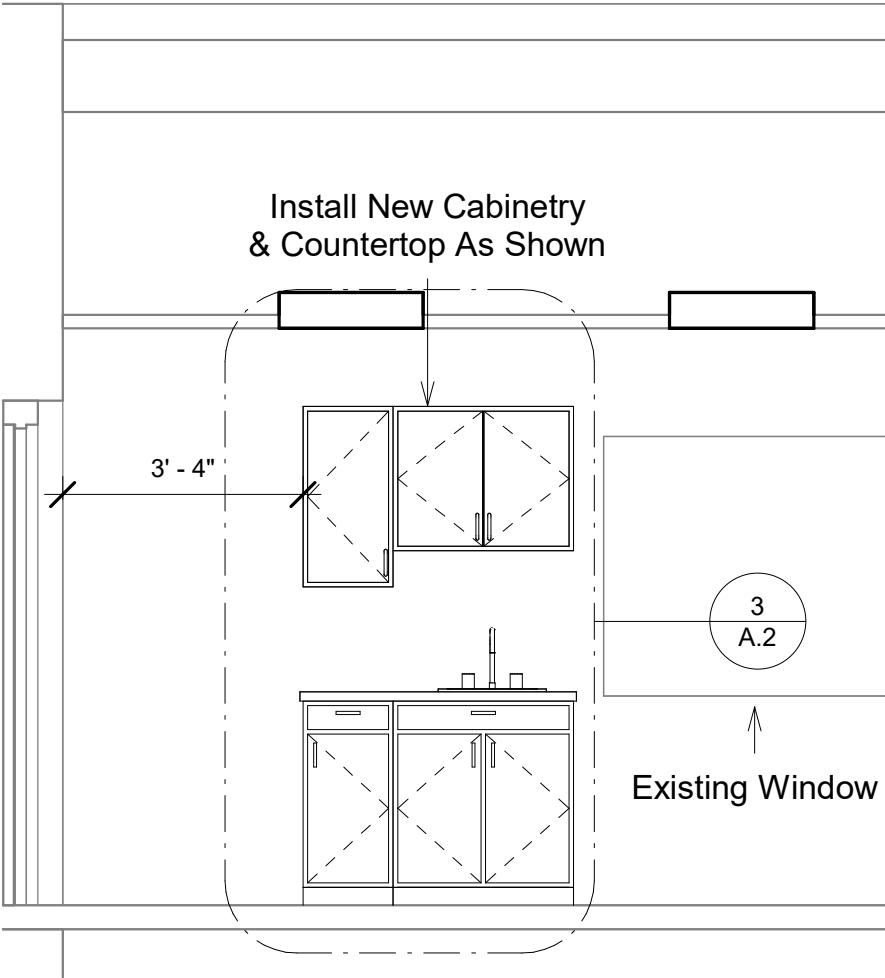


① North Wall Cabinets Copy 1
3/8" = 1'-0"

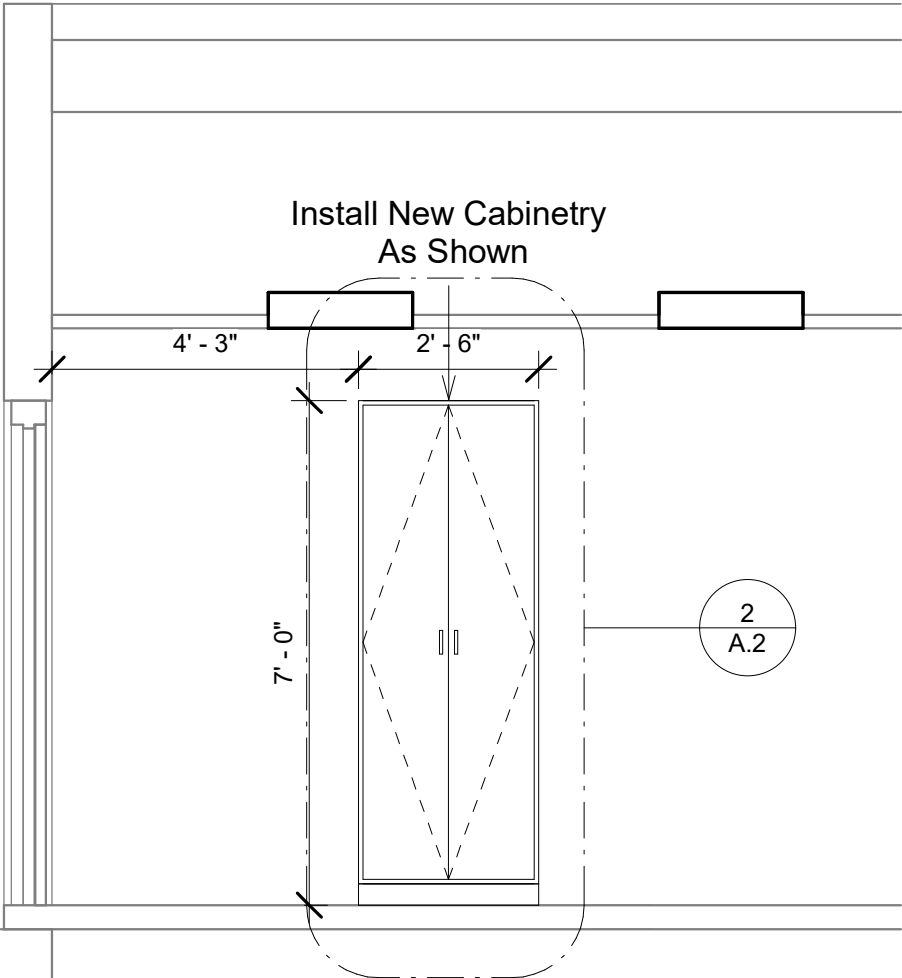

② South Wall Cabinets Copy 1
3/8" = 1'-0"

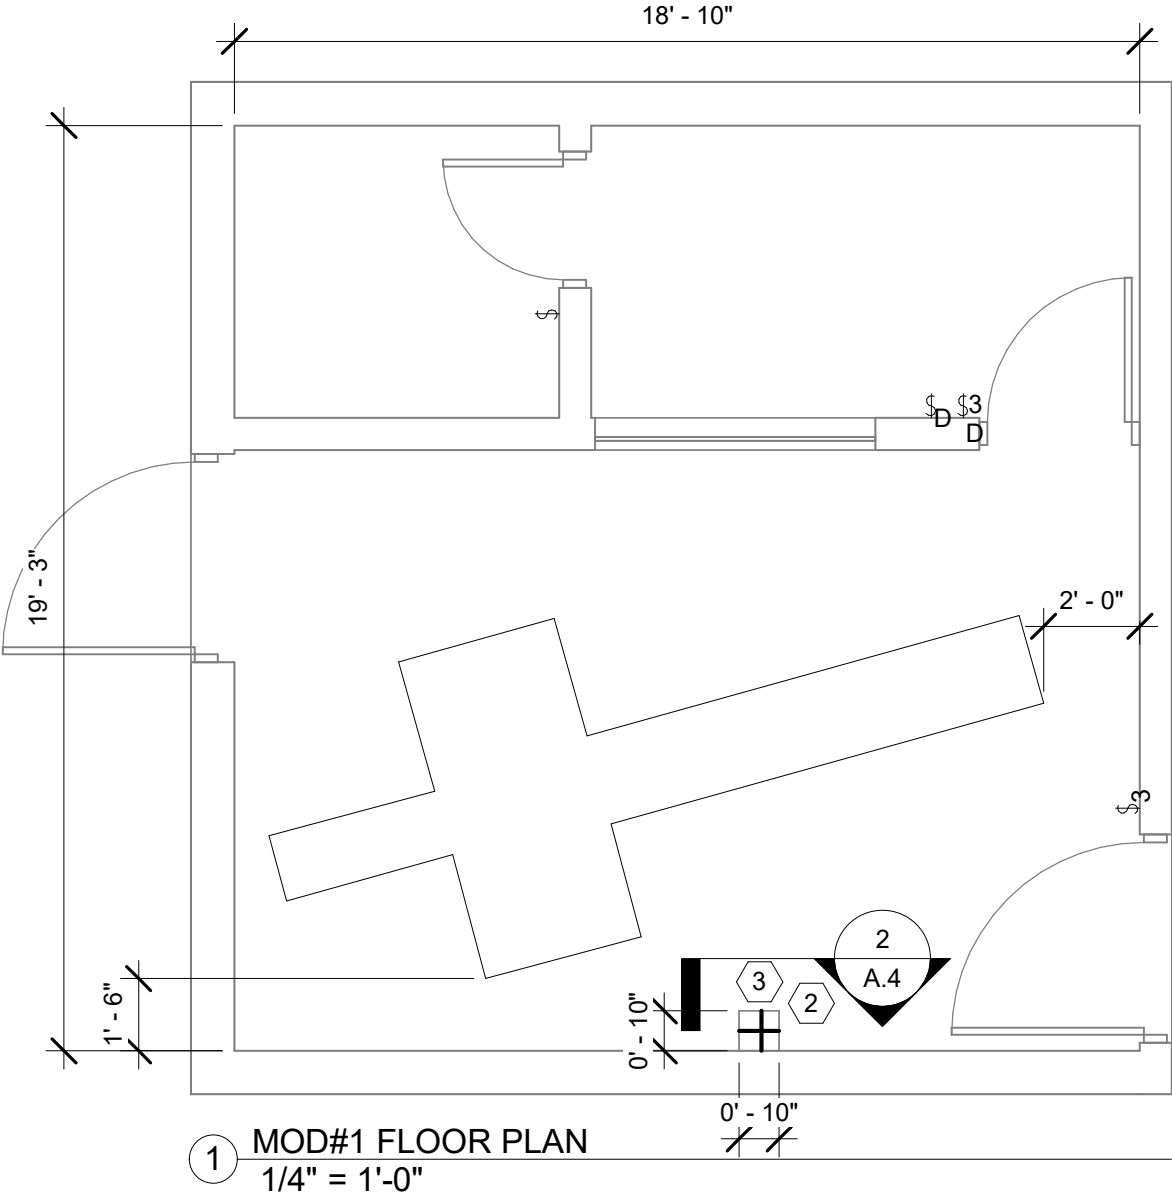

MASTER KEYNOTE	
Note Number	Note Content
1	Tac Weld 1" Form Decking to Existing Decking to Provide Construction Support for Concrete Floor.
2	Core 3/8" Rebar into Existing Concrete Slab. Space as Shown.
3	Saw Cut Edge of Existing Hole to Provide Smooth Straight Edge for New Concrete.
4	Install New 3" 5000 PSI Concrete Slab. Provide Smooth Trowel Finish.

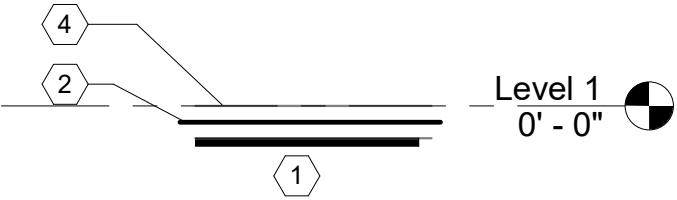

2 Section 1
1/2" = 1'-0"



GREAT PLAINS AREA INDIAN HEALTH SERVICE
OFFICE OF ENVIRONMENTAL
HEALTH & ENGINEERING

DIVISION OF FACILITIES MANAGEMENT
115 4TH AVENUE SE, RM 309
ABERDEEN, SD 57401
(605) 226-7451 FAX (605) 226-7580

www.ihs.gov


Quentin N. Burdick
Memorial Health Facility

Replace RTU &
Cabinetry - CT Area

CONTRACT NO:	
TASK ORDER NO:	
PROJECT NUMBER:	GP22TM300H10
DATE:	08/26/2025
DRAWN BY:	Taylor Strand
CHECKED BY:	Brad Weekley
LAST REVISION DATE:	

CONCRETE

A.4

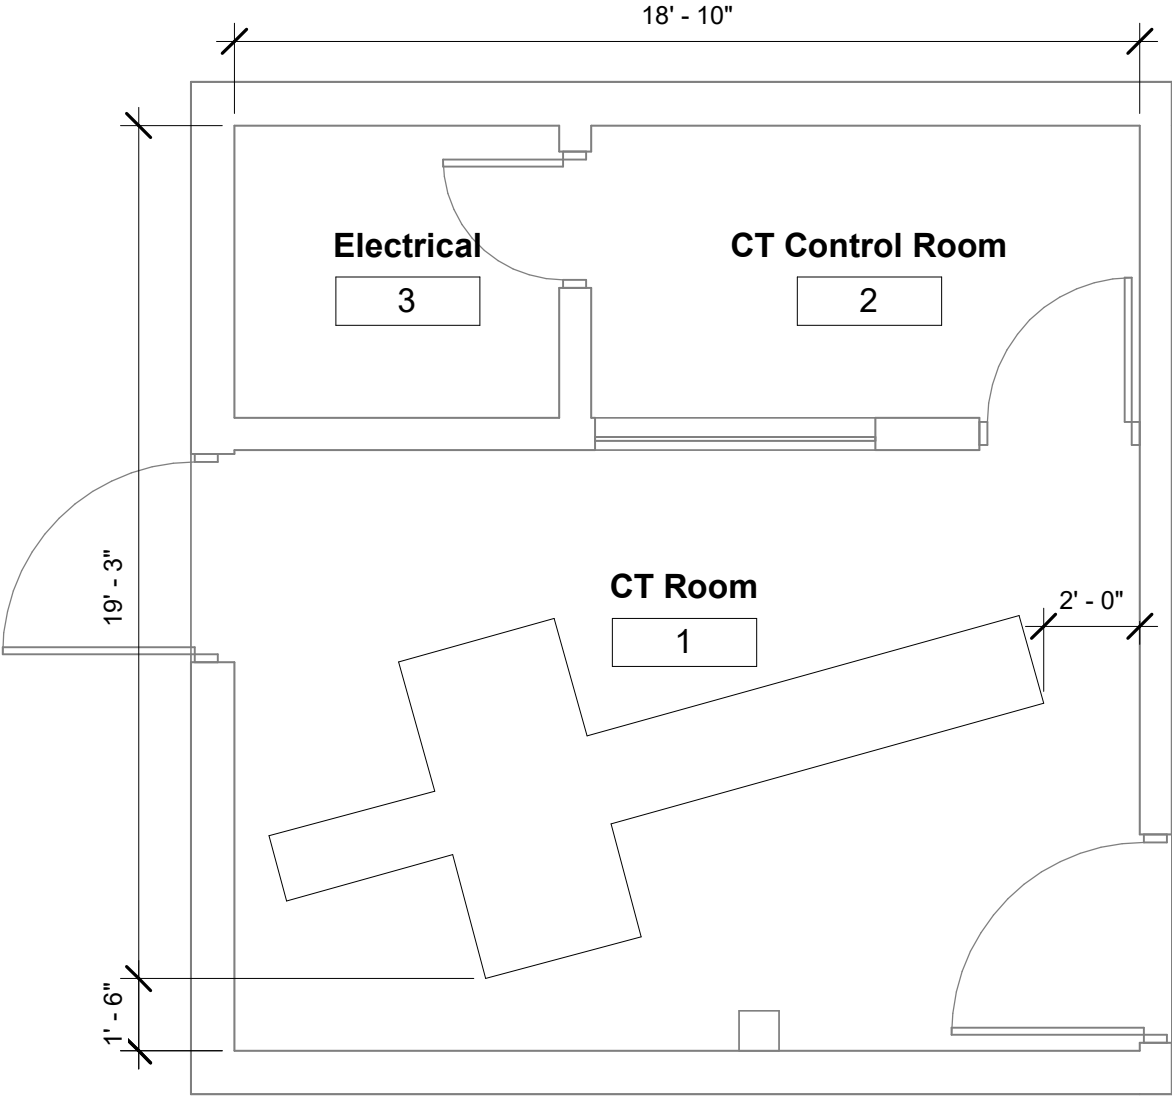

① MOD#1 ROOM FINISH
1/4" = 1'-0"

Room Schedule							
Number	Name	Area	Perimeter	Base Finish	Ceiling Finish	Wall Finish	Floor Finish
1	CT Room	240 SF	63'	6" Johnsonite Rubber. See SOW	2'x4'x1" Armstrong. See SOW	Clarks & Kensington. See SOW	Tarkett iQ Granit. See SOW
2	CT Control Room	70 SF	35'	6" Johnsonite Rubber. See SOW	2'x4'x1" Armstrong. See SOW	Clarks & Kensington. See SOW	Tarkett iQ Granit. See SOW
3	Electrical	40 SF	26'	6" Johnsonite Rubber. See SOW	2'x4'x1" Armstrong. See SOW	Clarks & Kensington. See SOW	Tarkett iQ Granit. See SOW
		350 SF	123'				



GREAT PLAINS AREA INDIAN HEALTH SERVICE
OFFICE OF ENVIRONMENTAL
HEALTH & ENGINEERING

DIVISION OF FACILITIES MANAGEMENT
115 4TH AVENUE SE, RM 309
ABERDEEN, SD 57401
(605) 226-7451 FAX (605) 226-7580


www.ihs.gov

Quentin N. Burdick
Memorial Health Facility

Replace RTU &
Cabinetry - CT Area

CONTRACT NO:	
TASK ORDER NO:	
PROJECT NUMBER:	GP22TM300H10
DATE:	08/26/2025
DRAWN BY:	Taylor Strand
CHECKED BY:	Brad Weekley
LAST REVISION DATE:	

ROOM FINISH

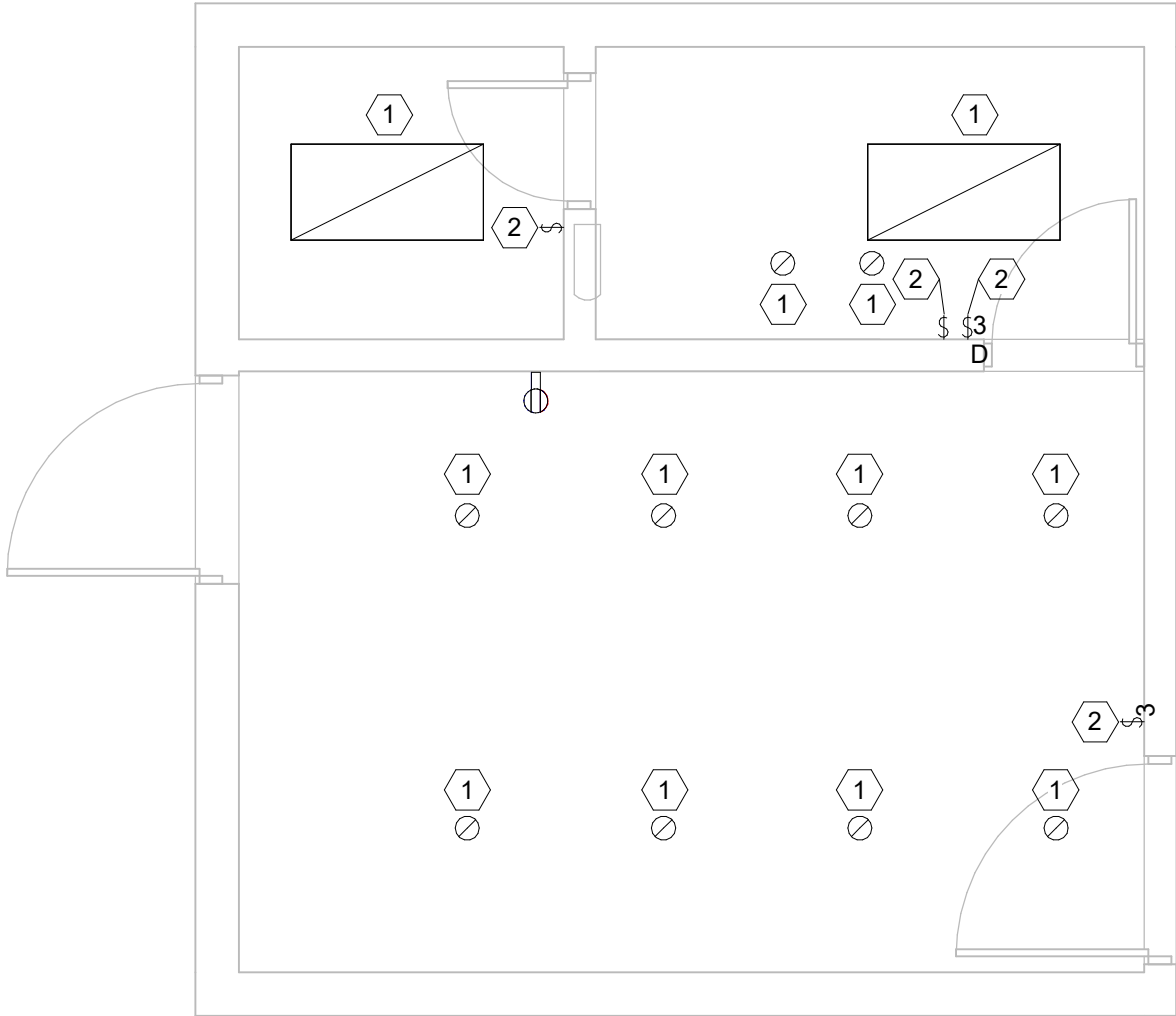

1 ELECTRICAL DEMOLITION
1/4" = 1'-0"

MASTER KEYNOTE	
Note Number	Note Content
1	Demolish Existing Light Fixture
2	Demolish Existing Light Switch.



GREAT PLAINS AREA INDIAN HEALTH SERVICE
OFFICE OF ENVIRONMENTAL
HEALTH & ENGINEERING

DIVISION OF FACILITIES MANAGEMENT
115 4TH AVENUE SE, RM 309
ABERDEEN, SD 57401
(605) 226-7451 FAX (605) 226-7580

www.ihs.gov


Quentin N. Burdick
Memorial Health Facility

Replace RTU &
Cabinetry - CT Area

CONTRACT NO:	
TASK ORDER NO:	
PROJECT NUMBER:	GP22TM300H10
DATE:	08/26/2025
DRAWN BY:	Taylor Strand
CHECKED BY:	Brad Weekley
LAST REVISION DATE:	

ELECTRICAL
DEMOLITION

E.1

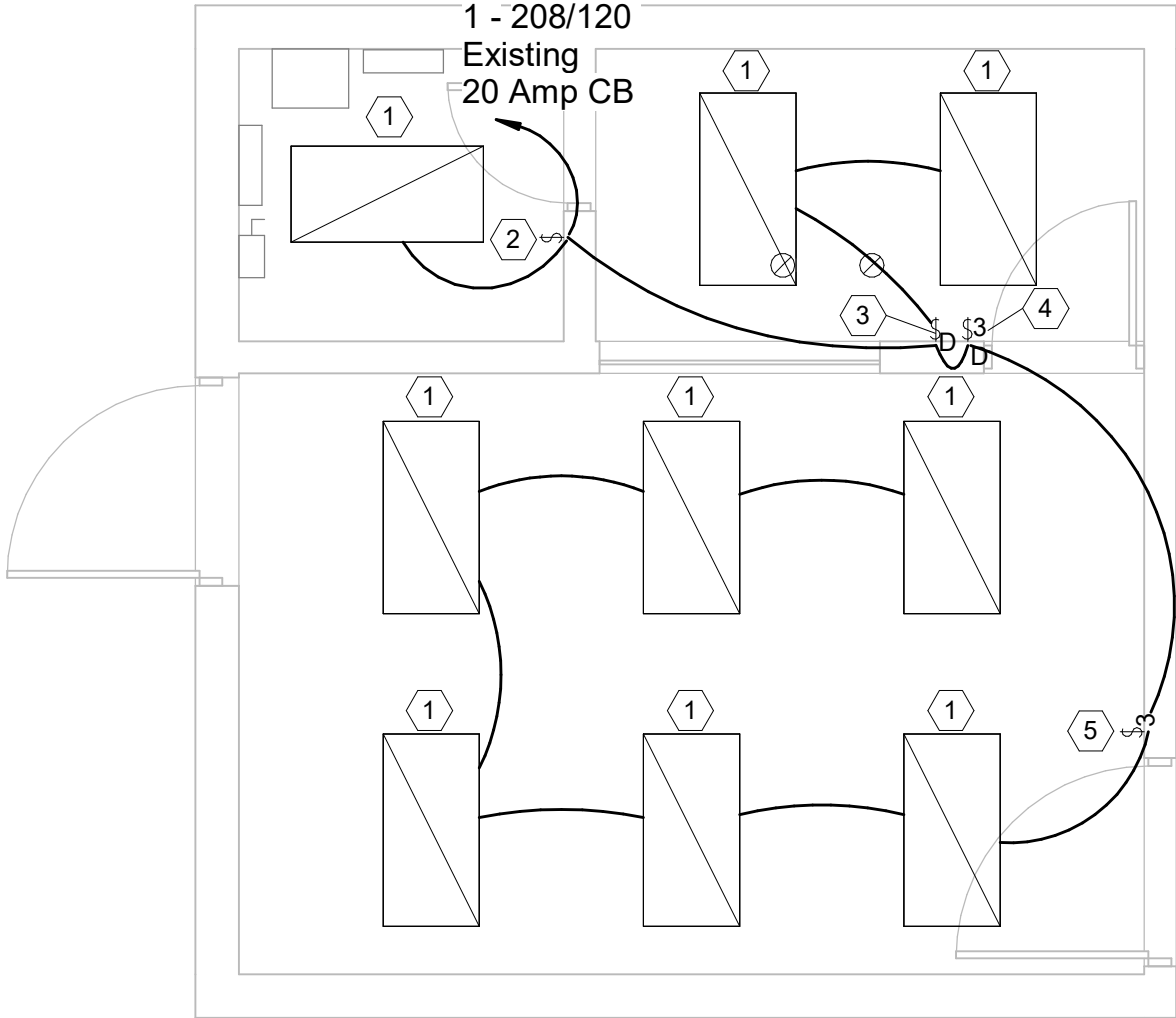

1 ELECTRICAL INSTALLATION
1/4" = 1'-0"

MASTER KEYNOTE	
Note Number	Note Content
1	Install New LED Light Fixture. See SOW.
2	Install New Single Pole Switch. See SOW.
3	Install New Single Pole Dimmer Switch. See SOW.
4	Install New Three Way Dimmer Switch. See SOW.
5	Install New Three Way Switch. See SOW.



GREAT PLAINS AREA INDIAN HEALTH SERVICE
OFFICE OF ENVIRONMENTAL
HEALTH & ENGINEERING

DIVISION OF FACILITIES MANAGEMENT
115 4TH AVENUE SE, RM 309
ABERDEEN, SD 57401
(605) 226-7451 FAX (605) 226-7580

www.ihs.gov

Quentin N. Burdick
Memorial Health Facility

Replace RTU &
Cabinetry - CT Area

CONTRACT NO:	
TASK ORDER NO:	
PROJECT NUMBER:	GP22TM300H10
DATE:	08/26/2025
DRAWN BY:	Taylor Strand
CHECKED BY:	Brad Weekley
LAST REVISION DATE:	

ELECTRICAL
INSTALLATION

E.2



GREAT PLAINS AREA INDIAN HEALTH SERVICE
OFFICE OF ENVIRONMENTAL
HEALTH & ENGINEERING

DIVISION OF FACILITIES MANAGEMENT
115 4TH AVENUE SE, RM 309
ABERDEEN, SD 57401
(605) 226-7451 FAX (605) 226-7580

www.ihs.gov


Quentin N. Burdick
Memorial Health Facility

Replace RTU &
Cabinetry - CT Area

CONTRACT NO:	
TASK ORDER NO:	
PROJECT NUMBER:	GP22TM300H10
DATE:	08/26/2025
DRAWN BY:	Taylor Strand
CHECKED BY:	Brad Weekley
LAST REVISION DATE:	

CRAWL SPACE STEAM
PIPE TIE IN

M.1

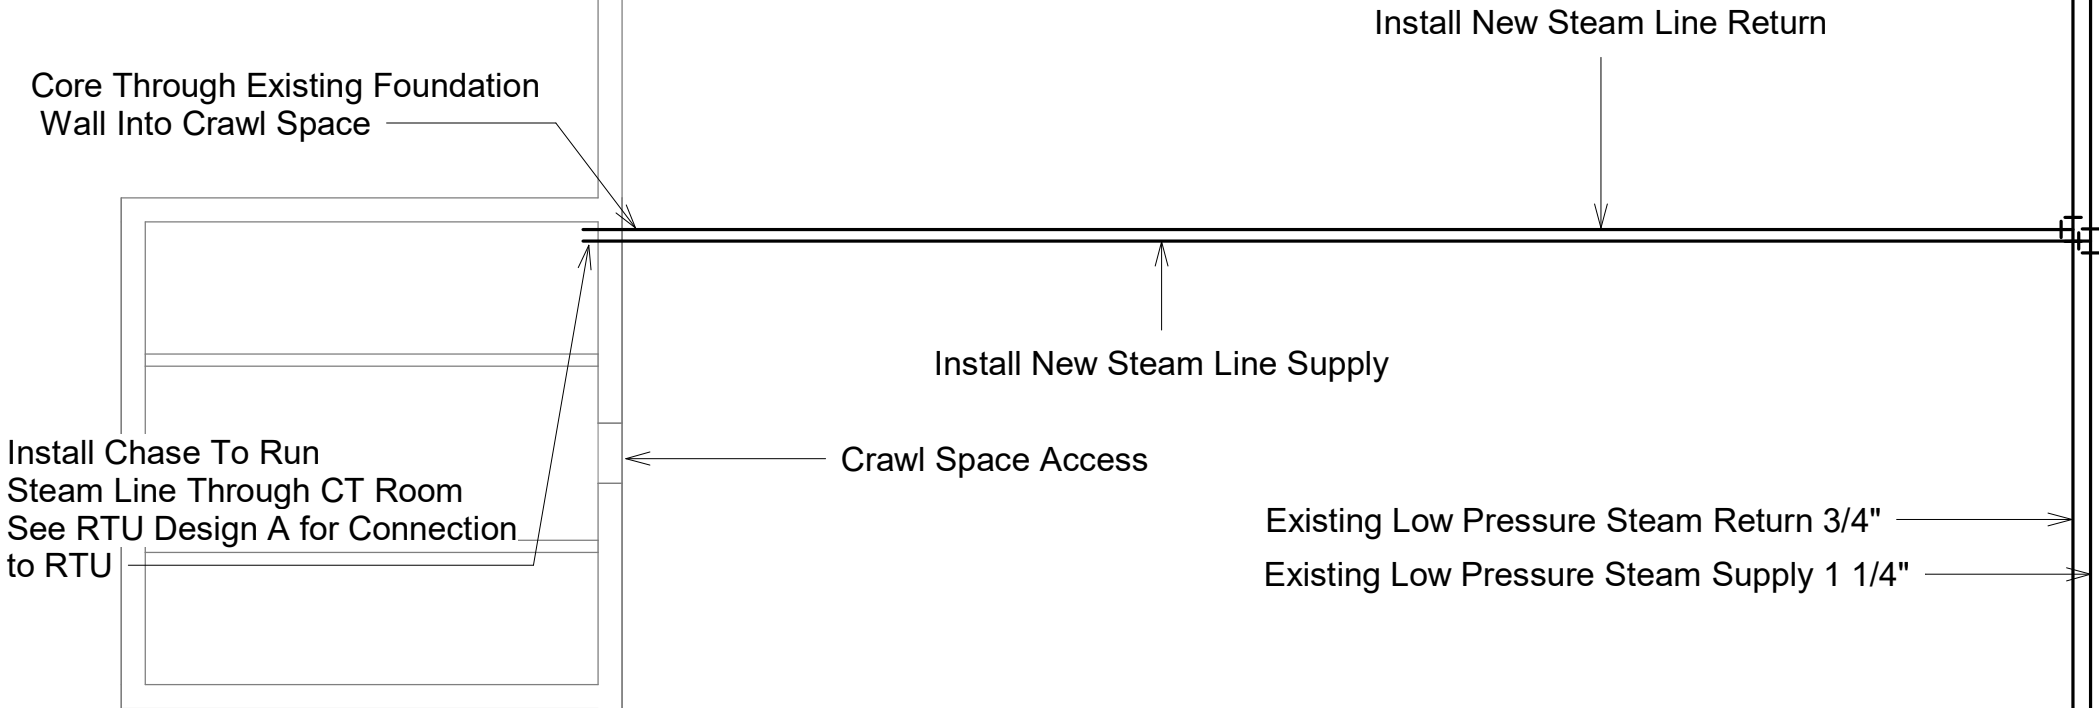

1 CRAWL SPACE PIPING
1/8" = 1'-0"