




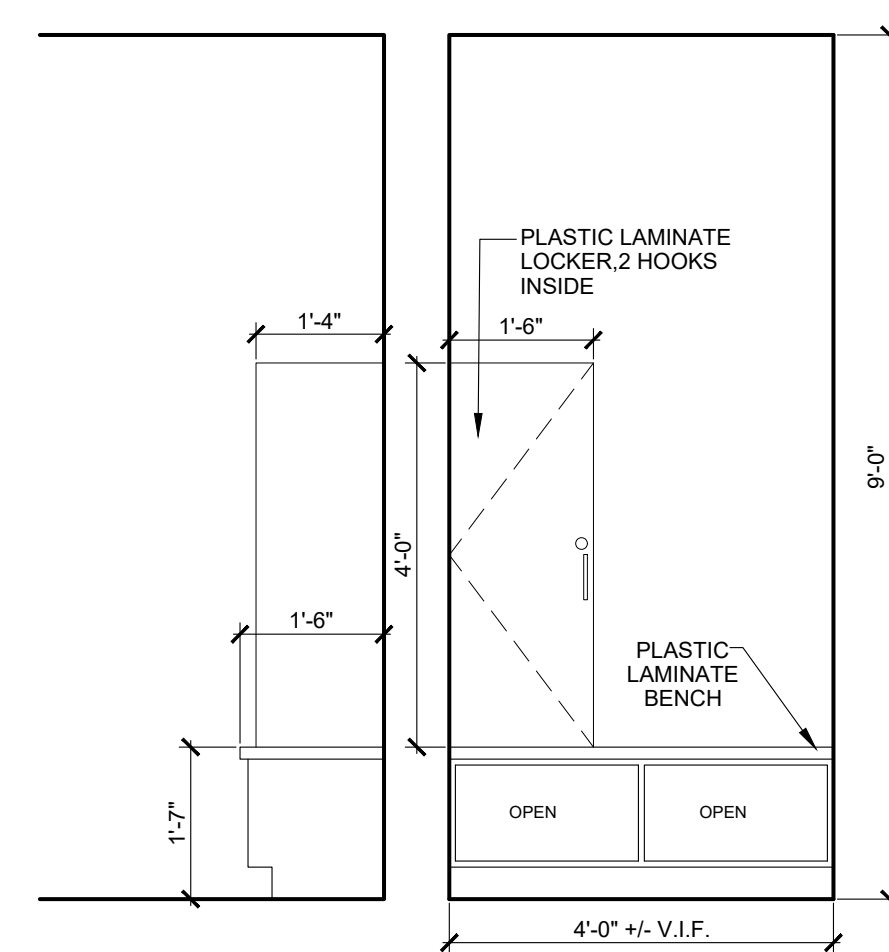


1 DRESS 101 ELEVATION
AE401 SCALE: 1/2" = 1'-0"

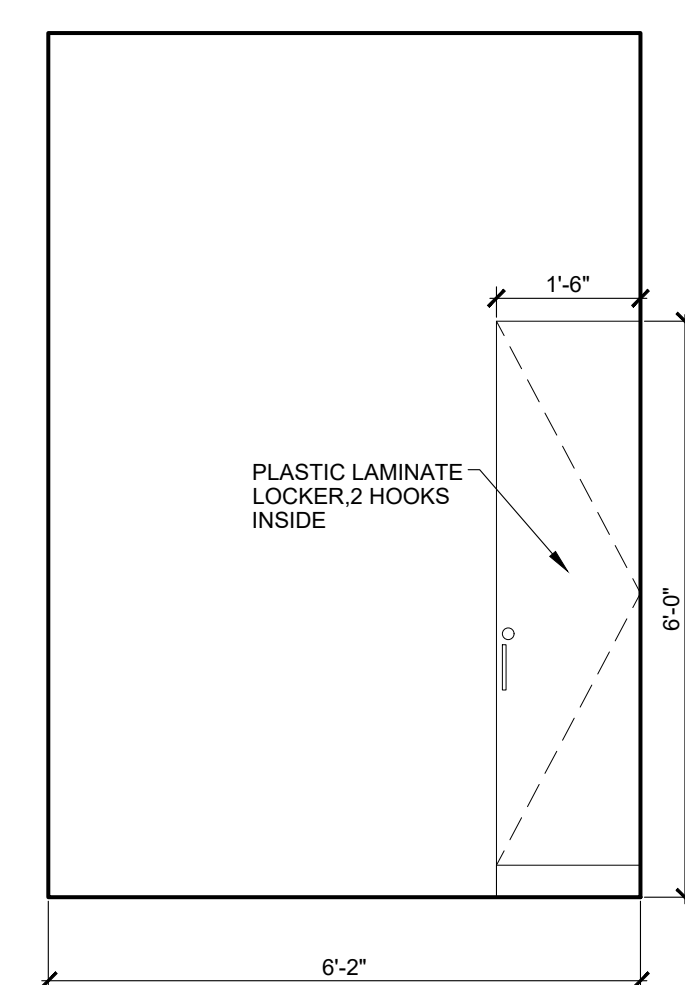


2 DRESS 102 ELEVATION
AE401 SCALE: 1/2" = 1'-0"

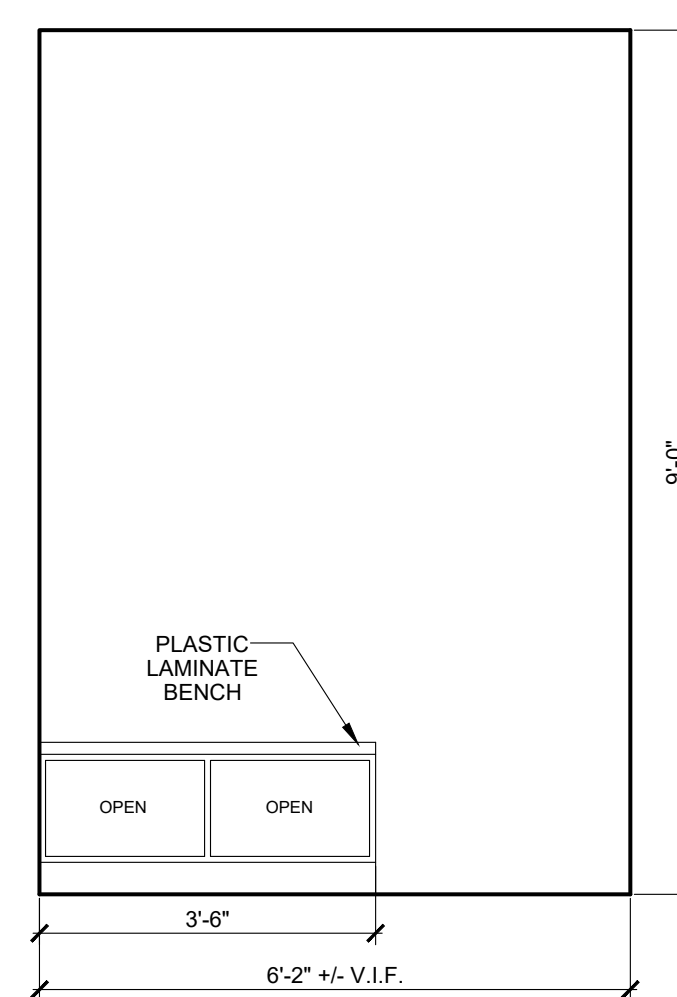


3 DRESS 102 ELEVATION
AE401 SCALE: 1/2" = 1'-0"

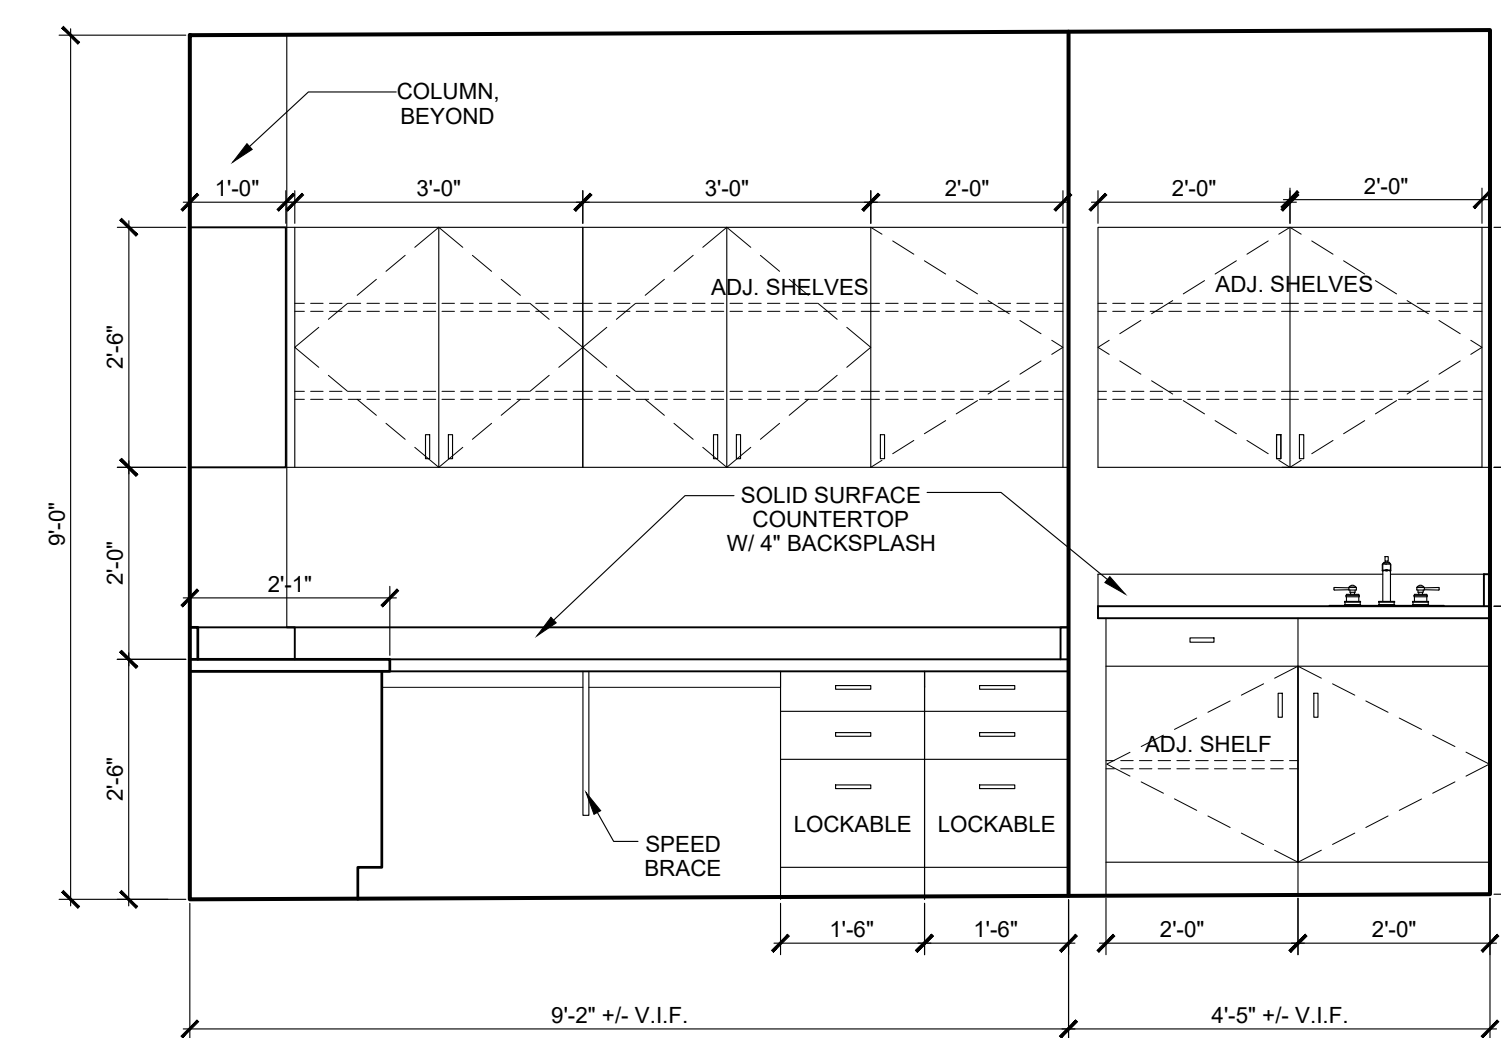


4 CONTROL ROOM 105
AE401 SCALE: 1/2" = 1'-0"

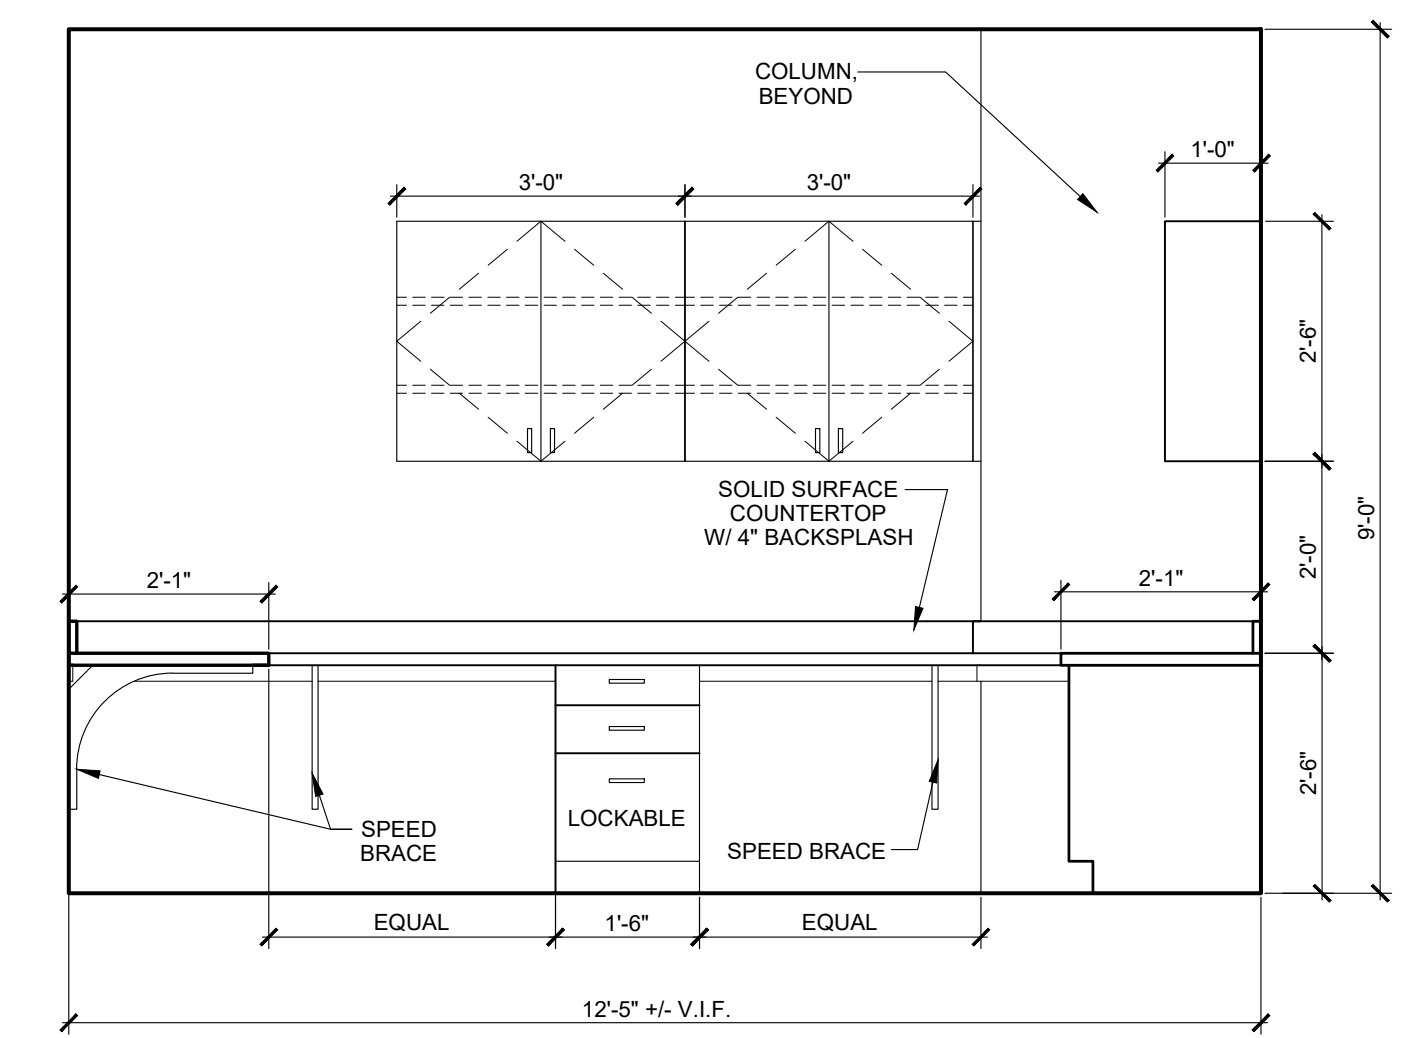


5 CONTROL ROOM 105
AE401 SCALE: 1/2" = 1'-0"

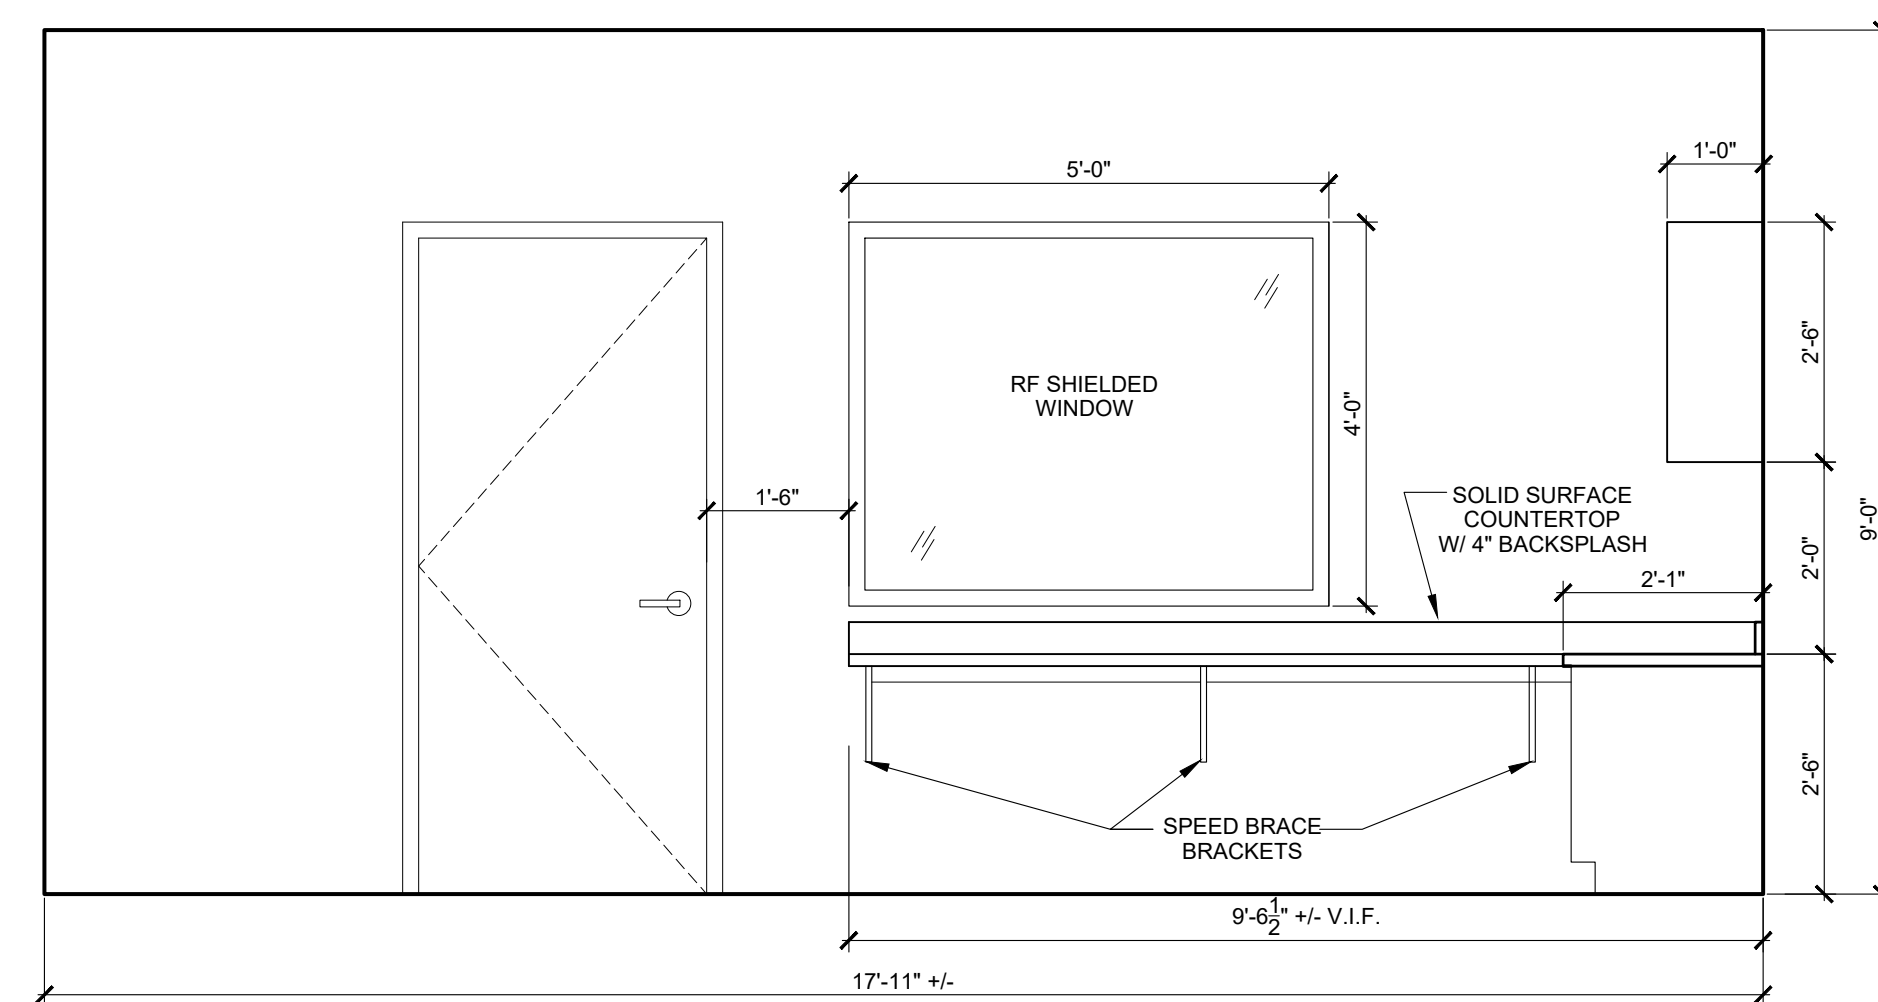

6 CONTROL ROOM 105
AE401 SCALE: 1/2" = 1'-0"

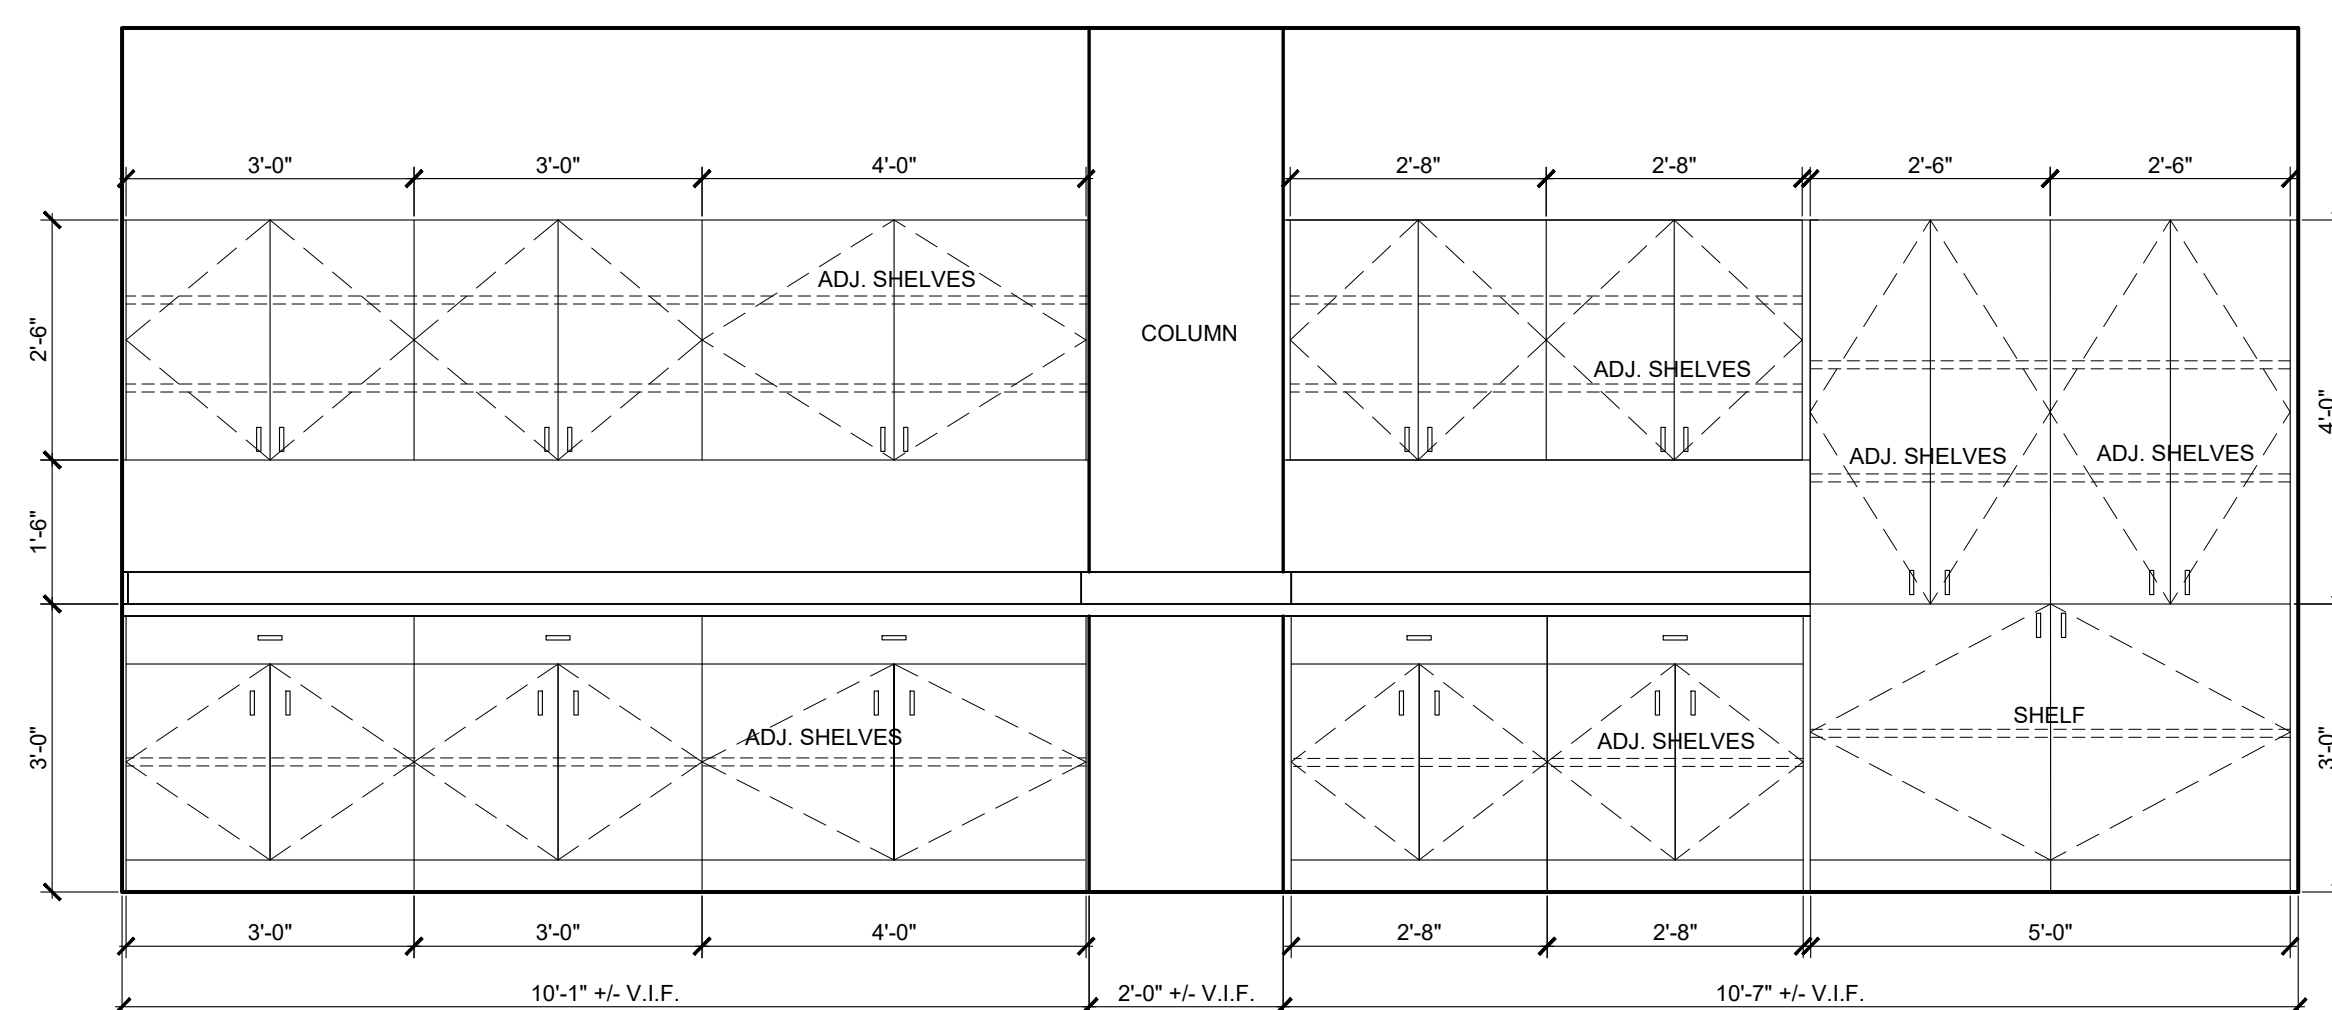


7 MRI SCAN ROOM 107
AE401 SCALE: 1/2" = 1'-0"

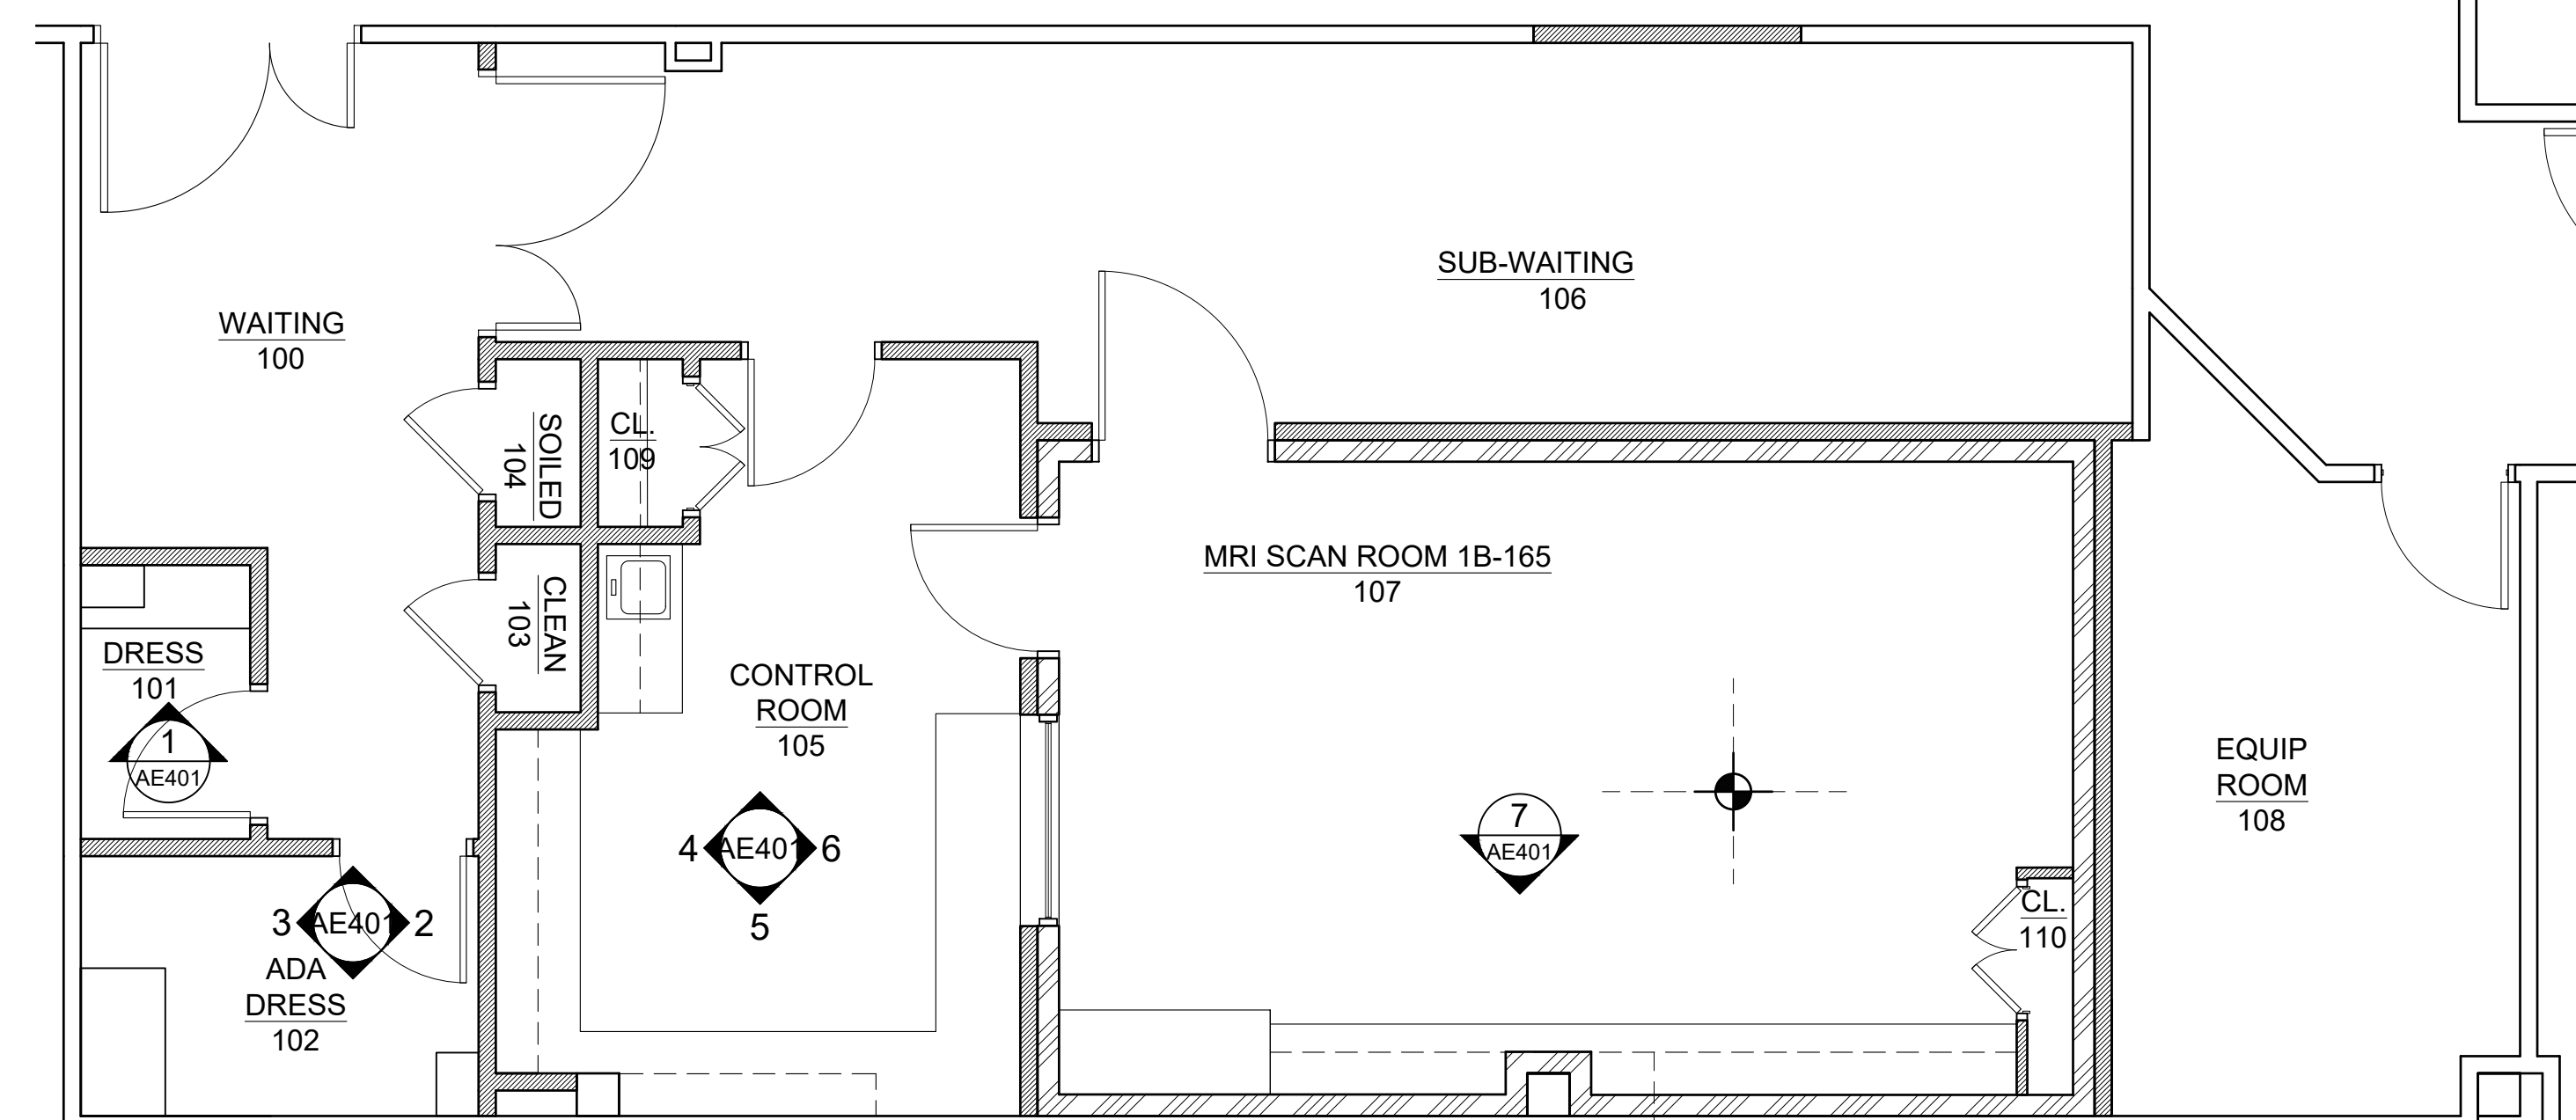


8 MILLWORK PLAN
AE401 SCALE: 1/4" = 1'-0"

MILLWORK NOTES


- 1: WALL AND BASE CABINETS EXTERIOR TO BE PLASTIC LAMINATE, SEE FINISH SCHEDULE FOR SPECIFICATION.
- 2: WALL AND BASE CABINET INTERIOR TO BE WHITE MELAMINE.
- 3: COUNTERTOPS WITH 4" BACKSPLASH TO BE SOLID SURFACE, SEE FINISH SCHEDULE FOR SPECIFICATION.
- 4: PROVIDE ADJUSTABLE SHELVES AS INDICATED ON ELEVATIONS.
- 5: DOORS AND DRAWERS TO HAVE 4" BRUSHED CHROME WIRE SHELVES

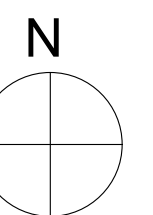[illegible]

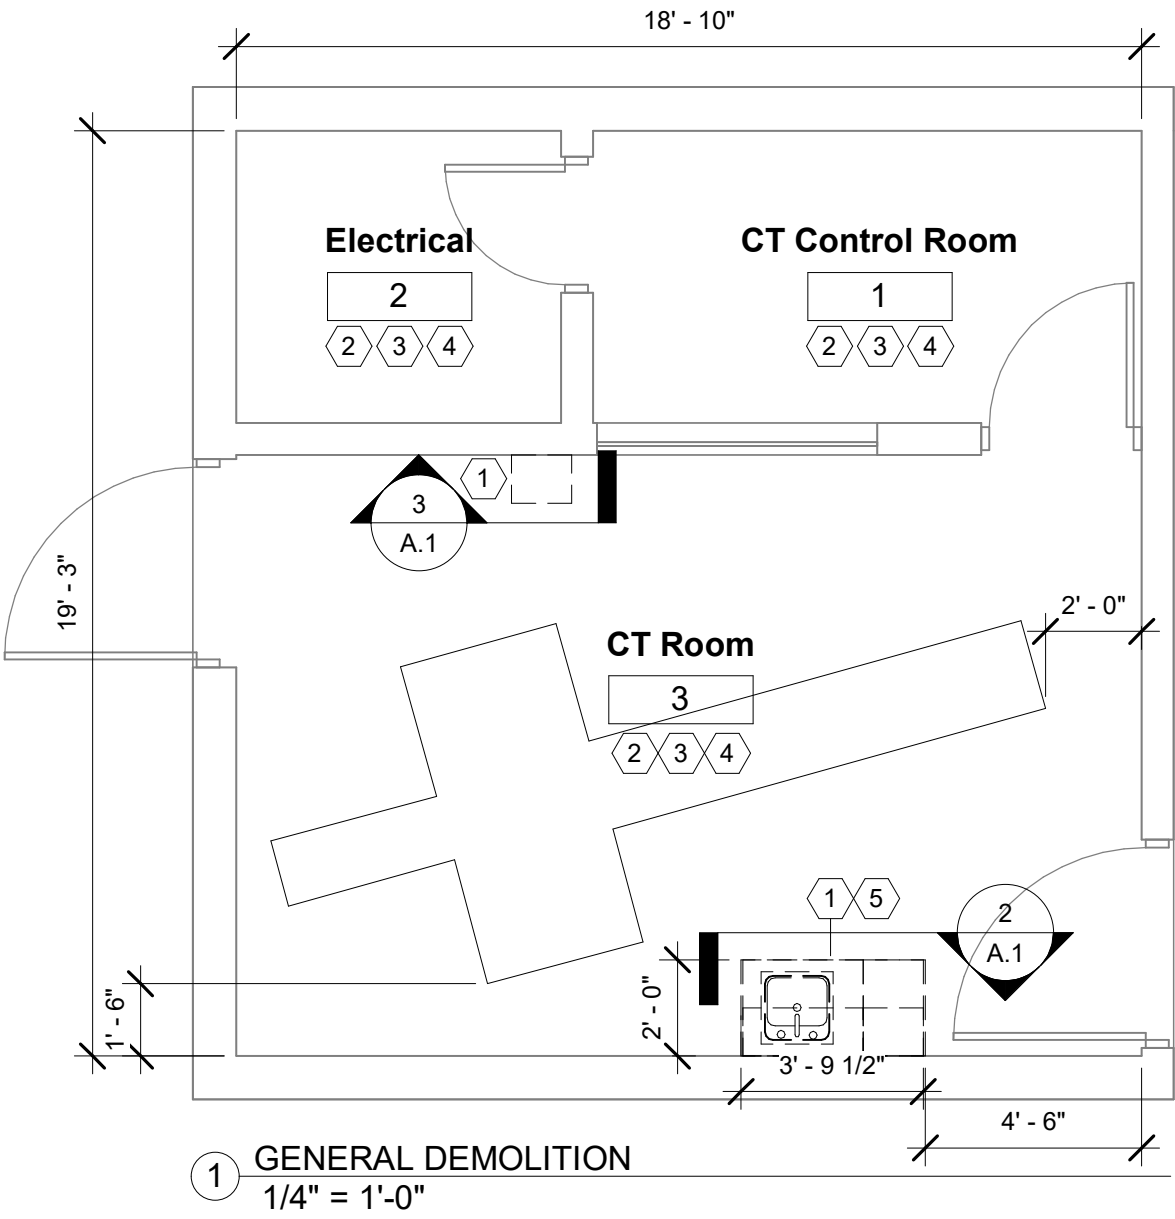

MASTER KEYNOTE	
Note Number	Note Content
1	Demolition Existing Cabinets as Per Base Bid
2	Demolish Existing VCT Flooring & Rubber Wall Base
3	Demolish Existing 2'x4' Ceiling Tile
4	Demolish Existing Ceiling Grid
5	Demolish Existing PVC Sewer Line 1' Below Floor & Cap. Demolish Water Line & Cap Above Ceiling Grid.

General Notes:
1. The contractor shall demolish throughout the following: flooring, ceiling tile, and ceiling grid. See SOW

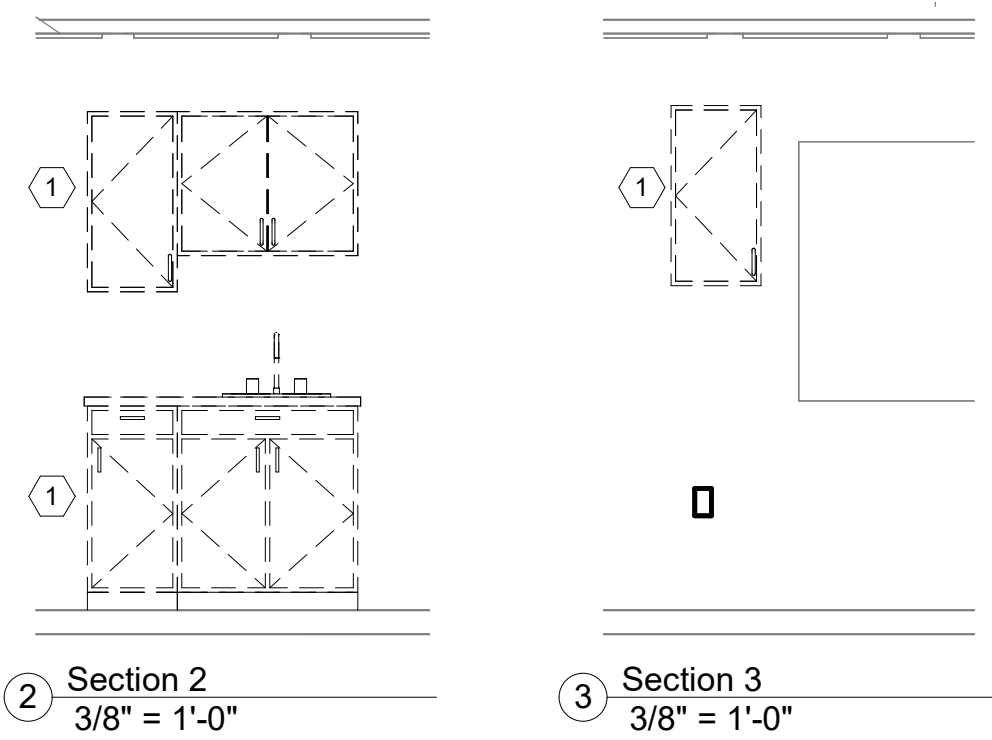

GREAT PLAINS AREA INDIAN HEALTH SERVICE
OFFICE OF ENVIRONMENTAL
HEALTH & ENGINEERING

DIVISION OF FACILITIES MANAGEMENT
115 4TH AVENUE SE, RM 309
ABERDEEN, SD 57401
(605) 226-7451 FAX (605) 226-7580
www.ihs.gov

Quentin N. Burdick
Memorial Health Facility

Replace RTU &
Cabinetry - CT Area

CONTRACT NO:	
TASK ORDER NO:	
PROJECT NUMBER:	GP22TM300H10
DATE:	08/26/2025
DRAWN BY:	Taylor Strand
CHECKED BY:	Brad Weekley
LAST REVISION DATE:	

GENERAL DEMOLITION

A.1

DENTAL LAB GENERAL NOTES

- DENTAL LAB CASEWORK AND WORK BENCHES ARE SPECIFIED IN SECTION 12 35 40. VENDOR DRAWINGS ARE PROVIDED IN APPENDIX. CC SHALL COORDINATE INSTALLATION OF UTILITY CONNECTIONS WITH REQUIREMENTS SPECIFIED AND SHOWN THEREIN.
- AVOID CUTTING CONCRETE FLOOR JOIST.

EQUIPMENT ABBREVIATIONS

- CC: CONTRACTOR FURNISHED & INSTALLED
VV: VA FURNISHED & INSTALLED
VC: VA FURNISHED & CONTRACTOR INSTALLED

EQUIPMENT SCHEDULE - SHEET AE124


JSN	DESCRIPTION	ACTIVATED BY	Comments
A1012	TELEPHONE, WALL MOUNTED	VV	
A1066	MIRROR, FLOAT GLASS, WITH SS FRAME, 18 X 36	CC	
A5075	DISPENSER, HAND SOAP	VV	
A5077	HAND SANITIZER DISPENSER	VV	
A5080	DISPENSER, PAPER TOWEL	VV	
A5106	WASTE DISPOSAL UNIT, SHARPS	VV	
A5145	HOOK, GARMENT, DOUBLE, SS, SURFACE MOUNTED	CC	
D0670	CONSOLE, TREATMENT UNIT, DENTAL OPERATORY	CC	SEE SPEC SECTION 12 35 70.74
D0680	CONSOLE, ACCESSORY/SIDE DENTAL OPERATORY	CC	SEE SPEC SECTION 12 35 70.74
D0682	3 GLOVE DISPENSING CABINET, DENTAL OPERATORY	CC	SEE SPEC SECTION 12 35 70.74
D0685	STORAGE CABINET, DENTAL OPERATORY - 34 INCH WIDE	CC	SEE SPEC SECTION 12 35 70.74
D0685B	STORAGE CABINET, FULL HEIGHT, 2 DOORS, LOCKABLE DENTAL	CC	SEE SPEC SECTION 12 35 70.74
D0755	TANK ASSEMBLY, BOILOUT - CURING, DOUBLE	CC	SEE SPEC SECTION 12 34 50, SEE EP103 & PL106 MEP FOR CONNECTIONS
D2520	MOBILE STORAGE CABINET	CC	SEE SPEC SECTION 12 35 70.74
D3320	CHAIR, DENTAL OPERATING	CC	SEE SPEC SECTION 11 74 00
D3565	RESIN CURING UNIT, VISABLE LIGHT	VV	
D4100	CLEANER, STEAM, DENTAL	VV	
D4260	HANDPIECE, LABORATORY, DENTAL, ELECTRIC	VV	
D4320	PRESS, FLASK, HYDRAULIC, SINGLE FLASK	VV	
D4560	ENGINE, DENTAL BENCH, ELECTRIC	VV	
D4590	CHISEL, DENTAL, PNEUMATIC	VV	
D6600	MIXER/INVESTOR, WITH VACUUM	VV	
D6650	FROMER, VACUUM, W/MOTOR, VACCUM PUMP, HEATER	VV	
D8250	DELIVERY SYSTEM, DENTAL OPERATORY WITH ASST INSTRUMENTATION	CC	SEE SPEC SECTION 11 74 00
D8530	DENTAL POLISHER	VV	
D8850	AMAL GAMATOR, DENTAL	VV	
D8950	VIBRATOR, DENTAL, HEAVY DUTY	VV	
D9015	MICROFINISHER, DENTAL, COUNTER MOUNTED	VV	
D9035	DRIVER, MODEL INDEXING PINS	VV	
D9050	TRIMMER, MODEL, DENTAL 0.25 HP	VV	
DX001	PRESSURE POT 8 QUART	VV	
DX002	DENTAL WORK BENCH, 23" DEPTH	VC	SEE SPEC SECTION 12 34 50
DX003	AIR HOSE X6 + ACCESSORIES	VV	
DX004	SAND SHELL XL	VV	
DX005	WAXING UNIT	VV	
DX006	TOUCH O MATIC BUN BURNER NATURAL GAS #77-0	VV	
DX007	AIR PURIFIER 301F	VV	
DX008	SAND VAC GRAY	VV	
DX009	ATLAS UPPER FLASK W/REAR GUIDE PIN #44U	VV	
DX010	ATLAS LOWER FLASK W/REAR GUIDE PIN #44L	VV	
DX011	COMPRESS FLASKS F2	VV	
DX012	RELINIE JIG 2 POST	VV	
DX013	IMPULSE HEAT SEALER	VV	
DX014	FLAMMABLE CABINET	VV	
DX016	ARTICULATOR MOUNTING PLATE	VV	
DX017	HANAU WIDE - VUE ARTICULATOR HANAU ARCON 183-2	VV	
DX018	WHIP MIX MODEL 2240 ARTICULATOR W/SERIES 200 FRAME	VV	
DX019	CURING UNIT	VV	
DX020	DENTAL MOLDING VIBRATOR	VV	
DX021	FUME HOOD	CC	SEE SPEC SECTION 23 38 13
DX023	DENTAL LAB CASEWORK	VC	SEE SPEC SECTION 12 34 50
M1801A	LAPTOP COMPUTER	VV	
M1803	COMPUTER WORKSTATION, WALL MOUNTED	CC	
P7650	TRAP, PLASTER, SMALL	CC	
X6600	RADIOGRAPHIC XRAY UNIT (PLANMECA PRO-X)	VV	
X6610	SENSOR, DENTAL IMAGING SYSTEM (PLANMECA PRO-X)	VV	
X6620	EXPOSURE SWITCH - DENTAL XRAY (PLANMECA PRO-X)	VV	

NOTE: LAB CASEWORK AND DENTAL WORK BENCHES SHOWN ARE FOR REFERENCE ONLY. REFER TO VENDOR DRAWINGS IN APPENDIX & SPECIFICATION SECTION 12 35 40.

0 1'-2" 2'-4" 4'-8"

1 DENTAL LAB 5B113 & SHIPPING/RECEIVING ROOM 5B110

AE124 3/8" = 1'-0"

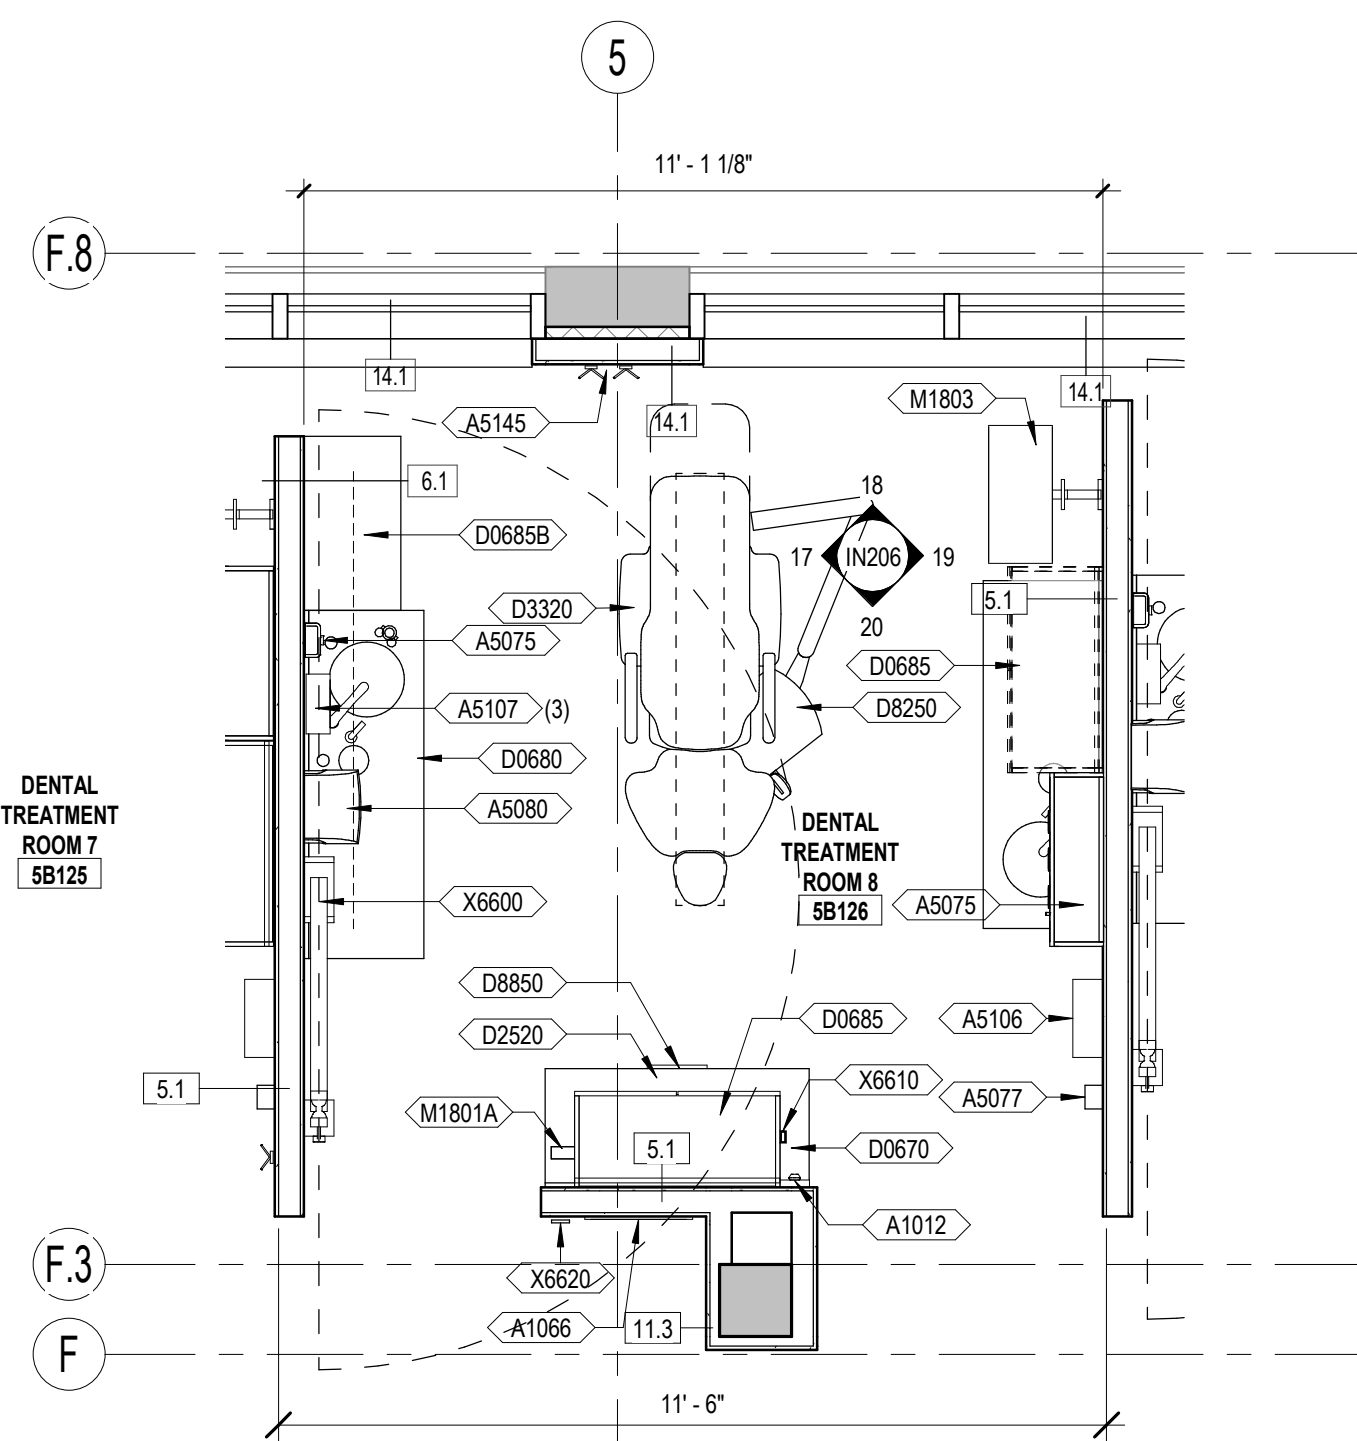


NOTE:
SIM: 5B116, 5B117, 5B118, 5B119, 5B120, 5B121, 5B125, 5B133, 5B139

2 DENTAL TREATMENT ROOM

AE124 3/8" = 1'-0"

0 1'-2" 2'-4" 4'-8"

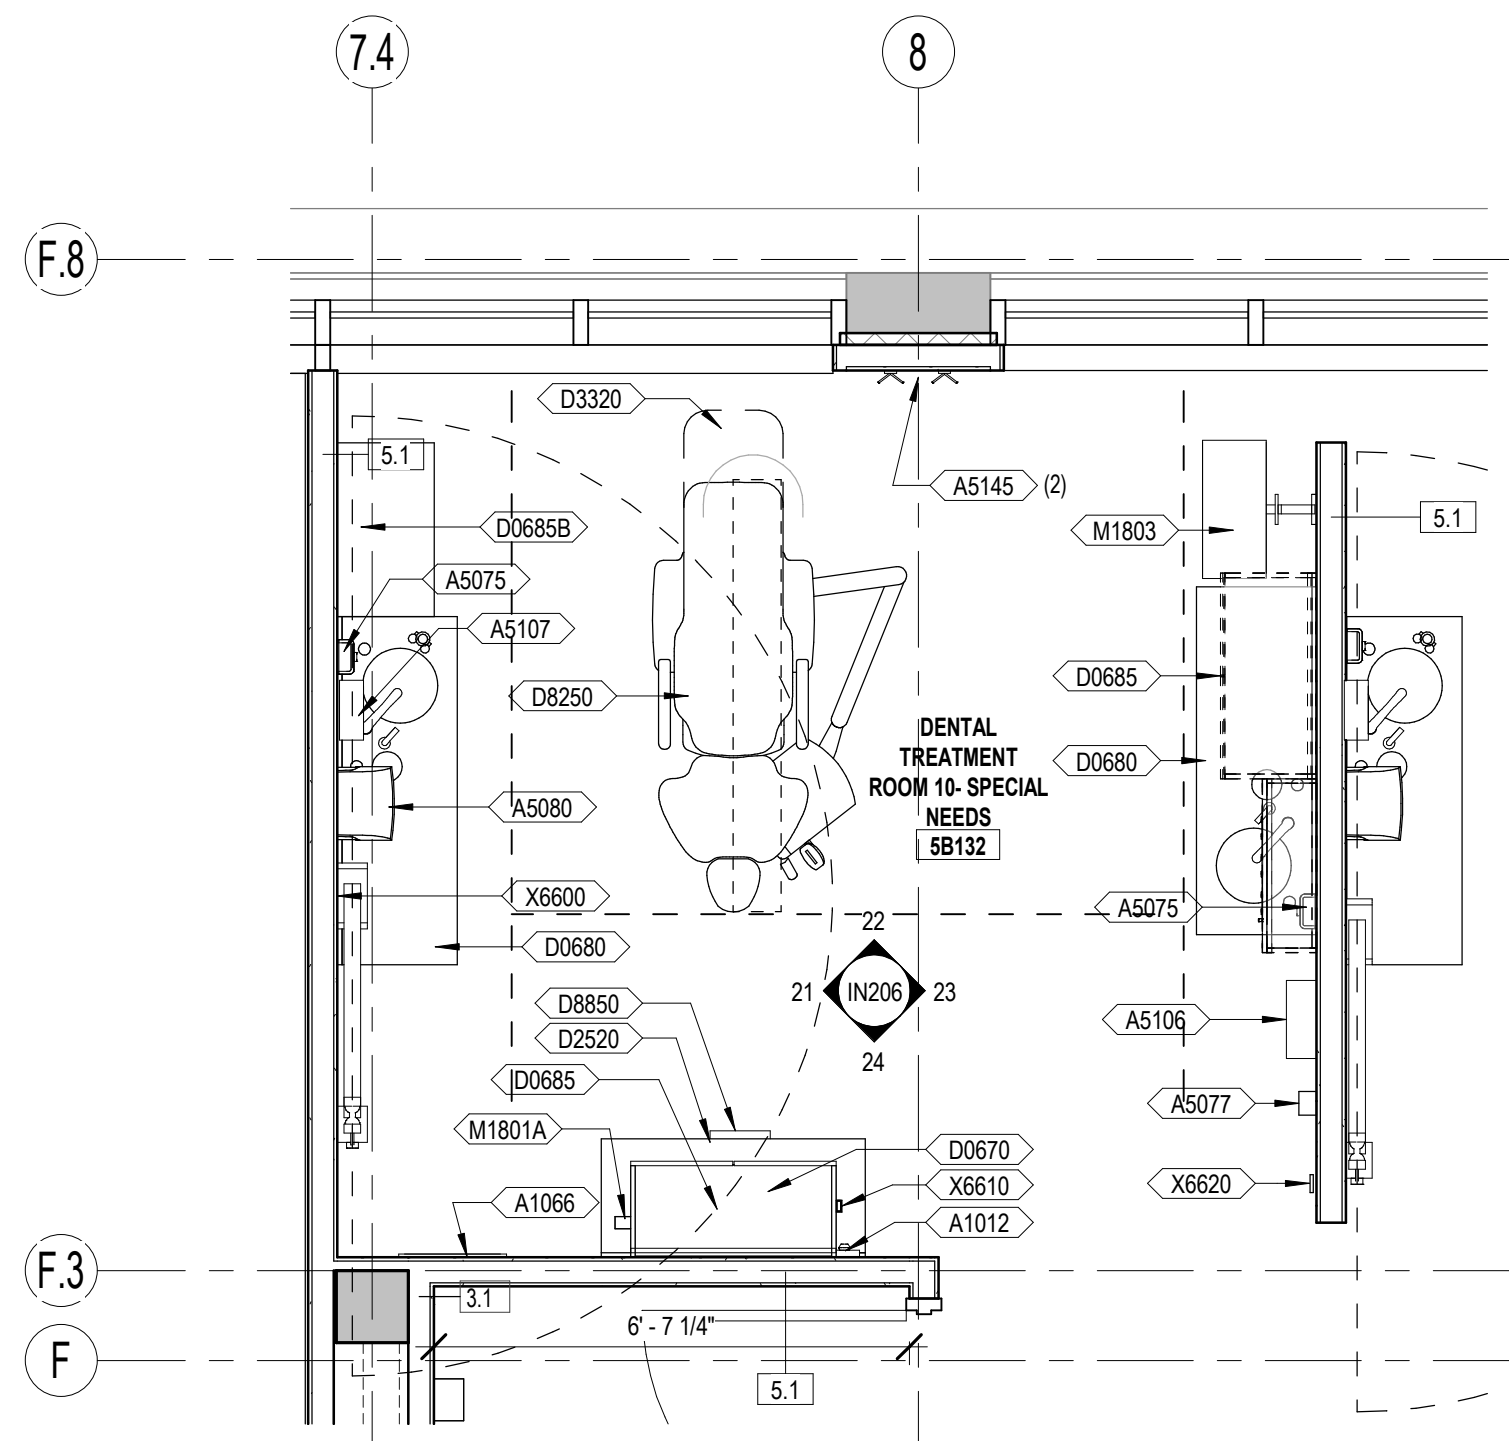


NOTE:
SIM: 5B127

3 DENTAL TREATMENT ROOM 10 - SPECIAL NEEDS

AE124 3/8" = 1'-0"


0 1'-2" 2'-4" 4'-8"

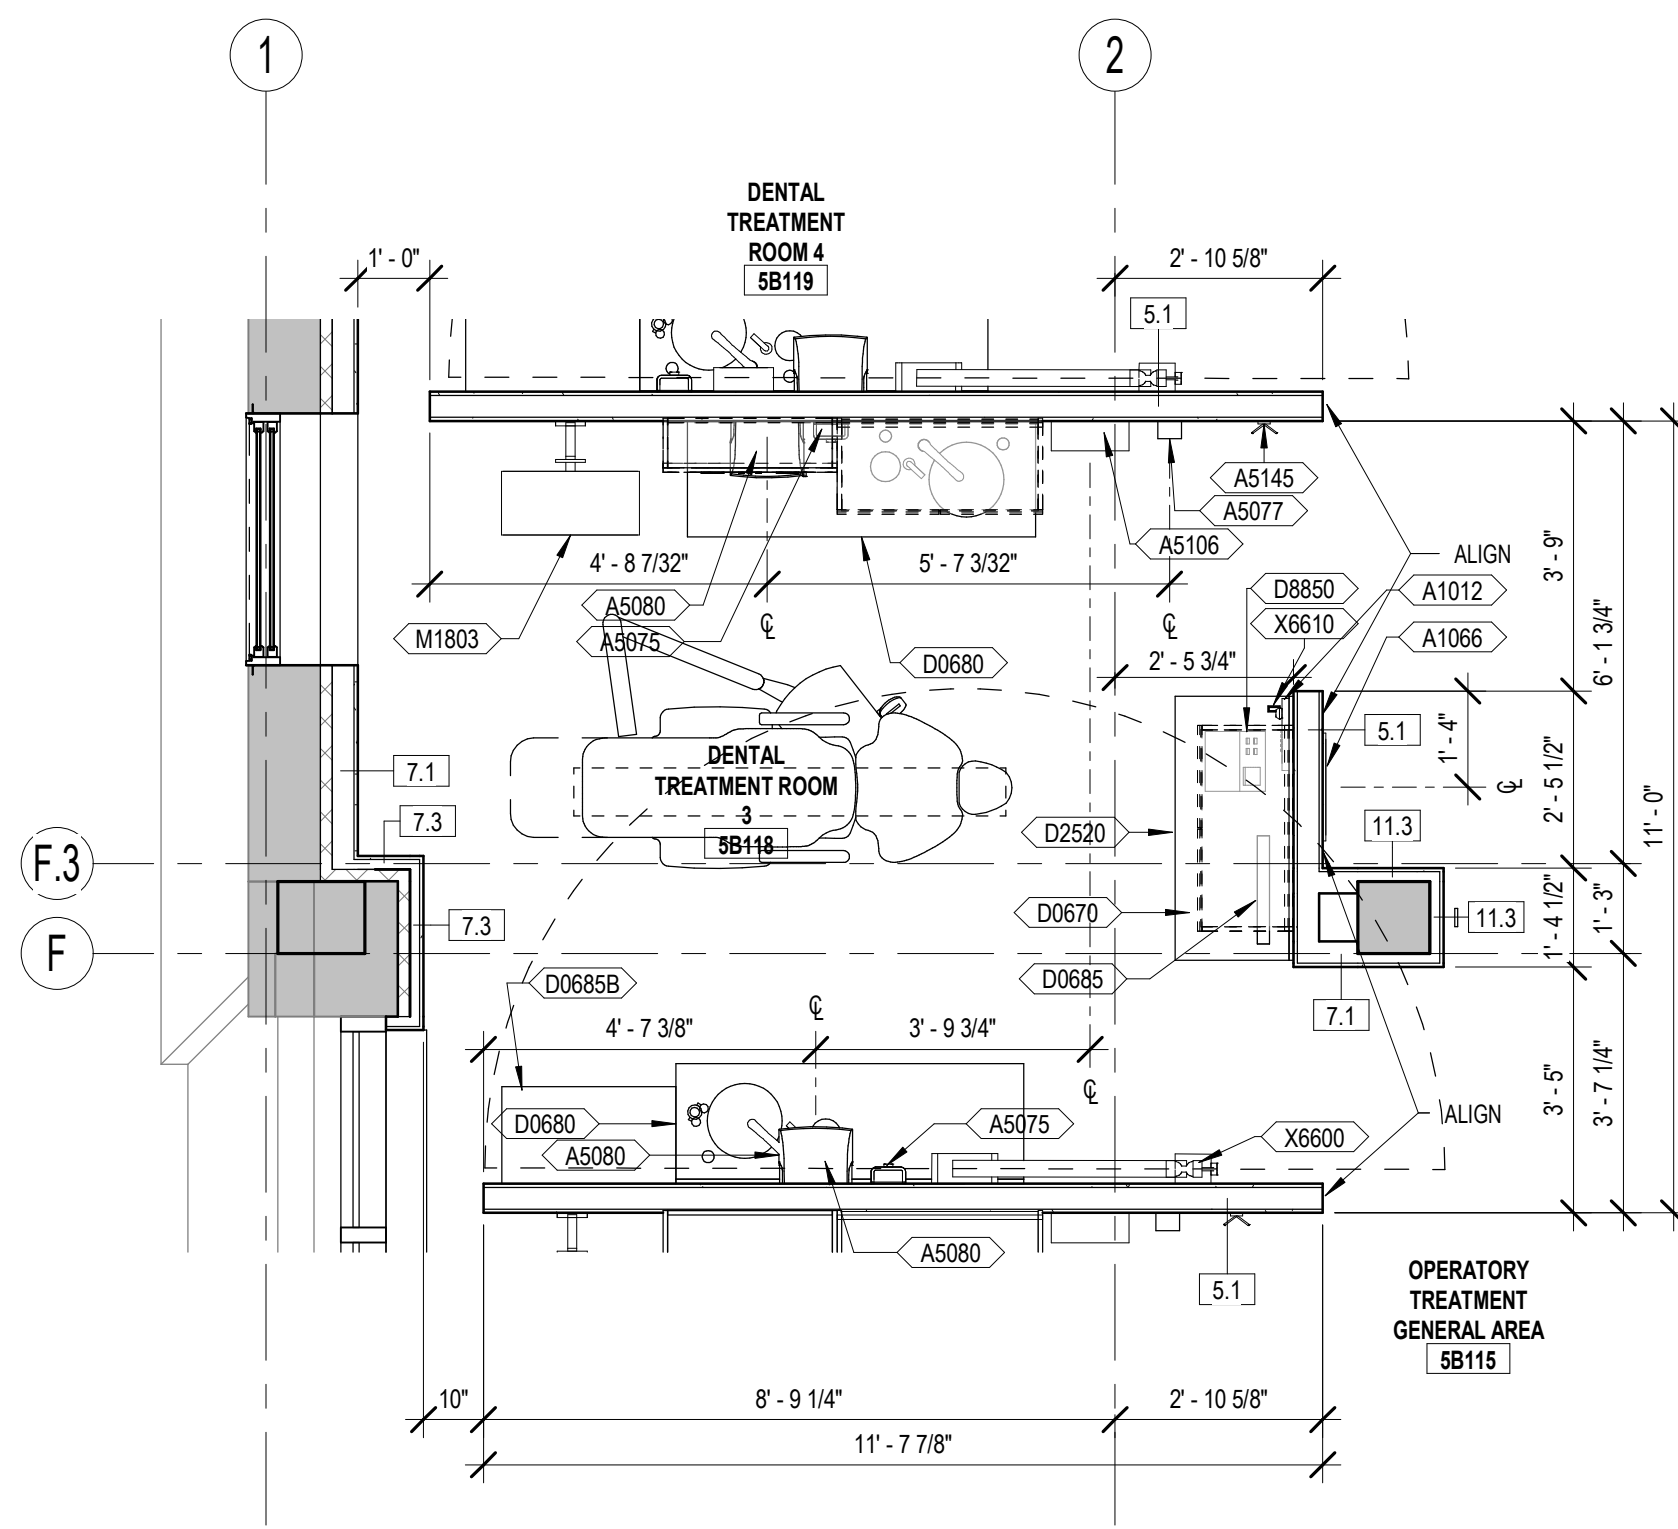

4 DENTAL TREATMENT ROOM 3

AE124 3/8" = 1'-0"

0 1'-2" 2'-4" 4'-8"

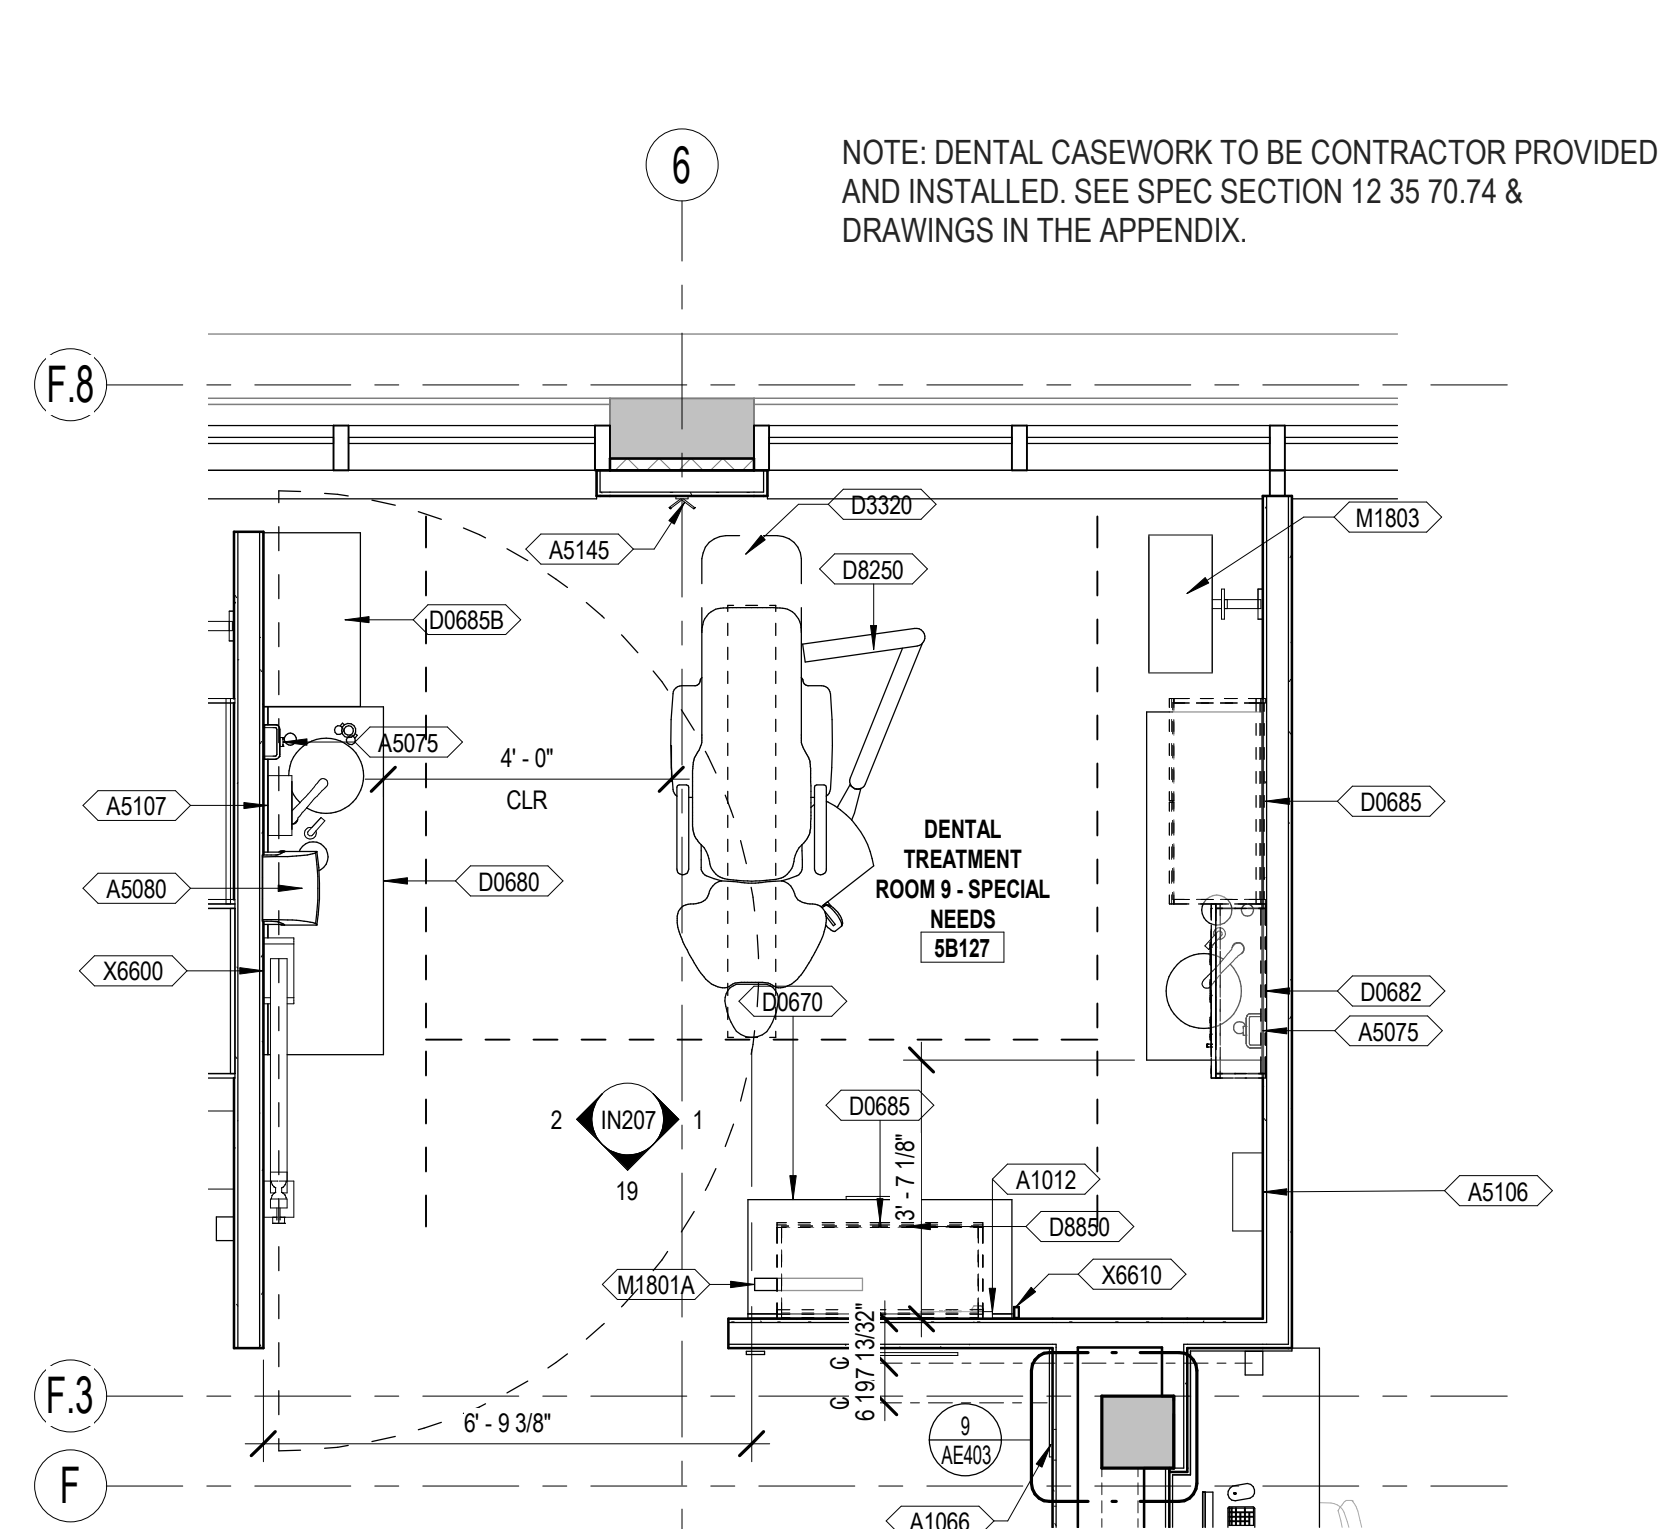

5 DENTAL TREATMENT ROOM 9 - SPECIAL NEEDS

AE124 3/8" = 1'-0"

0 1'-2" 2'-4" 4'-8"

BID DOCUMENTS

NO.	REVISIONS	DATE

CONSULTANT

ARCHITECT/ENGINEER OF RECORD

THOMAS OLESAC, ARCHITECT

MS Lic # 5505

1050 HOYT AVE WEST ST PAUL, MN 55117
952-451-0460

STAMP



Office of
Construction
and Facilities
Management

VA

U.S. Department of
Veterans
Affairs

Drawing Title
ENLARGED FLOOR PLANS

Approved:

Phase
CONSTRUCTION
DOCUMENTS

FULLY SPRINKLERED

Project Title
RENOVATE BUILDING 1

Location
BILOXI, MISSISSIPPI

Issue Date
03/10/2023

Checked
LA

Drawn
CD,PC

Project Number
520-317X

Building Number
1

Drawing Number
AE124

Dwg. 80 of 238

GENERAL REFLECTED CEILING PLAN NOTES

- A. ALL FINISH CEILING HEIGHTS TO BE INSTALLED AT 8'-0" A.F.F. UNLESS OTHERWISE NOTED.
- B. MECHANICAL AND ELECTRICAL DEVICES SHOWN ARE FOR INDICATION OF THEIR RESPECTIVE LOCATION ONLY. NOT ALL SUCH DEVICES ARE SHOWN BY THIS PLAN. MECHANICAL AND ELECTRICAL DEVICES TYPE, SIZE AND OTHER REQUIREMENTS ARE DOCUMENTED BY THE CORRESPONDING M.E.P. PLAN, DETAIL AND/OR SPECIFICATION SECTION.
- C. REFER TO SPECIFICATION SECTION 07 21 13 FOR ACOUSTICAL CEILING BATT INSULATION.
- D. REFER TO SPECIFICATION SECTION 09 29 00 FOR GYPSUM BOARD CEILING SYSTEM.
- E. REFER TO SPECIFICATION SECTION 09 51 00 FOR ACOUSTICAL CEILING SYSTEM.
- F. COORDINATE FIRE PROTECTION SYSTEM TO PROVIDE NEW SPRINKLER HEADS AT THE CENTER POINT OF CEILING TILES SHOWN.
- G. REFER TO PHASING PLAN AND SPECIFICATION SECTION 01 00 00 GENERAL REQUIREMENTS FOR PHASING REQUIREMENTS OF WORK SHOWN.
- H. REFER TO SPECIFICATION SECTION 01 35 26 FOR INFECTION CONTROL REQUIREMENTS FOR WORK SHOWN.
- I. ROOM TAGS REMOVED FOR CLARITY. REFER TO SHEETS AE103 & AE105 FOR ROOM NAMES.


REFLECTED CEILING PLAN NOTES (#)

1. NO NEW CEILING IN THIS AREA.
2. FULL CEILING TILE.
3. SINGLE TRACK BARIATRIC PATIENT LIFT SYSTEM. REFER TO EQUIPMENT LEGEND, SHT. AE305 AND SPECIFICATION SECTION 11 73 00.
4. BOOM LIGHT/MEDICAL GAS ARM. REFER TO MECHANICAL.


REFLECTED CEILING PLAN LEGEND

- 2' X 4' ACOUSTICAL TILE CEILING
- 2' X 2' ACOUSTICAL TILE CEILING
- 2' X 2' FLUORESCENT LIGHT
- 2' X 4' FLUORESCENT LIGHT
- RECESSED CAN LIGHT
- 1' X 4' STRIP LIGHT
- AREA NOT IN CONTRACT
- HVAC RETURN
- HVAC SUPPLY
- EXHAUST
- CURTAIN TRACK
- SHOWER CURTAIN
- GYPSUM BOARD CEILING ON METAL FRAMING
- RADIANT HEAT PANEL

NOTE: ALL SYMBOLS MAY NOT BE USED

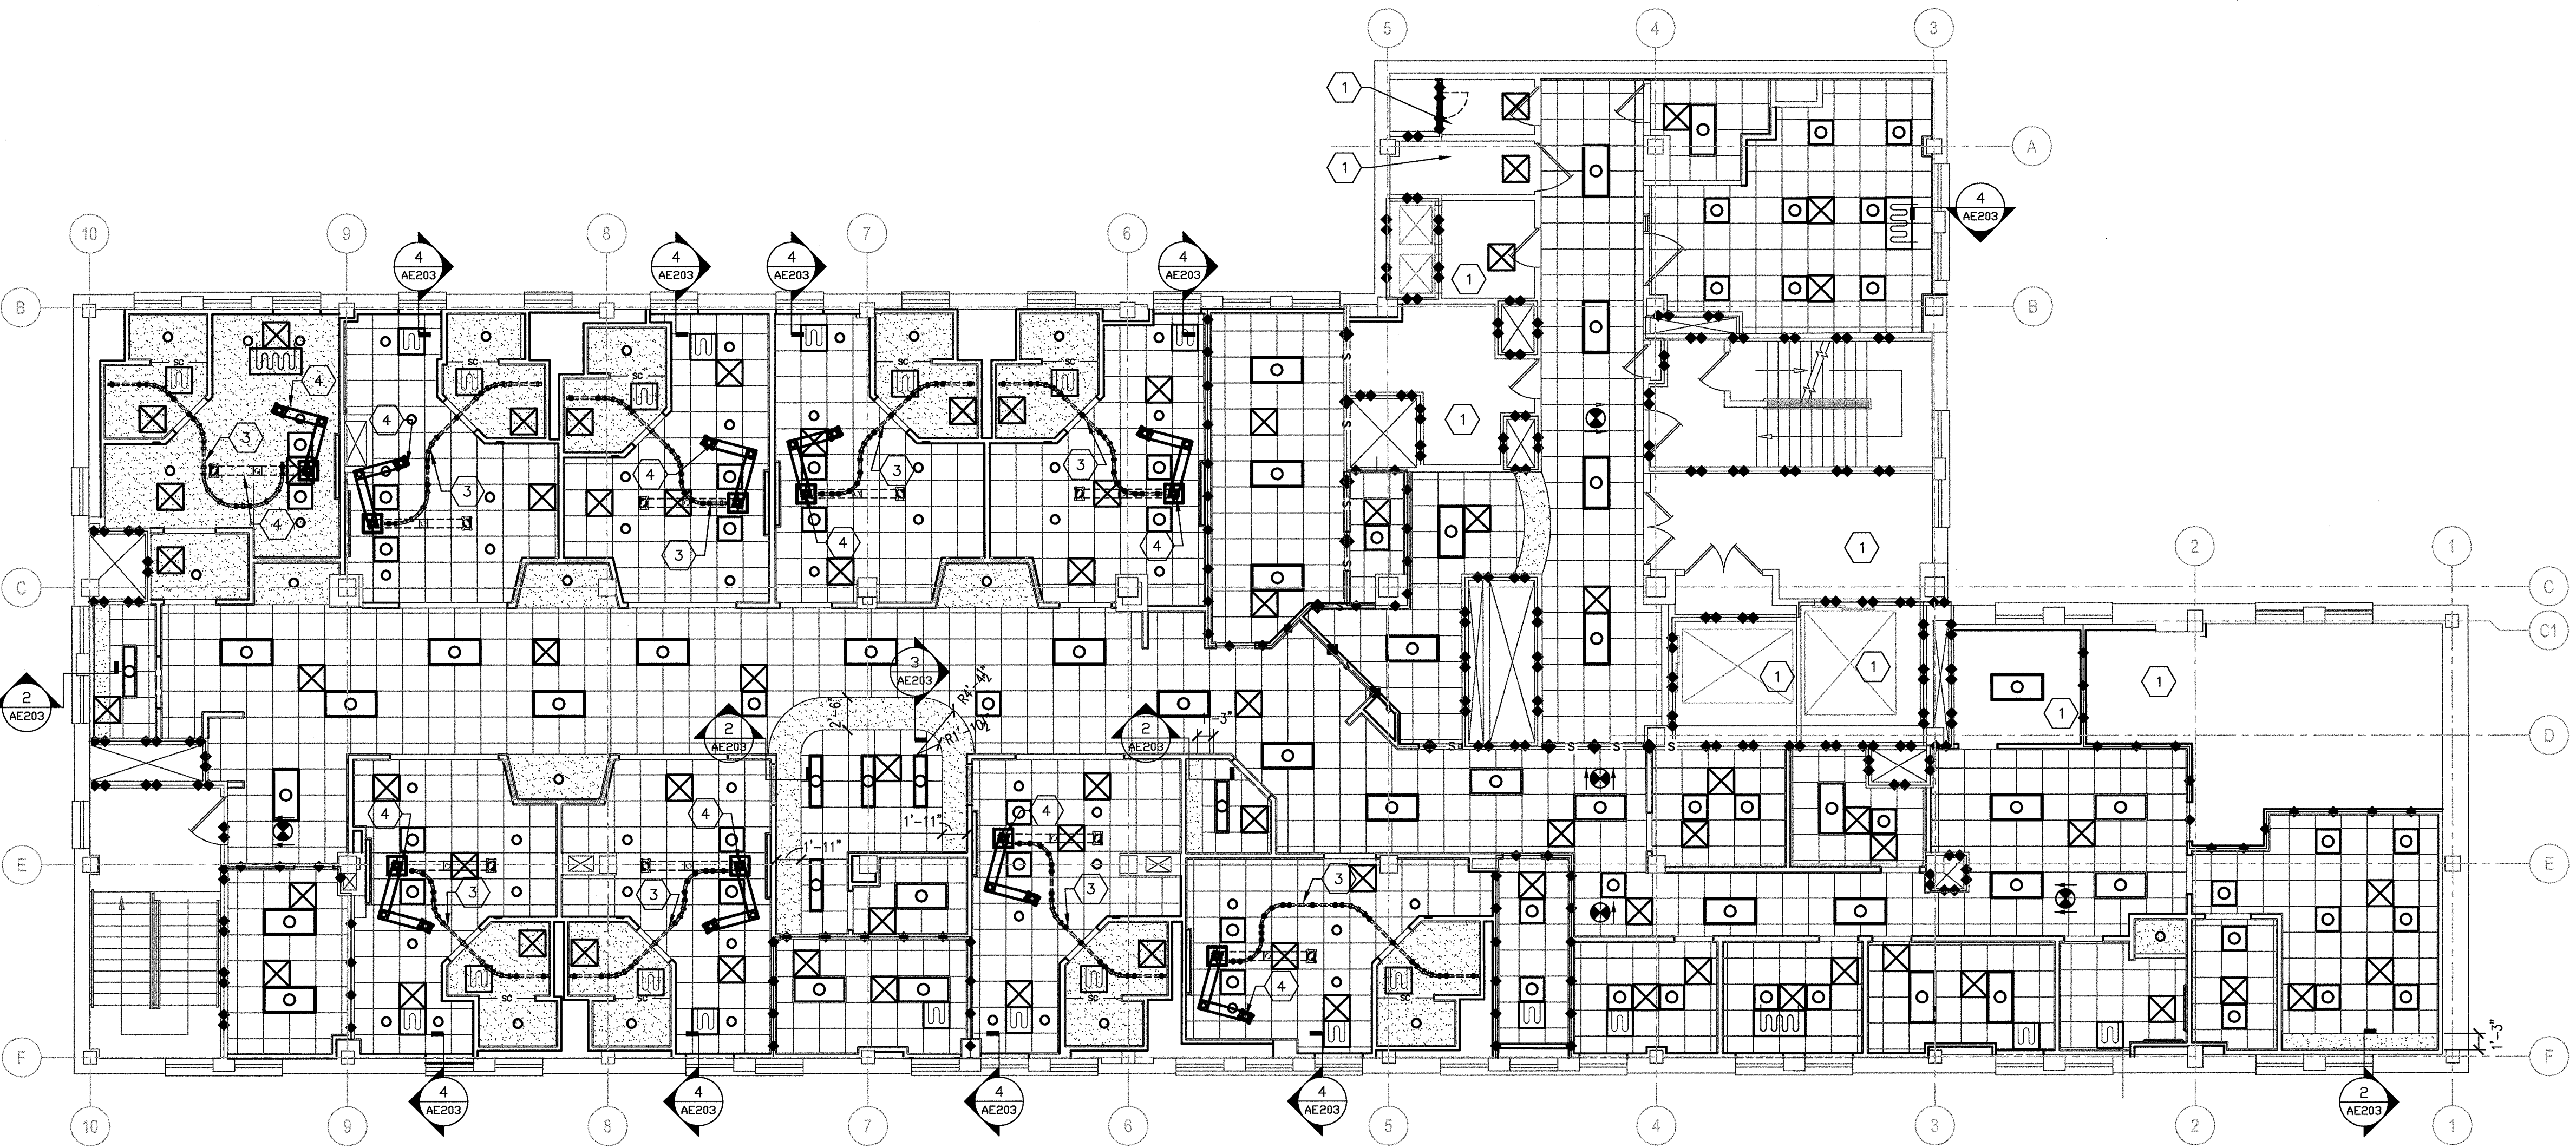


F1 FIFTH FLOOR REFLECTED CEILING PLAN
SCALE 1/8" = 1'-0"

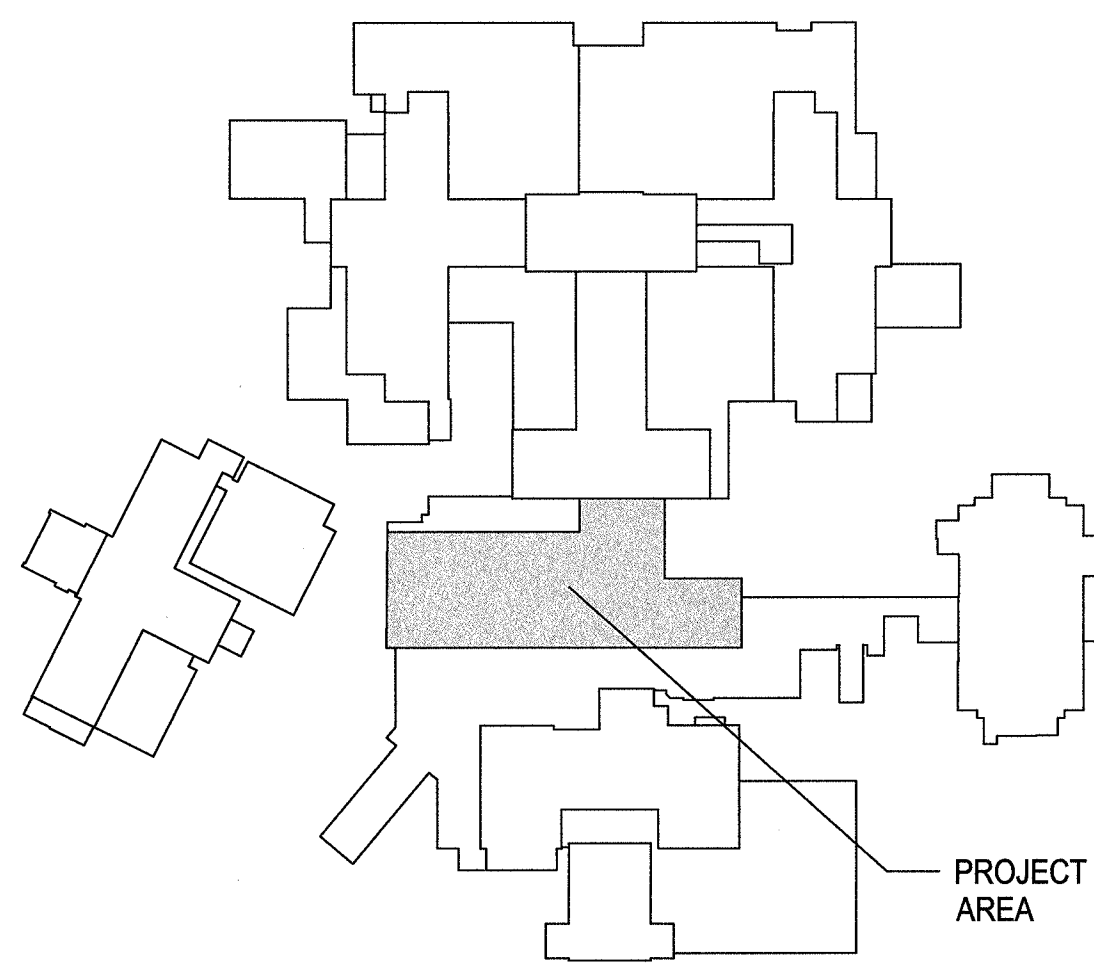

KEY PLAN - FIFTH FLOOR
NTS

FULLY SPRINKLED

--	--	

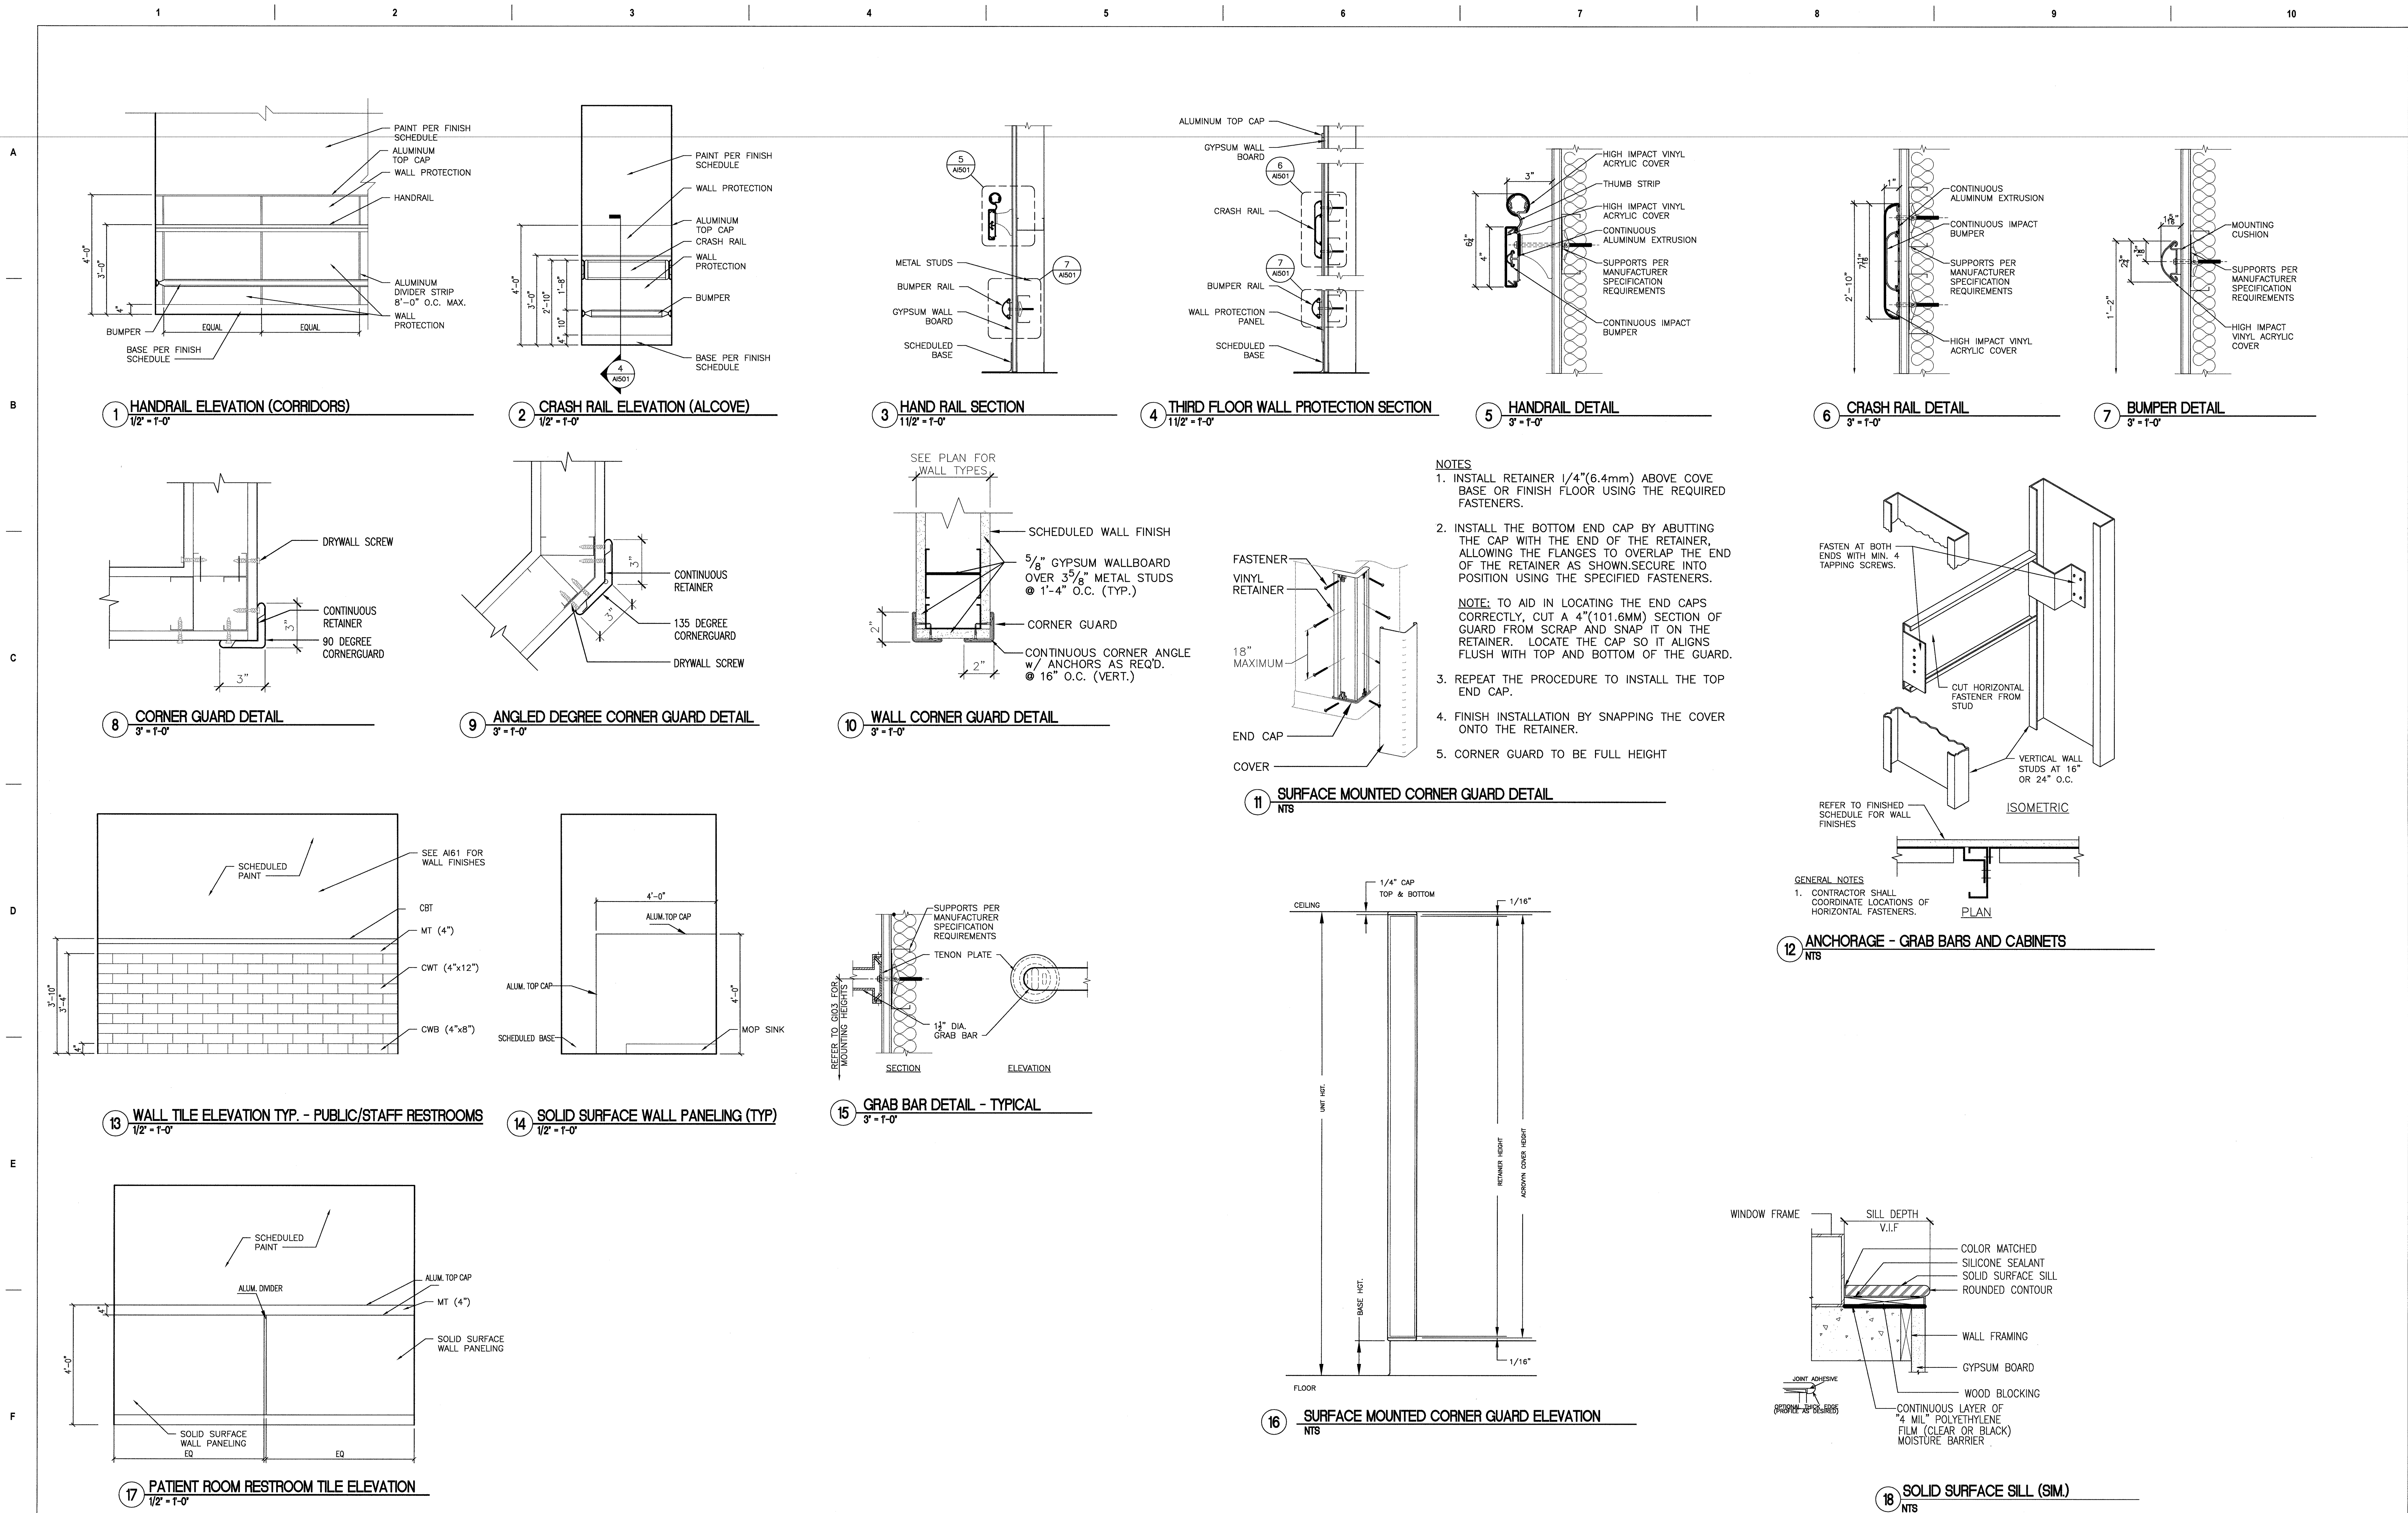




U.S. Department
of Veterans Affairs

Class 1 Radiology Imaging Room, Imgng Svcs (CI011)


ELEVATIONS

SKETCH TITLE

SCALE: 1/4" = 1'-0"

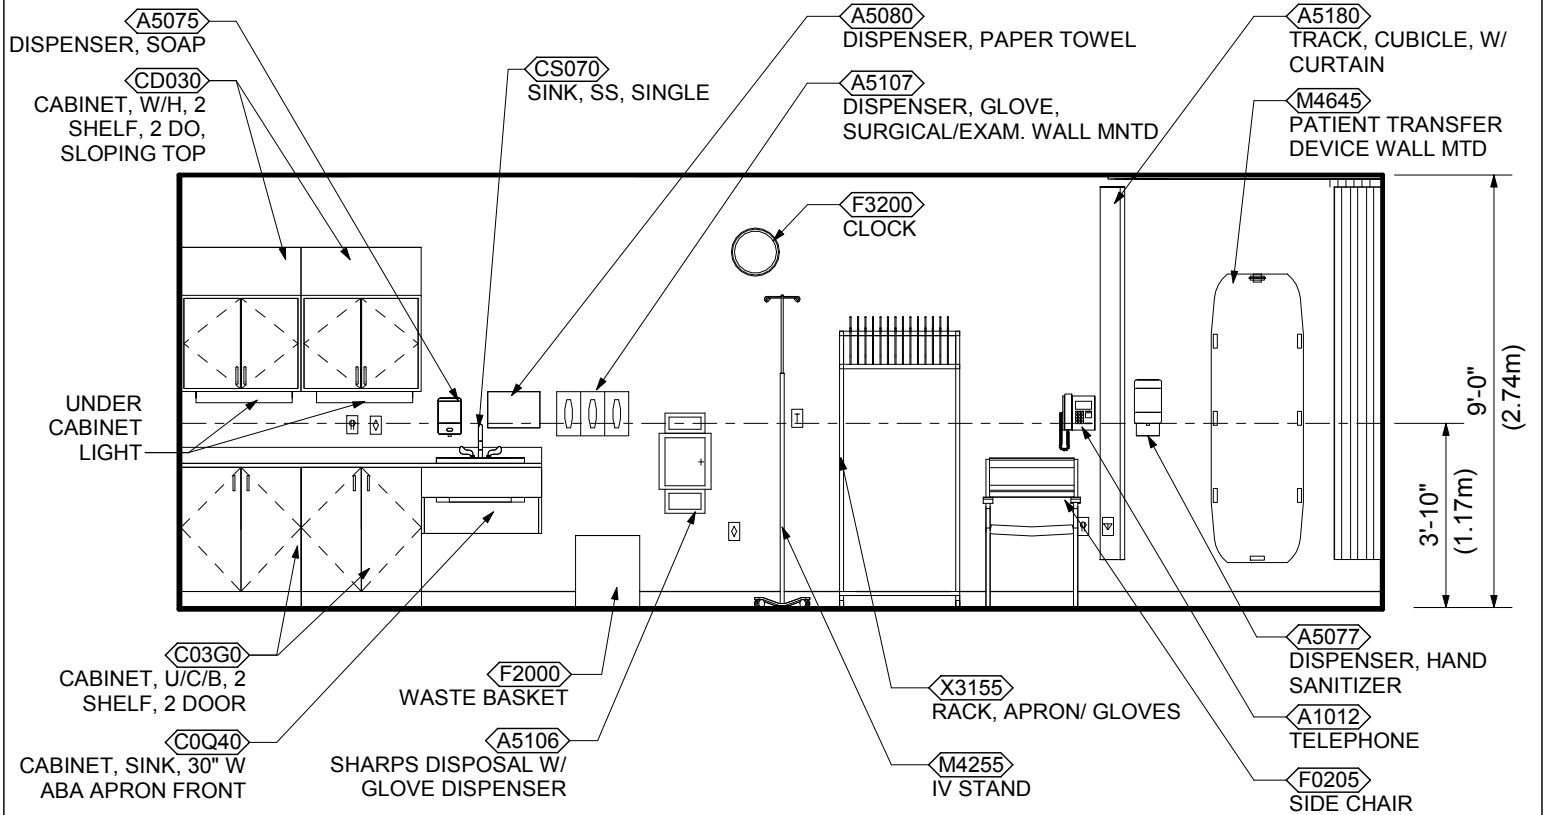


ELEVATION 1

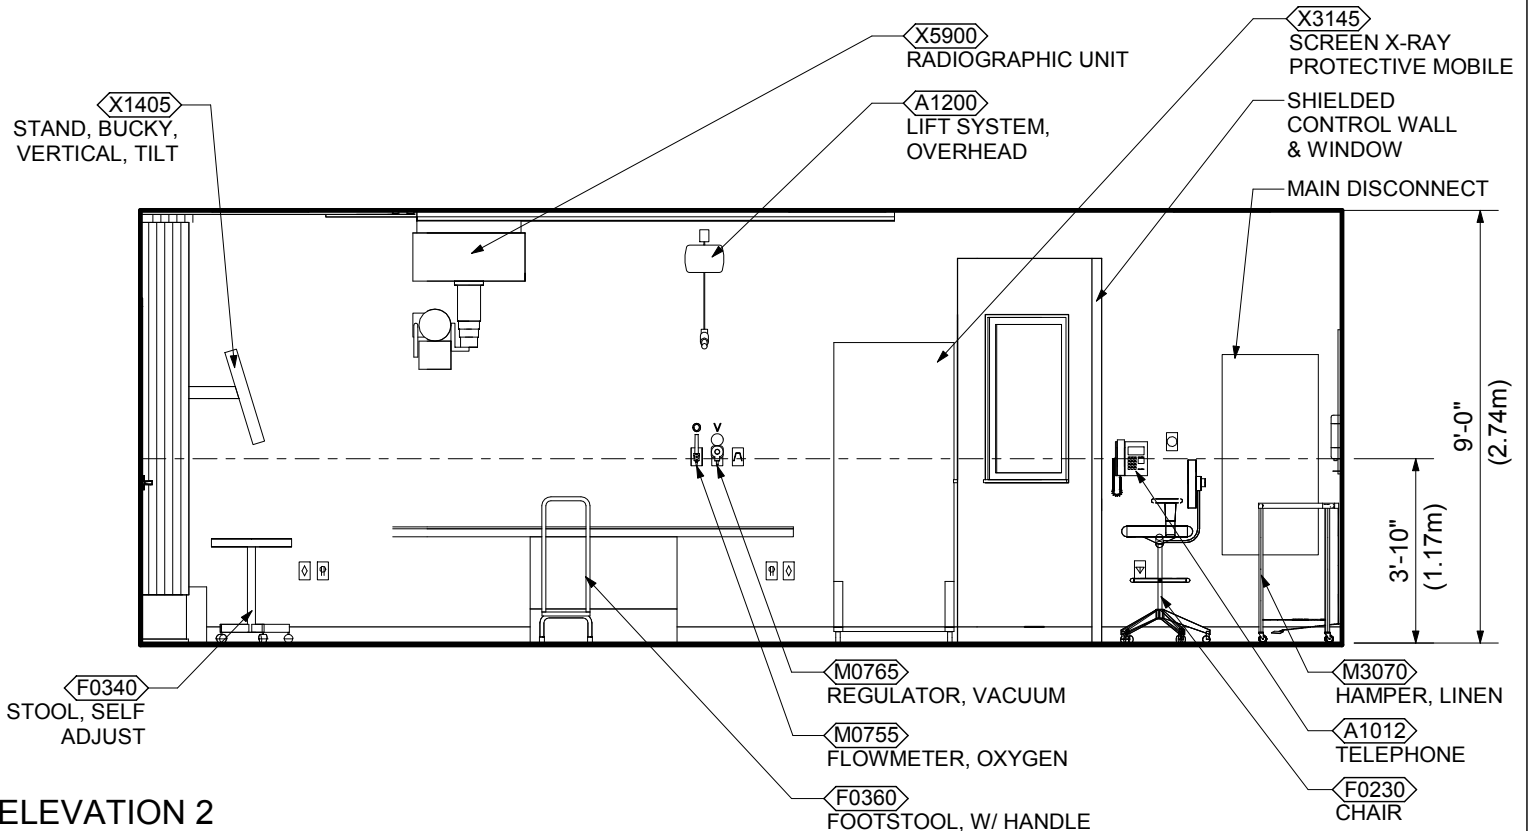


ELEVATION 2


DISCLAIMER: ROOM TEMPLATES ARE GRAPHICAL REPRESENTATIONS OF SELECTED ROOM TYPES THAT ILLUSTRATE VA PLANNING REQUIREMENTS FOR SPACE, ROOM CONTENTS, AND ROOM SPECIFIC ENGINEERING SYSTEMS. THEY PROVIDE TYPICAL CONFIGURATIONS, PLANNING CRITERIA, AND GENERAL TECHNICAL GUIDANCE, AND ARE NOT INTENDED TO BE PROJECT SPECIFIC REQUIREMENTS.

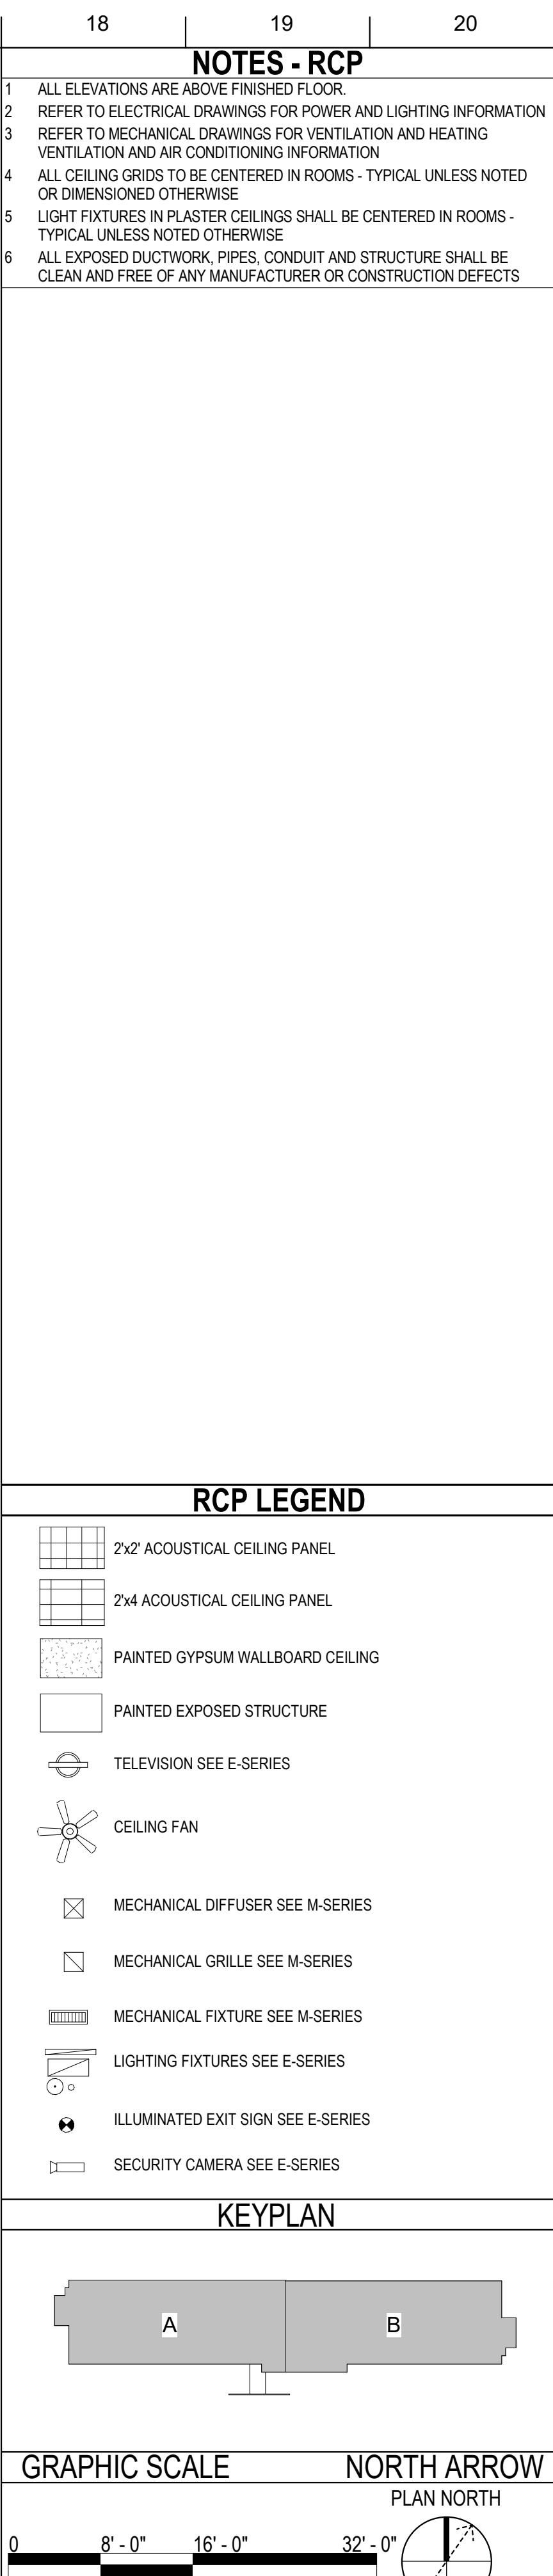


% FINAL DESIGN SUBMITTAL Plot Date: 3/23/2024 12:10:33 PM File Path: Autocad Docs\198175-BIM\03_Dorm Reno - B2019-02-262\1\PTF1221019-30019-A.rvt

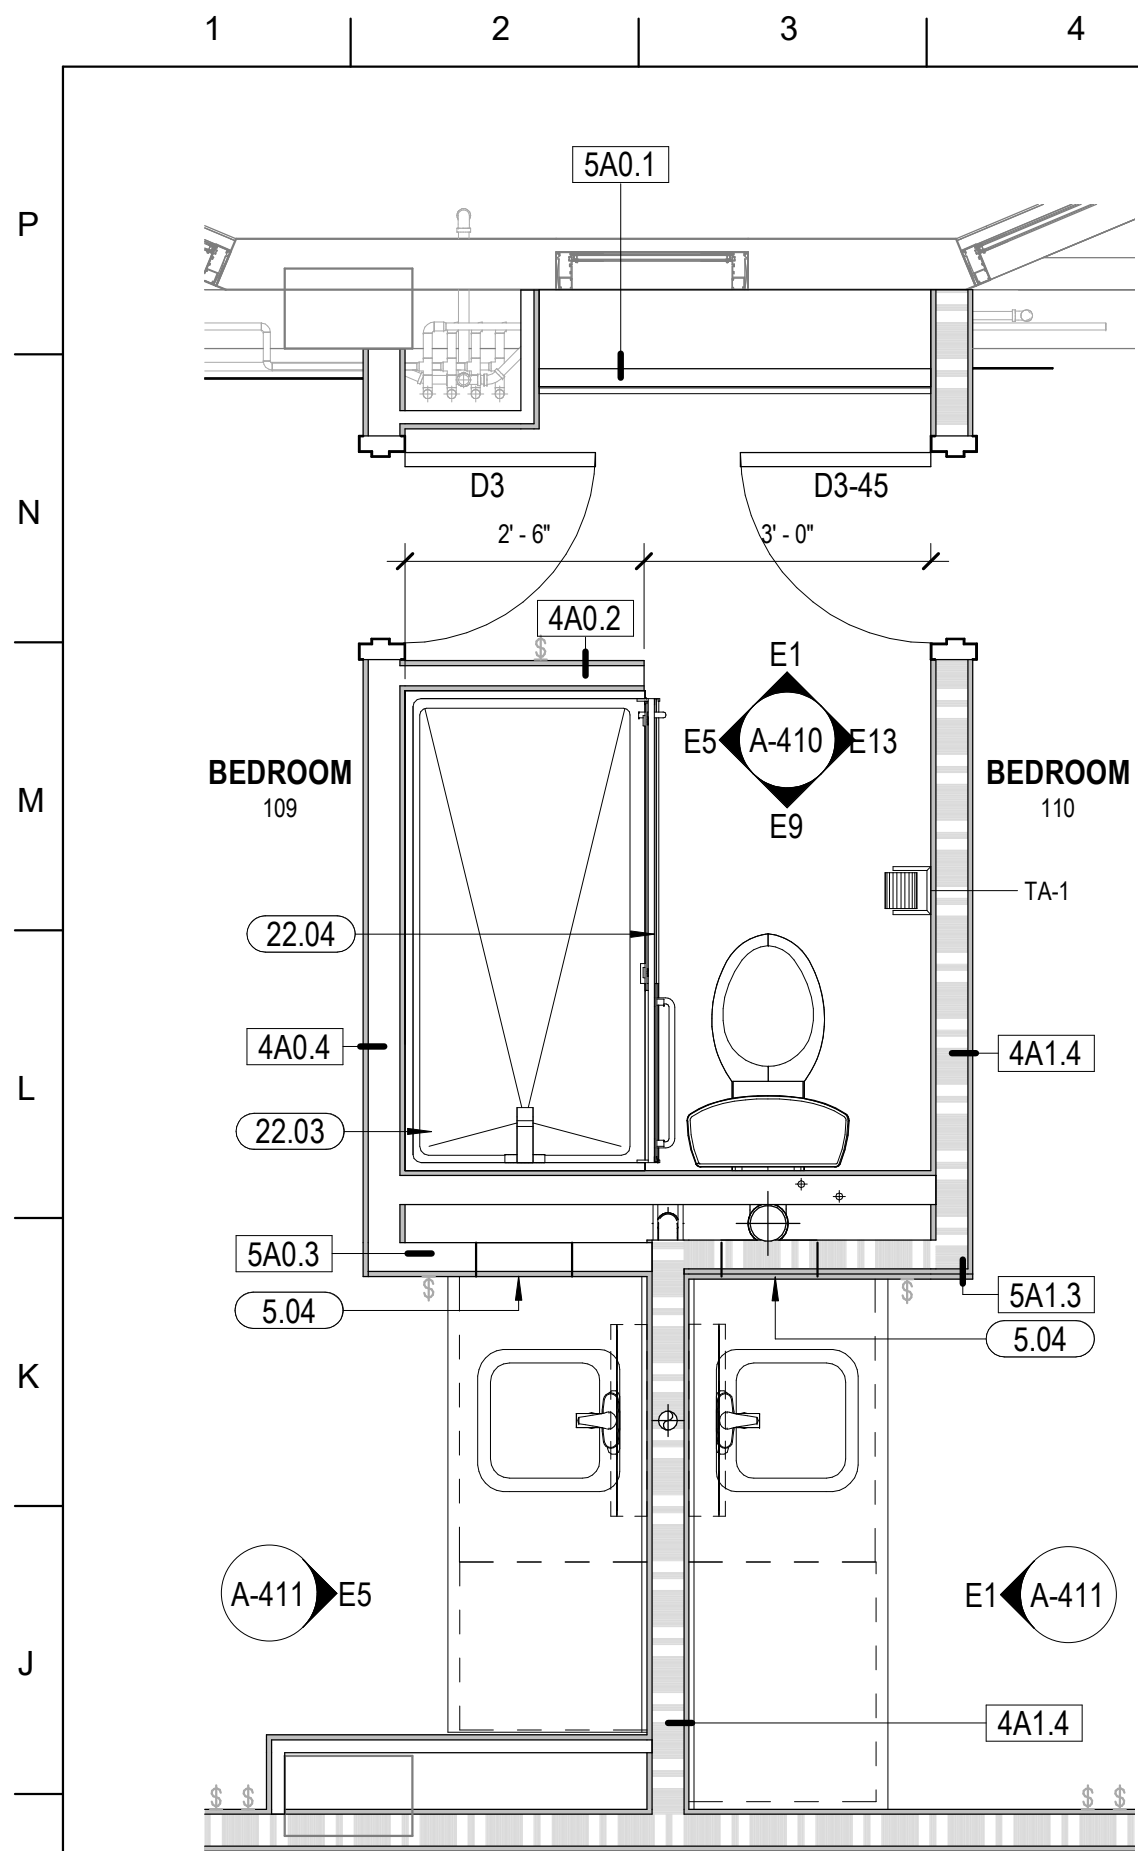


G1 BATHROOM - 1ST FL - TYP
1/2" = 1'-0"

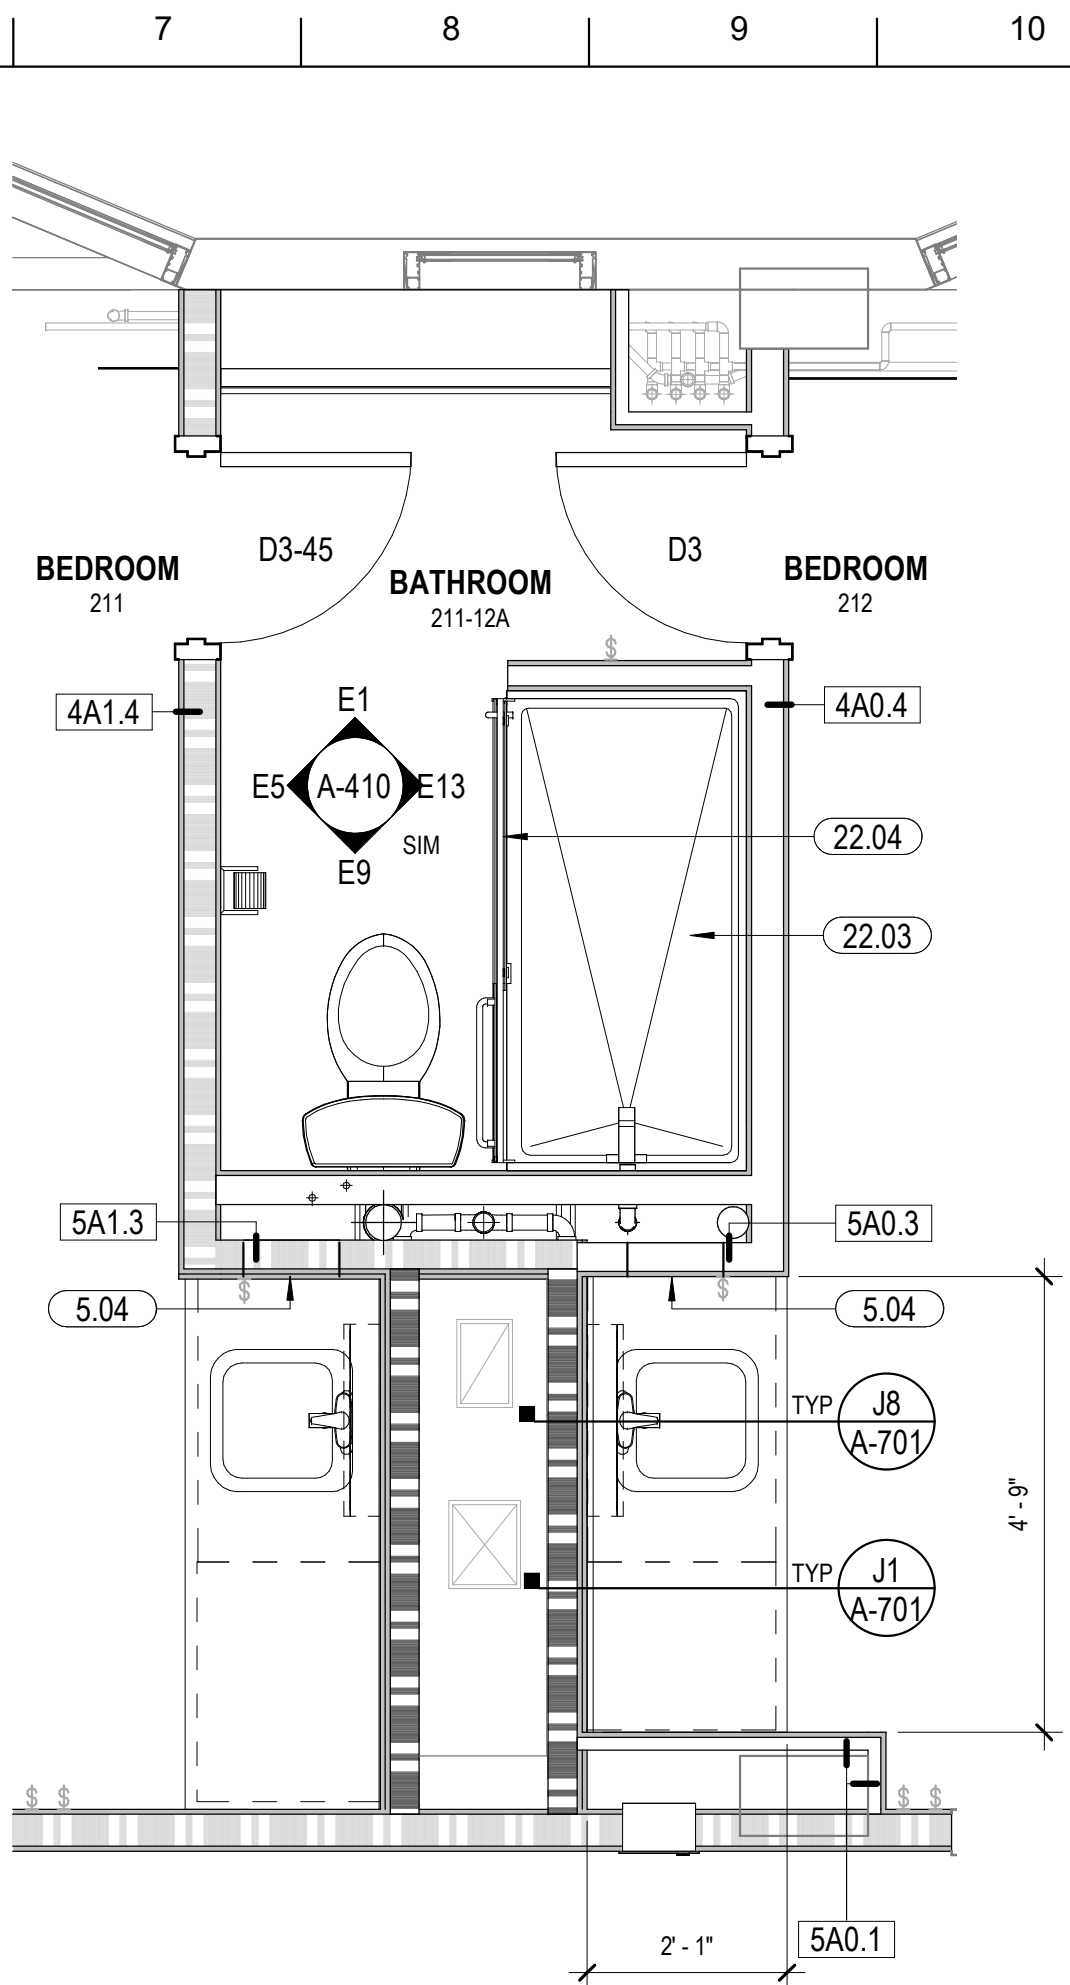


G7 BATHROOM - 2ND/3RD FL - TYP
1/2" = 1'-0"

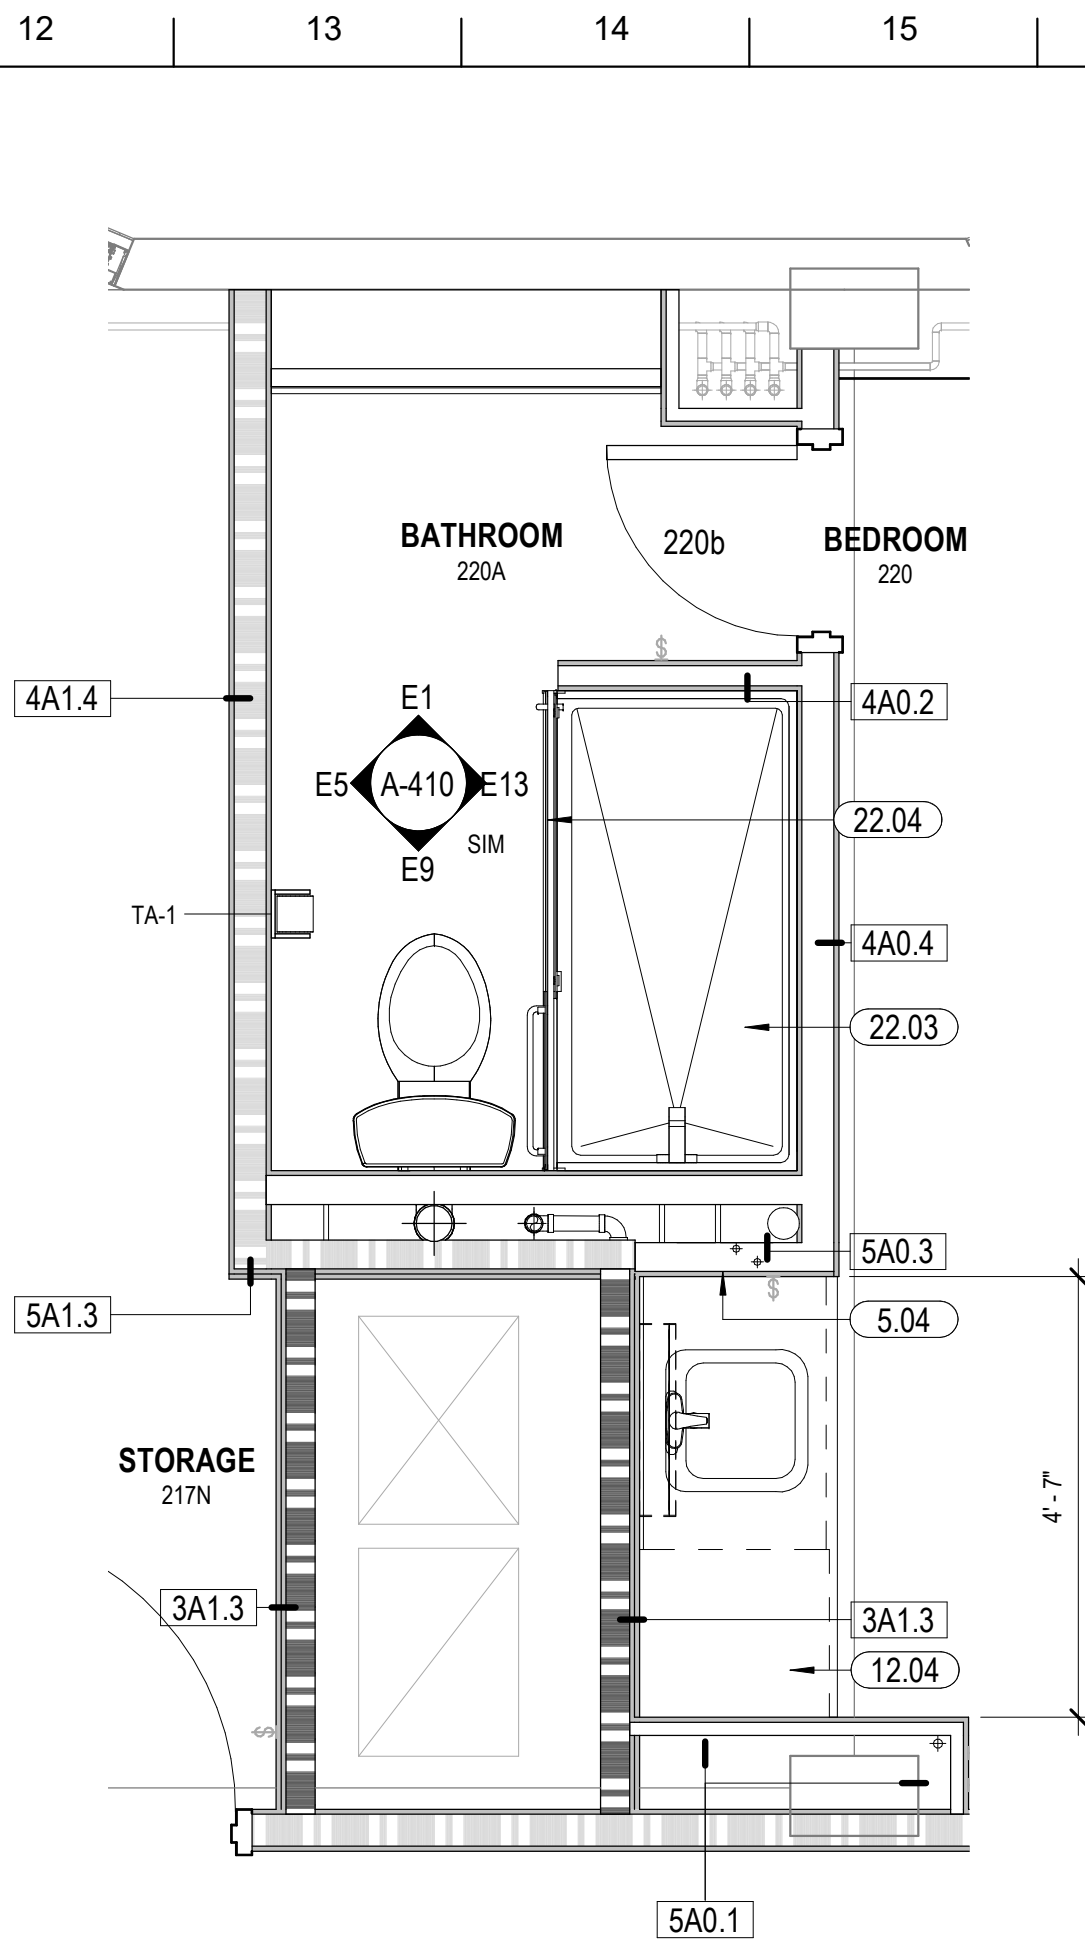


G12 BATHROOM - 2ND/3RD FL - RM 220A, 320A
1/2" = 1'-0"

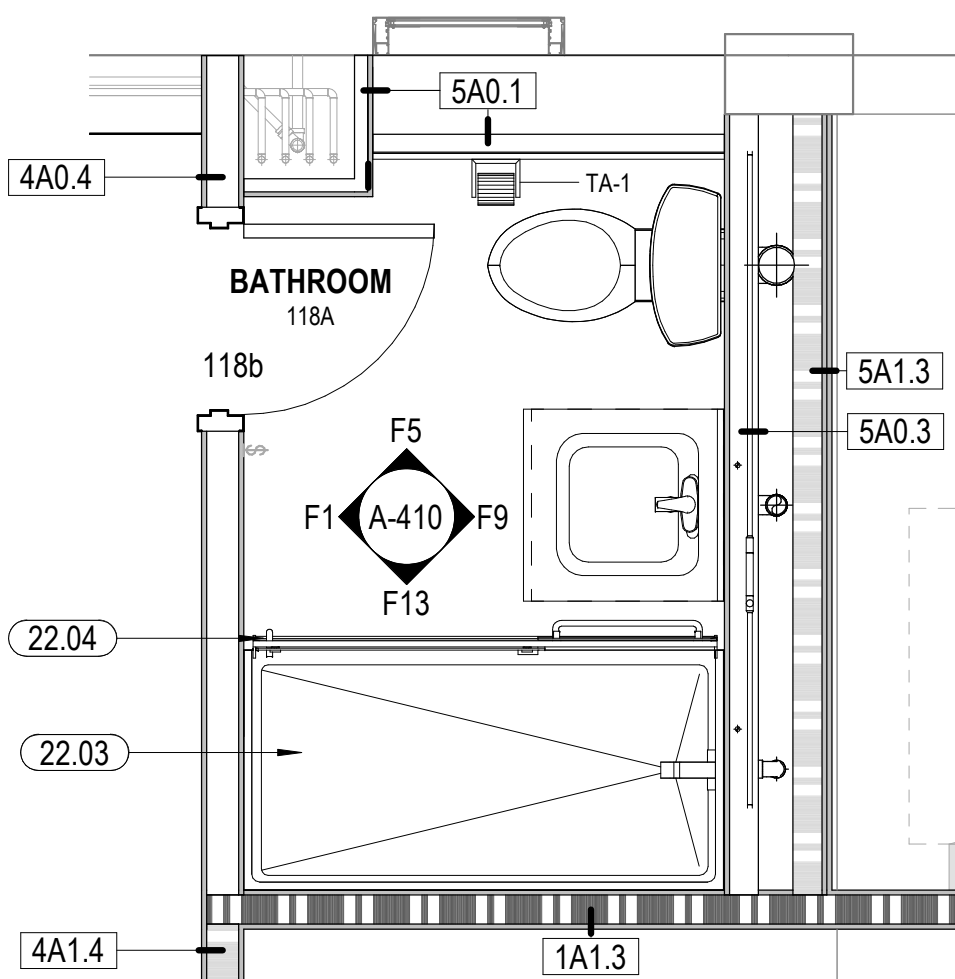

A1 BATHROOM - 1ST/2ND/3RD FL - RM 118A, 218A, 318A
1/2" = 1'-0"

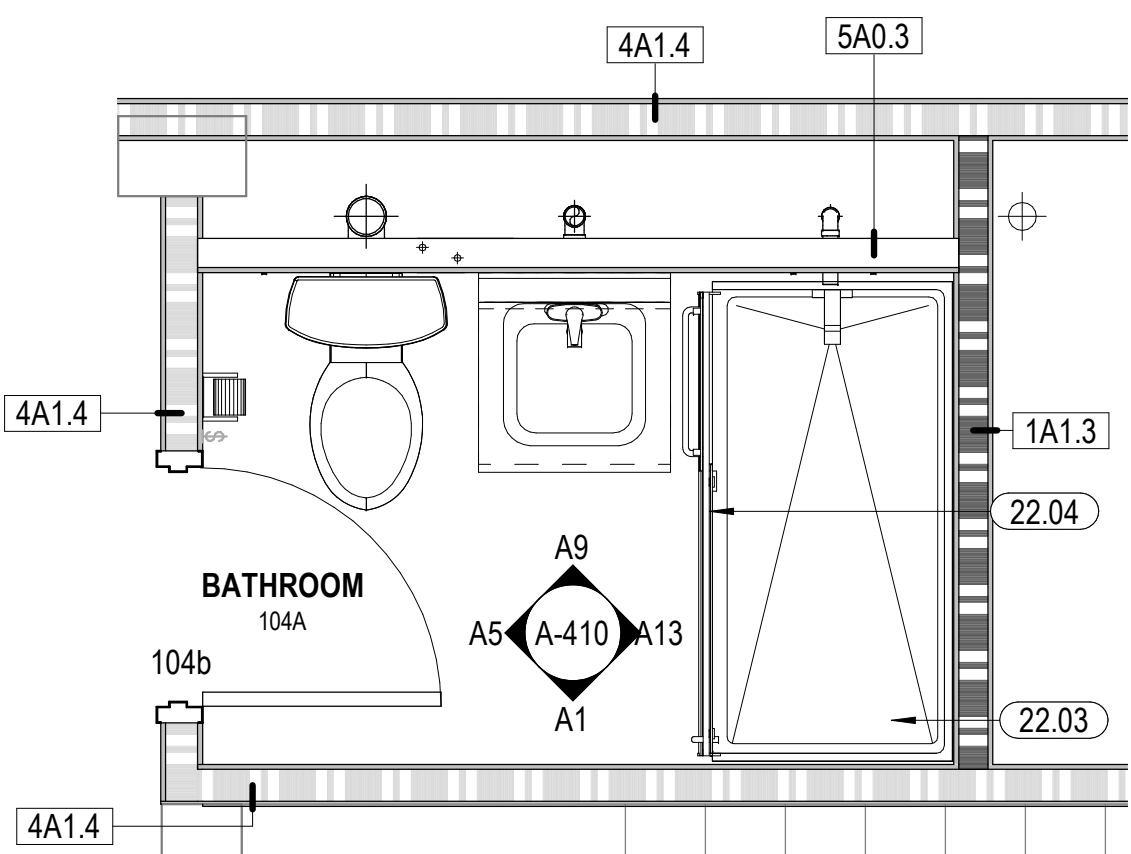

A7 BATHROOM - 1ST/2ND/3RD FL - RM 104A, 204A, 304A
1/2" = 1'-0"

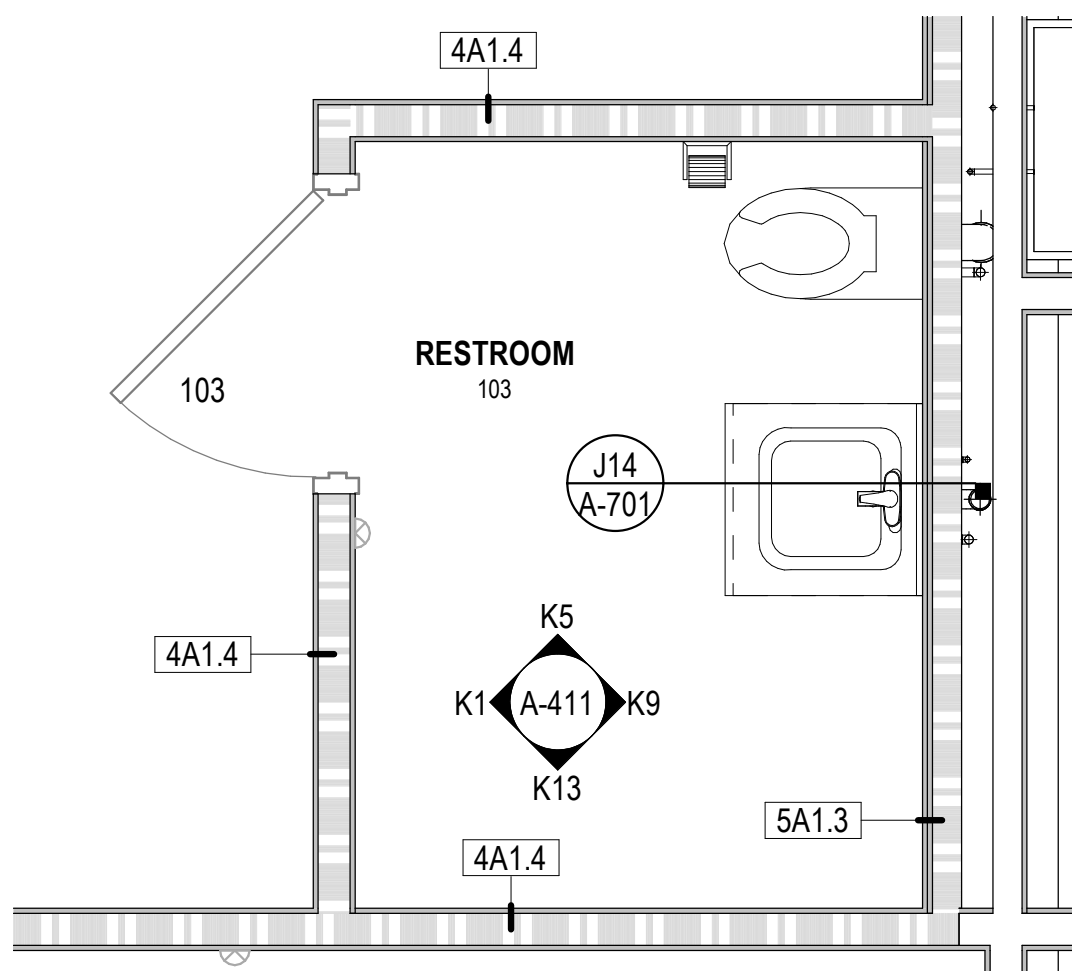

A12 BATHROOM - 1ST FL - RM 103
1/2" = 1'-0"

GENERAL NOTES - ENLARGED PLANS


SHEET KEYNOTES

5.04	1" X 1" PLUMBING ACCESS PANELS IN BASE CABINET - FIRE/NRC RATINGS AS APPLICABLE. SEE PLUMBING SERIES
12.04	SOLID SURFACE COUNTER, SEE INTERIORS
22.03	NEW DROP-IN ACRYLIC SHOWER ENCLOSURE, SEE PLUMBING
22.04	NEW TEMPERED SLIDING GLASS SHOWER DOOR

TOILET ACCESSORIES

TA-1	SURFACE MOUNTED SINGLE ROLL TOILET TISSUE DISPENSER
TA-2	DOOR MOUNTED ROBE HOOK
TA-4	SURFACE MOUNTED CHANNEL FRAME MIRROR
TA-6	SURFACE MOUNTED MEDICINE CABINET WITH MIRROR

GRAPHIC SCALE

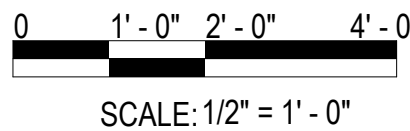

MARK	DESCRIPTION	DATE



ISSUE DATE: 22 MARCH 2024	DESIGNED BY: C. COPPOLA	US AIR FORCE CIVIL ENGINEER CENTER MC GUIRE AFB LAKEHURST, NEW JERSEY
SOLICITATION NO.: PTCL 22-1019	DRAWN BY: C. COPPOLA	BAKER-STANLEY-CARDNO JOINT VENTURE McGuire Air Force Base Lakehurst, NJ 08041
CONTRACT NO.: FA8903-21-D-0004	CHECKED BY: C. FRANCES	BAKER-STANLEY-CARDNO JOINT VENTURE McGuire Air Force Base Lakehurst, NJ 08041
	SUBMITTED BY: BSC-JV	BAKER-STANLEY-CARDNO JOINT VENTURE McGuire Air Force Base Lakehurst, NJ 08041
	SIZE: ANSI D	BAKER-STANLEY-CARDNO JOINT VENTURE McGuire Air Force Base Lakehurst, NJ 08041

MC GUIRE AFB, NEW JERSEY
RENOVATION OF DORMITORY BUILDING 2619
ENLARGED BATHROOM PLANS

SHEET ID
A-401

