




three inches = one foot
one and one half inches = one foot
one inch = one foot
three quarters inch = one foot
one half inch = one foot
three eighths inch = one foot
one quarter inch = one foot
one eighth inch = one foot
one eighth inch = one foot

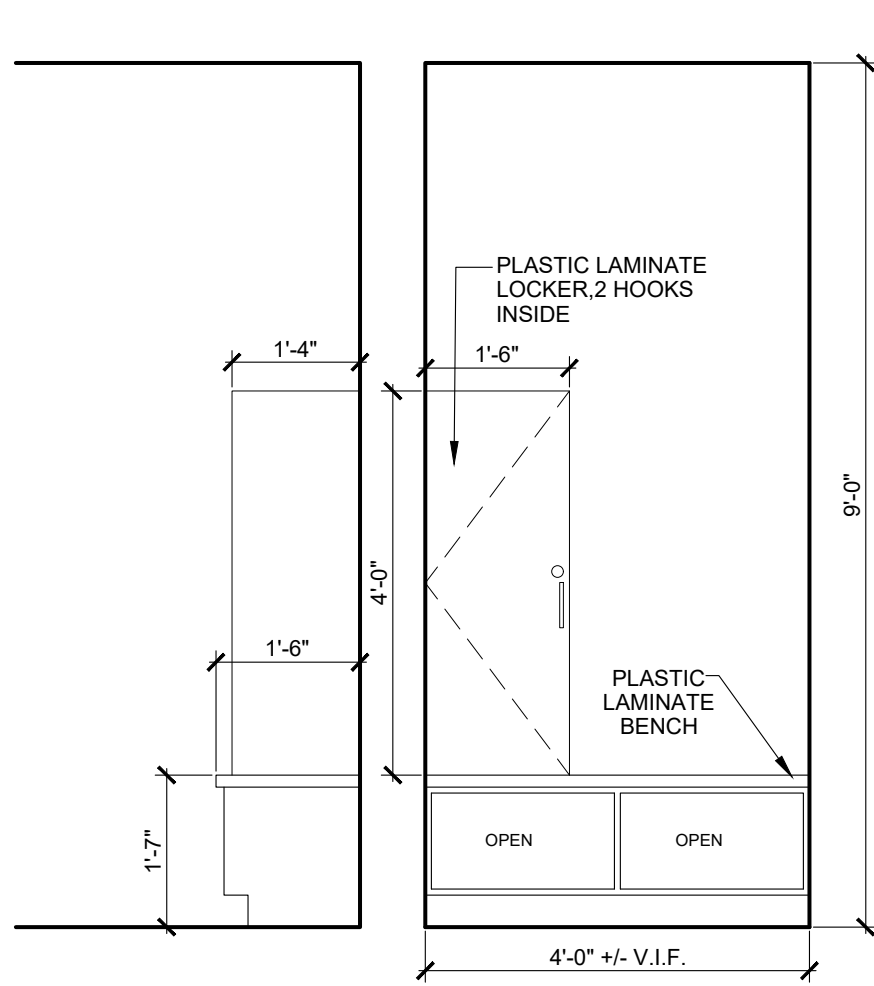


1 DRESS 101 ELEVATION
SCALE: 1/2" = 1'-0"

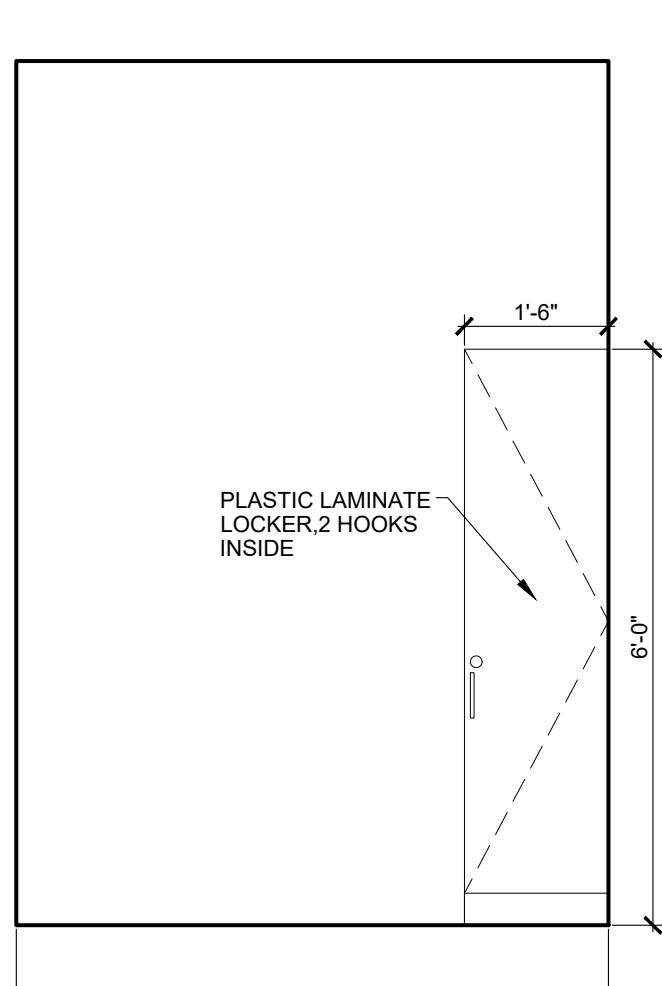


2 DRESS 102 ELEVATION
SCALE: 1/2" = 1'-0"

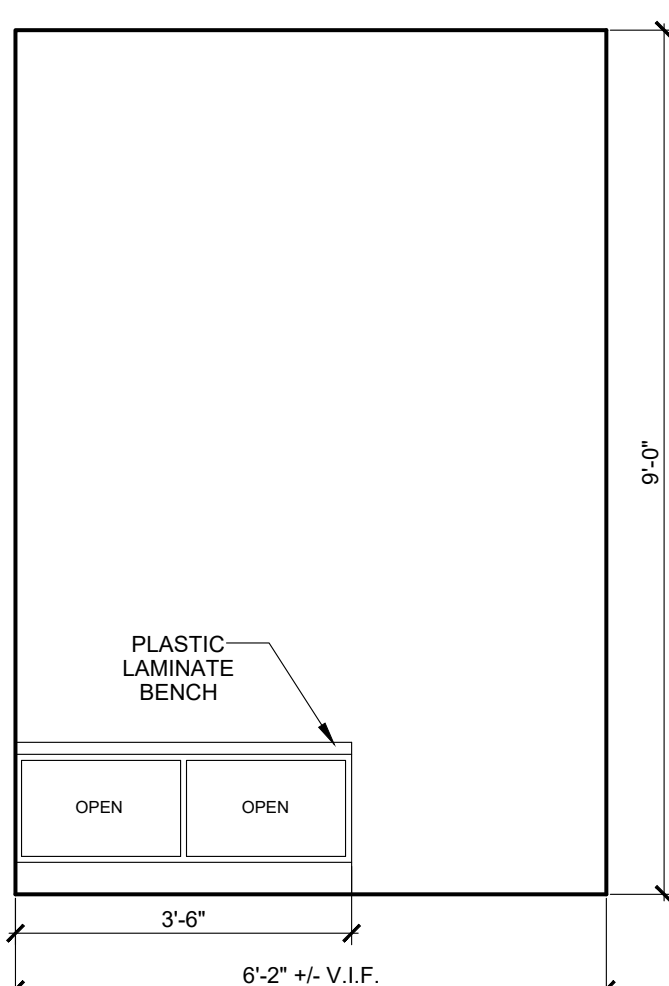


3 DRESS 102 ELEVATION
SCALE: 1/2" = 1'-0"

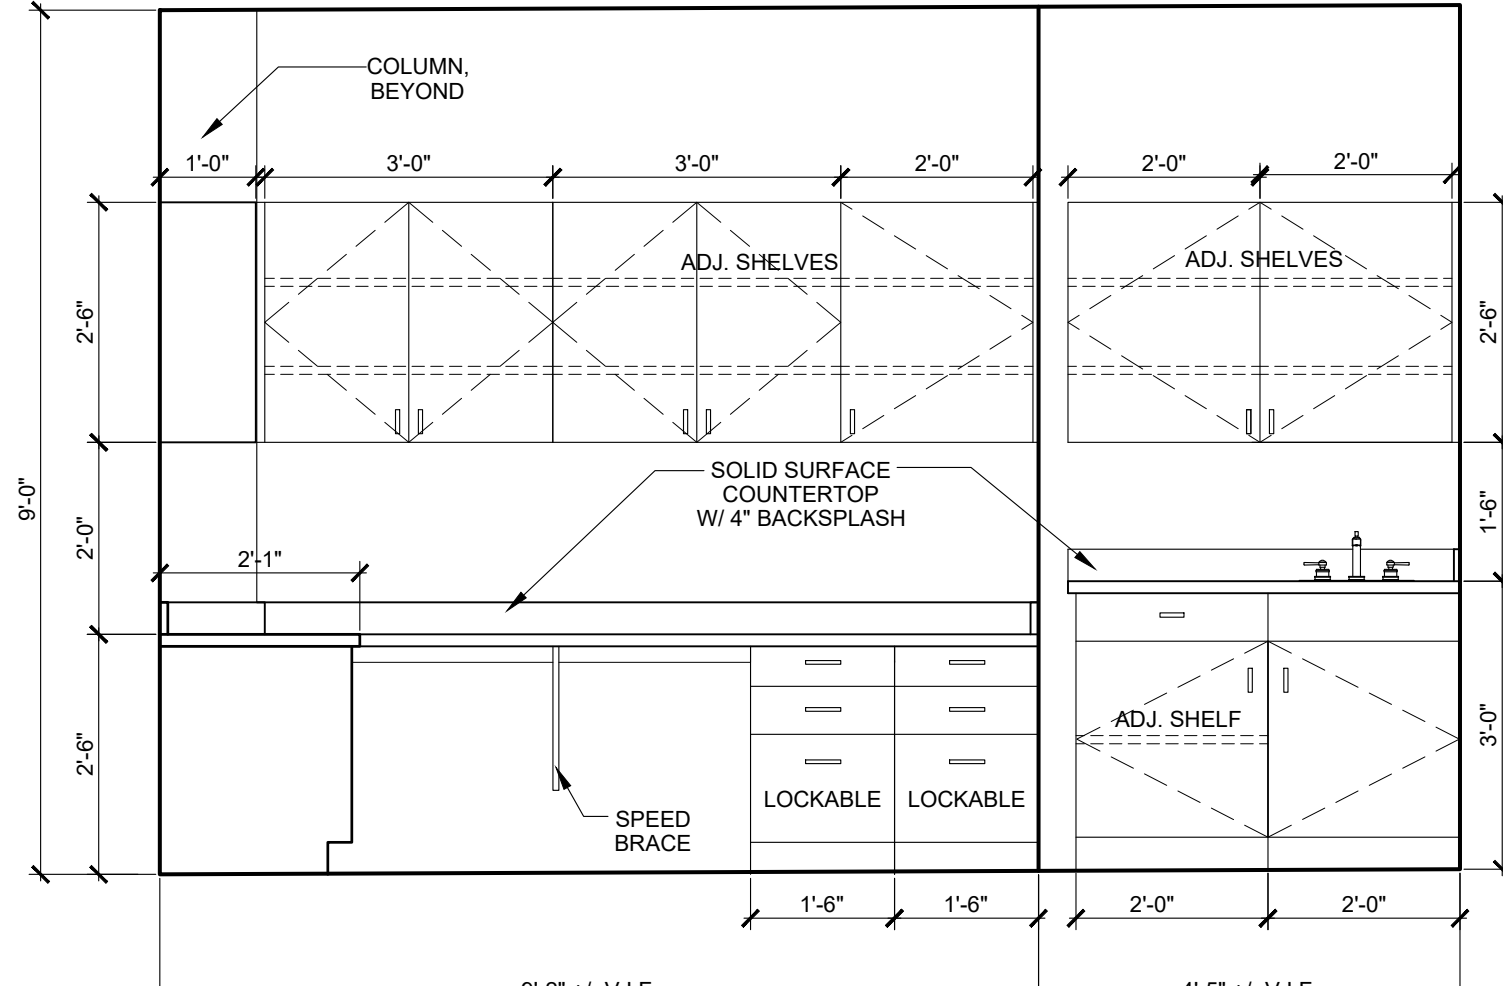


4 CONTROL ROOM 105
SCALE: 1/2" = 1'-0"

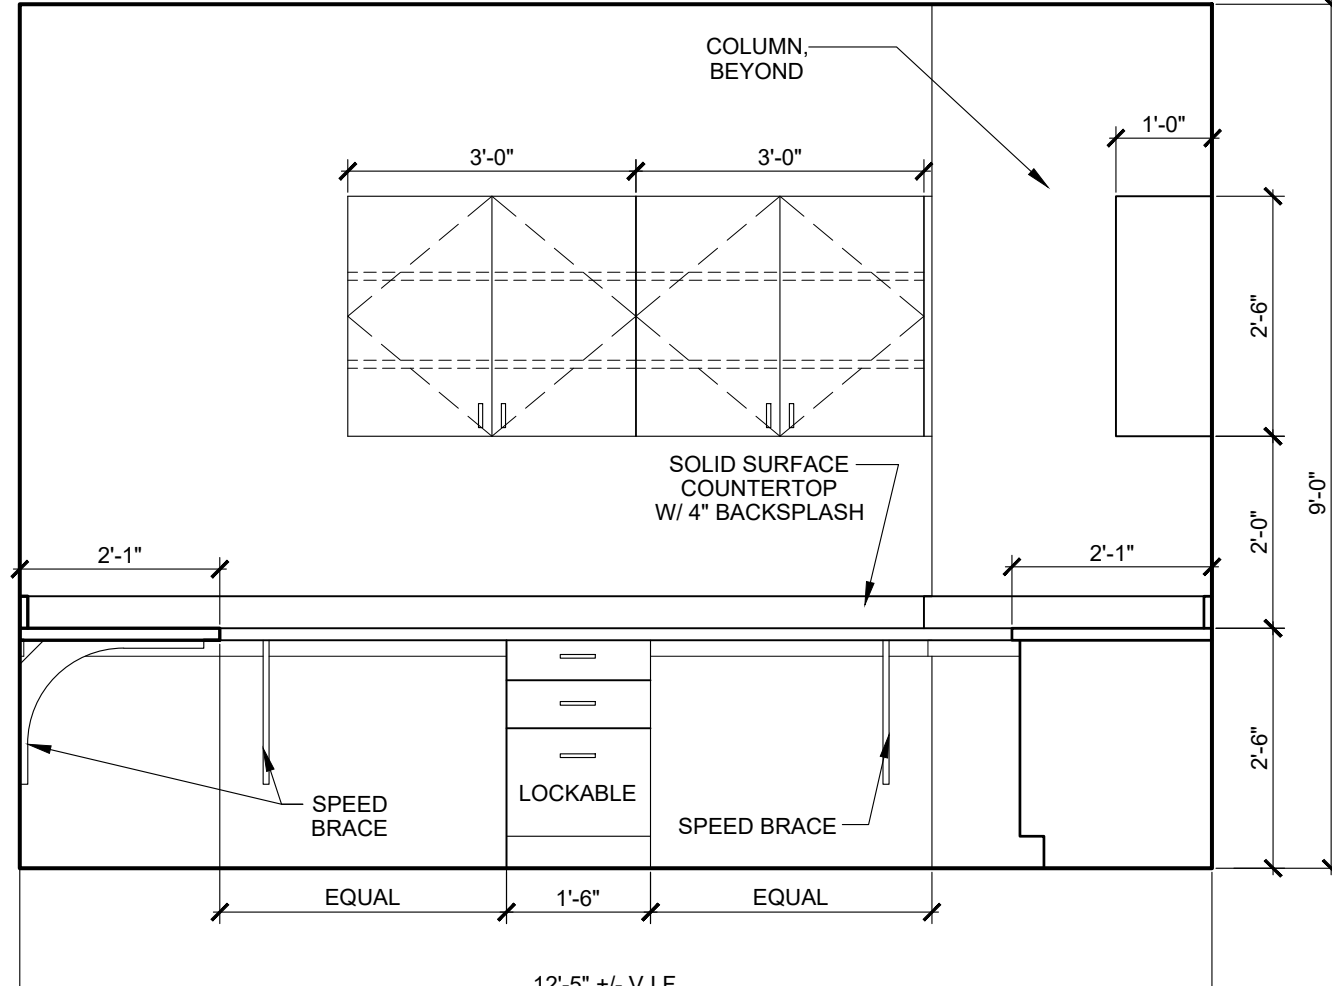


5 CONTROL ROOM 105
SCALE: 1/2" = 1'-0"

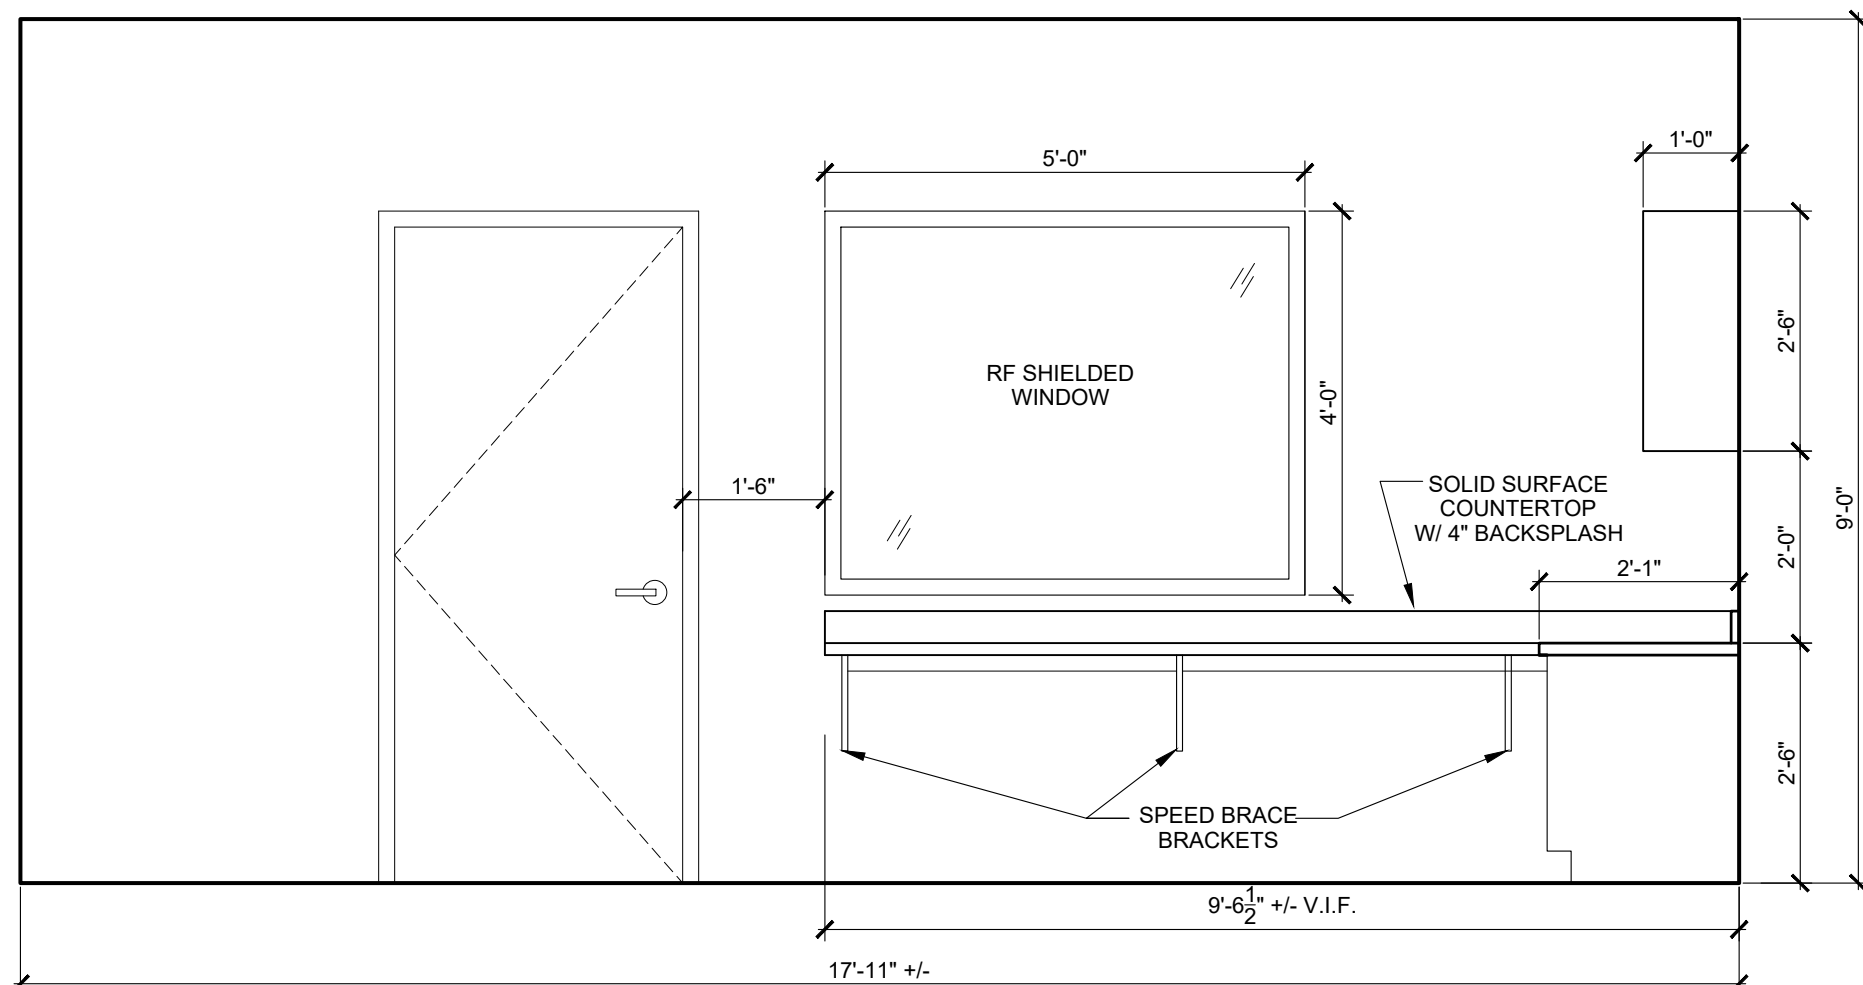

6 CONTROL ROOM 105
SCALE: 1/2" = 1'-0"

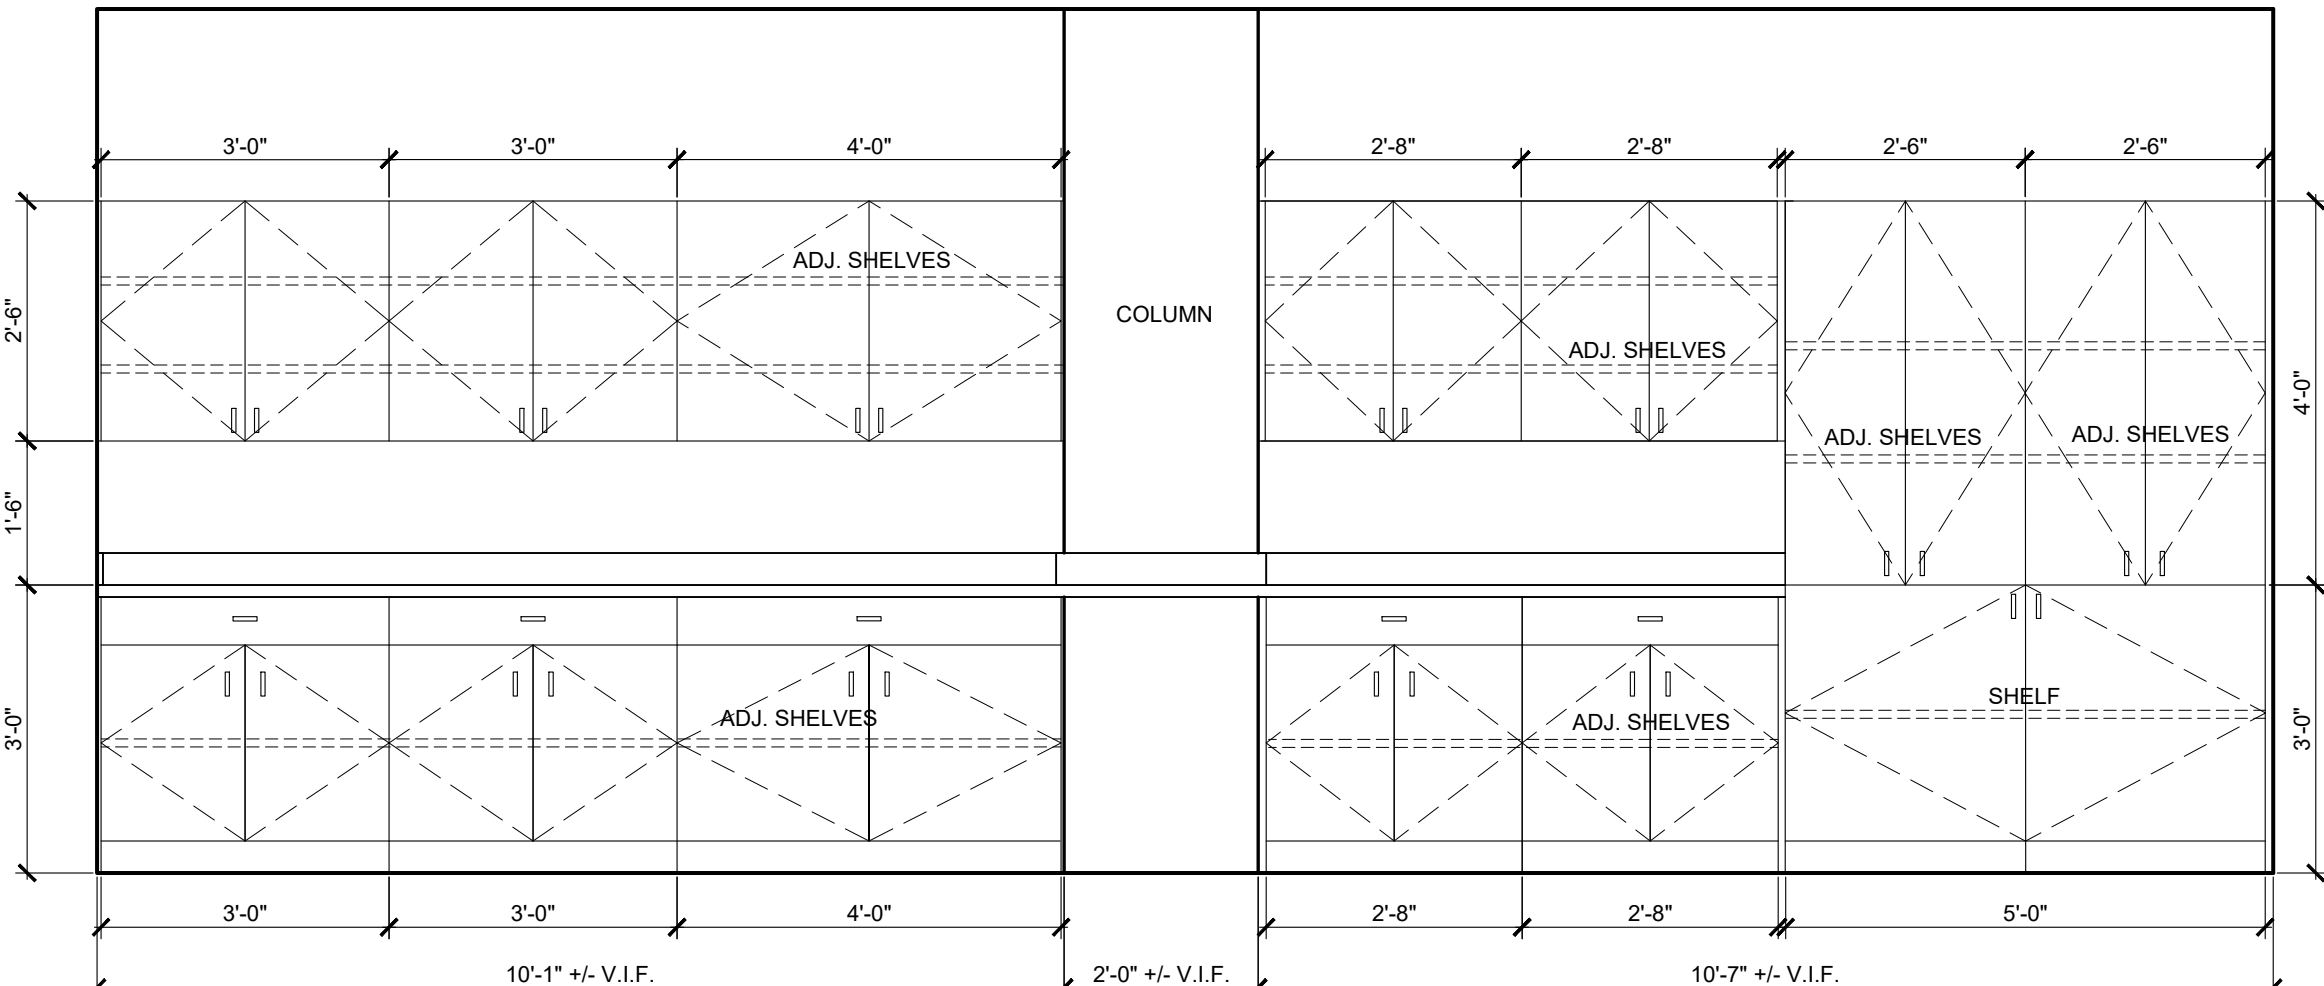

7 MRI SCAN ROOM 107
SCALE: 1/2" = 1'-0"

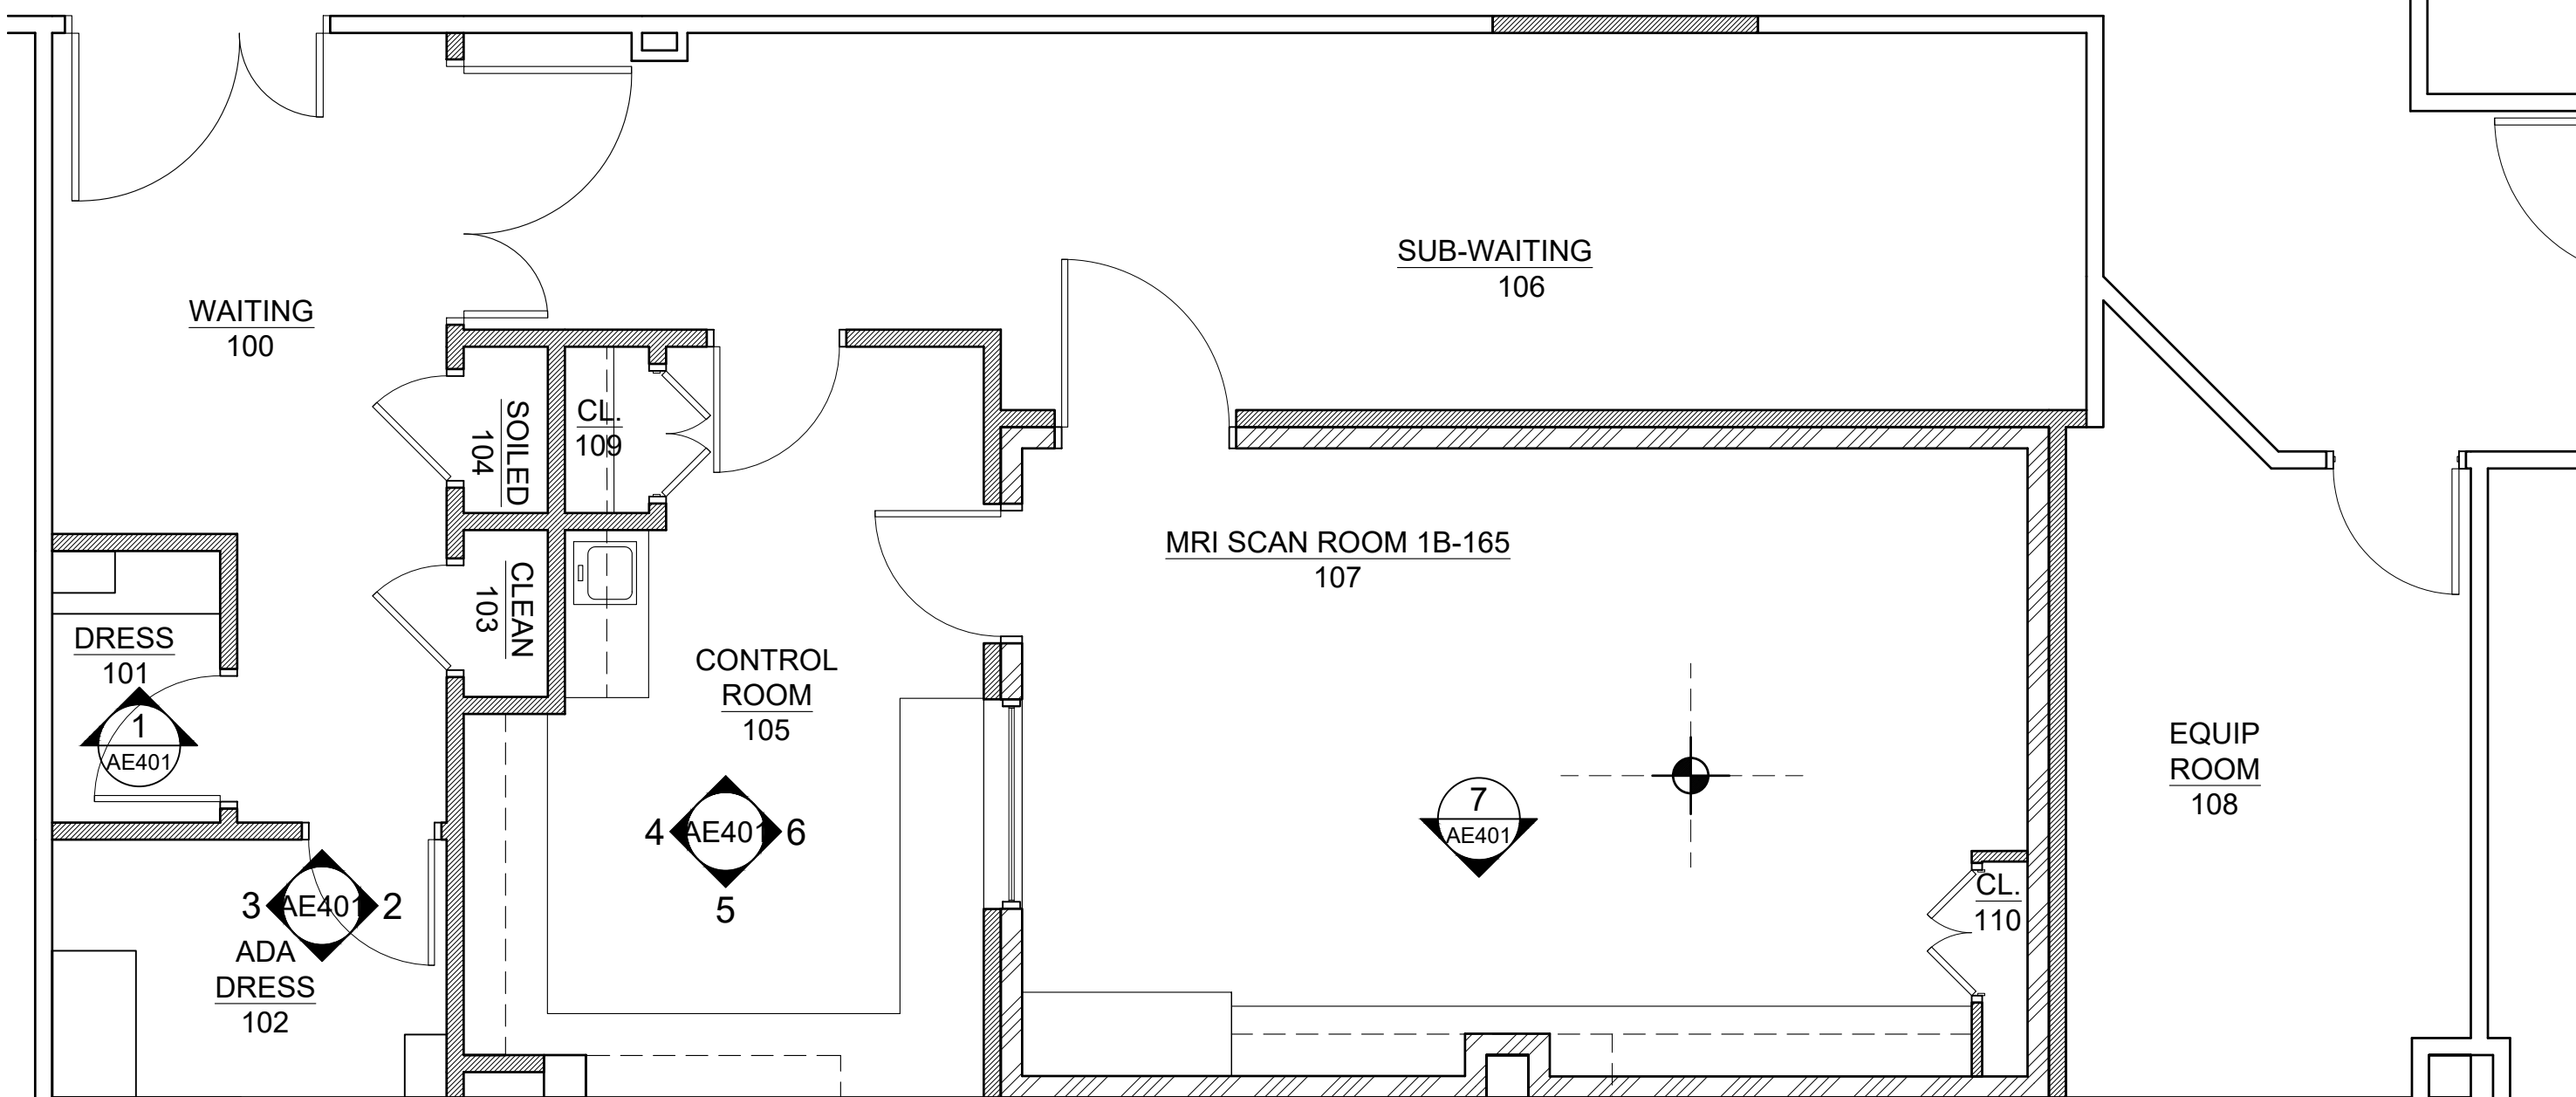

8 MILLWORK PLAN
SCALE: 1/4" = 1'-0"

MILLWORK NOTES

- 1: WALL AND BASE CABINETS EXTERIOR TO BE PLASTIC LAMINATE, SEE FINISH SCHEDULE FOR SPECIFICATION.
- 2: WALL AND BASE CABINET INTERIOR TO BE WHITE MELAMINE.
- 3: COUNTERTOPS WITH 4" BACKSPLASH TO BE SOLID SURFACE, SEE FINISH SCHEDULE FOR SPECIFICATION.
- 4: PROVIDE ADJUSTABLE SHELVES AS INDICATED ON ELEVATIONS.
- 5: DOORS AND DRAWERS TO HAVE 4" BRUSHED CHROME WIRE SHELVES

For review and approval	6.2.21
Revisions:	Date


DESIGN/BUILDER:
Deerfield Construction Group 610 Professional Drive, Suite 210 Gaithersburg, Maryland 20879 (301)947-4701

ARCHITECT/ENGINEERS:
Nicholas Lucarelli Architects, LLC 6723 Whittier Avenue Suite 414 McLean, VA 22101 Tel: (703) 790-9606

D2 Engineering, LLC
18310 Montgomery Village Ave
Suite 520
Gaithersburg, MD 20879
Tel: (301) 208-9575
Fax: (301) 208-9405

PROPERTY OF THE UNITED STATES GOVERNMENT
FOR OFFICIAL USE ONLY
DO NOT REMOVE THIS NOTICE.
PROPERLY DESTROY DOCUMENTS WHEN NO LONGER NEEDED.

Stamp/Seal

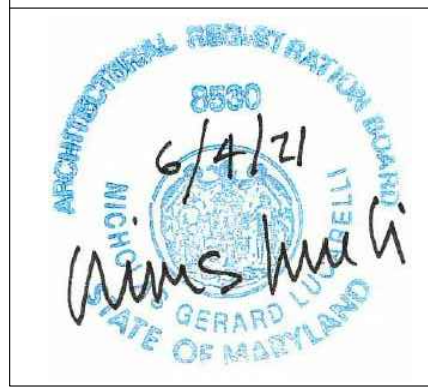

Drawing Title
MILLWORK PLAN & ELEVATIONS

Approved: Project Director

Project Title
VA BALTIMORE MEDICAL
CENTER ROOM 1B-165

Location
10 NORTH GREENE STREET, BALTIMORE, MD 21201

Date
6.2.2021

Checked

Drawn

Project Number
PROJECT #

Building Number
-

Drawing Number
AE401





GREAT PLAINS AREA INDIAN HEALTH SERVICE
OFFICE OF ENVIRONMENTAL
HEALTH & ENGINEERING

DIVISION OF FACILITIES MANAGEMENT
115 4TH AVENUE SE, RM 309
ABERDEEN, SD 57401
(605) 226-7451 FAX (605) 226-7580

www.ihs.gov


Quentin N. Burdick
Memorial Health Facility

Replace RTU &
Cabinetry - CT Area


CONTRACT NO:	
TASK ORDER NO:	
PROJECT NUMBER:	GP22TM300H10
DATE:	08/26/2025
DRAWN BY:	Taylor Strand
CHECKED BY:	Brad Weekley
LAST REVISION DATE:	

CASEWORK SECTION
VIEWS


A.3

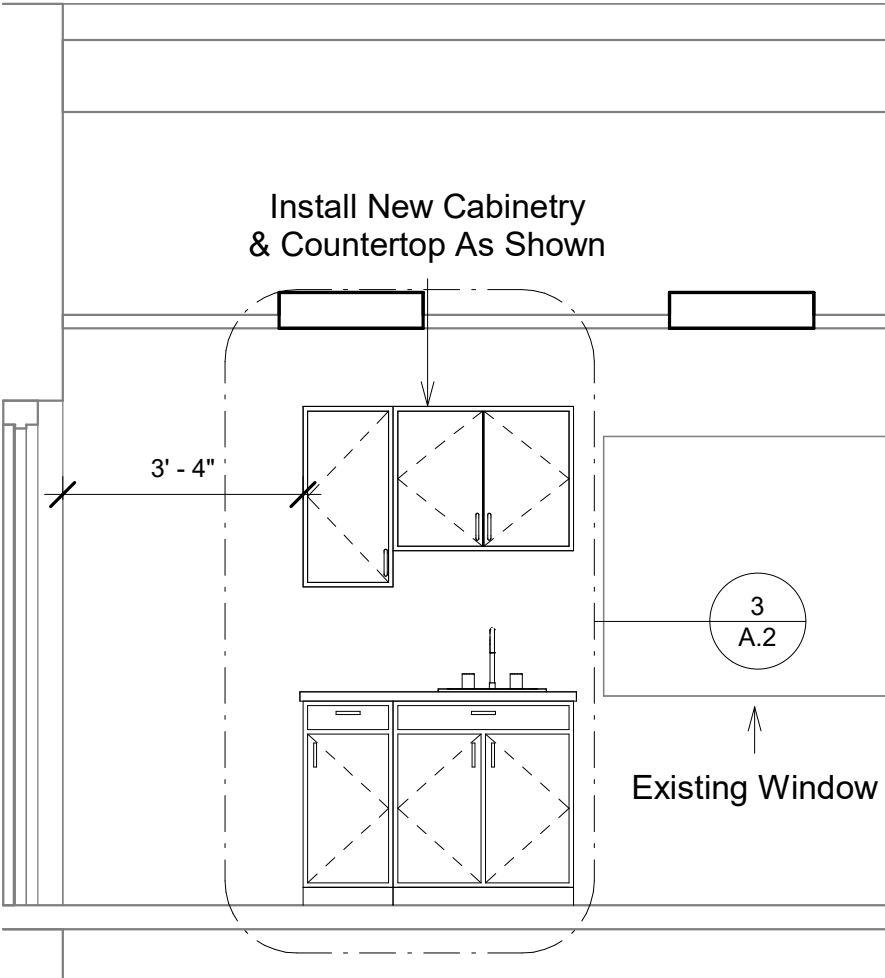

① North Wall Cabinets Copy 1
3/8" = 1'-0"

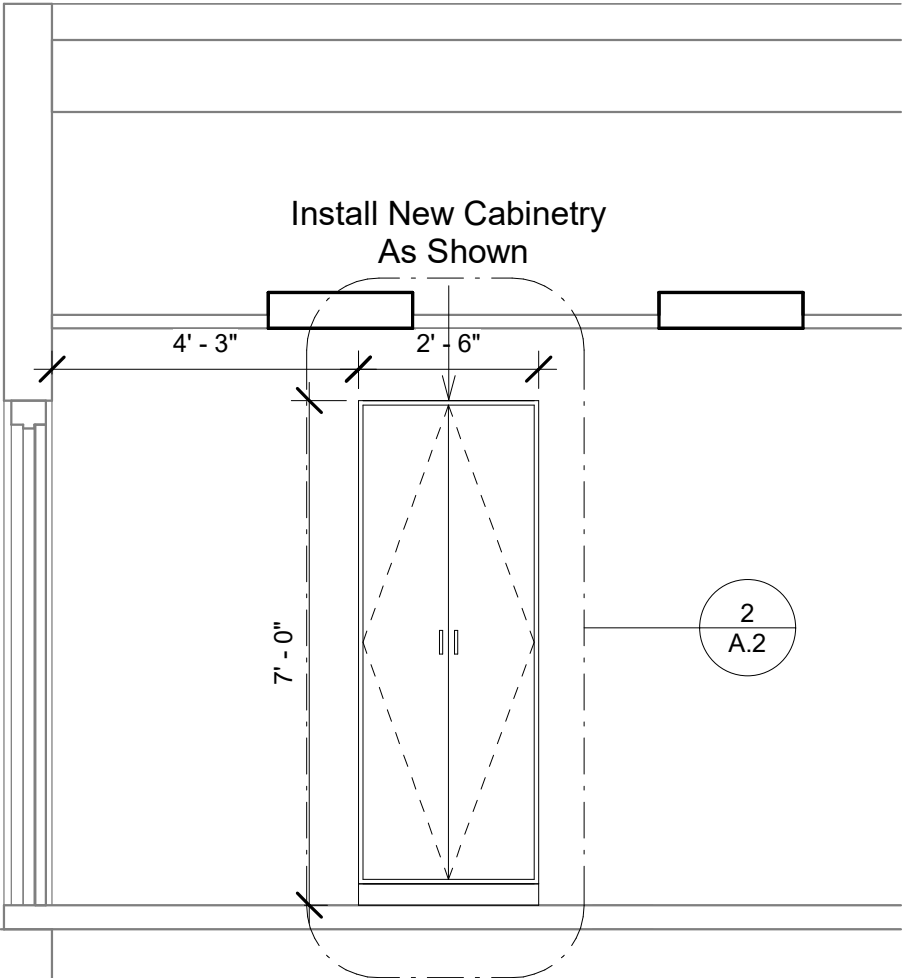

② South Wall Cabinets Copy 1
3/8" = 1'-0"

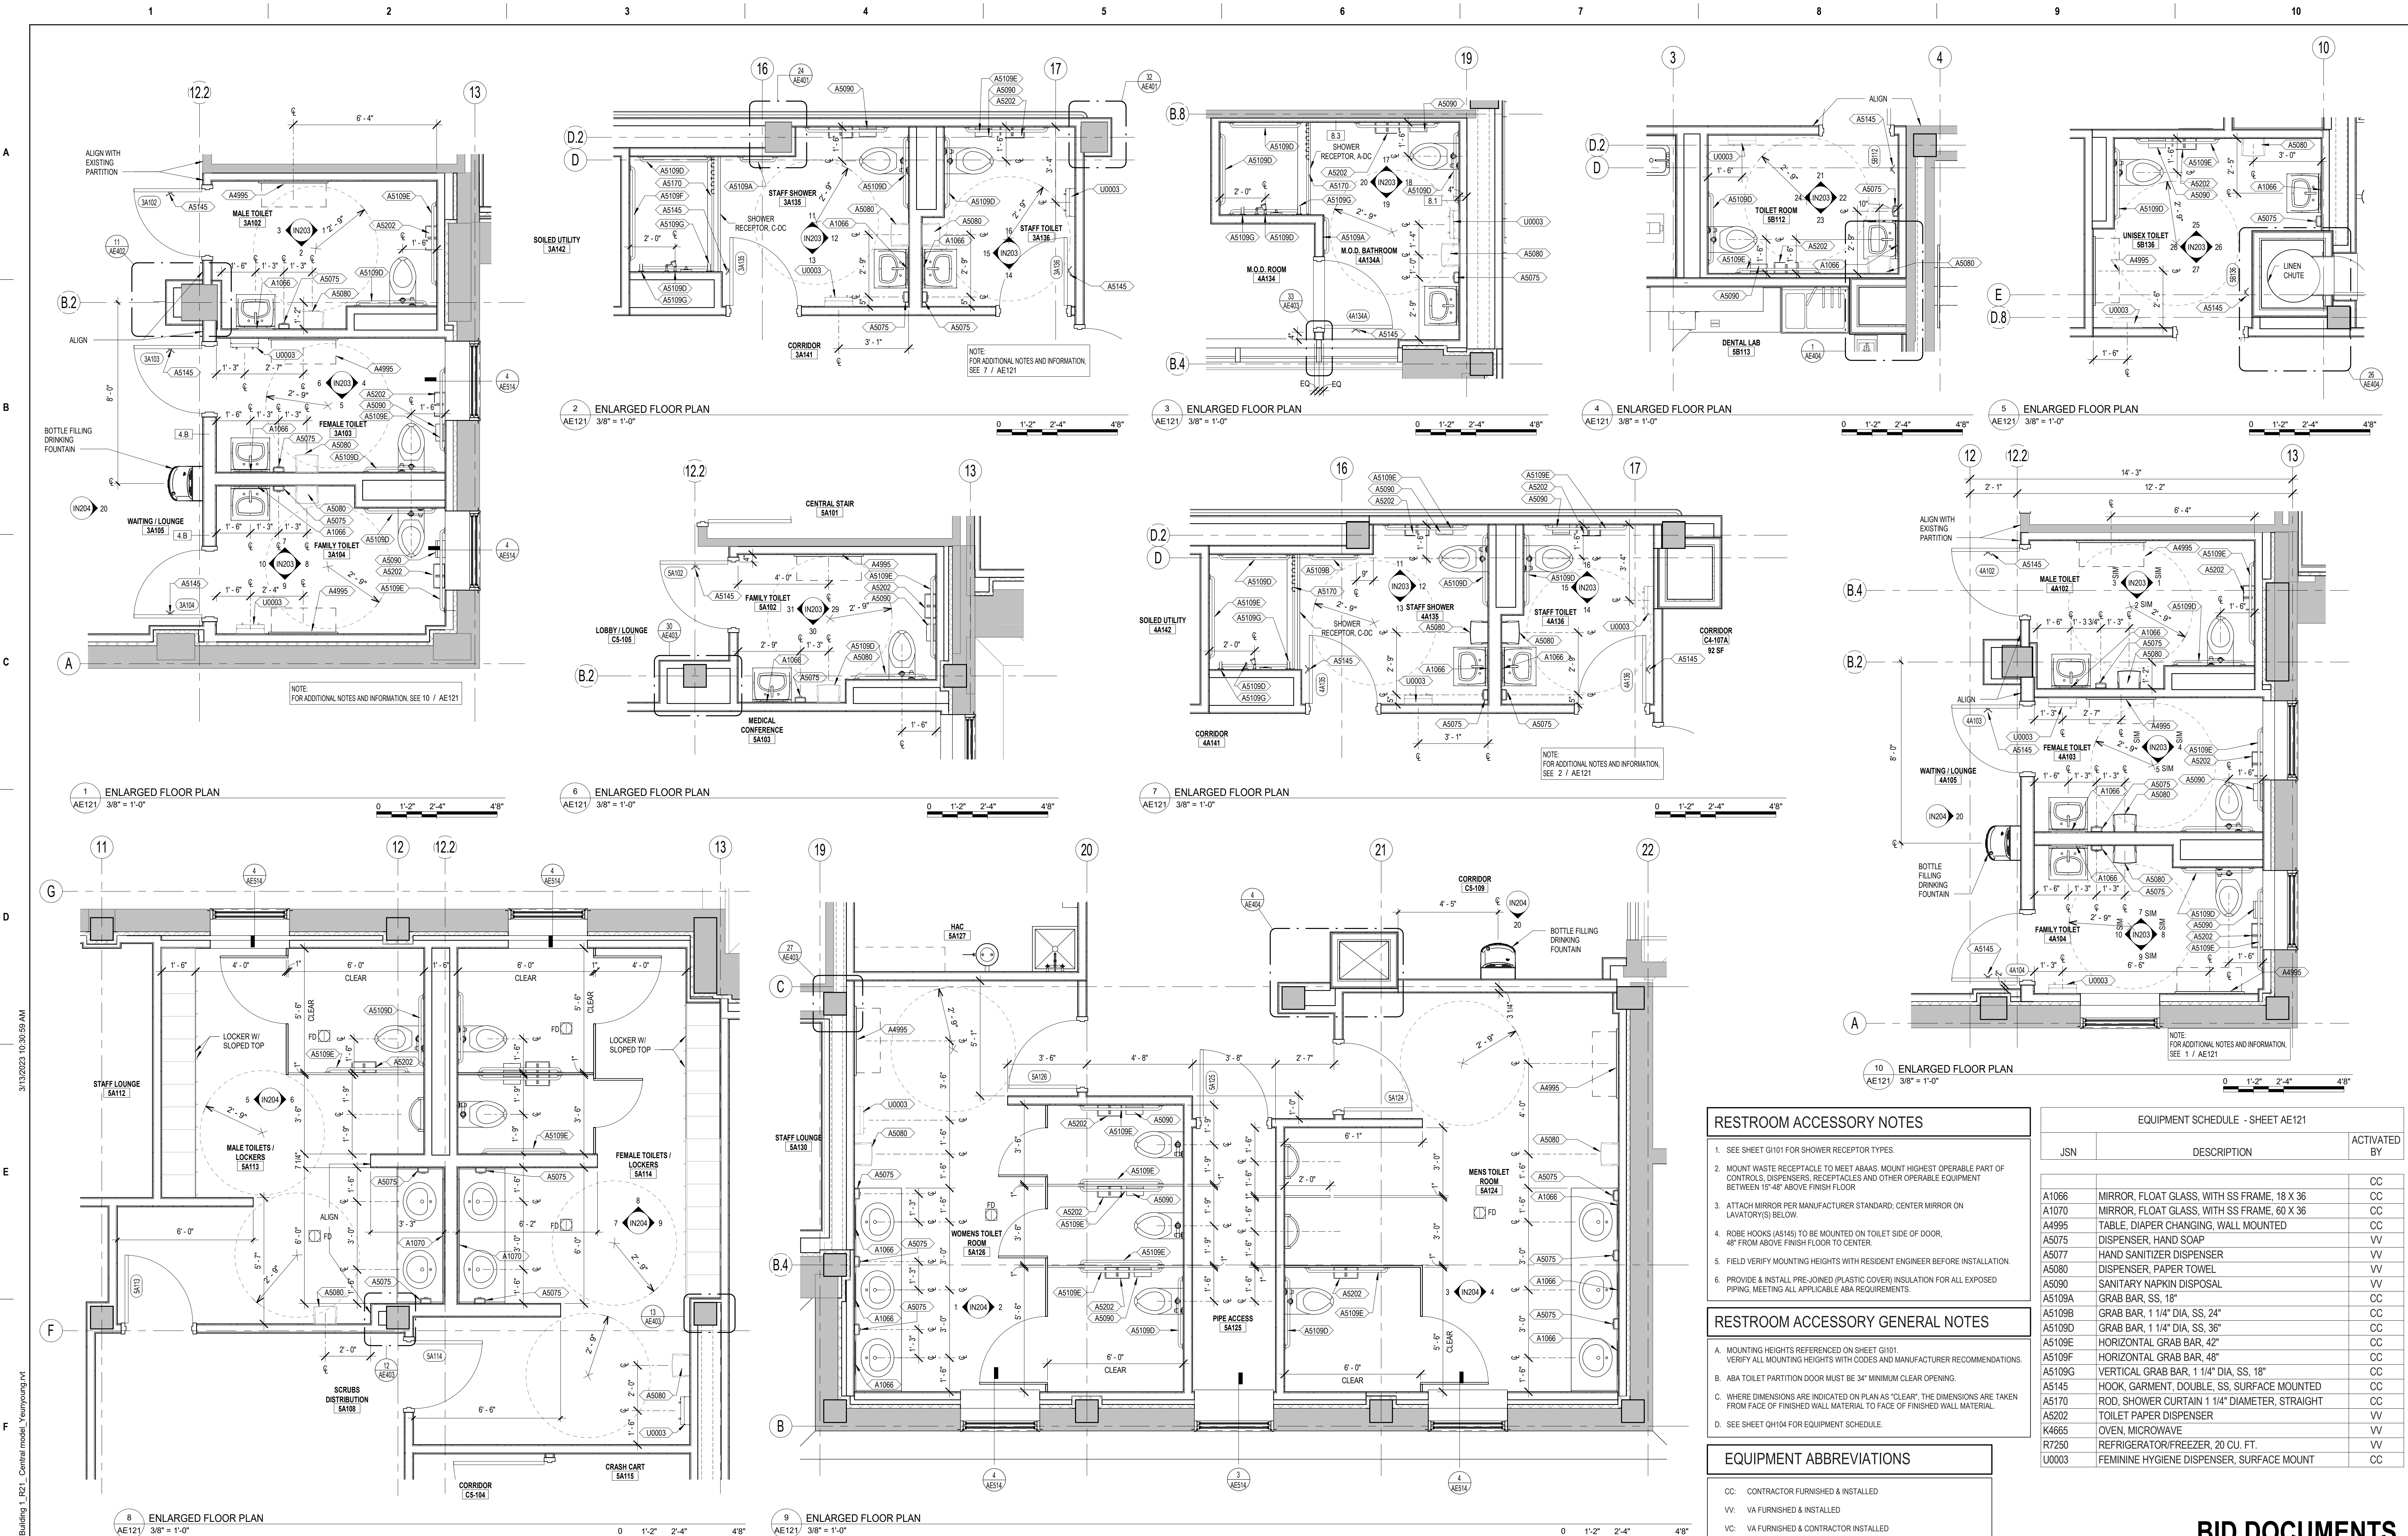


RESTROOM ACCESSORY NOTES		
1. SEE SHEET G101 FOR SHOWER RECEPTOR TYPES.		
2. MOUNT WASTE RECEPTACLE TO MEET ABAAS. MOUNT HIGHEST OPERABLE PART OF CONTROLS, DISPENSERS, RECEPTACLES AND OTHER OPERABLE EQUIPMENT BETWEEN 15'-48" ABOVE FINISH FLOOR.		
3. ATTACH MIRROR PER MANUFACTURER STANDARD; CENTER MIRROR ON LAVATORY(S) BELOW.		
4. ROBE HOOKS (A5145) TO BE MOUNTED ON TOILET SIDE OF DOOR, 48" FROM ABOVE FINISH FLOOR TO CENTER.		
5. FIELD VERIFY MOUNTING HEIGHTS WITH RESIDENT ENGINEER BEFORE INSTALLATION.		
6. PROVIDE & INSTALL PRE-JOINED (PLASTIC COVER) INSULATION FOR ALL EXPOSED PIPING, MEETING ALL APPLICABLE ABA REQUIREMENTS.		
RESTROOM ACCESSORY GENERAL NOTES		
A. MOUNTING HEIGHTS REFERENCED ON SHEET G101.		
B. ABA TOILET PARTITION DOOR MUST BE 34" MINIMUM CLEAR OPENING.		
C. WHERE DIMENSIONS ARE INDICATED ON PLAN AS "CLEAR", THE DIMENSIONS ARE TAKEN FROM FACE OF FINISHED WALL MATERIAL TO FACE OF FINISHED WALL MATERIAL.		
D. SEE SHEET Q1104 FOR EQUIPMENT SCHEDULE.		
EQUIPMENT ABBREVIATIONS		
CC: CONTRACTOR FURNISHED & INSTALLED		
VV: VA FURNISHED & INSTALLED		
VC: VA FURNISHED & CONTRACTOR INSTALLED		


EQUIPMENT SCHEDULE - SHEET AE121		
JSN	DESCRIPTION	ACTIVATED BY
A1066	MIRROR, FLOAT GLASS, WITH SS FRAME, 18 X 36	CC
A1070	MIRROR, FLOAT GLASS, WITH SS FRAME, 60 X 36	CC
A4995	TABLE, DIAPER CHANGING, WALL MOUNTED	CC
A5075	DISPENSER, HAND SOAP	VV
A5077	HAND SANITIZER DISPENSER	VV
A5080	DISPENSER, PAPER TOWEL	VV
A5090	SANITARY NAPKIN DISPOSAL	VV
A5109A	GRAB BAR, SS, 18"	CC
A5109B	GRAB BAR, 1 1/4" DIA, SS, 24"	CC
A5109D	GRAB BAR, 1 1/4" DIA, SS, 36"	CC
A5109E	HORIZONTAL GRAB BAR, 42"	CC
A5109F	HORIZONTAL GRAB BAR, 48"	CC
A5109G	VERTICAL GRAB BAR, 1 1/4" DIA, SS, 18"	CC
A5145	HOOK, GARMENT, DOUBLE, SS, SURFACE MOUNTED	CC
A5170	ROD, SHOWER CURTAIN 1 1/4" DIAMETER, STRAIGHT	CC
A5202	TOILET PAPER DISPENSER	VV
K4665	OVEN, MICRO/WAVE	VV
R7250	REFRIGERATOR/FREEZER, 20 CU. FT.	VV
U0003	FEMININE HYGIENE DISPENSER, SURFACE MOUNT	CC

BID DOCUMENTS

--	--	

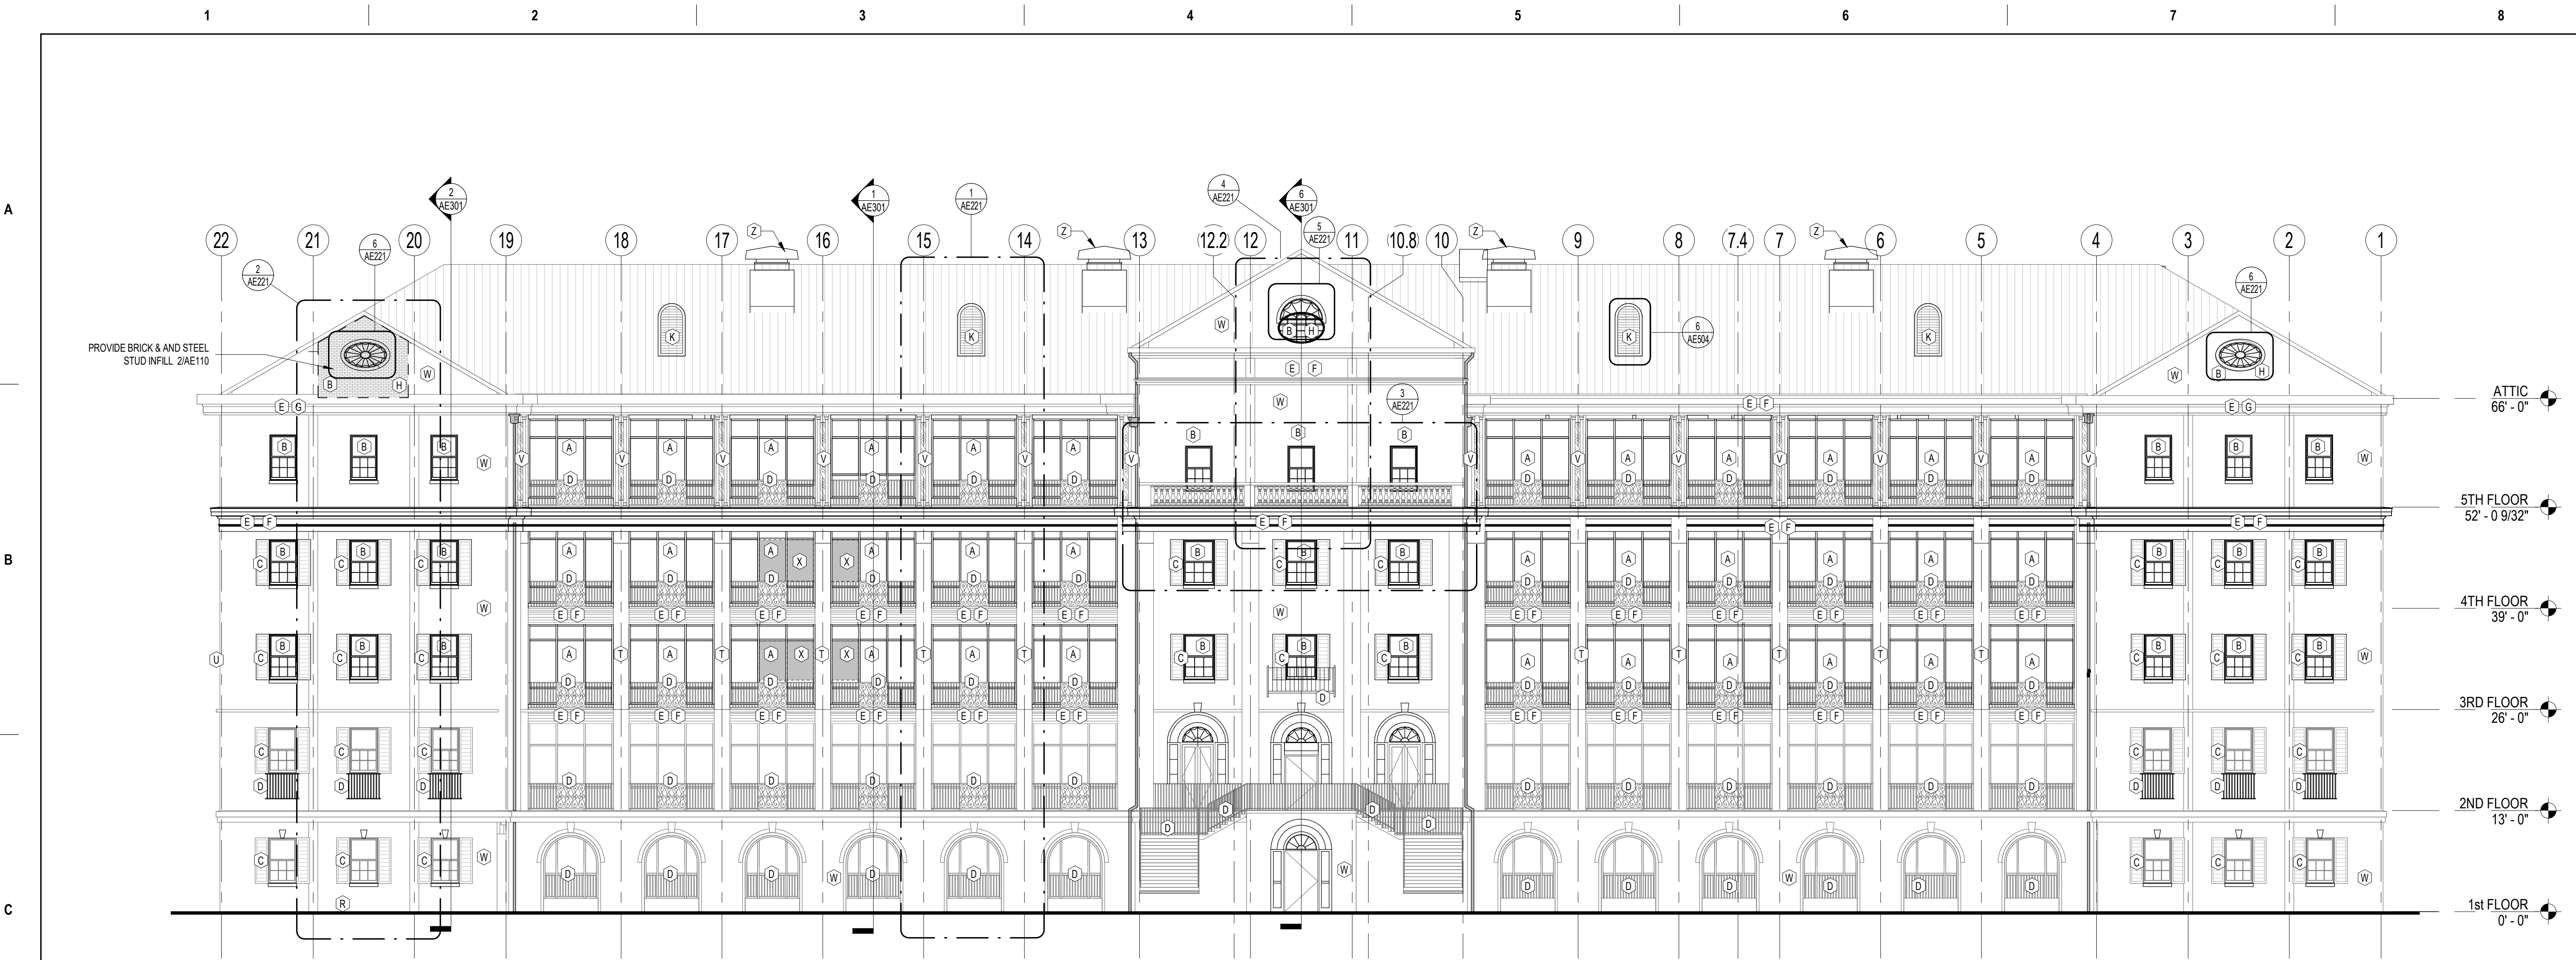

1 NORTH EXTERIOR ELEVATION
3/32" = 1'-0"

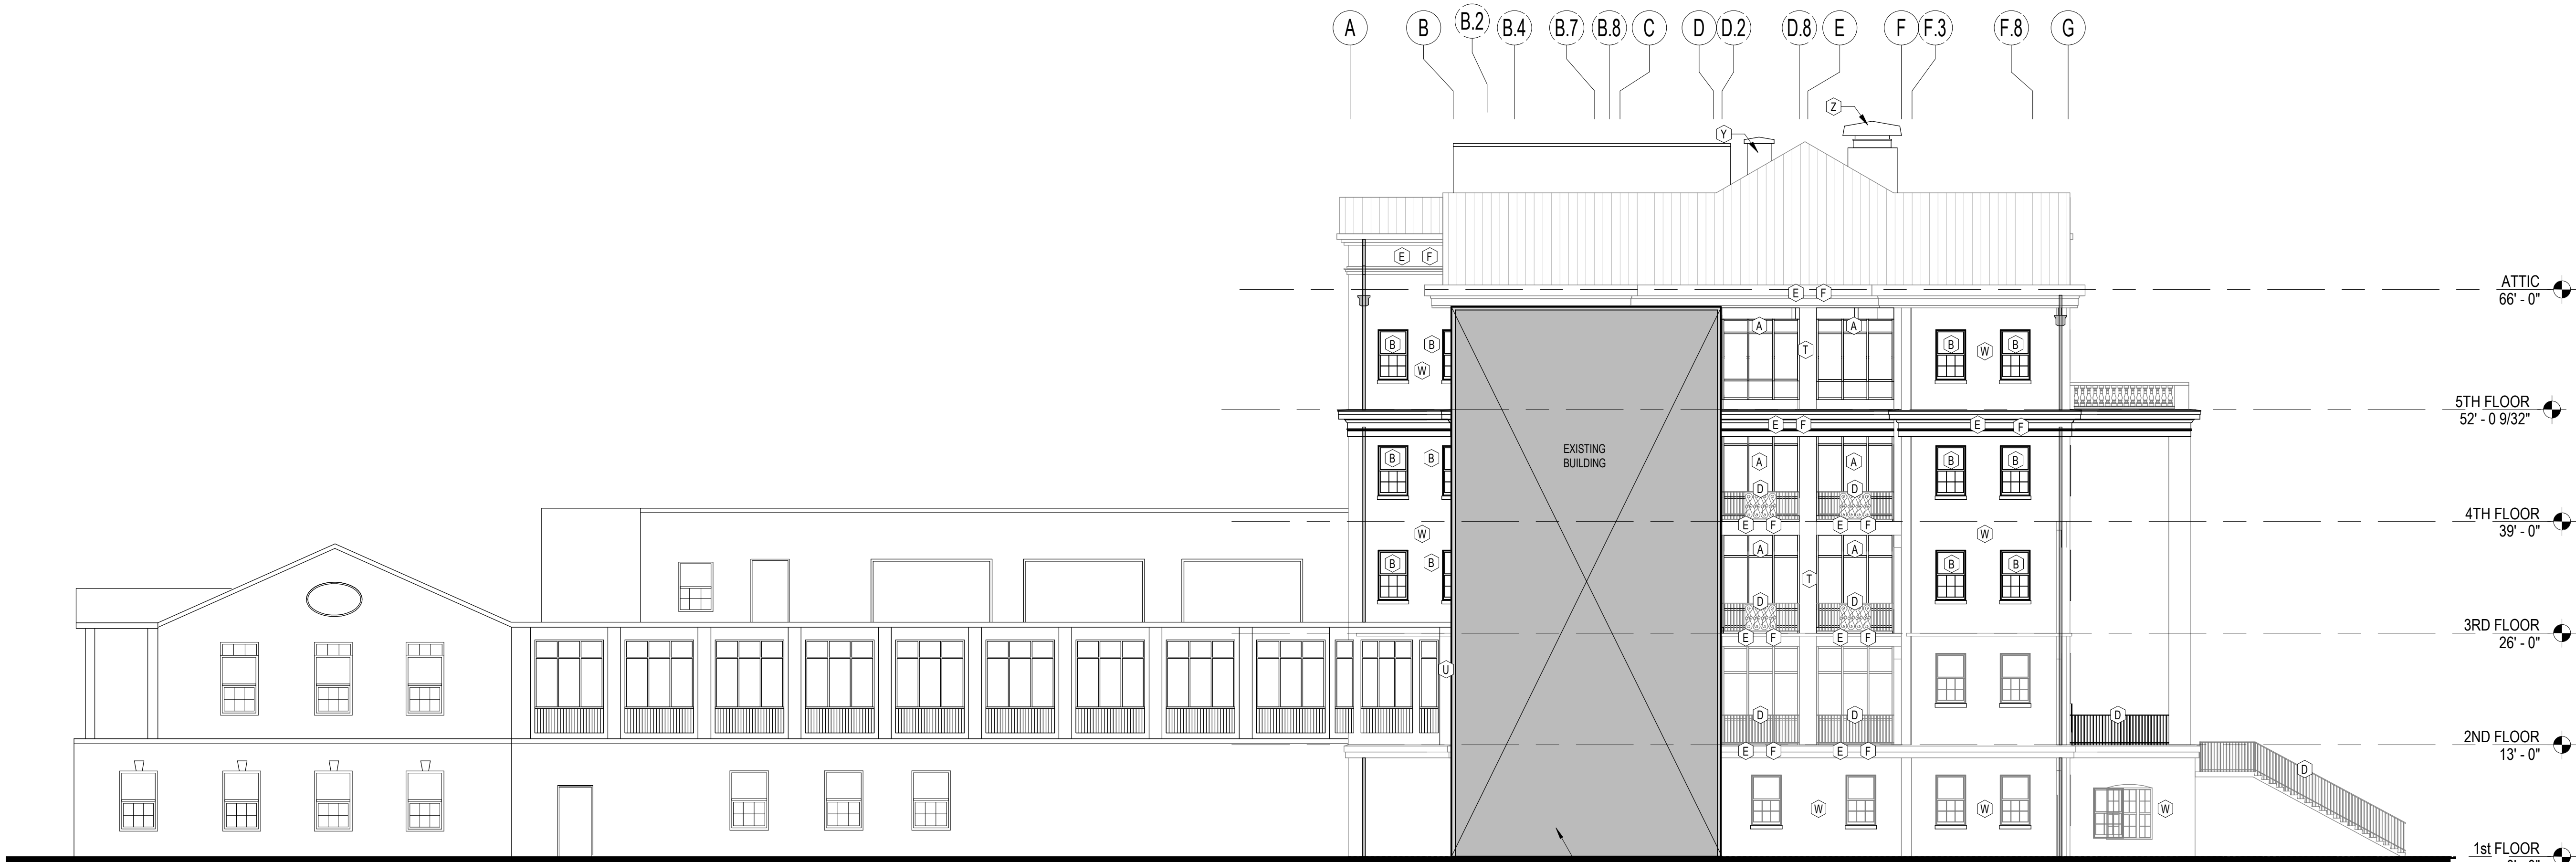

2 EAST EXTERIOR ELEVATION
3/32" = 1'-0"

EXTERIOR ELEVATIONS GENERAL NOTES

- CONTRACTOR IS TO FIELD VERIFY ALL DIMENSIONS AND CONDITIONS
- UPON DISCOVERY OF ANY DISCREPANCIES BETWEEN DRAWINGS DEPICTING EXISTING CONDITIONS OR UPON DISCOVERY OF UNKNOWN CONDITIONS DETRIMENTAL TO THE COMPLETION OF THE WORK AS INDICATED IN THE DOCUMENTS, THE CONTRACTOR SHALL IMMEDIATELY NOTIFY THE ARCHITECT & RESIDENT ENGINEER, IN WRITING, OF THE CONDITION IN QUESTION BEFORE PROCEEDING WITH WORK IN THE AREA.
- CONTRACTOR SHALL MAINTAIN SAFE METHODS OF EGRESS FOR OCCUPIED PORTIONS OF BUILDING AND IN SITE AREA DURING CONSTRUCTION.
- DO NOT SCALE DRAWINGS. IF DIMENSIONS ARE IN QUESTION, THE CONTRACTOR SHALL BE RESPONSIBLE FOR OBTAINING CLARIFICATION FROM THE ARCHITECT & RESIDENT ENGINEER BEFORE CONTINUING WITH THE CONSTRUCTION.
- COORDINATE WORK WITH OTHER PHASES
- COORDINATE SITE LAYOUT / ACCESS / WORK AREAS / LAYDOWN AREAS / PHASING WITH RESIDENT ENGINEER
- SEE SHEETS S402 AND S403 FOR CURTAINWALL / WINDOW OPENING TYPES AND ASSOCIATED WORK
- SEE SHEET ADT01 - ADT05 FOR PHOTOGRAPHS
- ALL MASONRY / STONE IS TO HAVE A WATER RESISTANCE COATING. MORTAR JOINTS ARE TO BE RETOOLLED, AS REQUIRED.
- ALL EIFS SYSTEM TO HAVE WATERPROOF COATING OVER INSULATION BOARD / FOAM SHAPE, BASE COAT AND PRIMER, WHERE REQUIRED
- BACKWRAP EIFS FOAM INSULATION BOARDS / SHAPE PER MANUFACTURER'S RECOMMENDATIONS
- ALL DIFFERING MATERIAL JOINTS TO HAVE BACKER ROD AND SEALANT INSTALLED
- INSTALL NEW GUTTERS AND DOWNSPOUTS. SEE ROOF PLAN ON SHEET AE105 FOR ADDITIONAL WORK NOT SHOWN. PROVIDE CONCRETE SPLASH BLOCKS AT ALL DOWNSPOUT LOCATIONS THAT SPLASH AT GRADE
- REMOVE ALL SIGNAGE IN AREAS OF WORK. PREDRILL HOLES FOR FASTENERS AND FILL WITH SEALANT PRIOR TO INSTALL FASTENER.
- REINSTALL ALL ELECTRICAL, COMMUNICATIONS, SECURITY, ACCESS CONTROL, IN EXISTING LOCATIONS. PROVIDE WATERTIGHTNESS AT PENETRATIONS
- COLORS (SUBMIT WATERPROOF COATING, PAINT AND METAL COLORS TO BE APPROVED IN SHOP DRAWINGS PHASE BY ARCHITECT OR RESIDENT ENGINEER - COLORS TO MATCH EXISTING CAMPUS COLOR SCHEME):
 - BRICK (BELOW SECOND FLOOR STONE BANDING TO GRADE 0): LIGHT TAN
 - BRICK & NEW EIFS GABLE (ABOVE SECOND FLOOR STONE BANDING TO ROOF) MEDIUM TAN
 - STONE BANDING, SILL, KEYSTONES, ETC: GRAY
 - EIFS (COLUMN, TRIM, FASCIA, CORNICE, ETC): WHITE
 - STOREFRONT, WINDOW UNITS AND ASSOCIATED FLASHING: WHITE
 - RAILINGS: BLACK
 - ROOF AND ROOF FLASHINGS: COLONIAL RED (MATCH EXISTING)
 - ROOF GUTTERS COLONIAL RED, ROOF DOWNSPOUTS TO MATCH ADJACENT WALL COLOR

ELEVATION LEGEND

- EXISTING TO REMAIN
- - - - - TO BE REMOVED
- (N) KEYNOTE

EXTERIOR ELEVATION KEYNOTES

- (A) NEW ALUMINUM CURTAINWALL INCLUDING FASTENER, BLOCKING, FLASHING, SEALANTS. SEE DETAILS FOR ADDITIONAL INFORMATION. SEE PLANS FOR CURTAINWALL TYPES.
- (B) NEW ALUMINUM WINDOW INCLUDING FASTENERS, BLOCKING, FLASHING, SEALANTS. SEE DETAILS FOR ADDITIONAL INFORMATION. SEE PLANS FOR WINDOW TYPES.
- (C) REINSTALL EXISTING SHUTTERS. PREDRILL HOLES FOR FASTENERS, CLEAN, AND FILL WITH SEALANT PRIOR TO INSTALLING FASTENERS. TYPICAL FOR NORTH ELEVATION.
- (D) REINSTALL REFINISHED RAILINGS. FILL ANY SOCKETS IN STONE WITH EPOXY, REMOVE BOTTOM OF POST IF APPLICABLE AND PROVIDE L-BRACKET TO FASTEN RAIL TO ADJACENT COLUMN.
- (E) INSTALL SILICONE ELASTOMERIC COATING OVER EIFS PILASTERS AND FASCIA. PROVIDE SUPPORTING LIGHT GAGE FRAMING, TRTD WOOD BLOCKING AND FLASHING.
- (F) INSTALL EIFS APPLIED CORNICES, TRIM AND PREFINISHED MITL FLASHING.
- (G) INSTALL EIFS ASSEMBLY. SEE DETAILS FOR EXTENT, ADJUST EXISTING THRU-WALL FLASHING TO COORDINATE WITH NEW WORK.
- (H) INSTALL EIFS APPLIED WINDOW TRIM. SEE WINDOW TYPES FOR ADDITIONAL INFORMATION.
- (J) PAINT EXISTING GUARD RAIL SYSTEM.
- (K) NEW LOUVER AND PREFINISHED MITL ON DORMERS, SEE ROOF PLAN - COORDINATE WITH MECH.
- (L) REINSTALL ACCESS CONTROL SYSTEM. PREDRILL HOLES FOR FASTENERS AND FILL WITH SEALANT TO INSTALLING FASTENERS.
- (M) REINSTALL LIGHT FIXTURE. PRE-DRILL HOLES FOR FASTENERS AND FILL WITH SEALANT PRIOR TO INSTALLING FASTENERS. PROVIDE GASKETS AT CONNECTION TO JUNCTION BOX.
- (N) REINSTALL SECURITY/COMMUNICATIONS FIXTURE FOR REINSTALLATION. PREDRILL HOLES FOR FASTENERS AND FILL WITH SEALANT PRIOR TO INSTALLING FASTENERS. PROVIDE GASKETS AT CONNECTION TO JUNCTION BOX. SEAL ALL HOLES IN MASONRY.
- (P) NOT USED.
- (Q) INSTALL NEW BACKER ROD AND SEALANT ALL AROUND EXISTING LOUVER.
- (R) INSTALL APPLIED GRATE OVER EXISTING FOUNDATION VENT HOLES. RECONNECT UTILITIES AS REQUIRED.
- (S) CLEAN EXISTING DOOR FINISHES. INSTALL NEW SEALANT AND BACKER RODS ALL AROUND. INSTALL GASKETS ALL AROUND.
- (T) INSTALL WATERPROOFING SILICONE ELASTOMERIC COATING OVER EIFS PILASTERS AND FASCIA. PROVIDE SUPPORTING LIGHT GAGE FRAMING, TRTD WOOD BLOCKING AND FLASHING.
- (U) INSTALL NEW ALUMINUM EXPANSION JOINT ASSEMBLY AND COVER AT CONNECTIONS BETWEEN BUILDING 1 AND BUILDING 53 AT NORTH AND SOUTH ELEVATIONS. REFER TO SPEC SECTION 07 95 13 (EXPANSION JOINT COVER ASSEMBLY) FOR ADDITIONAL INFORMATION.
- (V) REPAIR METAL COLUMNS AT 5TH FLOOR FACADE. SANDBLAST, REWELDED BASES, AND REPAINT AT ALL COLUMNS.
- (W) PROVIDE MORTAR JOINT REPAIR/REPLACEMENT TO EXISTING BRICK. PAINT EXISTING MASONRY/BRICK AND INSTALL SILICONE ELASTOMERIC COATING.
- (X) APPLY UV FILM AT INTERIOR OF THIS WINDOW. REFER TO SPEC SECTION 06 80 10 (GLAZING) FOR ADDITIONAL INFORMATION.
- (Y) EXISTING MECHANICAL EXHAUST.
- (Z) MECHANICAL EXHAUST.
- (Z-1) REBUILD OUTER WYTHE OF BRICK FROM SALVAGE BRICK.

BID DOCUMENTS

NO.	REVISIONS	DATE

CONSULTANT

ARCHITECT/ENGINEER OF RECORD

THOMAS OLESAC, ARCHITECT
MS Lic # 5505

1050 HOYT AVE WEST ST PAUL, MN 55117
952-451-0460

STAMP



Office of
Construction
and Facilities
Management

VA

U.S. Department
of Veterans
Affairs

Drawing Title

EXTERIOR ELEVATIONS

Approved:

Phase

CONSTRUCTION
DOCUMENTS

FULLY SPRINKLERED

Project Title

RENOVATE BUILDING 1

Location

BILOXI, MISSISSIPPI

Issue Date

03/10/2023

Checked

LA

Drawn

CD,PC

Project Number

520-317X

Building Number

1

Drawing Number

AE202

Dwg. 84 of 238


GENERAL REFLECTED CEILING PLAN NOTES

- A. ALL FINISH CEILING HEIGHTS TO BE INSTALLED AT 8'-0" A.F.F. UNLESS OTHERWISE NOTED.
- B. MECHANICAL AND ELECTRICAL DEVICES SHOWN ARE FOR INDICATION OF THEIR RESPECTIVE LOCATION ONLY. NOT ALL SUCH DEVICES ARE SHOWN BY THIS PLAN. MECHANICAL AND ELECTRICAL DEVICES TYPE, SIZE AND OTHER REQUIREMENTS ARE DOCUMENTED BY THE CORRESPONDING M.E.P. PLAN, DETAIL AND/OR SPECIFICATION SECTION.
- C. REFER TO SPECIFICATION SECTION 07 21 13 FOR ACOUSTICAL CEILING BATT INSULATION.
- D. REFER TO SPECIFICATION SECTION 09 29 00 FOR GYPSUM BOARD CEILING SYSTEM.
- E. REFER TO SPECIFICATION SECTION 09 51 00 FOR ACOUSTICAL CEILING SYSTEM.
- F. COORDINATE FIRE PROTECTION SYSTEM TO PROVIDE NEW SPRINKLER HEADS AT THE CENTER POINT OF CEILING TILES SHOWN.
- G. REFER TO PHASING PLAN AND SPECIFICATION SECTION 01 00 00 GENERAL REQUIREMENTS FOR PHASING REQUIREMENTS OF WORK SHOWN.
- H. REFER TO SPECIFICATION SECTION 01 35 26 FOR INFECTION CONTROL REQUIREMENTS FOR WORK SHOWN.
- I. ROOM TAGS REMOVED FOR CLARITY. REFER TO SHEETS AE103 & AE105 FOR ROOM NAMES.



REFLECTED CEILING PLAN NOTES

1. NO NEW CEILING IN THIS AREA.
2. FULL CEILING TILE.
3. SINGLE TRACK BARIATRIC PATIENT LIFT SYSTEM. REFER TO EQUIPMENT LEGEND, SHT. AE305 AND SPECIFICATION SECTION 11 73 00.


REFLECTED CEILING PLAN LEGEND

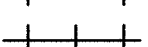	2' X 4' ACOUSTICAL TILE		HVAC RETURN
	2' X 2' ACOUSTICAL TILE		HVAC SUPPLY
	2' X 2' FLUORESCENT LIGHT		EXHAUST
	2' X 4' FLUORESCENT LIGHT		CURTAIN TRACK
	RECESSED CAN LIGHT		SHOWER CURTAIN
	1' X 4' STRIP LIGHT		GYPSUM BOARD CEILING ON METAL FRAMING
	AREA NOT IN CONTRACT		RADIANT HEAT PANEL

NOTE: ALL SYMBOLS MAY NOT BE USED

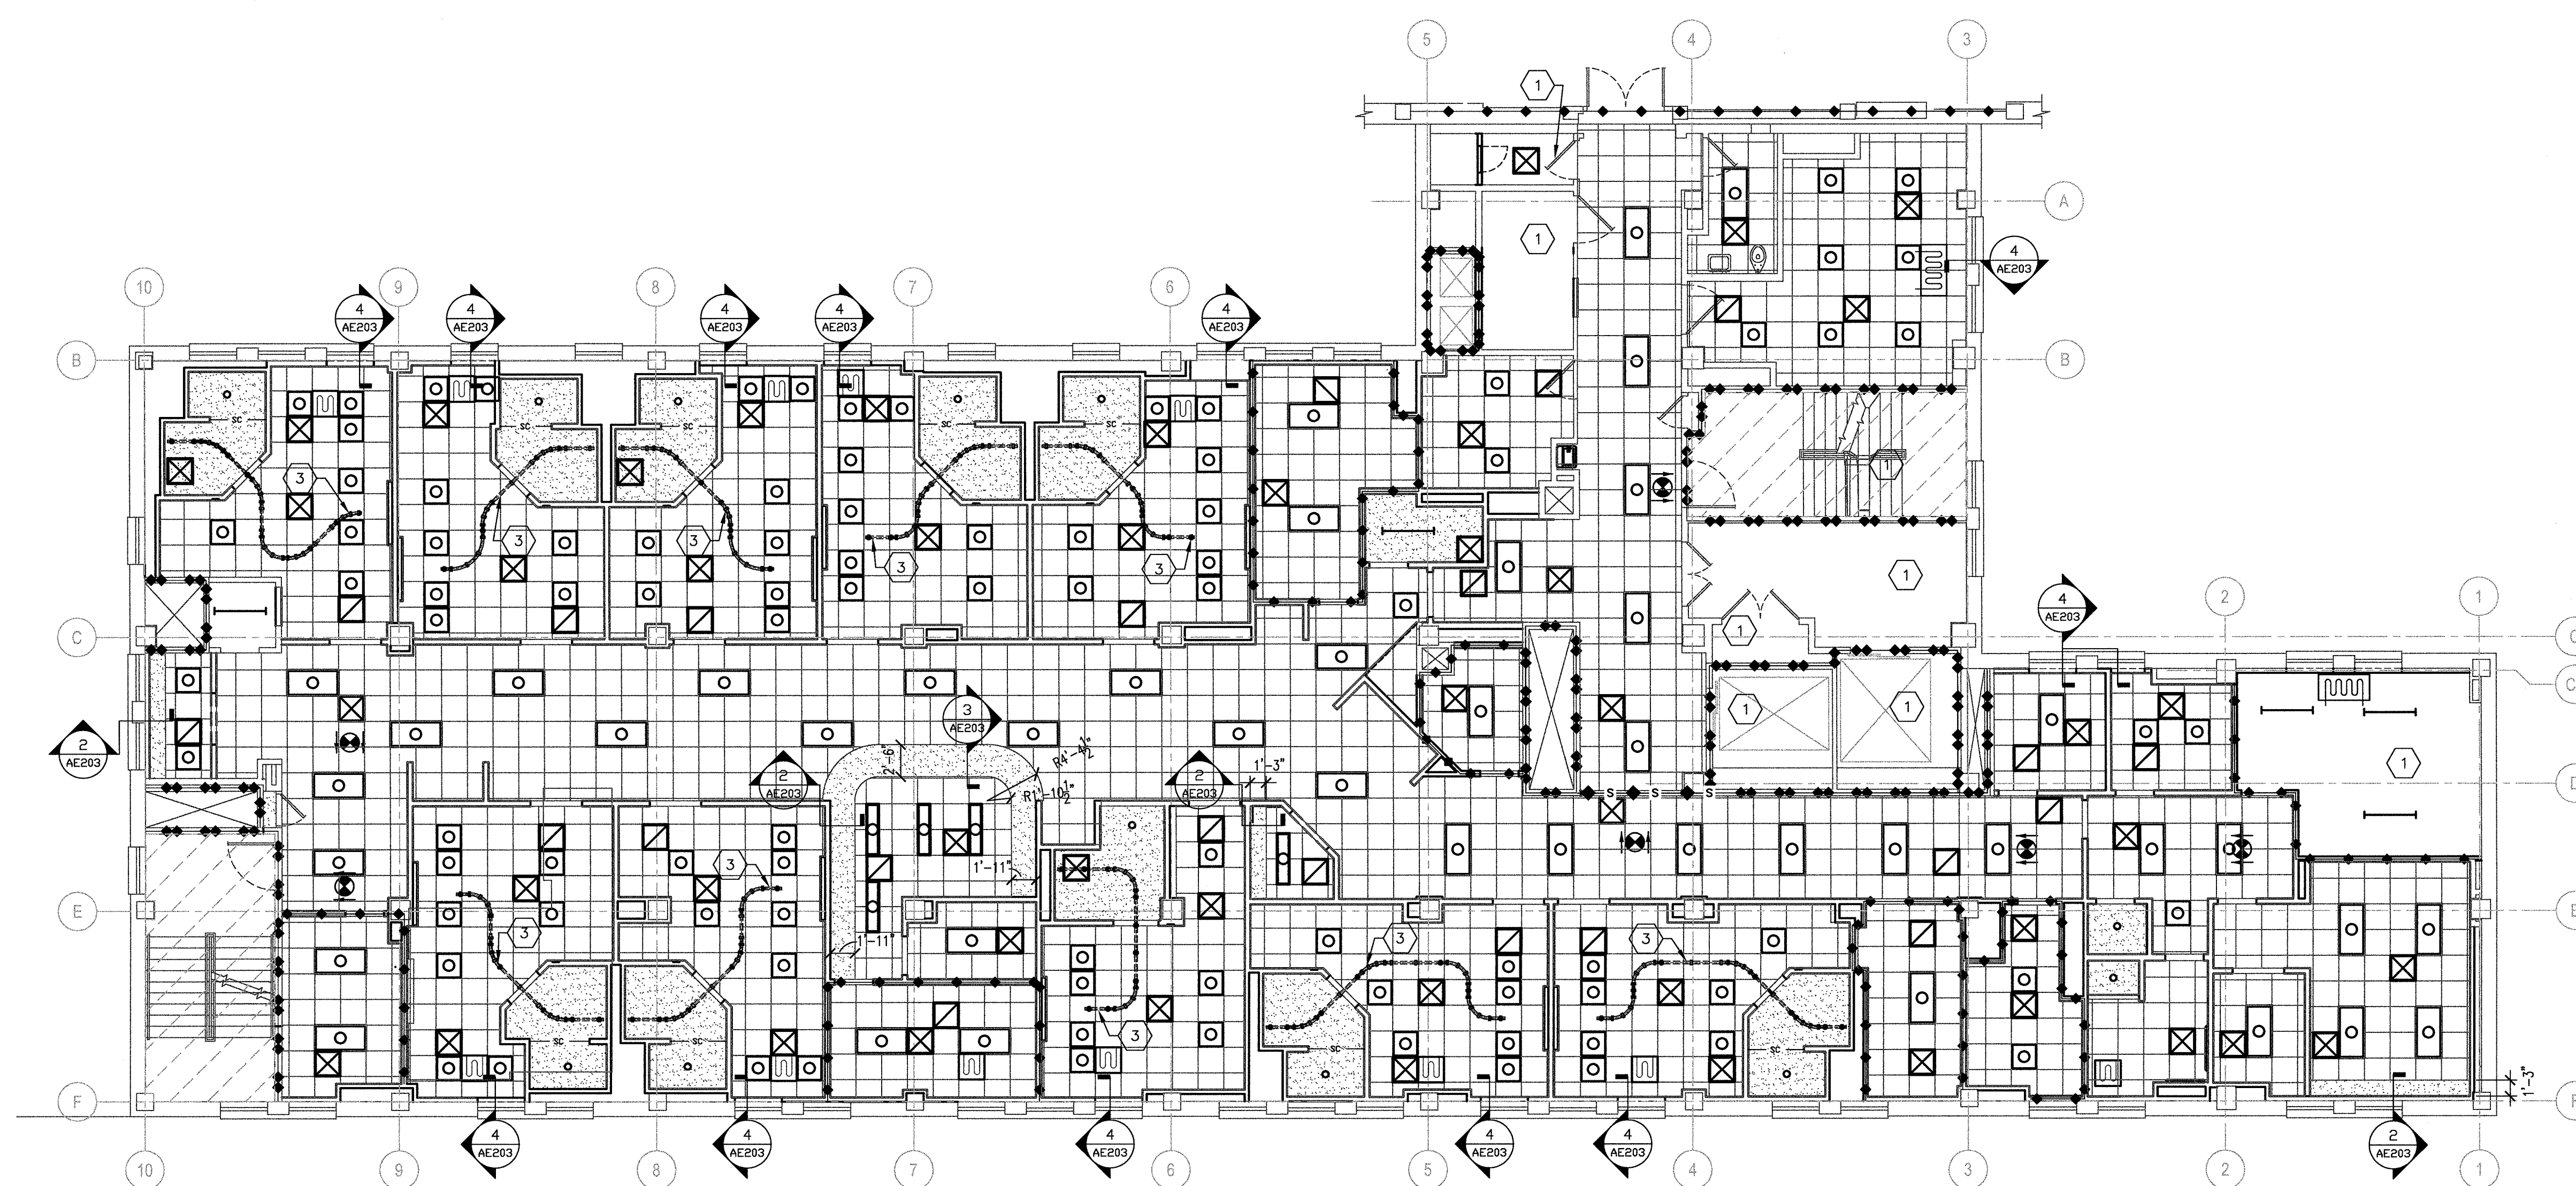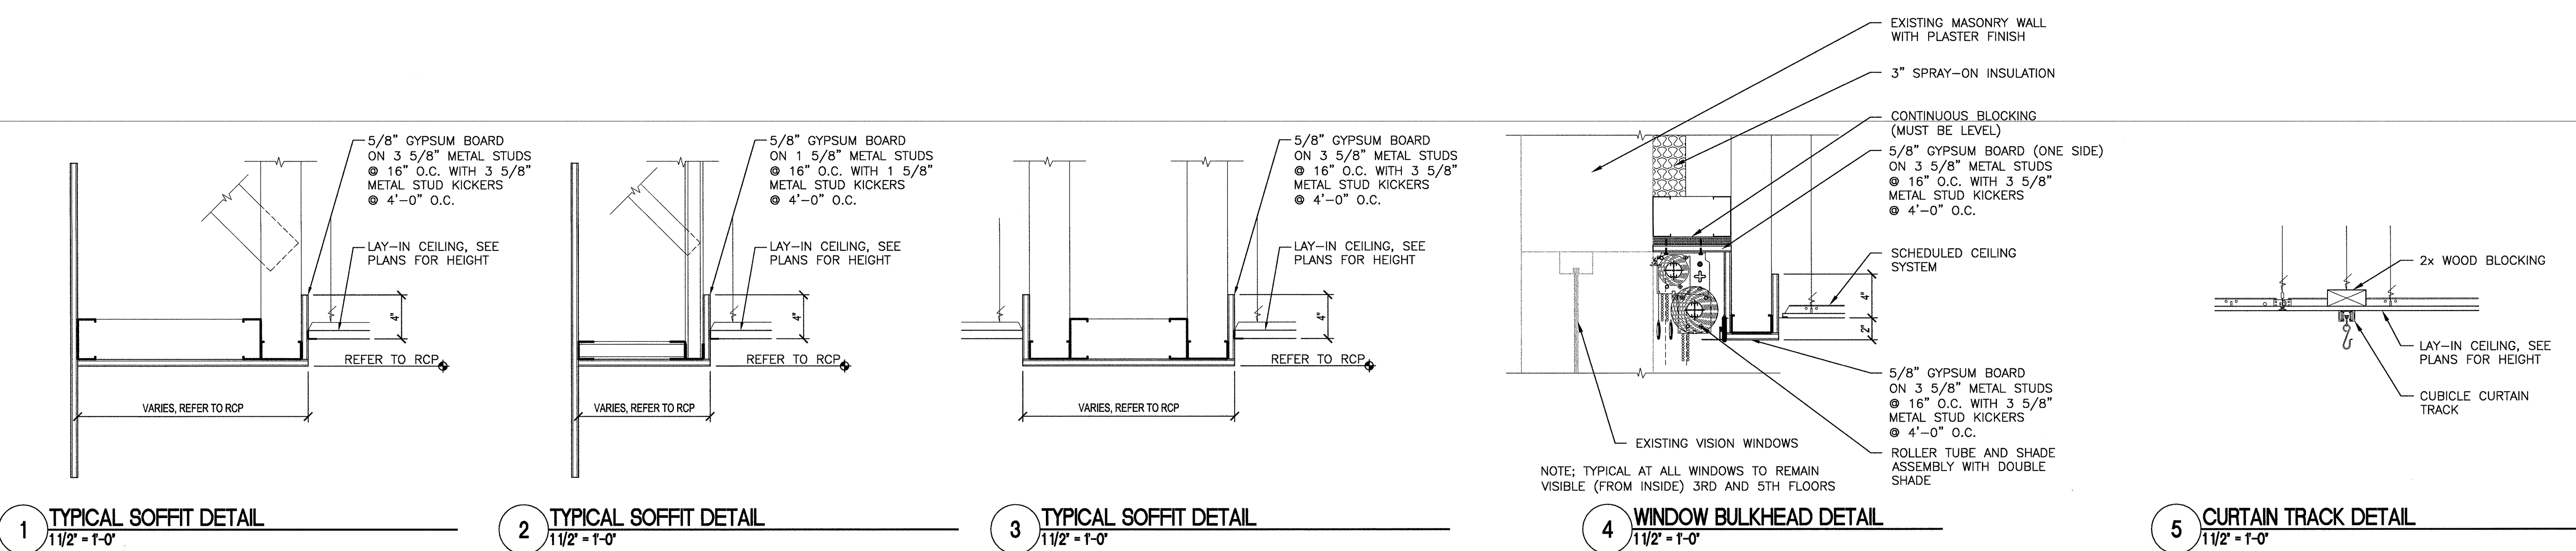













F1 THIRD FLOOR REFLECTED CEILING PLAN
SCALE 1/8" = 1'-0"

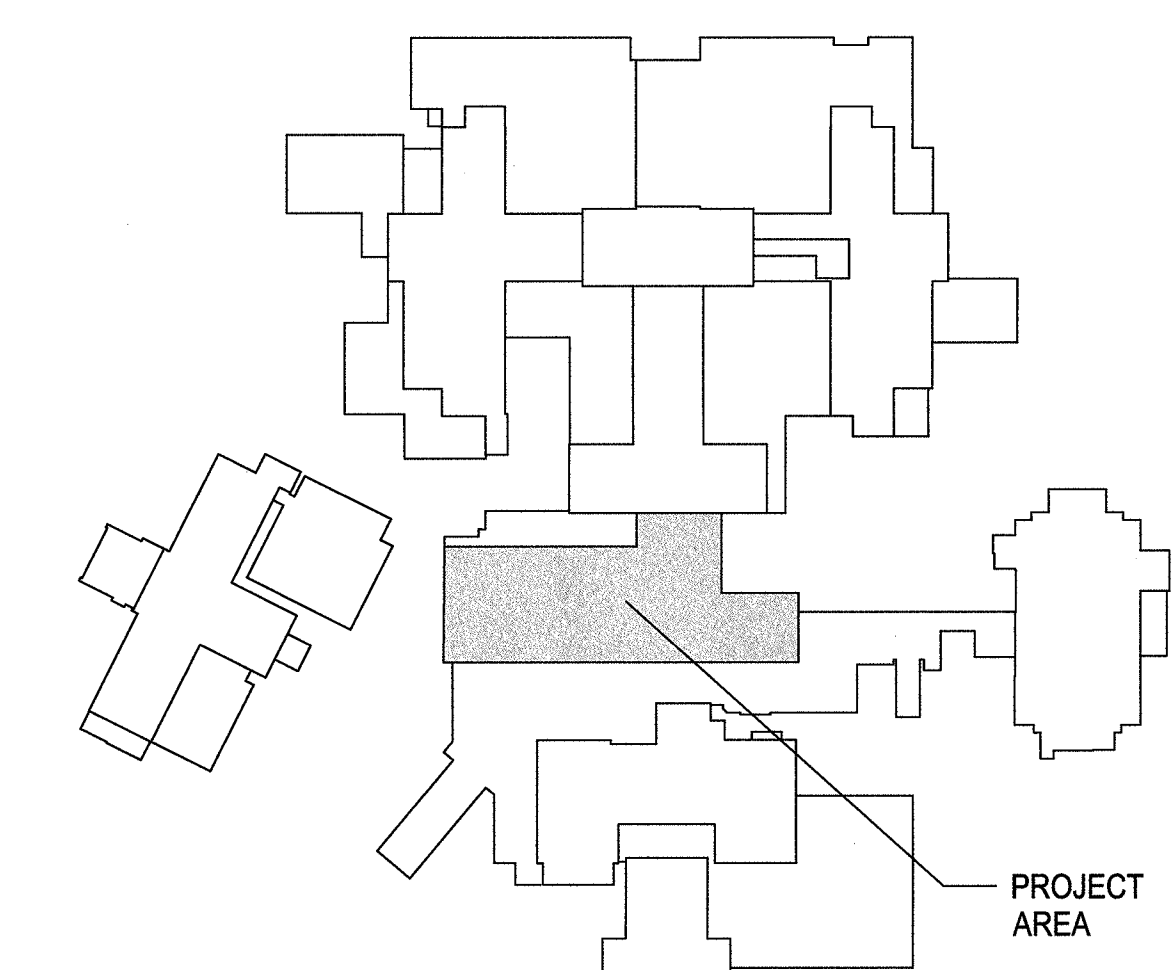

KEY PLAN - THIRD FLOOR
NTS

FULLY SPRINKLED

		CONSULTANT	ARCHITECT/ENGINEER OF RECORD	STAMP 	Office of Construction and Facilities Management VA U.S. Department of Veterans Affairs	Drawing Title THIRD FLOOR REFLECTED CEILING PLAN Approved: Project Director	Phase ISSUED FOR CONSTRUCTION FULLY SPRINKLERED	Project Title REMODEL ICU - TELEMETRY FOR PATIENT PRIVACY Location VA MEDICAL CENTER 3800 30TH ST, DES MOINES, IOWA 50309	Project Number 636A6-18-313 Building Number IW Drawing Number AE203
Revisions:	Date:							Issue Date 12-06-2019	Checked BW Drawn TLC

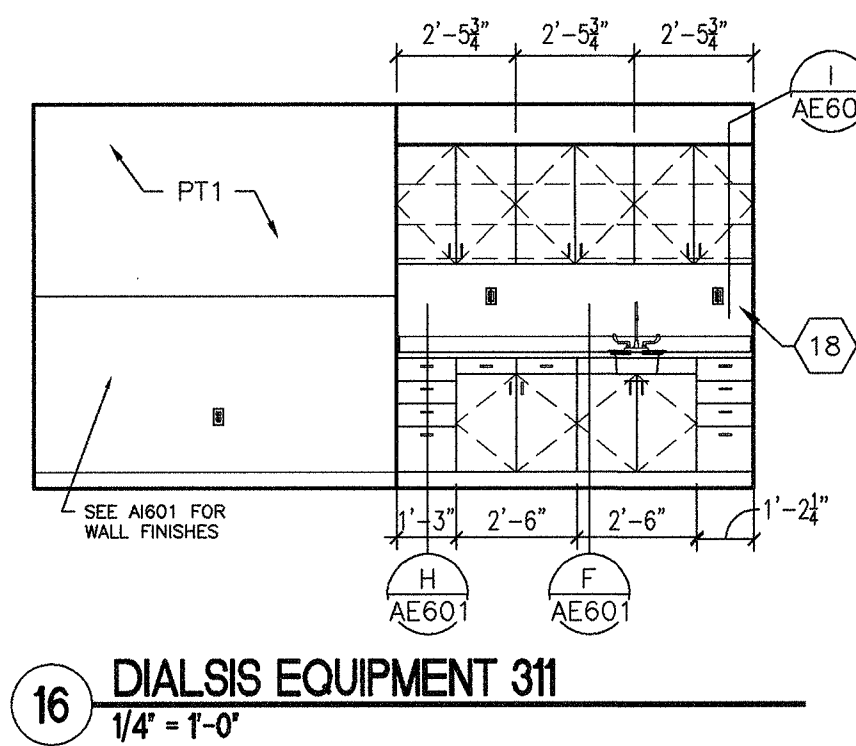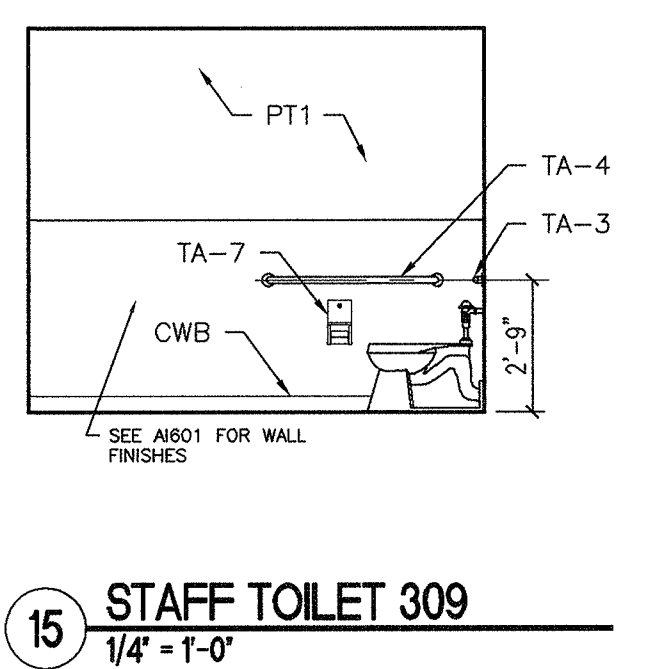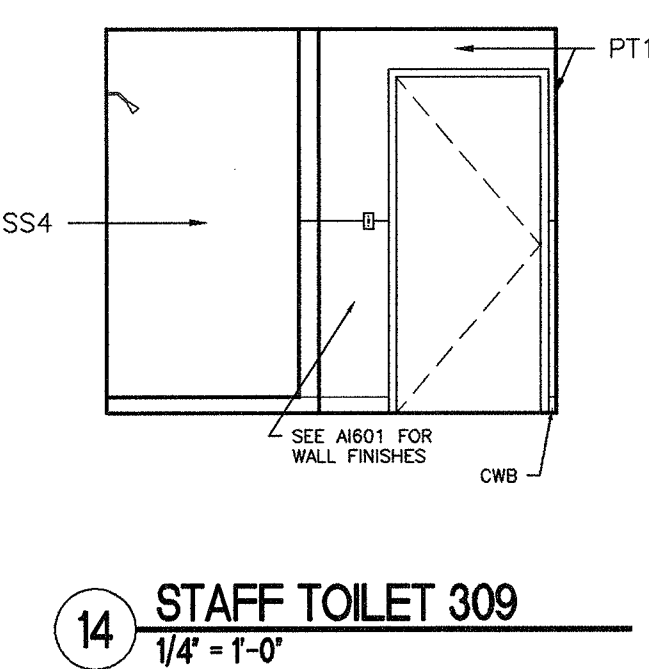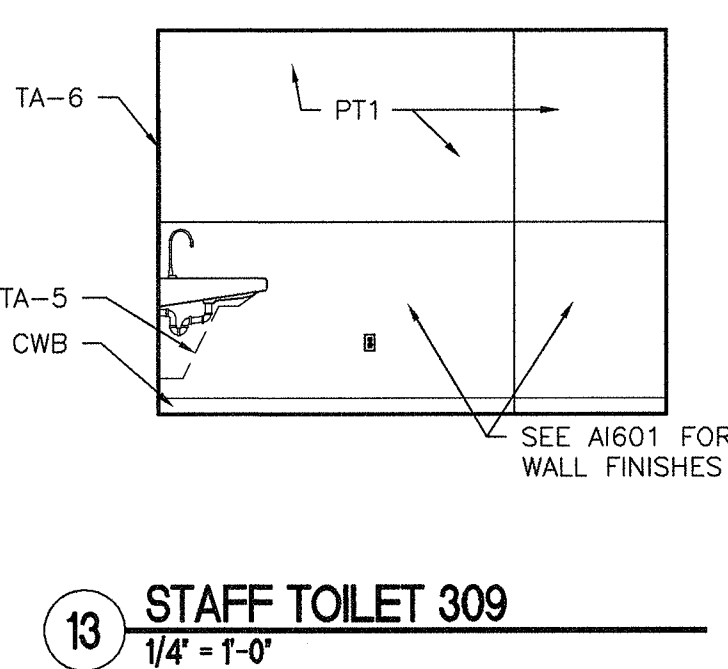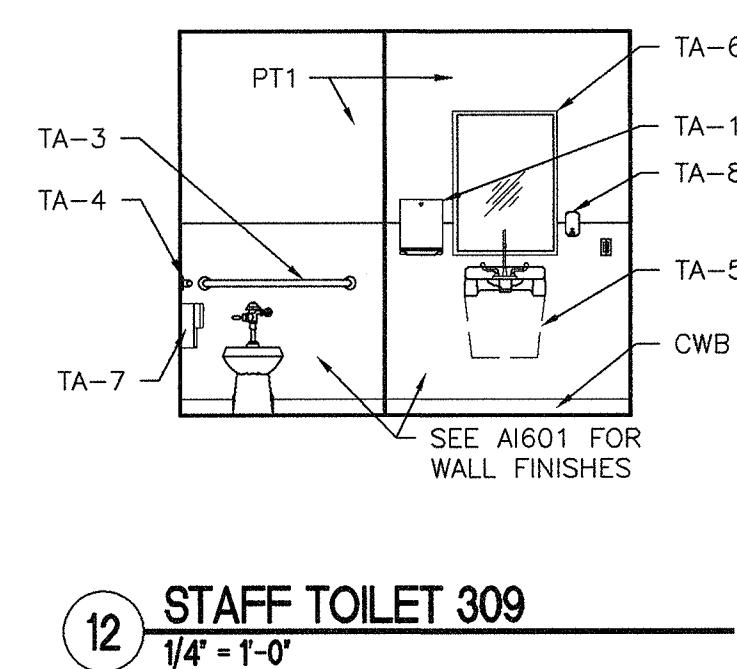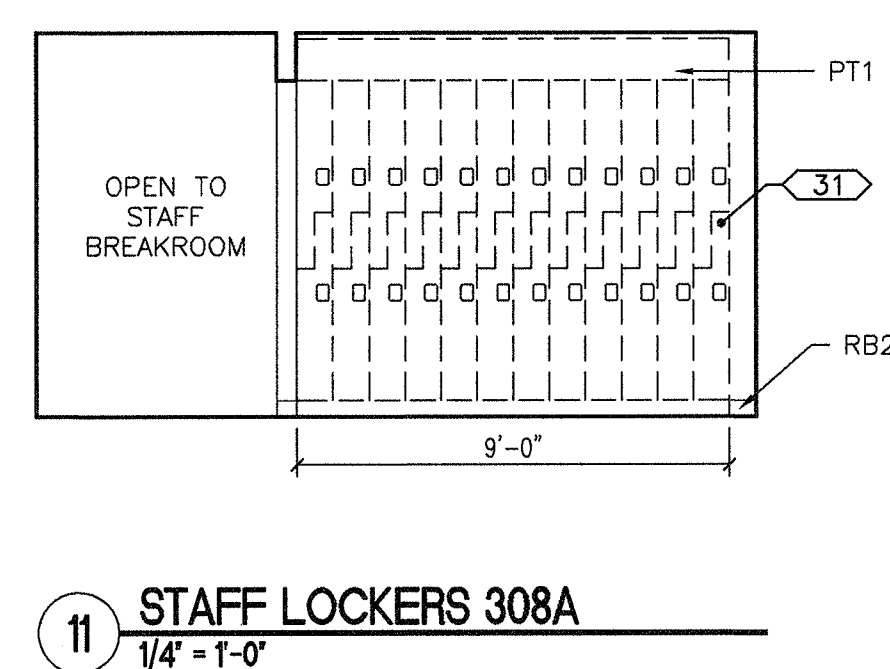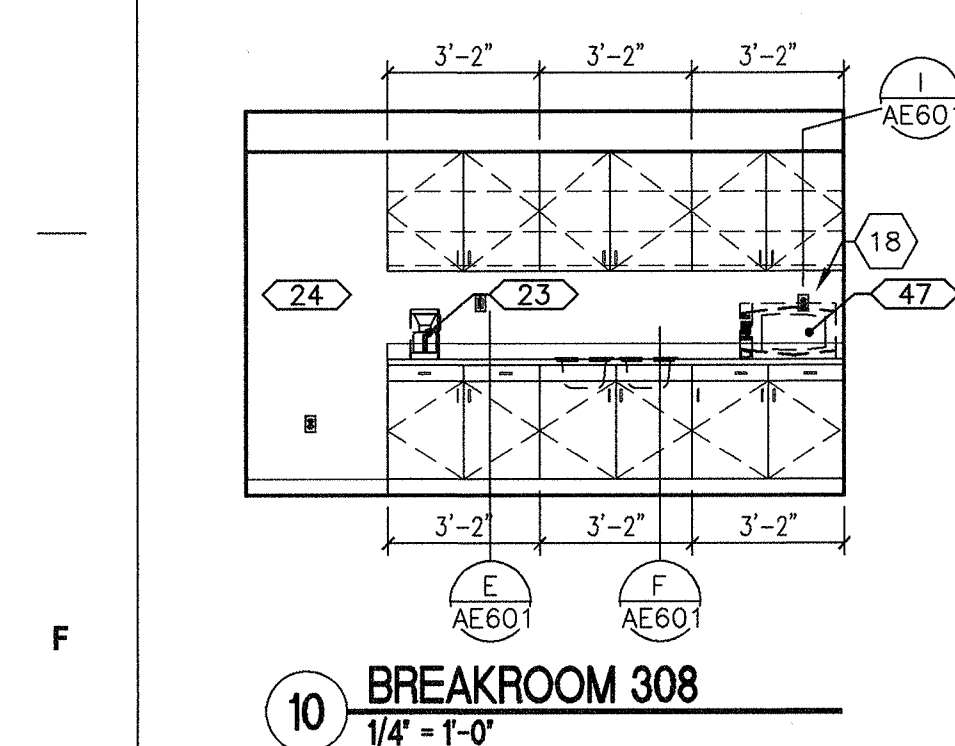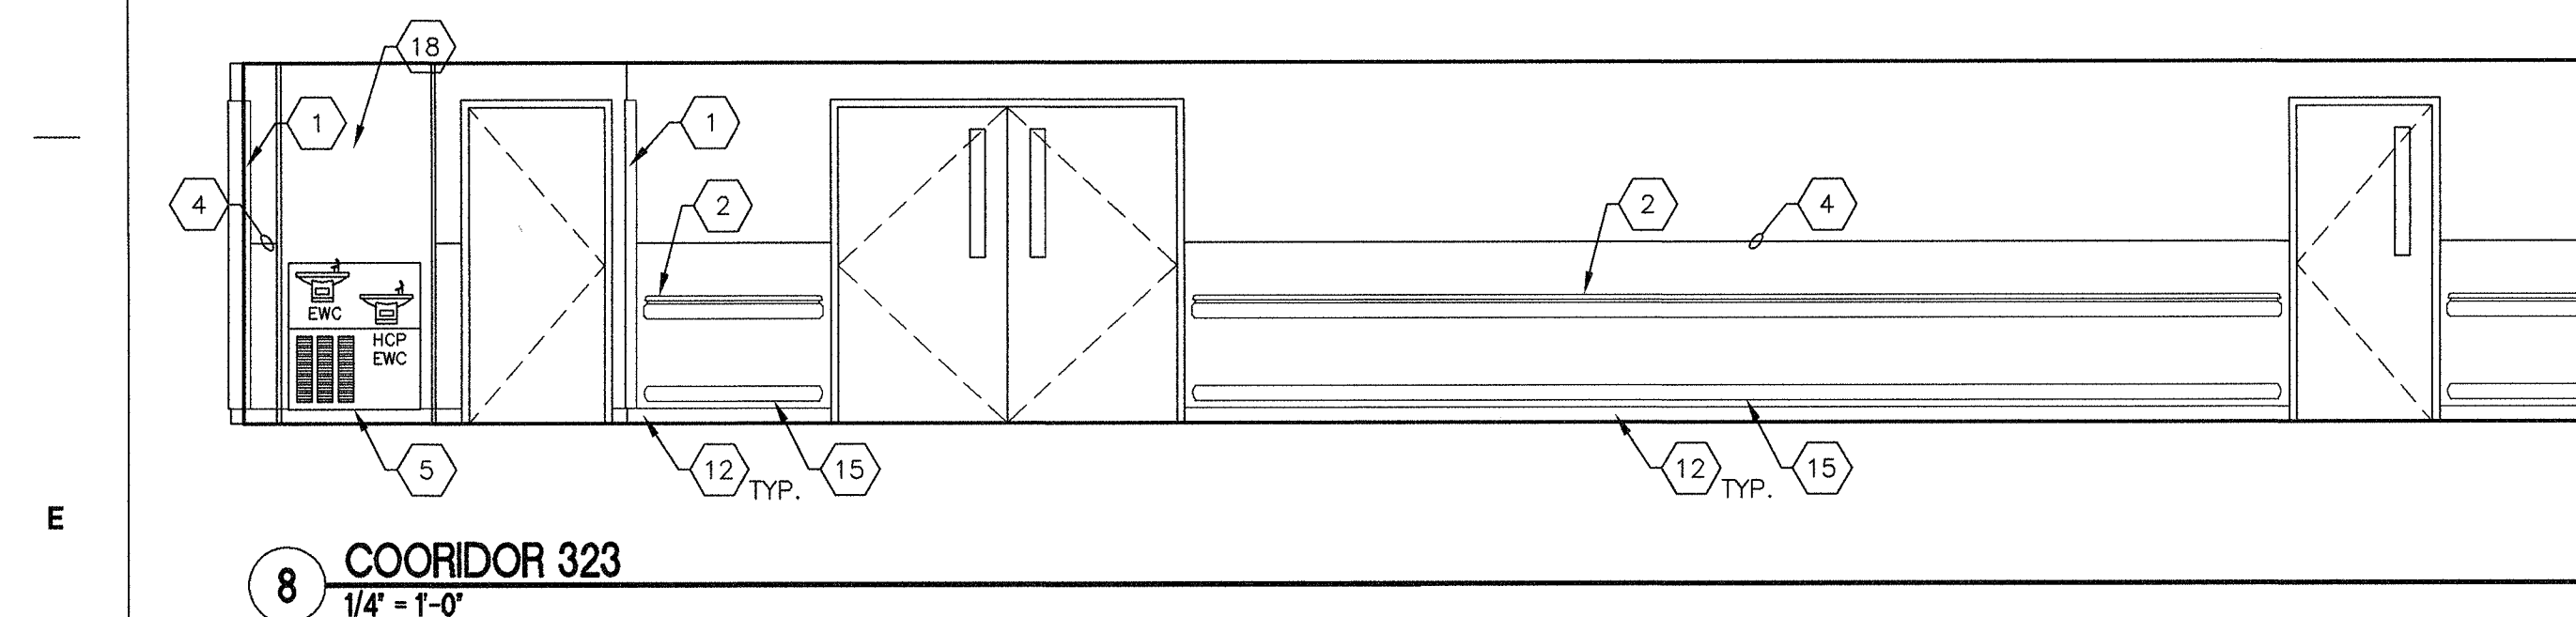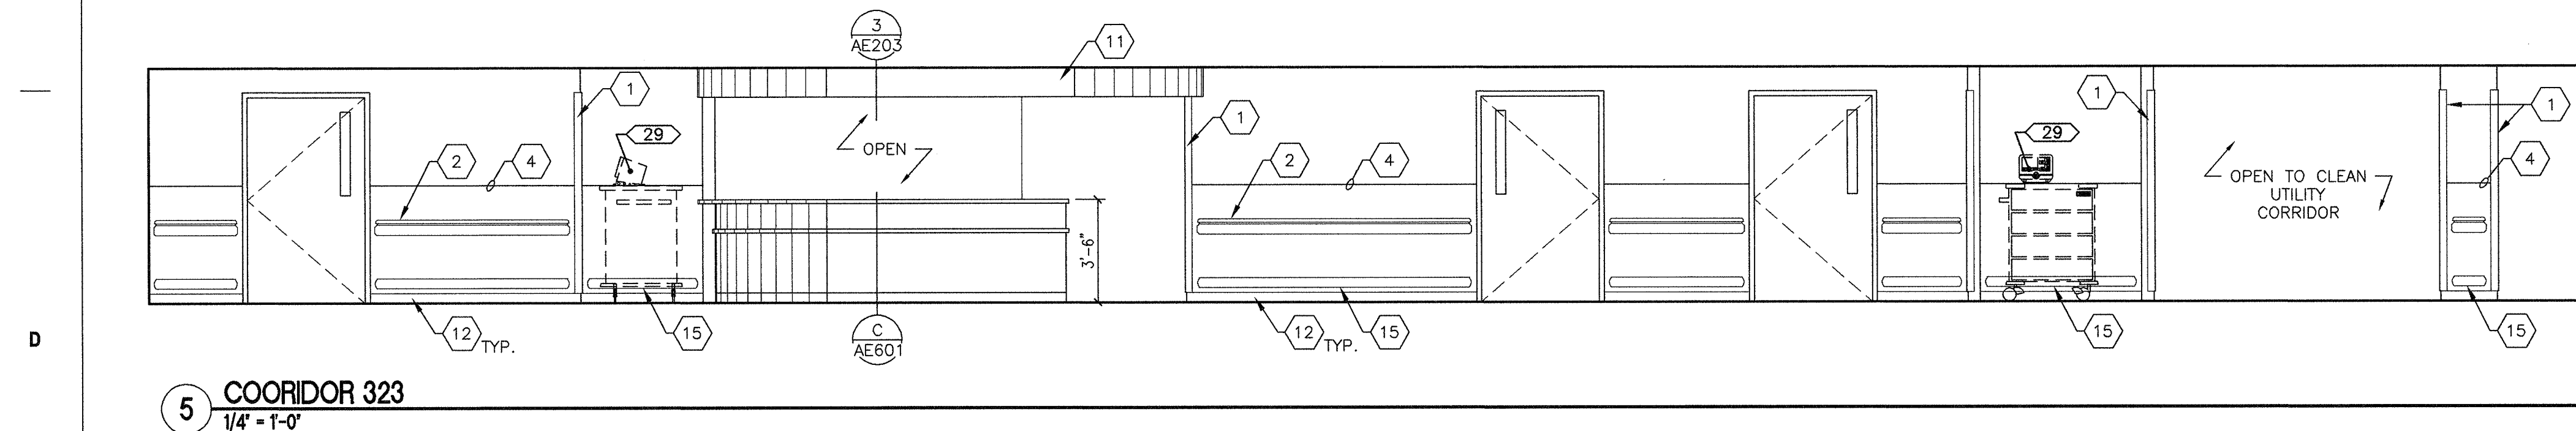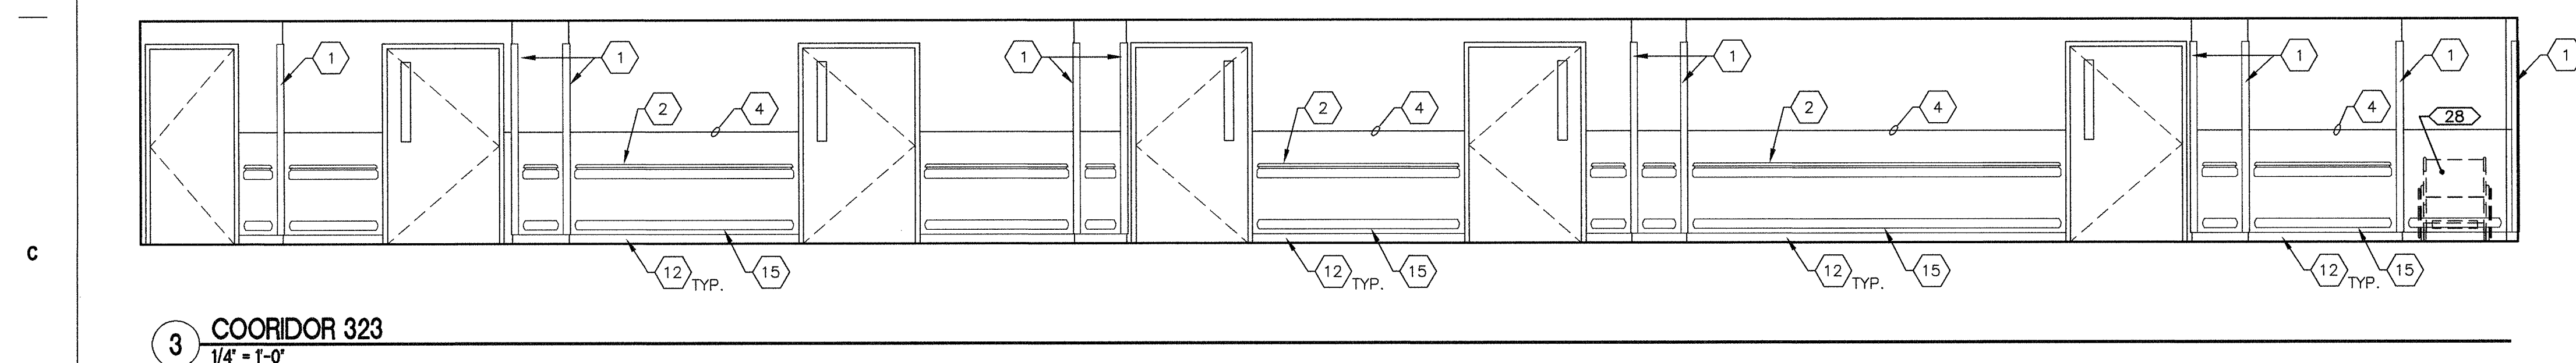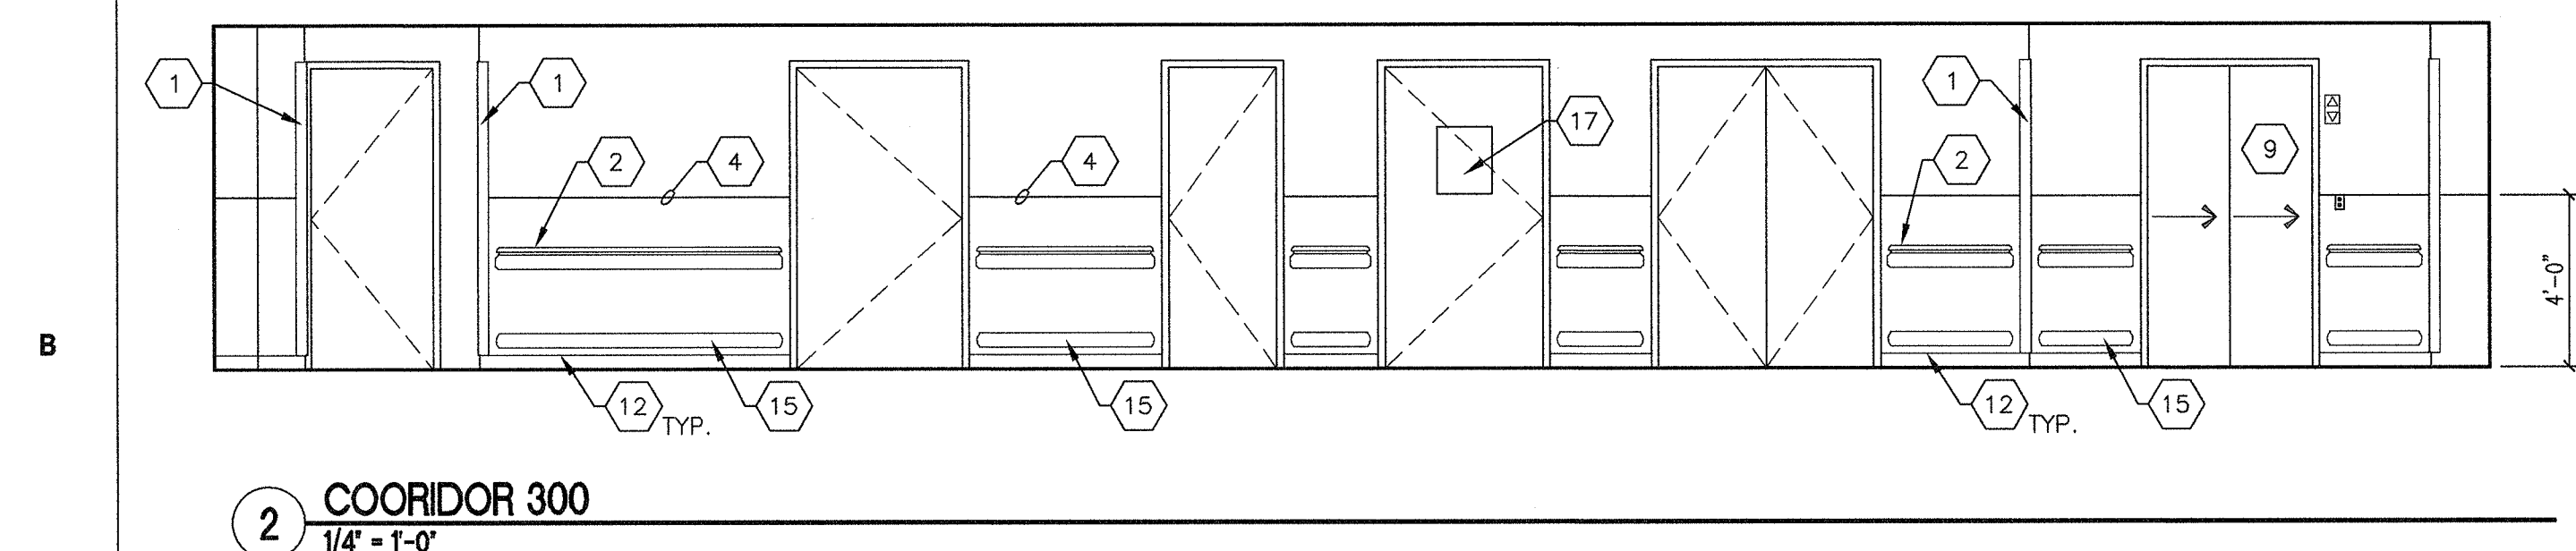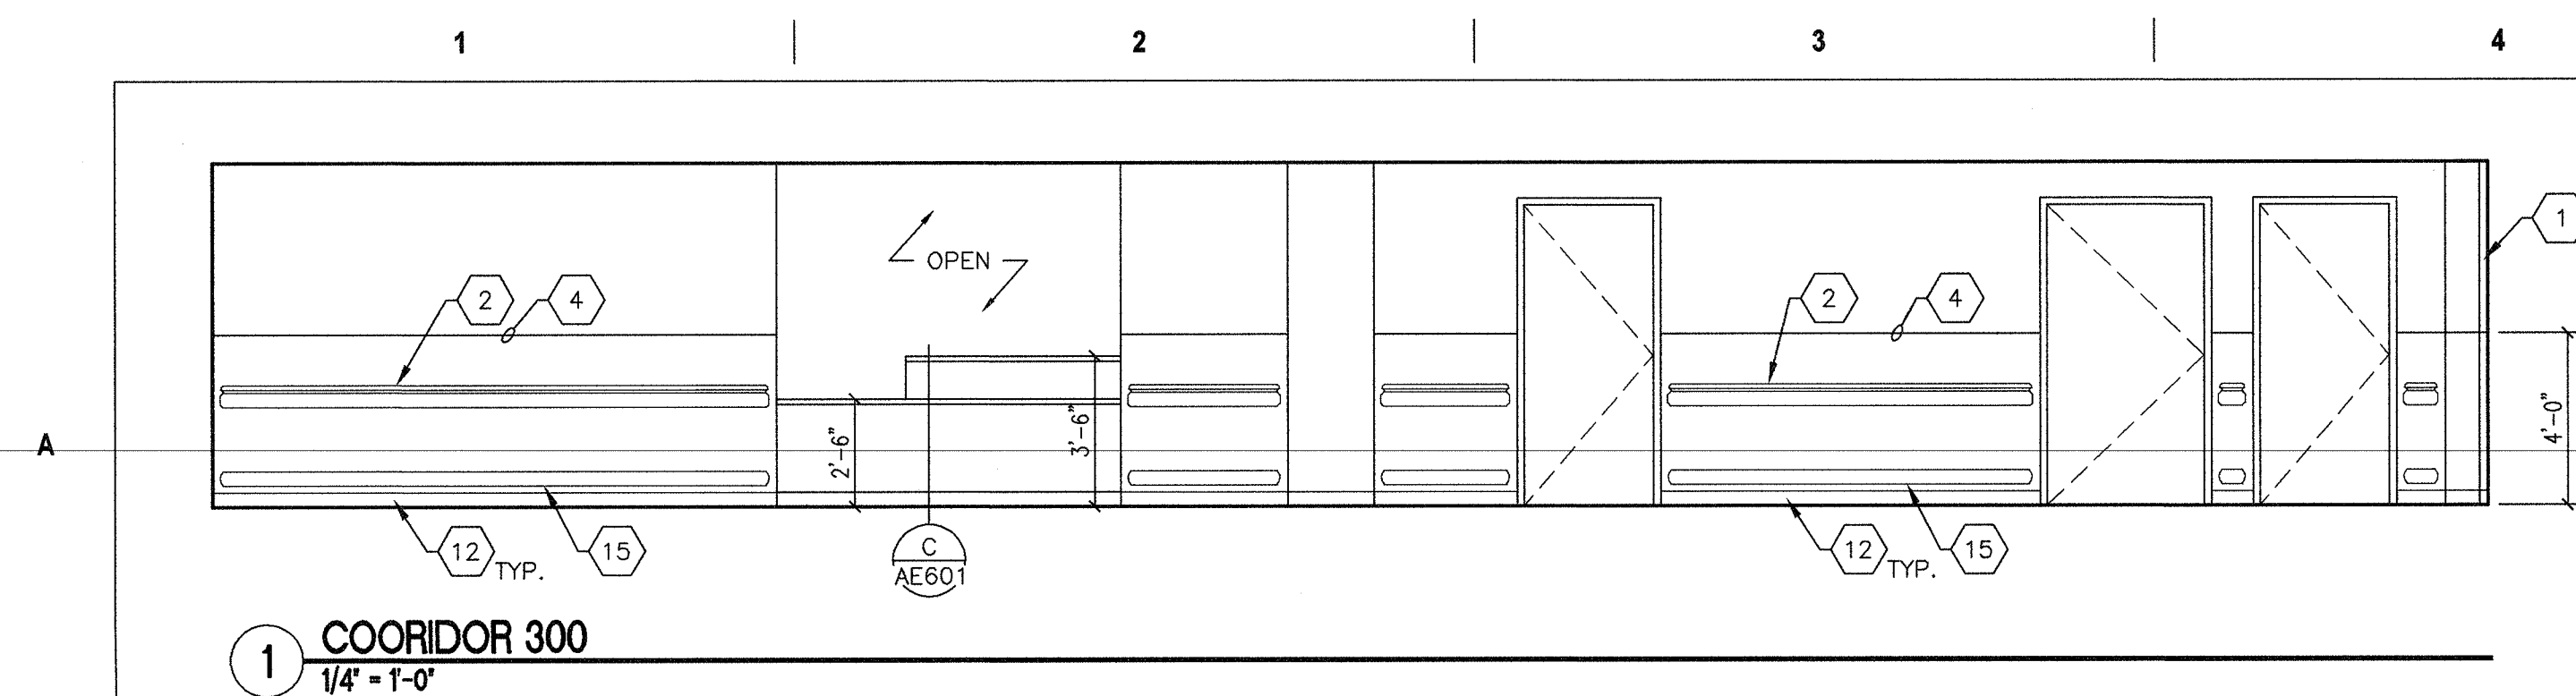


TOILET ACCESSORIES SCHEDULE	
ITEM	NAME
TA-1	18" GRAB BAR
TA-2	26" GRAB BAR (SWING UP) WITH TOILET PAPER HOLDER
TA-3	36" GRAB BAR
TA-4	42" GRAB BAR
TA-5	SINK-KNEE-GUARD
TA-6	MIRROR
TA-7	TOILET PAPER DISPENSER
TA-8	SOAP DISPENSER
TA-9	COAT HOOK
TA-10	PAPER TOWEL DISPENSER
TA-11	SHELF
TA-12	NURSE CALL
TA-13	SOAP DISH
TA-14	24" GRAB BAR
TA-15	REVERSIBLE FOLDING SHOWER SEAT
TA-16	TWO-WALL GRAB BAR

EQUIPMENT SCHEDULE				
ITEM	JSN	NAME	PROVIDED BY	INSTALLED BY
1		PATIENT BED W/ OVERBED TABLE	VA	VA
2		IV STAND	VA	VA
3		SLEEPER COUCH/CHAIR	VA	VA
4		TABLE	VA	VA
5		HEADWALL UNIT	GC	GC
6		GLUCOSE ANALYZER	VA	VA
7		LINEN HAMPER	VA	VA
8		WASTE RECEPTACLE	VA	VA
9		BEDSIDE CHARTING	VA	VA
10		STORAGE CART	VA	VA
11		WHITEBOARD, SMALL	VA	VA
12		WHITE BOARD, LARGE	GC	GC
13		GLOVE DISPENSER	VA	VA
14		TELEVISION	VA	VA
15		SHARPS DISPOSAL	VA	VA
16		SHELF UNIT	VA	VA
17		COMPUTER	VA	VA
18		HEADWALL SYSTEM BOOM (CEILING)	GC	GC
19		MEDICATION DISTRIBUTION SYSTEM (OMNI)	VA	VA
20		ICE MAKER	VA	GC
21		CARDIAC MONITOR	VA	VA
22		TELEMETRY ICU CAMERA (CEILING)	VA	VA
23		COFFEE BREWER	VA	VA
24		REFRIGERATOR	VA	VA
25		PRINTER / FAX	VA	VA
26		ADJUSTABLE NURSE CHAIR	VA	VA
27		STRETCHER	VA	VA
28		WHEELCHAIR	VA	VA
29		CRASH CART	VA	VA
30		CHAIR-RECLINER	VA	VA
31		LOCKERS	VA	VA
32		CHANGING CHAIR	VA	VA
33		PERSONNEL PROTECTION EQUIPMENT	VA	VA
34		DIALYSIS BOX	VA	VA
35		OFFICE CHAIR	VA	VA
36		CCTV MONITORS	VA	VA
37		DIALYSIS MACHINE	VA	VA
38		LARGE FLAT SCREEN MONITOR	VA	VA
39		(2) FLAT SCREEN MONITORS, (1 OVER 1)	VA	VA
40		MONITOR BRACKET, TILT/ANGLE	VA	VA
41		LINEN CART	VA	VA
42		X-RAY MACHINE	VA	VA
43		UNDER COUNTER REFRIGERATOR	VA	VA
44		TRANSPORT MONITOR	VA	VA
45		EKG MACHINE	VA	VA
46		SHELVING	VA	VA
47		MICROWAVE	VA	VA
48		HARD PIPED COFFEE MAKER	VA	GC
49		LAPTOP COMPUTER	VA	VA

INTERIOR ELEVATION NOTES

1. CORNER GUARD. REFER TO DETAIL 8/AI501 FOR ADDITIONAL INFORMATION.
2. HAND RAIL. REFER TO DETAIL 5/AI501 FOR ADDITIONAL INFORMATION.
3. CEILING MOUNTED PATIENT LIFT.
4. WALL PROTECTION. REFER TO FINISH PLANS FOR ADDITIONAL INFORMATION.
5. HI-LO WATER FOUNTAIN.
6. MOP SINK.
7. FIRE EXTINGUISHER CABINET.
8. OVER BED LIGHT. REFER TO LIGHTING PLANS FOR ADDITIONAL INFORMATION.
9. ELEVATOR DOOR.
10. PRIVACY CURTAIN.
11. GYPSUM BOARD SOFFIT.
12. WALL BASE. REFER TO FINISH PLANS FOR ADDITIONAL INFORMATION.
13. SOLID SURFACE WALL PANELING. REFER TO FINISH PLANS FOR ADDITIONAL INFORMATION.
14. RUBBER CHAIR RAIL. REFER TO FINISH PLANS FOR ADDITIONAL INFORMATION.
15. CRASH RAIL. REFER TO DETAIL 6/AI501 FOR ADDITIONAL INFORMATION.
16. METAL TILE FINISHING EDGE.
17. EXIT SIGNAGE.
18. MOSAIC TILE. REFER TO FINISH PLANS AND LEGEND.

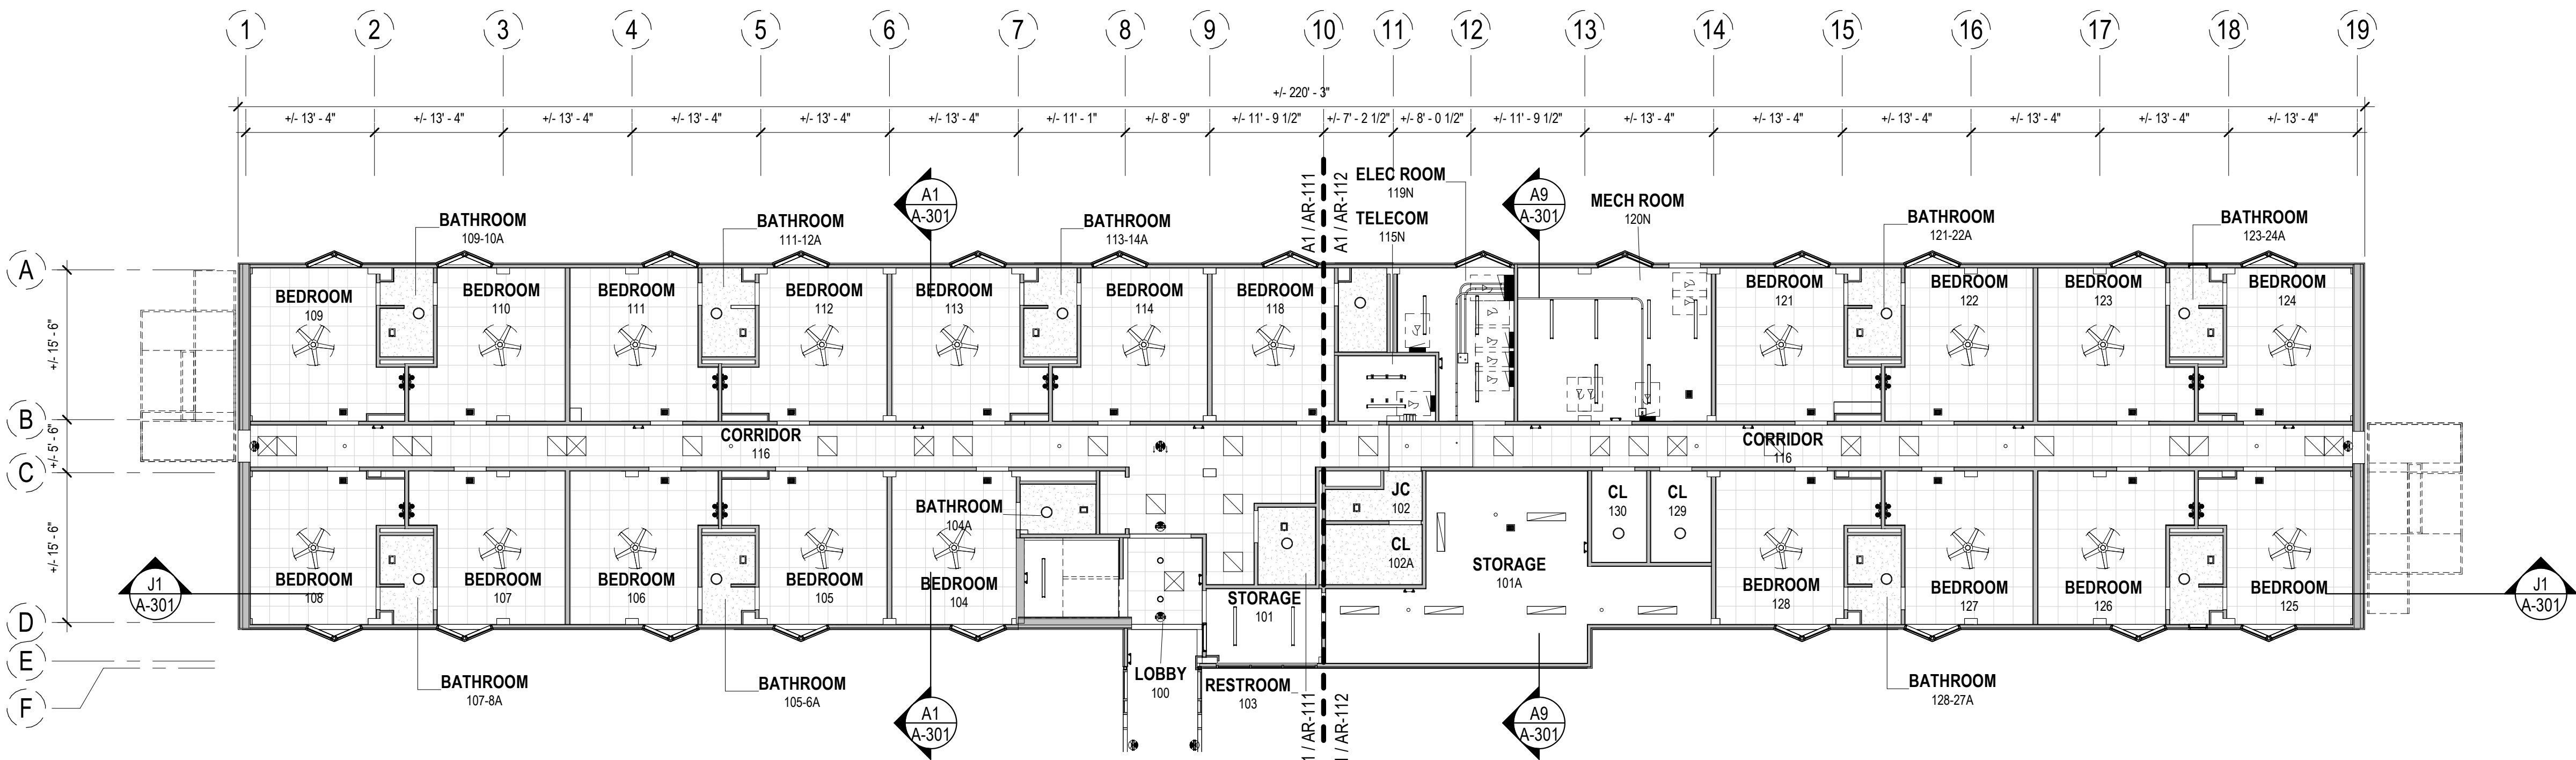

A1 PLAN
3/32" = 1'-0"

$$3/32'' = 1'-0''$$


- 

US AIR FORCE CIVIL ENGINEER CENTER
MCGUIRE AFB
LAKEHURST, NEW JERSEY

	2x2' ACOUSTICAL CEILING PANEL
	2x4 ACOUSTICAL CEILING PANEL
	PAINTED GYPSUM WALLBOARD CEILING
	PAINTED EXPOSED STRUCTURE
	TELEVISION SEE E-SERIES
	CEILING FAN
	MECHANICAL DIFFUSER SEE M-SERIES
	MECHANICAL GRILLE SEE M-SERIES
	MECHANICAL FIXTURE SEE M-SERIES
	LIGHTING FIXTURES SEE E-SERIES
	ILLUMINATED EXIT SIGN SEE E-SERIES
	SECURITY CAMERA SEE E-SERIES

The diagram shows a horizontal rectangular block divided into two equal halves. The left half is labeled 'A' and the right half is labeled 'B'. A vertical line separates the two halves. Below the block, there are two small vertical lines, one under each half, representing connections to a common ground or reference point.

NORTH ARROW

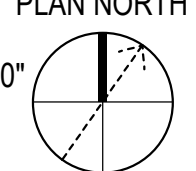

SHEET ID
AR-110

100% FINAL DESIGN SUBMITTAL

MARK	DESCRIPTION
Autodesk Descr: (H0817E IDMIN	Norm Descr: D2610 D2610DTE1 231010 D2610 A n4

2008-2009

