




three inches = one foot
one and one half inches = one foot
one inch = one foot
three quarters inch = one foot
one half inch = one foot
three eighths inch = one foot
one quarter inch = one foot
one eighth inch = one foot
one eighth inch = one foot

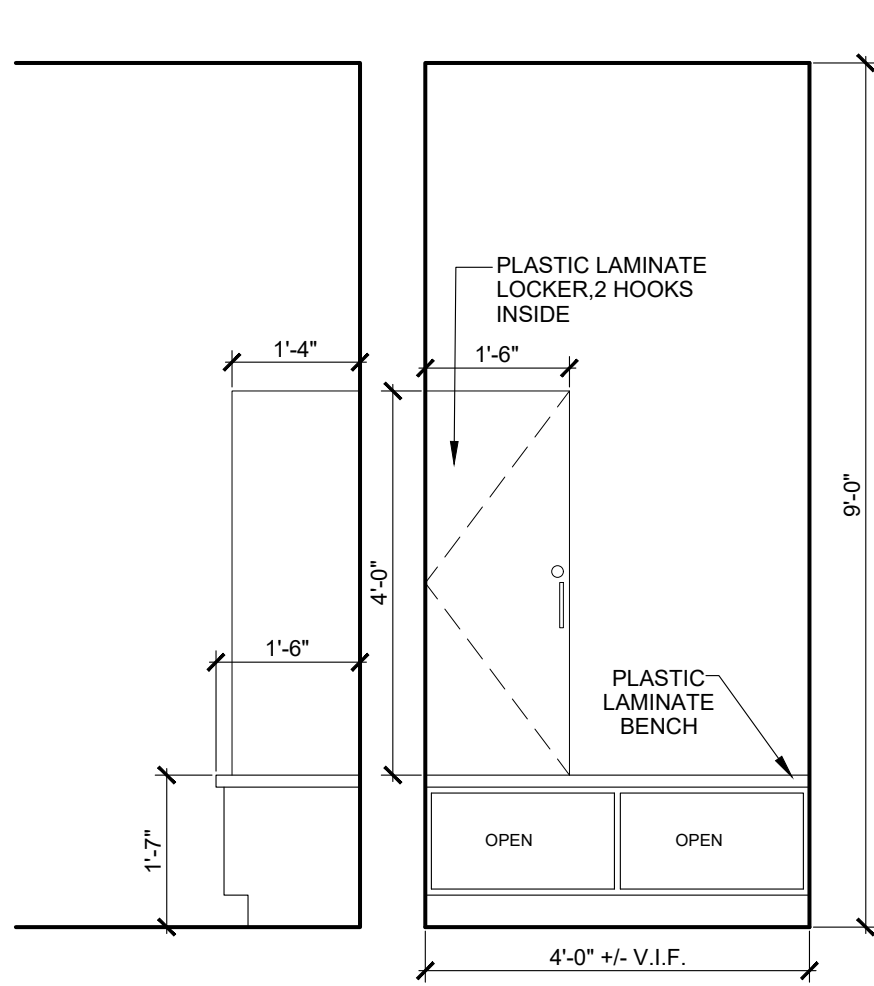


1 DRESS 101 ELEVATION
SCALE: 1/2" = 1'-0"

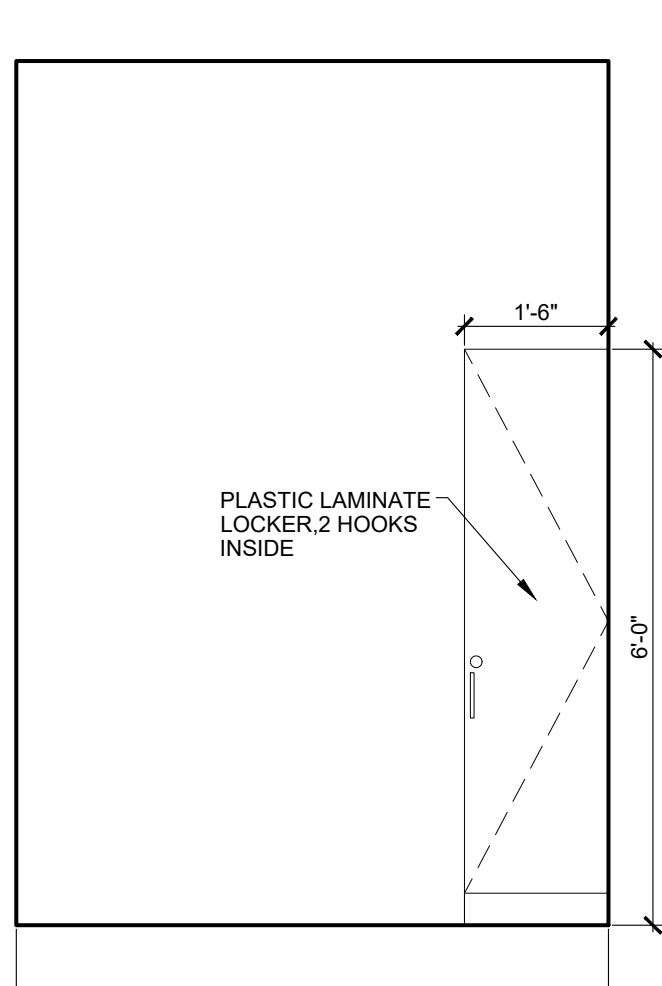


2 DRESS 102 ELEVATION
SCALE: 1/2" = 1'-0"

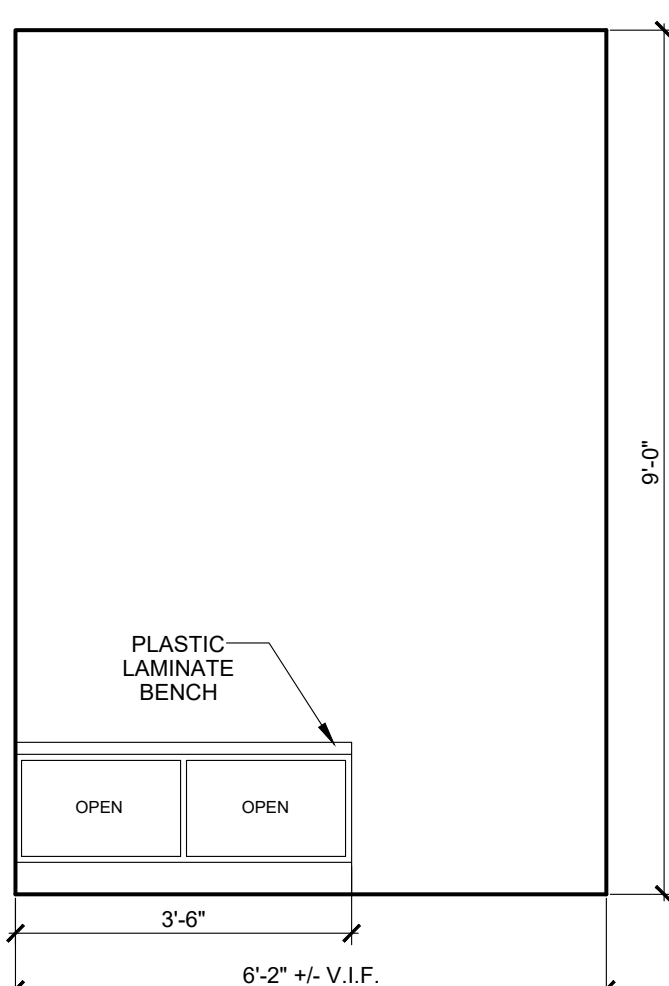


3 DRESS 102 ELEVATION
SCALE: 1/2" = 1'-0"

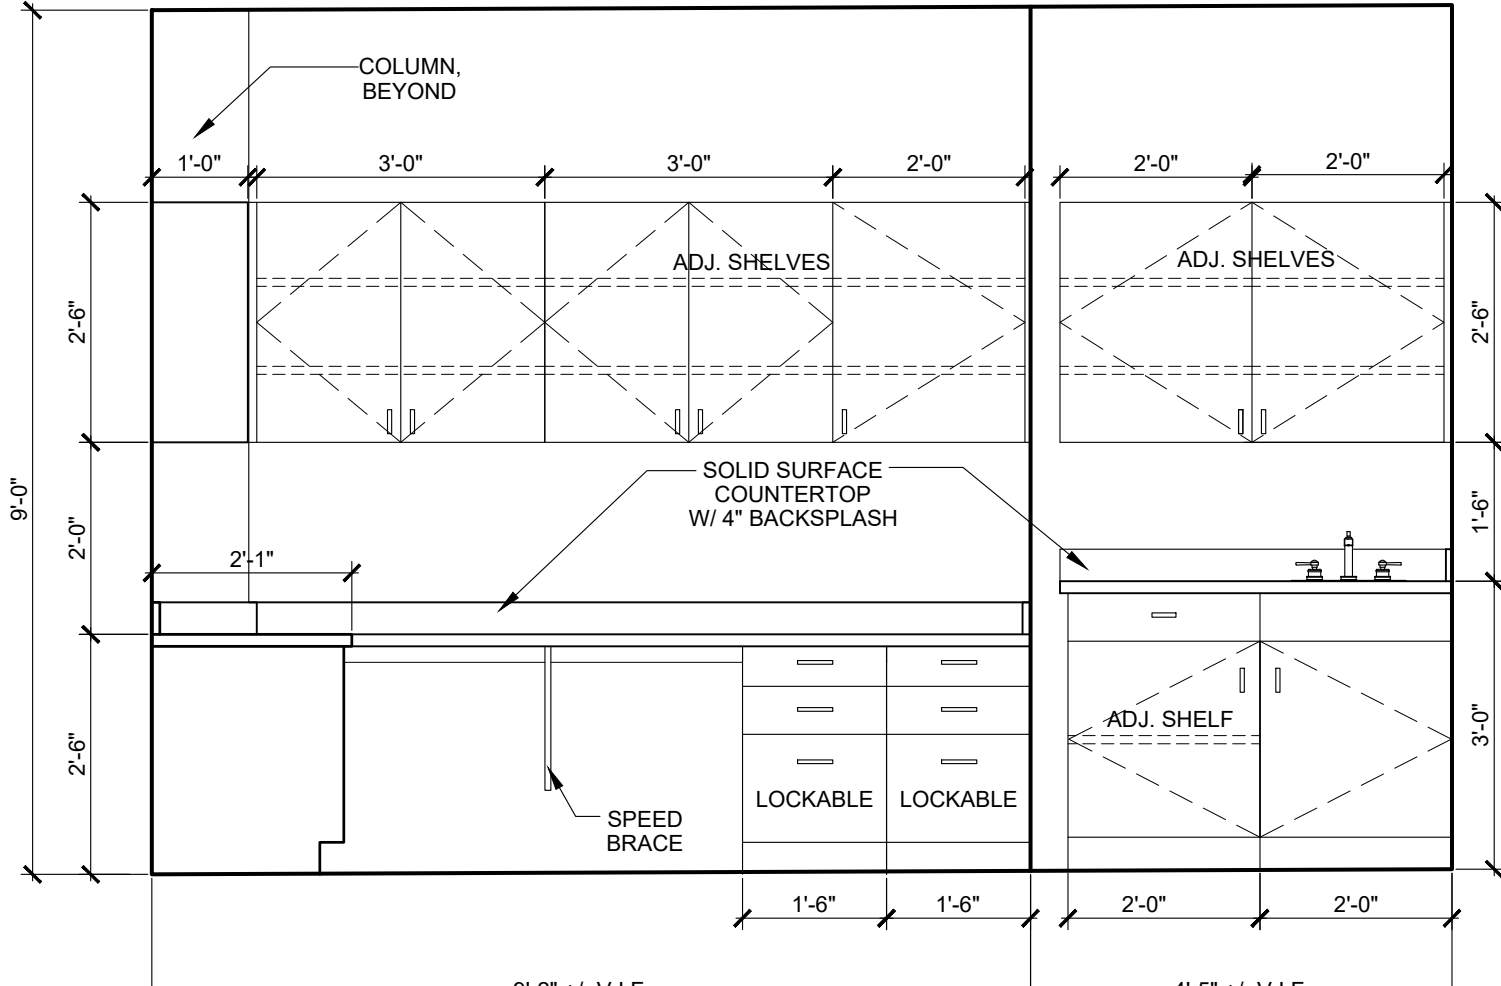


4 CONTROL ROOM 105
SCALE: 1/2" = 1'-0"

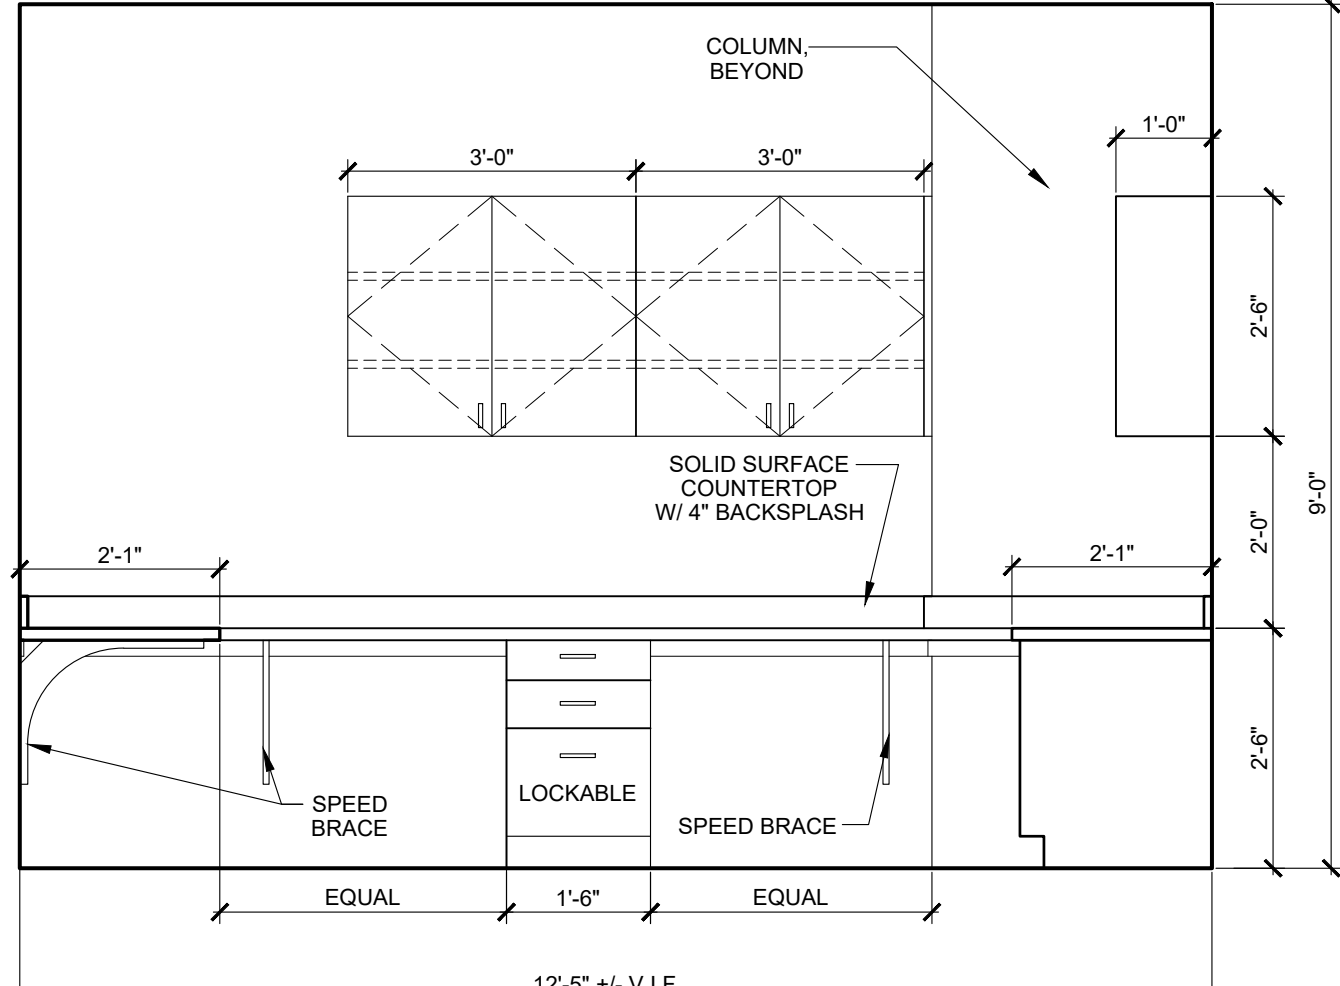


5 CONTROL ROOM 105
SCALE: 1/2" = 1'-0"

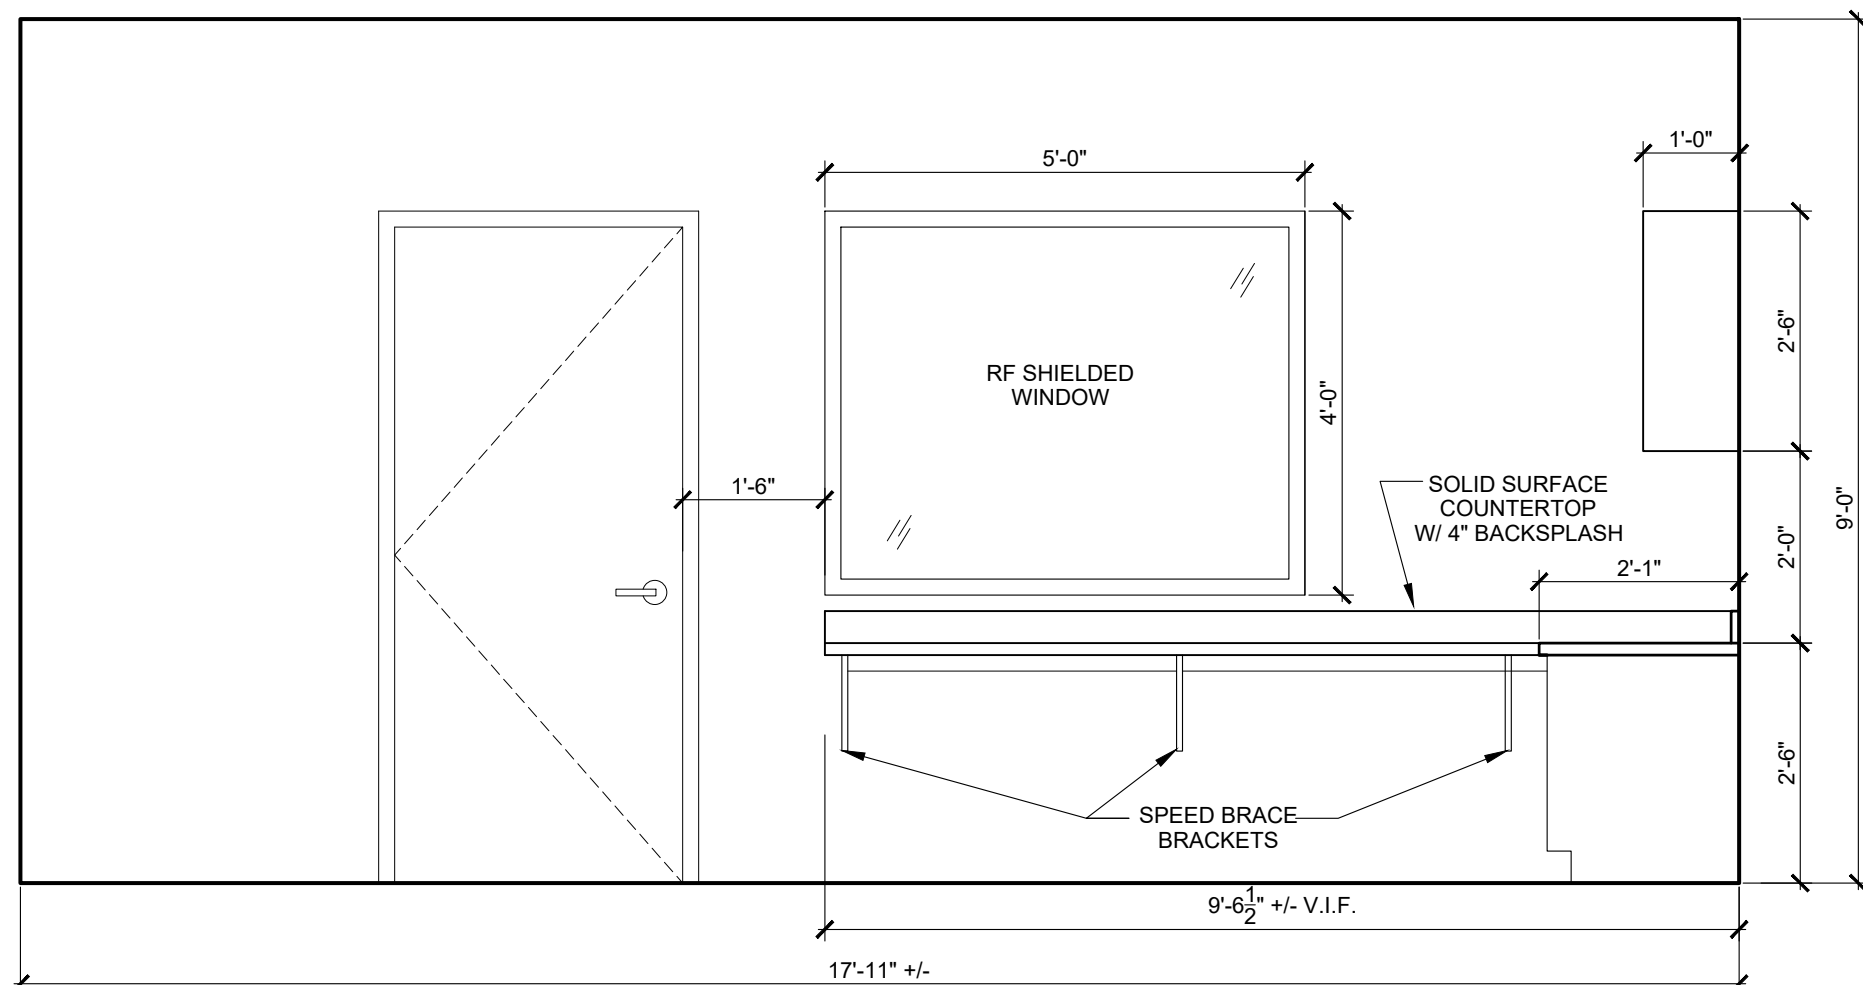

6 CONTROL ROOM 105
SCALE: 1/2" = 1'-0"

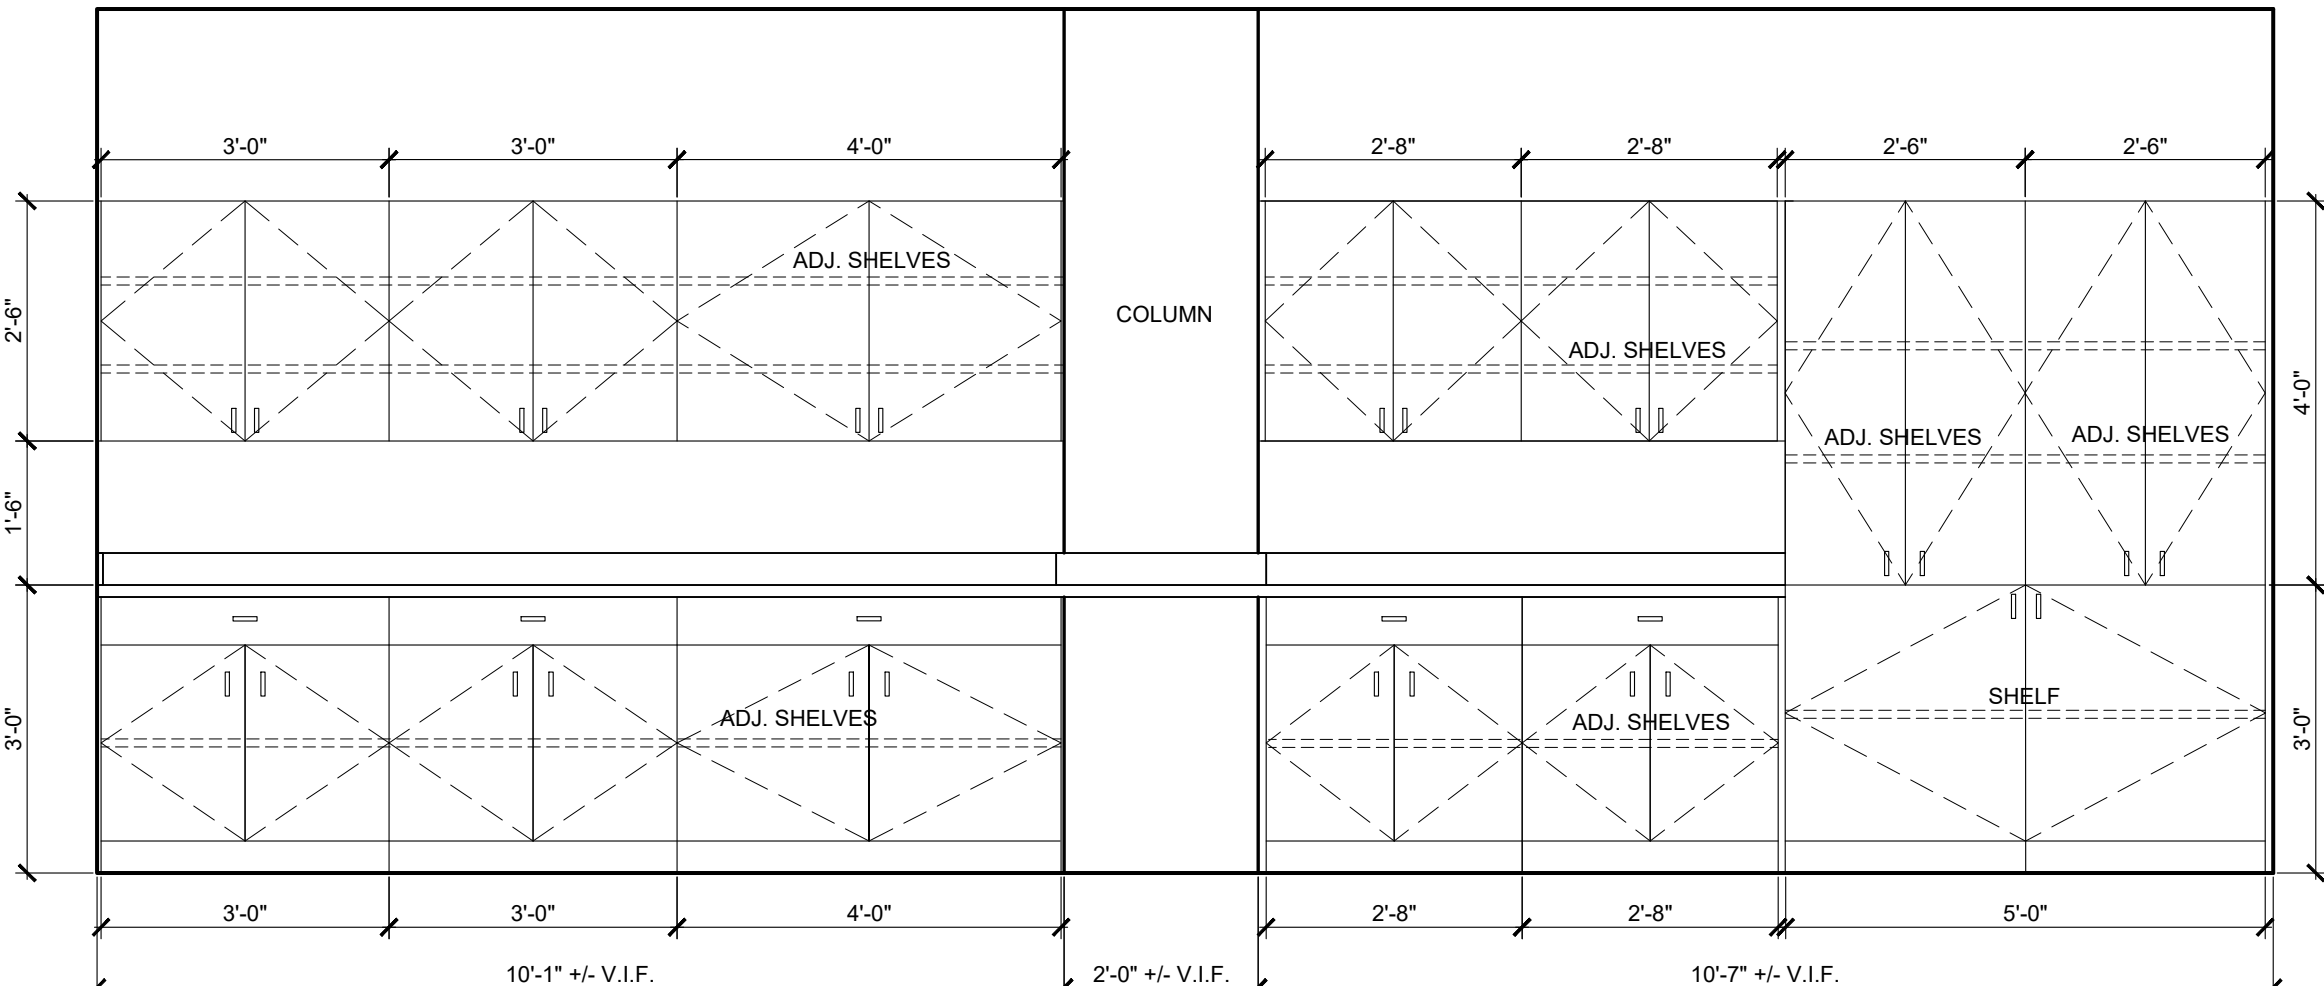

7 MRI SCAN ROOM 107
SCALE: 1/2" = 1'-0"

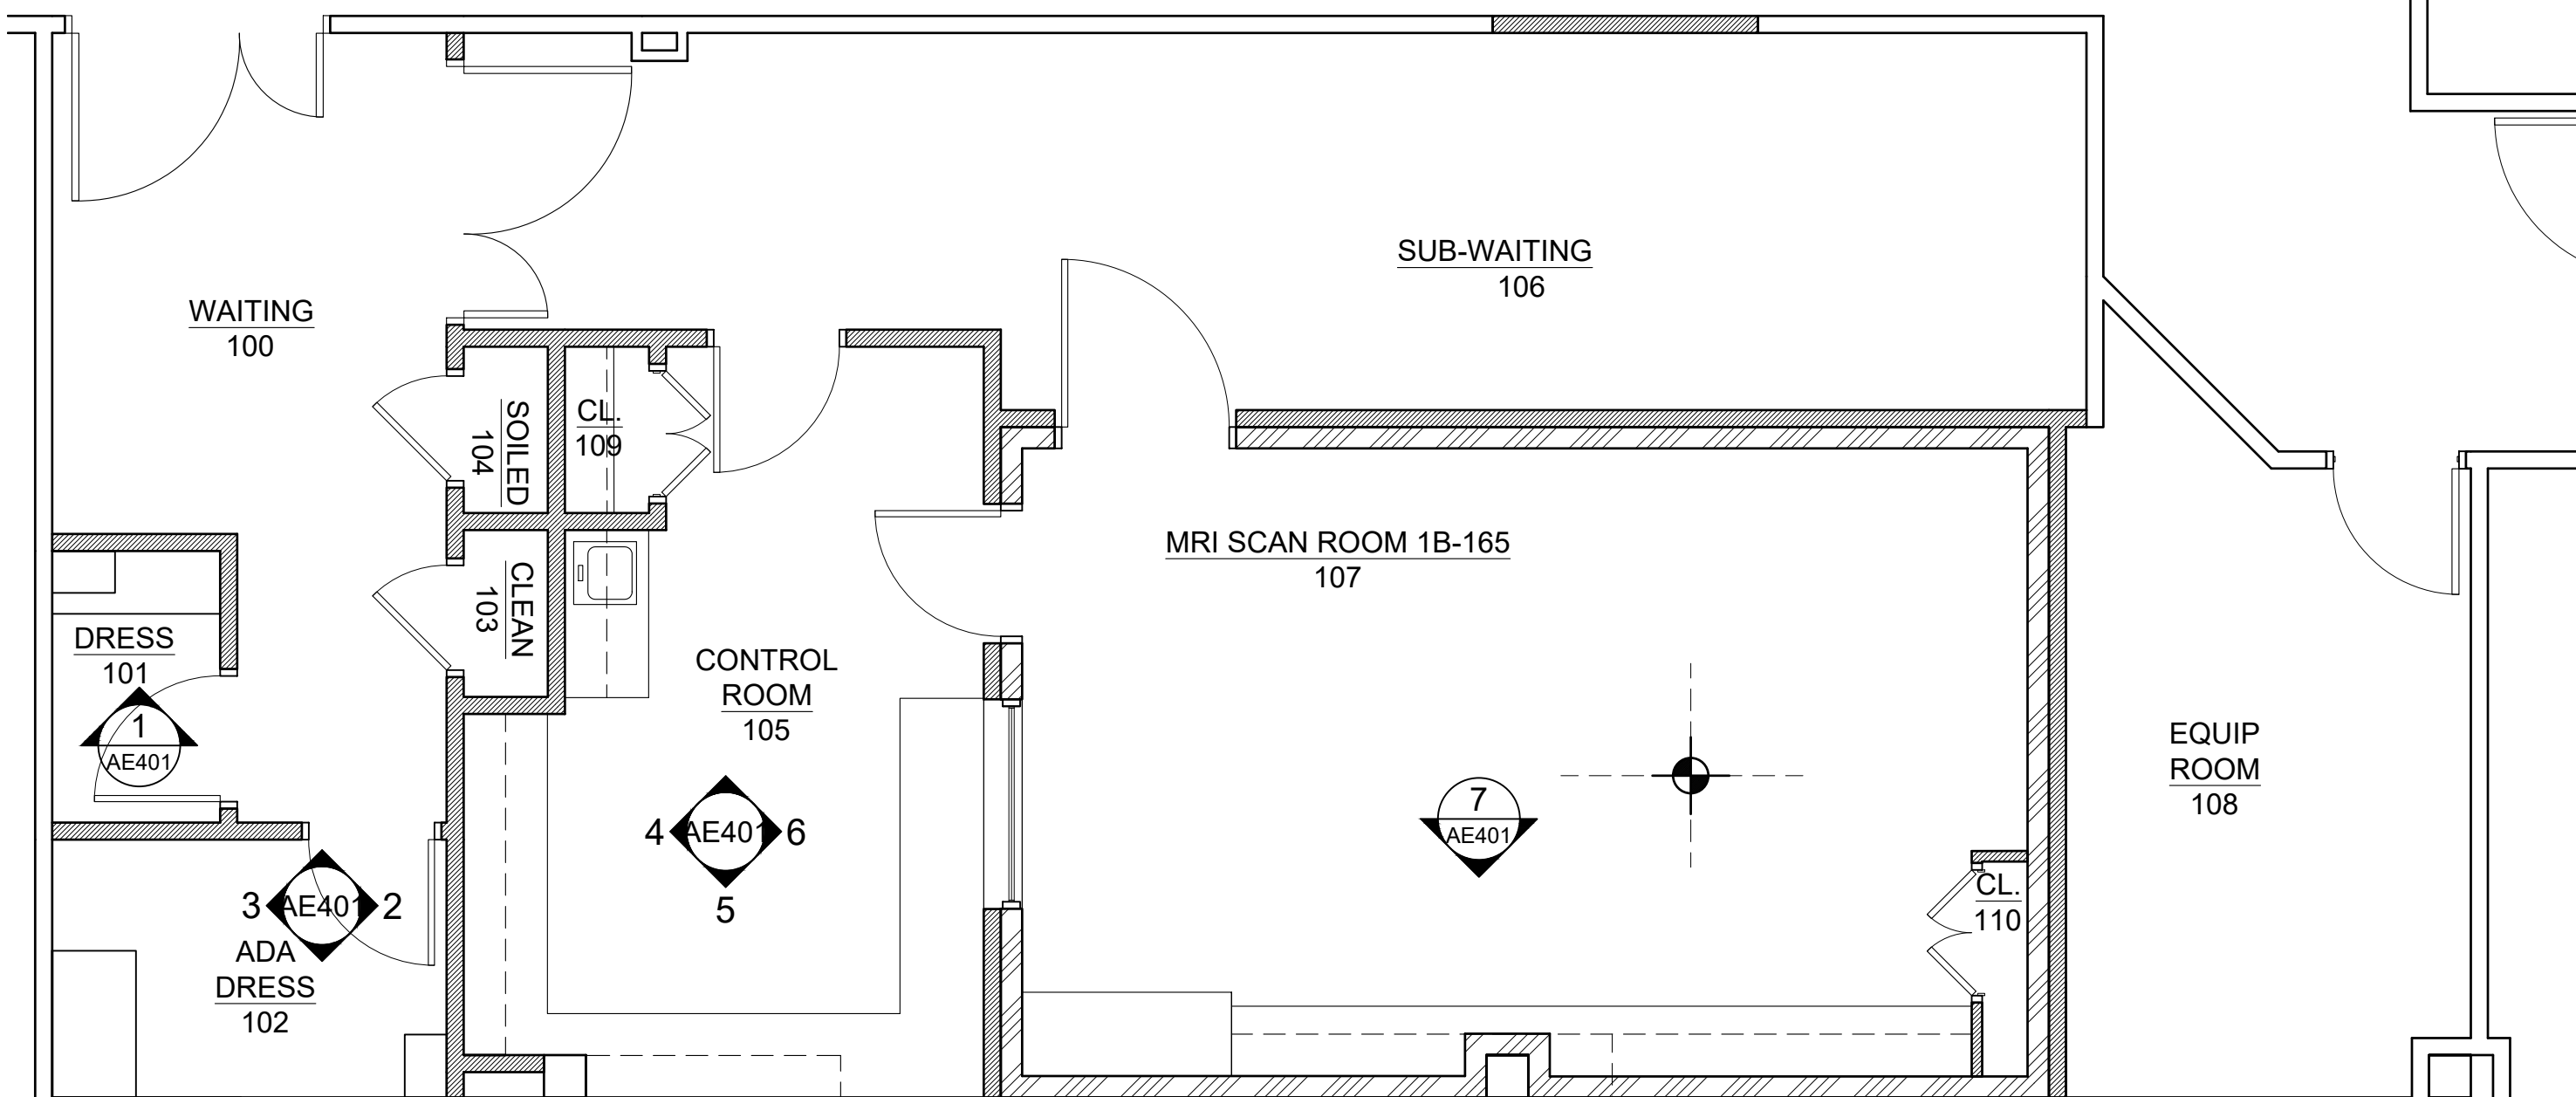

8 MILLWORK PLAN
SCALE: 1/4" = 1'-0"

MILLWORK NOTES

- 1: WALL AND BASE CABINETS EXTERIOR TO BE PLASTIC LAMINATE, SEE FINISH SCHEDULE FOR SPECIFICATION.
- 2: WALL AND BASE CABINET INTERIOR TO BE WHITE MELAMINE.
- 3: COUNTERTOPS WITH 4" BACKSPLASH TO BE SOLID SURFACE, SEE FINISH SCHEDULE FOR SPECIFICATION.
- 4: PROVIDE ADJUSTABLE SHELVES AS INDICATED ON ELEVATIONS.
- 5: DOORS AND DRAWERS TO HAVE 4" BRUSHED CHROME WIRE SHELVES

DESIGN/BUILDER:		ARCHITECT/ENGINEERS:		Stamp/Seal	Drawing Title	Project Title	Project Number
Deerfield Construction Group 610 Professional Drive, Suite 210 Gaithersburg, Maryland 20879 (301)947-4701		Nicholas Lucarelli Architects, LLC 6723 Whittier Avenue Suite 414 McLean, VA 22101 Tel: (703) 790-9606		PROPERTY OF THE UNITED STATES GOVERNMENT FOR OFFICIAL USE ONLY DO NOT REMOVE THIS NOTICE. PROPERLY DESTROY DOCUMENTS WHEN NO LONGER NEEDED.	MILLWORK PLAN & ELEVATIONS	VA BALTIMORE MEDICAL CENTER ROOM 1B-165	PROJECT #
For review and approval 6.2.21		D2 Engineering, LLC 18310 Montgomery Village Ave Suite 520 Gaithersburg, MD 20879 Tel: (301) 208-9575 Fax: (301) 208-9405					Building Number -
Revisions:		Date		Approved: Project Director		Location 10 NORTH GREENE STREET, BALTIMORE, MD 21201	Drawing Number
						Date 6.2.2021	AE401

three inches = one foot

one and one half inches = one foot

one inch = one foot

three quarters inch = one foot

one half inch = one foot

one quarter inch = one foot

one eighth inch = one foot

one quarter inch = one foot

one eighth inch = one foot

one eighth inch = one foot

one eighth inch = one foot

FINISH SCHEDULE					FINISH SPECIFICATIONS				
NO.	ROOM	FLOORS		WALLS	WELDED SHEET VINYL		PLASTIC LAMINATE		
		WVS/VCT	P		WVS/VCT	P	PL-1	P	
100	WAITING	1	1	1	WVS-1	MANF. JONESTONE COLOR: WALNUT STREET W/ INTERGLAZE BASE	PL-1	MANF. WILSONART COLOR: ASIAN SAND - 7552K-18	
101	DRESS	1	1	1	VCT-1	MANF. JONESTONE COLOR: LUNAR BLUE 51932	PL-2	MANF. WILSONART COLOR: PASADENA OAK - 7552K-18	
102	ADA DRESS	1	1	1					
103	CLEAN	1	1	1					
104	SOILED	1	1	1					
105	CONTROL ROOM	1	1	1					
106	SUB-WAITING	1	1	1					
107	MRI SCAN ROOM	1	1	1					
108	EQUIP. ROOM	1	1	1					
109	CL	1	1	1					
110	CL	1	1	1					

PARTITION TYPES				
ALL NEW WALLS PARTITION TYPE #1 UNLESS OTHER WISE NOTED				

INTERIOR DOOR SCHEDULE						
NO.	LOCATION	TYPE	DESCRIPTION	SIZE	FINISH	HARDWARE
1	WAITING - 100	4	HINGED DOUBLE	6'-0" x 7'-0" x 1 3/4"	STAINED	1
2	DRESS - 101	1	HINGED SINGLE	3'-0" x 7'-0" x 1 3/4"	STAINED	3
3	DRESS - 102	1	HINGED SINGLE	3'-0" x 7'-0" x 1 3/4"	STAINED	3
4	CLEAN - 103	3	HINGED DOUBLE	3'-0" x 7'-0" x 1 3/4"	STAINED	4
5	SOILED - 104	3	HINGED DOUBLE	3'-0" x 7'-0" x 1 3/4"	STAINED	4
6	WAITING - 100	1	HINGED DOUBLE	3'-0" x 7'-0" x 1 3/4"	STAINED	1
7	CL - 109	3	HINGED DOUBLE	3'-0" x 7'-0" x 1 3/4"	STAINED	5
8	CONTROL ROOM - 105	1	HINGED SINGLE	3'-0" x 7'-0" x 1 3/4"	STAINED	6
9	CONTROL ROOM - 105	1	HINGED SINGLE	3'-0" x 7'-0" x 1 3/4"	STAINED	2
10	MRI SCAN ROOM - 107	2	HINGED SINGLE	4'-0" x 7'-0" x 1 3/4"	PL-2	2
11	EQUIP. ROOM - 108	1	HINGED SINGLE	3'-0" x 7'-0" x 1 3/4"	STAINED	1
12	CL - 110	3	HINGED DOUBLE	3'-0" x 7'-0" x 1 3/4"	STAINED	5


INTERIOR DOOR TYPES				

HARDWARE SPECIFICATIONS		HARDWARE SCHEDULE	
BUTT HINGES (A) INTERIOR DOORS USED (B) EXTERIOR DOORS WHICH ARE DEFINED AS DOORS EXPOSED TO THE ELEMENTS SHALL BE US32D.		HW SET #1 3 PAIR 1 LATCHSET 1 DUMMY LEVER SET 2 CLOSERS 1 FLUSH BOLT	
LOCKS/SETS AND LATCHSETS YALE CAMEL - CRI LEVER HARDWARE - COORDINATE FINISH WITH BUILDING MANAGEMENT		HW SET #2 HINGES PER DOOR MANF. ELECTRONIC LOCK PER MANF. CLOSER	
STOPS STOPS #436 AND #407 AS MANUFACTURED BY IVES OR APPROVED EQUAL. PROVIDE ONE FOR EACH INTERIOR DOOR.		HW SET #3 1 1/2 PAIR 1 CLOSER 1 PRIVACY LOCKSET	
MISCELLANEOUS ITEMS (1) SILENCERS OLIVIA-JOHNSON Q384 THREE PAIRS PER EACH SINGLE DOOR, TWO EACH PER PAIR OF DOORS SHALL BE FURNISHED.		HW SET #4 1 1/2 PAIR 1 BUTT HINGES 1 STORAGE LOCKSET	
NOTES: 1. ALL DOORS MUST OPEN TO A FULL 90 DEGREES UNLESS OTHERWISE NOTED. 2. ALL HARDWARE TO BE ADA COMPLIANT. 3. OWNER TO SELECTION FINISHES.		HW SET #5 3 1/2 PAIR 2 HINGES 2 DUMMY LEVER 2 MAGNETIC CATCH	


PLAN/CEILING SYMBOLS			
D-DEMOLISH	E-EXISTING	R-RELOCATED	N-NEW
	WALL TO BE REMOVED		
	EXIST WALL, TO REMAIN		
	NEW WALL		
	SHIELDING WALL		
	01	DOOR NUMBER	
	1	PARTITION TYPE	
		2' X 2' LAY-IN FIXTURE	

DESIGN/BUILDER:		ARCHITECT/ENGINEERS:	
Deerfield Construction Group 610 Professional Drive, Suite 210 Gaithersburg, Maryland 20879 (301)947-4701		Nicholas Lucarelli Architects, LLC 6723 Whittier Avenue Suite 414 Mclean, VA 22101 Tel: (703) 790-9606	
For review and approval 6.2.21		D2 Engineering, LLC 18310 Montgomery Village Ave Suite 520 Gaithersburg, MD 20879 Tel: (301) 208-9575 Fax: (301) 208-9405	
Revisions:		PROPERTY OF THE UNITED STATES GOVERNMENT FOR OFFICIAL USE ONLY DO NOT REMOVE THIS NOTICE. PROPERLY DESTROY DOCUMENTS WHEN NO LONGER NEEDED.	


VA FORM 08-6231

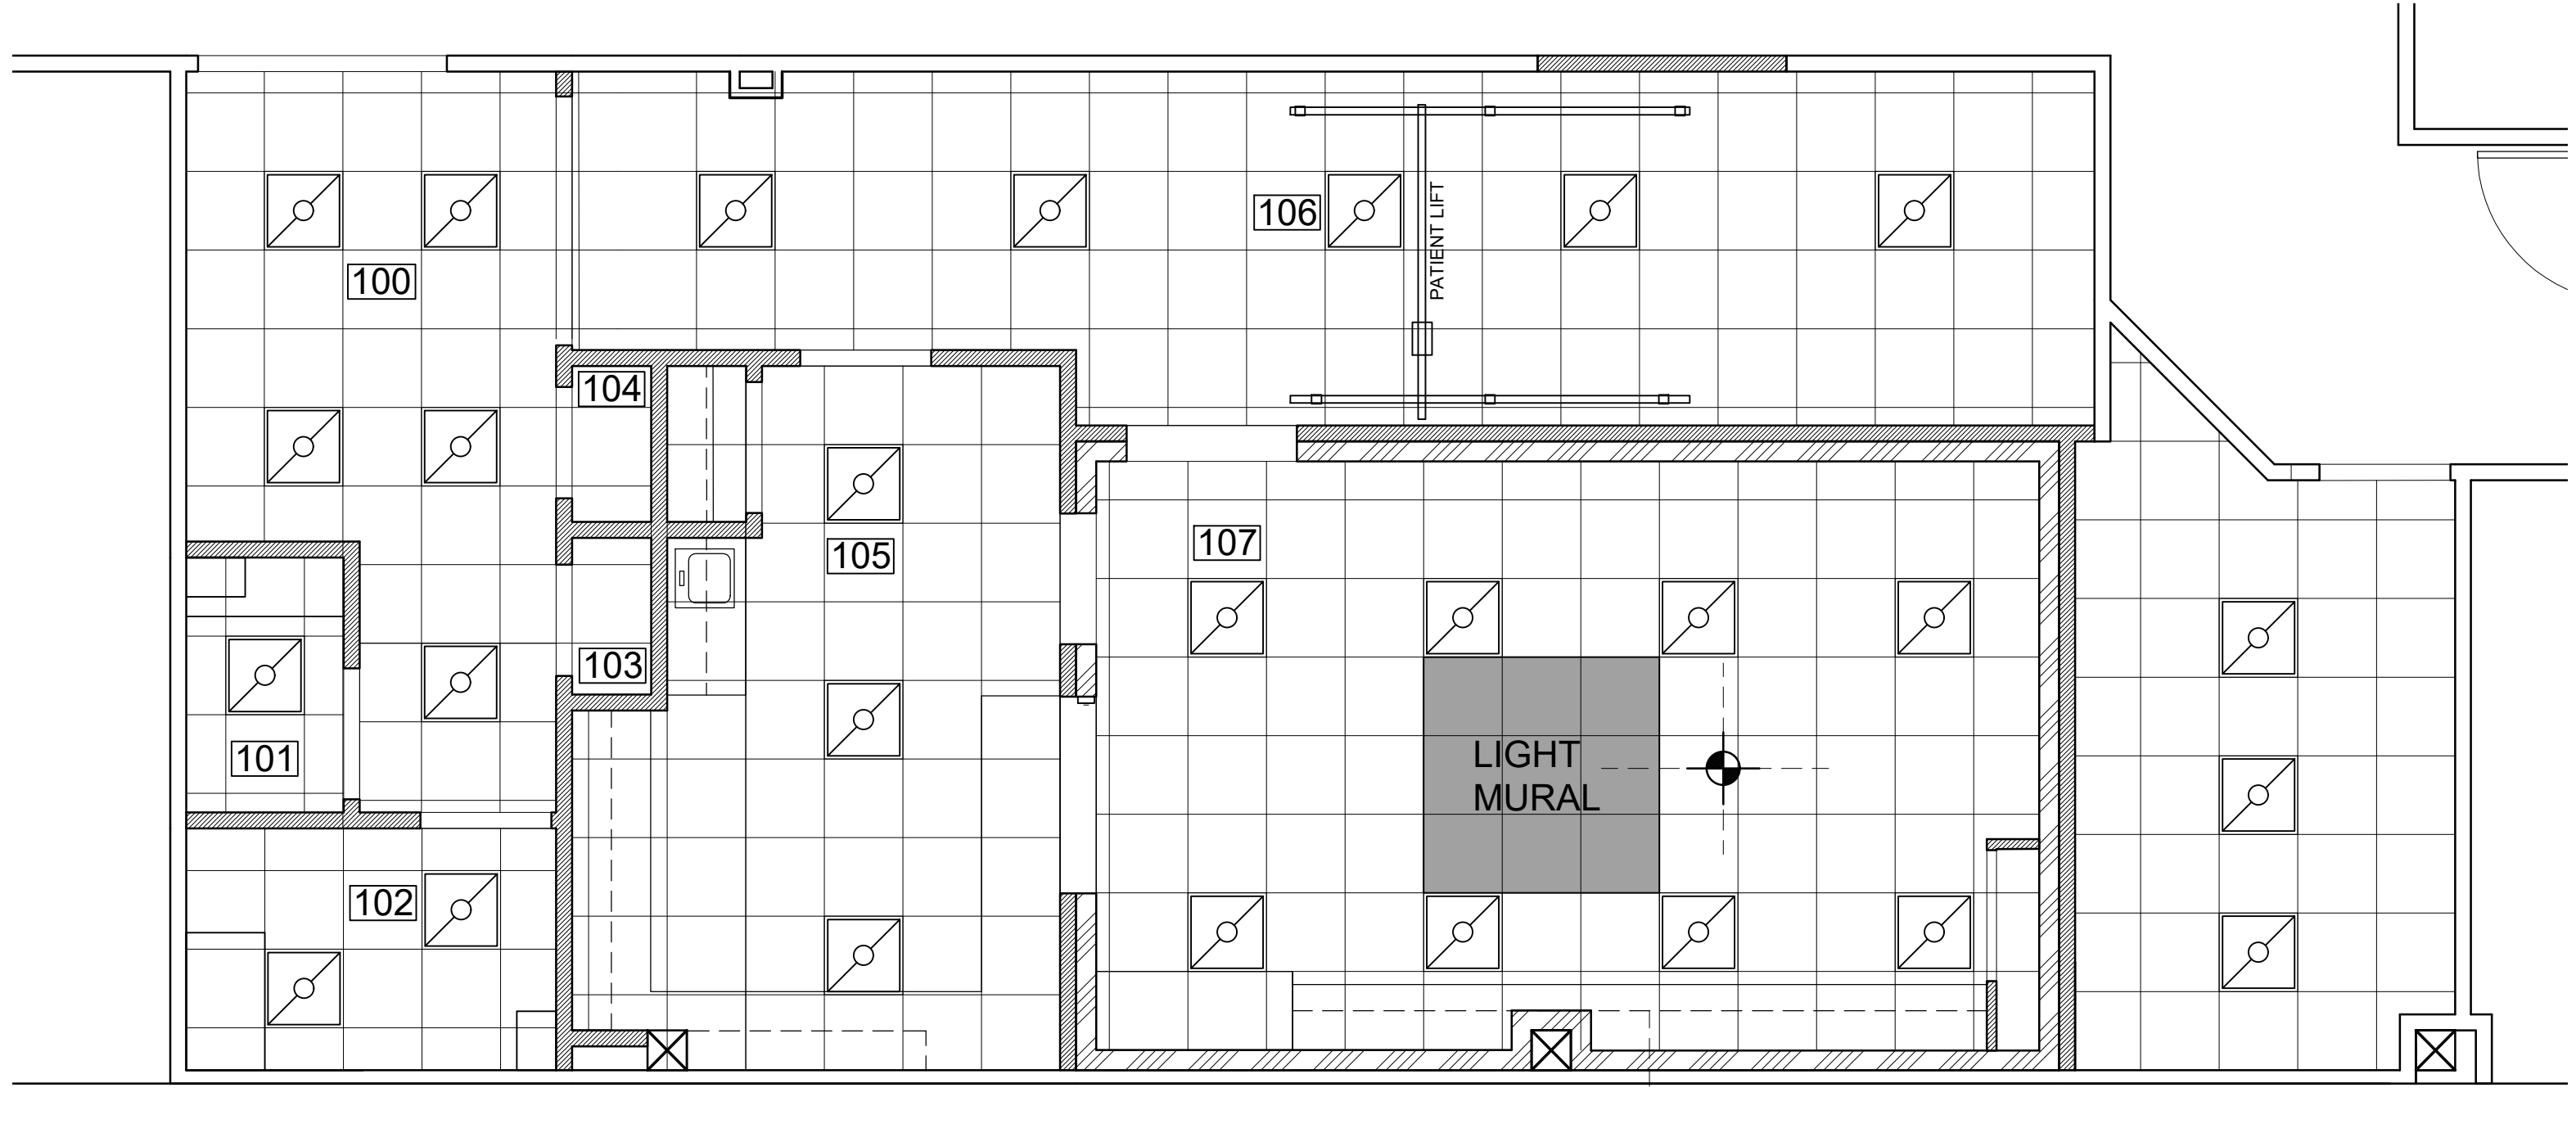

1 REFLECTED CEILING PLAN
SCALE: 1/4" = 1'-0"

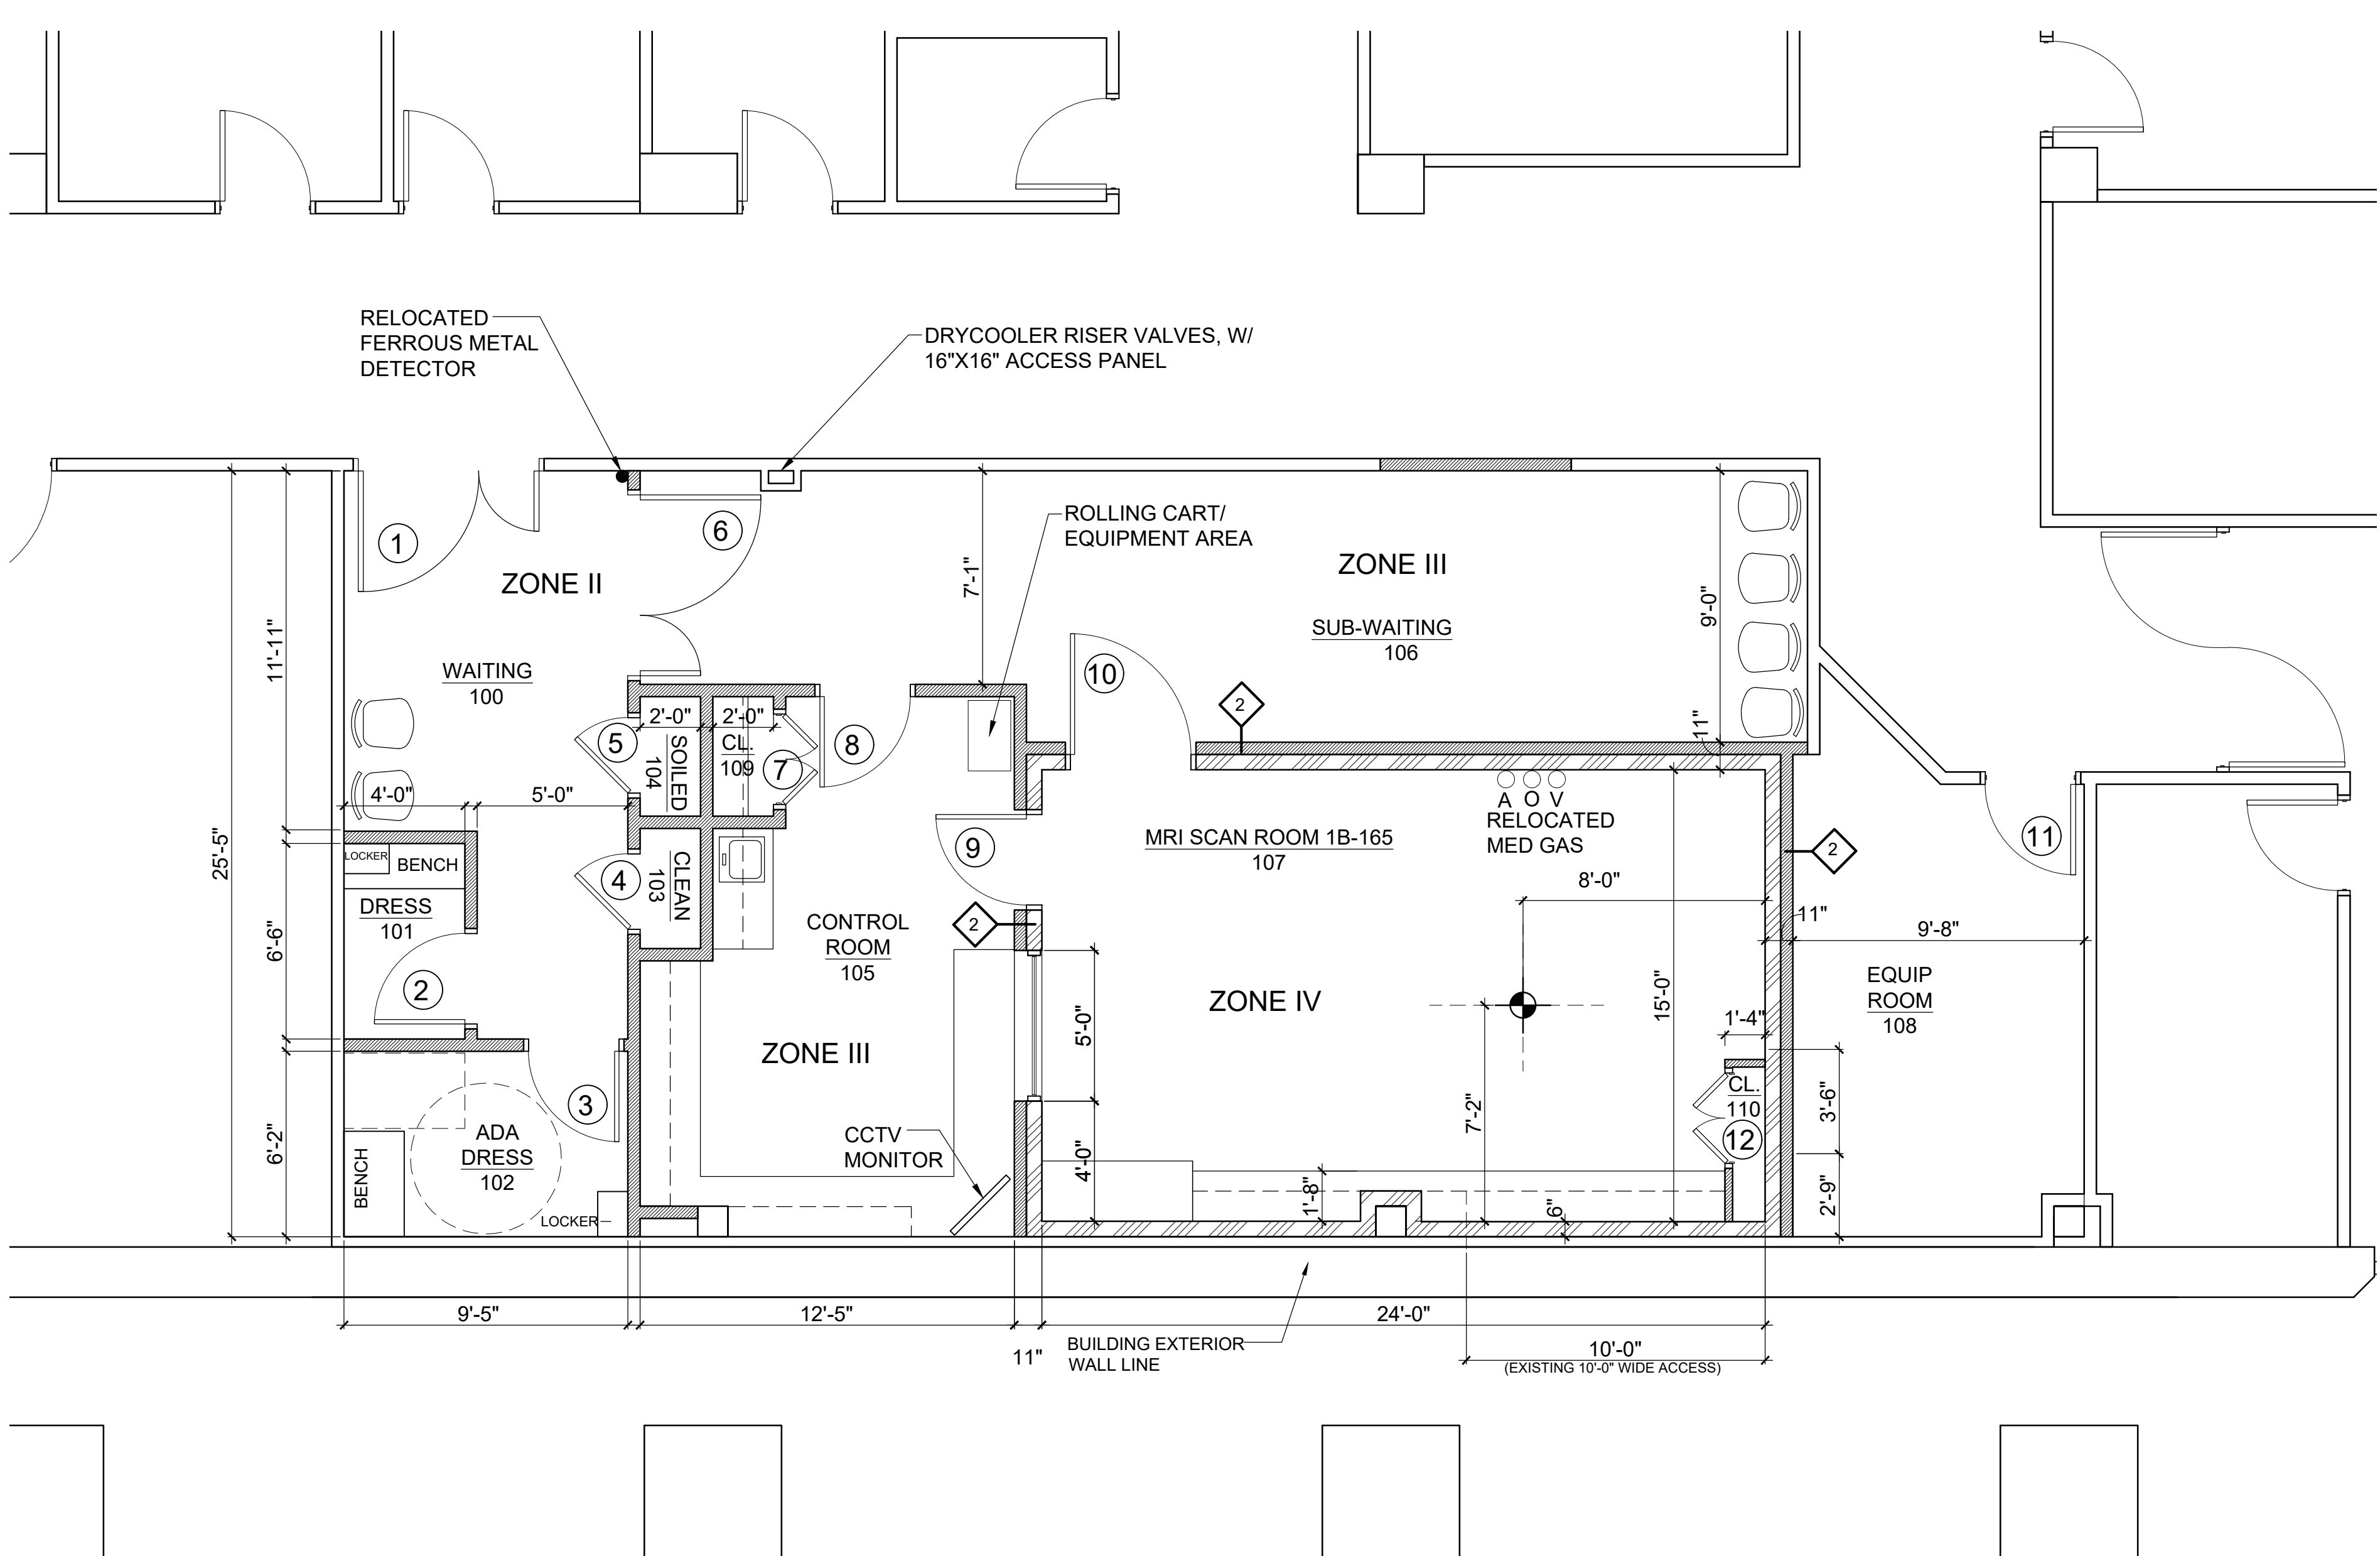

1 FLOOR PLAN
SCALE: 1/4" = 1'-0"

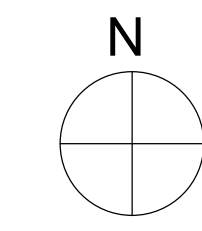

Stamp/Seal 	Drawing Title FLOOR PLAN, REFLECTED CEILING PLAN & SCHEDULES Approved: Project Director	Project Title VA BALTIMORE MEDICAL CENTER ROOM 1B-165 Location 10 NORTH GREENE STREET, BALTIMORE, MD 21201 Date 6.2.2021	Project Number PROJECT # Building Number - Drawing Number AE101
----------------	---	---	--

