



three inches = one foot

one and one half inches = one foot

one inch = one foot

three quarters inch = one foot

one half inch = one foot

one quarter inch = one foot

one eighth inch = one foot

one quarter inch = one foot

one eighth inch = one foot

one eighth inch = one foot

one eighth inch = one foot

| FINISH SCHEDULE |               |         |   |       | FINISH SPECIFICATIONS |                                                            |                  |                                                   |  |
|-----------------|---------------|---------|---|-------|-----------------------|------------------------------------------------------------|------------------|---------------------------------------------------|--|
| NO.             | ROOM          | FLOORS  |   | WALLS | WELDED SHEET VINYL    |                                                            | PLASTIC LAMINATE |                                                   |  |
|                 |               | WVS/VCT | P |       | WVS/VCT               | P                                                          | PL-1             | P                                                 |  |
| 100             | WAITING       | 1       | 1 | 1     | WVS-1                 | MANF. JONESTONE<br>COLOR: WALNUT STREET W/ INTERGLAZE BASE | PL-1             | MANF. WILSONART<br>COLOR: ASIAN SAND - 7552K-18   |  |
| 101             | DRESS         | 1       | 1 | 1     | VCT-1                 | MANF. JONESTONE<br>COLOR: LUNAR BLUE 51932                 | PL-2             | MANF. WILSONART<br>COLOR: PASADENA OAK - 7552K-18 |  |
| 102             | ADA DRESS     | 1       | 1 | 1     |                       |                                                            |                  |                                                   |  |
| 103             | CLEAN         | 1       | 1 | 1     |                       |                                                            |                  |                                                   |  |
| 104             | SOILED        | 1       | 1 | 1     |                       |                                                            |                  |                                                   |  |
| 105             | CONTROL ROOM  | 1       | 1 | 1     |                       |                                                            |                  |                                                   |  |
| 106             | SUB-WAITING   | 1       | 1 | 1     |                       |                                                            |                  |                                                   |  |
| 107             | MRI SCAN ROOM | 1       | 1 | 1     |                       |                                                            |                  |                                                   |  |
| 108             | EQUIP. ROOM   | 1       | 1 | 1     |                       |                                                            |                  |                                                   |  |
| 109             | CL            | 1       | 1 | 1     |                       |                                                            |                  |                                                   |  |
| 110             | CL            | 1       | 1 | 1     |                       |                                                            |                  |                                                   |  |

| PARTITION TYPES                                                  |  |  |  |  |
|------------------------------------------------------------------|--|--|--|--|
| ALL NEW WALLS<br>PARTITION TYPE #1<br>UNLESS OTHER<br>WISE NOTED |  |  |  |  |
|                                                                  |  |  |  |  |
|                                                                  |  |  |  |  |


| INTERIOR DOOR SCHEDULE |                     |      |               |                        |         |          |
|------------------------|---------------------|------|---------------|------------------------|---------|----------|
| NO.                    | LOCATION            | TYPE | DESCRIPTION   | SIZE                   | FINISH  | HARDWARE |
| 1                      | WAITING - 100       | 4    | HINGED DOUBLE | 6'-0" x 7'-0" x 1 3/4" | STAINED | 1        |
| 2                      | DRESS - 101         | 1    | HINGED SINGLE | 3'-0" x 7'-0" x 1 3/4" | STAINED | 3        |
| 3                      | DRESS - 102         | 1    | HINGED SINGLE | 3'-0" x 7'-0" x 1 3/4" | STAINED | 3        |
| 4                      | CLEAN - 103         | 3    | HINGED DOUBLE | 3'-0" x 7'-0" x 1 3/4" | STAINED | 4        |
| 5                      | SOILED - 104        | 3    | HINGED DOUBLE | 3'-0" x 7'-0" x 1 3/4" | STAINED | 4        |
| 6                      | WAITING - 100       | 1    | HINGED DOUBLE | 3'-0" x 7'-0" x 1 3/4" | STAINED | 1        |
| 7                      | CL - 109            | 3    | HINGED DOUBLE | 3'-0" x 7'-0" x 1 3/4" | STAINED | 5        |
| 8                      | CONTROL ROOM - 105  | 1    | HINGED SINGLE | 3'-0" x 7'-0" x 1 3/4" | STAINED | 6        |
| 9                      | CONTROL ROOM - 105  | 1    | HINGED SINGLE | 3'-0" x 7'-0" x 1 3/4" | STAINED | 2        |
| 10                     | MRI SCAN ROOM - 107 | 2    | HINGED SINGLE | 4'-0" x 7'-0" x 1 3/4" | PL-2    | 2        |
| 11                     | EQUIP. ROOM - 108   | 1    | HINGED SINGLE | 3'-0" x 7'-0" x 1 3/4" | STAINED | 1        |
| 12                     | CL - 110            | 3    | HINGED DOUBLE | 3'-0" x 7'-0" x 1 3/4" | STAINED | 5        |

| INTERIOR DOOR TYPES |  |  |  |  |
|---------------------|--|--|--|--|
|                     |  |  |  |  |
|                     |  |  |  |  |
|                     |  |  |  |  |
|                     |  |  |  |  |


| HARDWARE SPECIFICATIONS   |  | HARDWARE SCHEDULE   |  |
|---|--|---|--|
| <b>BUTT HINGES</b><br>(A) INTERIOR DOORS USED<br>(B) EXTERIOR DOORS WHICH ARE DEFINED AS DOORS EXPOSED TO THE ELEMENTS SHALL BE US32D.                          |  | <b>HW SET #1</b><br>3 PAIR<br>1<br>1<br>2<br>1                                                                                      |  |
| <b>LOCKSETS AND LATCHSETS</b><br>YALE CAMEL - CRI LEVER HARDWARE - COORDINATE FINISH WITH BUILDING MANAGEMENT                                                   |  | <b>BUTT HINGES</b><br>LATCHSET<br>DUMMY LEVER SET<br>CLOSERS<br>FLUSH BOLT                                                          |  |
| <b>STOPS</b><br>STOPS #436 AND #407 AS MANUFACTURED BY IVES OR APPROVED EQUAL. PROVIDE ONE FOR EACH INTERIOR DOOR.                                              |  | <b>HW SET #2</b><br>-<br>1<br>1   |  |
| <b>MISCELLANEOUS ITEMS</b><br>(1) SILENCERS OLIVIA-JOHNSON Q384 THREE PAIRS PER EACH SINGLE DOOR, TWO EACH PER PAIR OF DOORS SHALL BE FURNISHED.                |  | <b>HINGES PER DOOR MANF. -</b><br>ELECTRONIC LOCK PER MANF.<br>CLOSER                                                               |  |
| <b>NOTES:</b><br>1. ALL DOORS MUST OPEN TO A FULL 90 DEGREES UNLESS OTHERWISE NOTED.<br>2. ALL HARDWARE TO BE ADA COMPLIANT.<br>3. OWNER TO SELECTION FINISHES. |  | <b>HW SET #3</b><br>1 1/2 PAIR<br>1<br>1<br><br><b>HW SET #4</b><br>1 1/2 PAIR<br>1<br><br><b>HW SET #5</b><br>3 1/2 PAIR<br>2<br>2 |  |

| PLAN/CEILING SYMBOLS |                        |              |        |
|----------------------|------------------------|--------------|--------|
| D- DEMOLISH          | E- EXISTING            | R- RELOCATED | N- NEW |
|                      | WALL TO BE REMOVED     |              |        |
|                      | EXIST. WALL, TO REMAIN |              |        |
|                      | NEW WALL               |              |        |
|                      | SHIELDING WALL         |              |        |
|                      | DOOR NUMBER            |              |        |
|                      | PARTITION TYPE         |              |        |
|                      | 2' X 2' LAY-IN FIXTURE |              |        |


| DESIGN/BUILDER:   |  | ARCHITECT/ENGINEERS:   |  |
|---|--|---|--|
| <b>Deerfield Construction Group</b><br>610 Professional Drive, Suite 210<br>Gaithersburg, Maryland 20879<br>(301)947-4701                       |  | <b>Nicholas Lucarelli Architects, LLC</b><br>6723 Whittier Avenue Suite 414<br>Mclean, VA 22101<br>Tel: (703) 790-9606                                          |  |
| <b>D2 Engineering, LLC</b><br>18310 Montgomery Village Ave<br>Suite 520<br>Gaithersburg, MD 20879<br>Tel: (301) 208-9575<br>Fax: (301) 208-9405 |  | <b>PROPERTY OF THE UNITED STATES GOVERNMENT</b><br><br>FOR OFFICIAL USE ONLY<br>DO NOT REMOVE THIS NOTICE.<br>PROPERLY DESTROY DOCUMENTS WHEN NO LONGER NEEDED. |  |

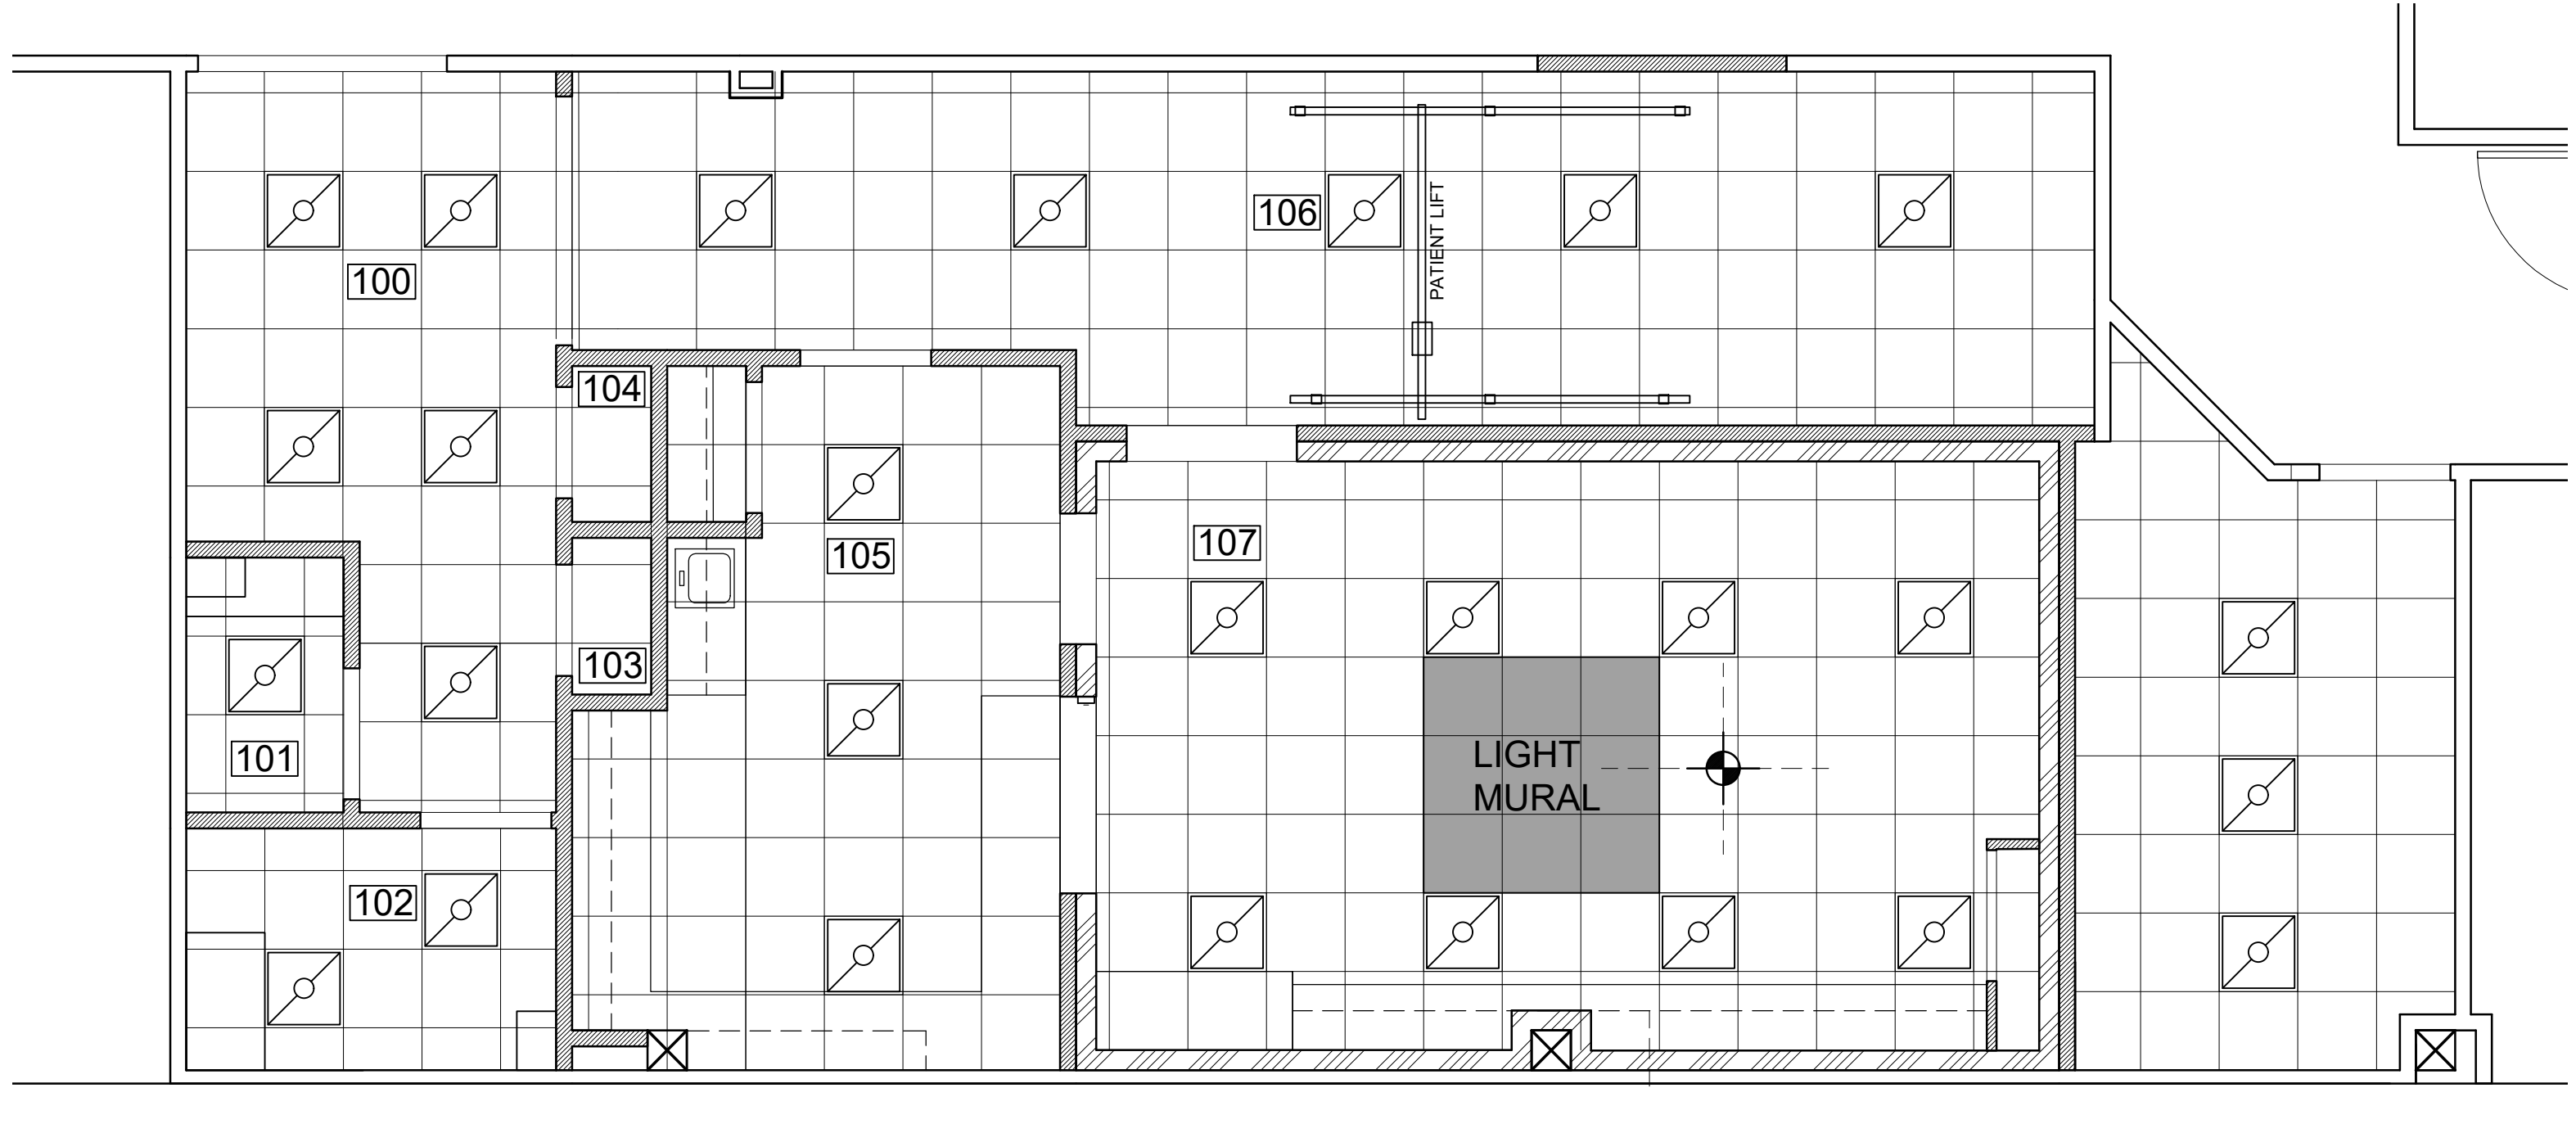


1 REFLECTED CEILING PLAN  
SCALE: 1/4" = 1'-0"

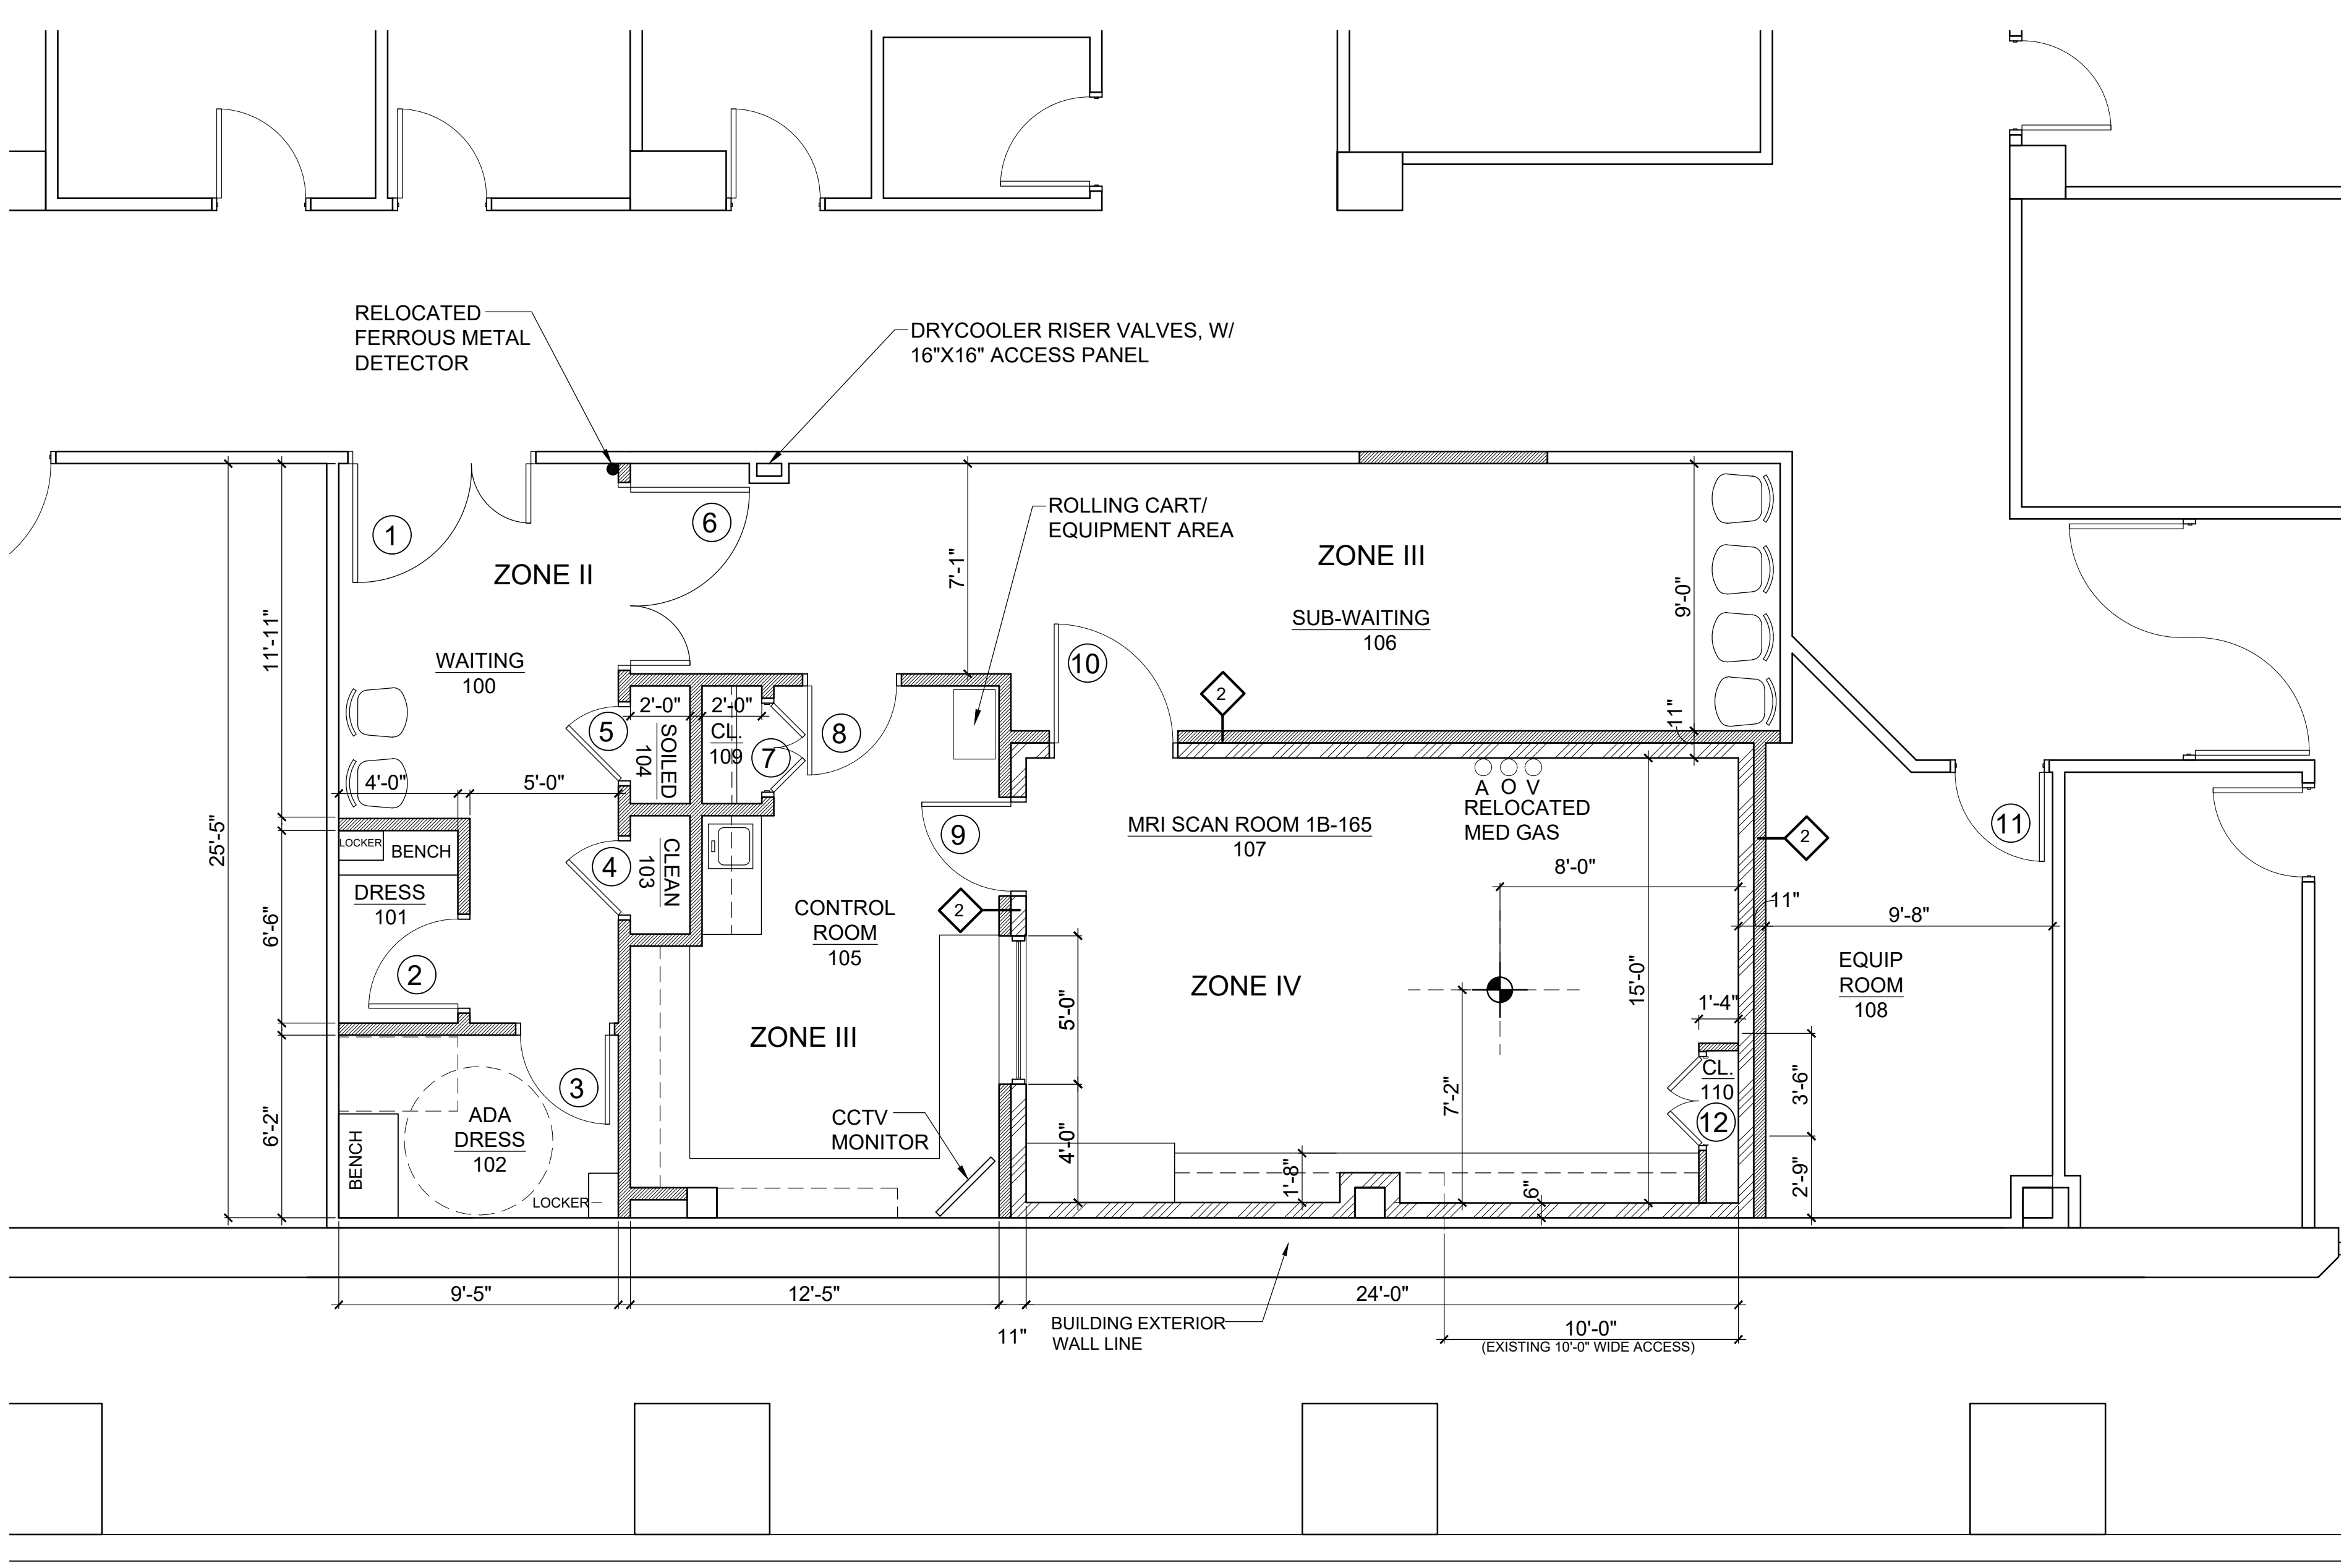


1 FLOOR PLAN  
SCALE: 1/4" = 1'-0"

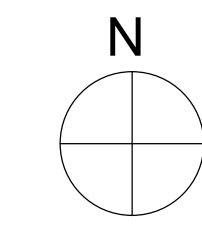

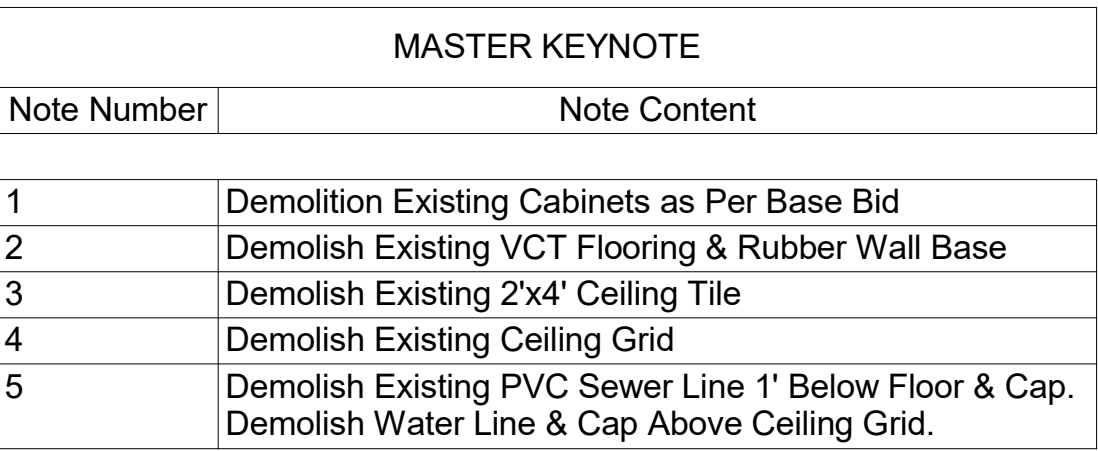

**General Notes:**  
1. The contractor shall demolish throughout the following: flooring, ceiling tile, and ceiling grid. See SOW

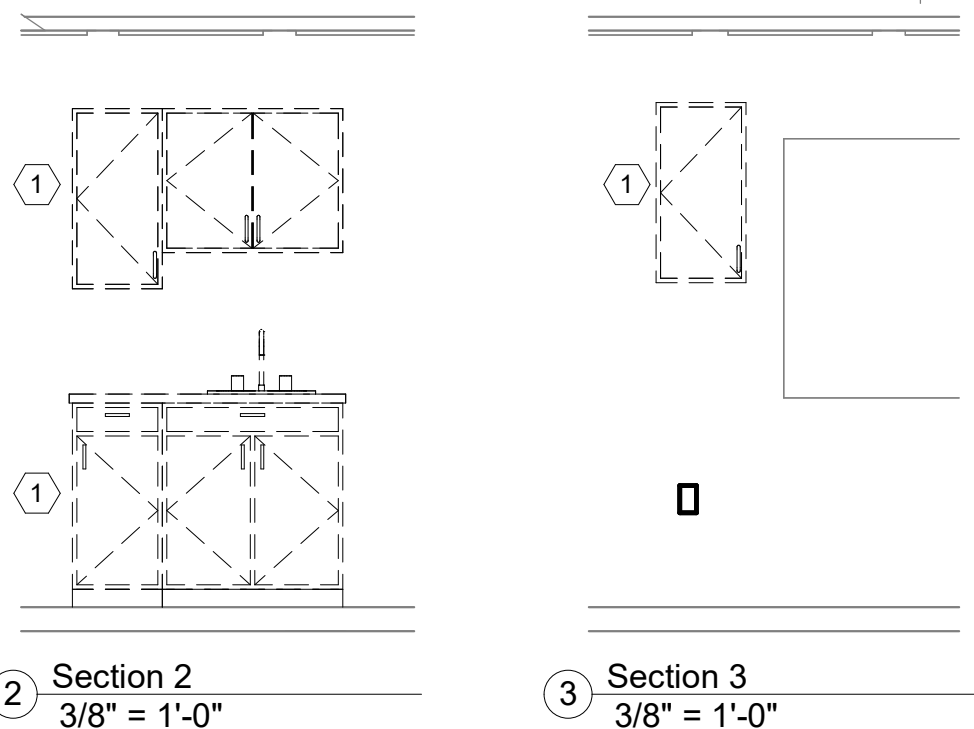

**GREAT PLAINS AREA INDIAN HEALTH SERVICE**  
OFFICE OF ENVIRONMENTAL  
HEALTH & ENGINEERING

**DIVISION OF FACILITIES MANAGEMENT**  
115 4TH AVENUE SE, RM 309  
ABERDEEN, SD 57401  
(605) 226-7451 FAX (605) 226-7580

***www.ihs.gov***

Quentin N. Burdick  
Memorial Health Facility

## Replace RTU & Cabinetry - CT Area

|                     |                      |
|---------------------|----------------------|
| CONTRACT NO:        |                      |
| TASK ORDER NO:      |                      |
| PROJECT NUMBER:     | <b>GP22TM300H10</b>  |
| DATE:               | <b>08/26/2025</b>    |
| DRAWN BY:           | <b>Taylor Strand</b> |
| CHECKED BY:         | <b>Brad Weekley</b>  |
| LAST REVISION DATE: |                      |

# GENERAL DEMOLITION

## A.1



#### RESTROOM ACCESSORY NOTES

1. SEE SHEET G101 FOR SHOWER RECEPTOR TYPES.
2. MOUNT WASTE RECEPTACLE TO MEET ABAAS. MOUNT HIGHEST OPERABLE PART OF CONTROLS, DISPENSERS, RECEPTABLES AND OTHER OPERABLE EQUIPMENT BETWEEN 15" - 48" ABOVE FINISH FLOOR.
3. ATTACH MIRROR PER MANUFACTURER STANDARD. CENTER MIRROR ON LAVATORY(S) BELOW.
4. ROBE HOOKS (A8145) TO BE MOUNTED ON TOILET SIDE OF DOOR, 48" FIELD FROM ABOVE FINISH FLOOR TO CENTER.
5. FIELD VERIFY MOUNTING HEIGHTS WITH RESIDENT ENGINEER BEFORE INSTALLATION.
6. PROVIDE & INSTALL PRE-JOINED (PLASTIC COVER) INSULATION FOR ALL EXPOSED PIPING, MEETING ALL APPLICABLE ABA REQUIREMENTS.

## RESTROOM ACCESSORY GENERAL NOTES

- A. MOUNTING HEIGHTS REFERENCED ON SHEET G101.  
VERIFY ALL MOUNTING HEIGHTS WITH CODES AND MANUFACTURER RECOMMENDATIONS.
- B. ABA TOILET PARTITION DOOR MUST BE 34" MINIMUM CLEAR OPENING.
- C. WHERE DIMENSIONS ARE INDICATED ON PLAN AS "CLEAR", THE DIMENSIONS ARE TAKEN FROM FACE OF FINISHED WALL MATERIAL TO FACE OF FINISHED WALL MATERIAL.
- D. SEE SHEET QH104 FOR EQUIPMENT SCHEDULE.

## EQUIPMENT ABBREVIATIONS

|     |                                     |
|-----|-------------------------------------|
| CC: | CONTRACTOR FURNISHED & INSTALLED    |
| VV: | VA FURNISHED & INSTALLED            |
| VC: | VA FURNISHED & CONTRACTOR INSTALLED |

## BID DOCUMENTS

[illegible]

|            |                              |       |   |                                                                               |                                                                                 |   |   |
|------------|------------------------------|-------|---|-------------------------------------------------------------------------------|---------------------------------------------------------------------------------|---|---|
| CONSULTANT | ARCHITECT/ENGINEER OF RECORD | STAMP | <div> <div>Office of Construction and Facilities Management</div> <div>  </div> </div> <div>  <div>U.S. Department of Veterans Affairs</div> </div> | <div>Drawing Title</div> <div>ENLARGED FLOOR PLANS</div> <div>Approved:</div> | <div>Phase</div> <div>CONSTRUCTION DOCUMENTS</div> <div>FULLY SPRINKLERED</div> | <div>Project Title</div> <div>RENOVATE BUILDING 1</div> <div>Location</div> <div>BILOXI, MISSISSIPPI</div> <div> <div>Issue Date</div> <div>03/10/2023</div> </div> <div> <div>Checked</div> <div>LA</div> </div> <div> <div>Drawn</div> <div>CD,PC</div> </div> | <div>Project Number</div> <div>520-317X</div> <div>Building Number</div> <div>1</div> <div>Drawing Number</div> <div>AE123</div> <div> <div>Dwg.</div> <div>79</div> <div>of</div> <div>238</div> </div> |
|------------|------------------------------|-------|---|-------------------------------------------------------------------------------|---------------------------------------------------------------------------------|---|---|

A

B












C

D

E

F

3/13/2023 10:31:27 AM  
C:\Users\pjd\Documents\15950 - VAHC-Bldg Building 1\_R21 - Dental.mxd\_Yeunyoung.n

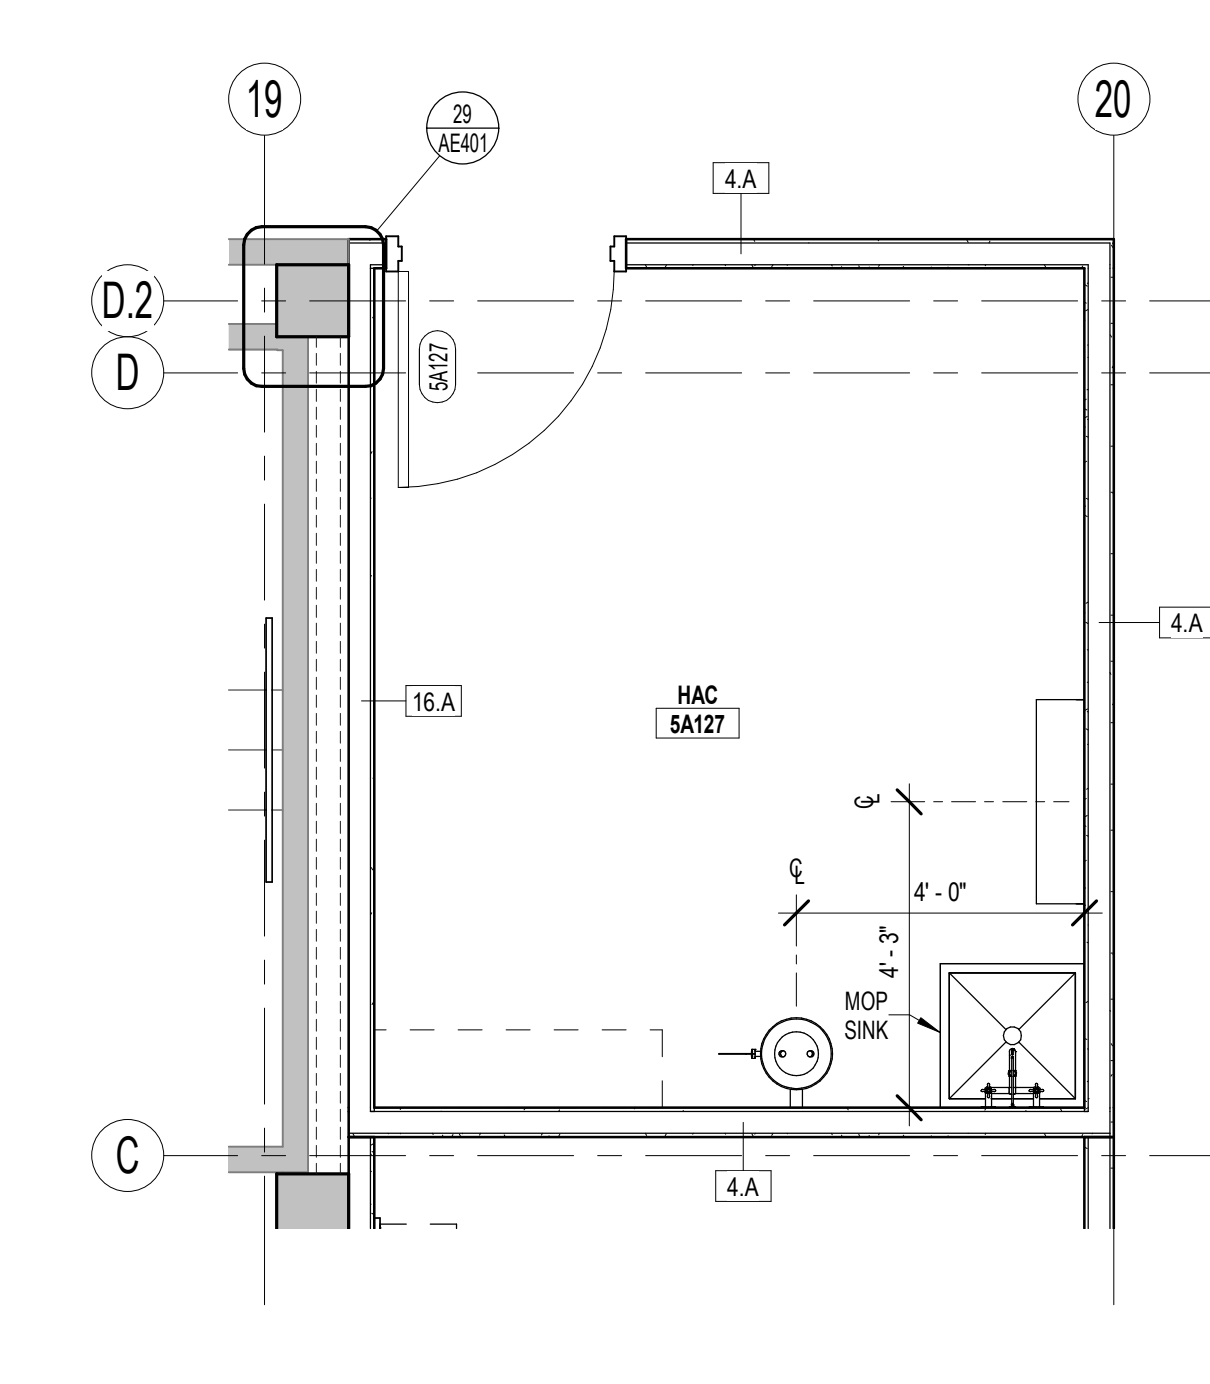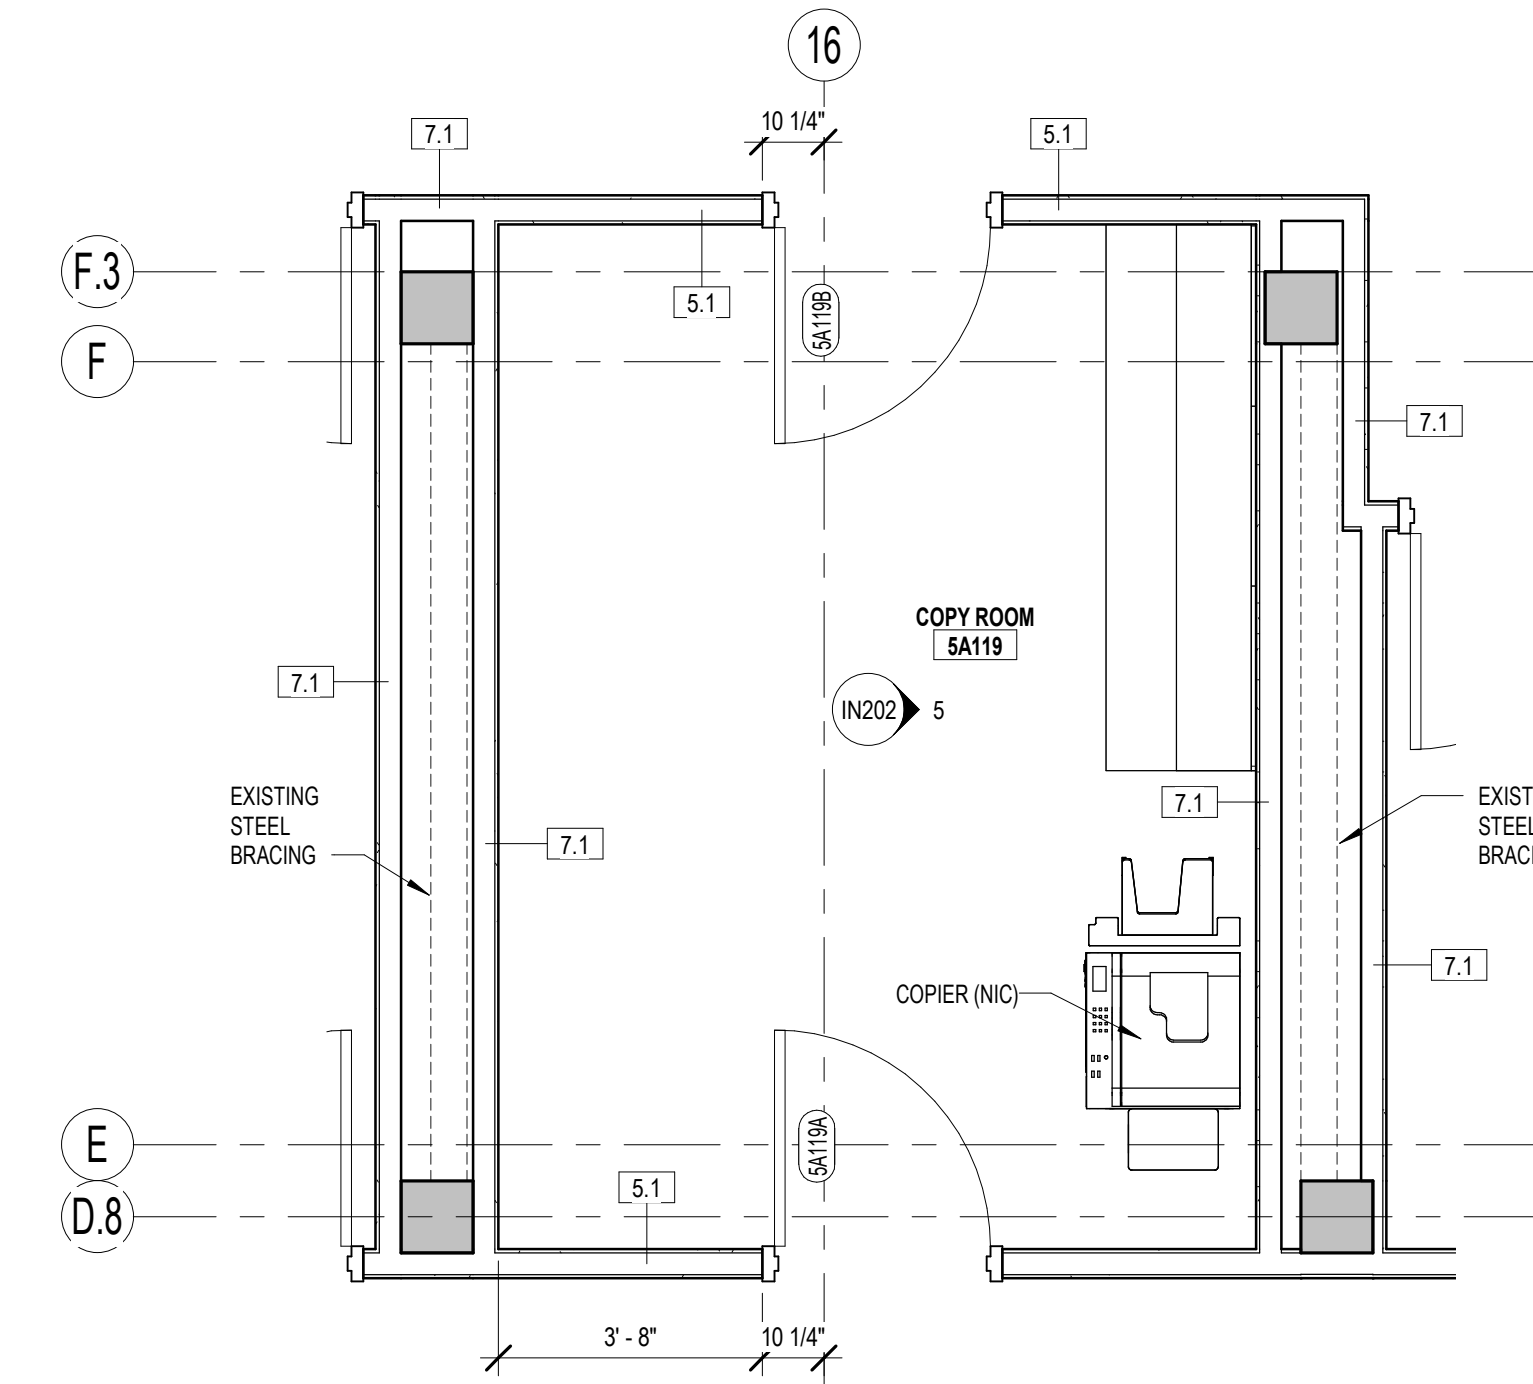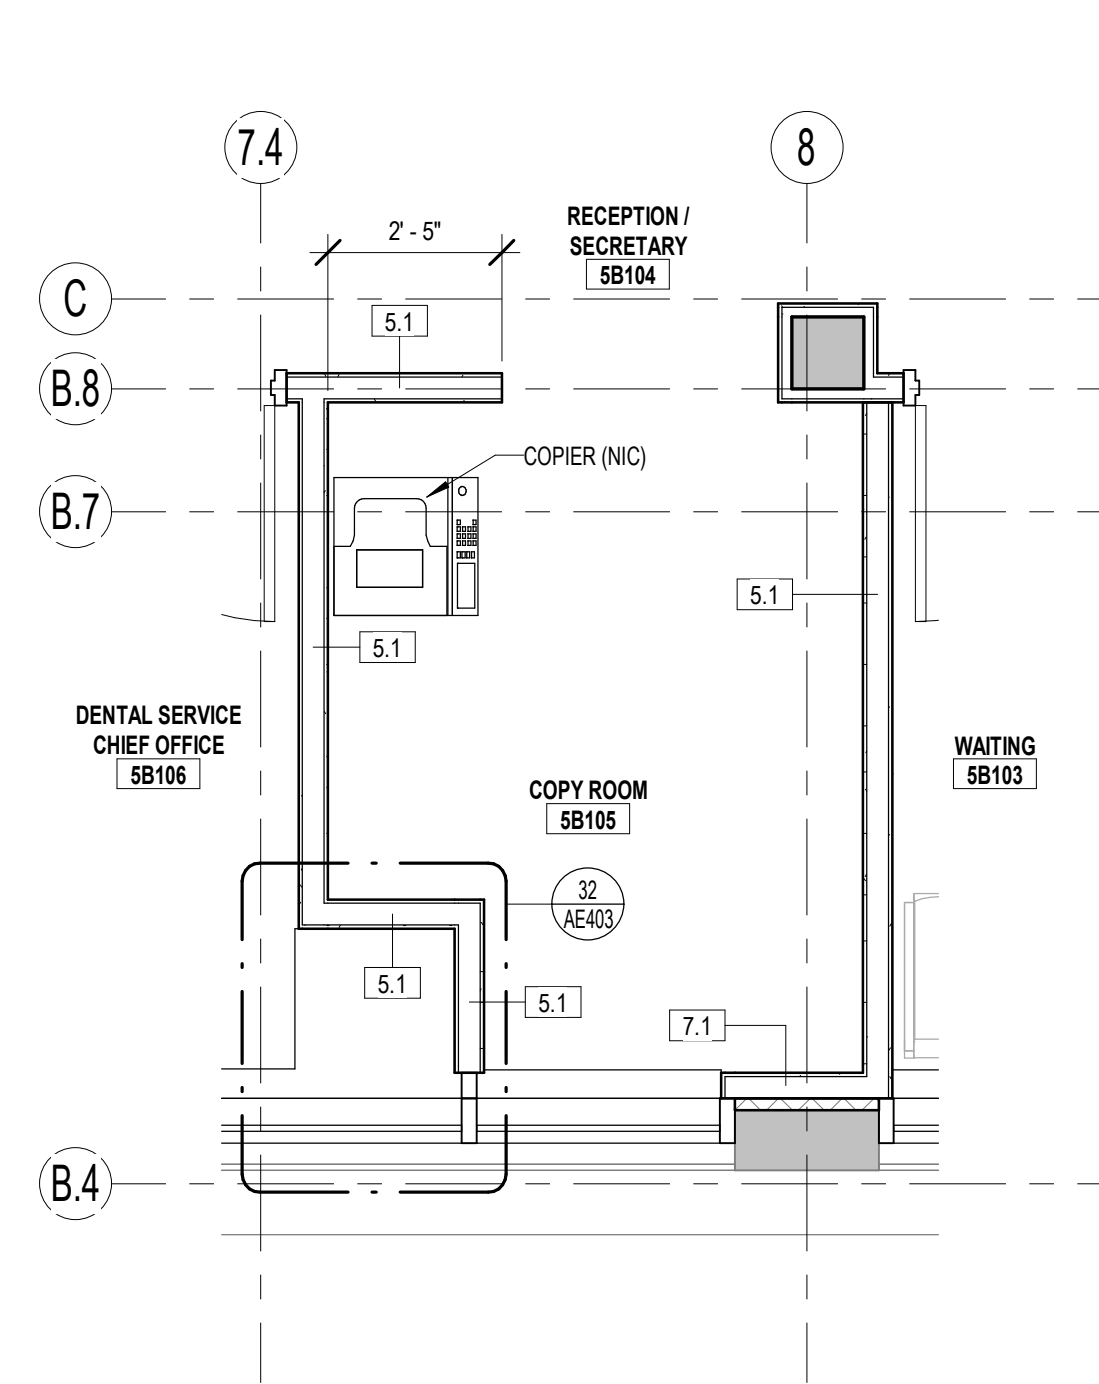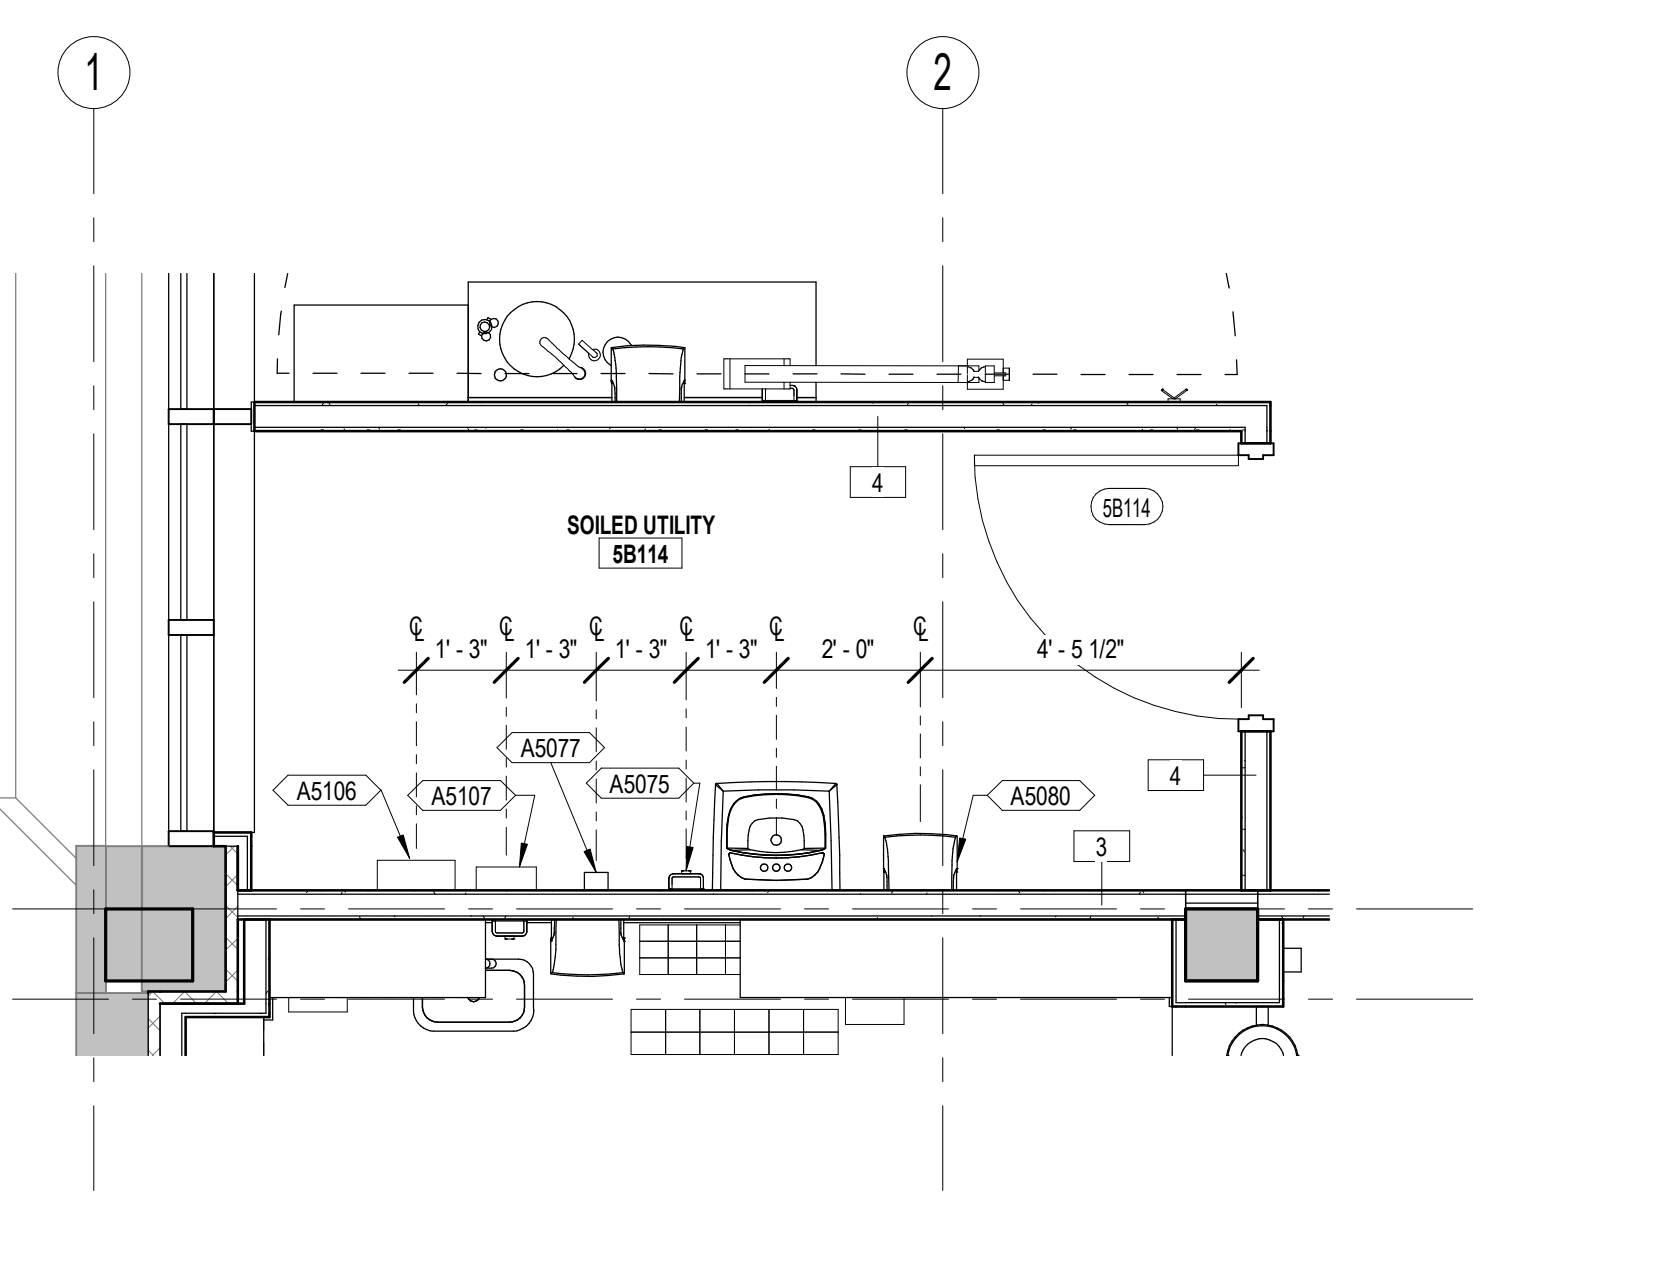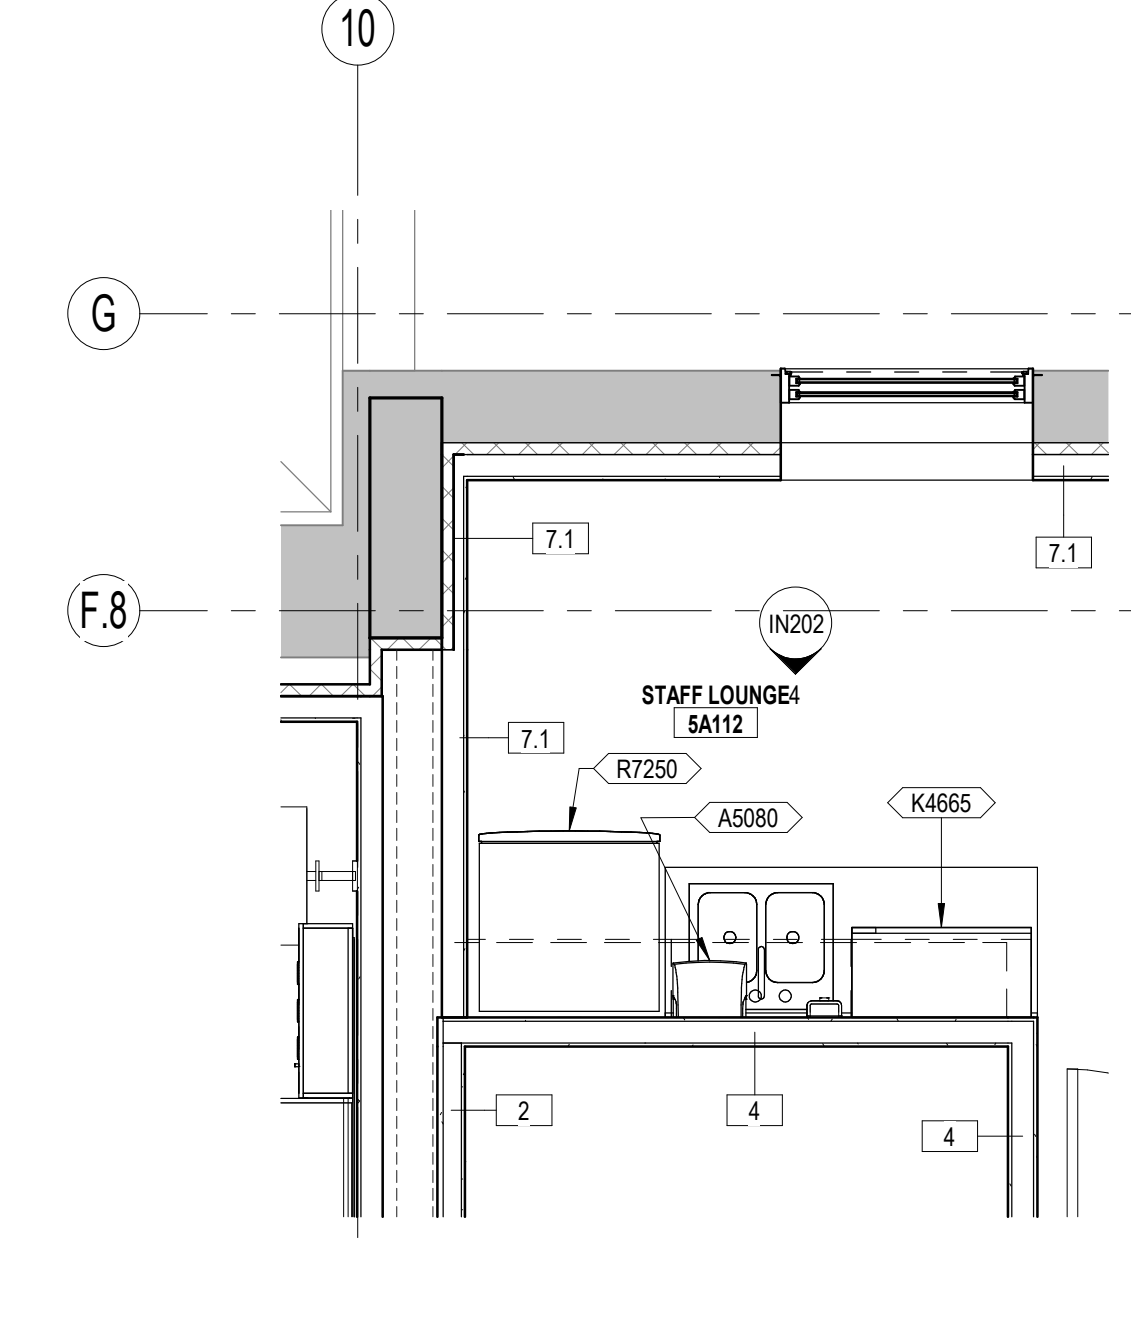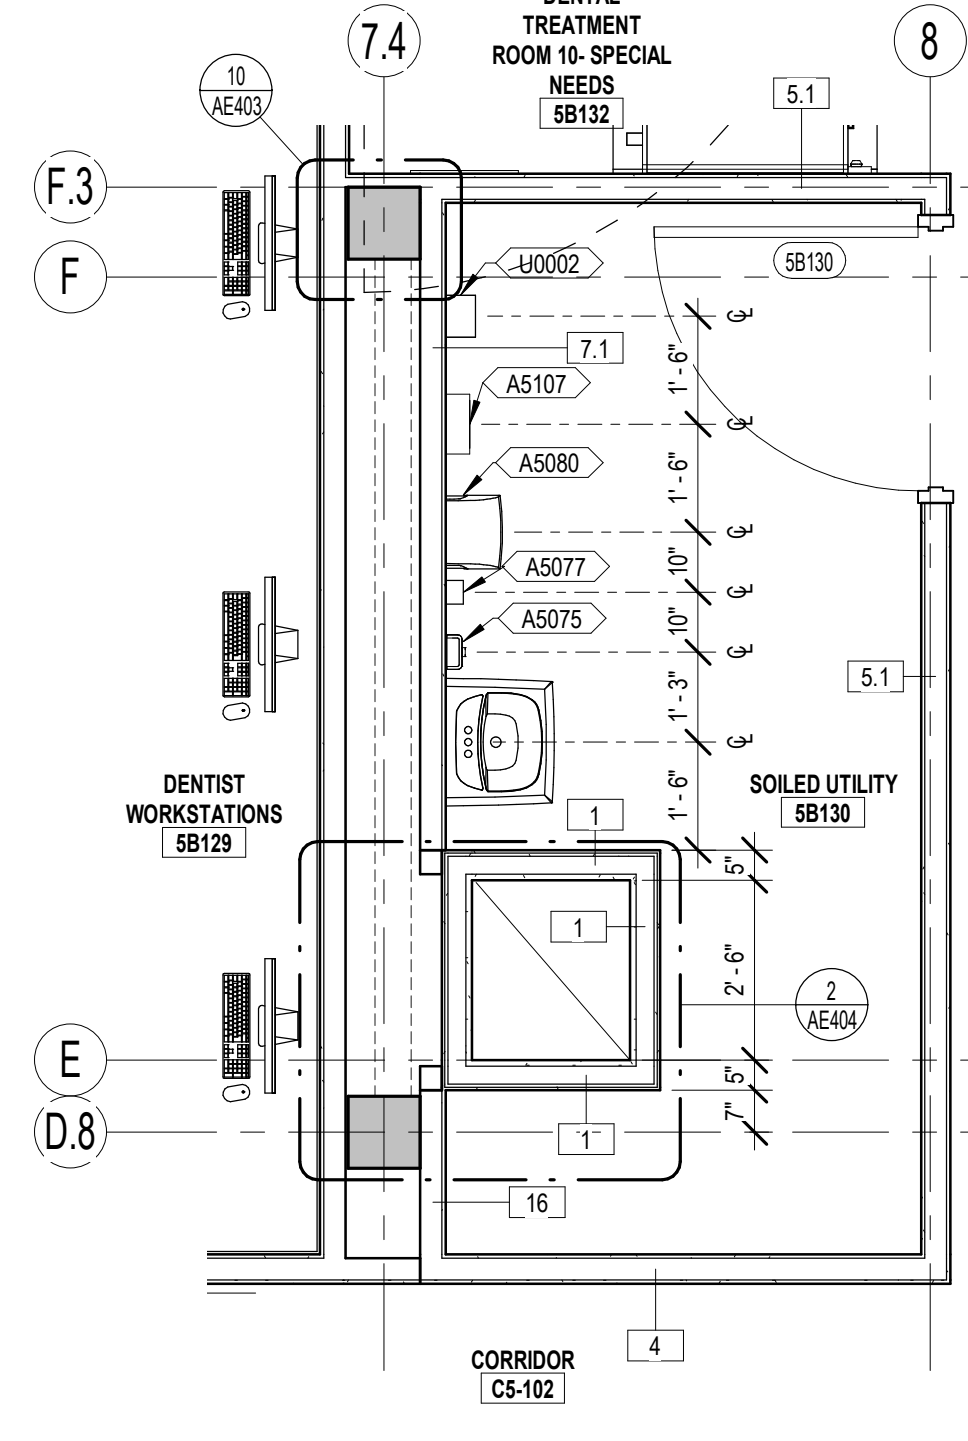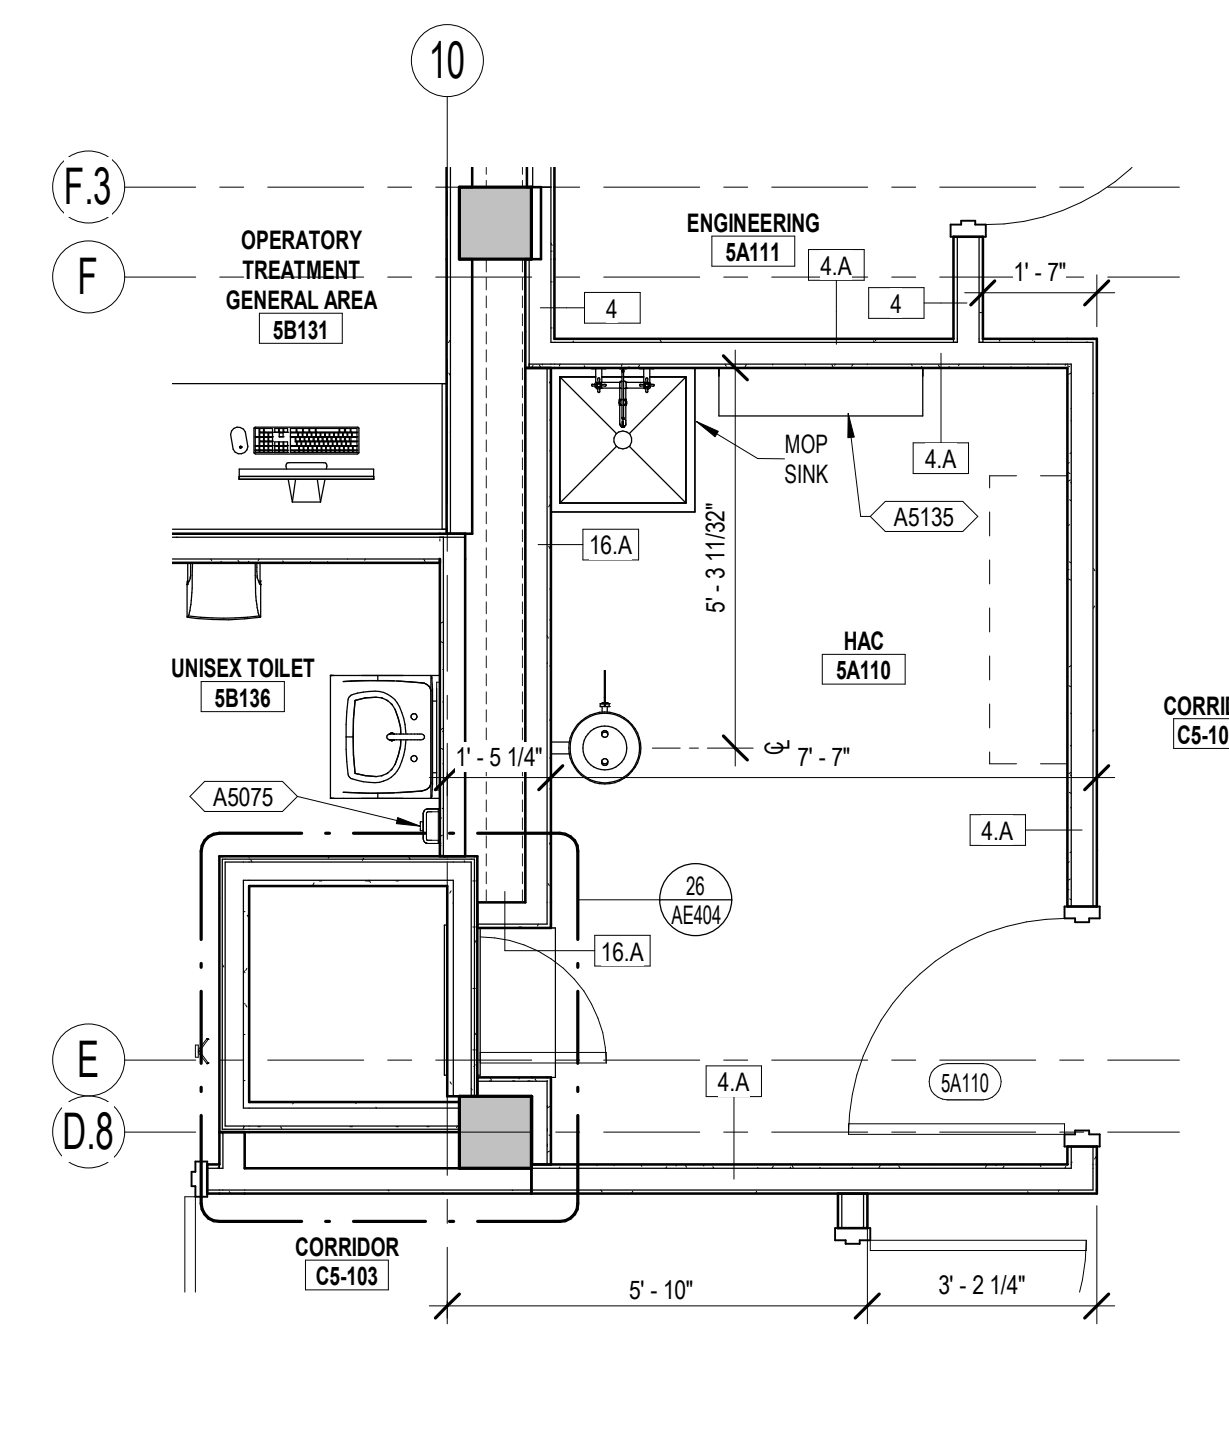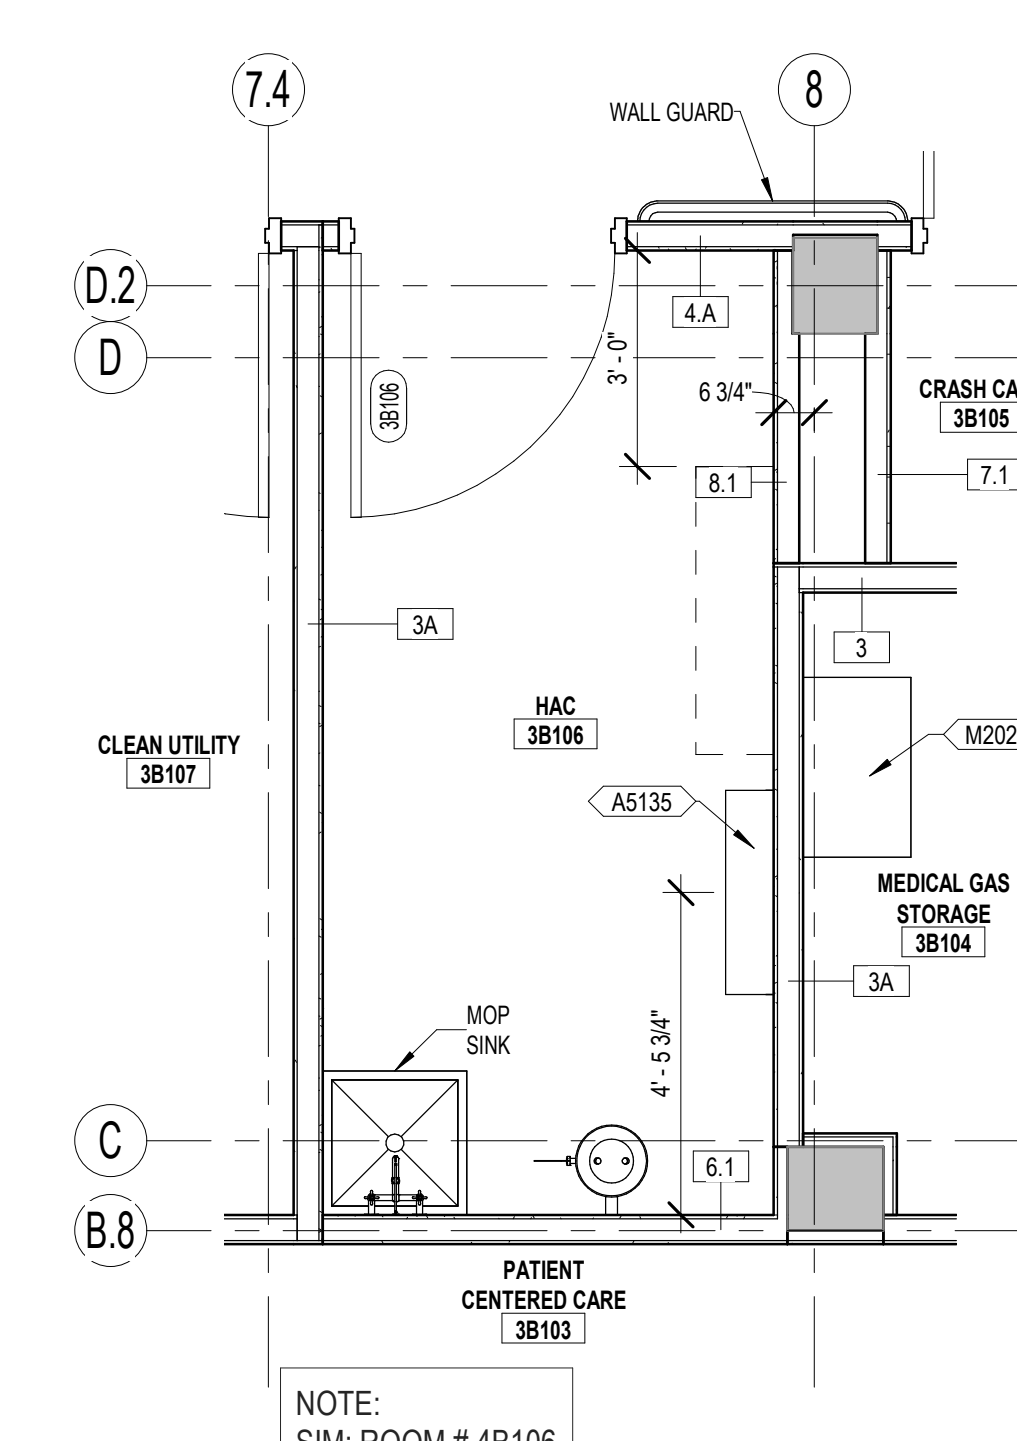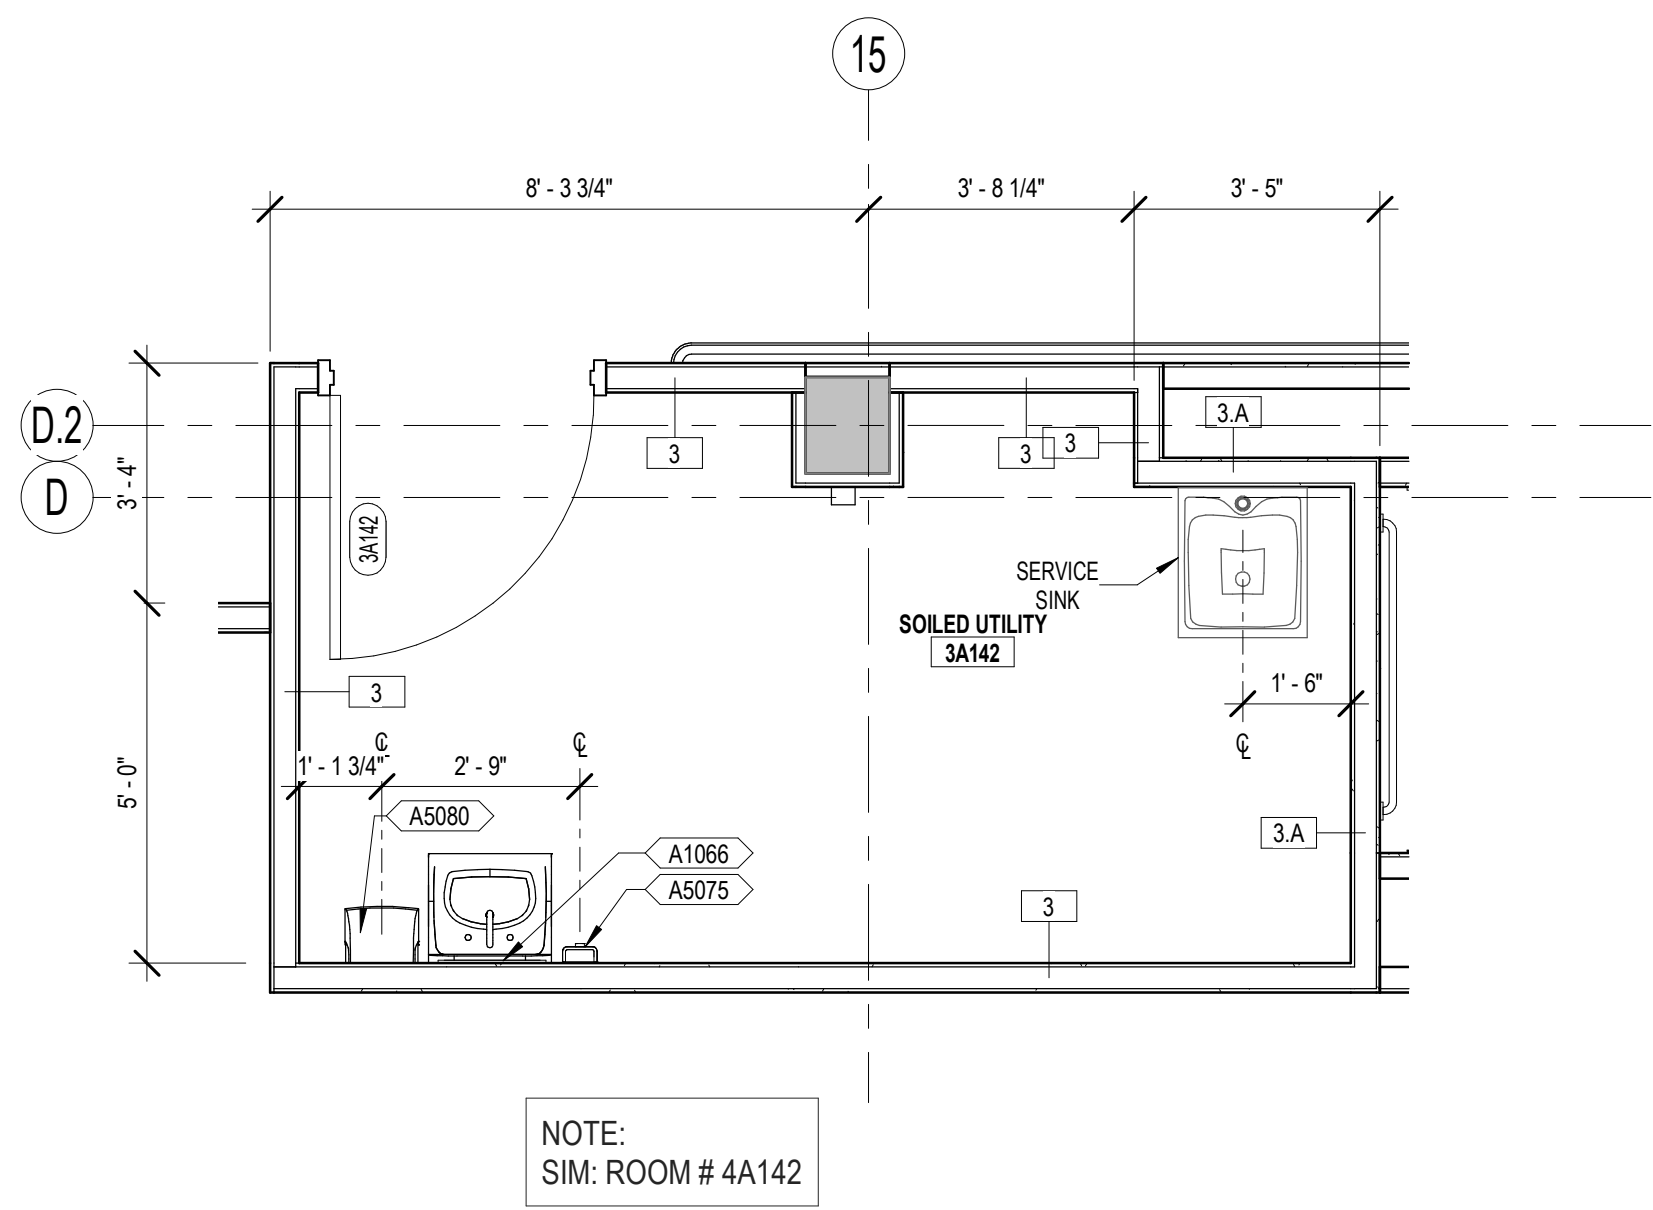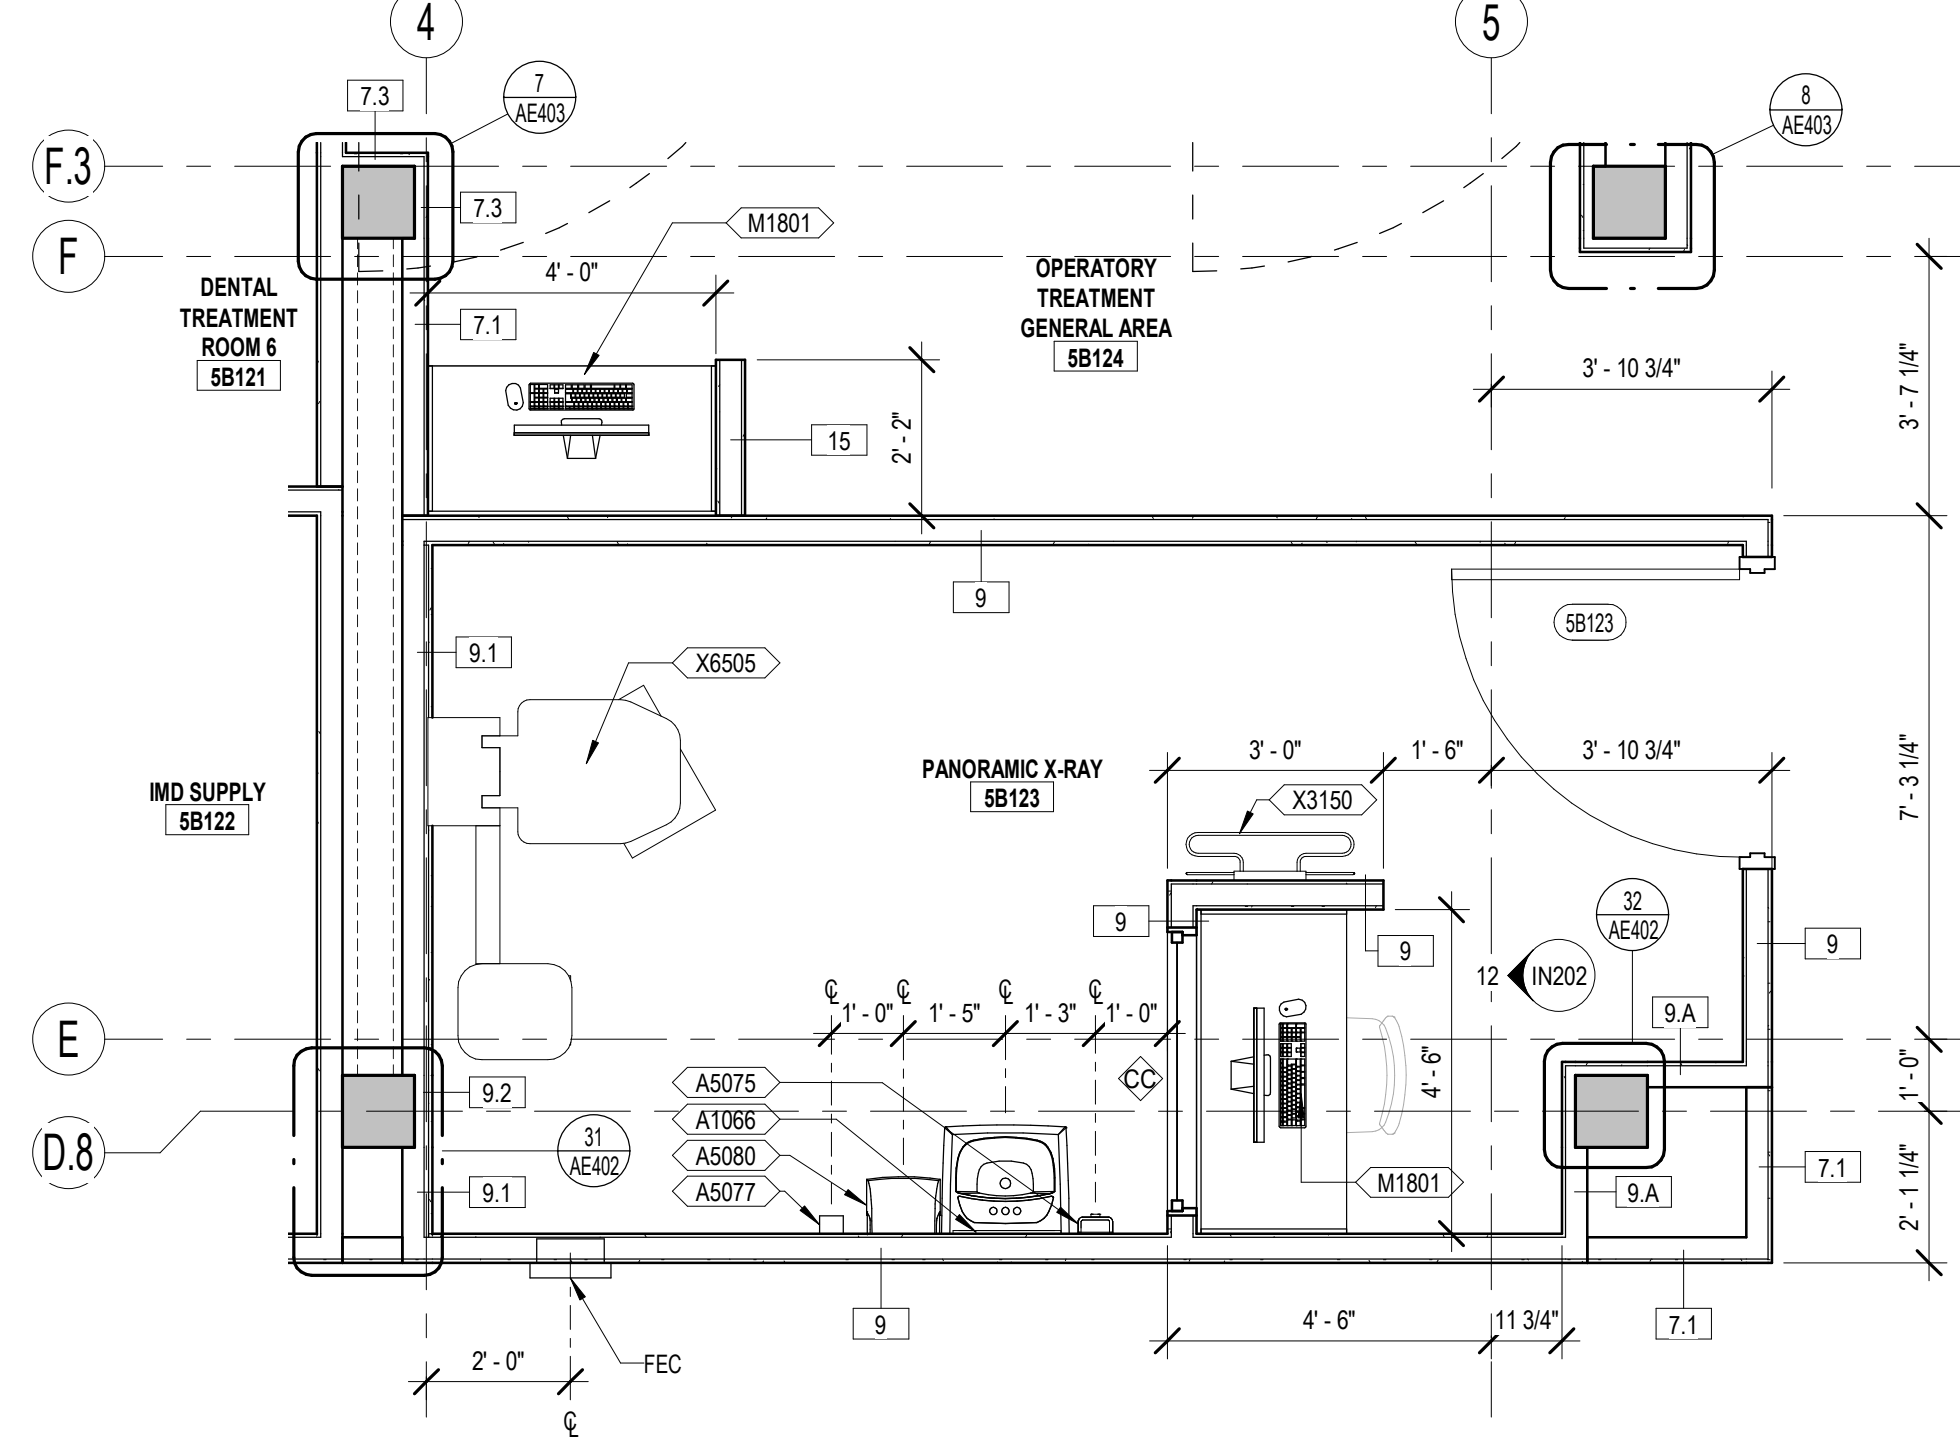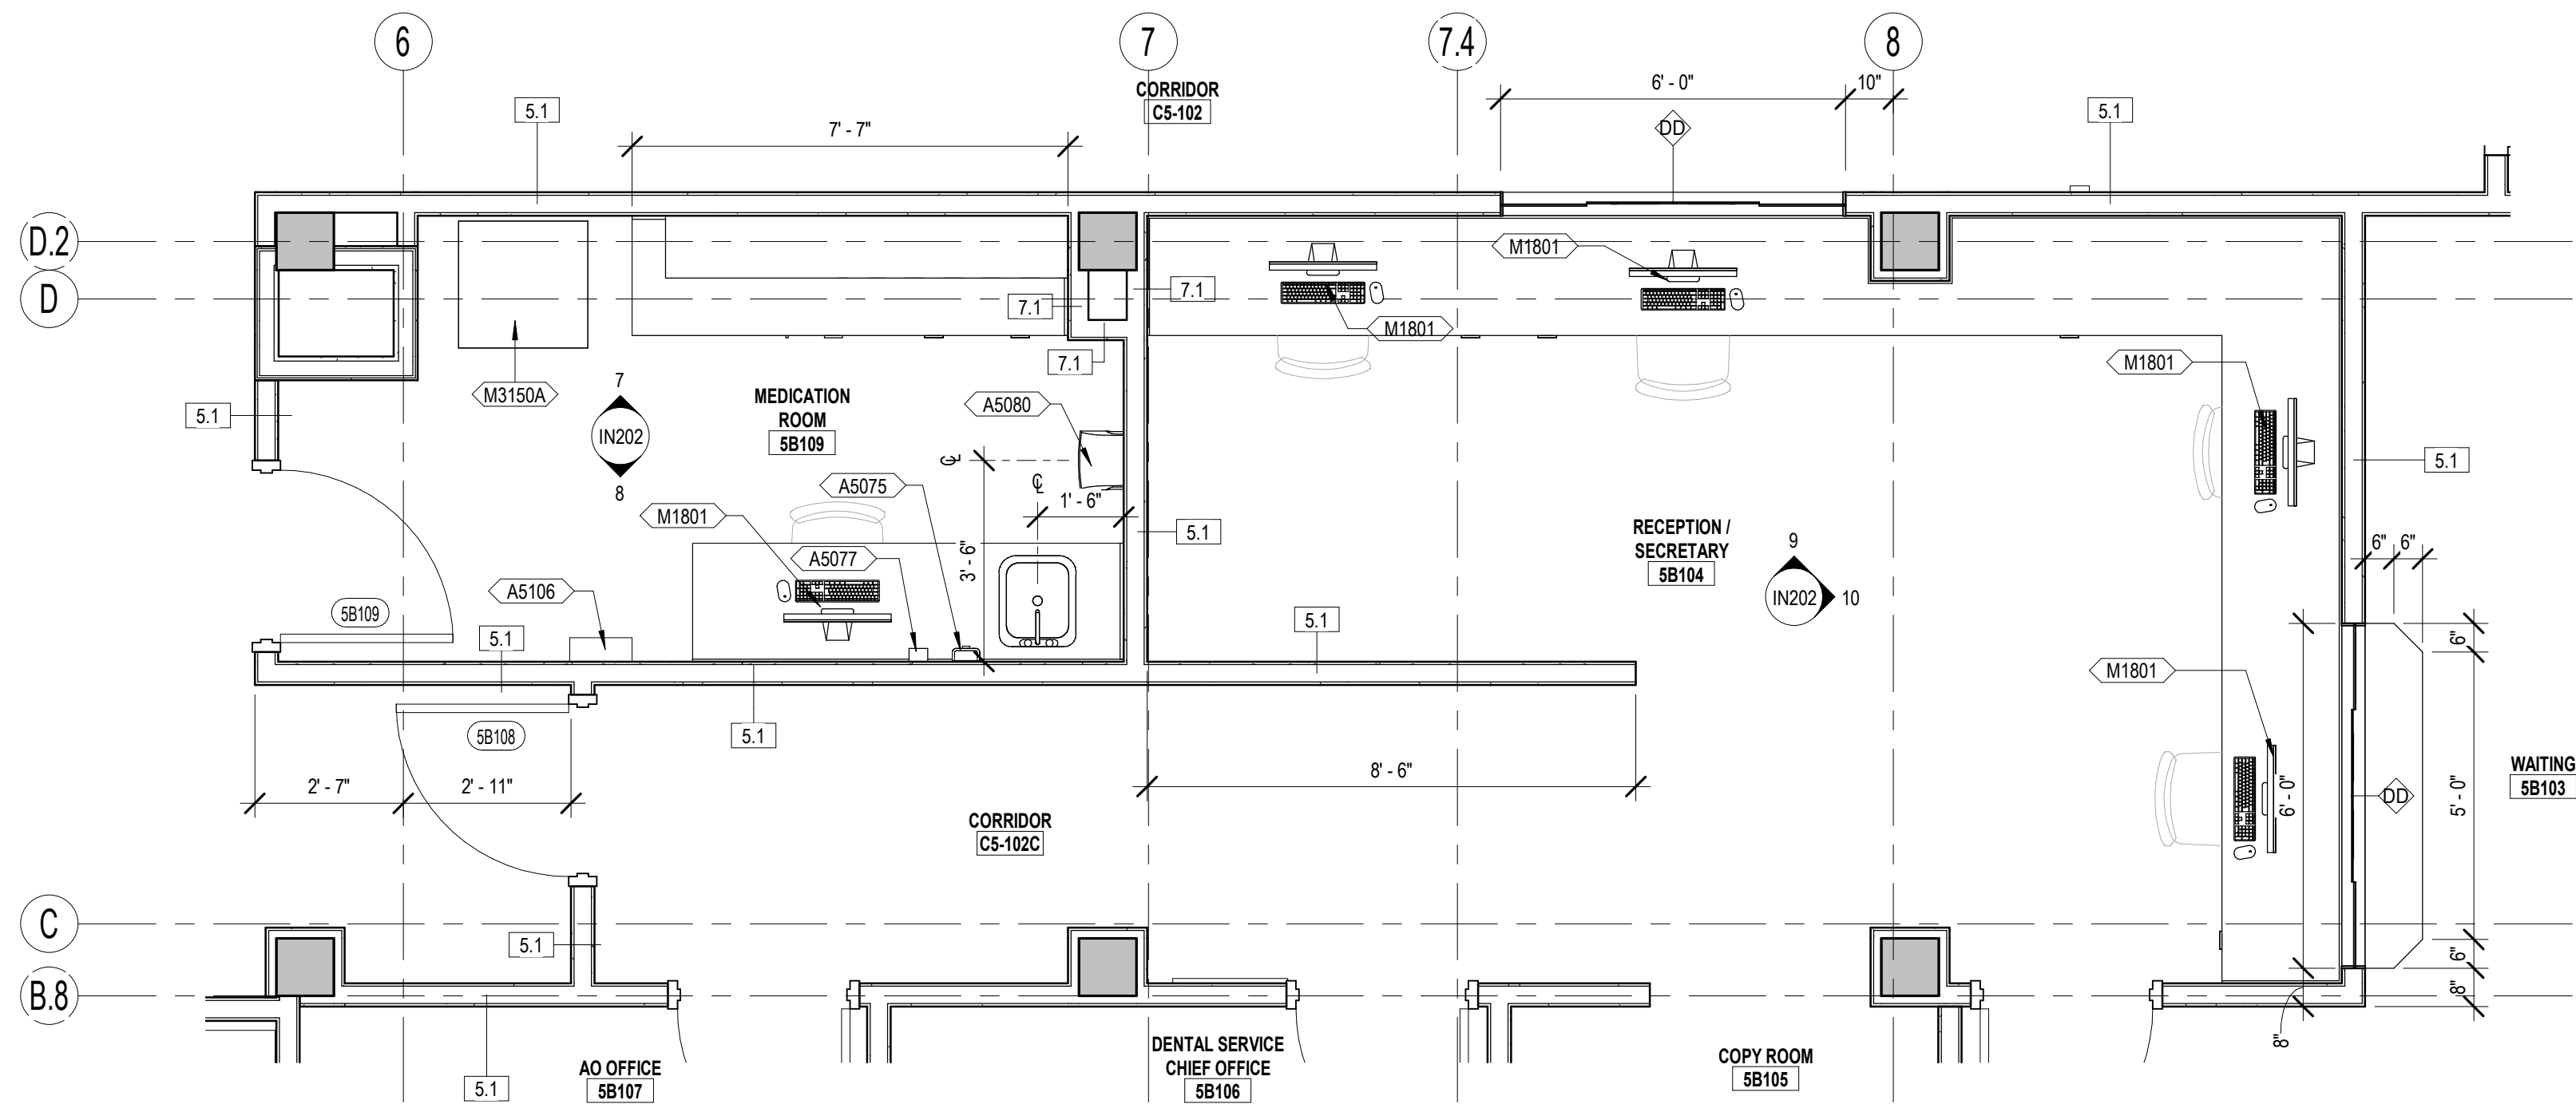

| EQUIPMENT SCHEDULE - SHEET AE125 |                                                        |              |
|----------------------------------|--------------------------------------------------------|--------------|
| JSN                              | DESCRIPTION                                            | ACTIVATED BY |
| A1066                            | MIRROR, FLOAT GLASS, WITH SS FRAME, 18 X 36            | CC           |
| A5075                            | DISPENSER, HAND SOAP                                   | VV           |
| A5077                            | HAND SANITIZER DISPENSER                               | VV           |
| A5080                            | DISPENSER, PAPER TOWEL                                 | VV           |
| A5106                            | WASTE DISPOSAL UNIT, SHARPS                            | VV           |
| A5107                            | GLOVE DISPENSER RACK                                   | VV           |
| A5135                            | SHELF, UTILITY W/MP/BROOM HOLDERS, SS, SURFACE MOUNTED | CC           |
| K4665                            | OVEN, MICROWAVE                                        | VV           |
| M1801                            | COMPUTER AND MONITOR                                   | VV           |
| M2025                            | RACK, STORAGE CYLINDER, GAS                            | VV           |
| M3150A                           | AUTOMATED STORAGE/DISPENSING UNIT(OMNICELL) - 1 CELL   | VV           |
| R6200                            | REFRIGERATOR, UNDERCOUNTER, 5 CU. FT                   | VV           |
| R7250                            | REFRIGERATOR/FREEZER, 20 CU. FT.                       | VV           |
| U0002                            | PDI WIPE DISPENSER                                     | VV           |
| X3150                            | RACK, APRON & GLOVE, WALL MOUNT                        | VV           |
| X6505                            | RADIOGRAPHIC UNIT, DENTAL PANOGRAPHIC                  | VV           |

| EQUIPMENT ABBREVIATIONS |                                     |
|-------------------------|-------------------------------------|
| CC:                     | CONTRACTOR FURNISHED & INSTALLED    |
| VV:                     | VA FURNISHED & INSTALLED            |
| VC:                     | VA FURNISHED & CONTRACTOR INSTALLED |

| RESTROOM ACCESSORY NOTES |   |
|--------------------------|---|
| 1.                       | SEE SHEET G101 FOR SHOWER RECEPTOR TYPES.   |
| 2.                       | MOUNT WASTE RECEPTACLE TO MEET ABAS. MOUNT HIGHEST OPERABLE PART OF CONTROLS, DISPENSERS, RECEPTACLES AND OTHER OPERABLE EQUIPMENT BETWEEN 15'-48" ABOVE FINISH FLOOR. |
| 3.                       | ATTACH MIRROR PER MANUFACTURER STANDARD; CENTER MIRROR ON LAVATORY(S) BELOW.                                                                                           |
| 4.                       | ROBE HOOKS (A5145) TO BE MOUNTED ON TOILET SIDE OF DOOR, 48" FROM ABOVE FINISH FLOOR TO CENTER.                                                                        |
| 5.                       | FIELD VERIFY MOUNTING HEIGHTS WITH RESIDENT ENGINEER BEFORE INSTALLATION.                                                                                              |
| 6.                       | PROVIDE & INSTALL PRE-JOINED (PLASTIC COVER) INSULATION FOR ALL EXPOSED PIPING, MEETING ALL APPLICABLE ABA REQUIREMENTS.                                               |

| RESTROOM ACCESSORY GENERAL NOTES |   |
|----------------------------------|---|
| A.                               | MOUNTING HEIGHTS REFERENCED ON SHEET G101. VERIFY ALL MOUNTING HEIGHTS WITH CODES AND MANUFACTURER RECOMMENDATIONS.                                |
| B.                               | ABA TOILET PARTITION DOOR MUST BE 34" MINIMUM CLEAR OPENING.                                                                                       |
| C.                               | WHERE DIMENSIONS ARE INDICATED ON PLAN AS "CLEAR," THE DIMENSIONS ARE TAKEN FROM FACE OF FINISHED WALL MATERIAL TO FACE OF FINISHED WALL MATERIAL. |
| D.                               | SEE SHEET Q104 FOR EQUIPMENT SCHEDULE.   |

## BID DOCUMENTS

| NO. | REVISIONS | DATE |
|-----|-----------|------|
|     |           |      |
|     |           |      |
|     |           |      |
|     |           |      |
|     |           |      |

|            |
|------------|
| CONSULTANT |
|------------|

|                                      |
|--------------------------------------|
| ARCHITECT/ENGINEER OF RECORD         |
| THOMAS OLESAC, ARCHITECT             |
| MS Lic # 5505                        |
| 1050 HOYT AVE WEST ST PAUL, MN 55117 |
| 952-451-0460                         |


|                      |
|----------------------|
| STAMP                |
| REGISTERED ARCHITECT |
| Thomas Olesac        |
| STATE OF MISSISSIPPI |
| 03.10.2023           |

|                                                  |
|--------------------------------------------------|
| Office of Construction and Facilities Management |
| VA U.S. Department of Veterans Affairs           |

|                      |
|----------------------|
| Drawing Title        |
| ENLARGED FLOOR PLANS |
| Approved:            |

|                        |
|------------------------|
| Phase                  |
| CONSTRUCTION DOCUMENTS |
| FULLY SPRINKLERED      |

|                     |
|---------------------|
| Project Title       |
| RENOVATE BUILDING 1 |
| Location            |
| BILOXI, MISSISSIPPI |
| Issue Date          |
| 03/10/2023          |
| Checked             |
| LA                  |
| Drawn               |
| CD,PC               |
| Project Number      |
| 520-317X            |
| Building Number     |
| 1                   |
| Drawing Number      |
| AE125               |
| Dwg. 81 of 238      |

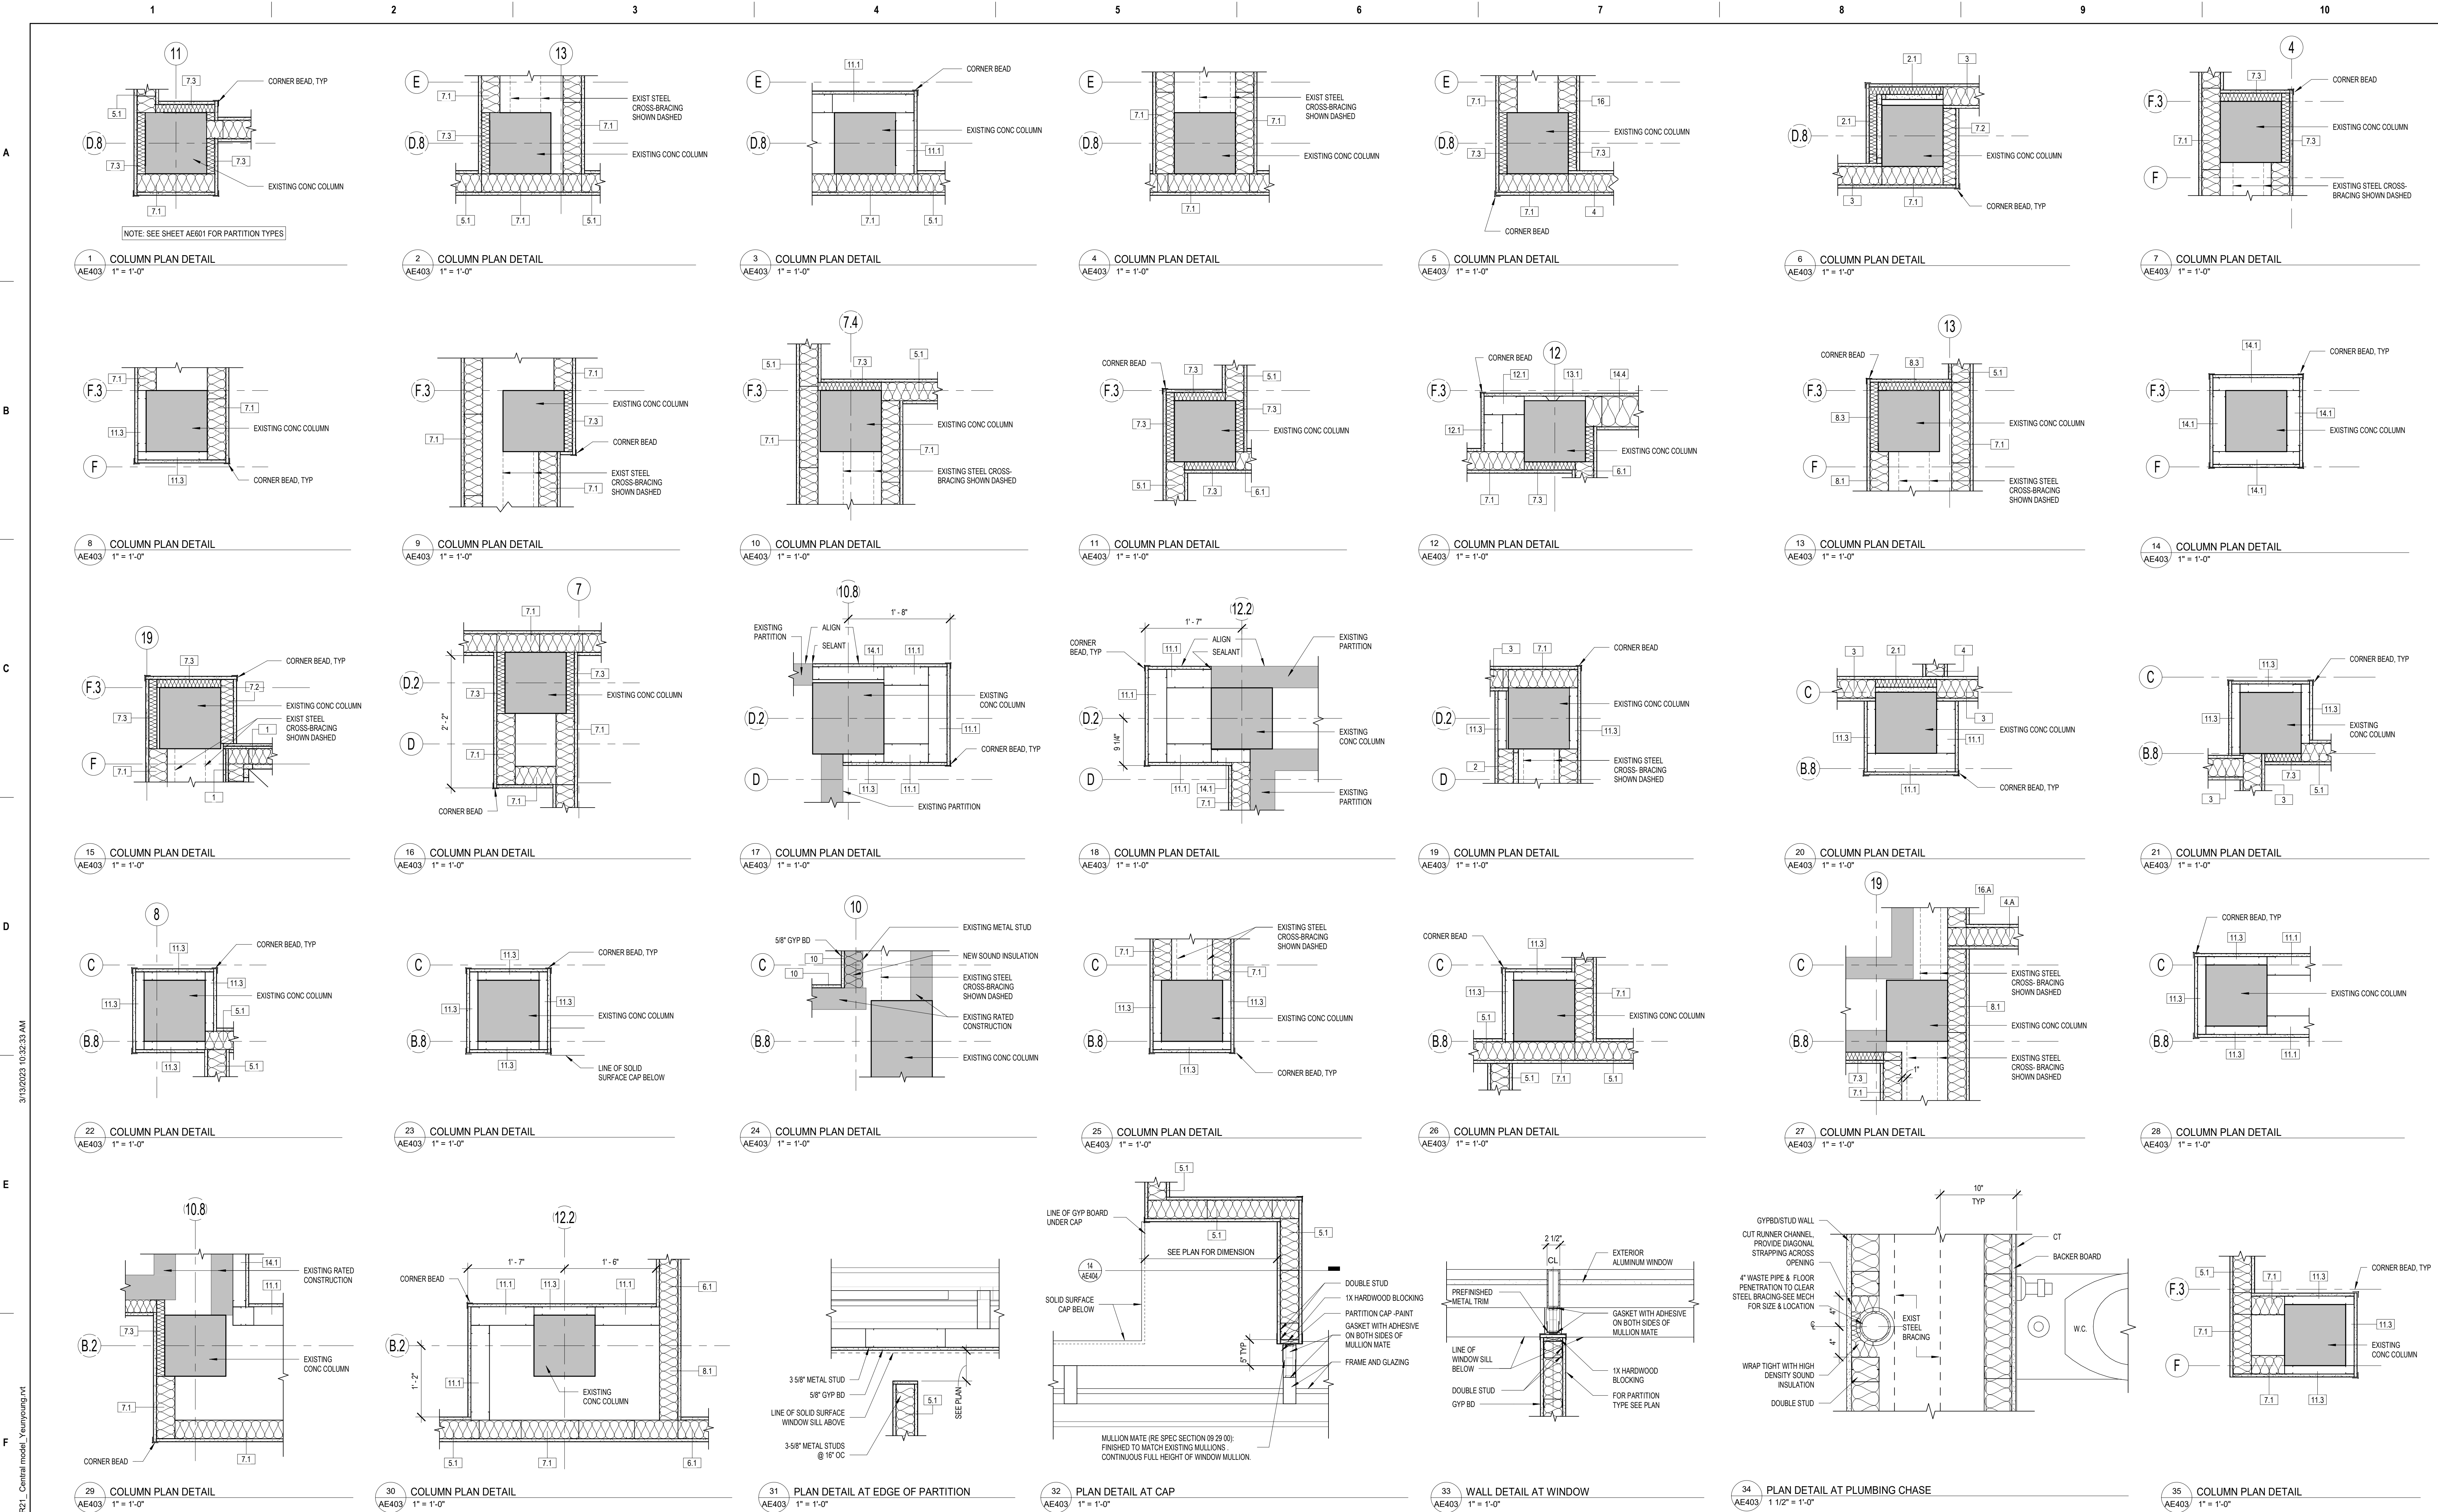

BID DOCUMENTS

| NO. | REVISIONS | DATE |
|-----|-----------|------|
|     |           |      |
|     |           |      |
|            |
|------------|
| CONSULTANT |
|            |
|            |
|                                      |
|--------------------------------------|
| ARCHITECT/ENGINEER OF RECORD         |
| THOMAS OLESAK, ARCHITECT             |
| MS Lic # 5505                        |
| 1050 HOYT AVE WEST ST PAUL, MN 55117 |
| 952-451-0460                         |

|                      |
|----------------------|
| STAMP                |
| REGISTERED ARCHITECT |
| Thomas Olesak        |
| STATE OF MISSISSIPPI |
| 03.10.2023           |


|                                                           |
|-----------------------------------------------------------|
| Office of<br>Construction<br>and Facilities<br>Management |
| VA U.S. Department<br>of Veterans<br>Affairs              |

|               |
|---------------|
| Drawing Title |
| PLAN DETAILS  |
| Approved:     |
|               |

|                           |
|---------------------------|
| Phase                     |
| CONSTRUCTION<br>DOCUMENTS |
| FULLY SPRINKLERED         |

|                     |
|---------------------|
| Project Title       |
| RENOVATE BUILDING 1 |
| Location            |
| BILOXI, MISSISSIPPI |
| Issue Date          |
| 03/10/2023          |
| Checked             |
| LA                  |
| Drawn               |
| CD, PC              |

|                 |
|-----------------|
| Project Number  |
| 520-317X        |
| Building Number |
| 1               |
| Drawing Number  |
| AE403           |
| Dwg. 94 of 238  |

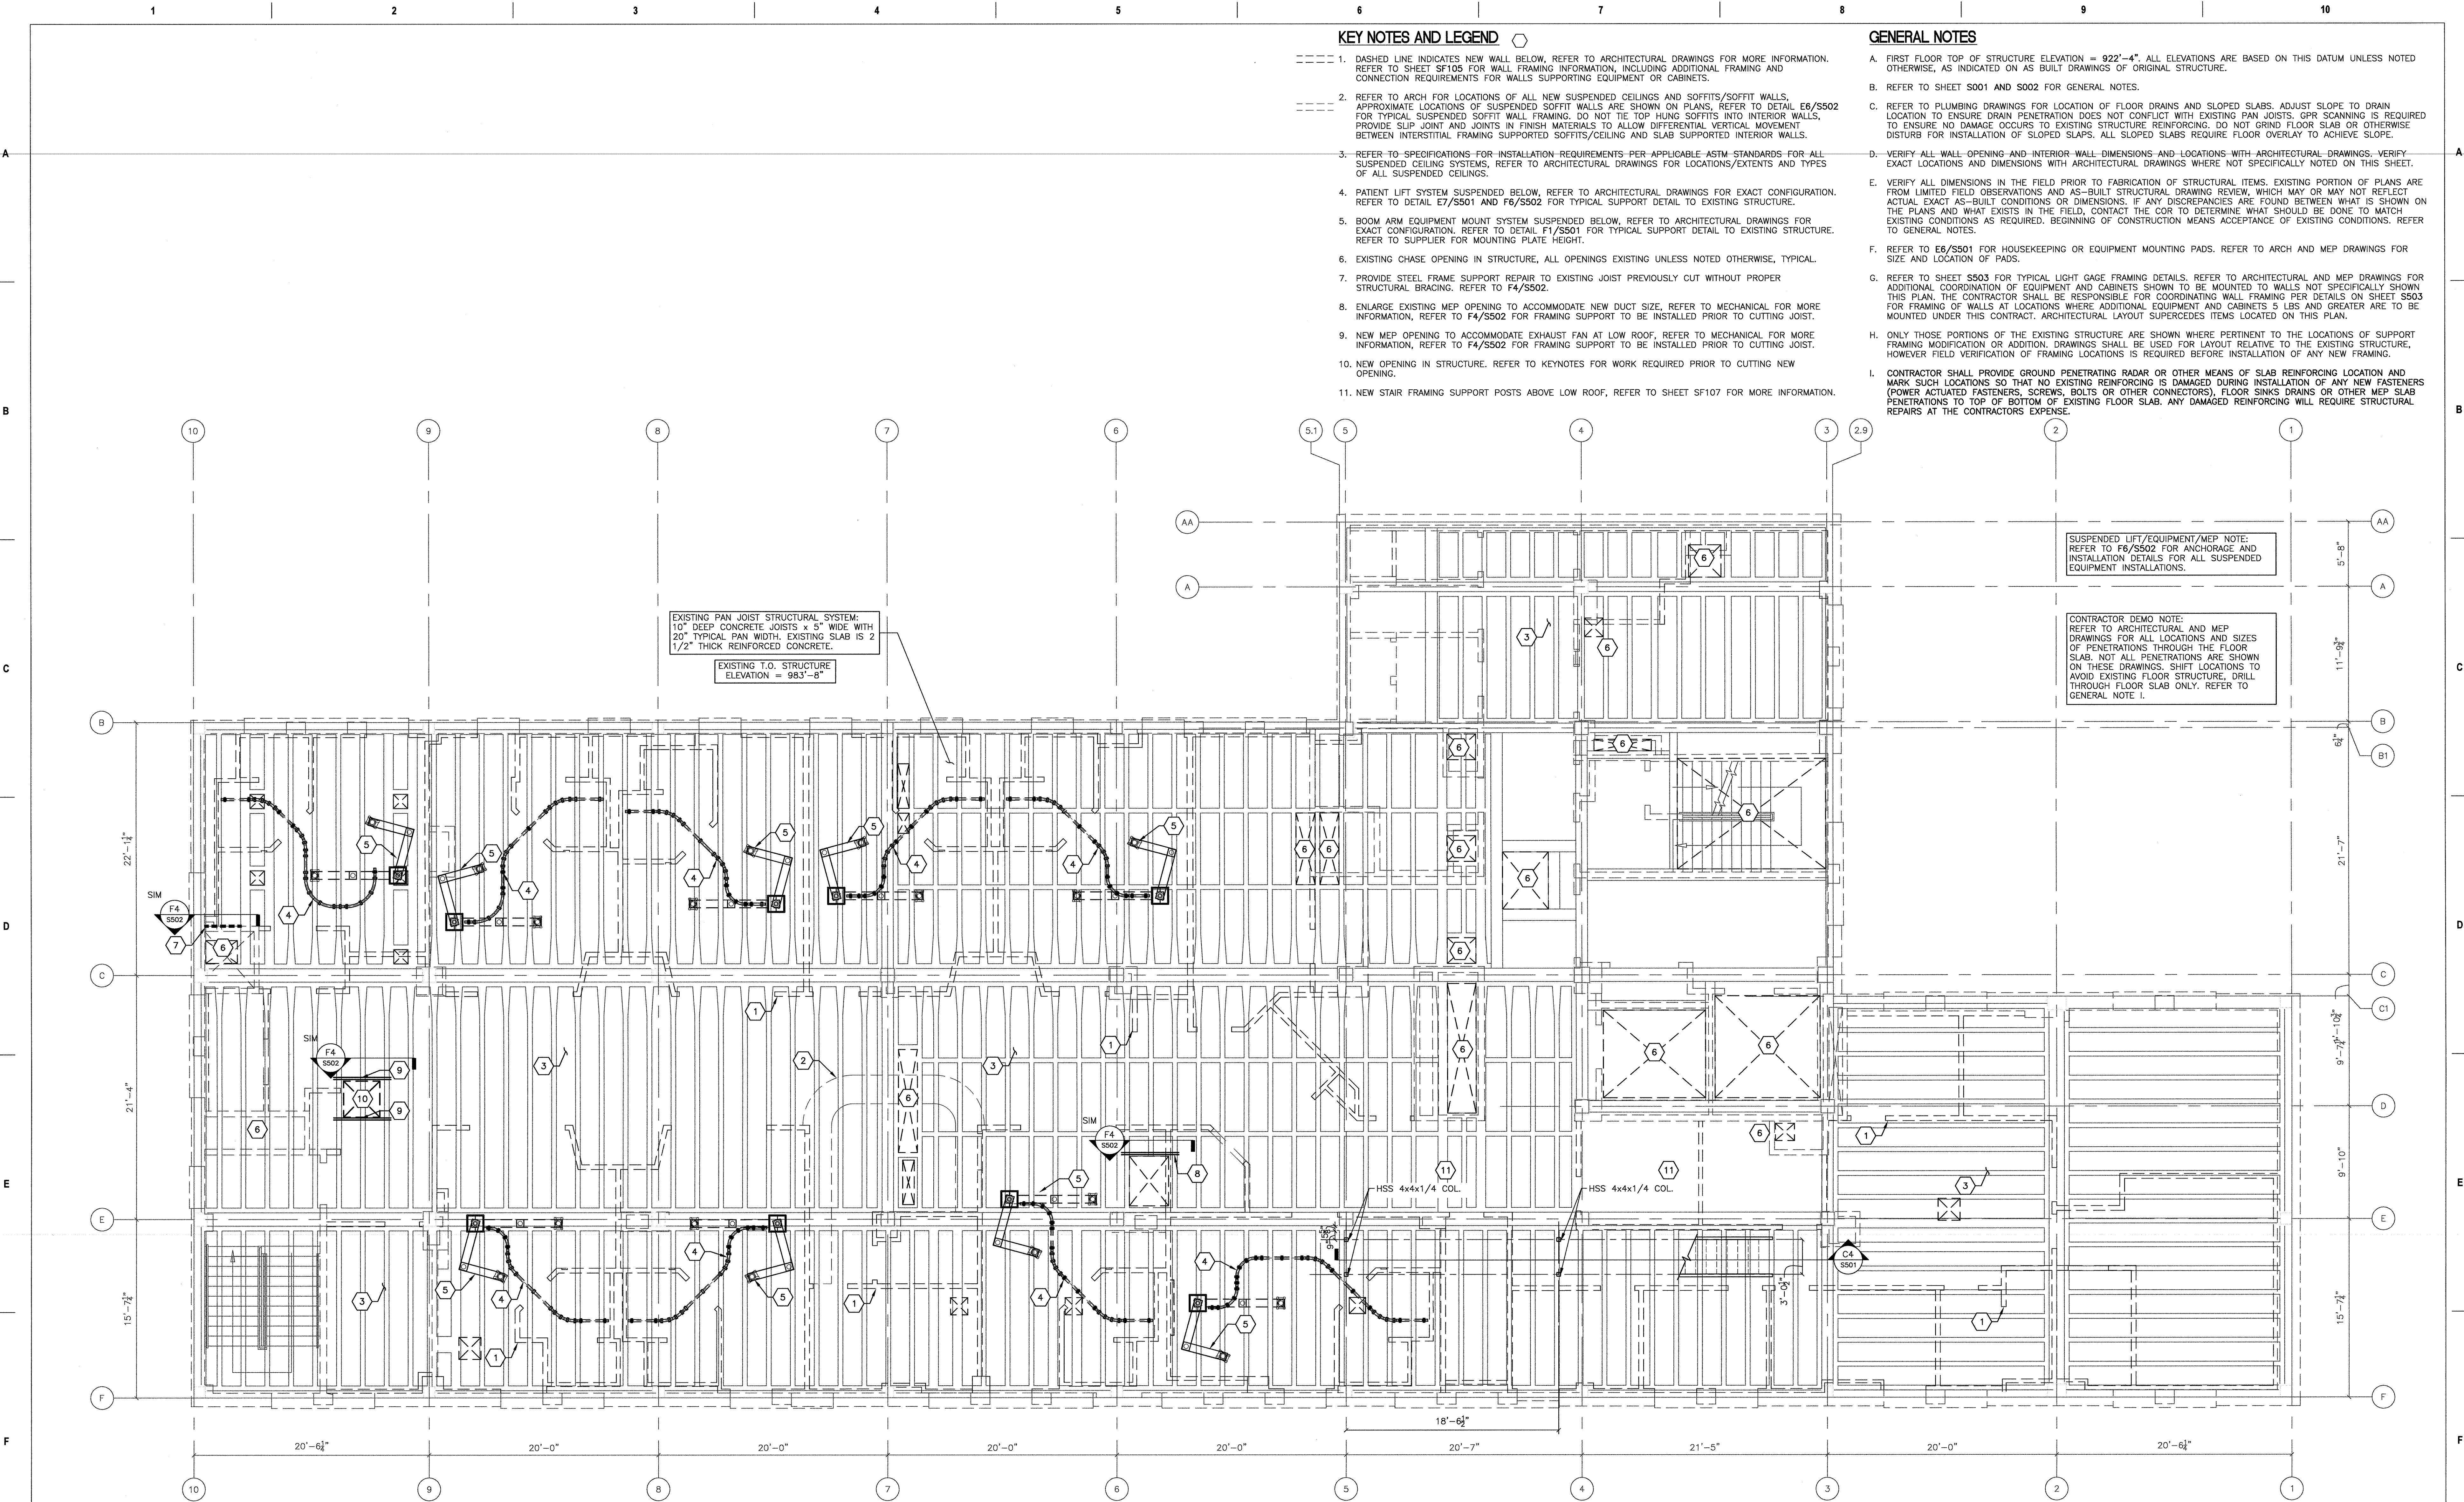

FI ROOF FRAMING FRAMING PLAN  
3/16" = 1'-0"

FULLY SPRINKLED


|            |       |
|------------|-------|
| Revisions: | Date: |
|            |       |
|            |       |
CONSULTANT

ARCHITECT/ENGINEER OF RECORD

**paradigm**  
Architecture | Engineering | Design-Build  
200 Envoy Circle, Suite 201, Louisville, KY 40299  
www.paradigmusa.com

STAMP

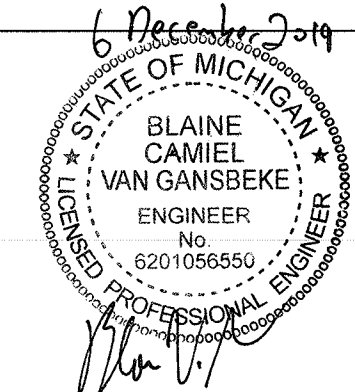

Office of  
Construction  
and Facilities  
Management

**VA** U.S. Department  
of Veterans Affairs

Drawing Title

ROOF FRAMING PLAN

Approved: Project Director

Phase

ISSUED FOR CONSTRUCTION

FULLY SPRINKLERED

Project Title

REMODEL ICU -TELEMETRY FOR  
PATIENT PRIVACY

Location

VA MEDICAL CENTER  
3800 30TH ST, DES MOINES, IOWA 5030

Issue Date

12-06-2019

Checked

BVG

Drawn

DRW

Project Number



636A6-18-313


Building Number

1W


Drawing Number

SF106

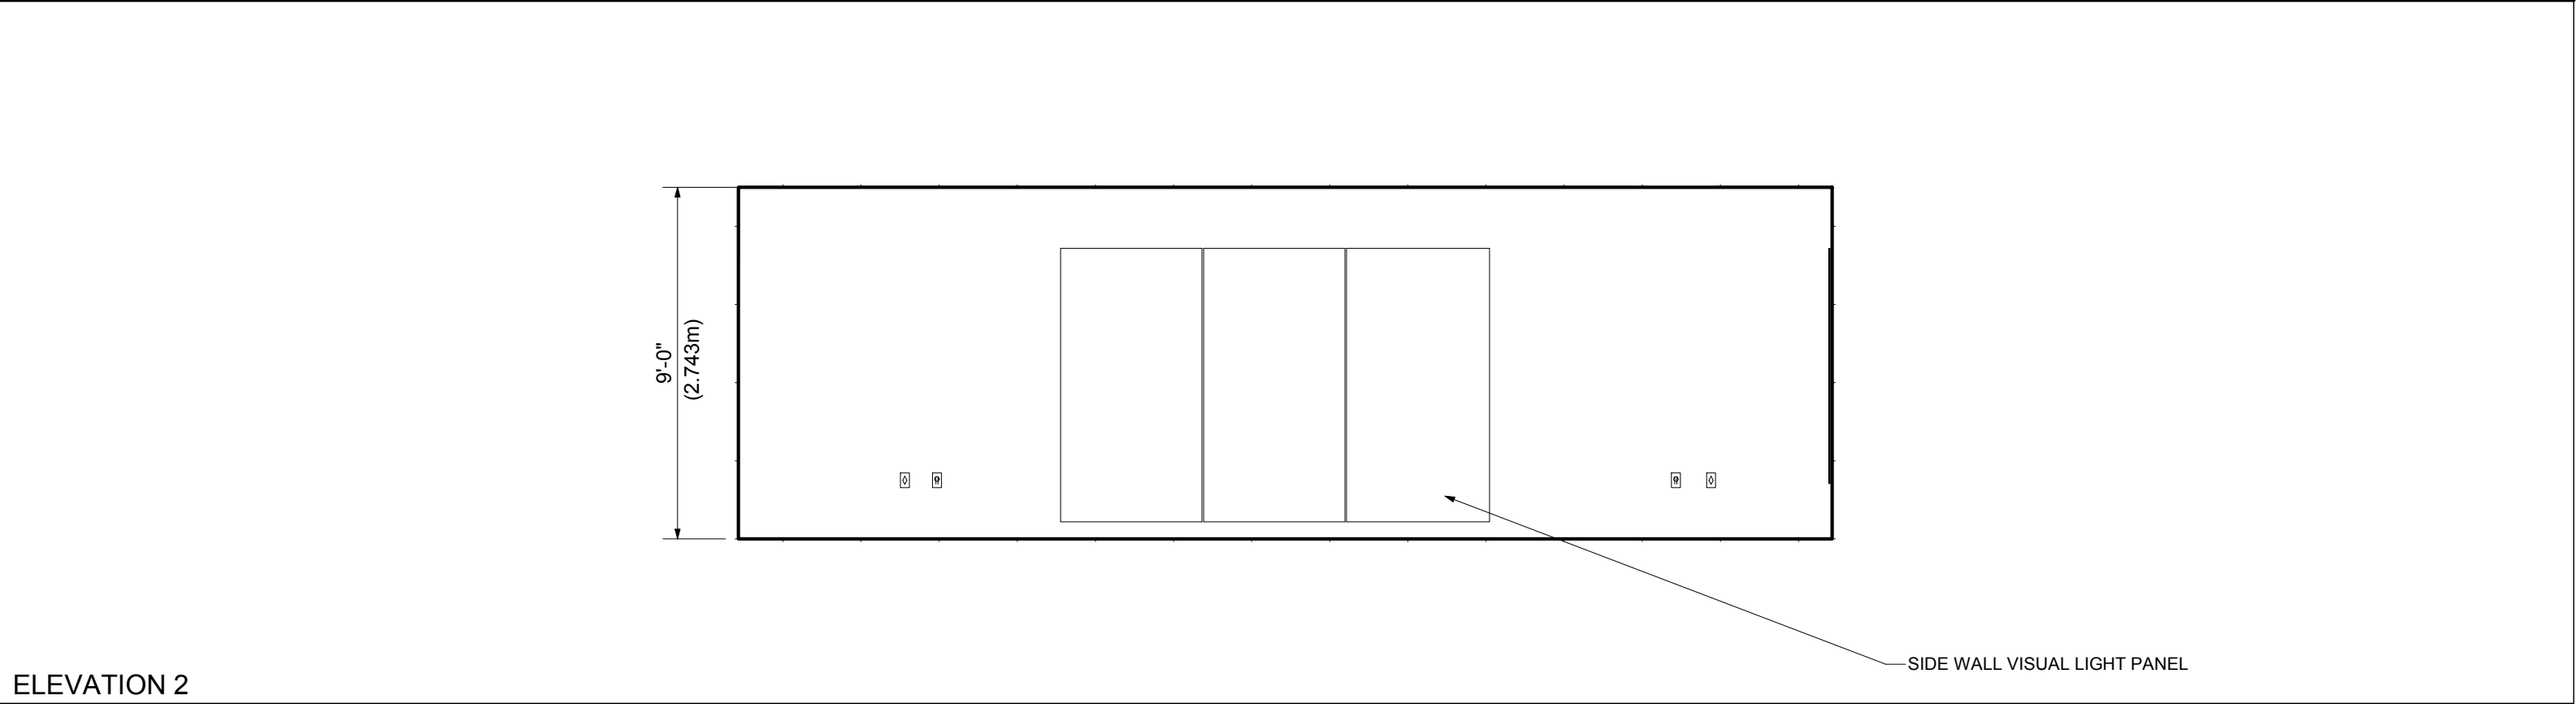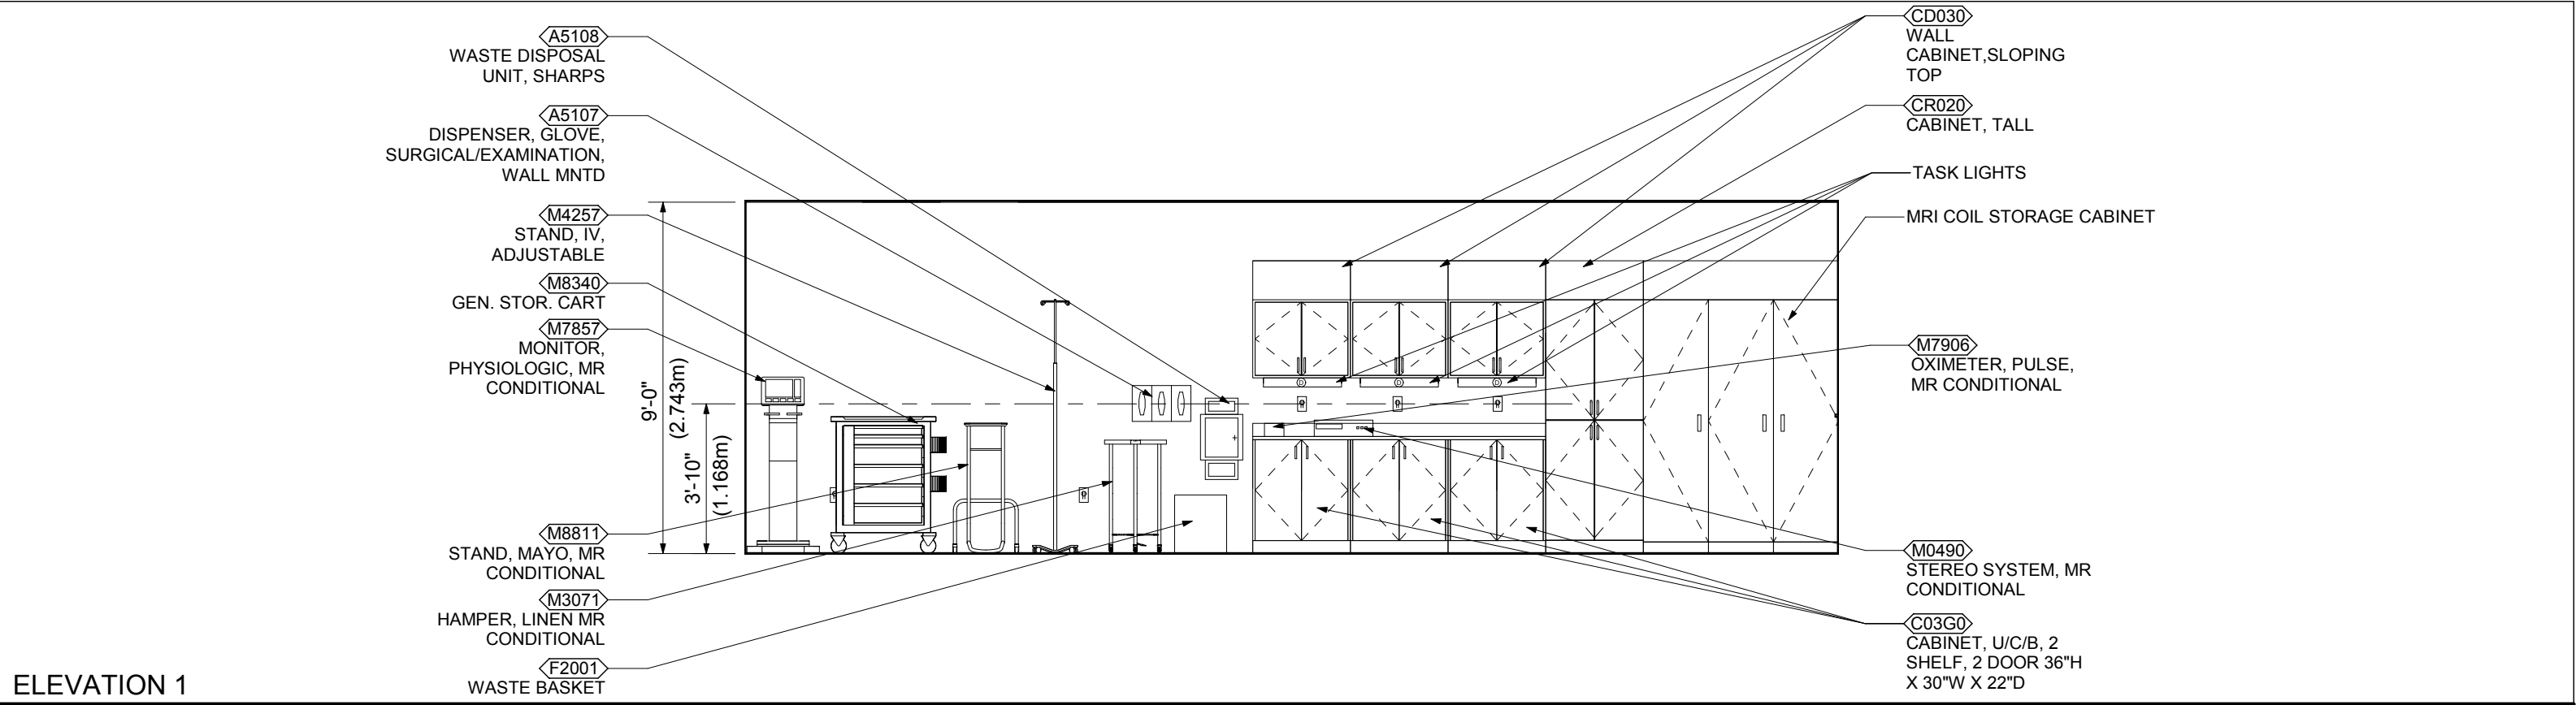


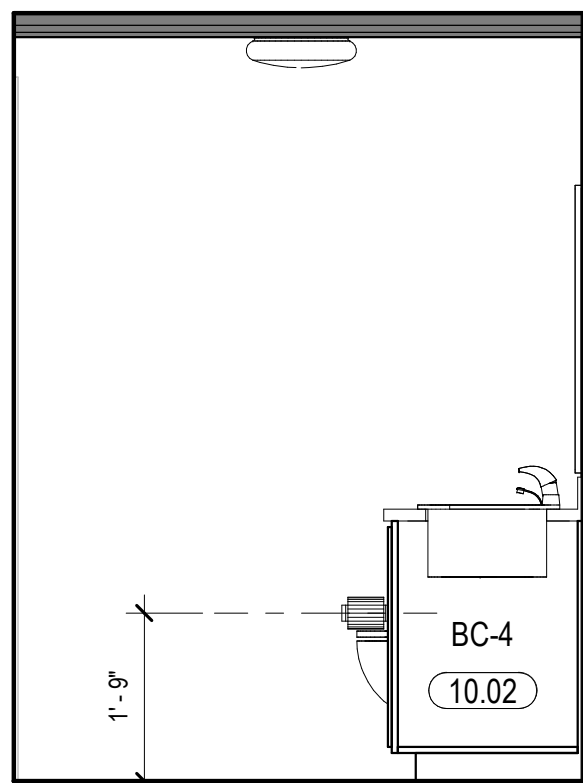


**(K5) BATHROOM - RM 103 - INT EL 2**  
1/2" = 1'-0"

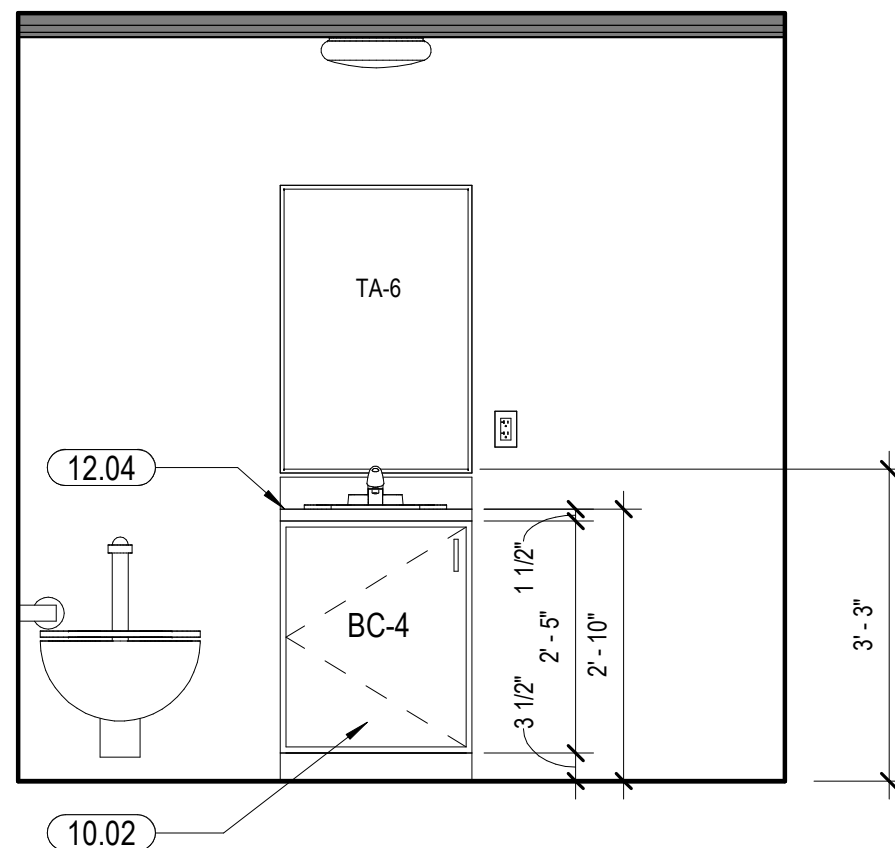


**(K9) BATHROOM - RM 103 - INT EL 3**  
1/2" = 1'-0"

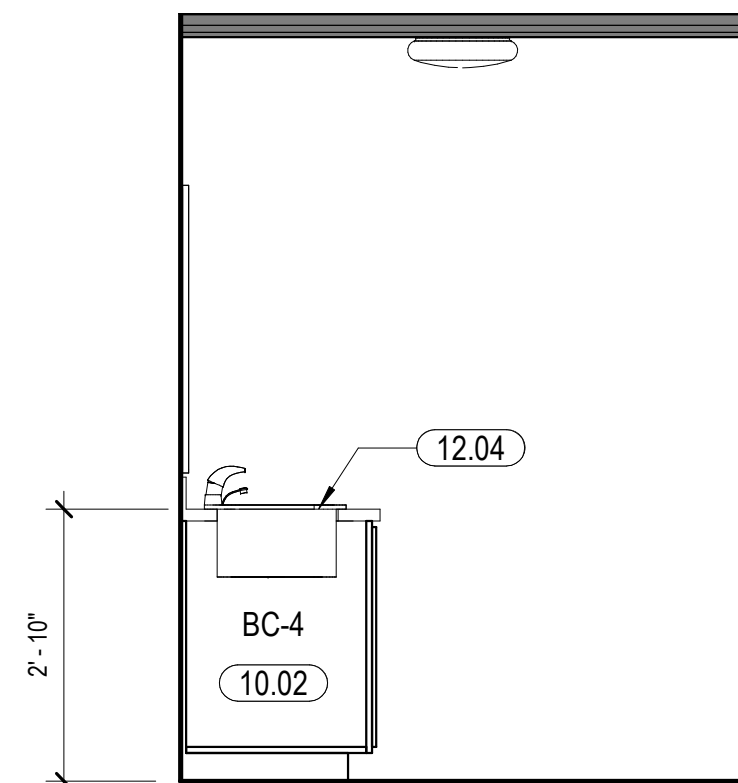


**K13** BATHROOM - RM 103 - INT EL 4  
1/2" = 1'-0"

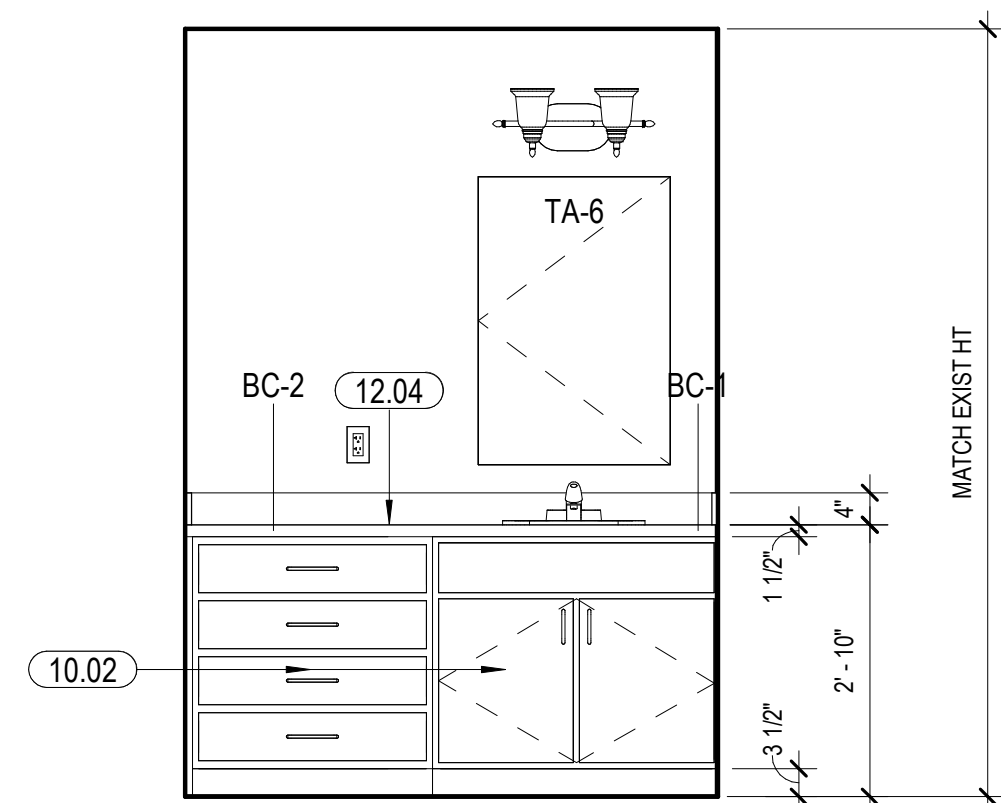


**E1** **BEDROOM CASEWORK - INT EL 1**  
1/2" = 1'-0"

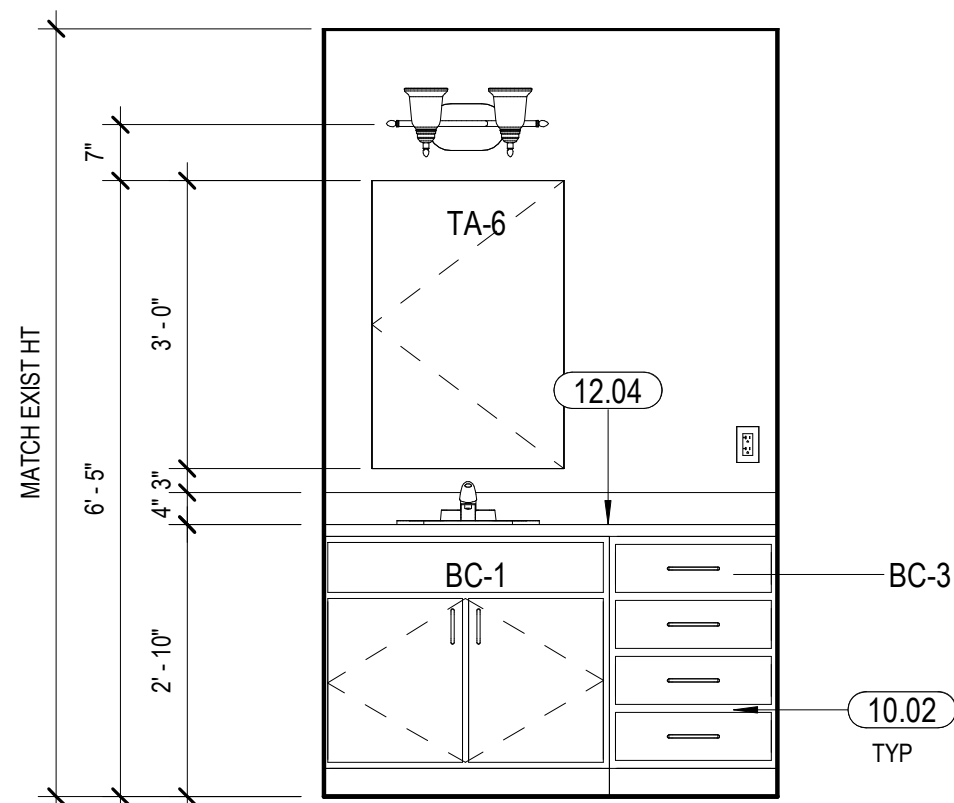


**(E5) BEDROOM CASEWORK - INT EL 2**  
1/2" = 1'-0"

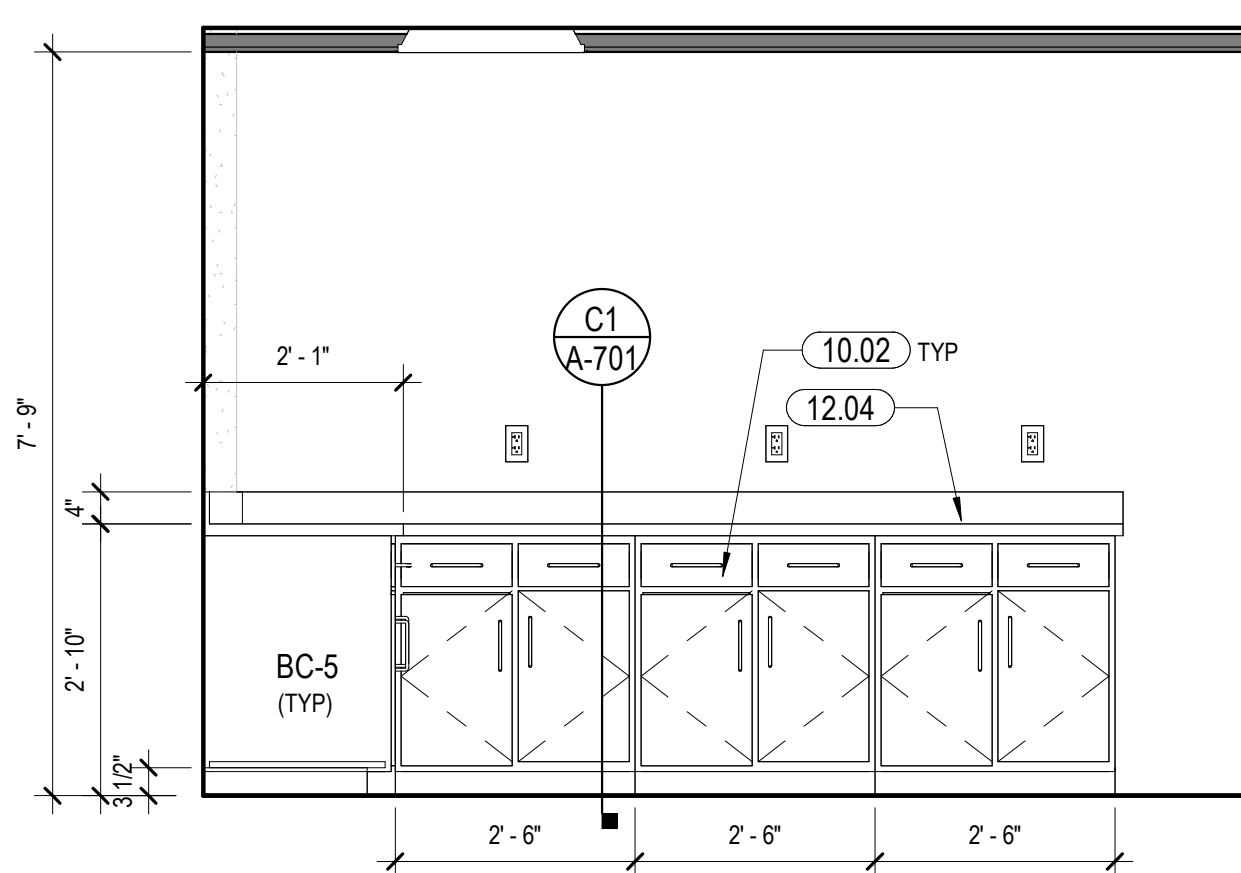

**E9 LOUNGE/CAFE - INT EL 1**  
1/2" = 1'-0"

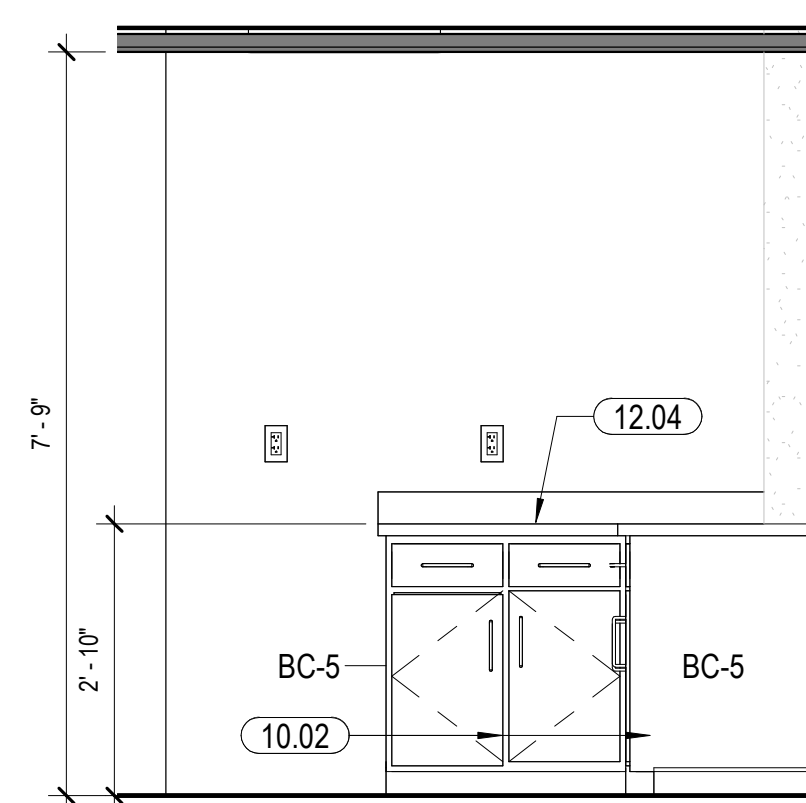

**E13** LOUNGE/CAFE - INT EL 2  
1/2" = 1'-0"

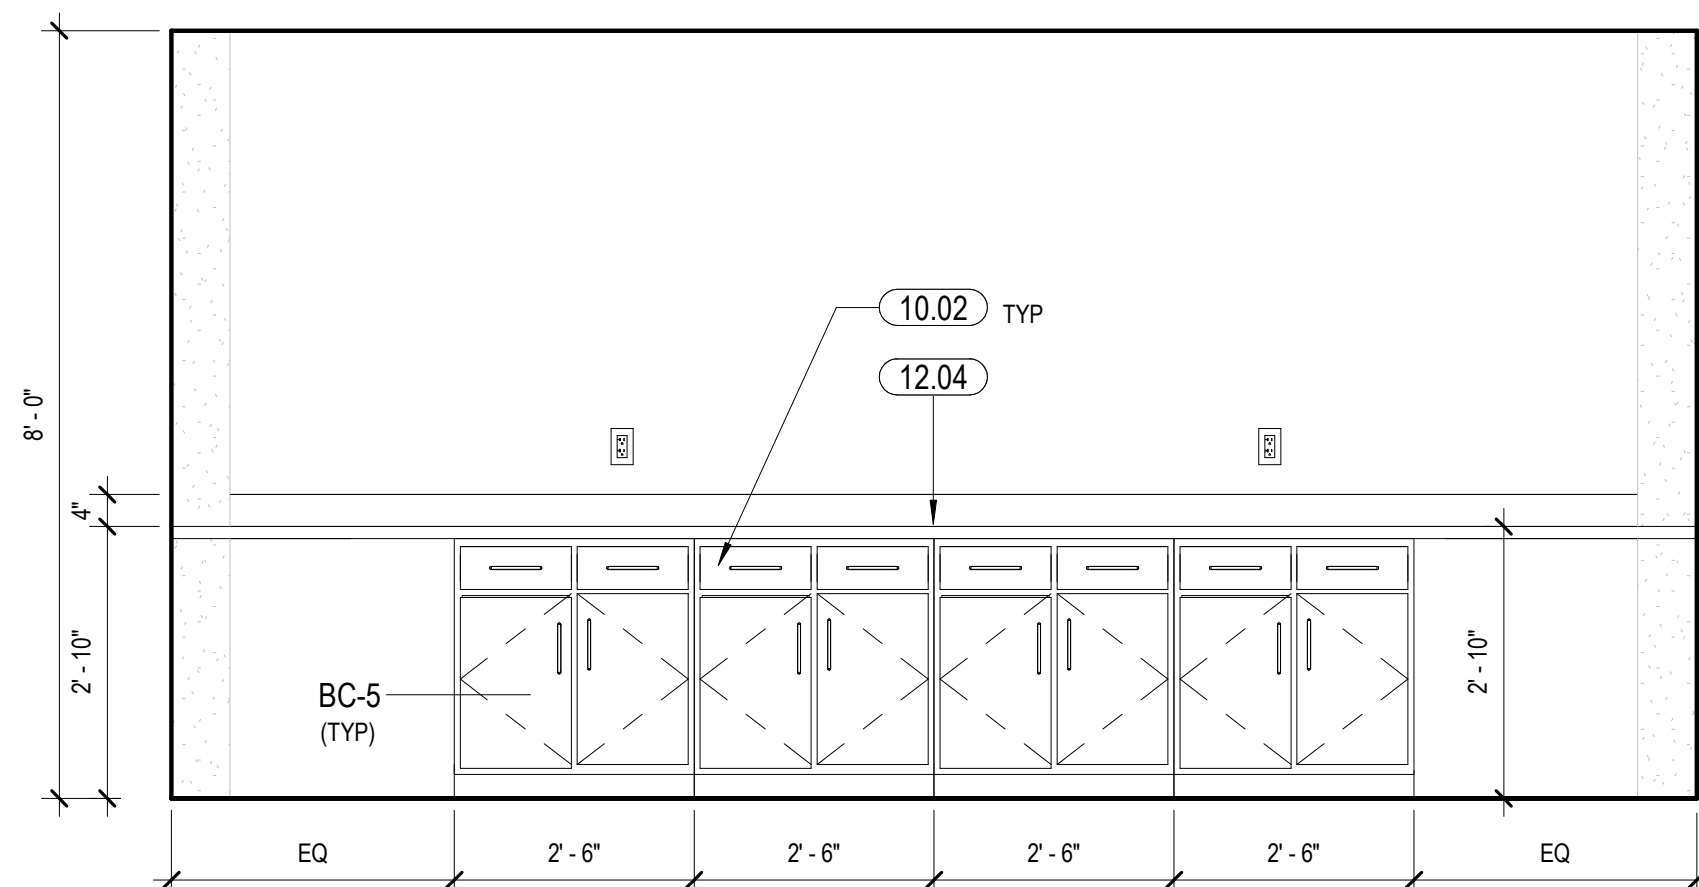


**(A1) DAYROOM - INT EL 1**  
1/2" = 1'-0"

1. SEE INTERIORS FOR TILE PATTERN
2. REF SHEET A-002 FOR ACCESSORIES INSTALLATION HEIGHTS

[illegible]

|       |                                                                      |
|-------|----------------------------------------------------------------------|
| 10.02 | NEW PLASTIC LAMINATE CASEWORK, BASE AND WALL CABINETS. SEE INTERIORS |
| 12.04 | SOLID SURFACE COUNTER, SEE INTERIORS                                 |

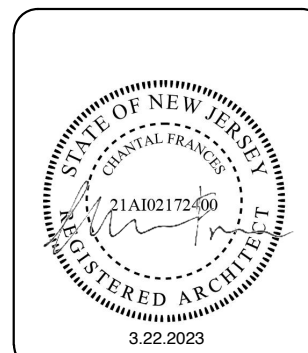

|                            |                                   |
|----------------------------|-----------------------------------|
| DESIGNED BY:<br>C. COPPOLA | ISSUE DATE:<br>22 MARCH 2024      |
| DRAWN BY:<br>C. COPPOLA    | SOLICITATION NO.:<br>PTFL 22-1019 |
| CHECKED BY:<br>C. FRANCES  | CONTRACT NO.:<br>FA8903-2-1-0004  |
| SUBMITTED BY:<br>BSC-IV    |                                   |
| SIZE:<br>ANSI D            |                                   |

|      |                                                     |
|------|-----------------------------------------------------|
| TA-1 | SURFACE MOUNTED SINGLE ROLL TOILET TISSUE DISPENSER |
| TA-2 | DOOR MOUNTED ROBE HOOK                              |
| TA-4 | SURFACE MOUNTED CHANNEL FRAME MIRROR                |
| TA-6 | SURFACE MOUNTED MEDICINE CABINET WITH MIRROR        |

|      |                                                     |
|------|-----------------------------------------------------|
| TA-1 | SURFACE MOUNTED SINGLE ROLL TOILET TISSUE DISPENSER |
| TA-2 | DOOR MOUNTED ROBE HOOK                              |
| TA-4 | SURFACE MOUNTED CHANNEL FRAME MIRROR                |
| TA-6 | SURFACE MOUNTED MEDICINE CABINET WITH MIRROR        |

US AIR FORCE CIVIL ENGINEER CENTER  
MCQUIRE AFB  
LAKEHURST, NEW JERSEY

---

BAKER - STANLEY - CARDONO JOINT VENTURE

**Michael Baker**  
INTERNATIONAL

**Cardono**  
Stanley Consultants

Full-Service Design & Consulting

MCGUIRE AFB, NEW JERSEY  
RENOVATION OF DORMITORY BUILDING 2619


SHEET ID  
A-411

100% FINAL DESIGN SUBMITTAL


Plot Date: 3/23/2024 12:10:13 PM

File Path: AutodesK Docs://196175.JBMDL Dorm Reno - B2619-B2621/PTFL221019-B2619-A.mt


| SYMBOL | NO. OF X-RAY | LOCATION OF X-RAY UNITS |
|--------|--------------|-------------------------|
| A      | 1            | ROOM 112B               |
| B      | 1            | ROOM 114B               |
| C      | 1            | ROOM 109B + ROOM 110B   |
| D      | 1            | ROOM 119B + ROOM 120B   |
| E      | 1            | ROOM 126B + ROOM 127B   |
| F      | 1            | ROOM 128B               |
| H      | 1            | ROOM 132B + ROOM 133B   |
| G      | 1            | ROOM 134B               |

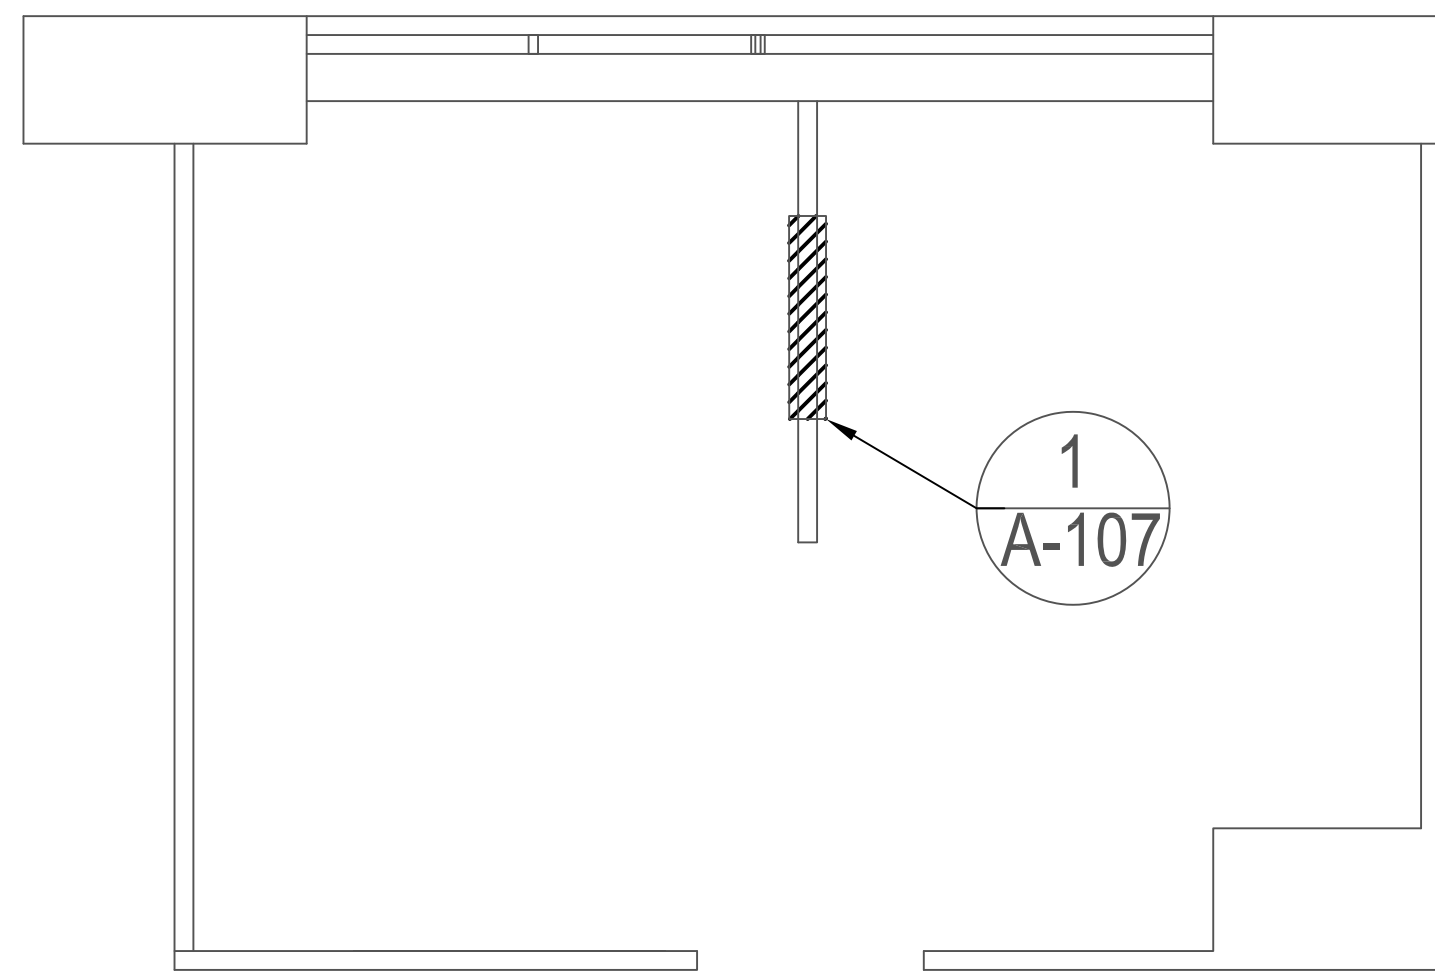


C 109-B, 110-B

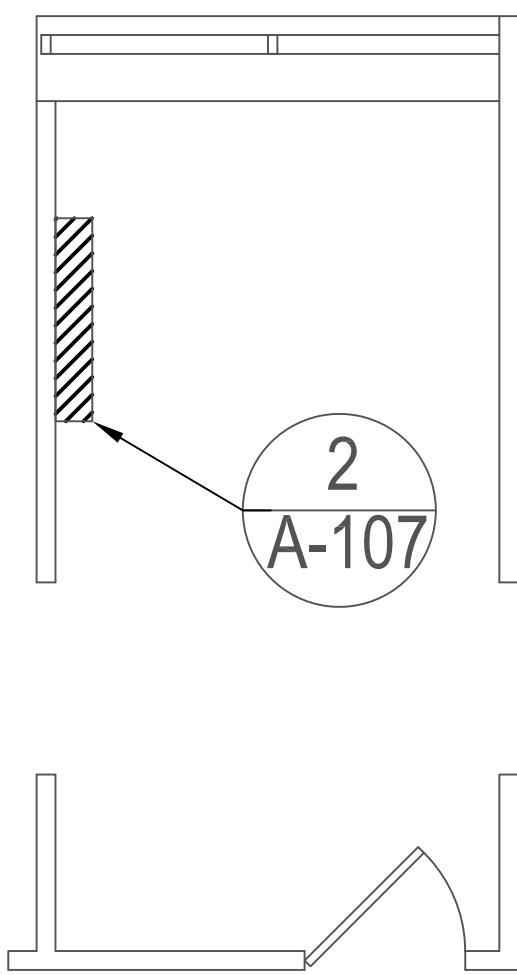


A 112-B

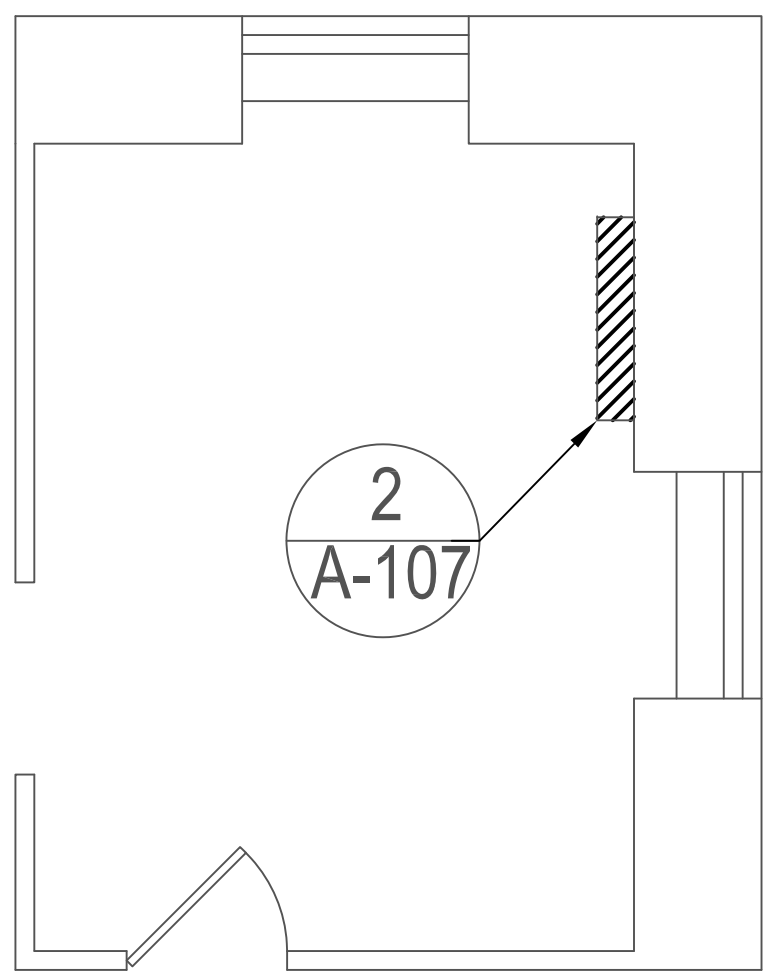


B 114-B

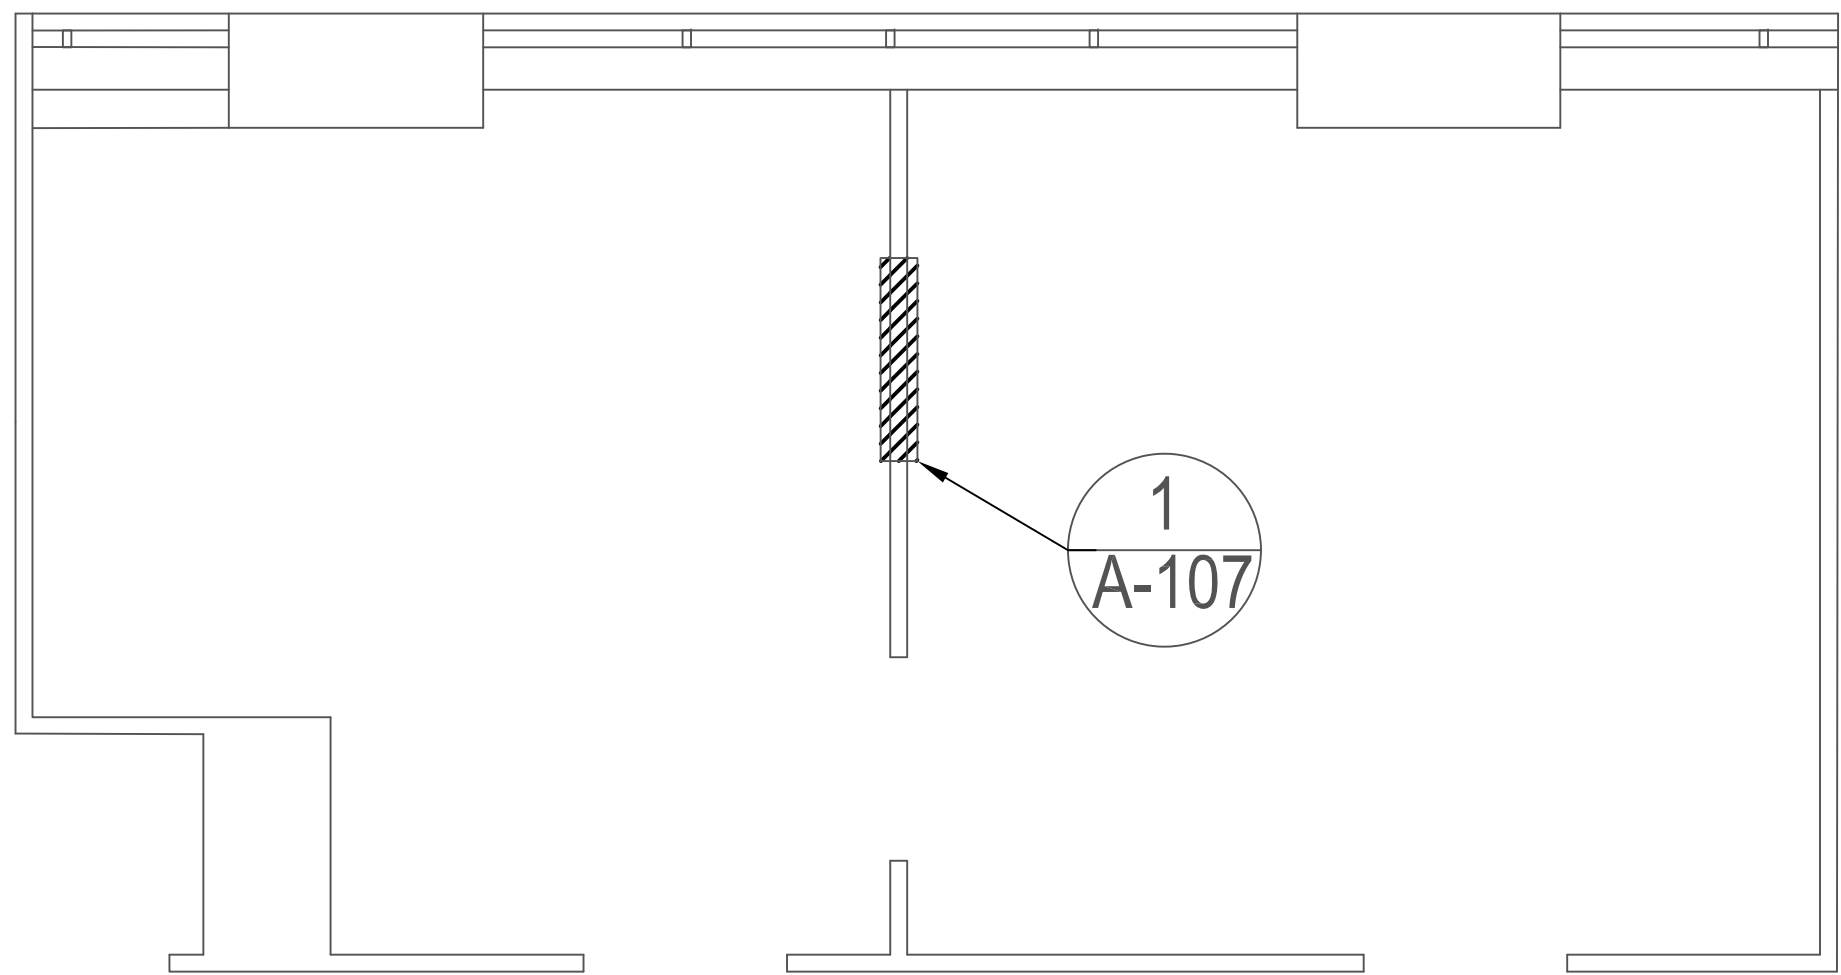


E 126-B, 127-B

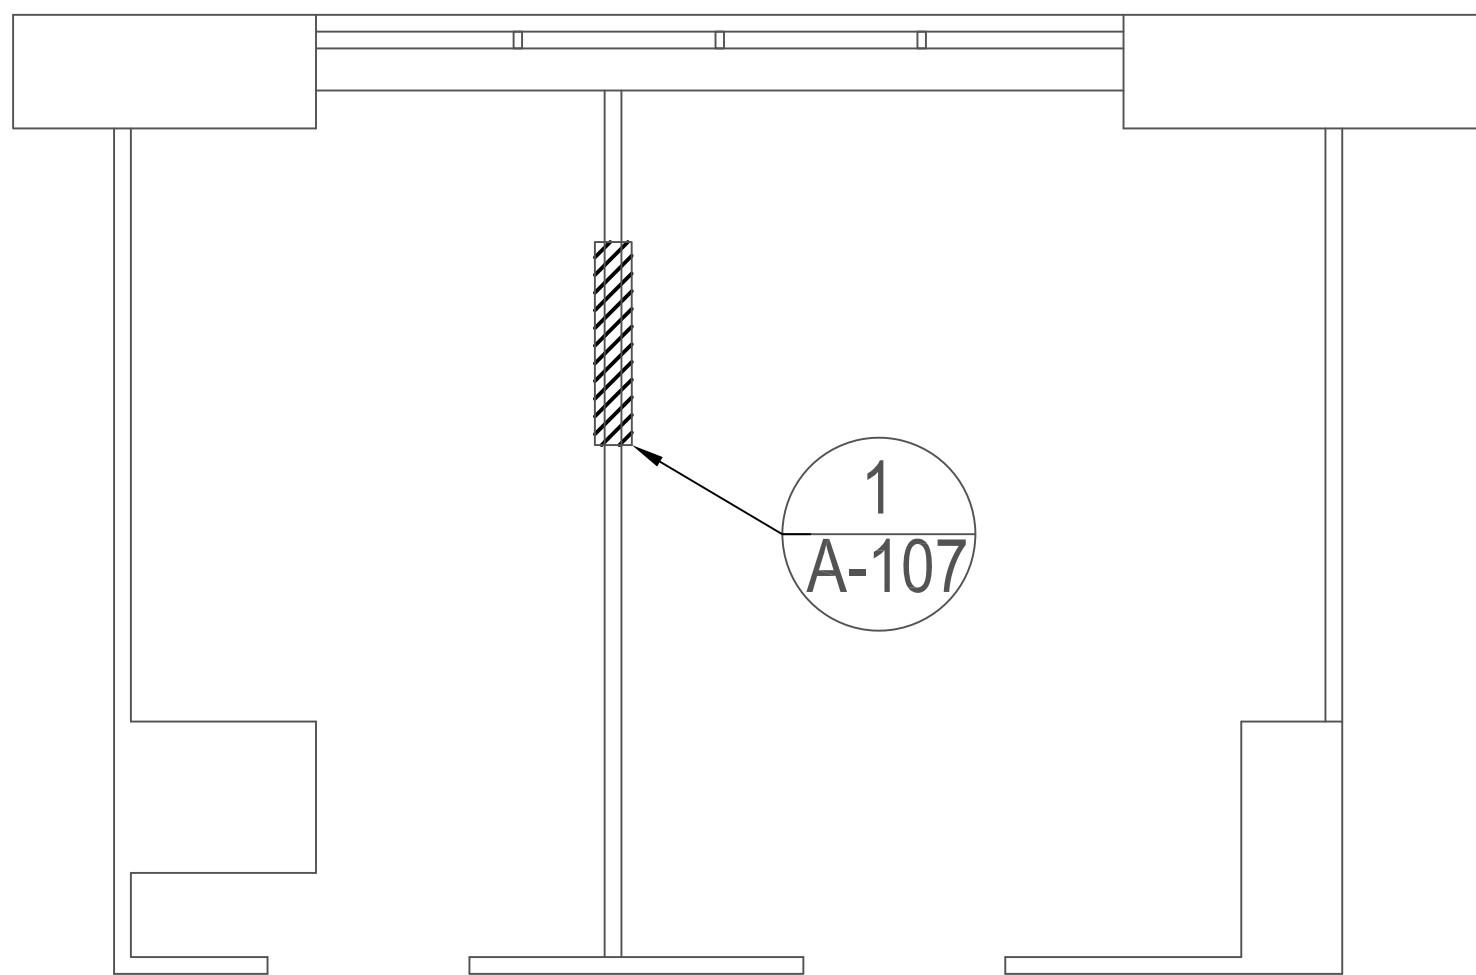


D 119-B, 120-B

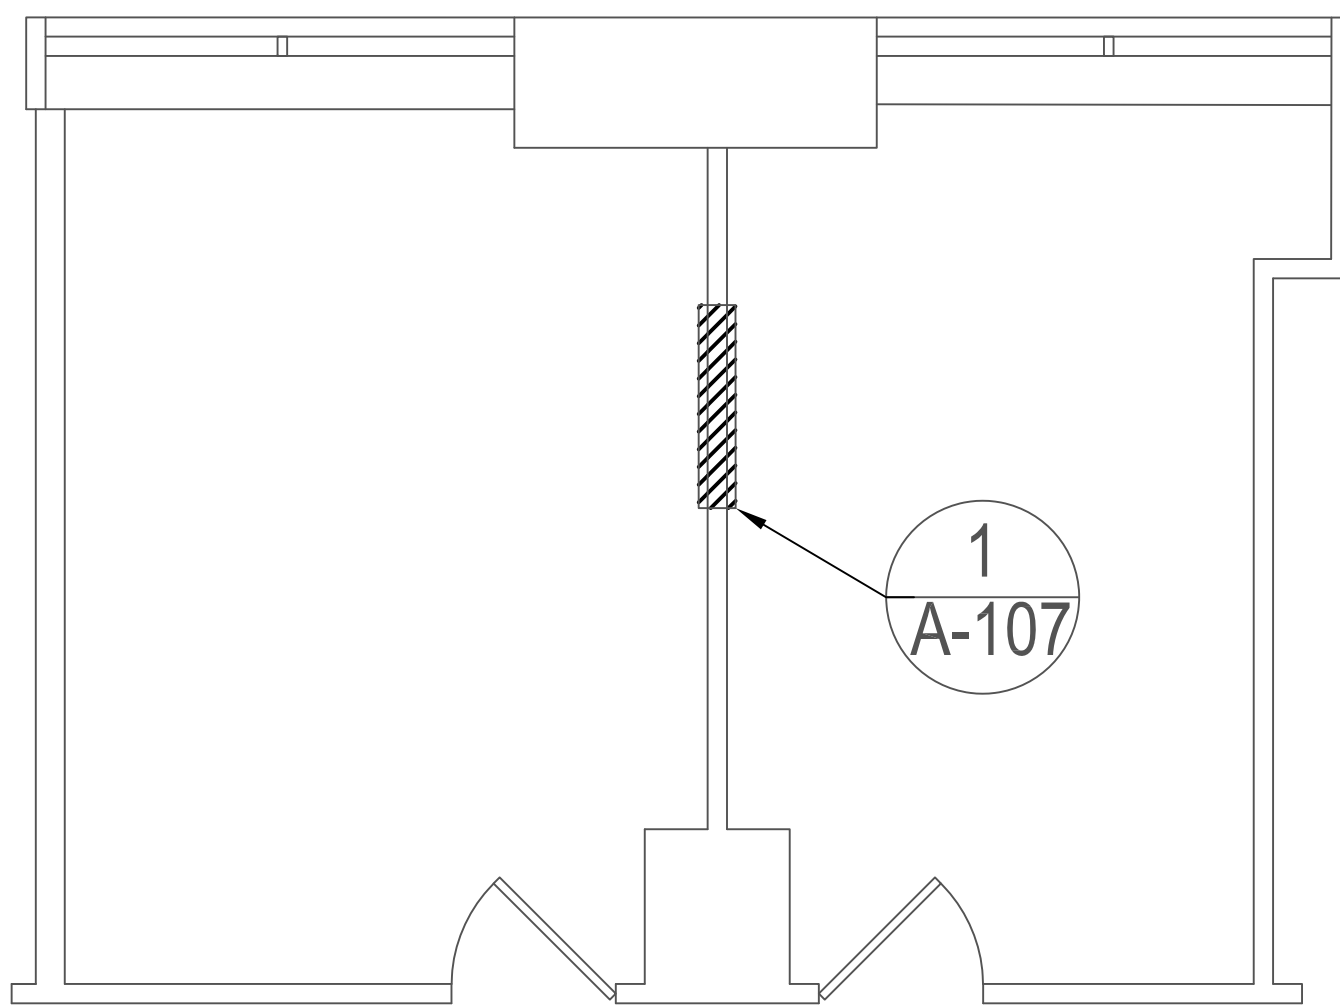


H 132-B, 133-B

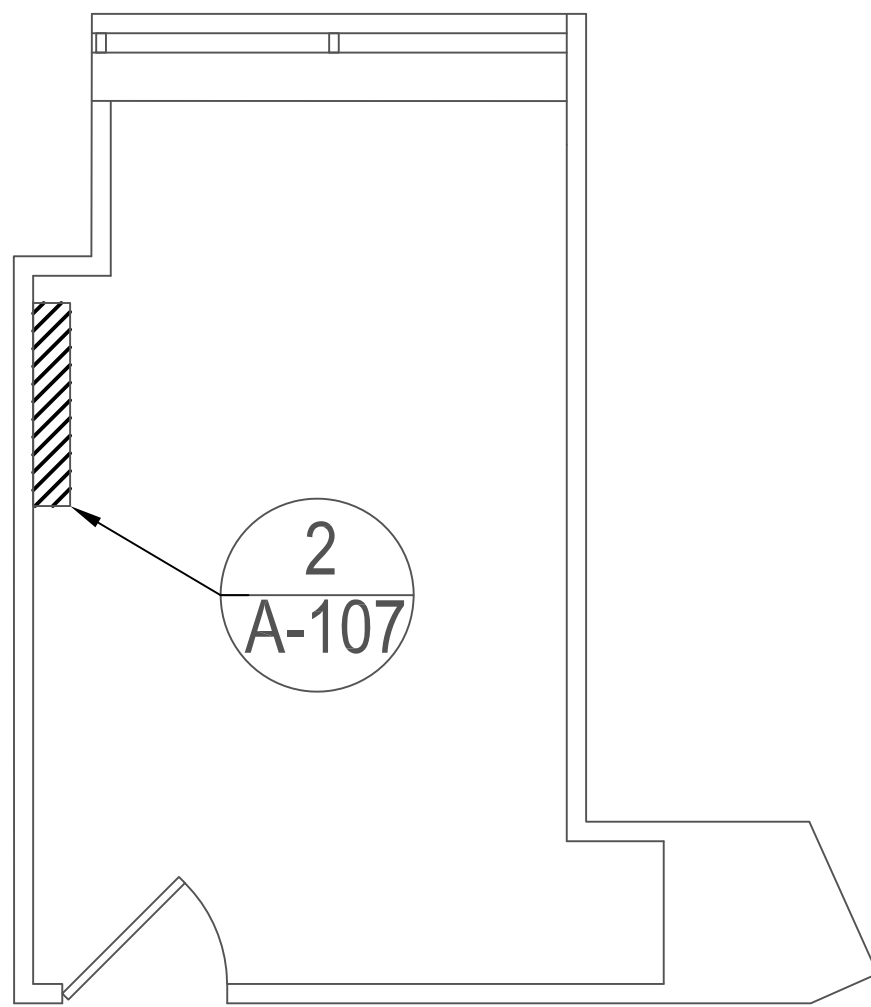

G 134-B

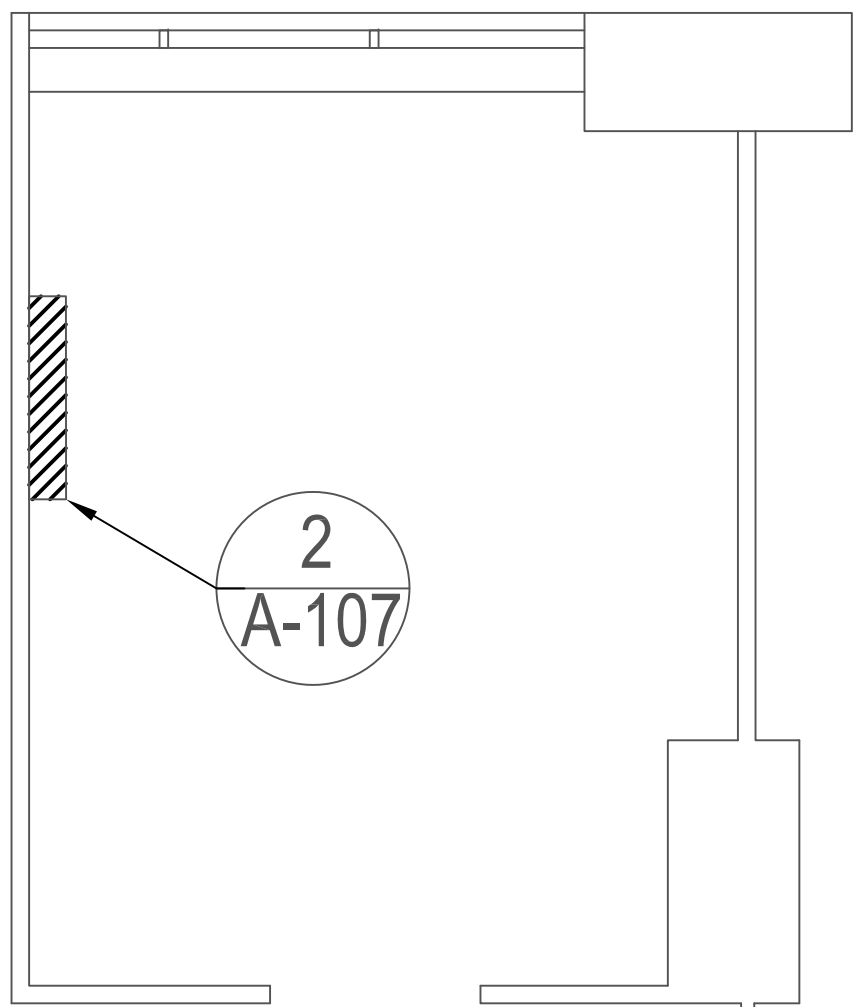

F 128-B

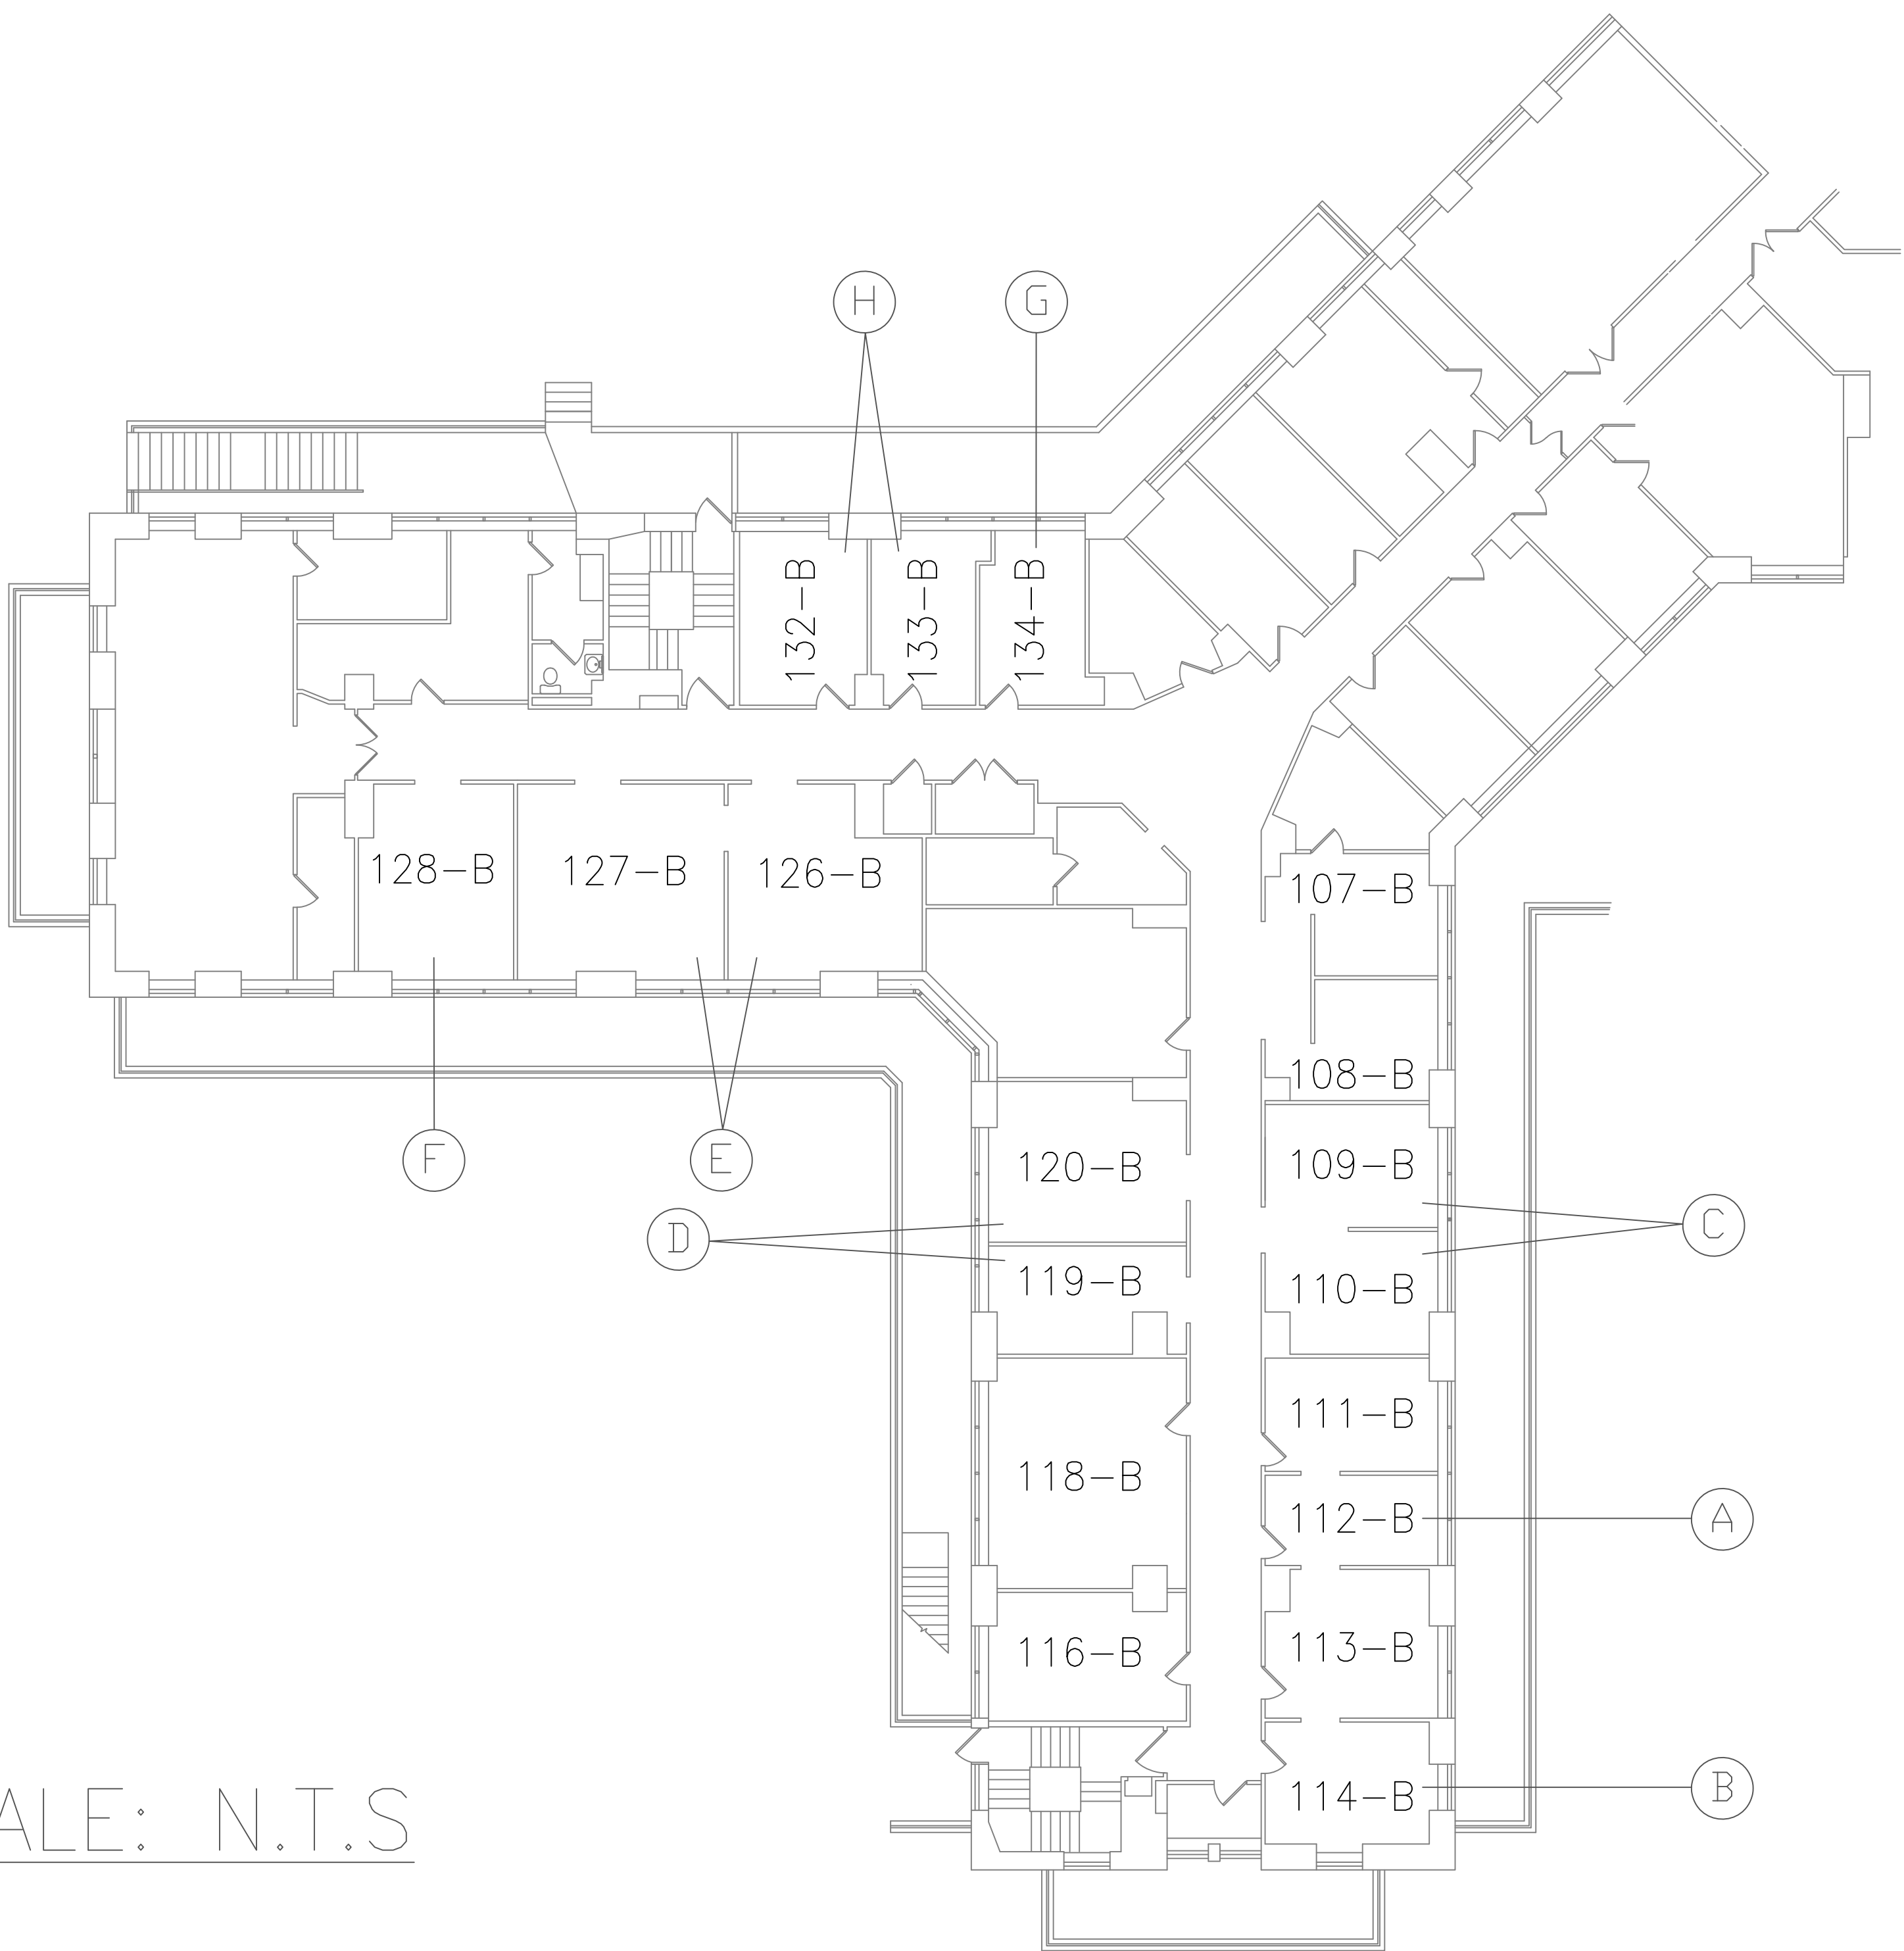

SCALE: N.T.S

"B" WING, 1ST FLOOR, BLDG1

|                       |                  |            |   |       |   |                                                      |                     |                                   |                |                              |
|-----------------------|------------------|------------|---|-------|---|------------------------------------------------------|---------------------|-----------------------------------|----------------|------------------------------|
| <div>Revisions:</div> | <div>Date:</div> | CONSULTANT | ARCHITECT/ENGINEER OF RECORD<br>WNYHCS ENGINEERING<br>BUFFALO VETERANS ADMINISTRATION MEDICAL CENTER<br>3495 BAILEY AVENUE<br>BUFFALO, NEW YORK 14215<br>716-834-9200 | STAMP | Office of<br>Construction<br>and Facilities<br>Management<br><br>VA U.S. Department<br>of Veterans Affairs | Drawing Title<br>LOCATION OF EXISTING X-RAY<br>UNITS | Phase<br>PHASE FOUR | Project Title<br>DENTAL EXAM ROOM |                | Project Number<br>528-22-127 |
|                       |                  |            |   |       |   | Approved: Project Director                           |                     | Location<br>BUFFALO VAMC          |                | Building Number<br>1         |
|                       |                  |            |   |       |   |                                                      |                     | Issue Date<br>03/24/2023          | Checked<br>RJC | Drawn<br>MTA                 |
|                       |                  |            |   |       |   |                                                      |                     | Drawing Number<br>A-106           |                |                              |
|                       |                  |            |   |       |   |                                                      |                     |                                   |                |                              |