

three inches = one foot

one and one half inches = one foot

one inch = one foot

three quarters inch = one foot

one half inch = one foot

one quarter inch = one foot

one eighth inch = one foot


one quarter inch = one foot

one eighth inch = one foot


one eighth inch = one foot

FINISH SCHEDULE				FINISH SPECIFICATIONS			
NO.	ROOM	FLOORS		WALLS		FLOORS	
		WVS/VCT	P	VB	WP	WVS/VCT	P
100	WAITING	1	1	1	1	1	1
101	DRESS	1	1	1	1	1	1
102	ADA DRESS	1	1	1	1	1	1
103	CLEAN	1	1	1	1	1	1
104	SOILED	1	1	1	1	1	1
105	CONTROL ROOM	1	1	1	1	1	1
106	SUB-WAITING	1	1	1	1	1	1
107	MRI SCAN ROOM	1	1	1	1	1	1
108	EQUIP. ROOM	1	1	1	1	1	1
109	CL	1	1	1	1	1	1
110	CL	1	1	1	1	1	1

WELDED SHEET VINYL		PLASTIC LAMINATE	
WVS-1	MANF: JONESTONE COLOR: WALNUT STREET W/ INTERGLAZE BASE	PL-1	MANF: WILSONART COLOR: ASIAN SAND - 7552K-18
VCT-1	MANF: ARISTOCOLOR COLOR: LUNAR BLUE 51932	PL-2	MANF: WILSONART COLOR: PASADENA OAK - 785K-38
VINYL COMPOSITION TILE		CEILING GRID	
VC-1	MANF: ARISTOCOLOR COLOR: LUNAR BLUE 51932	CG-1	2X2 - MATCH CT ROOM
VINYL WALL BASE		WOOD DOORS	
VB-1	MANF: JONESTONE PRODUCT: F-COVE BASE COLOR: WINDSOR BLUE 51	WD-1	CLEAR RED OAK
PAINT		WALL PROTECTION	
P-1	MANF: SHERWIN WILLIAMS PRODUCT: EGG SHELL COLOR: SAND DUNE 59966	WP-1	MANF: IMPRO PRODUCT: 4" CORNER GUARDS COLOR: PONT BLUE 018 LOCATION: OUTSIDE CORNERS
P-2	MANF: SHERWIN WILLIAMS PRODUCT: SEMI-GLOSS COLOR: SHIRAZ 59935	WP-2	MANF: IMPRO PRODUCT: 4" SHEET PANEL COLOR: PONT BLUE 018
SOLID SURFACE			
SS-1	MANF: CORIAN COLOR: PLATINUM		

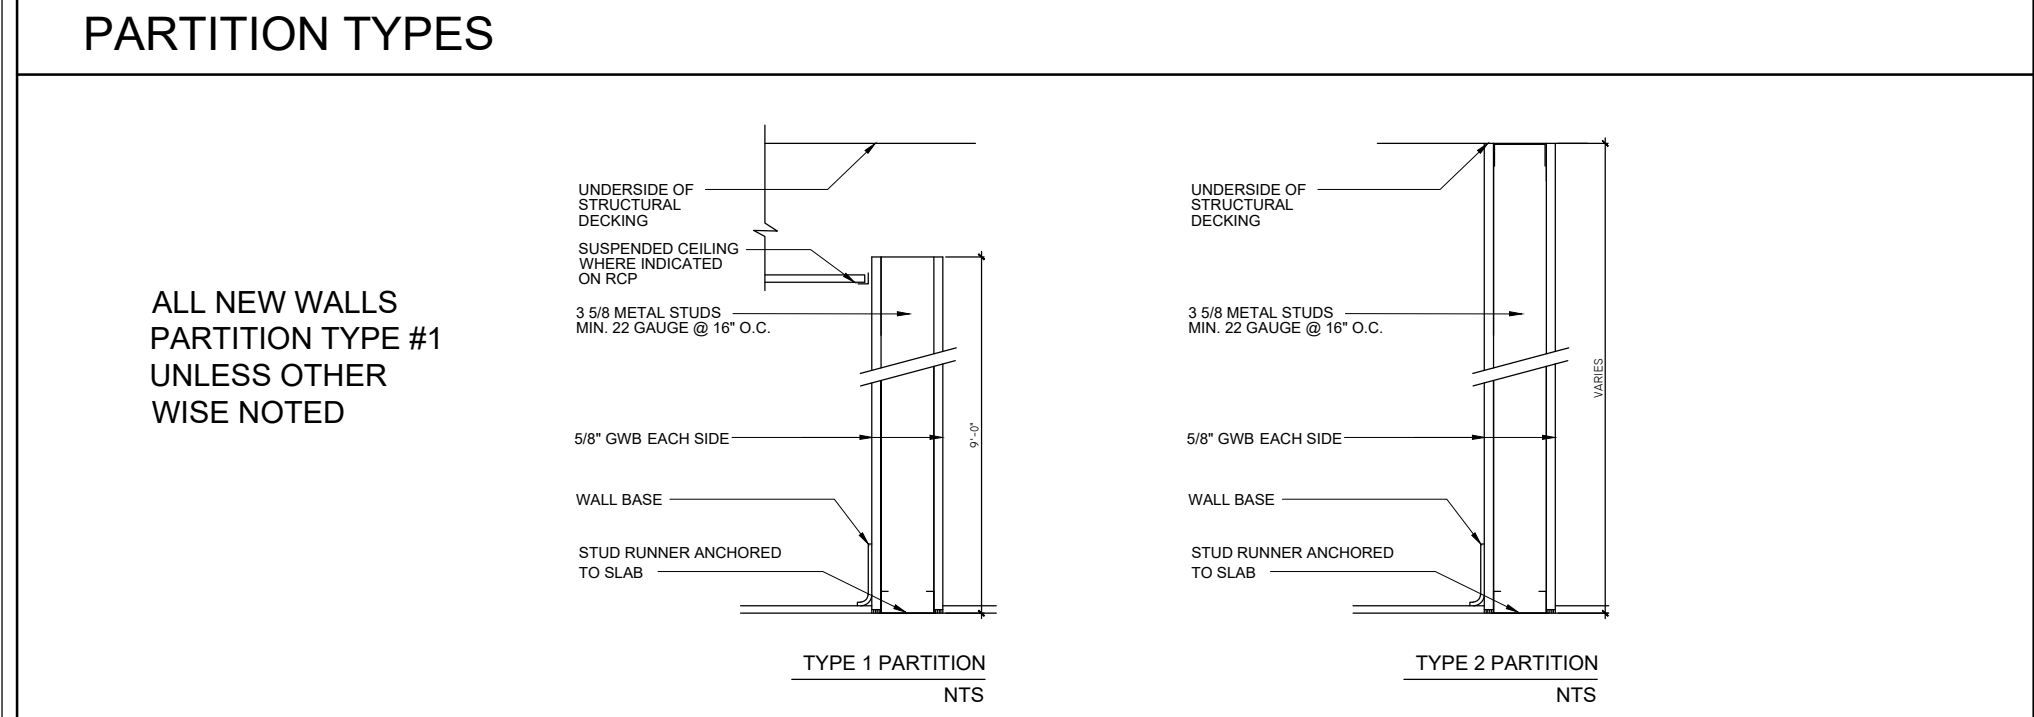

NO.	LOCATION	TYPE	DESCRIPTION	SIZE	FINISH	HARDWARE	COMMENTS
1	WAITING - 100	4	HINGED DOUBLE	6'-0" x 7'-0" x 1 3/4"	STAINED	1	
2	DRESS - 101	1	HINGED SINGLE	3'-0" x 7'-0" x 1 3/4"	STAINED	3	
3	DRESS - 102	1	HINGED SINGLE	3'-0" x 7'-0" x 1 3/4"	STAINED	3	
4	CLEAN - 103	3	HINGED DOUBLE	3'-0" x 7'-0" x 1 3/4"	STAINED	4	
5	SOILED - 104	3	HINGED DOUBLE	3'-0" x 7'-0" x 1 3/4"	STAINED	4	
6	WAITING - 100	1	HINGED DOUBLE	3'-0" x 7'-0" x 1 3/4"	STAINED	1	
7	CL - 109	3	HINGED DOUBLE	3'-0" x 7'-0" x 1 3/4"	STAINED	5	
8	CONTROL ROOM - 105	1	HINGED SINGLE	3'-0" x 7'-0" x 1 3/4"	STAINED	6	
9	CONTROL ROOM - 105	1	HINGED SINGLE	3'-0" x 7'-0" x 1 3/4"	STAINED	2	
10	MRI SCAN ROOM - 107	2	HINGED SINGLE	4'-0" x 7'-0" x 1 3/4"	PL-2	2	
11	EQUIP. ROOM - 108	1	HINGED SINGLE	3'-0" x 7'-0" x 1 3/4"	STAINED	1	
12	CL - 110	3	HINGED DOUBLE	3'-0" x 7'-0" x 1 3/4"	STAINED	5	

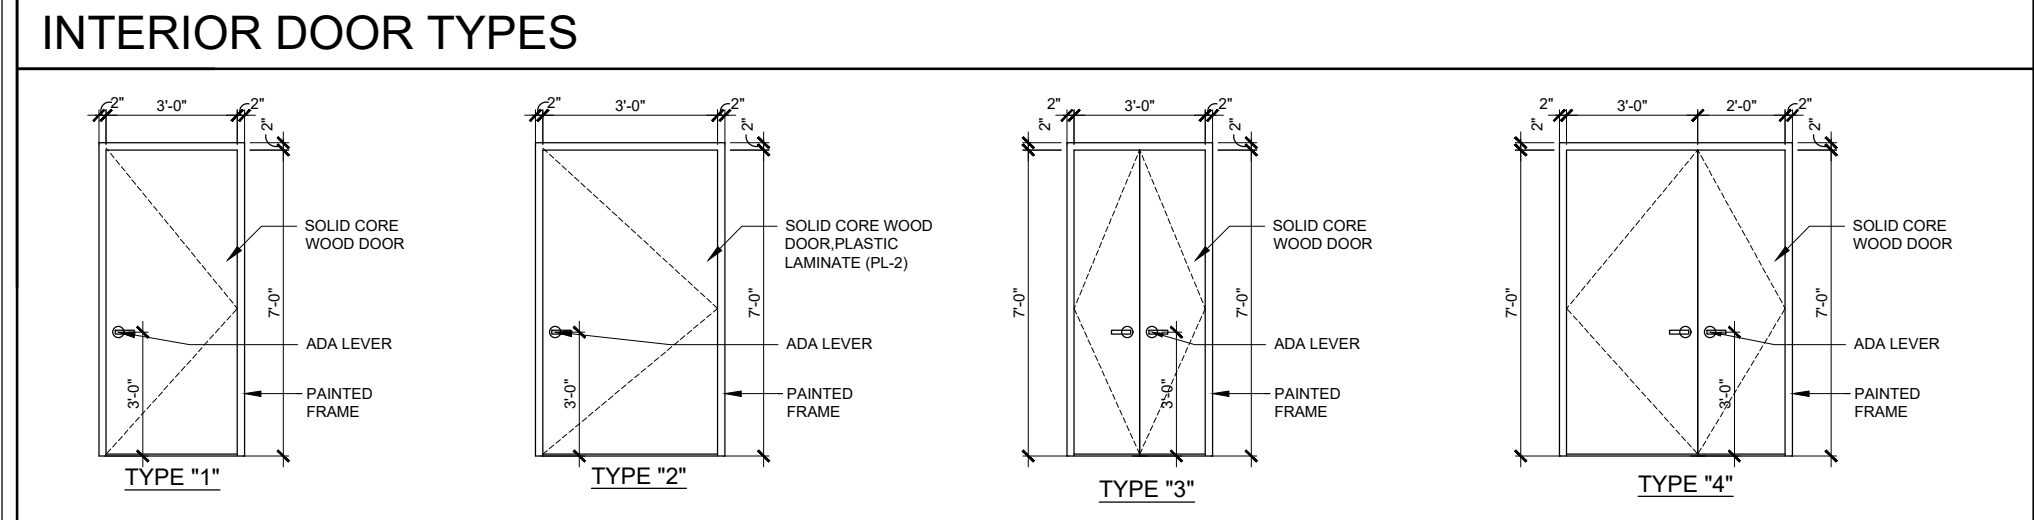


HARDWARE SPECIFICATIONS		HARDWARE SCHEDULE	
BUTT HINGES (A) INTERIOR DOORS USED (B) EXTERIOR DOORS WHICH ARE DEFINED AS DOORS EXPOSED TO THE ELEMENTS SHALL BE US32D.		HW SET #1 3 PAIR 1 1 2 1	
LOCKSETS AND LATCHSETS YALE CAMEL - CHL LEVER HARDWARE - COORDINATE FINISH WITH BUILDING MANAGEMENT		BUTT HINGES LATCHSET DUMMY LEVER SET CLOSERS FLUSH BOLT	
STOPS STOPS #436 AND #407 AS MANUFACTURED BY IVES OR APPROVED EQUAL. PROVIDE ONE FOR EACH INTERIOR DOOR.		HW SET #2 - 1	
MISCELLANEOUS ITEMS (1) SILENCERS OLIVIA-JOHNSON Q384 THREE PAIRS PER EACH SINGLE DOOR, TWO EACH PER PAIR OF DOORS SHALL BE FURNISHED.		HW SET #3 1 1/2 PAIR 1 1	
NOTES: 1. ALL DOORS MUST OPEN TO A FULL 90 DEGREES UNLESS OTHERWISE NOTED. 2. ALL HARDWARE TO BE ADA COMPLIANT. 3. OWNER TO SELECTION FINISHES.		HW SET #4 1 1/2 PAIR 1 1	
		HW SET #5 3 1/2 PAIR 2 2	

PLAN/CEILING SYMBOLS			
D - DEMOLISH	E - EXISTING	R - RELOCATED	N - NEW
	WALL TO BE REMOVED		DOOR NUMBER
	EXIST WALL, TO REMAIN		PARTITION TYPE
	NEW WALL		2' X 2' LAY-IN FIXTURE
	SHIELDING WALL		


DESIGN/BUILDER:		ARCHITECT/ENGINEERS:	
Deerfield Construction Group 610 Professional Drive, Suite 210 Gaithersburg, Maryland 20879 (301)947-4701		Nicholas Lucarelli Architects, LLC 6723 Whittier Avenue Suite 414 Mclean, VA 22101 Tel: (703) 790-9606	
D2 Engineering, LLC 18310 Montgomery Village Ave Suite 520 Gaithersburg, MD 20879 Tel: (301) 208-9575 Fax: (301) 208-9405		PROPERTY OF THE UNITED STATES GOVERNMENT FOR OFFICIAL USE ONLY DO NOT REMOVE THIS NOTICE. PROPERLY DESTROY DOCUMENTS WHEN NO LONGER NEEDED.	
For review and approval Revisions:		Date	

DESIGN/BUILDER:		ARCHITECT/ENGINEERS:	
Deerfield Construction Group 610 Professional Drive, Suite 210 Gaithersburg, Maryland 20879 (301)947-4701		Nicholas Lucarelli Architects, LLC 6723 Whittier Avenue Suite 414 Mclean, VA 22101 Tel: (703) 790-9606	
D2 Engineering, LLC 18310 Montgomery Village Ave Suite 520 Gaithersburg, MD 20879 Tel: (301) 208-9575 Fax: (301) 208-9405		PROPERTY OF THE UNITED STATES GOVERNMENT FOR OFFICIAL USE ONLY DO NOT REMOVE THIS NOTICE. PROPERLY DESTROY DOCUMENTS WHEN NO LONGER NEEDED.	
For review and approval Revisions:		Date	


Stamp/Seal 	Drawing Title FLOOR PLAN, REFLECTED CEILING PLAN & SCHEDULES Approved: Project Director	Project Title VA BALTIMORE MEDICAL CENTER ROOM 1B-165 Location 10 NORTH GREENE STREET, BALTIMORE, MD 21201 Date 6.2.2021	Project Number PROJECT # Building Number - Drawing Number AE101
----------------	---	---	--

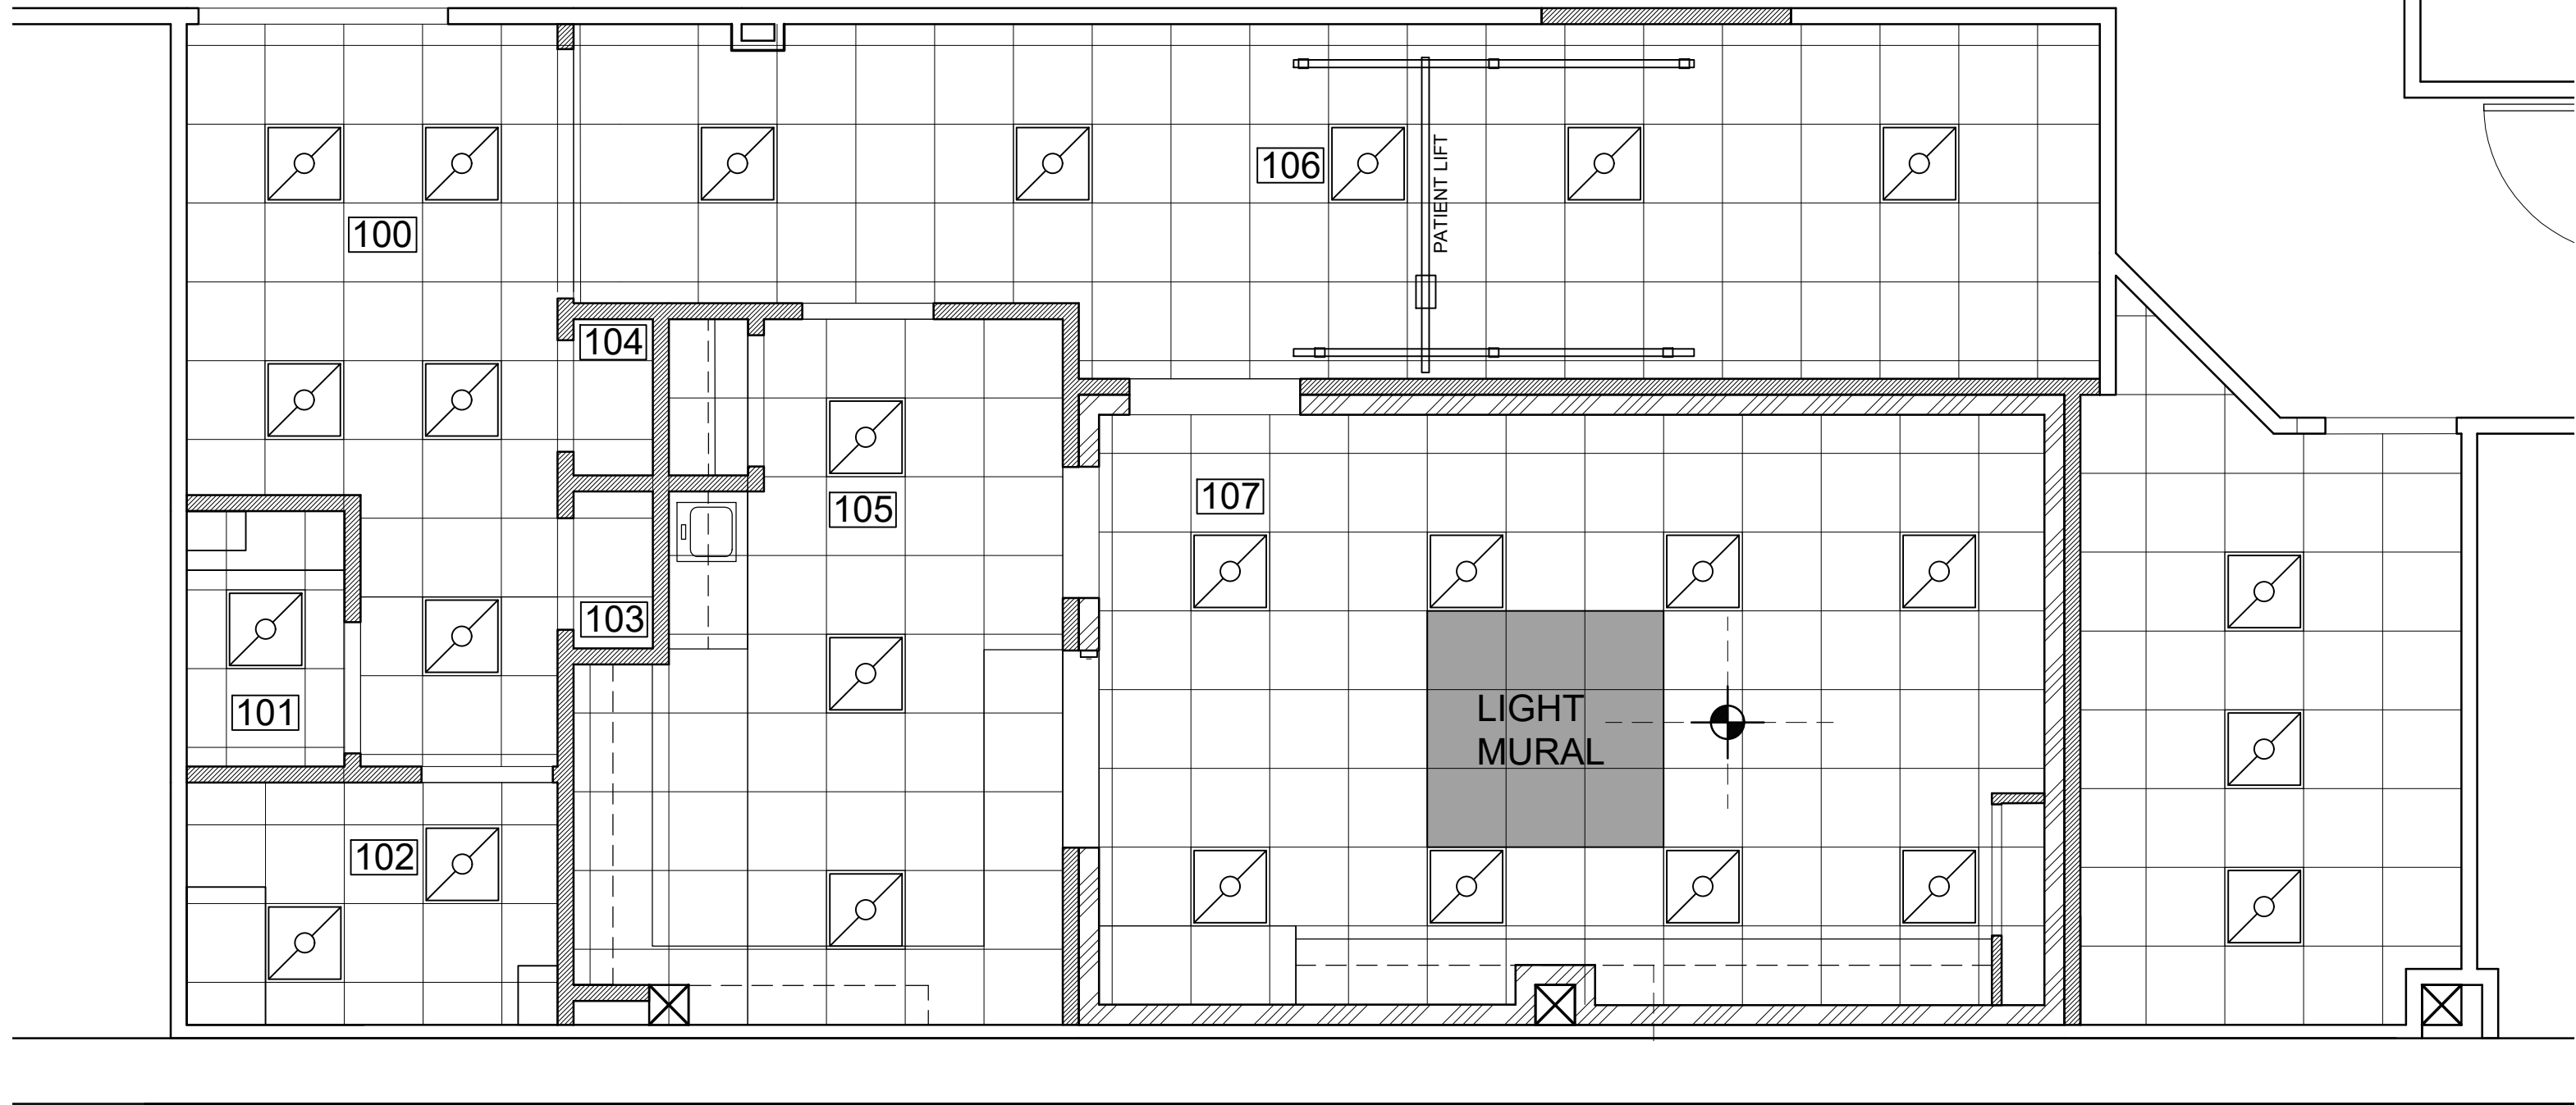


1 REFLECTED CEILING PLAN
SCALE: 1/4" = 1'-0"

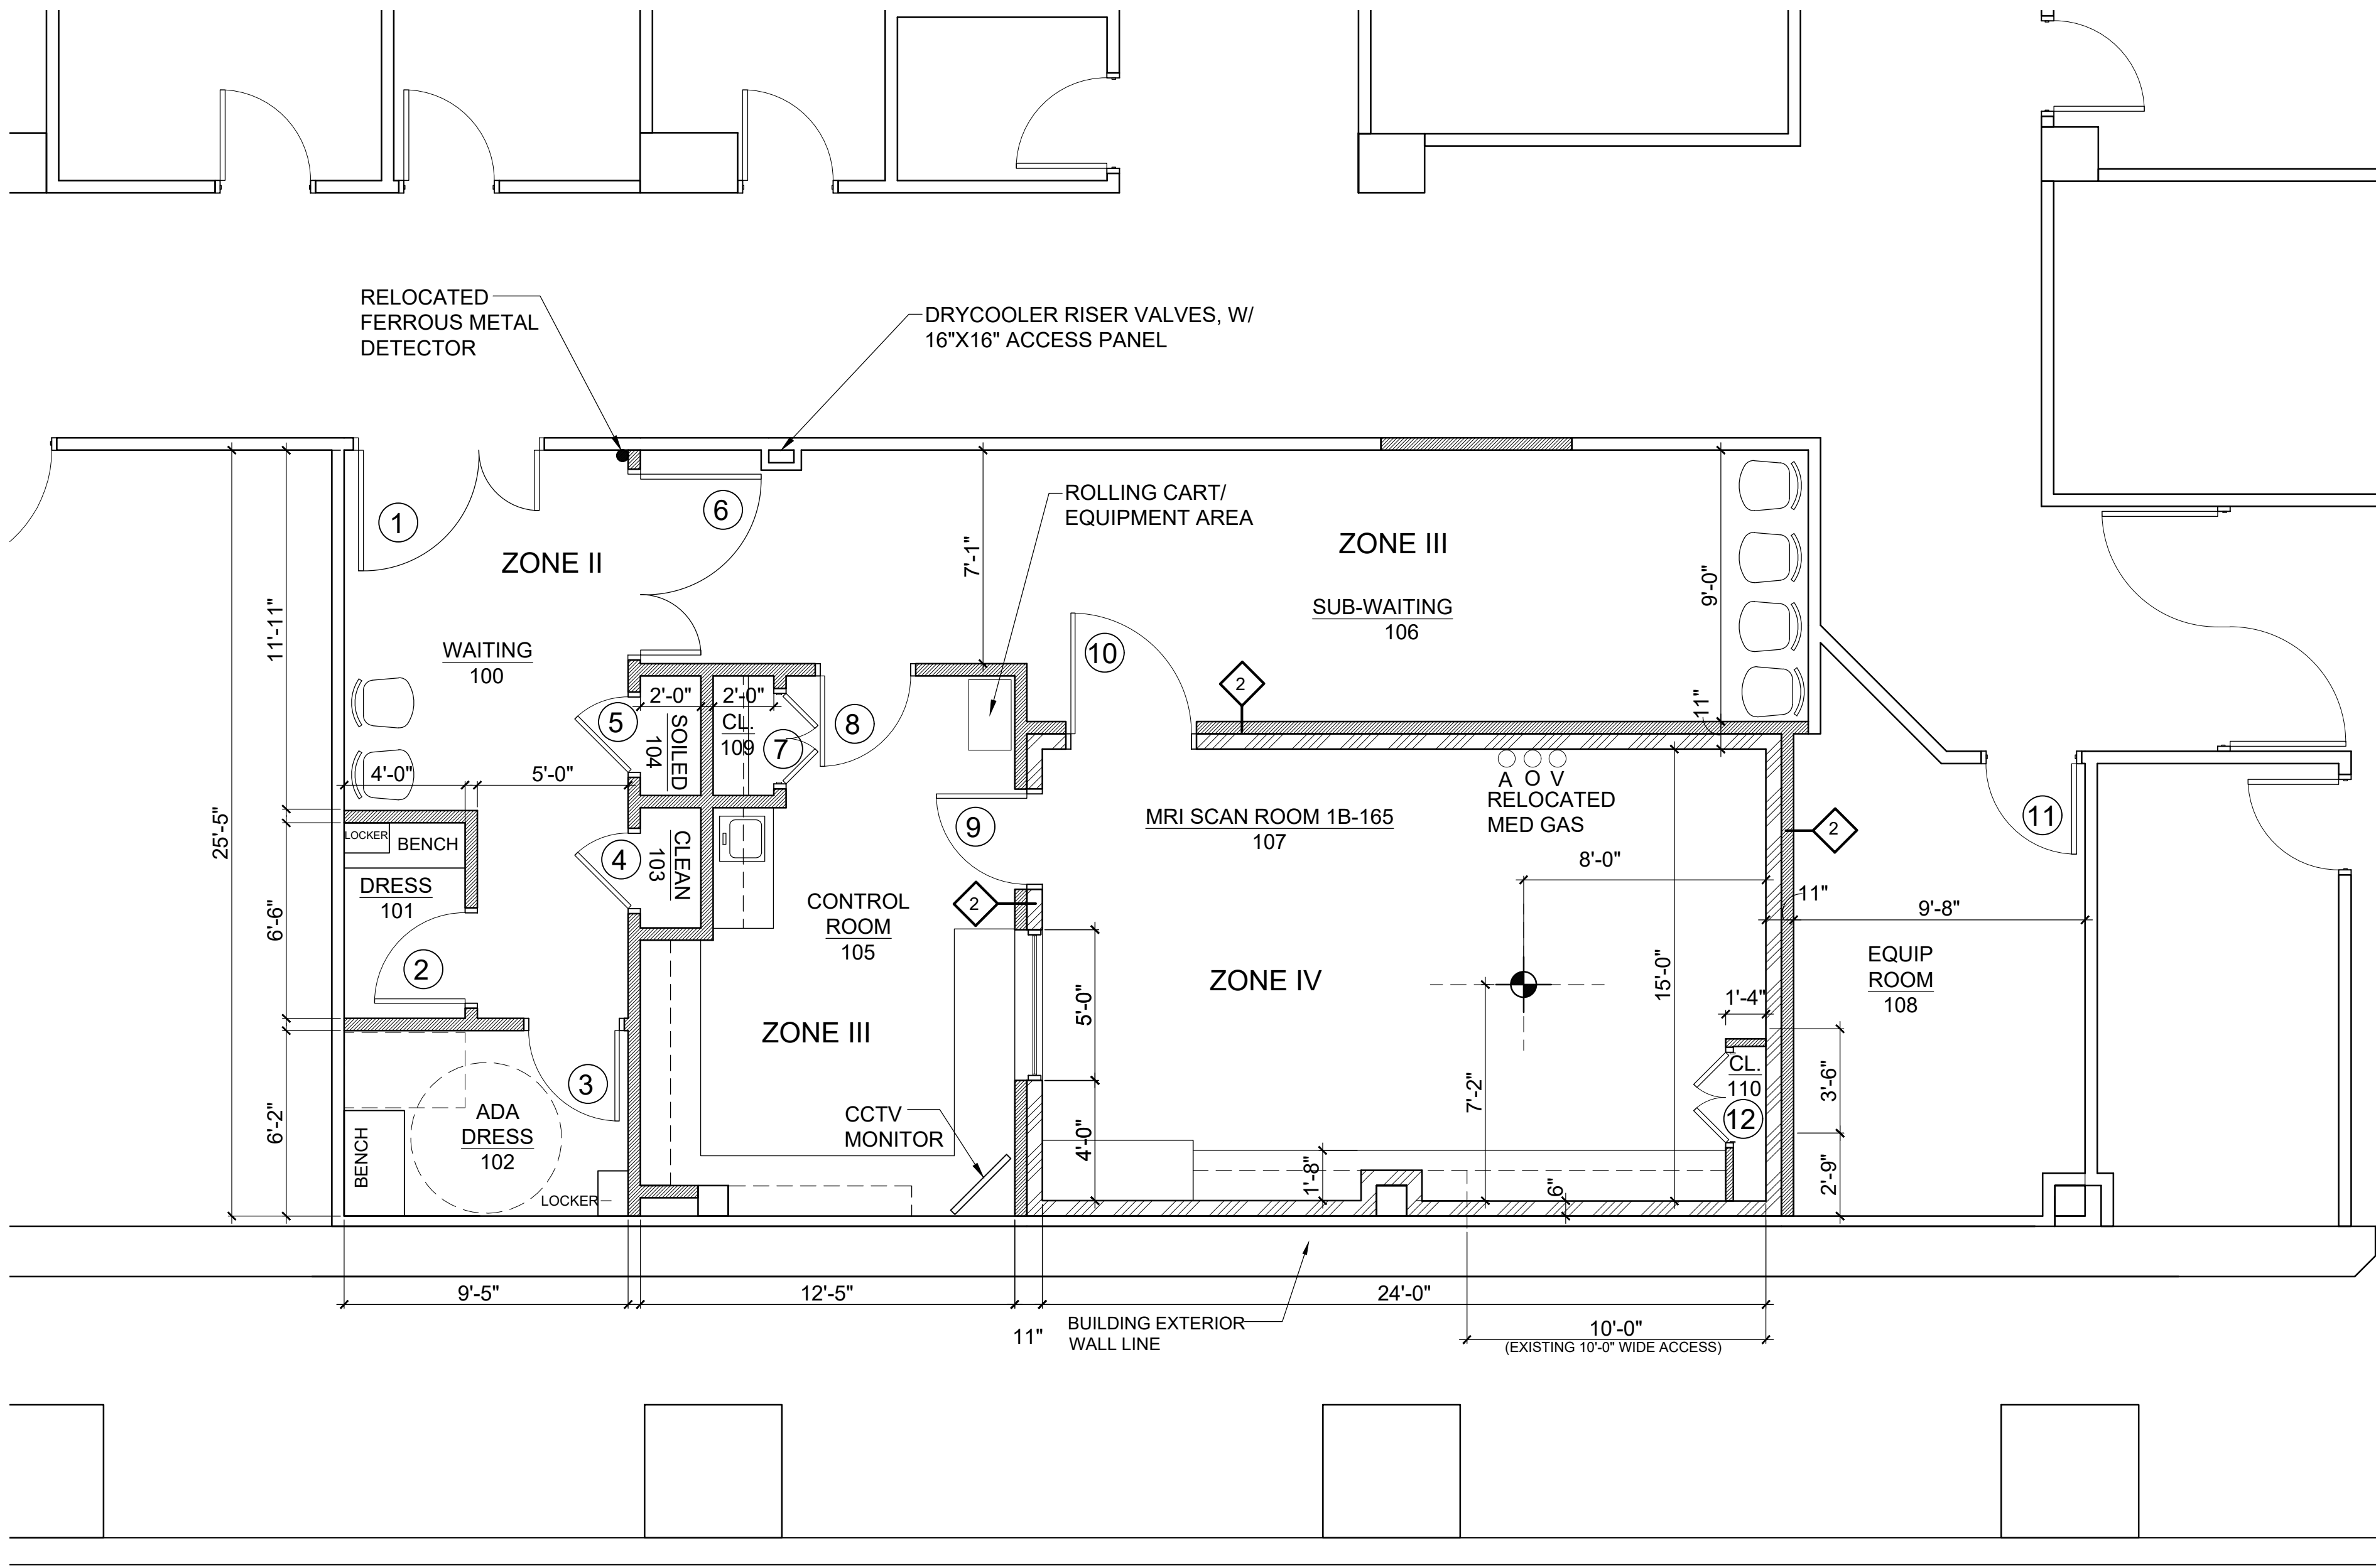


1 FLOOR PLAN
SCALE: 1/4" = 1'-0"

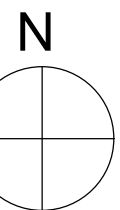


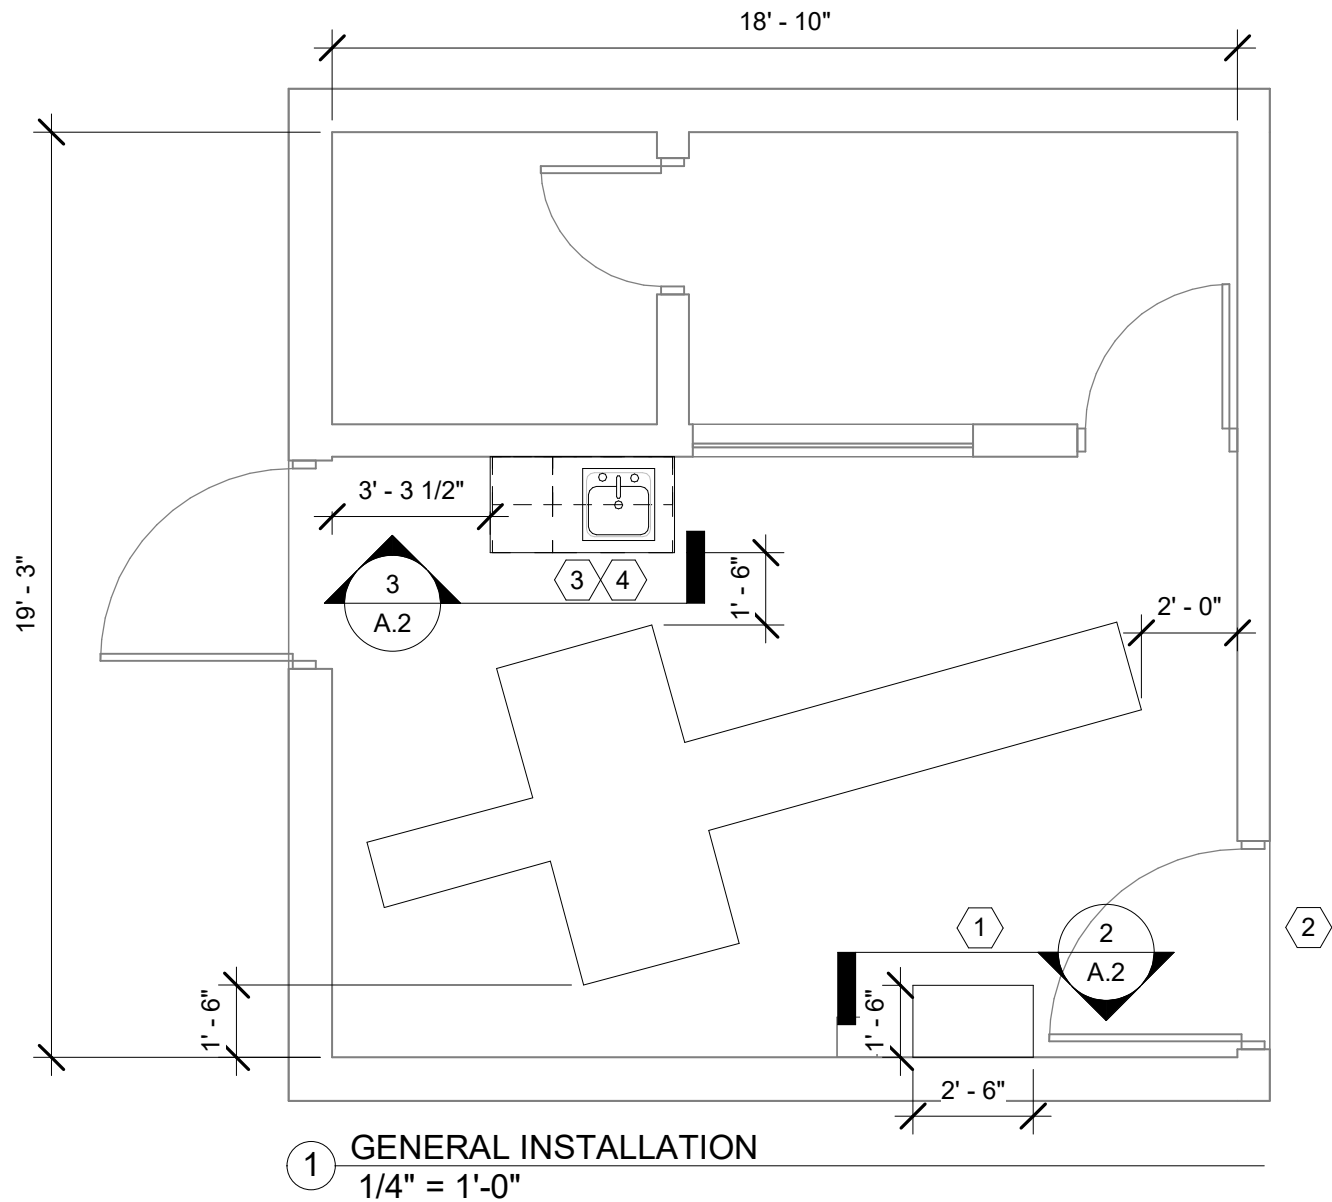

MASTER KEYNOTE	
Note Number	Note Content
1	Base Bid Cabinetry. MOD#1 Updates the Installation Location Only. See Base Bid for Further Details
2	Install New 4' Steel Door. See SOW
3	Base Bid Cabinetry. MOD#1 Updates the Installation Location Only. See Base Bid for Further Details
4	Install New 1/2" Copper Hot & Cold Water Lines. Tie Into Existing Water Lines Above Previous Sink. Install New 2" PVC Sewer & P-Trap. Tie Into Existing Sewer Line Below Previous Sink

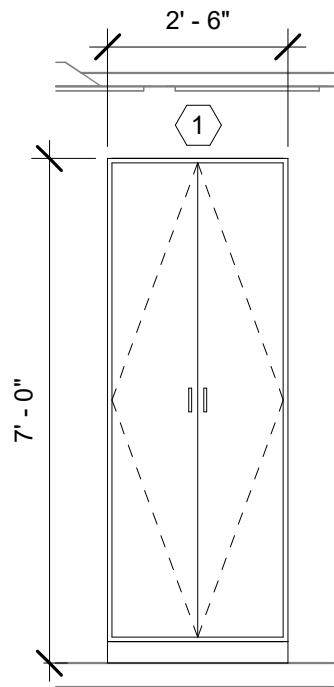

2 Section 4
3/8" = 1'-0"

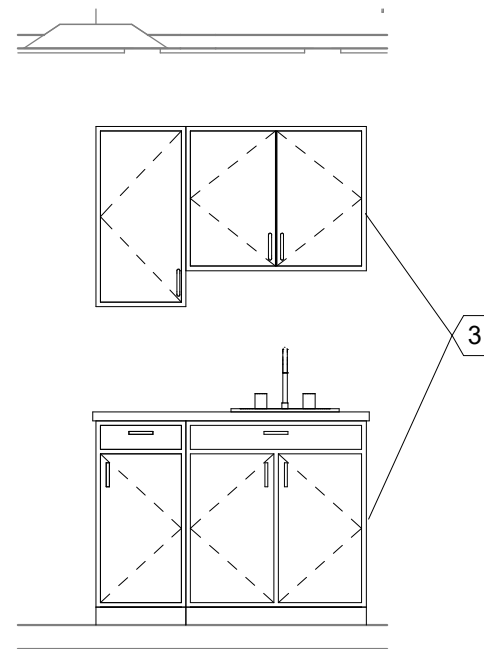

3 Section 5
3/8" = 1'-0"



GREAT PLAINS AREA INDIAN HEALTH SERVICE
OFFICE OF ENVIRONMENTAL
HEALTH & ENGINEERING

DIVISION OF FACILITIES MANAGEMENT
115 4TH AVENUE SE, RM 309
ABERDEEN, SD 57401
(605) 226-7451 FAX (605) 226-7580

www.ihs.gov


Quentin N. Burdick
Memorial Health Facility

Replace RTU &
Cabinetry - CT Area

CONTRACT NO:	
TASK ORDER NO:	
PROJECT NUMBER:	GP22TM300H10
DATE:	08/26/2025
DRAWN BY:	Taylor Strand
CHECKED BY:	Brad Weekley
LAST REVISION DATE:	

GENERAL INSTALL

A.2

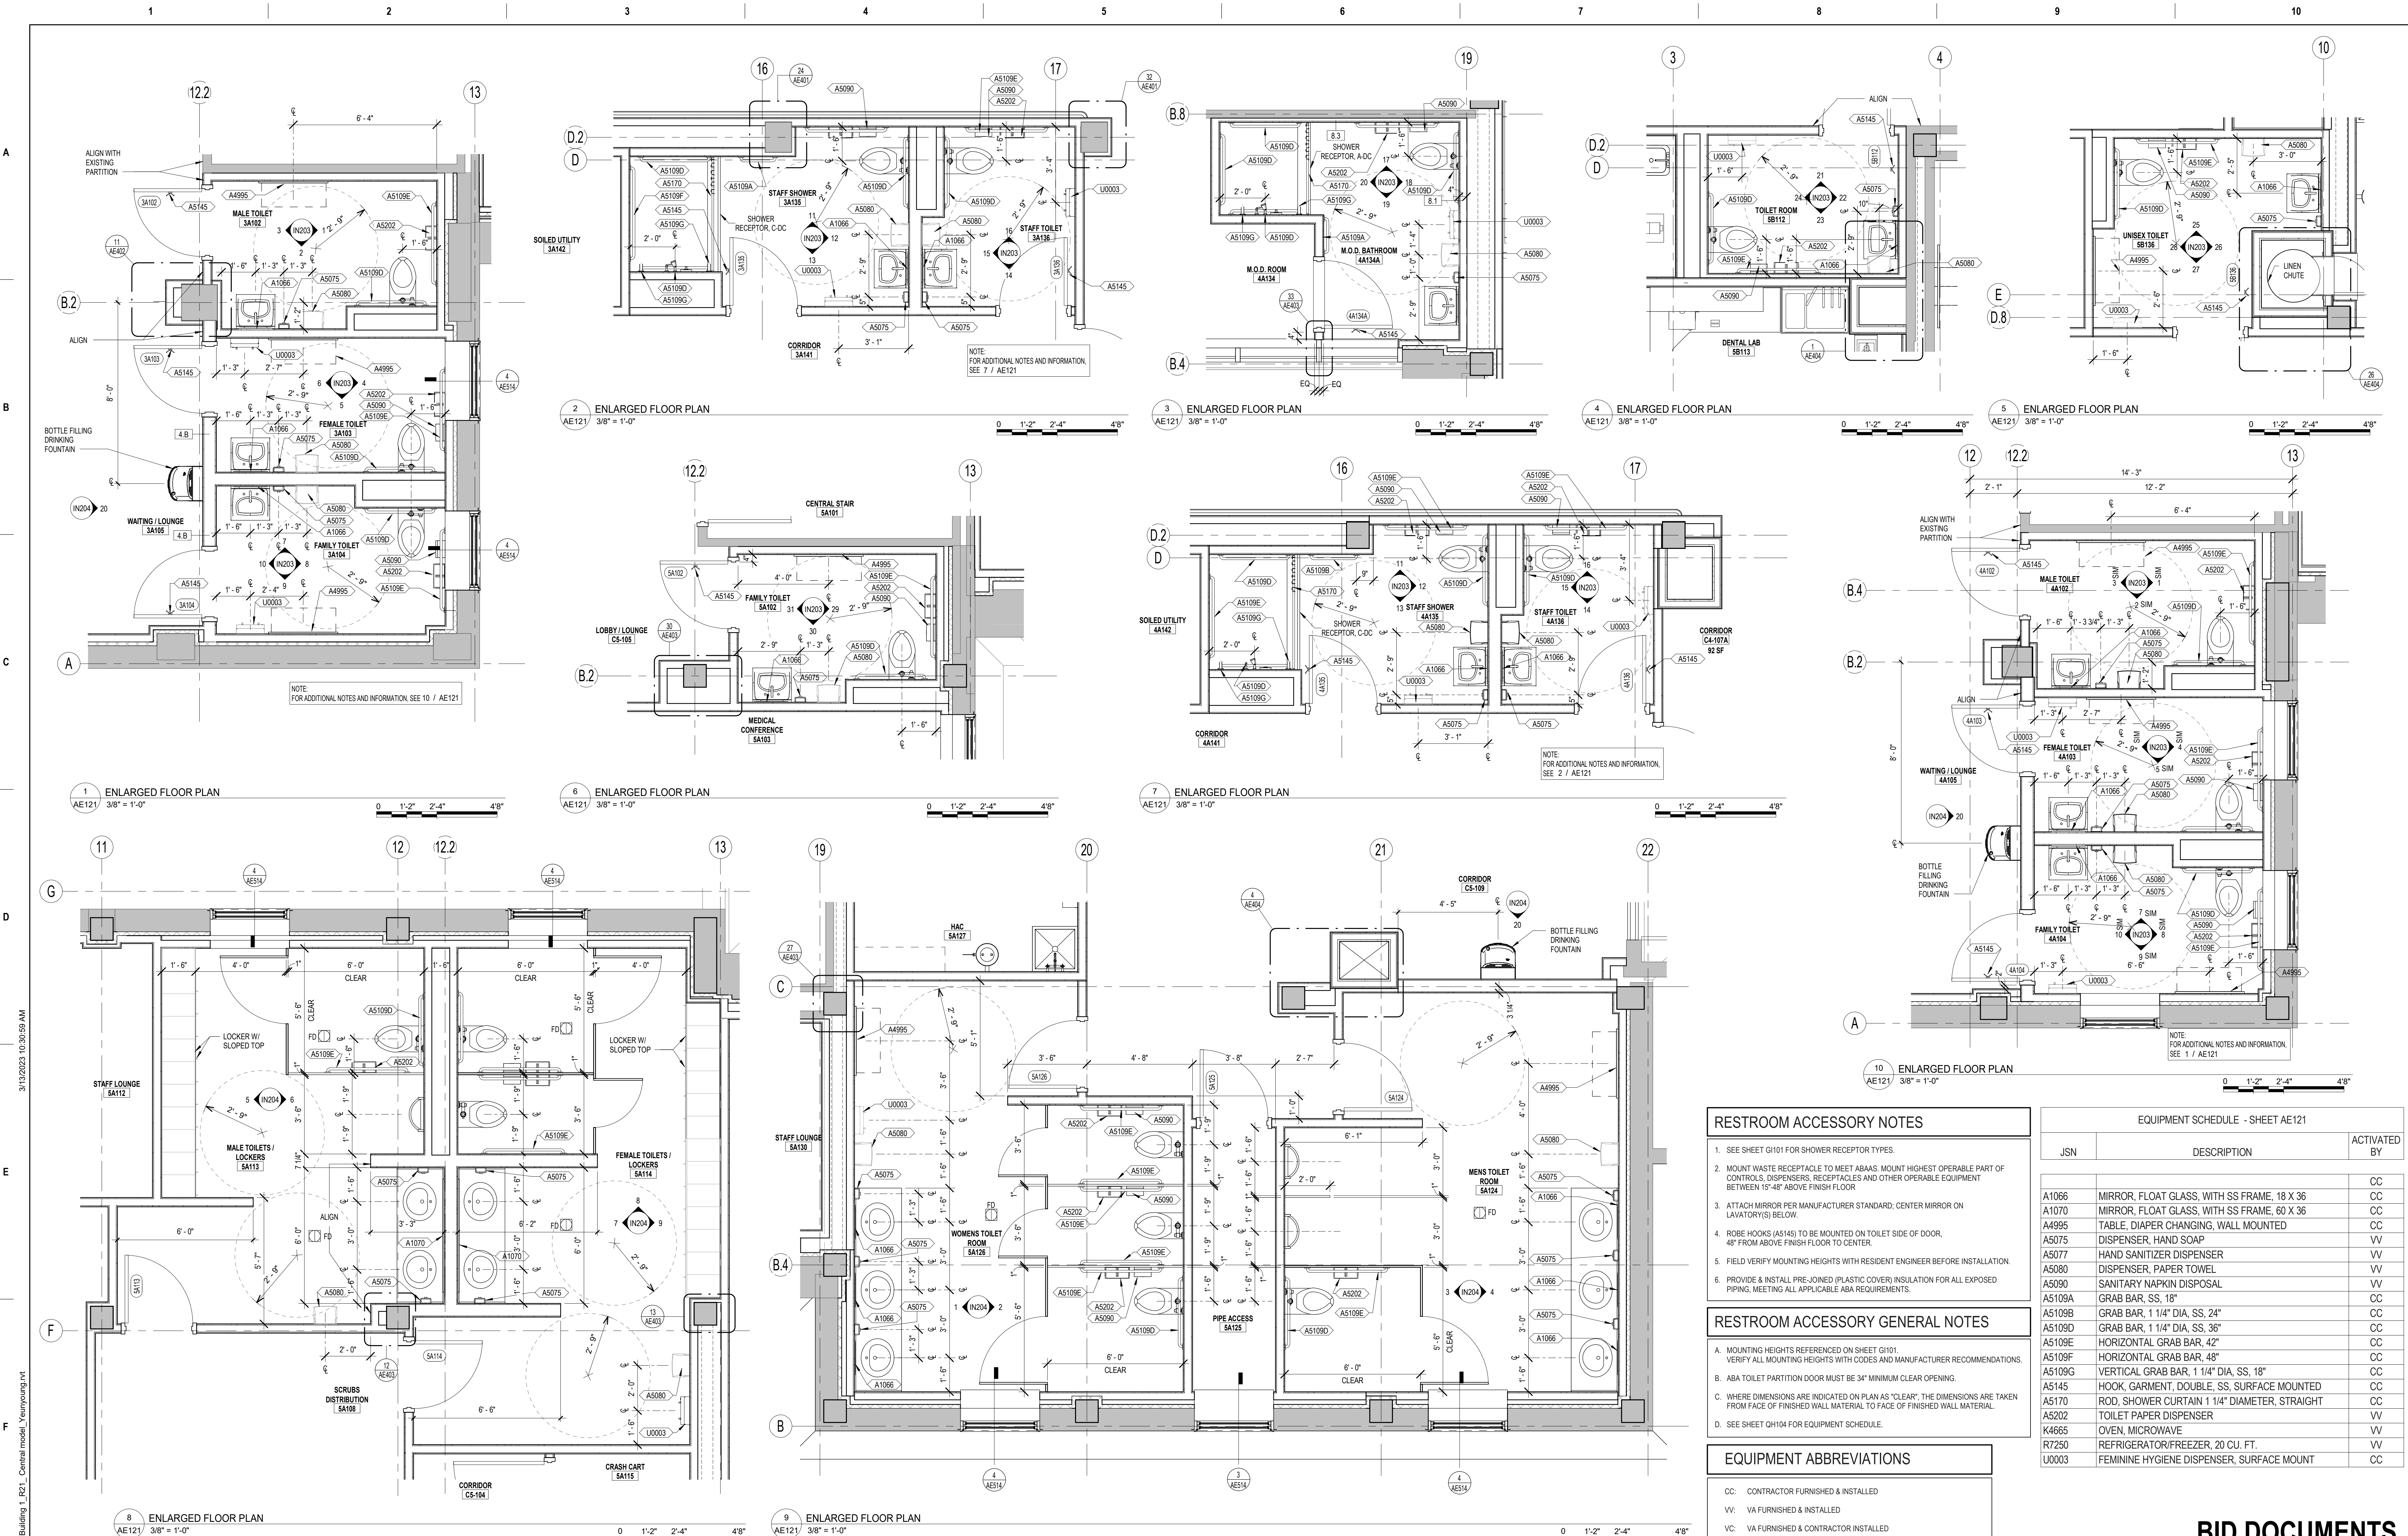


RESTROOM ACCESSORY NOTES		
1. SEE SHEET G101 FOR SHOWER RECEPTOR TYPES.		
2. MOUNT WASTE RECEPTACLE TO MEET ABAAS. MOUNT HIGHEST OPERABLE PART OF CONTROLS, DISPENSERS, RECEPTACLES AND OTHER OPERABLE EQUIPMENT BETWEEN 15'-48" ABOVE FINISH FLOOR.		
3. ATTACH MIRROR PER MANUFACTURER STANDARD; CENTER MIRROR ON LAVATORY(S) BELOW.		
4. ROBE HOOKS (A5145) TO BE MOUNTED ON TOILET SIDE OF DOOR, 48" FROM ABOVE FINISH FLOOR TO CENTER.		
5. FIELD VERIFY MOUNTING HEIGHTS WITH RESIDENT ENGINEER BEFORE INSTALLATION.		
6. PROVIDE & INSTALL PRE-JOINED (PLASTIC COVER) INSULATION FOR ALL EXPOSED PIPING, MEETING ALL APPLICABLE ABA REQUIREMENTS.		
RESTROOM ACCESSORY GENERAL NOTES		
A. MOUNTING HEIGHTS REFERENCED ON SHEET G101.		
B. ABA TOILET PARTITION DOOR MUST BE 34" MINIMUM CLEAR OPENING.		
C. WHERE DIMENSIONS ARE INDICATED ON PLAN AS "CLEAR", THE DIMENSIONS ARE TAKEN FROM FACE OF FINISHED WALL MATERIAL TO FACE OF FINISHED WALL MATERIAL.		
D. SEE SHEET Q1104 FOR EQUIPMENT SCHEDULE.		
EQUIPMENT ABBREVIATIONS		
CC: CONTRACTOR FURNISHED & INSTALLED		
VV: VA FURNISHED & INSTALLED		
VC: VA FURNISHED & CONTRACTOR INSTALLED		

EQUIPMENT SCHEDULE - SHEET AE121		
JSN	DESCRIPTION	ACTIVATED BY
A1066	MIRROR, FLOAT GLASS, WITH SS FRAME, 18 X 36	CC
A1070	MIRROR, FLOAT GLASS, WITH SS FRAME, 60 X 36	CC
A4995	TABLE, DIAPER CHANGING, WALL MOUNTED	CC
A5075	DISPENSER, HAND SOAP	VV
A5077	HAND SANITIZER DISPENSER	VV
A5080	DISPENSER, PAPER TOWEL	VV
A5090	SANITARY NAPKIN DISPOSAL	VV
A5109A	GRAB BAR, SS, 18"	CC
A5109B	GRAB BAR, 1 1/4" DIA, SS, 24"	CC
A5109D	GRAB BAR, 1 1/4" DIA, SS, 36"	CC
A5109E	HORIZONTAL GRAB BAR, 42"	CC
A5109F	HORIZONTAL GRAB BAR, 48"	CC
A5109G	VERTICAL GRAB BAR, 1 1/4" DIA, SS, 18"	CC
A5145	HOOK, GARMENT, DOUBLE, SS, SURFACE MOUNTED	CC
A5170	ROD, SHOWER CURTAIN 1 1/4" DIAMETER, STRAIGHT	CC
A5202	TOILET PAPER DISPENSER	VV
K4665	OVEN, MICRO/WAVE	VV
R7250	REFRIGERATOR/FREEZER, 20 CU. FT.	VV
U0003	FEMININE HYGIENE DISPENSER, SURFACE MOUNT	CC

BID DOCUMENTS

CONSULTANT		ARCHITECT/ENGINEER OF RECORD		STAMP		Office of Construction and Facilities Management		Drawing Title ENLARGED FLOOR PLANS		Phase CONSTRUCTION DOCUMENTS		Project Title RENOVATE BUILDING 1		Project Number 520-317X	
THOMAS OLESACK, ARCHITECT		MS Lic # 5505		Thomas Olesack STATE OF MISSISSIPPI 03.10.2023		U.S. Department of Veterans Affairs		Approved:		FULLY SPRINKLERED		Location BILOXI, MISSISSIPPI		Building Number 1	
1050 HOYT AVE WEST ST PAUL, MN 55117 952-451-0460												Issue Date 03/10/2023		Checked LA	
NO. REVISIONS		DATE										Drawn CD,PC		Dwg. 77 of 238	

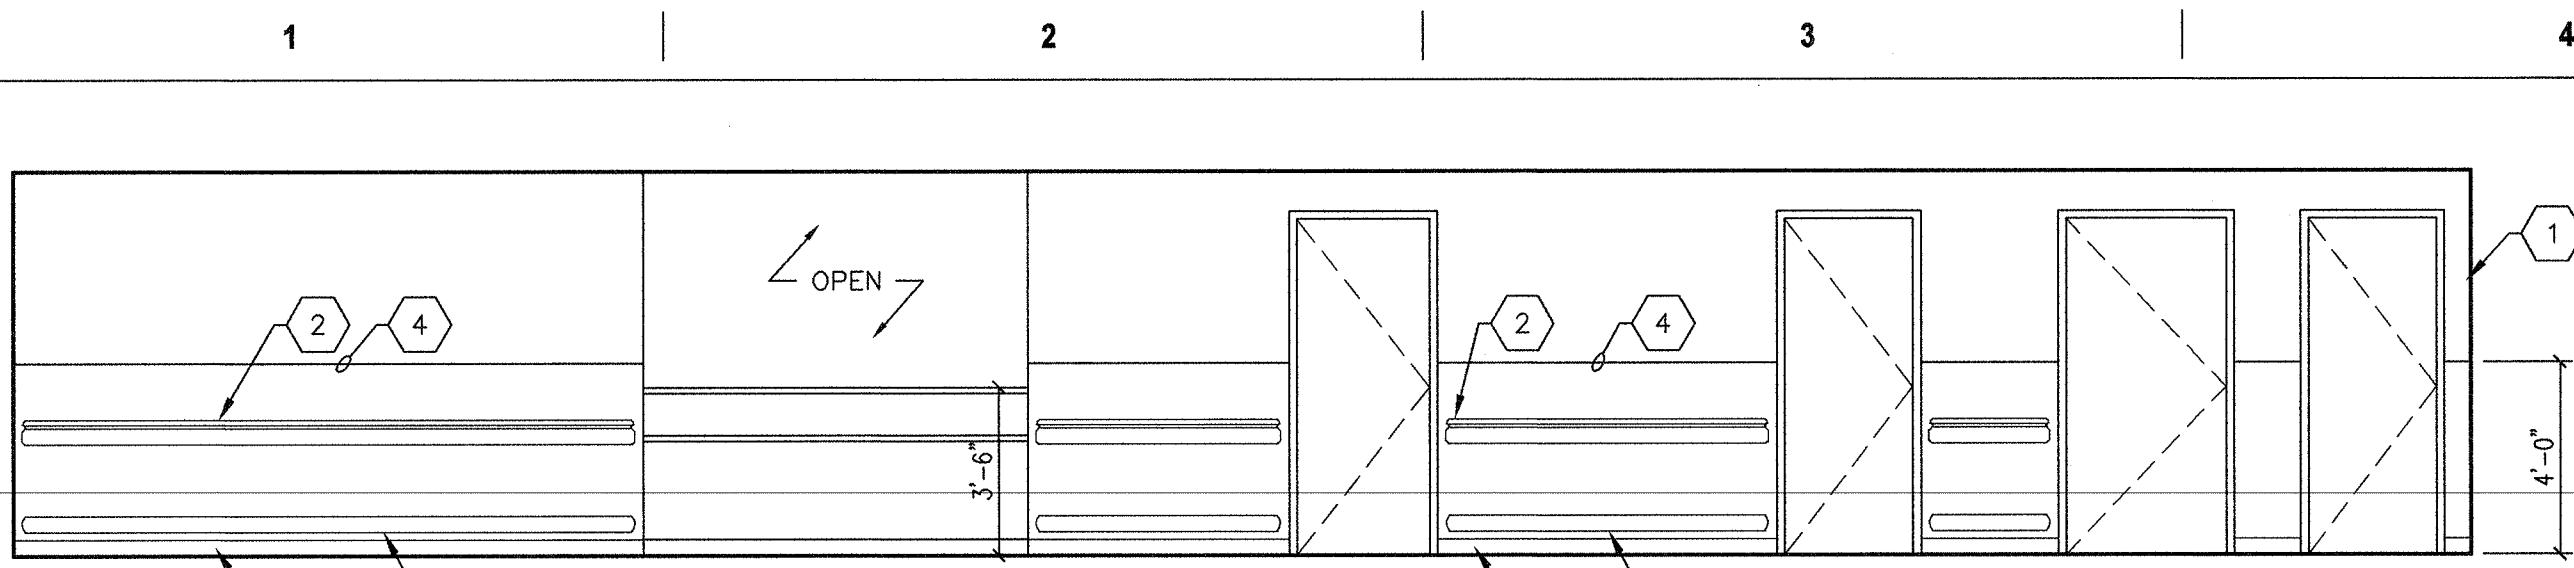




U.S. Department
of Veterans Affairs

Class 1 Radiology Imaging Room, Imgng Svcs (CI011)


ELEVATIONS

SKETCH TITLE

SCALE: 1/4" = 1'-0"

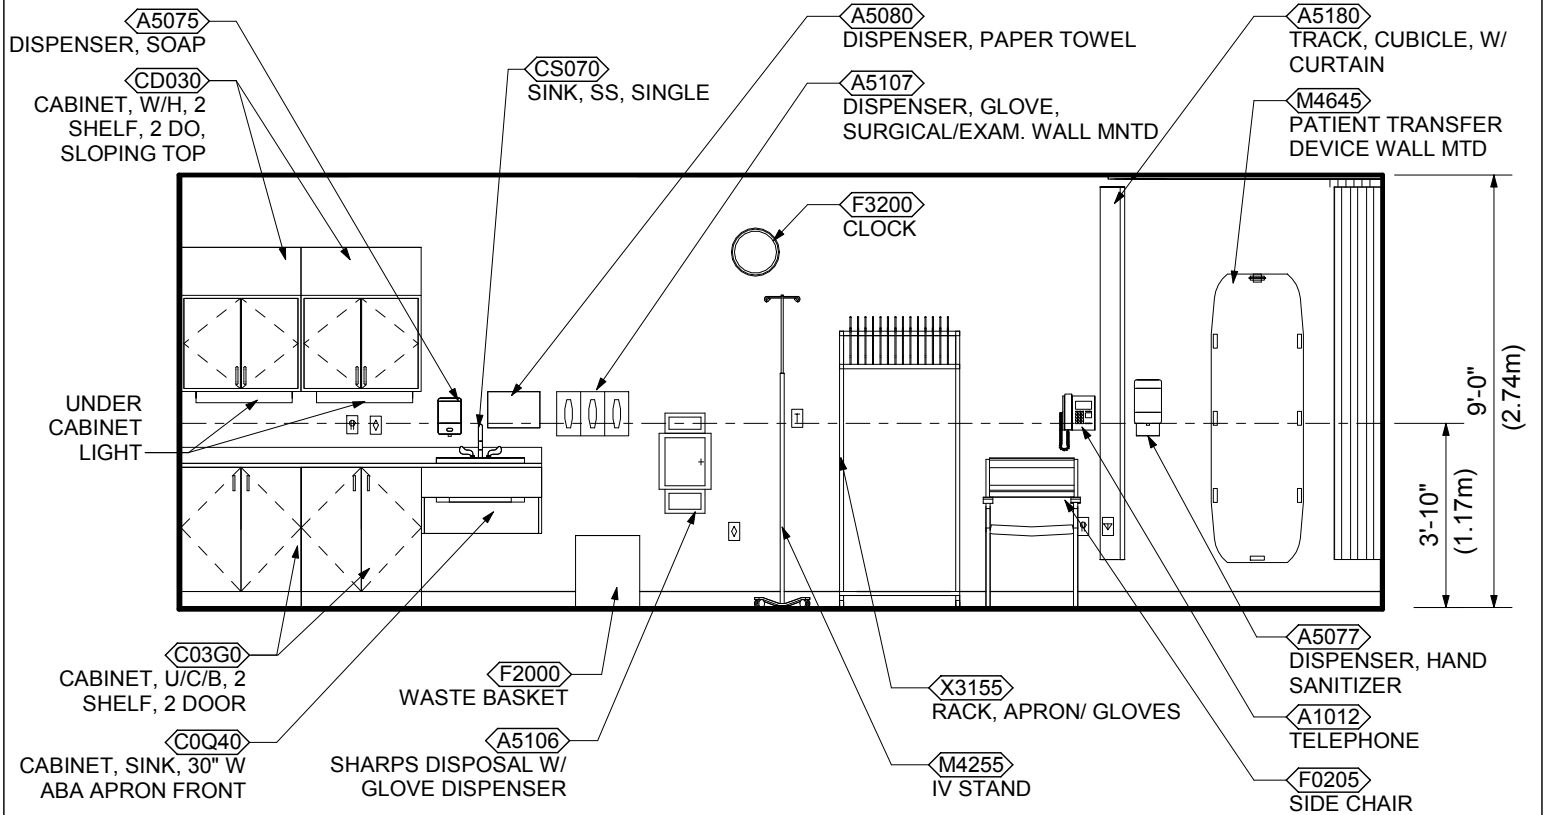

ELEVATION 1

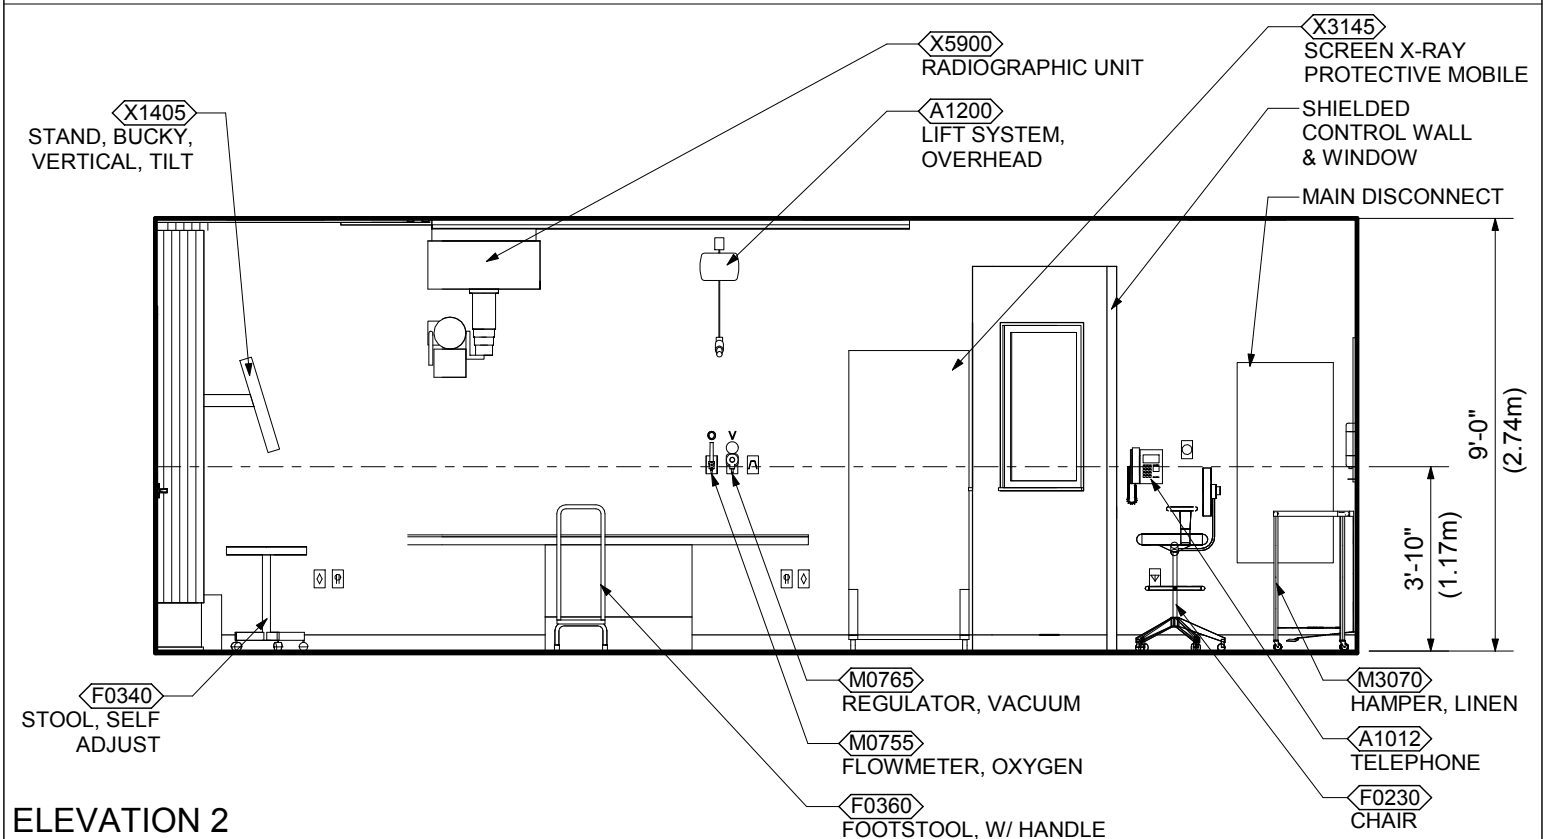

ELEVATION 2

DISCLAIMER: ROOM TEMPLATES ARE GRAPHICAL REPRESENTATIONS OF SELECTED ROOM TYPES THAT ILLUSTRATE VA PLANNING REQUIREMENTS FOR SPACE, ROOM CONTENTS, AND ROOM SPECIFIC ENGINEERING SYSTEMS. THEY PROVIDE TYPICAL CONFIGURATIONS, PLANNING CRITERIA, AND GENERAL TECHNICAL GUIDANCE, AND ARE NOT INTENDED TO BE PROJECT SPECIFIC REQUIREMENTS.

