

three inches = one foot

one and one half inches = one foot

one inch = one foot

three quarters inch = one foot

one half inch = one foot

one quarter inch = one foot

one eighth inch = one foot

one quarter inch = one foot

one eighth inch = one foot

one eighth inch = one foot

one eighth inch = one foot

FINISH SCHEDULE					FINISH SPECIFICATIONS				
NO.	ROOM	FLOORS		WALLS	WELDED SHEET VINYL		PLASTIC LAMINATE		
		WVS/VCT	P		WVS/VCT	P	PL-1	P	
100	WAITING	1	1	1	WVS-1	MANF. JONESTONE COLOR: WALNUT STREET W/ INTERGLAZE BASE	PL-1	MANF. WILSONART COLOR: ASIAN SAND - 7552K-18	
101	DRESS	1	1	1	VCT-1	MANF. JONESTONE COLOR: LUNAR BLUE 51932	PL-2	MANF. WILSONART COLOR: PASADENA OAK - 7552K-18	
102	ADA DRESS	1	1	1					
103	CLEAN	1	1	1					
104	SOILED	1	1	1					
105	CONTROL ROOM	1	1	1					
106	SUB-WAITING	1	1	1					
107	MRI SCAN ROOM	1	1	1					
108	EQUIP. ROOM	1	1	1					
109	CL	1	1	1					
110	CL	1	1	1					

PARTITION TYPES				
ALL NEW WALLS PARTITION TYPE #1 UNLESS OTHER WISE NOTED UNDERSIDE OF STRUCTURAL DECKING 3/8" METAL STUDS MIN. 22 GAUGE @ 16" O.C. 5/8" GWS EACH SIDE WALL BASE STUD RUNNER ANCHORED TO SUB TYPE 1 PARTITION NTS UNDERSIDE OF STRUCTURAL DECKING 3/8" METAL STUDS MIN. 22 GAUGE @ 16" O.C. 5/8" GWS EACH SIDE WALL BASE STUD RUNNER ANCHORED TO SUB TYPE 2 PARTITION NTS				


INTERIOR DOOR SCHEDULE						
NO.	LOCATION	TYPE	DESCRIPTION	SIZE	FINISH	HARDWARE
1	WAITING - 100	4	HINGED DOUBLE	6'-0" x 7'-0" x 1 3/4"	STAINED	1
2	DRESS - 101	1	HINGED SINGLE	3'-0" x 7'-0" x 1 3/4"	STAINED	3
3	DRESS - 102	1	HINGED SINGLE	3'-0" x 7'-0" x 1 3/4"	STAINED	3
4	CLEAN - 103	3	HINGED DOUBLE	3'-0" x 7'-0" x 1 3/4"	STAINED	4
5	SOILED - 104	3	HINGED DOUBLE	3'-0" x 7'-0" x 1 3/4"	STAINED	4
6	WAITING - 100	1	HINGED DOUBLE	3'-0" x 7'-0" x 1 3/4"	STAINED	1
7	CL - 109	3	HINGED DOUBLE	3'-0" x 7'-0" x 1 3/4"	STAINED	5
8	CONTROL ROOM - 105	1	HINGED SINGLE	3'-0" x 7'-0" x 1 3/4"	STAINED	6
9	CONTROL ROOM - 105	1	HINGED SINGLE	3'-0" x 7'-0" x 1 3/4"	STAINED	2
10	MRI SCAN ROOM - 107	2	HINGED SINGLE	4'-0" x 7'-0" x 1 3/4"	PL-2	2
11	EQUIP. ROOM - 108	1	HINGED SINGLE	3'-0" x 7'-0" x 1 3/4"	STAINED	1
12	CL - 110	3	HINGED DOUBLE	3'-0" x 7'-0" x 1 3/4"	STAINED	5

INTERIOR DOOR TYPES				
TYPE "1"	TYPE "2"	TYPE "3"	TYPE "4"	


HARDWARE SPECIFICATIONS		HARDWARE SCHEDULE	
BUTT HINGES STANLEY FBB199 4 1/2" x 4 1/2" (A) INTERIOR DOORS USED (B) EXTERIOR DOORS WHICH ARE DEFINED AS DOORS EXPOSED TO THE ELEMENTS SHALL BE US32D.		HW SET #1 3 PAIR 1 1 2 1	
LOCKSETS AND LATCHSETS YALE CAMEL - CRI LEVER HARDWARE - COORDINATE FINISH WITH BUILDING MANAGEMENT		BUTT HINGES LATCHSET DUMMY LEVER SET CLOSERS FLUSH BOLT	
STOPS STOPS #436 AND #407 AS MANUFACTURED BY IVES OR APPROVED EQUAL. PROVIDE ONE FOR EACH INTERIOR DOOR.		HW SET #2 - 1 1	
MISCELLANEOUS ITEMS (1) SILENCERS OLIVIA-JOHNSON Q384 THREE PAIRS PER EACH SINGLE DOOR, TWO EACH PER PAIR OF DOORS SHALL BE FURNISHED.		HW SET #3 1 1/2 PAIR 1 1	
NOTES: 1. ALL DOORS MUST OPEN TO A FULL 90 DEGREES UNLESS OTHERWISE NOTED. 2. ALL HARDWARE TO BE ADA COMPLIANT. 3. OWNER TO SELECTION FINISHES.		HW SET #4 1 1/2 PAIR 1 1	
		HW SET #5 3 1/2 PAIR 2 2	

PLAN/CEILING SYMBOLS			
D- DEMOLISH	E- EXISTING	R- RELOCATED	N- NEW
WALL TO BE REMOVED	EXIST WALL, TO REMAIN	NEW WALL	SHIELDING WALL
DOOR NUMBER	PARTITION TYPE	2' X 2' LAY-IN FIXTURE	

DESIGN/BUILDER:		ARCHITECT/ENGINEERS:	
Deerfield Construction Group 610 Professional Drive, Suite 210 Gaithersburg, Maryland 20879 (301)947-4701		Nicholas Lucarelli Architects, LLC 6723 Whittier Avenue Suite 414 Mclean, VA 22101 Tel: (703) 790-9606	
D2 Engineering, LLC 18310 Montgomery Village Ave Suite 520 Gaithersburg, MD 20879 Tel: (301) 208-9575 Fax: (301) 208-9405		PROPERTY OF THE UNITED STATES GOVERNMENT FOR OFFICIAL USE ONLY DO NOT REMOVE THIS NOTICE. PROPERLY DESTROY DOCUMENTS WHEN NO LONGER NEEDED.	

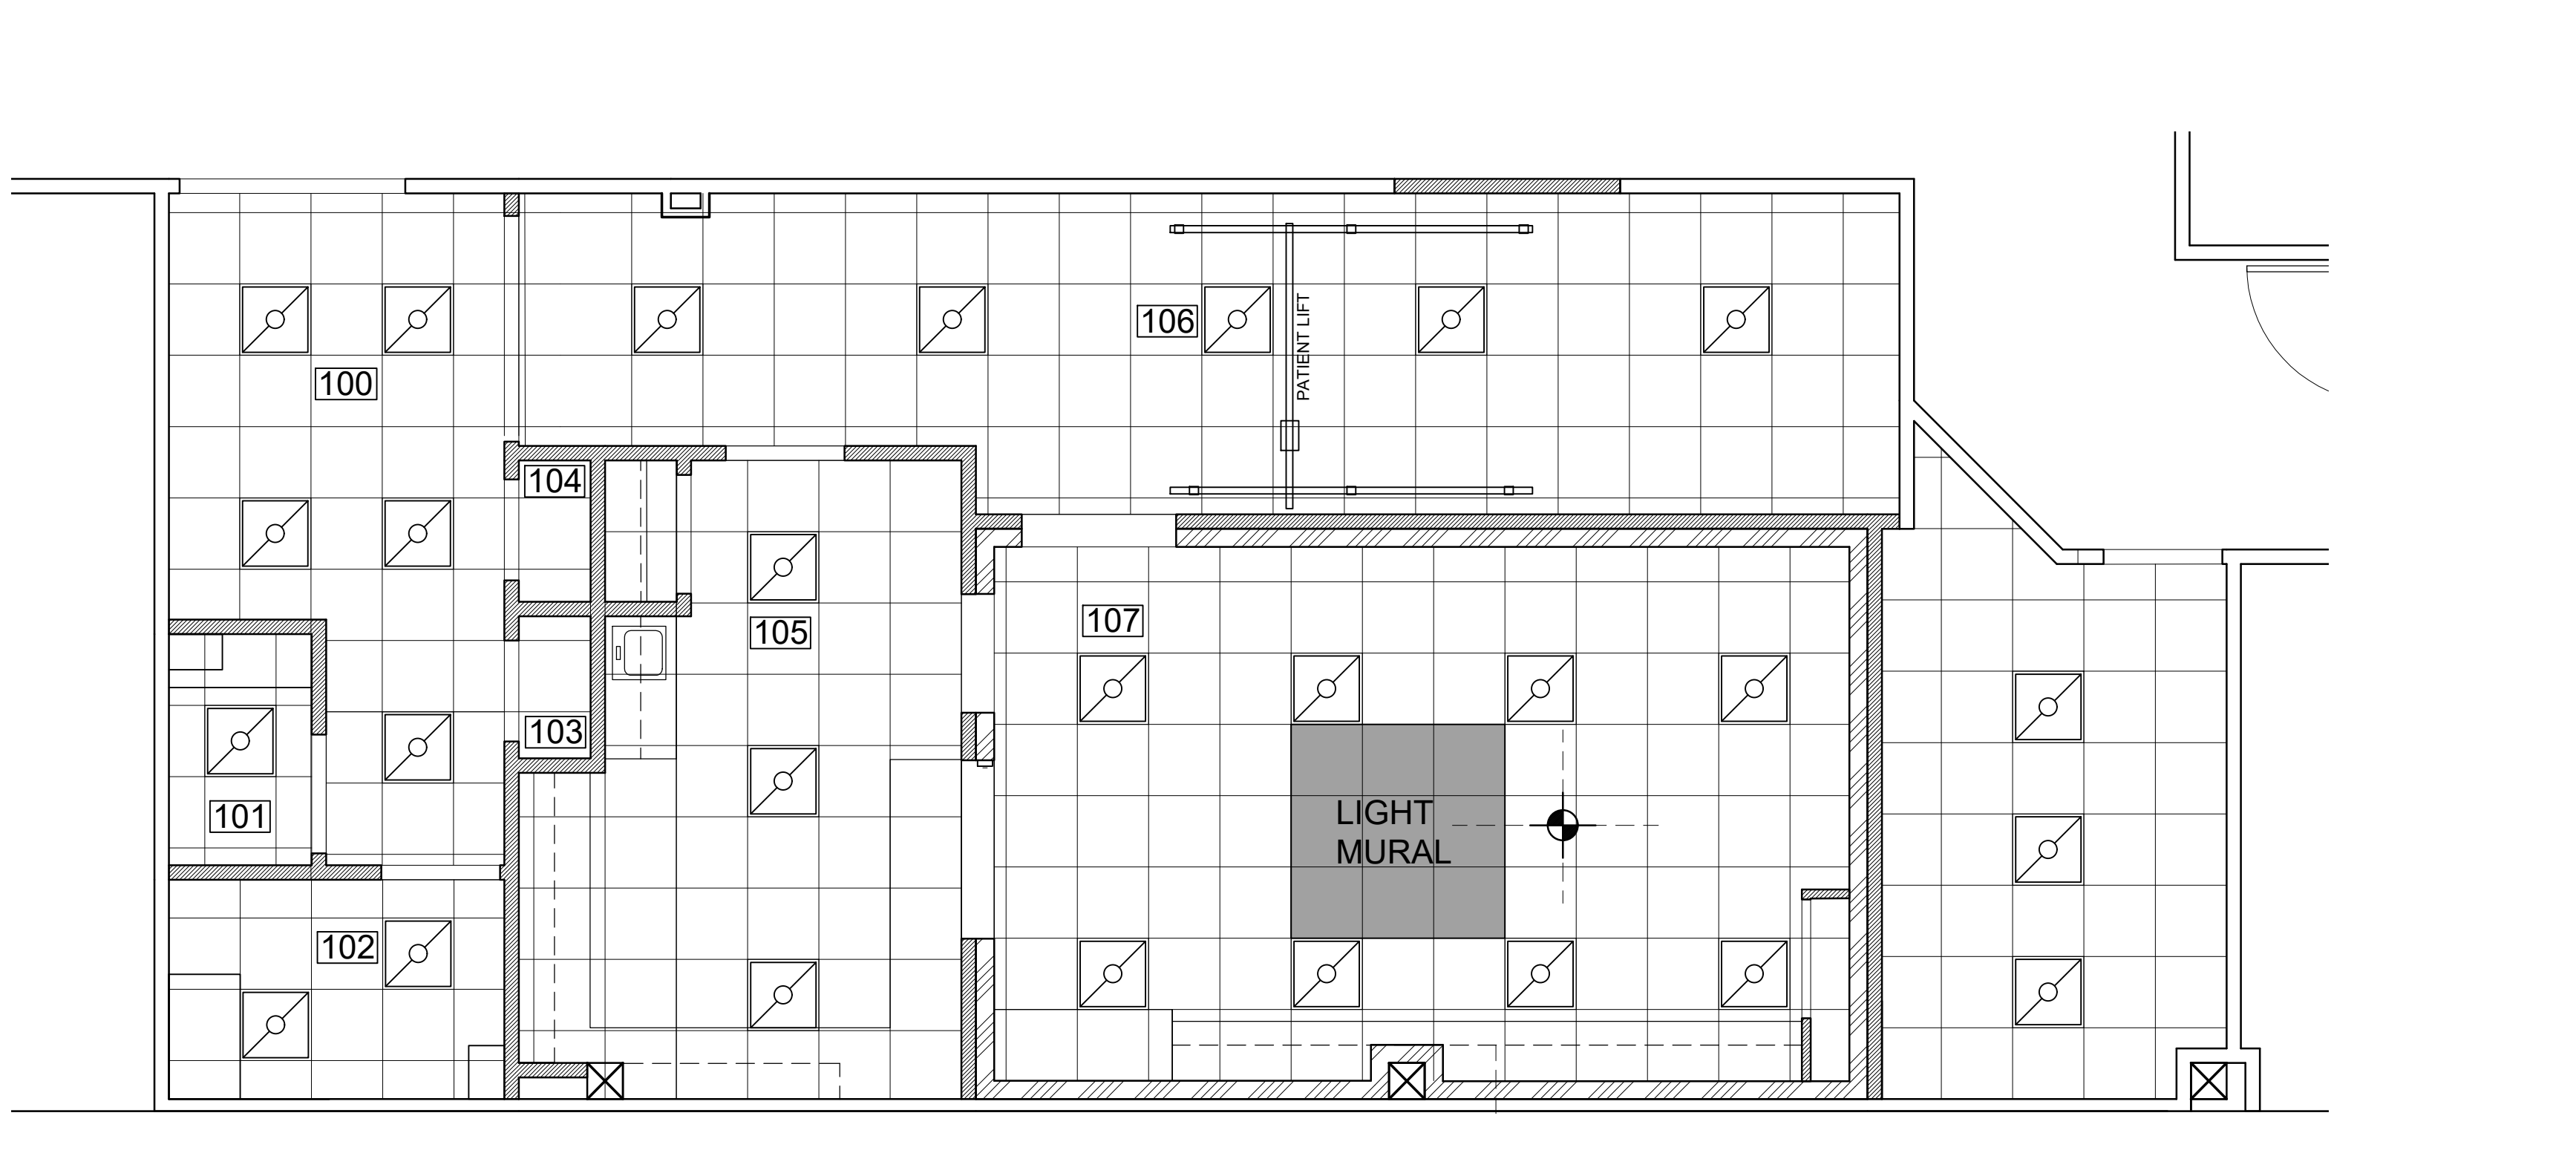

1 REFLECTED CEILING PLAN
SCALE: 1/4" = 1'-0"

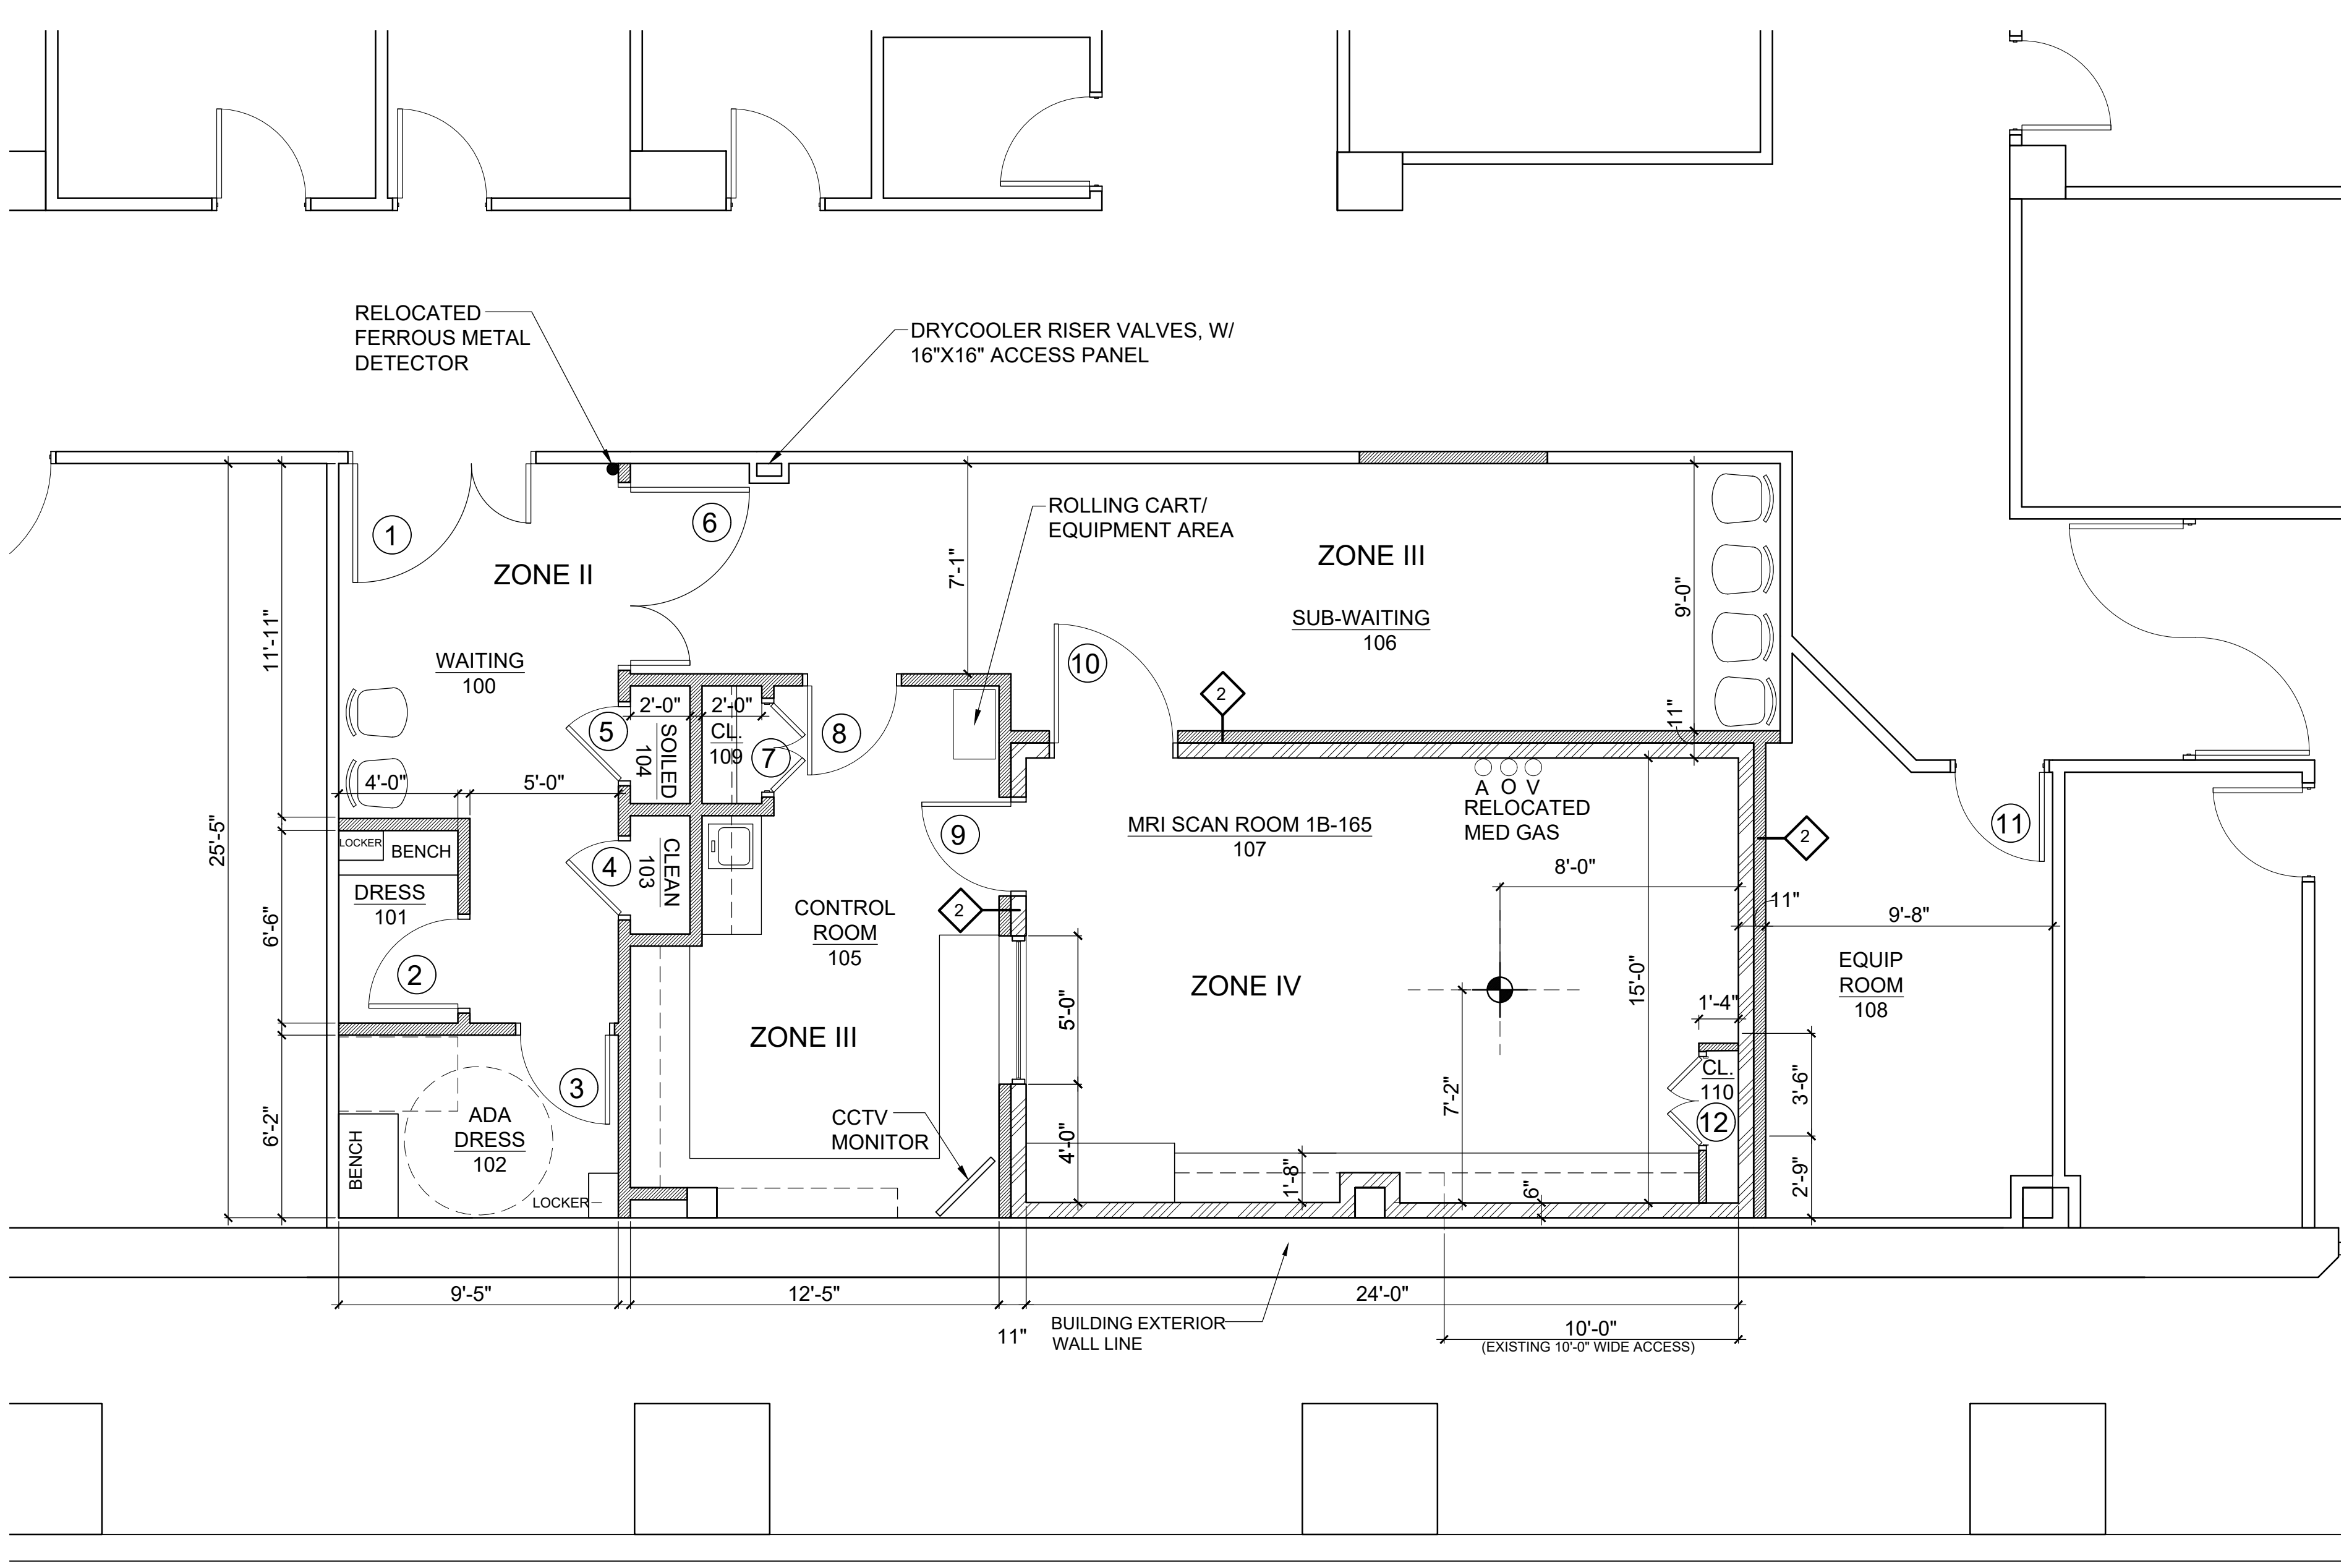

1 FLOOR PLAN
SCALE: 1/4" = 1'-0"



GREAT PLAINS AREA INDIAN HEALTH SERVICE
OFFICE OF ENVIRONMENTAL
HEALTH & ENGINEERING

DIVISION OF FACILITIES MANAGEMENT
115 4TH AVENUE SE, RM 309
ABERDEEN, SD 57401
(605) 226-7451 FAX (605) 226-7580

www.ihs.gov


Quentin N. Burdick
Memorial Health Facility

Replace RTU &
Cabinetry - CT Area


CONTRACT NO:	
TASK ORDER NO:	
PROJECT NUMBER:	GP22TM300H10
DATE:	08/26/2025
DRAWN BY:	Taylor Strand
CHECKED BY:	Brad Weekley
LAST REVISION DATE:	

CASEWORK SECTION
VIEWS

A.3

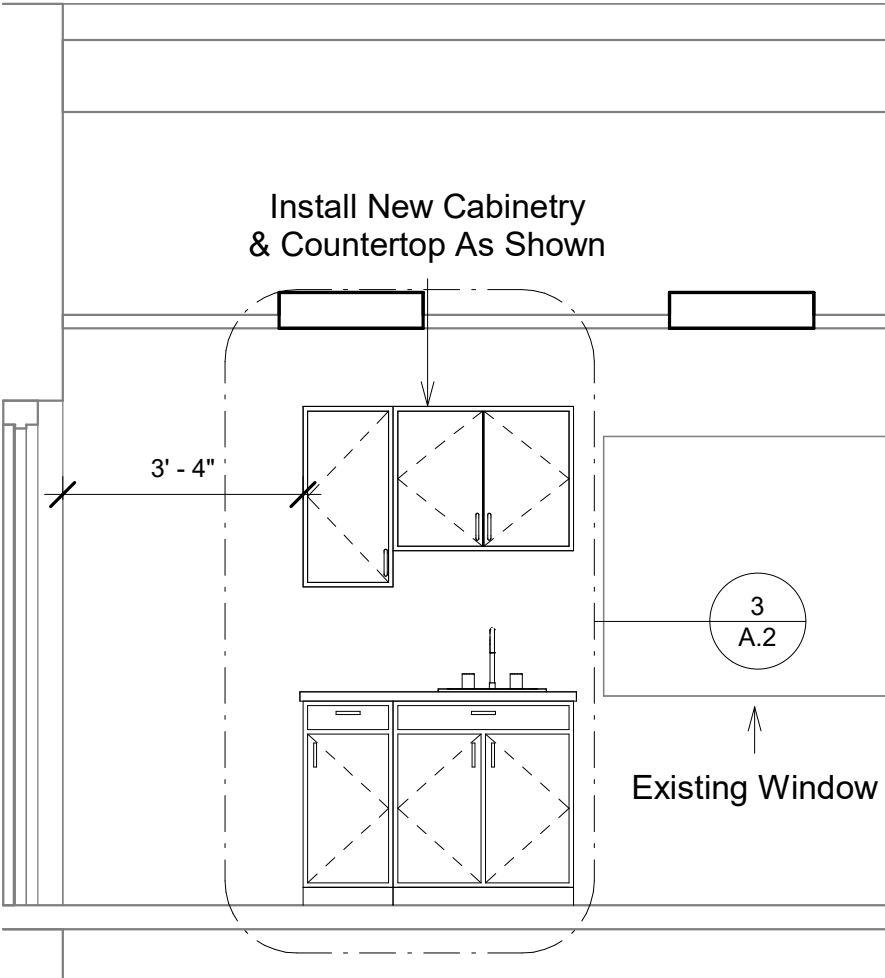

① North Wall Cabinets Copy 1
3/8" = 1'-0"

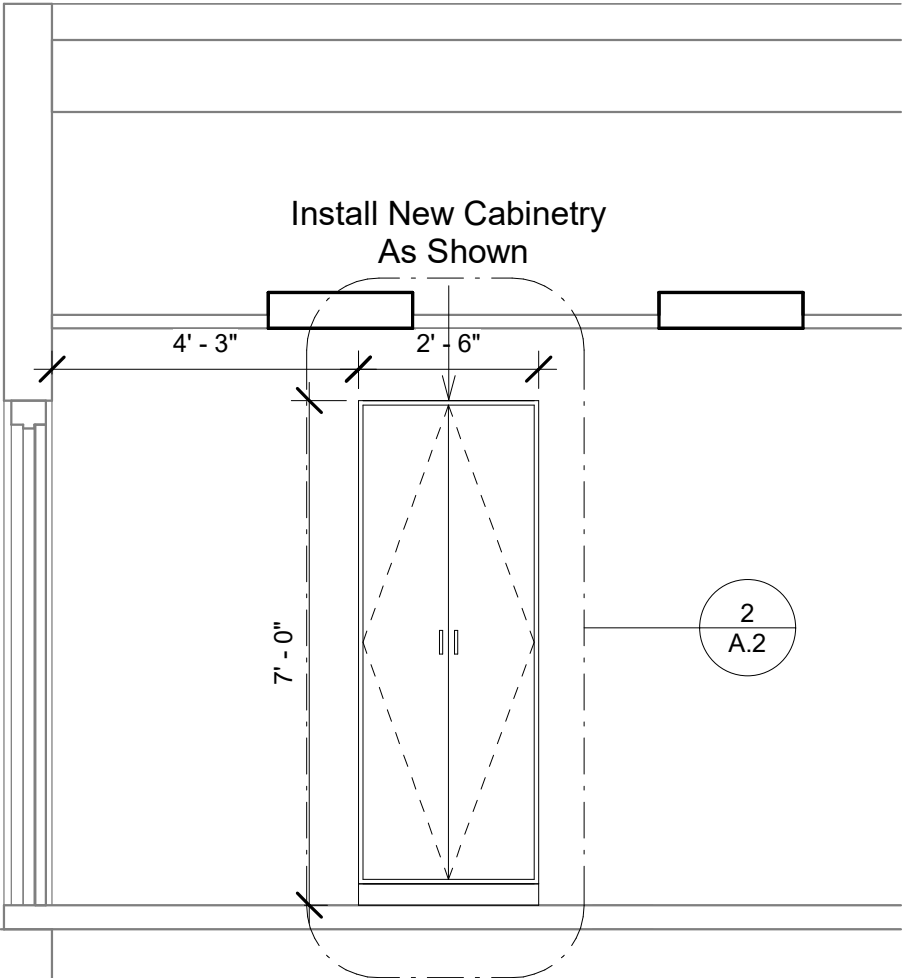

② South Wall Cabinets Copy 1
3/8" = 1'-0"

DENTAL LAB GENERAL NOTES

- DENTAL LAB CASEWORK AND WORK BENCHES ARE SPECIFIED IN SECTION 12 35 40. VENDOR DRAWINGS ARE PROVIDED IN APPENDIX. CC SHALL COORDINATE INSTALLATION OF UTILITY CONNECTIONS WITH REQUIREMENTS SPECIFIED AND SHOWN THEREIN.
- AVOID CUTTING CONCRETE FLOOR JOIST.

EQUIPMENT ABBREVIATIONS

- CC: CONTRACTOR FURNISHED & INSTALLED
VV: VA FURNISHED & INSTALLED
VC: VA FURNISHED & CONTRACTOR INSTALLED

EQUIPMENT SCHEDULE - SHEET AE124

JSN	DESCRIPTION	ACTIVATED BY	Comments
A1012	TELEPHONE, WALL MOUNTED	VV	
A1066	MIRROR, FLOAT GLASS, WITH SS FRAME, 18 X 36	CC	
A5075	DISPENSER, HAND SOAP	VV	
A5077	HAND SANITIZER DISPENSER	VV	
A5080	DISPENSER, PAPER TOWEL	VV	
A5106	WASTE DISPOSAL UNIT, SHARPS	VV	
A5145	HOOK, GARMENT, DOUBLE, SS, SURFACE MOUNTED	CC	
D0670	CONSOLE, TREATMENT UNIT, DENTAL OPERATORY	CC	SEE SPEC SECTION 12 35 70.74
D0680	CONSOLE, ACCESSORY/SIDE DENTAL OPERATORY	CC	SEE SPEC SECTION 12 35 70.74
D0682	3 GLOVE DISPENSING CABINET, DENTAL OPERATORY	CC	SEE SPEC SECTION 12 35 70.74
D0685	STORAGE CABINET, DENTAL OPERATORY - 34 INCH WIDE	CC	SEE SPEC SECTION 12 35 70.74
D0685B	STORAGE CABINET, FULL HEIGHT, 2 DOORS, LOCKABLE DENTAL	CC	SEE SPEC SECTION 12 35 70.74
D0755	TANK ASSEMBLY, BOILOUT - CURING, DOUBLE	CC	SEE SPEC SECTION 12 34 50, SEE EP103 & PL106 MEP FOR CONNECTIONS
D2520	MOBILE STORAGE CABINET	CC	SEE SPEC SECTION 12 35 70.74
D3320	CHAIR, DENTAL OPERATING	CC	SEE SPEC SECTION 11 74 00
D3565	RESIN CURING UNIT, VISABLE LIGHT	VV	
D4100	CLEANER, STEAM, DENTAL	VV	
D4260	HANDPIECE, LABORATORY, DENTAL, ELECTRIC	VV	
D4320	PRESS, FLASK, HYDRAULIC, SINGLE FLASK	VV	
D4560	ENGINE, DENTAL BENCH, ELECTRIC	VV	
D4590	CHISEL, DENTAL, PNEUMATIC	VV	
D6600	MIXER/INVESTOR, WITH VACUUM	VV	
D6650	FROMER, VACUUM, W/MOTOR, VACCUM PUMP, HEATER	VV	
D8250	DELIVERY SYSTEM, DENTAL OPERATORY WITH ASST INSTRUMENTATION	CC	SEE SPEC SECTION 11 74 00
D8530	DENTAL POLISHER	VV	
D8850	AMAL GAMATOR, DENTAL	VV	
D8950	VIBRATOR, DENTAL, HEAVY DUTY	VV	
D9015	MICROFINISHER, DENTAL, COUNTER MOUNTED	VV	
D9035	DRIVER, MODEL INDEXING PINS	VV	
D9050	TRIMMER, MODEL, DENTAL 0.25 HP	VV	
DX001	PRESSURE POT 8 QUART	VV	
DX002	DENTAL WORK BENCH, 23" DEPTH	VC	SEE SPEC SECTION 12 34 50
DX003	AIR HOSE X6 + ACCESSORIES	VV	
DX004	SAND SHELL XL	VV	
DX005	WAXING UNIT	VV	
DX006	TOUCH O MATIC BUN BURNER NATURAL GAS #77-0	VV	
DX007	AIR PURIFIER 301F	VV	
DX008	SAND VAC GRAY	VV	
DX009	ATLAS UPPER FLASK W/REAR GUIDE PIN #44U	VV	
DX010	ATLAS LOWER FLASK W/REAR GUIDE PIN #44L	VV	
DX011	COMPRESS FLASKS F2	VV	
DX012	RELINIE JIG 2 POST	VV	
DX013	IMPULSE HEAT SEALER	VV	
DX014	FLAMMABLE CABINET	VV	
DX016	ARTICULATOR MOUNTING PLATE	VV	
DX017	HANAU WIDE - VUE ARTICULATOR HANAU ARCON 183-2	VV	
DX018	WHIP MIX MODEL 2240 ARTICULATOR W/SERIES 200 FRAME	VV	
DX019	CURING UNIT	VV	
DX020	DENTAL MOLDING VIBRATOR	VV	
DX021	FUME HOOD	CC	SEE SPEC SECTION 23 38 13
DX023	DENTAL LAB CASEWORK	VC	SEE SPEC SECTION 12 34 50
M1801A	LAPTOP COMPUTER	VV	
M1803	COMPUTER WORKSTATION, WALL MOUNTED	CC	
P7650	TRAP, PLASTER, SMALL	CC	
X6600	RADIOGRAPHIC XRAY UNIT (PLANMECA PRO-X)	VV	
X6610	SENSOR, DENTAL IMAGING SYSTEM (PLANMECA PRO-X)	VV	
X6620	EXPOSURE SWITCH - DENTAL XRAY (PLANMECA PRO-X)	VV	

NOTE: LAB CASEWORK AND DENTAL WORK BENCHES SHOWN ARE FOR REFERENCE ONLY. REFER TO VENDOR DRAWINGS IN APPENDIX & SPECIFICATION SECTION 12 35 40.

0 1'-2" 2'-4" 4'-8"

NOTE: DENTAL CASEWORK TO BE CONTRACTOR PROVIDED AND INSTALLED. SEE SPEC SECTION 12 35 70.74 & DRAWINGS IN THE APPENDIX.

BID DOCUMENTS

NO.	REVISIONS	DATE

CONSULTANT

ARCHITECT/ENGINEER OF RECORD

THOMAS OLESAC, ARCHITECT
MS Lic # 5505

1050 HOYT AVE WEST ST PAUL, MN 55117
952-451-0460

STAMP



Office of
Construction
and Facilities
Management



U.S. Department of
Veterans
Affairs

Drawing Title

ENLARGED FLOOR PLANS

Approved:

Phase

CONSTRUCTION
DOCUMENTS

FULLY SPRINKLERED

Project Title

RENOVATE BUILDING 1

Location

BILOXI, MISSISSIPPI

Issue Date

03/10/2023

Checked

LA

Drawn

CD,PC

Project Number

520-317X


Building Number

1


Drawing Number

AE124

Dwg. 80 of 238

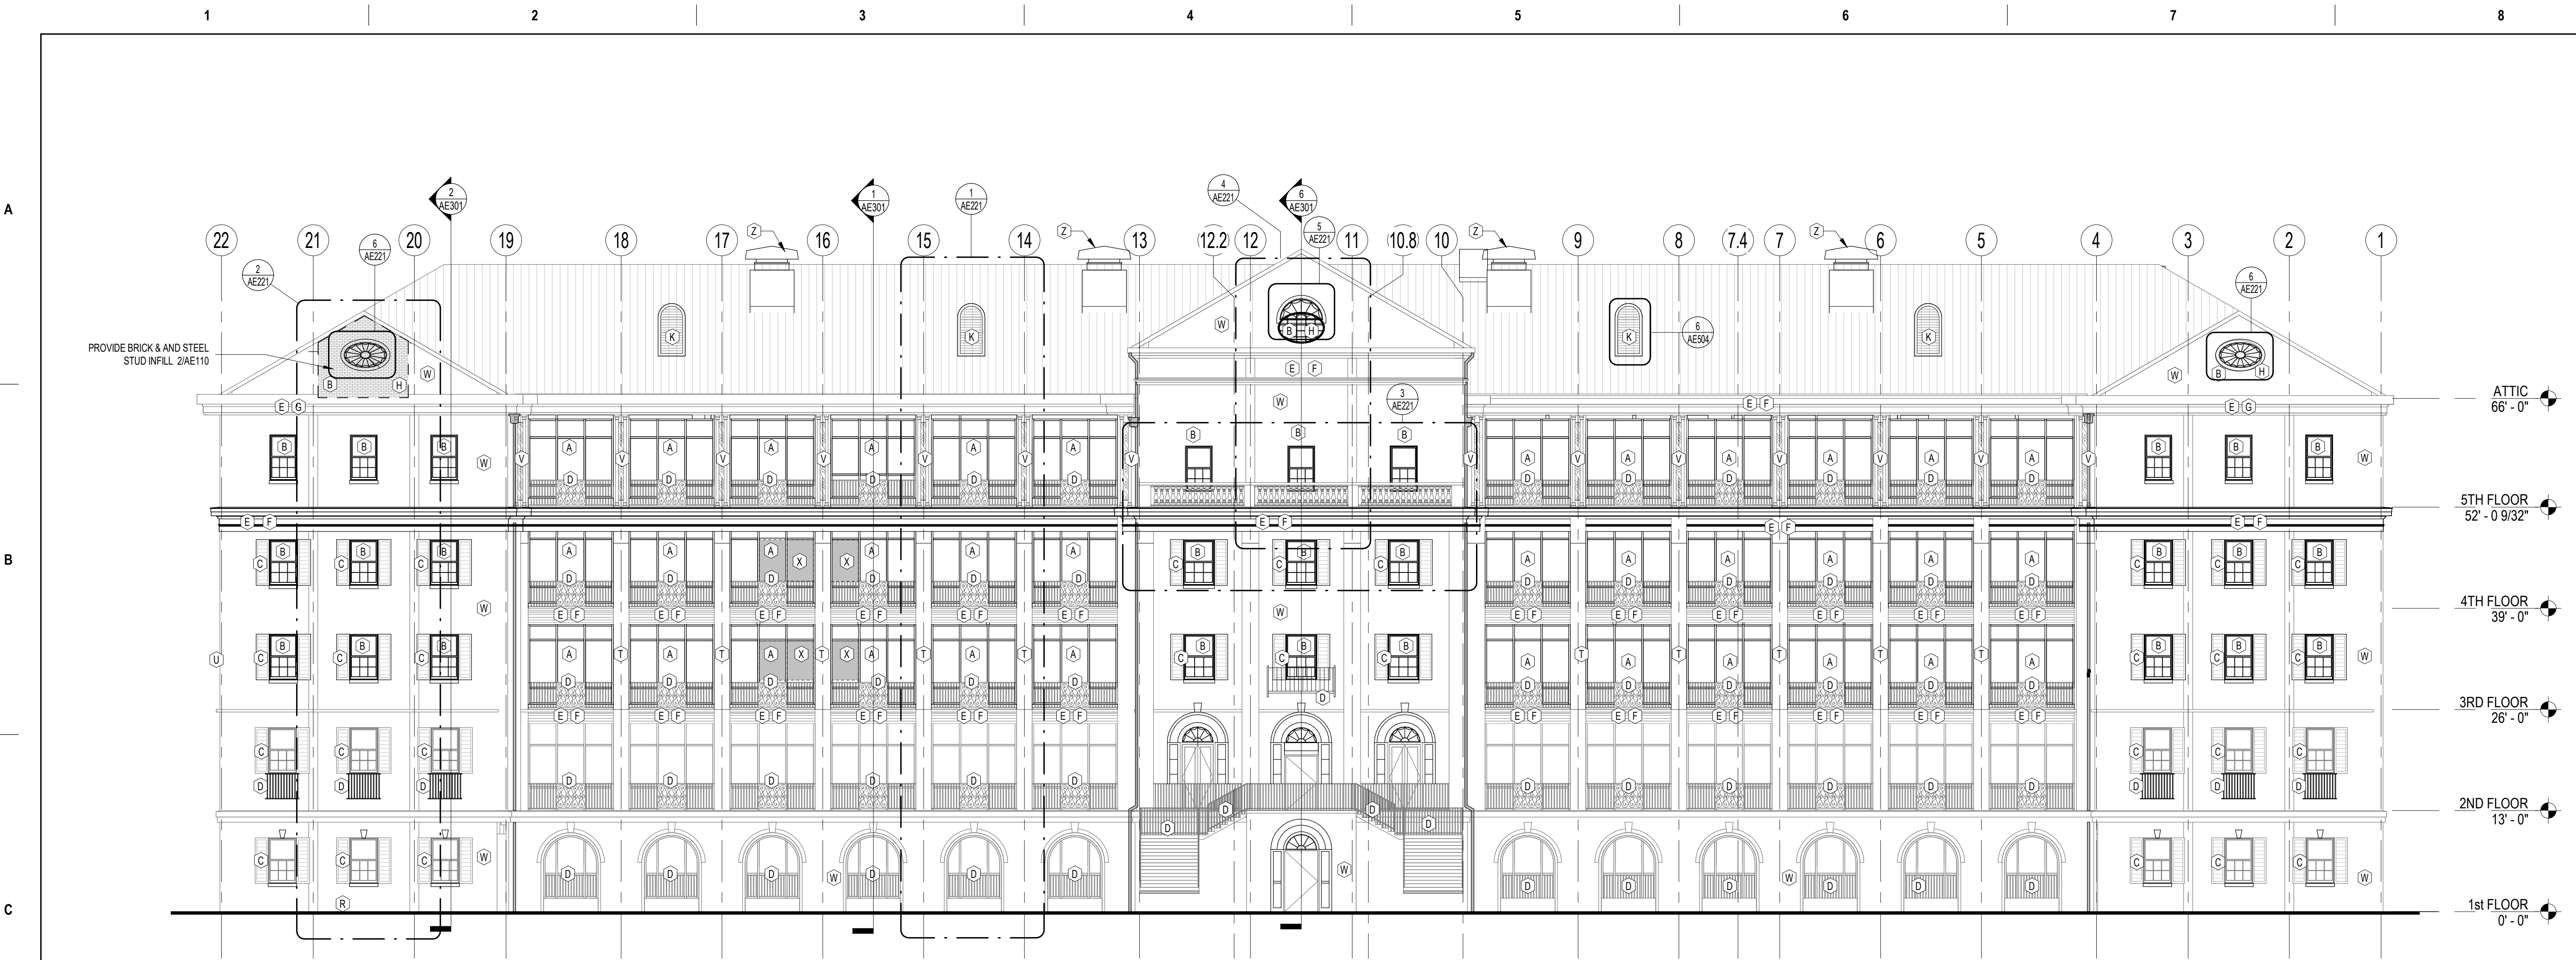

1 NORTH EXTERIOR ELEVATION
3/32" = 1'-0"

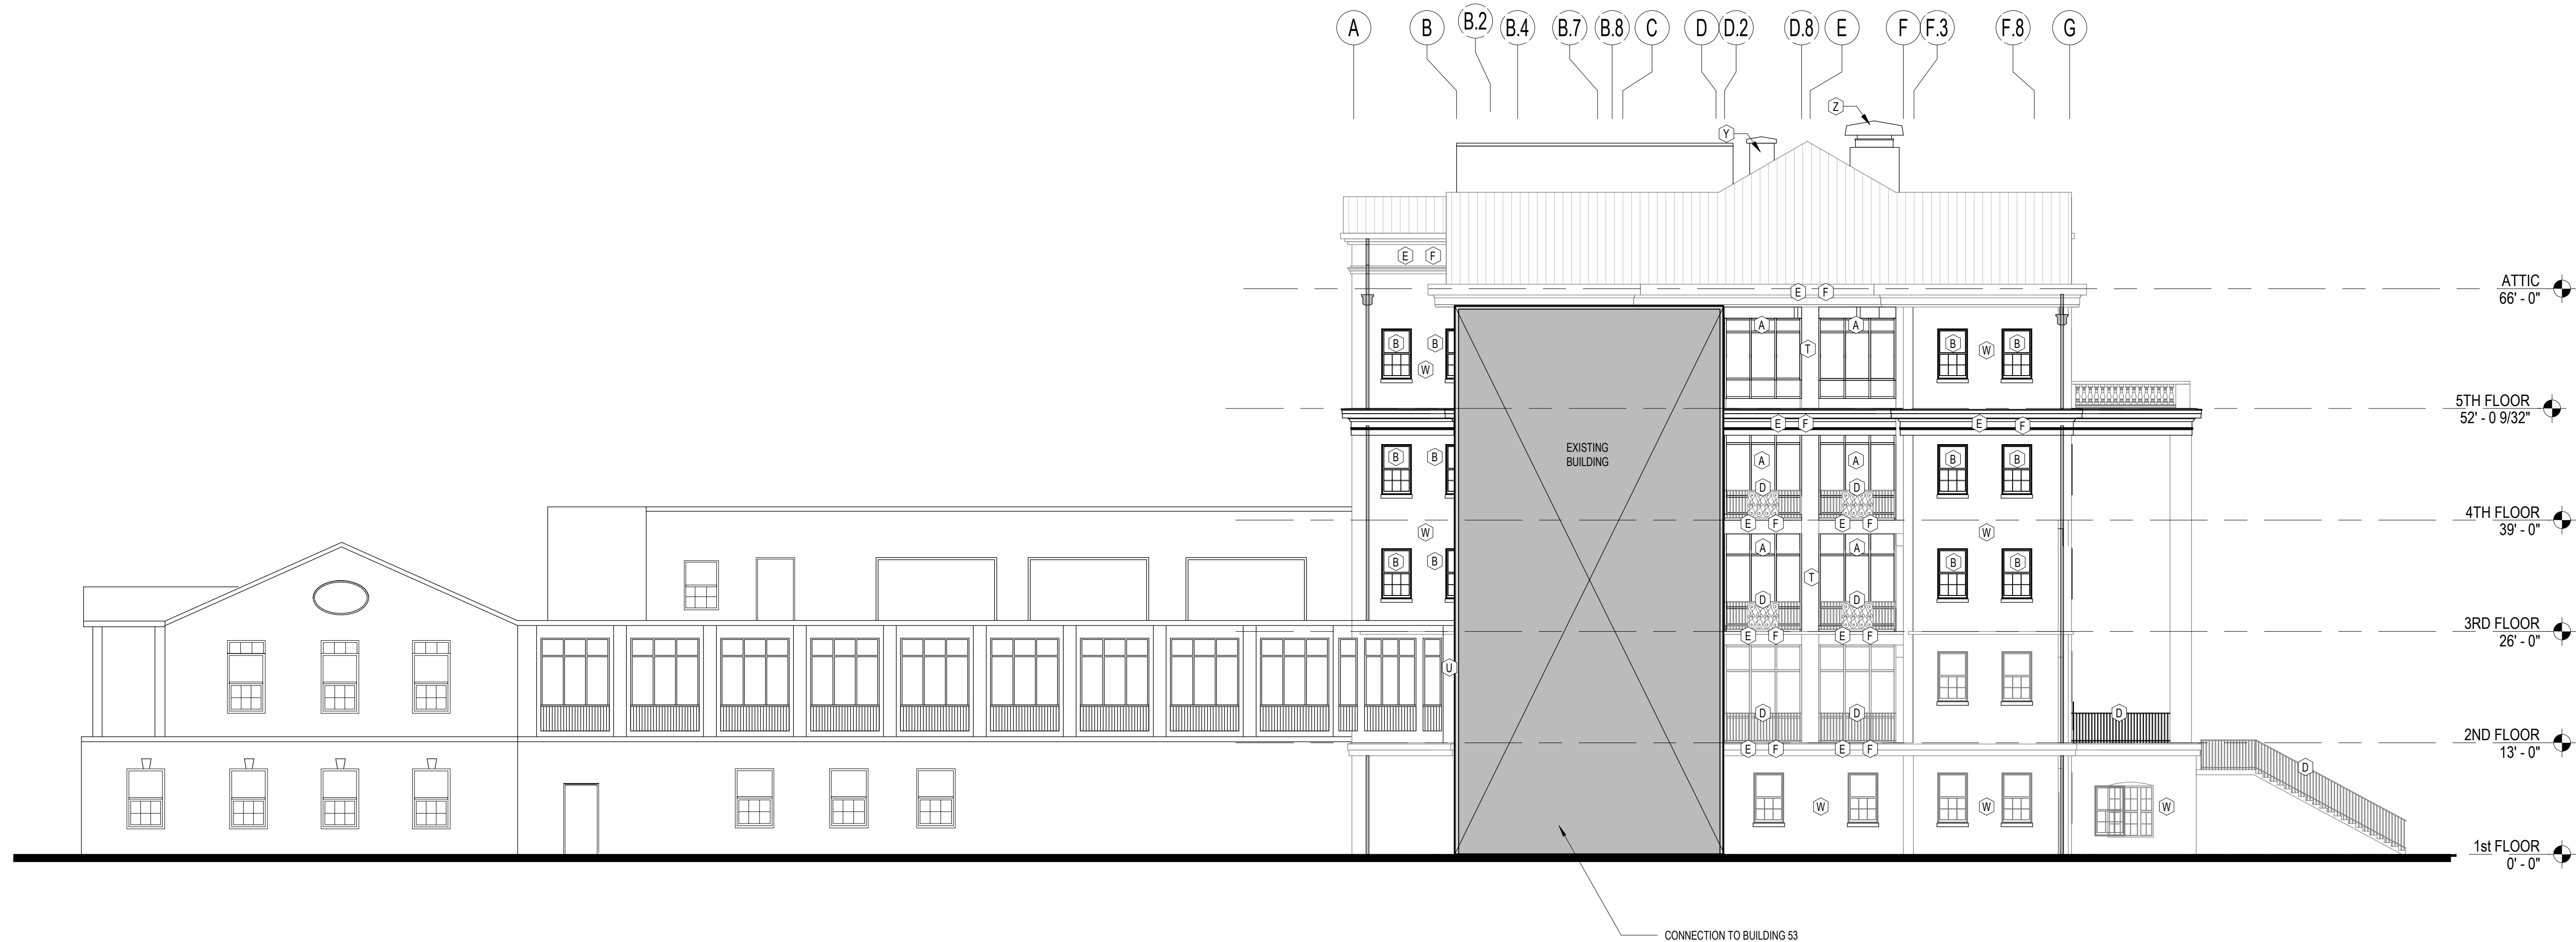

2 EAST EXTERIOR ELEVATION
3/32" = 1'-0"

EXTERIOR ELEVATIONS GENERAL NOTES

- CONTRACTOR IS TO FIELD VERIFY ALL DIMENSIONS AND CONDITIONS
- UPON DISCOVERY OF ANY DISCREPANCIES BETWEEN DRAWINGS DEPICTING EXISTING CONDITIONS OR UPON DISCOVERY OF UNKNOWN CONDITIONS DETRIMENTAL TO THE COMPLETION OF THE WORK AS INDICATED IN THE DOCUMENTS, THE CONTRACTOR SHALL IMMEDIATELY NOTIFY THE ARCHITECT & RESIDENT ENGINEER, IN WRITING, OF THE CONDITION IN QUESTION BEFORE PROCEEDING WITH WORK IN THE AREA.
- CONTRACTOR SHALL MAINTAIN SAFE METHODS OF EGRESS FOR OCCUPIED PORTIONS OF BUILDING AND IN SITE AREA DURING CONSTRUCTION.
- DO NOT SCALE DRAWINGS. IF DIMENSIONS ARE IN QUESTION, THE CONTRACTOR SHALL BE RESPONSIBLE FOR OBTAINING CLARIFICATION FROM THE ARCHITECT & RESIDENT ENGINEER BEFORE CONTINUING WITH THE CONSTRUCTION.
- COORDINATE WORK WITH OTHER PHASES
- COORDINATE SITE LAYOUT / ACCESS / WORK AREAS / LAYDOWN AREAS / PHASING WITH RESIDENT ENGINEER
- SEE SHEETS S402 AND S403 FOR CURTAINWALL / WINDOW OPENING TYPES AND ASSOCIATED WORK
- SEE SHEET ADT01 - ADT05 FOR PHOTOGRAPHS
- ALL MASONRY / STONE IS TO HAVE A WATER RESISTANCE COATING. MORTAR JOINTS ARE TO BE RETOOLLED, AS REQUIRED.
- ALL EIFS SYSTEM TO HAVE WATERPROOF COATING OVER INSULATION BOARD / FOAM SHAPE, BASE COAT AND PRIMER, WHERE REQUIRED
- BACKWRAP EIFS FOAM INSULATION BOARDS / SHAPE PER MANUFACTURER'S RECOMMENDATIONS
- ALL DIFFERING MATERIAL JOINTS TO HAVE BACKER ROD AND SEALANT INSTALLED
- INSTALL NEW GUTTERS AND DOWNSPOUTS. SEE ROOF PLAN ON SHEET AE105 FOR ADDITIONAL WORK NOT SHOWN. PROVIDE CONCRETE SPLASH BLOCKS AT ALL DOWNSPOUT LOCATIONS THAT SPLASH AT GRADE
- REMOVE ALL SIGNAGE IN AREAS OF WORK. PREDRILL HOLES FOR FASTENERS AND FILL WITH SEALANT PRIOR TO INSTALL FASTENER
- REINSTALL ALL ELECTRICAL, COMMUNICATIONS, SECURITY, ACCESS CONTROL, IN EXISTING LOCATIONS. PROVIDE WATERTIGHTNESS AT PENETRATIONS
- COLORS (SUBMIT WATERPROOF COATING, PAINT AND METAL COLORS TO BE APPROVED IN SHOP DRAWINGS PHASE BY ARCHITECT OR RESIDENT ENGINEER - COLORS TO MATCH EXISTING CAMPUS COLOR SCHEME):
 - BRICK (BELOW SECOND FLOOR STONE BANDING TO GRADE 0): LIGHT TAN
 - BRICK & NEW EIFS GABLE (ABOVE SECOND FLOOR STONE BANDING TO ROOF) MEDIUM TAN
 - STONE BANDING, SILL, KEYSTONES, ETC: GRAY
 - EIFS (COLUMN, TRIM, FASCIA, CORNICE, ETC): WHITE
 - STOREFRONT, WINDOW UNITS AND ASSOCIATED FLASHING: WHITE
 - RAILINGS: BLACK
 - ROOF AND ROOF FLASHINGS: COLONIAL RED (MATCH EXISTING)
 - ROOF GUTTERS COLONIAL RED, ROOF DOWNSPOUTS TO MATCH ADJACENT WALL COLOR

ELEVATION LEGEND

- EXISTING TO REMAIN
- - - - - TO BE REMOVED
- (N) KEYNOTE

EXTERIOR ELEVATION KEYNOTES

- (A) NEW ALUMINUM CURTAINWALL INCLUDING FASTENER, BLOCKING, FLASHING, SEALANTS. SEE DETAILS FOR ADDITIONAL INFORMATION. SEE PLANS FOR CURTAINWALL TYPES.
- (B) NEW ALUMINUM WINDOW INCLUDING FASTENERS, BLOCKING, FLASHING, SEALANTS. SEE DETAILS FOR ADDITIONAL INFORMATION. SEE PLANS FOR WINDOW TYPES.
- (C) REINSTALL EXISTING SHUTTERS. PREDRILL HOLES FOR FASTENERS, CLEAN, AND FILL WITH SEALANT PRIOR TO INSTALLING FASTENERS. TYPICAL FOR NORTH ELEVATION.
- (D) REINSTALL REFINISHED RAILINGS. FILL ANY SOCKETS IN STONE WITH EPOXY, REMOVE BOTTOM OF POST IF APPLICABLE AND PROVIDE L-BRACKET TO FASTEN RAIL TO ADJACENT COLUMN.
- (E) INSTALL SILICONE ELASTOMERIC COATING OVER EIFS PILASTERS AND FASCIA. PROVIDE SUPPORTING LIGHT GAGE FRAMING, TRTD WOOD BLOCKING AND FLASHING.
- (F) INSTALL EIFS APPLIED CORNICES, TRIM AND PREFINISHED MITL FLASHING.
- (G) INSTALL EIFS ASSEMBLY. SEE DETAILS FOR EXTENT, ADJUST EXISTING THRU-WALL FLASHING TO COORDINATE WITH NEW WORK.
- (H) INSTALL EIFS APPLIED WINDOW TRIM. SEE WINDOW TYPES FOR ADDITIONAL INFORMATION.
- (J) PAINT EXISTING GUARD RAIL SYSTEM.
- (K) NEW LOUVER AND PREFINISHED MITL ON DORMERS, SEE ROOF PLAN - COORDINATE WITH MECH.
- (L) REINSTALL ACCESS CONTROL SYSTEM. PREDRILL HOLES FOR FASTENERS AND FILL WITH SEALANT TO INSTALLING FASTENERS.
- (M) REINSTALL LIGHT FIXTURE. PRE-DRILL HOLES FOR FASTENERS AND FILL WITH SEALANT PRIOR TO INSTALLING FASTENERS. PROVIDE GASKETS AT CONNECTION TO JUNCTION BOX.
- (N) REINSTALL SECURITY/COMMUNICATIONS FIXTURE FOR REINSTALLATION. PREDRILL HOLES FOR FASTENERS AND FILL WITH SEALANT PRIOR TO INSTALLING FASTENERS. PROVIDE GASKETS AT CONNECTION TO JUNCTION BOX. SEAL ALL HOLES IN MASONRY.
- (P) NOT USED.
- (Q) INSTALL NEW BACKER ROD AND SEALANT ALL AROUND EXISTING LOUVER.
- (R) INSTALL APPLIED GRATE OVER EXISTING FOUNDATION VENT HOLES. RECONNECT UTILITIES AS REQUIRED.
- (S) CLEAN EXISTING DOOR FINISHES. INSTALL NEW SEALANT AND BACKER RODS ALL AROUND. INSTALL GASKETS ALL AROUND.
- (T) INSTALL WATERPROOFING SILICONE ELASTOMERIC COATING OVER EIFS PILASTERS AND FASCIA. PROVIDE SUPPORTING LIGHT GAGE FRAMING, TRTD WOOD BLOCKING AND FLASHING.
- (U) INSTALL NEW ALUMINUM EXPANSION JOINT ASSEMBLY AND COVER AT CONNECTIONS BETWEEN BUILDING 1 AND BUILDING 53 AT NORTH AND SOUTH ELEVATIONS. REFER TO SPEC SECTION 07 95 13 (EXPANSION JOINT COVER ASSEMBLY) FOR ADDITIONAL INFORMATION.
- (V) REPAIR METAL COLUMNS AT 5TH FLOOR FACADE. SANDBLAST, REWELDED BASES, AND REPAINT AT ALL COLUMNS.
- (W) PROVIDE MORTAR JOINT REPAIR/REPLACEMENT TO EXISTING BRICK. PAINT EXISTING MASONRY/BRICK AND INSTALL SILICONE ELASTOMERIC COATING.
- (X) APPLY UV FILM AT INTERIOR OF THIS WINDOW. REFER TO SPEC SECTION 06 80 10 (GLAZING) FOR ADDITIONAL INFORMATION.
- (Y) EXISTING MECHANICAL EXHAUST.
- (Z) MECHANICAL EXHAUST.
- (Z-1) REBUILD OUTER WYTHE OF BRICK FROM SALVAGE BRICK.

BID DOCUMENTS

NO.	REVISIONS	DATE

CONSULTANT

ARCHITECT/ENGINEER OF RECORD

THOMAS OLESAC, ARCHITECT
MS Lic # 5505

1050 HOYT AVE WEST ST PAUL, MN 55117
952-451-0460

STAMP



Office of
Construction
and Facilities
Management

VA

U.S. Department
of Veterans
Affairs

Drawing Title

EXTERIOR ELEVATIONS

Approved:

Phase

CONSTRUCTION
DOCUMENTS

FULLY SPRINKLERED

Project Title

RENOVATE BUILDING 1

Location

BILOXI, MISSISSIPPI

Issue Date

03/10/2023

Checked

LA

Drawn

CD,PC

Project Number

520-317X

Building Number

1

Drawing Number

AE202

Dwg. 84 of 238

GENERAL REFLECTED CEILING PLAN NOTES

- A. ALL FINISH CEILING HEIGHTS TO BE INSTALLED AT 8'-0" A.F.F. UNLESS OTHERWISE NOTED.
- B. MECHANICAL AND ELECTRICAL DEVICES SHOWN ARE FOR INDICATION OF THEIR RESPECTIVE LOCATION ONLY. NOT ALL SUCH DEVICES ARE SHOWN BY THIS PLAN. MECHANICAL AND ELECTRICAL DEVICES TYPE, SIZE AND OTHER REQUIREMENTS ARE DOCUMENTED BY THE CORRESPONDING M.E.P. PLAN, DETAIL AND/OR SPECIFICATION SECTION.
- C. REFER TO SPECIFICATION SECTION 07 21 13 FOR ACOUSTICAL CEILING BATT INSULATION.
- D. REFER TO SPECIFICATION SECTION 09 29 00 FOR GYPSUM BOARD CEILING SYSTEM.
- E. REFER TO SPECIFICATION SECTION 09 51 00 FOR ACOUSTICAL CEILING SYSTEM.
- F. COORDINATE FIRE PROTECTION SYSTEM TO PROVIDE NEW SPRINKLER HEADS AT THE CENTER POINT OF CEILING TILES SHOWN.
- G. REFER TO PHASING PLAN AND SPECIFICATION SECTION 01 00 00 GENERAL REQUIREMENTS FOR PHASING REQUIREMENTS OF WORK SHOWN.
- H. REFER TO SPECIFICATION SECTION 01 35 26 FOR INFECTION CONTROL REQUIREMENTS FOR WORK SHOWN.
- I. ROOM TAGS REMOVED FOR CLARITY. REFER TO SHEETS AE103 & AE105 FOR ROOM NAMES.


REFLECTED CEILING PLAN NOTES (#)

1. NO NEW CEILING IN THIS AREA.
2. FULL CEILING TILE.
3. SINGLE TRACK BARIATRIC PATIENT LIFT SYSTEM. REFER TO EQUIPMENT LEGEND, SHT. AE305 AND SPECIFICATION SECTION 11 73 00.
4. BOOM LIGHT/MEDICAL GAS ARM. REFER TO MECHANICAL.


REFLECTED CEILING PLAN LEGEND

- 2' X 4' ACOUSTICAL TILE CEILING
- 2' X 2' ACOUSTICAL TILE CEILING
- 2' X 2' FLUORESCENT LIGHT
- 2' X 4' FLUORESCENT LIGHT
- RECESSED CAN LIGHT
- 1' X 4' STRIP LIGHT
- AREA NOT IN CONTRACT
- HVAC RETURN
- HVAC SUPPLY
- EXHAUST
- CURTAIN TRACK
- SHOWER CURTAIN
- GYPSUM BOARD CEILING ON METAL FRAMING
- RADIANT HEAT PANEL

NOTE: ALL SYMBOLS MAY NOT BE USED

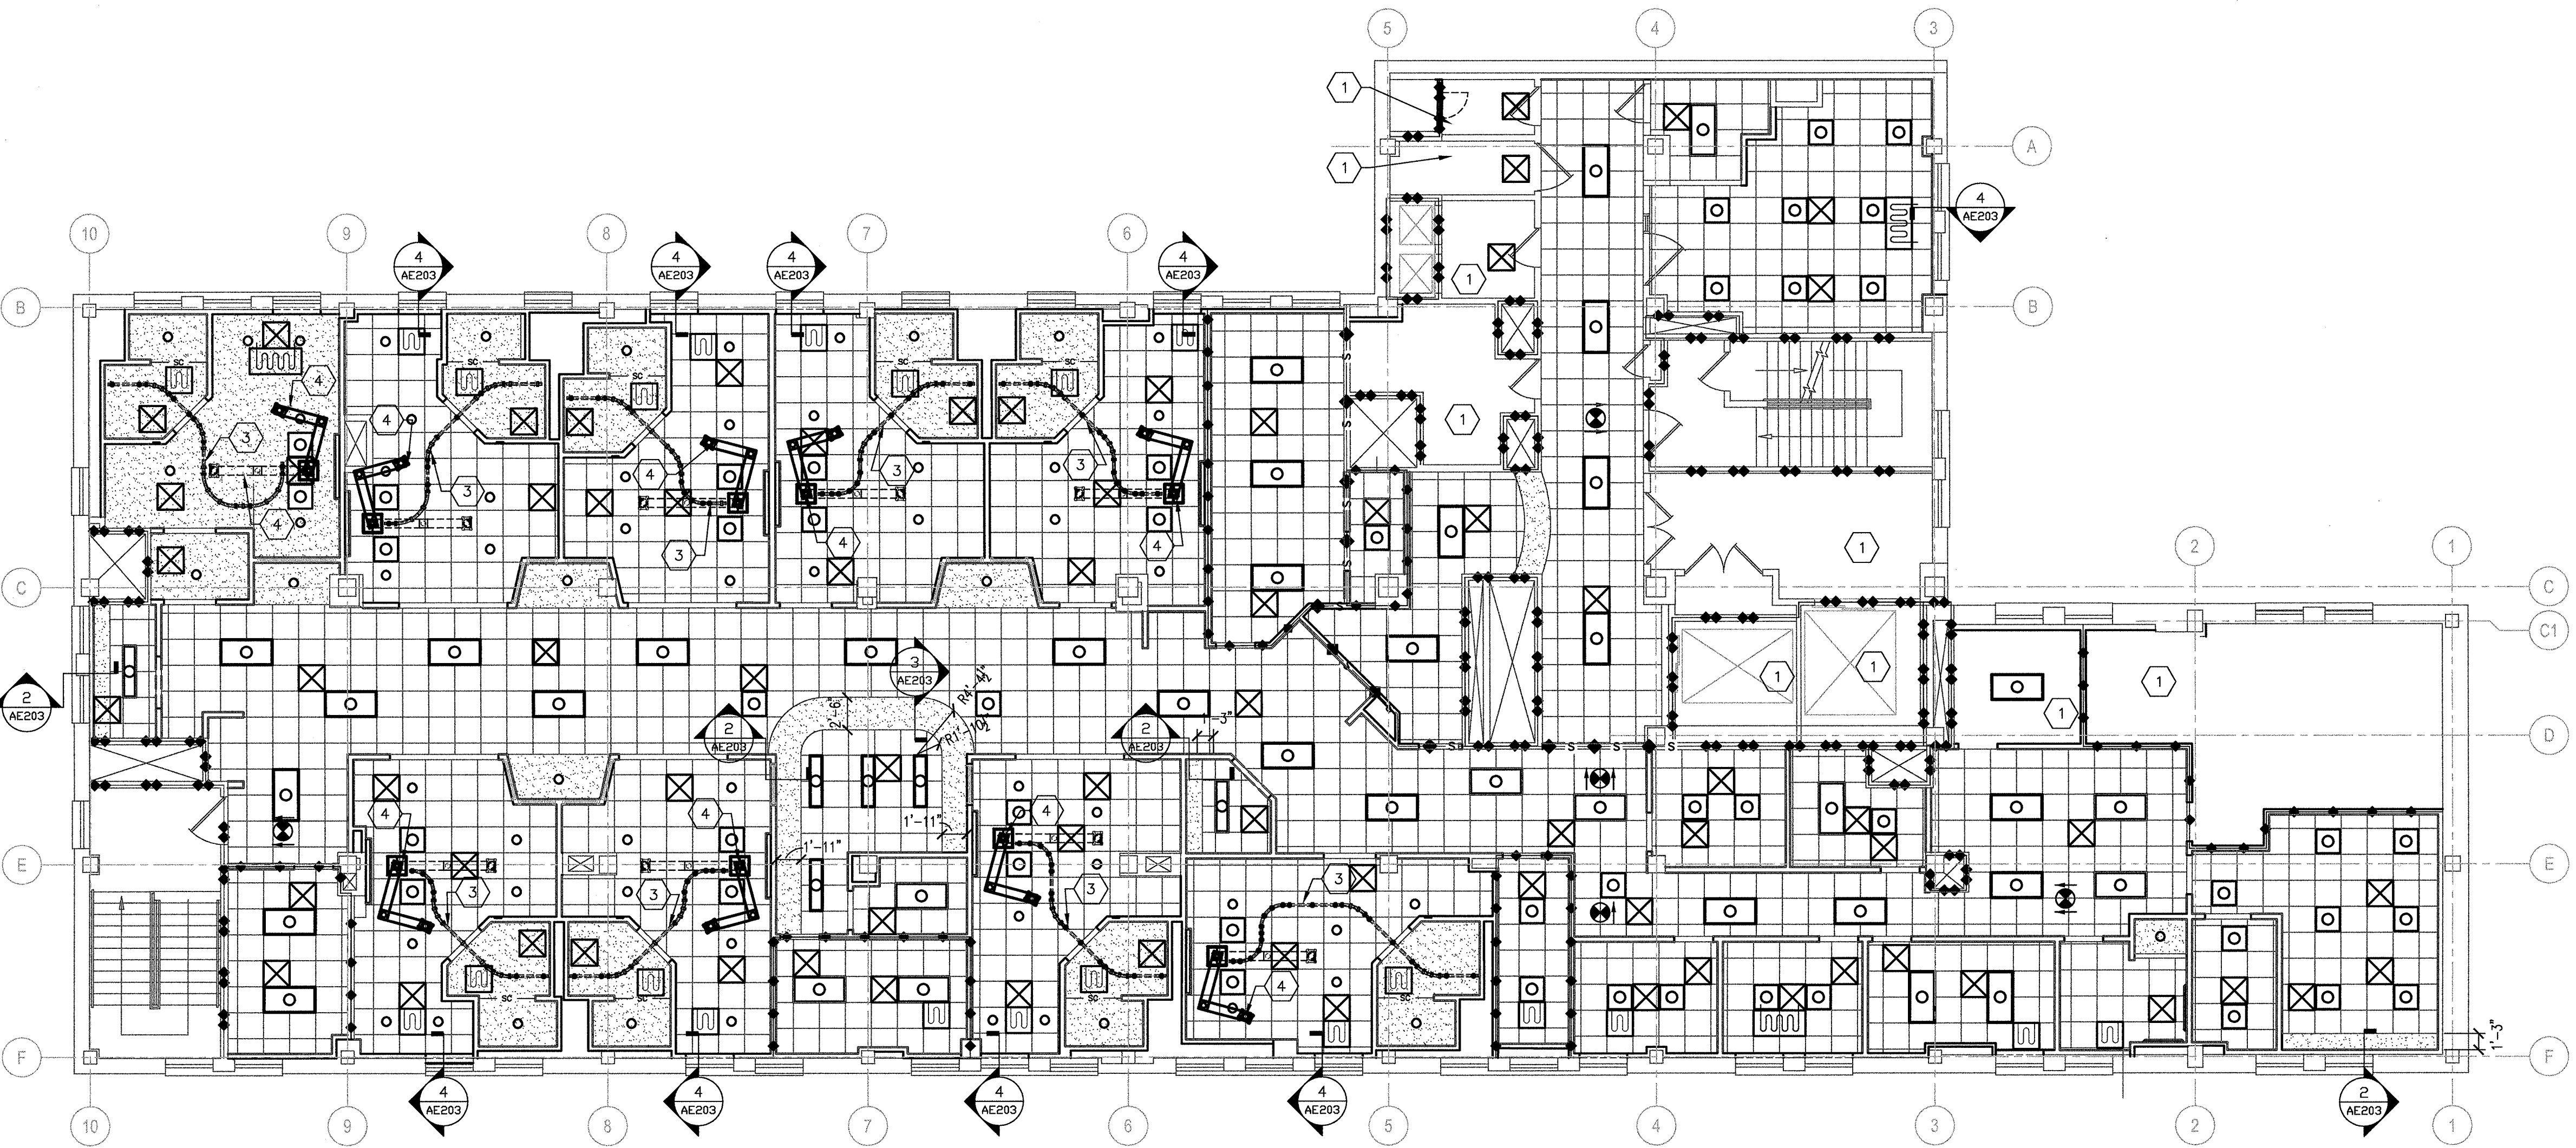


F1 FIFTH FLOOR REFLECTED CEILING PLAN
SCALE 1/8" = 1'-0"

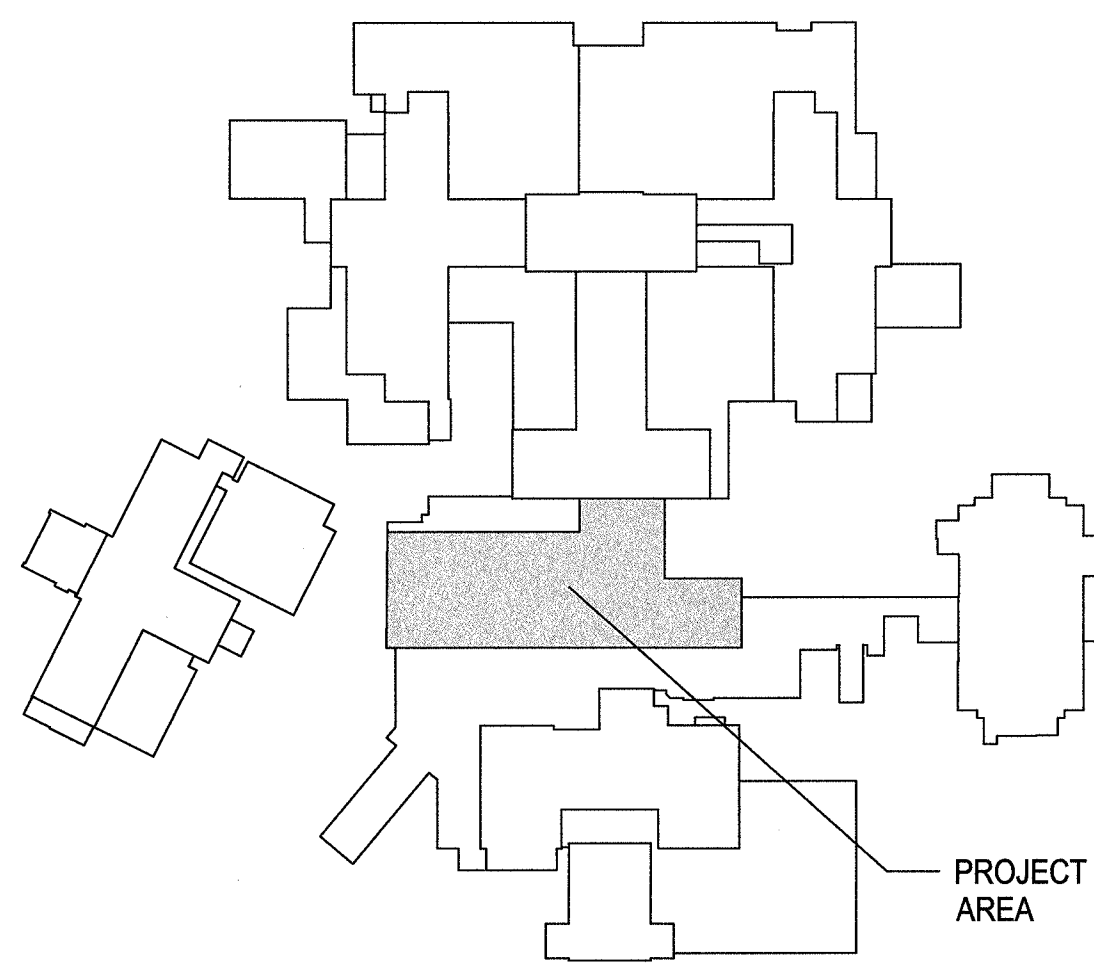

KEY PLAN - FIFTH FLOOR
NTS

FULLY SPRINKLED

--	--	

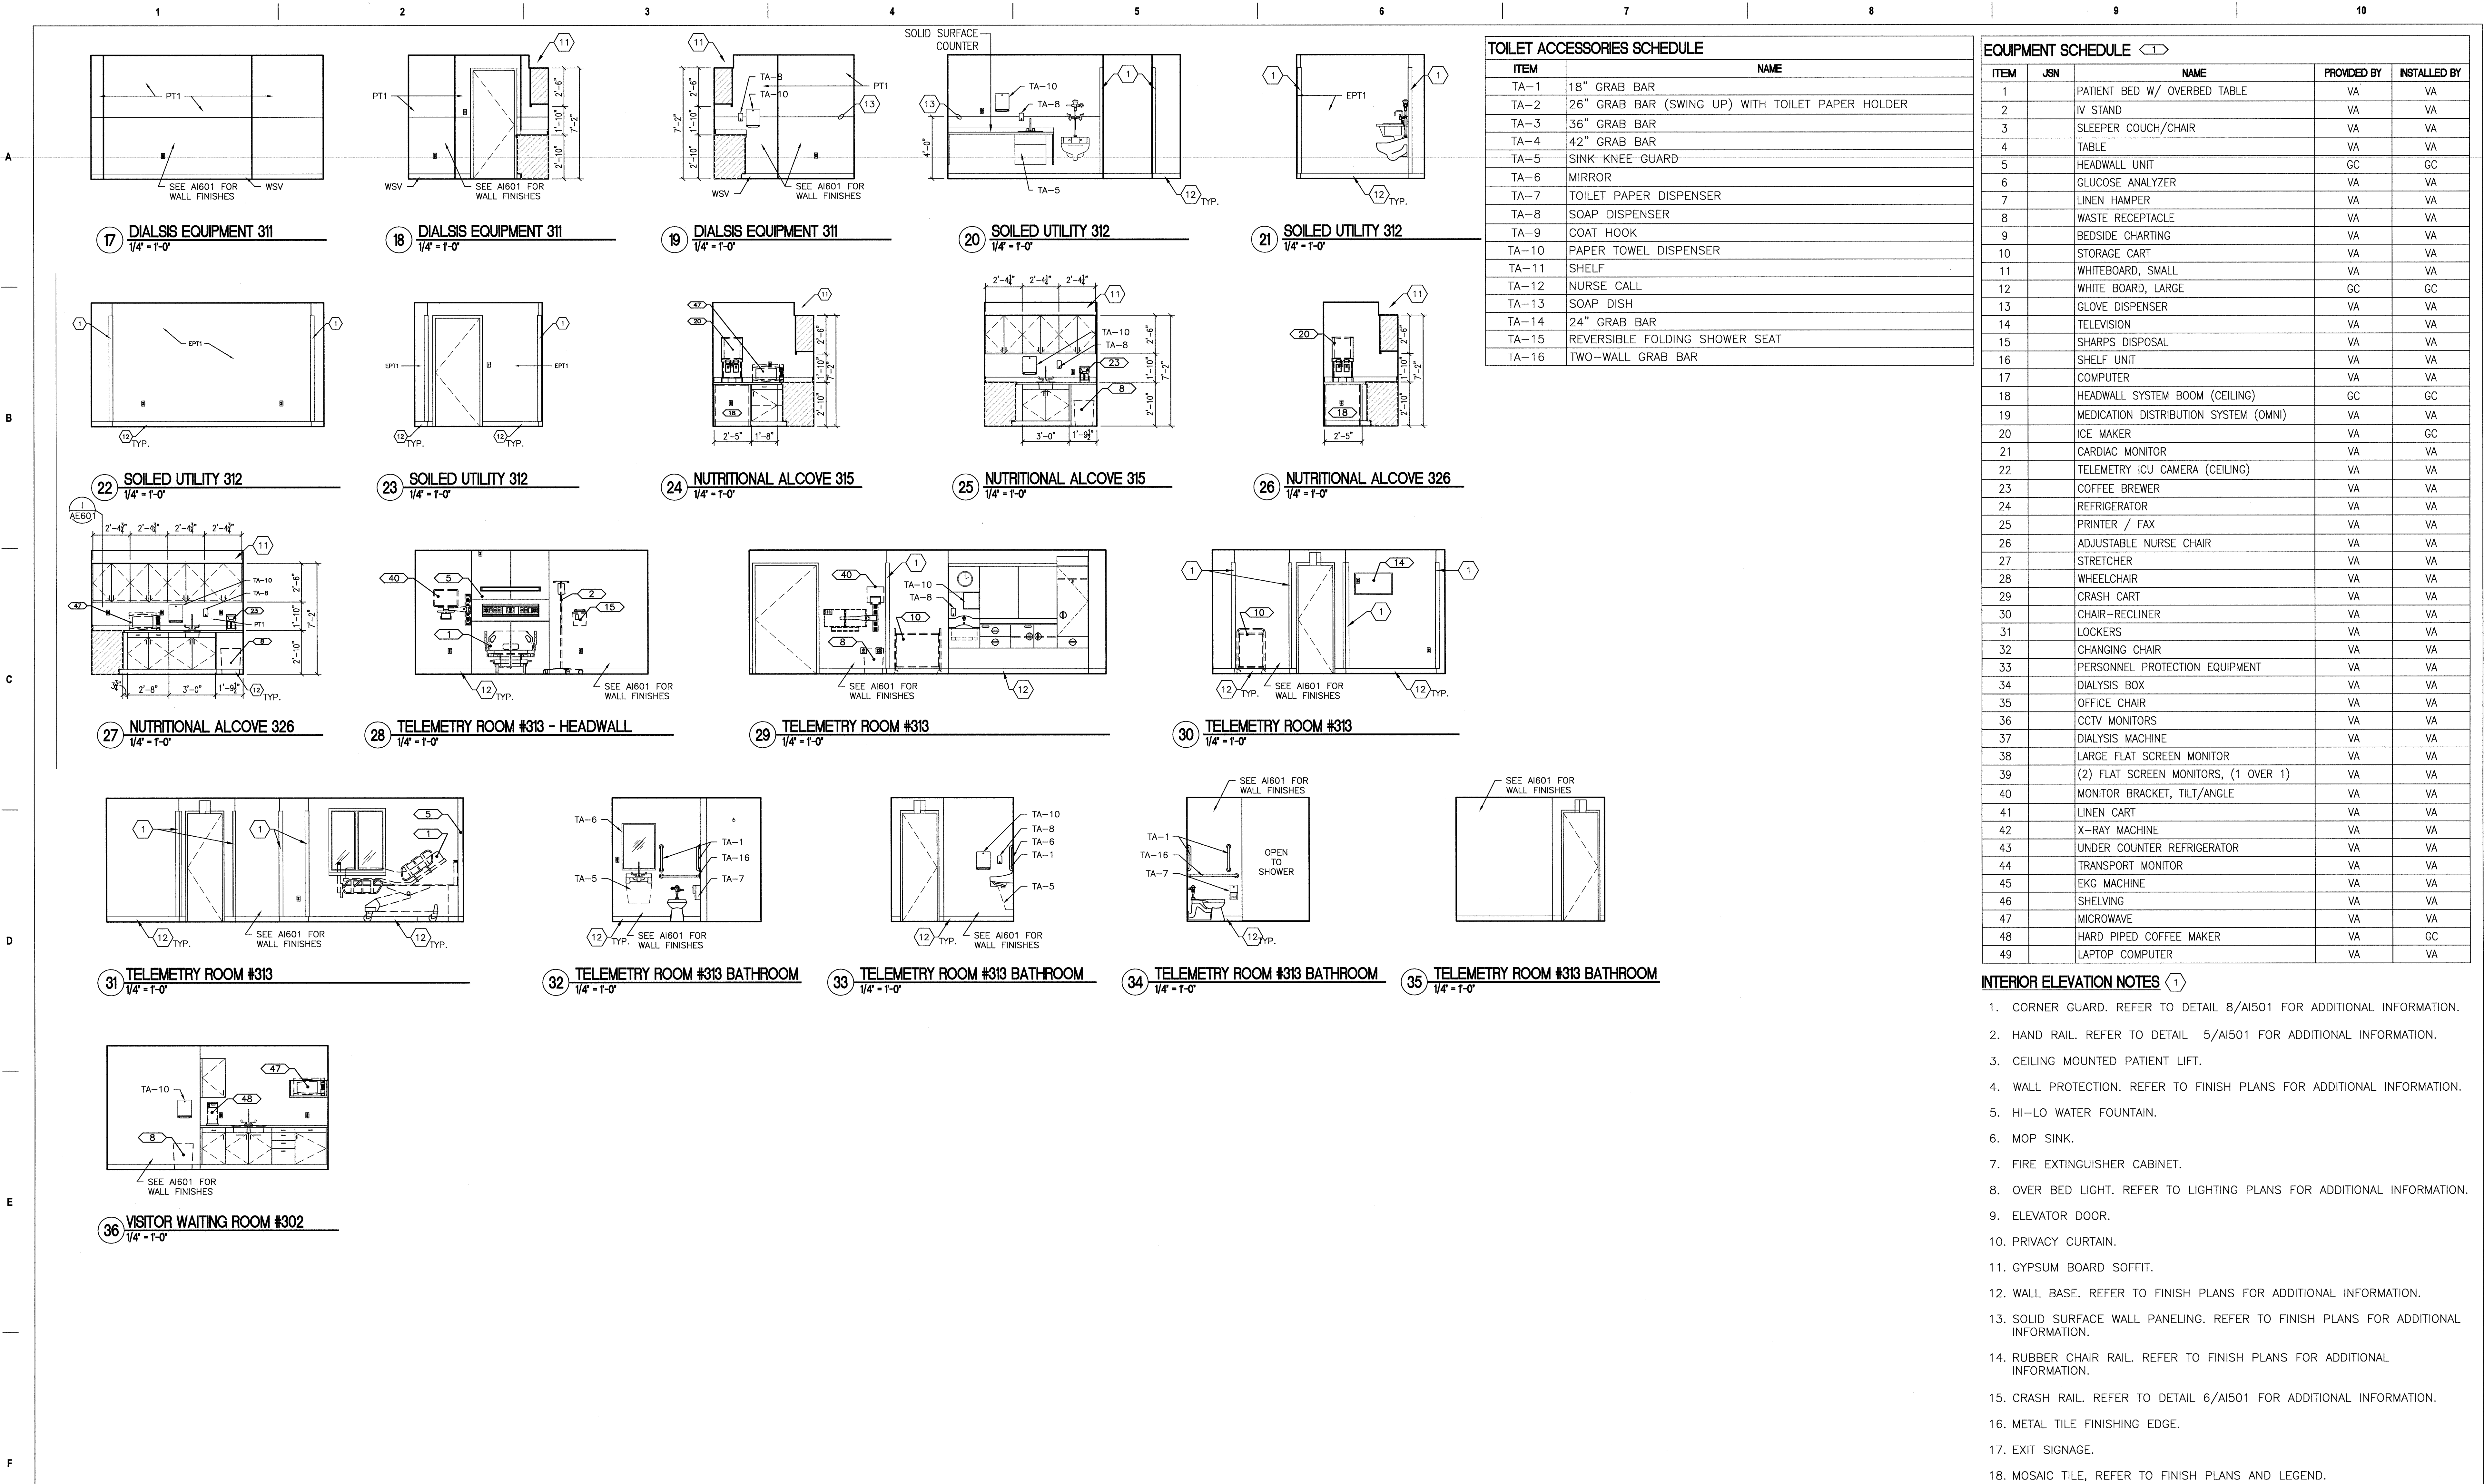

TOILET ACCESSORIES SCHEDULE	
ITEM	NAME
TA-1	18" GRAB BAR
TA-2	26" GRAB BAR (SWING UP) WITH TOILET PAPER HOLDER
TA-3	36" GRAB BAR
TA-4	42" GRAB BAR
TA-5	SINK KNEE GUARD
TA-6	MIRROR
TA-7	TOILET PAPER DISPENSER
TA-8	SOAP DISPENSER
TA-9	COAT HOOK
TA-10	PAPER TOWEL DISPENSER
TA-11	SHELF
TA-12	NURSE CALL
TA-13	SOAP DISH
TA-14	24" GRAB BAR
TA-15	REVERSIBLE FOLDING SHOWER SEAT
TA-16	TWO-WALL GRAB BAR

EQUIPMENT SCHEDULE				
ITEM	JSN	NAME	PROVIDED BY	INSTALLED BY
1		PATIENT BED W/ OVERBED TABLE	VA	VA
2		IV STAND	VA	VA
3		SLEEPER COUCH/CHAIR	VA	VA
4		TABLE	VA	VA
5		HEADWALL UNIT	GC	GC
6		GLUCOSE ANALYZER	VA	VA
7		LINEN HAMPER	VA	VA
8		WASTE RECEPTACLE	VA	VA
9		BEDSIDE CHARTING	VA	VA
10		STORAGE CART	VA	VA
11		WHITEBOARD, SMALL	VA	VA
12		WHITE BOARD, LARGE	GC	GC
13		GLOVE DISPENSER	VA	VA
14		TELEVISION	VA	VA
15		SHARPS DISPOSAL	VA	VA
16		SHELF UNIT	VA	VA
17		COMPUTER	VA	VA
18		HEADWALL SYSTEM BOOM (CEILING)	GC	GC
19		MEDICATION DISTRIBUTION SYSTEM (OMNI)	VA	VA
20		ICE MAKER	VA	GC
21		CARDIAC MONITOR	VA	VA
22		TELEMETRY ICU CAMERA (CEILING)	VA	VA
23		COFFEE BREWER	VA	VA
24		REFRIGERATOR	VA	VA
25		PRINTER / FAX	VA	VA
26		ADJUSTABLE NURSE CHAIR	VA	VA
27		STRETCHER	VA	VA
28		WHEELCHAIR	VA	VA
29		CRASH CART	VA	VA
30		CHAIR-RECLINER	VA	VA
31		LOCKERS	VA	VA
32		CHANGING CHAIR	VA	VA
33		PERSONNEL PROTECTION EQUIPMENT	VA	VA
34		DIALYSIS BOX	VA	VA
35		OFFICE CHAIR	VA	VA
36		CCTV MONITORS	VA	VA
37		DIALYSIS MACHINE	VA	VA
38		LARGE FLAT SCREEN MONITOR	VA	VA
39		(2) FLAT SCREEN MONITORS, (1 OVER 1)	VA	VA
40		MONITOR BRACKET, TILT/ANGLE	VA	VA
41		LINEN CART	VA	VA
42		X-RAY MACHINE	VA	VA
43		UNDER COUNTER REFRIGERATOR	VA	VA
44		TRANSPORT MONITOR	VA	VA
45		EKG MACHINE	VA	VA
46		SHELVING	VA	VA
47		MICROWAVE	VA	VA
48		HARD PIPED COFFEE MAKER	VA	GC
49		LAPTOP COMPUTER	VA	VA

- INTERIOR ELEVATION NOTES**
- CORNER GUARD. REFER TO DETAIL 8/AI501 FOR ADDITIONAL INFORMATION.
 - HAND RAIL. REFER TO DETAIL 5/AI501 FOR ADDITIONAL INFORMATION.
 - CEILING MOUNTED PATIENT LIFT.
 - WALL PROTECTION. REFER TO FINISH PLANS FOR ADDITIONAL INFORMATION.
 - HI-LO WATER FOUNTAIN.
 - MOP SINK.
 - FIRE EXTINGUISHER CABINET.
 - OVER BED LIGHT. REFER TO LIGHTING PLANS FOR ADDITIONAL INFORMATION.
 - ELEVATOR DOOR.
 - PRIVACY CURTAIN.
 - GYPSUM BOARD SOFFIT.
 - WALL BASE. REFER TO FINISH PLANS FOR ADDITIONAL INFORMATION.
 - SOLID SURFACE WALL PANELING. REFER TO FINISH PLANS FOR ADDITIONAL INFORMATION.
 - RUBBER CHAIR RAIL. REFER TO FINISH PLANS FOR ADDITIONAL INFORMATION.
 - CRASH RAIL. REFER TO DETAIL 6/AI501 FOR ADDITIONAL INFORMATION.
 - METAL TILE FINISHING EDGE.
 - EXIT SIGNAGE.
 - MOSAIC TILE, REFER TO FINISH PLANS AND LEGEND.

Revisions:

Date:

CONSULTANT

ARCHITECT/ENGINEER OF RECORD

paradigm

Architecture | Engineering | Design-Build

200 Envoy Circle, Suite 201, Louisville, KY 40299

www.paradigmusa.com

STAMP

6 Dec 2019

BLAINE CAMIEL
VAN GANSBEKE
ENGINEER
NO. 0201056550
PROFESSIONAL SEAL

Office of Construction and Facilities Management

VA U.S. Department of Veterans Affairs

Drawing Title

INTERIOR ELEVATIONS

Approved: Project Director

Phase

ISSUED FOR CONSTRUCTION

FULLY SPRINKLERED

Project Title

REMODEL ICU -TELEMETRY FOR PATIENT PRIVACY

Location VA MEDICAL CENTER
3800 30TH ST, DES MOINES, IOWA 50309

Issue Date 12-06-2019

Checked BW

Drawn TLC

Project Number


636A6-18-313

Building Number


1W

Drawing Number

AE502

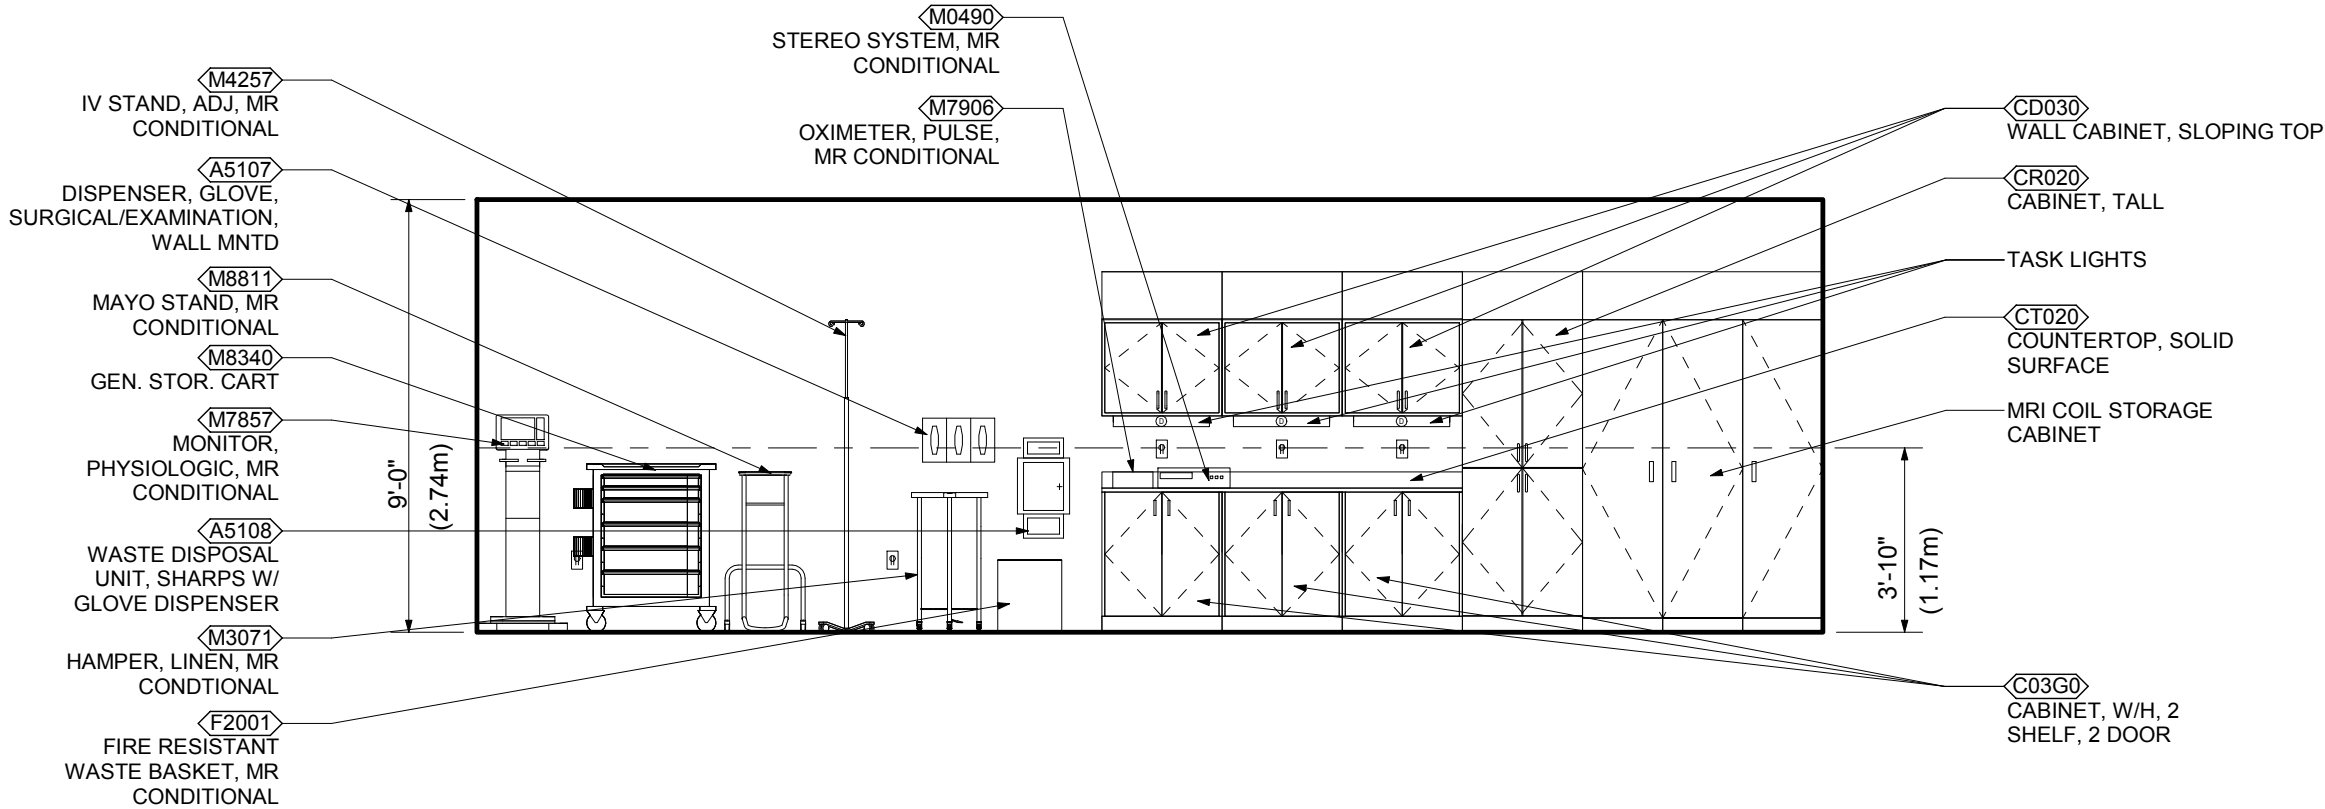


ELEVATION 1

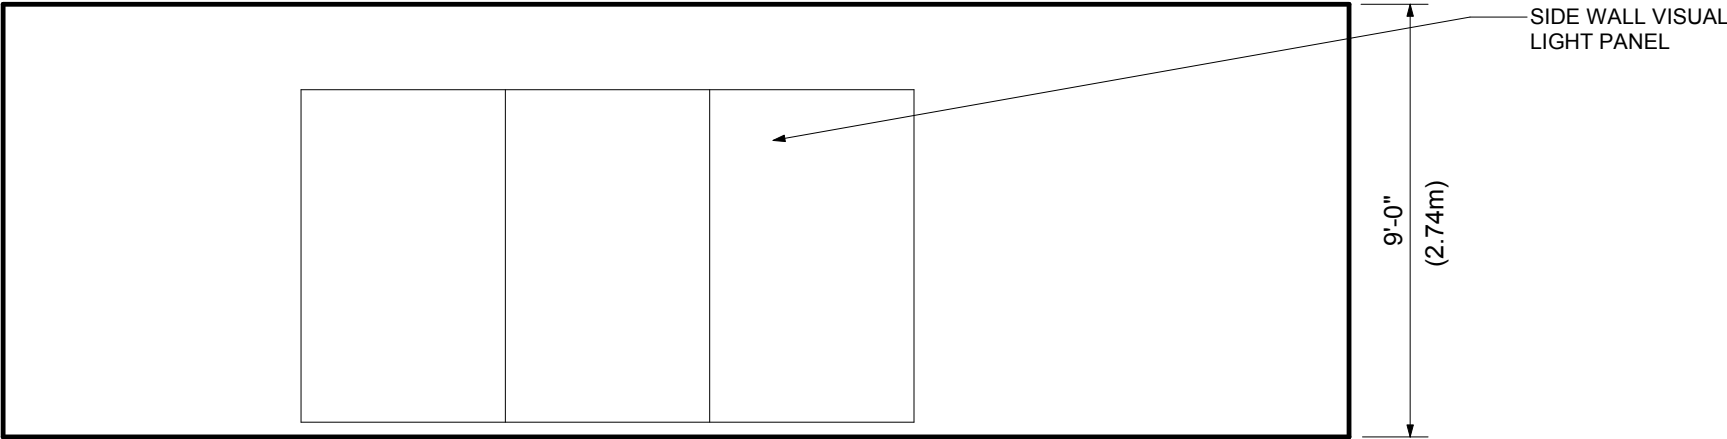


ELEVATION 2


SYMBOL	NO. OF X-RAY	LOCATION OF X-RAY UNITS
A	1	ROOM 112B
B	1	ROOM 114B
C	1	ROOM 109B + ROOM 110B
D	1	ROOM 119B + ROOM 120B
E	1	ROOM 126B + ROOM 127B
F	1	ROOM 128B
H	1	ROOM 132B + ROOM 133B
G	1	ROOM 134B

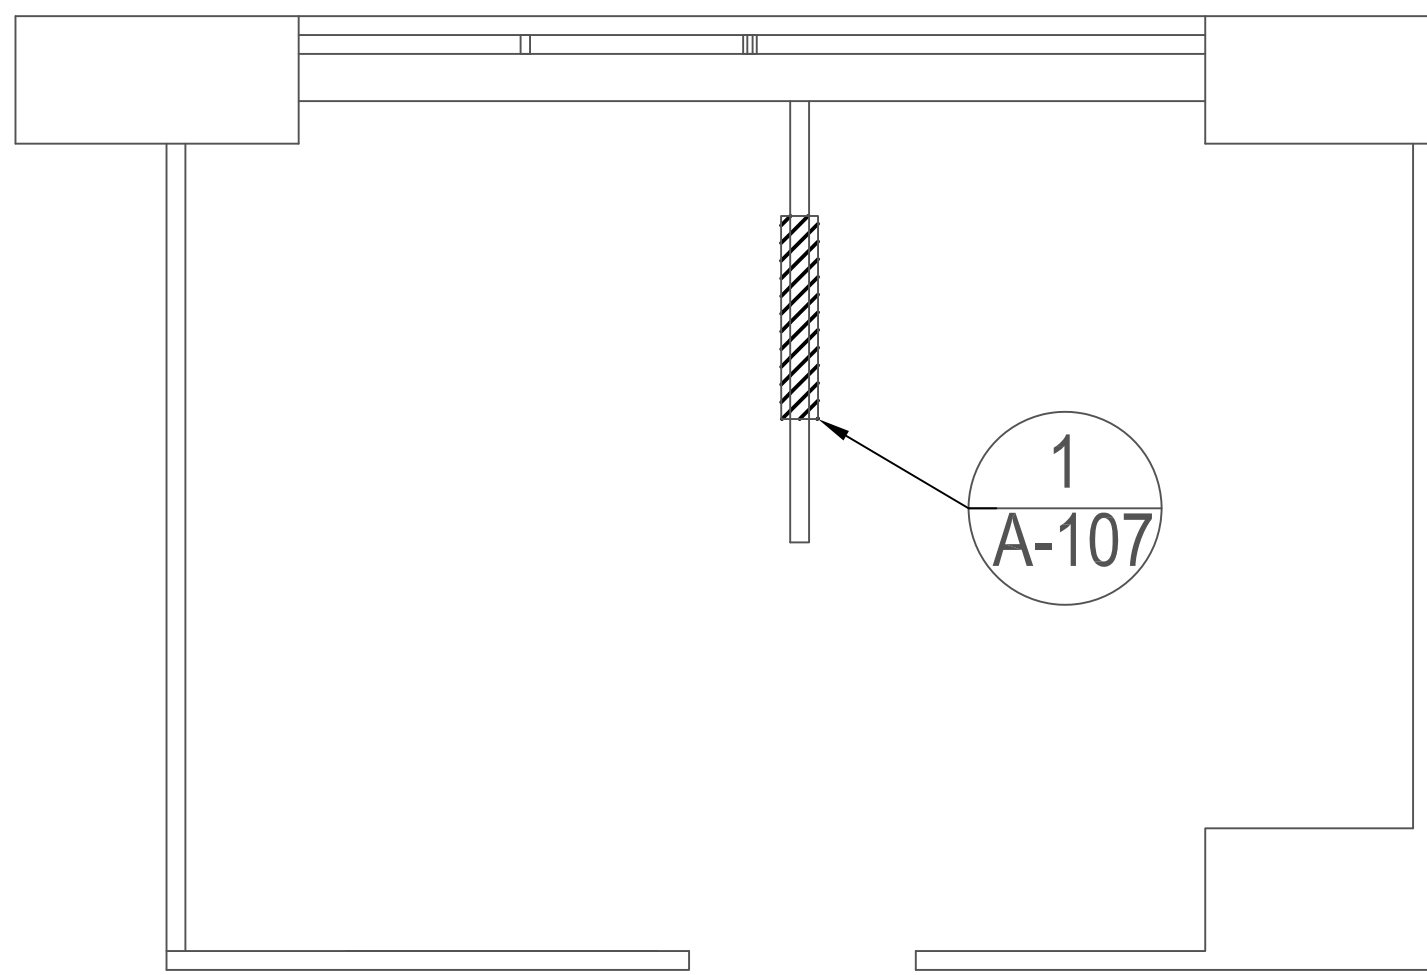


C 109-B, 110-B

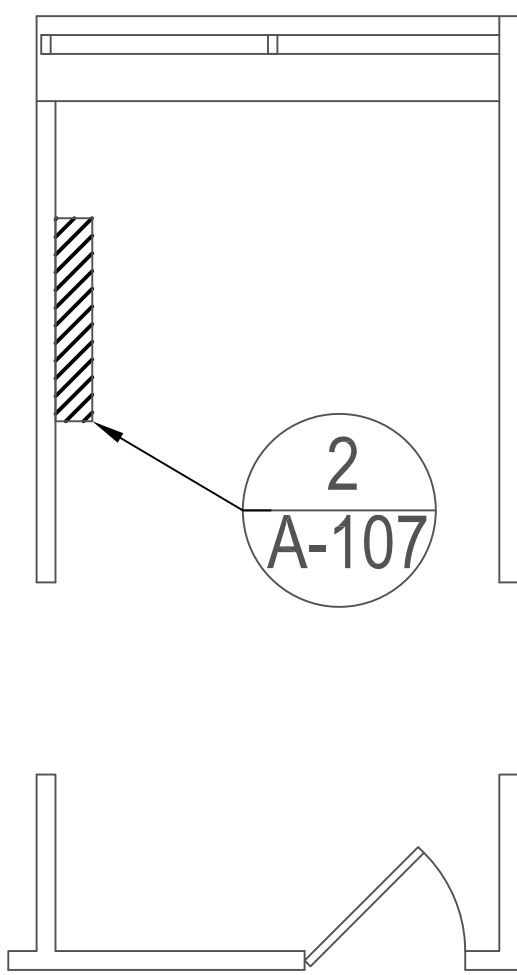


A 112-B

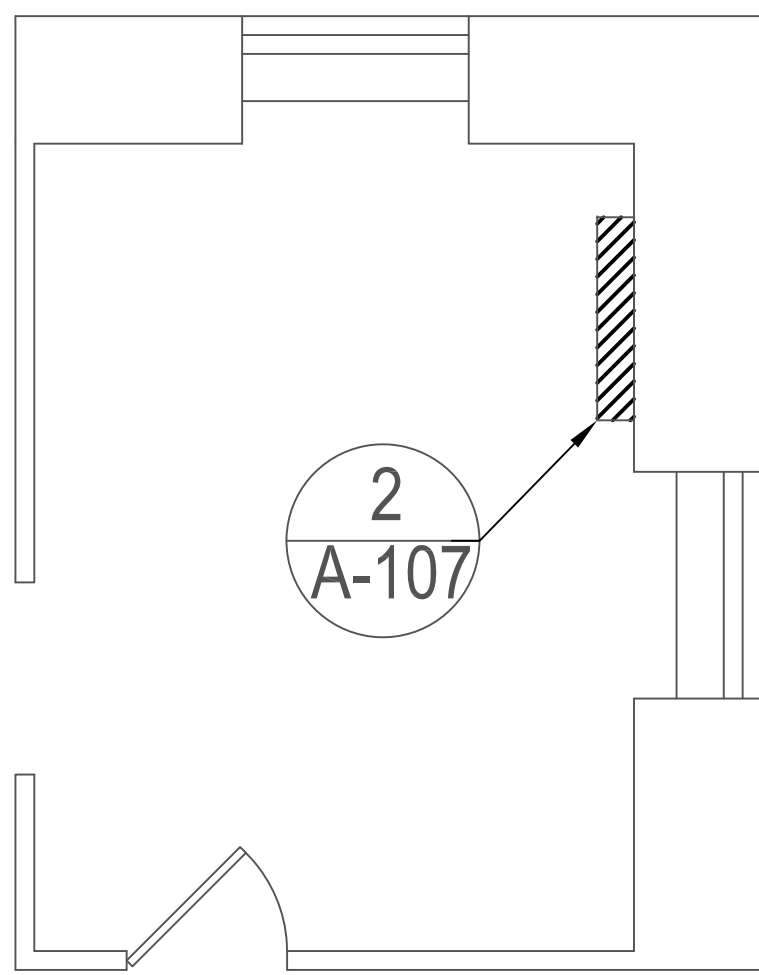


B 114-B

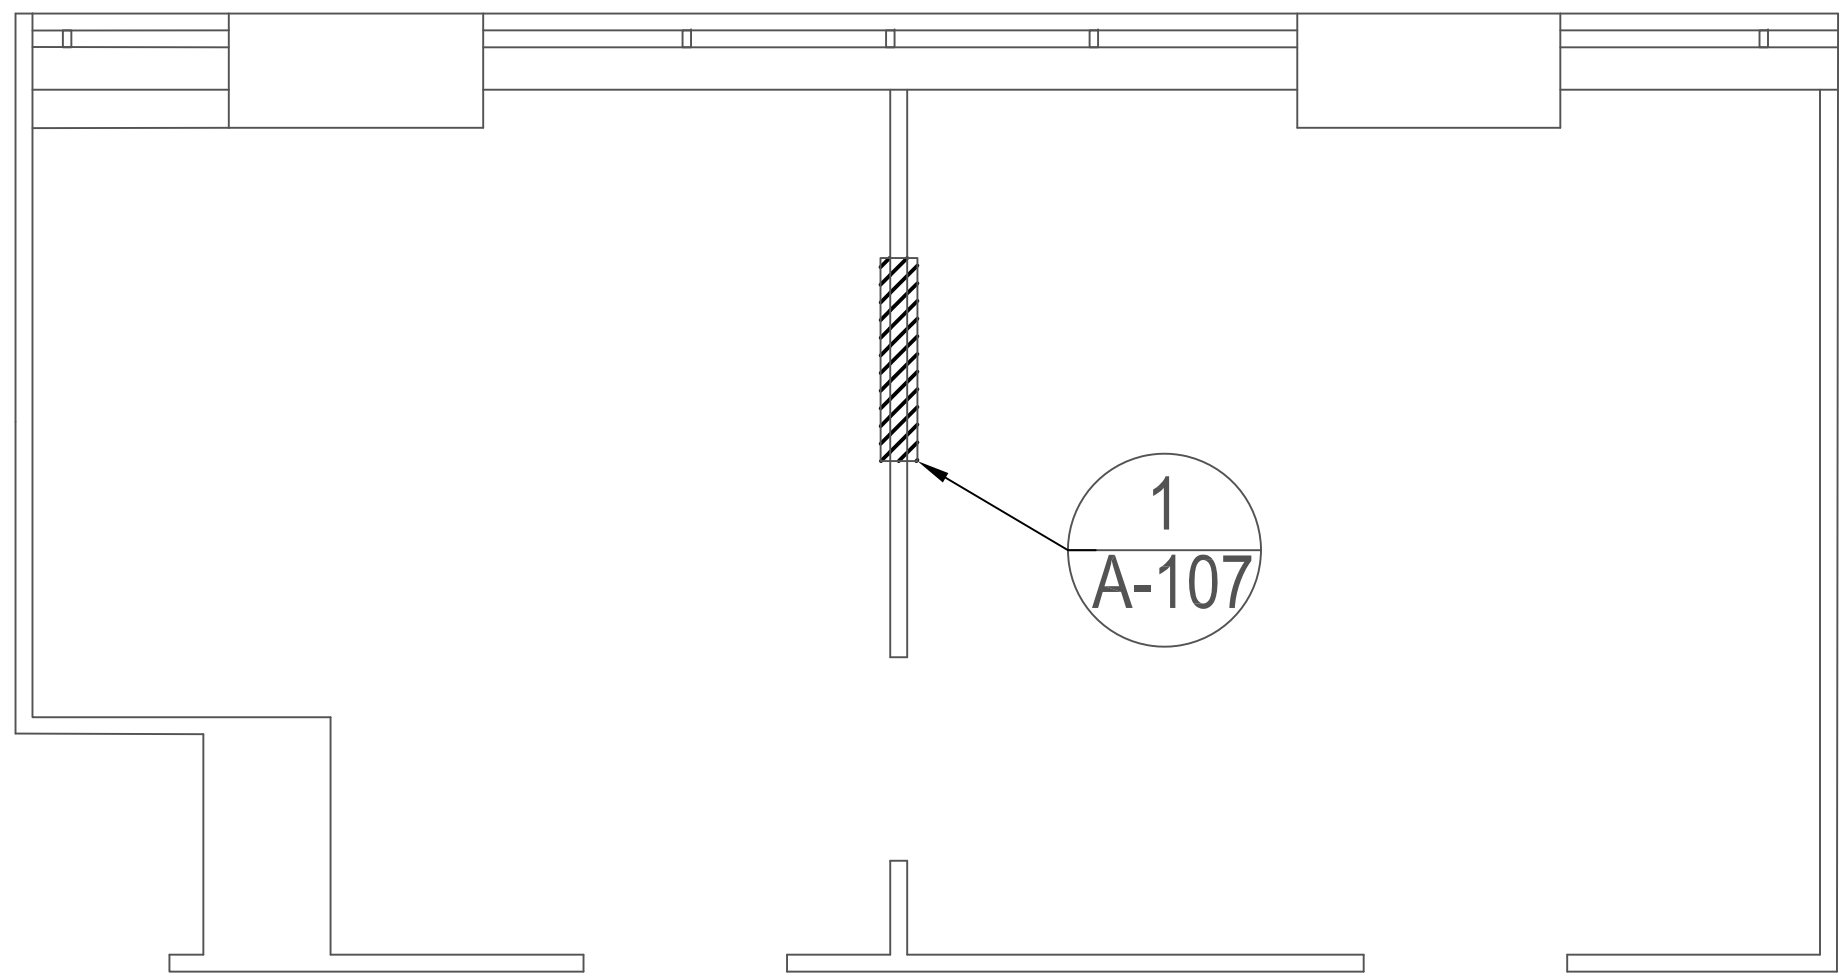


E 126-B, 127-B

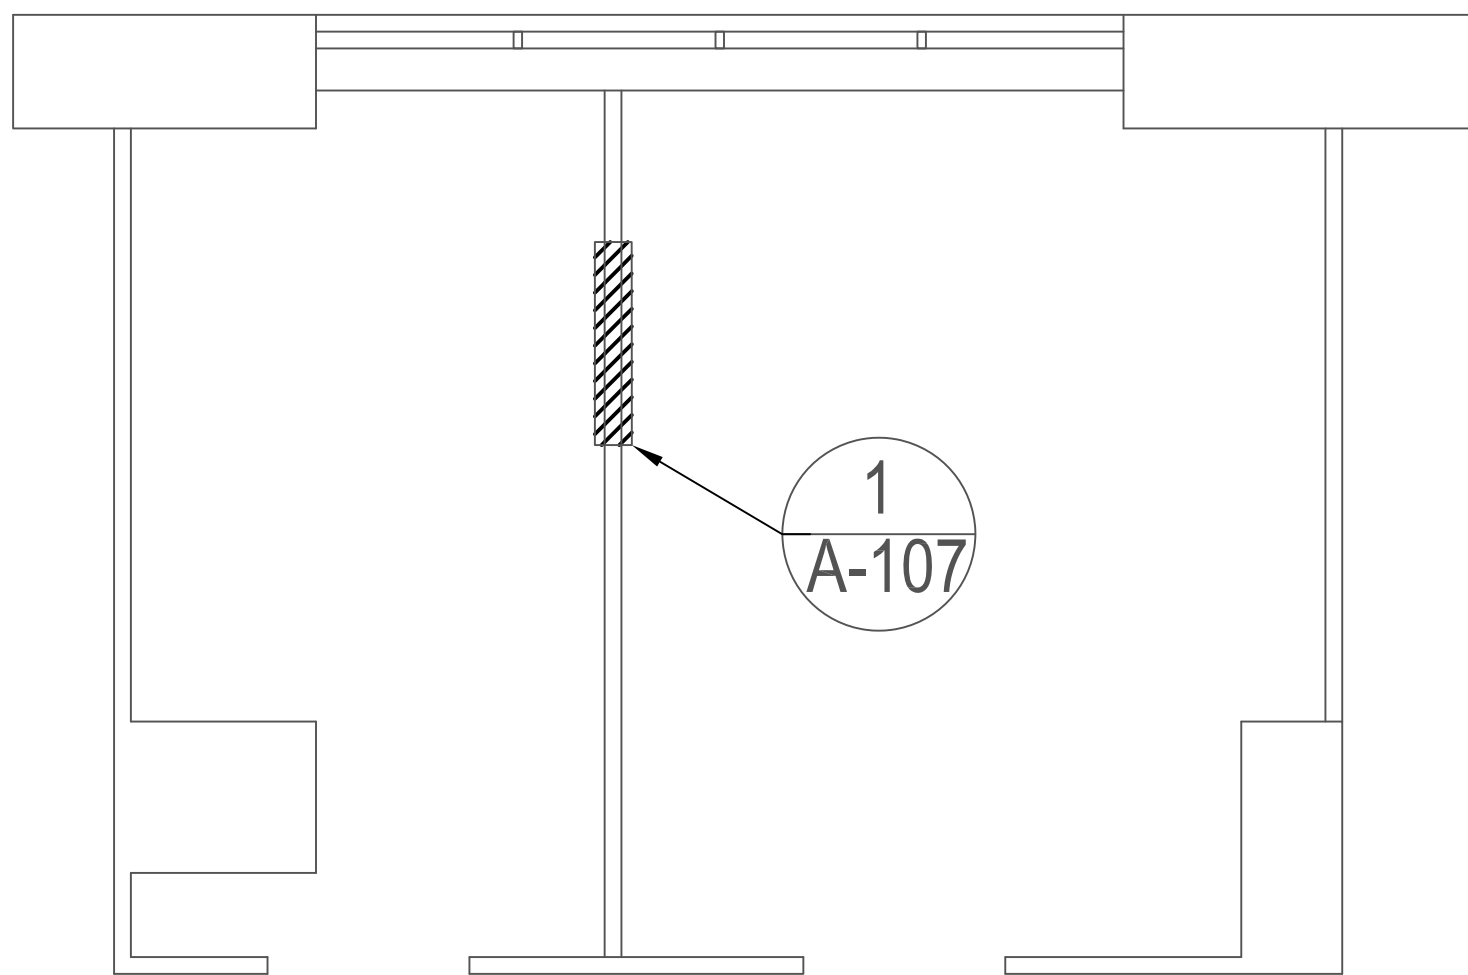


D 119-B, 120-B

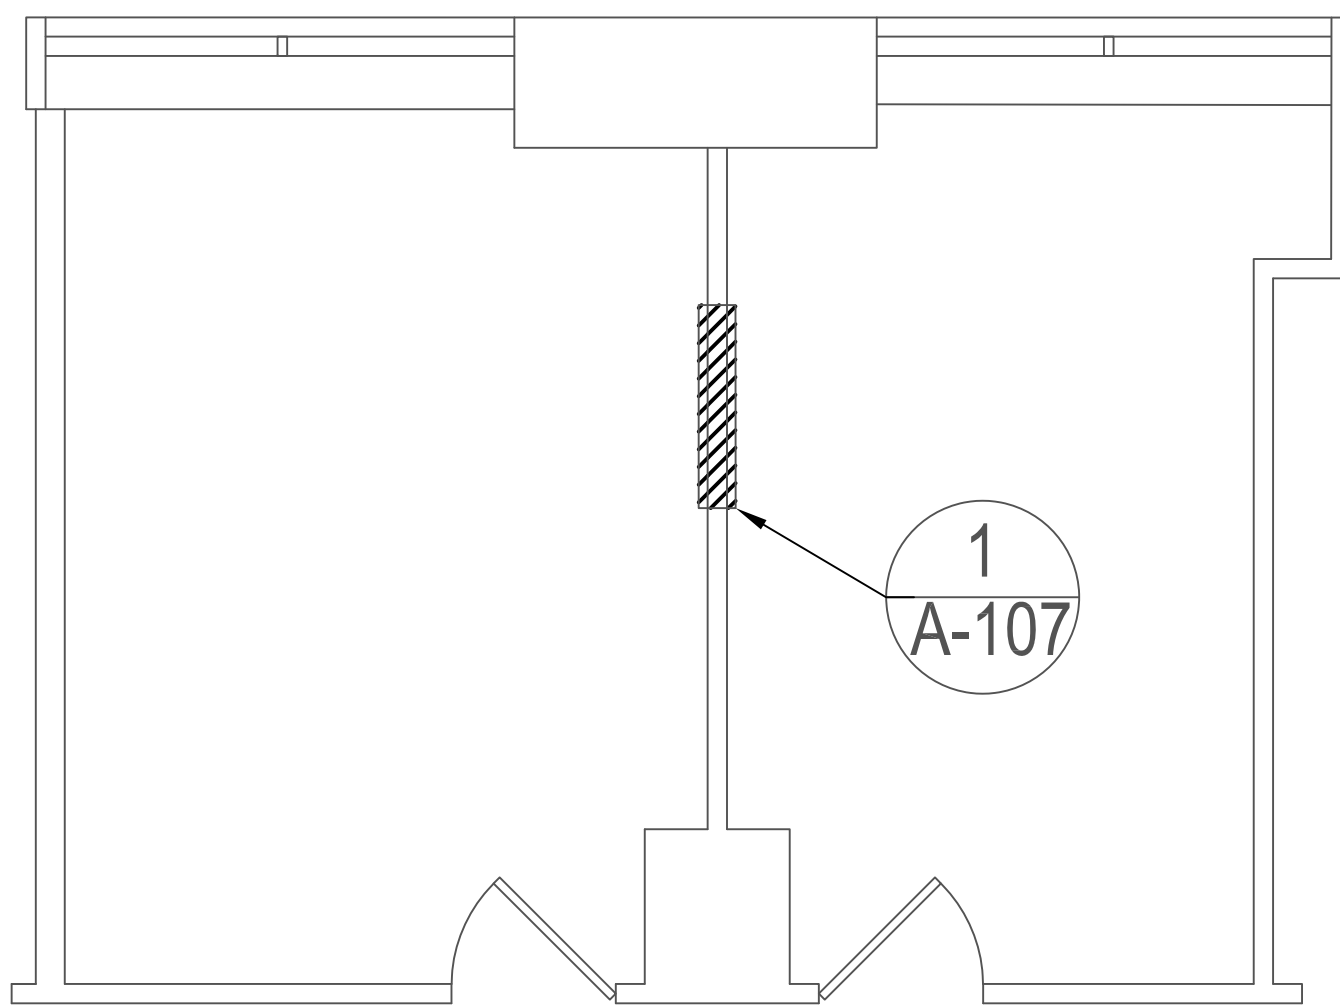


H 132-B, 133-B

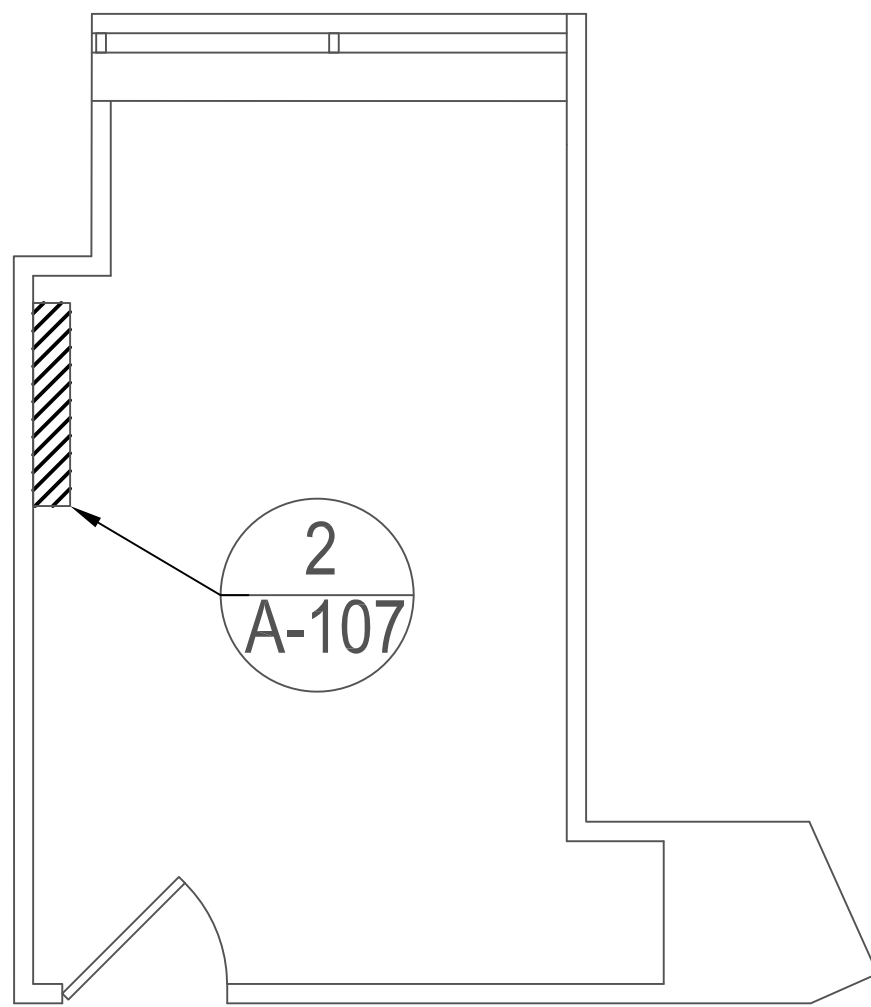

G 134-B

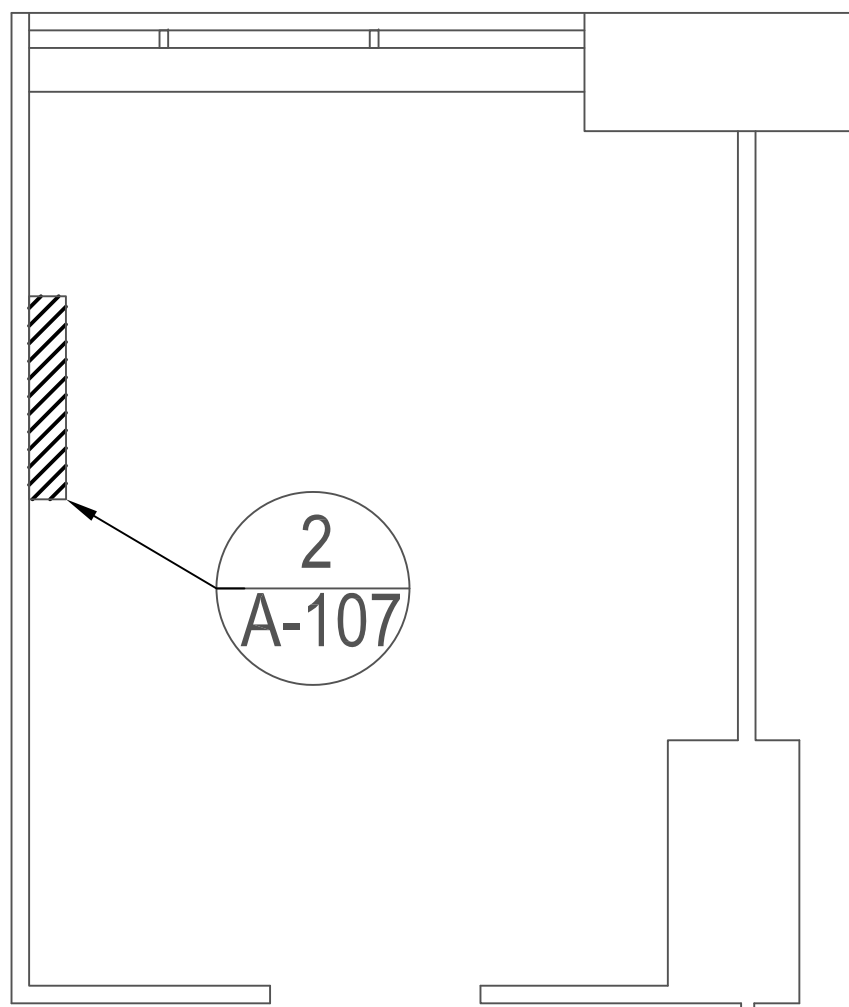

F 128-B

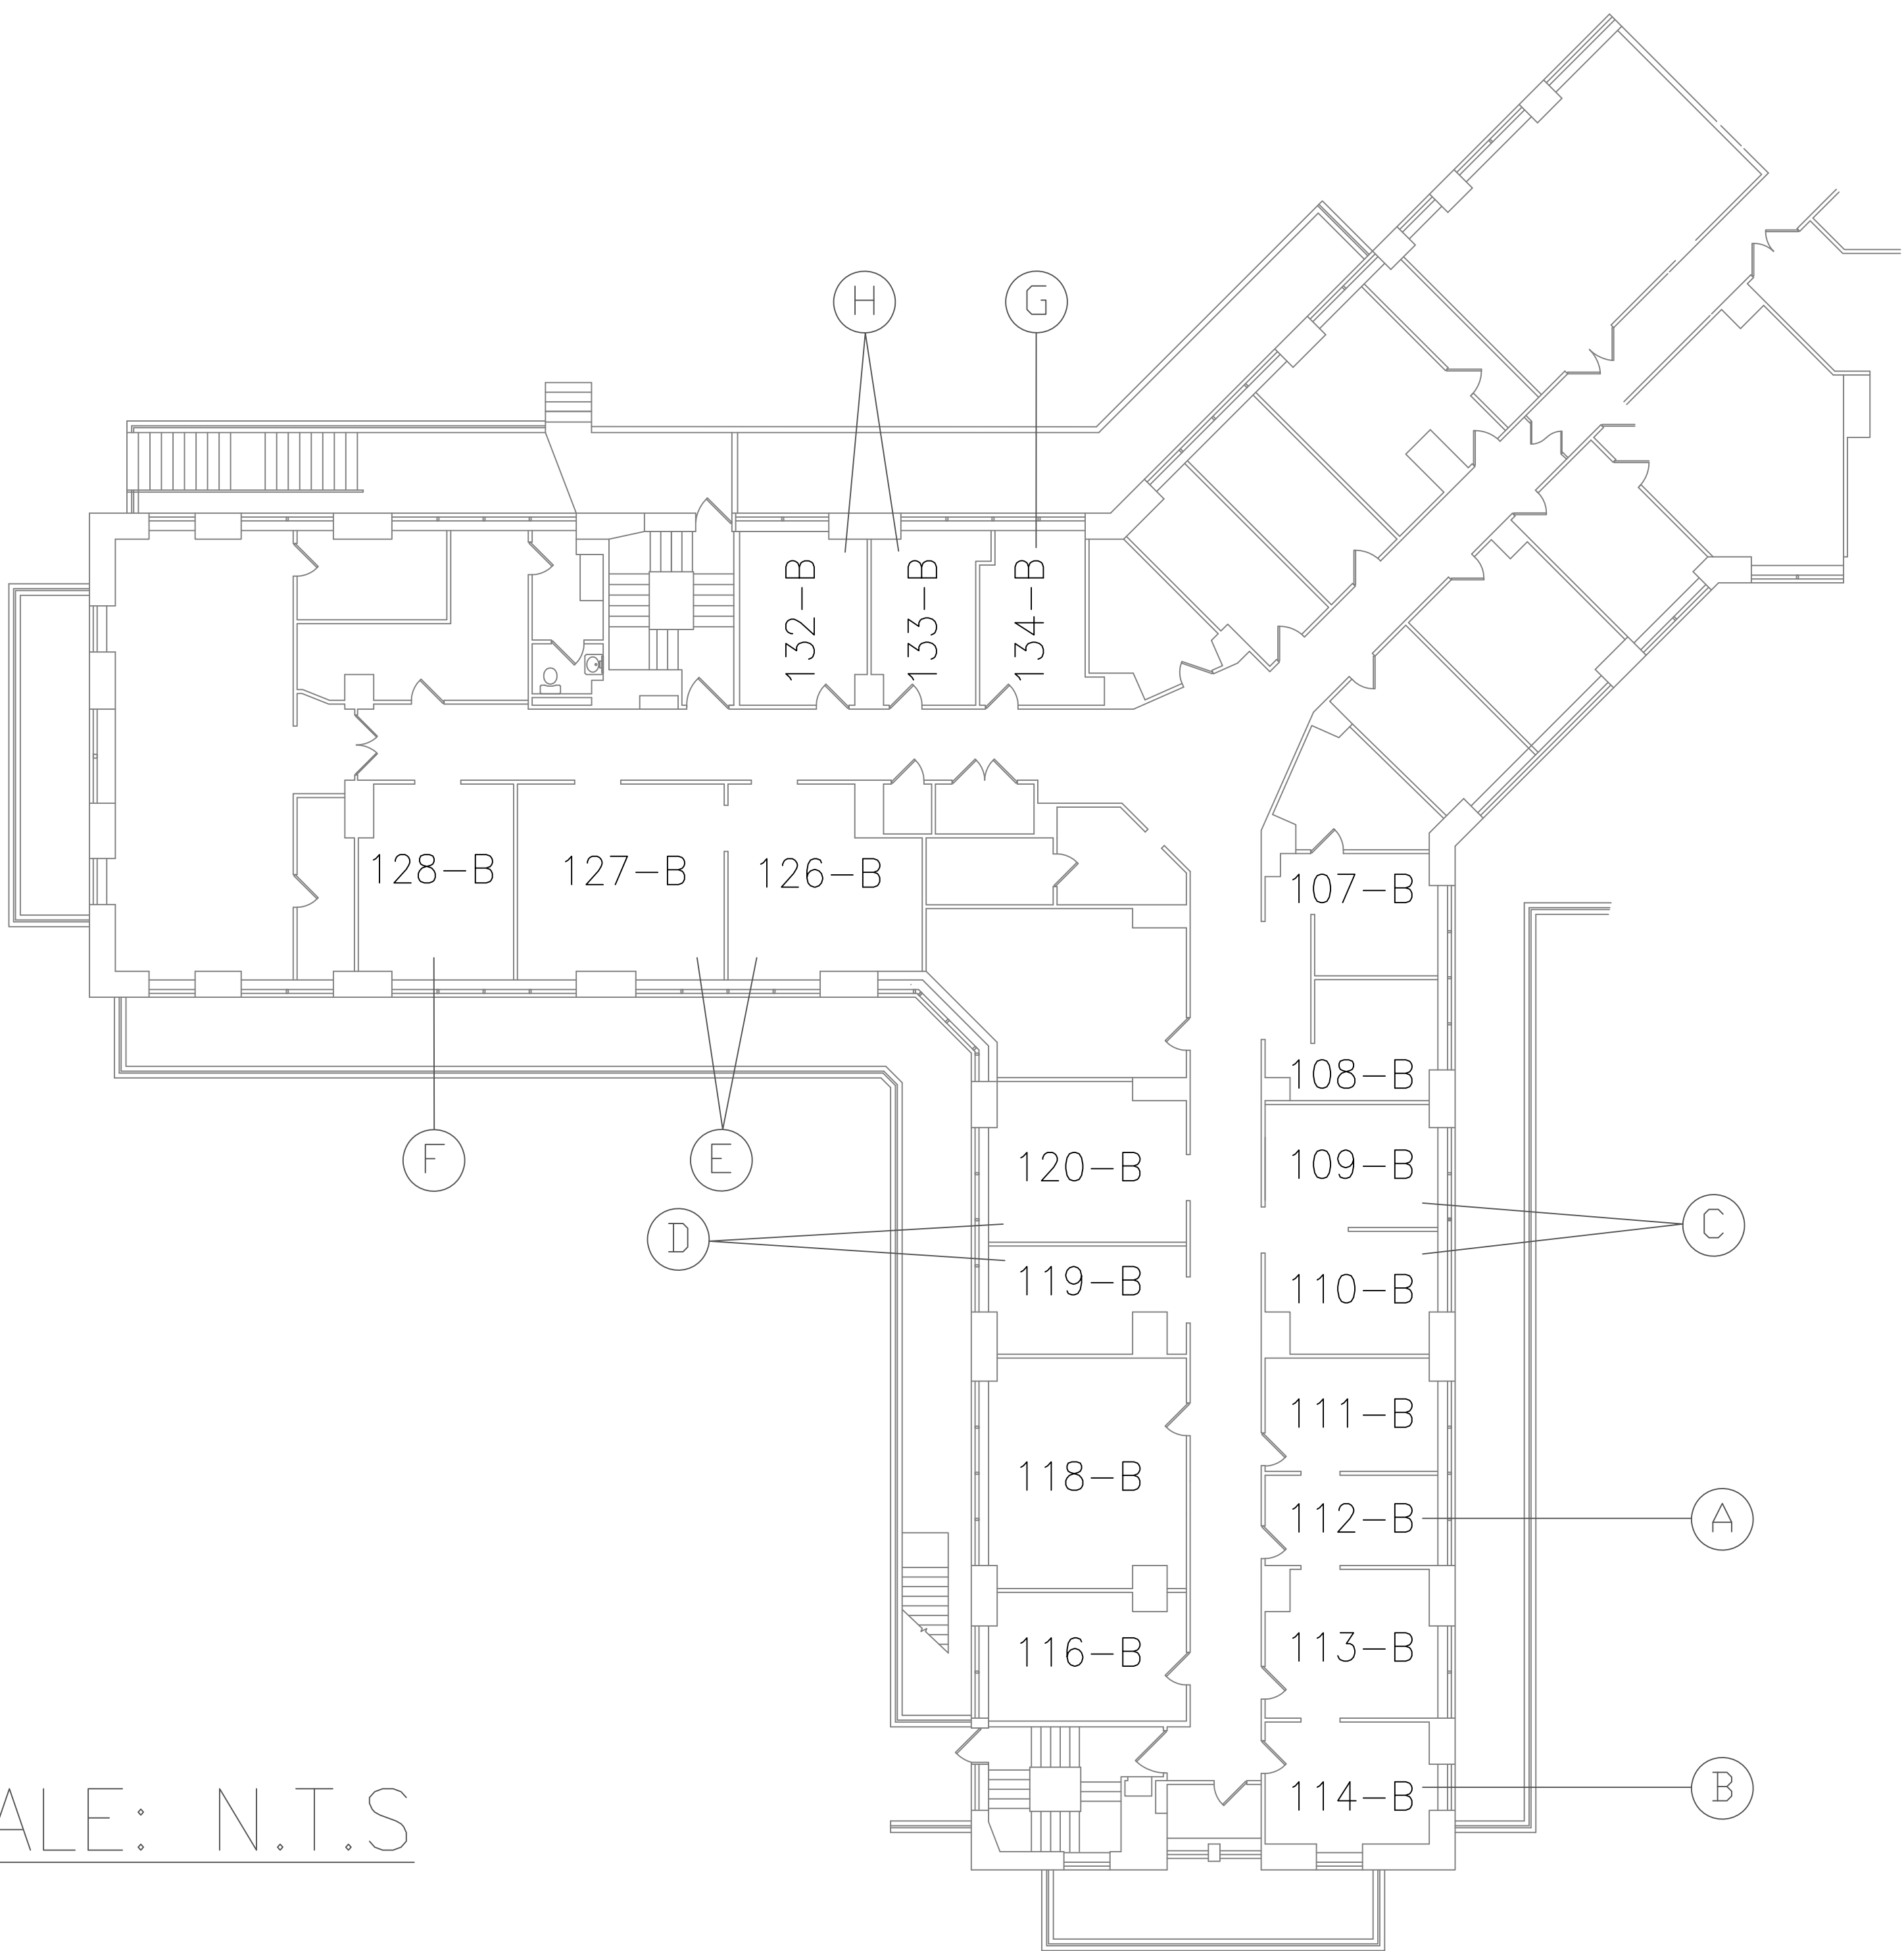

SCALE: N.T.S

"B" WING, 1ST FLOOR, BLDG1

Revisions:	Date:	CONSULTANT	ARCHITECT/ENGINEER OF RECORD WNYHCS ENGINEERING BUFFALO VETERANS ADMINISTRATION MEDICAL CENTER 3495 BAILEY AVENUE BUFFALO, NEW YORK 14215 716-834-9200	STAMP	Office of Construction and Facilities Management VA U.S. Department of Veterans Affairs	Drawing Title	Phase	Project Title		Project Number
						LOCATION OF EXISTING X-RAY UNITS	PHASE FOUR	DENTAL EXAM ROOM		528-22-127
						Approved: Project Director		Location BUFFALO VAMC		Building Number 1
								Issue Date 03/24/2023	Checked RJC	Drawn MTA
										Drawing Number A-106