

CONSULTANT

050 HOYT AVE WEST ST PAUL, MN 55117
952-451-0460

U.S. Department
of Veterans
Affairs

Dwg. 89 of 238



1 STAIR SECTION - CENTRAL STAIR
AE302 1/4" = 1'-0"

2 STAIR SECTION - CENTRAL STAIR
AE302 1/4" = 1'-0"

3 STAIR SECTION - CENTRAL STAIR
AE302 1/4" = 1'-0"

4 STAIR SECTION - CENTRAL STAIR
AE302 1/4" = 1'-0"

CONSULTANT		ARCHITECT/ENGINEER OF RECORD		STAMP		Office of Construction and Facilities Management		Drawing Title		Phase		Project Title		Project Number	
		THOMAS OLESAC, ARCHITECT				U.S. Department of Veterans Affairs		STAIR SECTIONS		CONSTRUCTION DOCUMENTS		RENOVATE BUILDING 1		520-317X	
		MS Lic # 5505						Approved:		FULLY SPRINKLERED		BILOXI, MISSISSIPPI		Building Number 1	
		1050 HOYT AVE WEST ST PAUL, MN 55117										Issue Date 03/10/2023		Drawing Number AE302	
		952-451-0460										Checked LA		Dwg. 90 of 238	
												Drawn CD			

BID DOCUMENTS

A

B

C

D

E

F

5/26/2023 11:11:25 AM

C:\Users\pjd\Documents\15950 - VA/C-Box Building 1_R21 - Central.mxd_Yunyoung.n

A


B

C

D

E

F

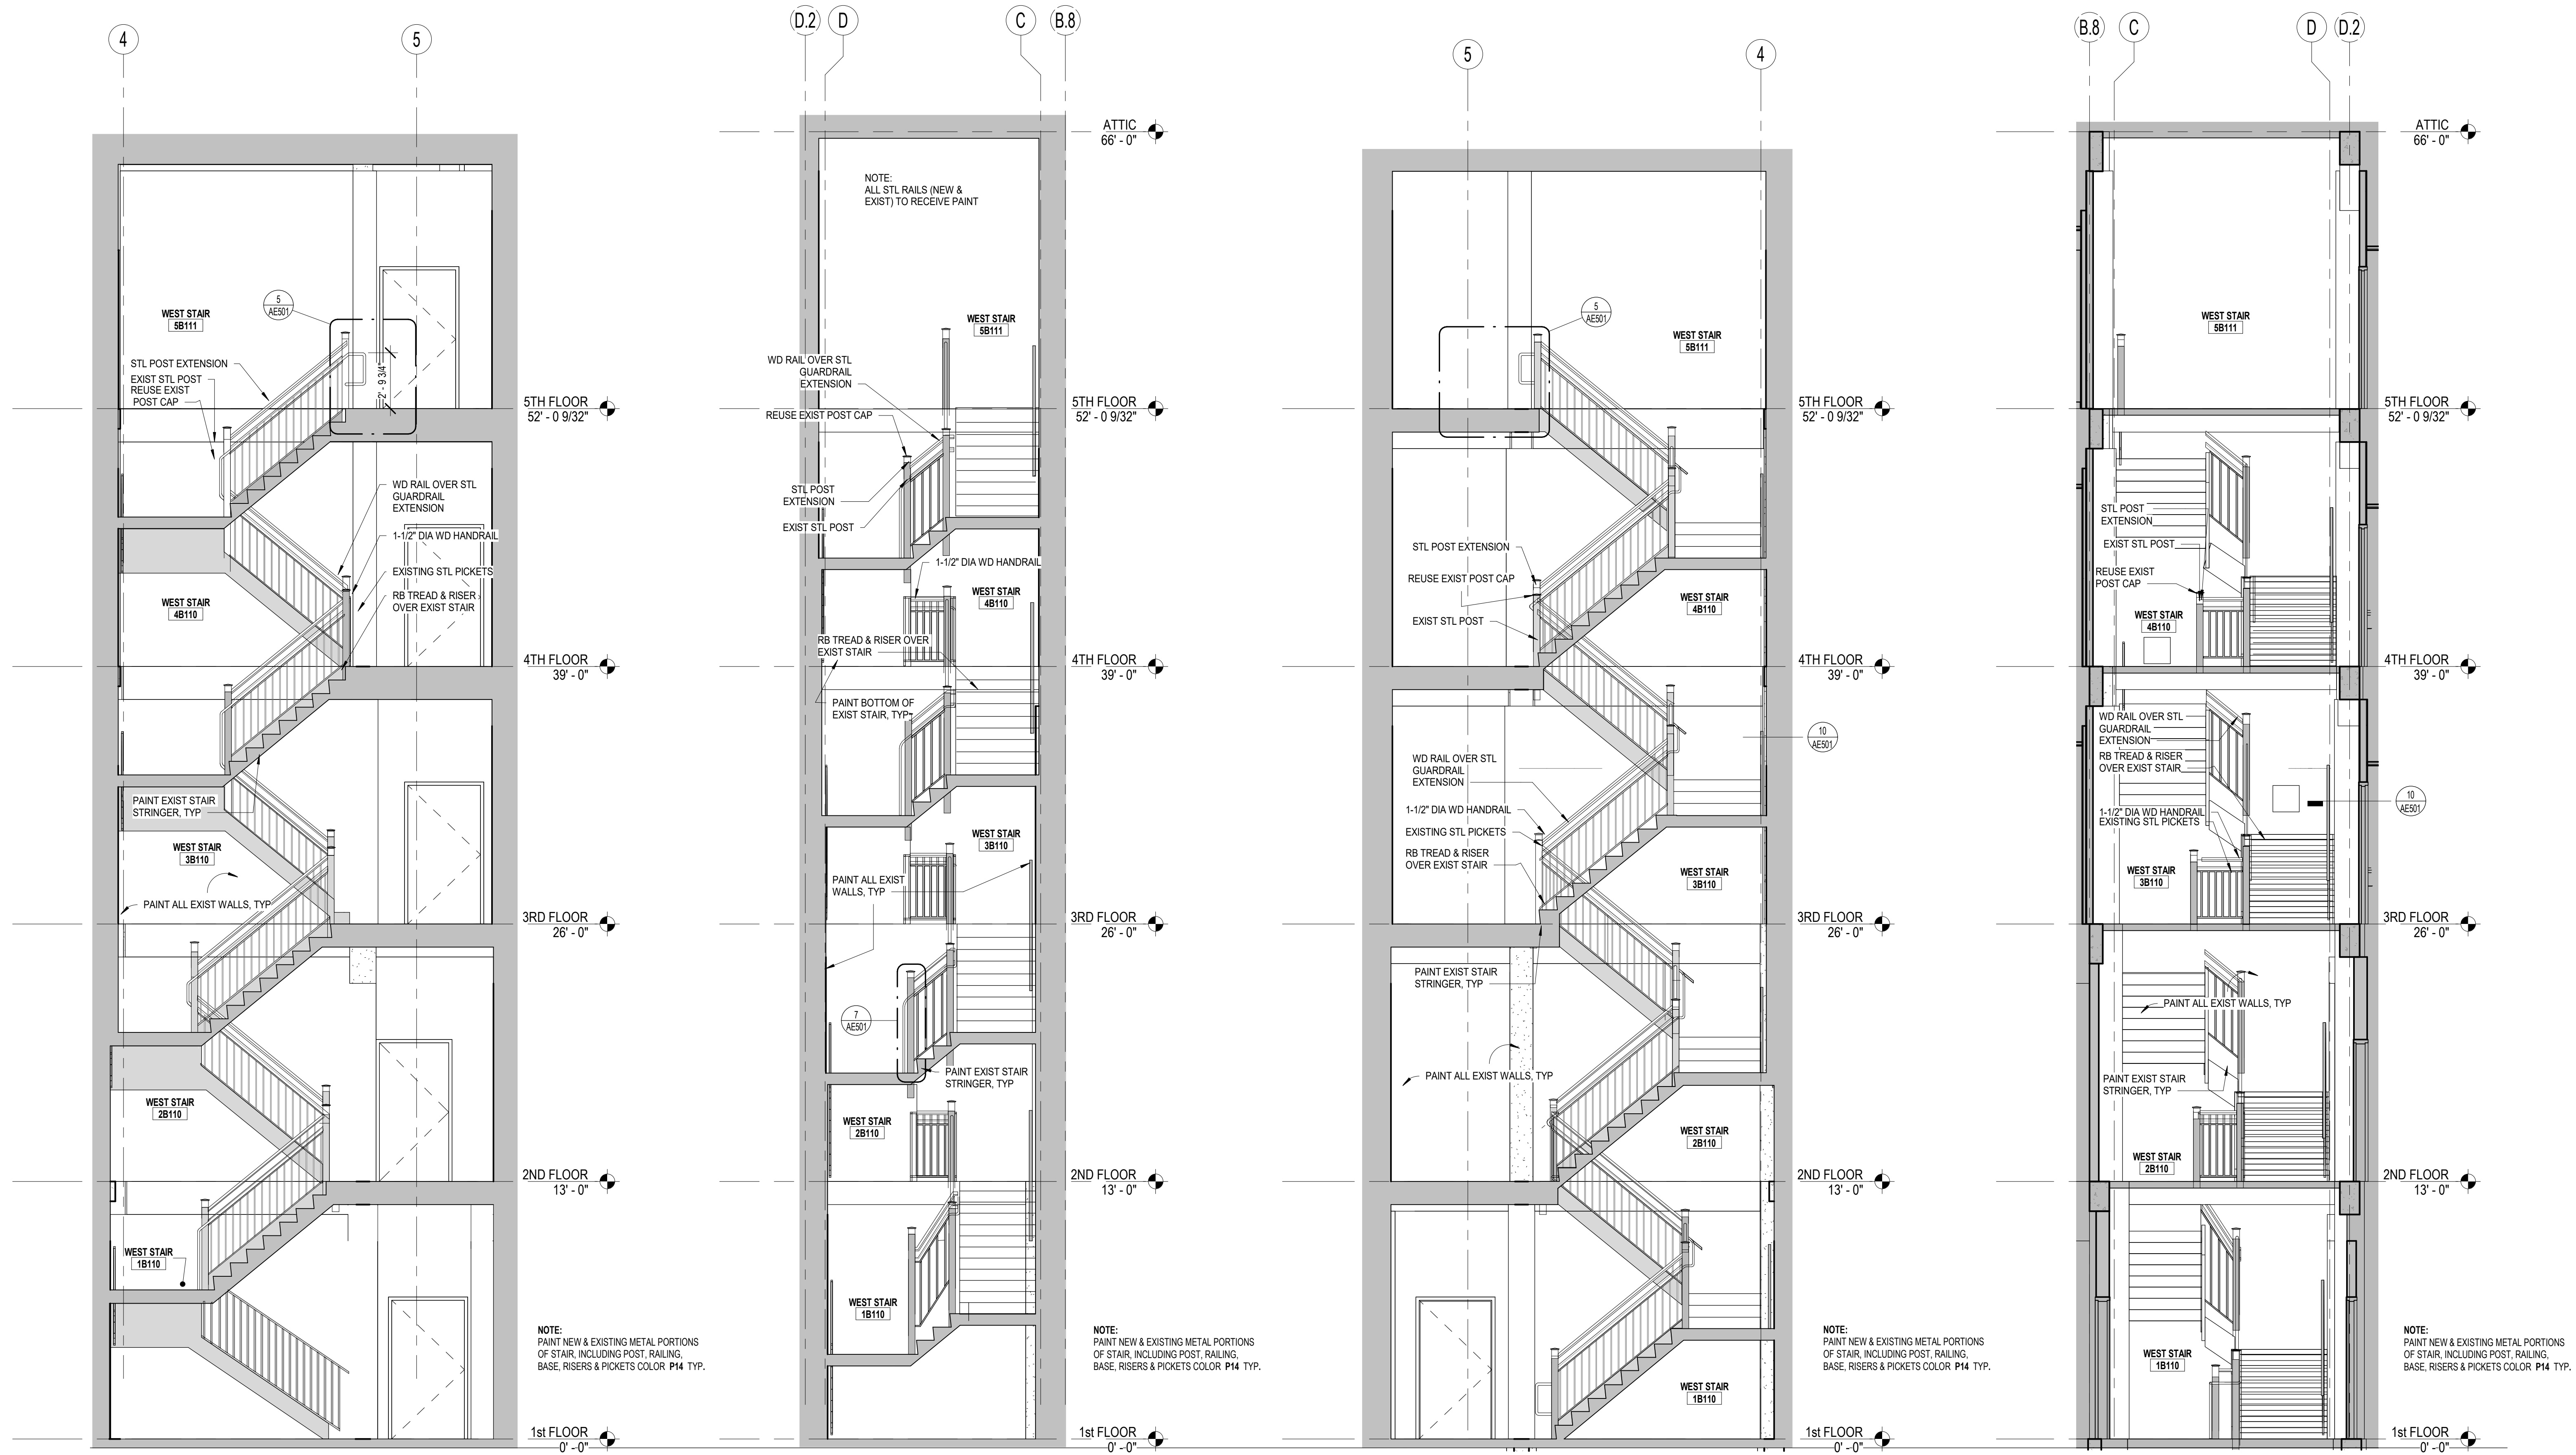

1 STAIR SECTION - WEST
AE303/ 1/4" = 1'-0"

NOTE: EAST STAIR SIMILAR BUT OPPOSITE

2 STAIR SECTION - WEST
AE303/ 1/4" = 1'-0"

NOTE: EAST STAIR SIMILAR BUT OPPOSITE

3 STAIR SECTION - WEST
AE303/ 1/4" = 1'-0"

NOTE: EAST STAIR SIMILAR BUT OPPOSITE

4 STAIR SECTION - WEST
AE303/ 1/4" = 1'-0"

NOTE: EAST STAIR SIMILAR BUT OPPOSITE

NO.	REVISIONS	DATE

CONSULTANT

ARCHITECT/ENGINEER OF RECORD
THOMAS OLESAC, ARCHITECT
MS Lic # 5505
1050 HOYT AVE WEST ST PAUL, MN 55117
952-451-0460

STAMP

Office of Construction and Facilities Management
VA U.S. Department of Veterans Affairs


Drawing Title
STAIR SECTIONS
Approved:

Phase
CONSTRUCTION DOCUMENTS
FULLY SPRINKLERED

Project Title
RENOVATE BUILDING 1
Location
BILOXI, MISSISSIPPI
Issue Date
03/10/2023
Checked
LA
Drawn
CD

Project Number
520-317X
Building Number
1
Drawing Number
AE303
Dwg. 91 of 238

BID DOCUMENTS

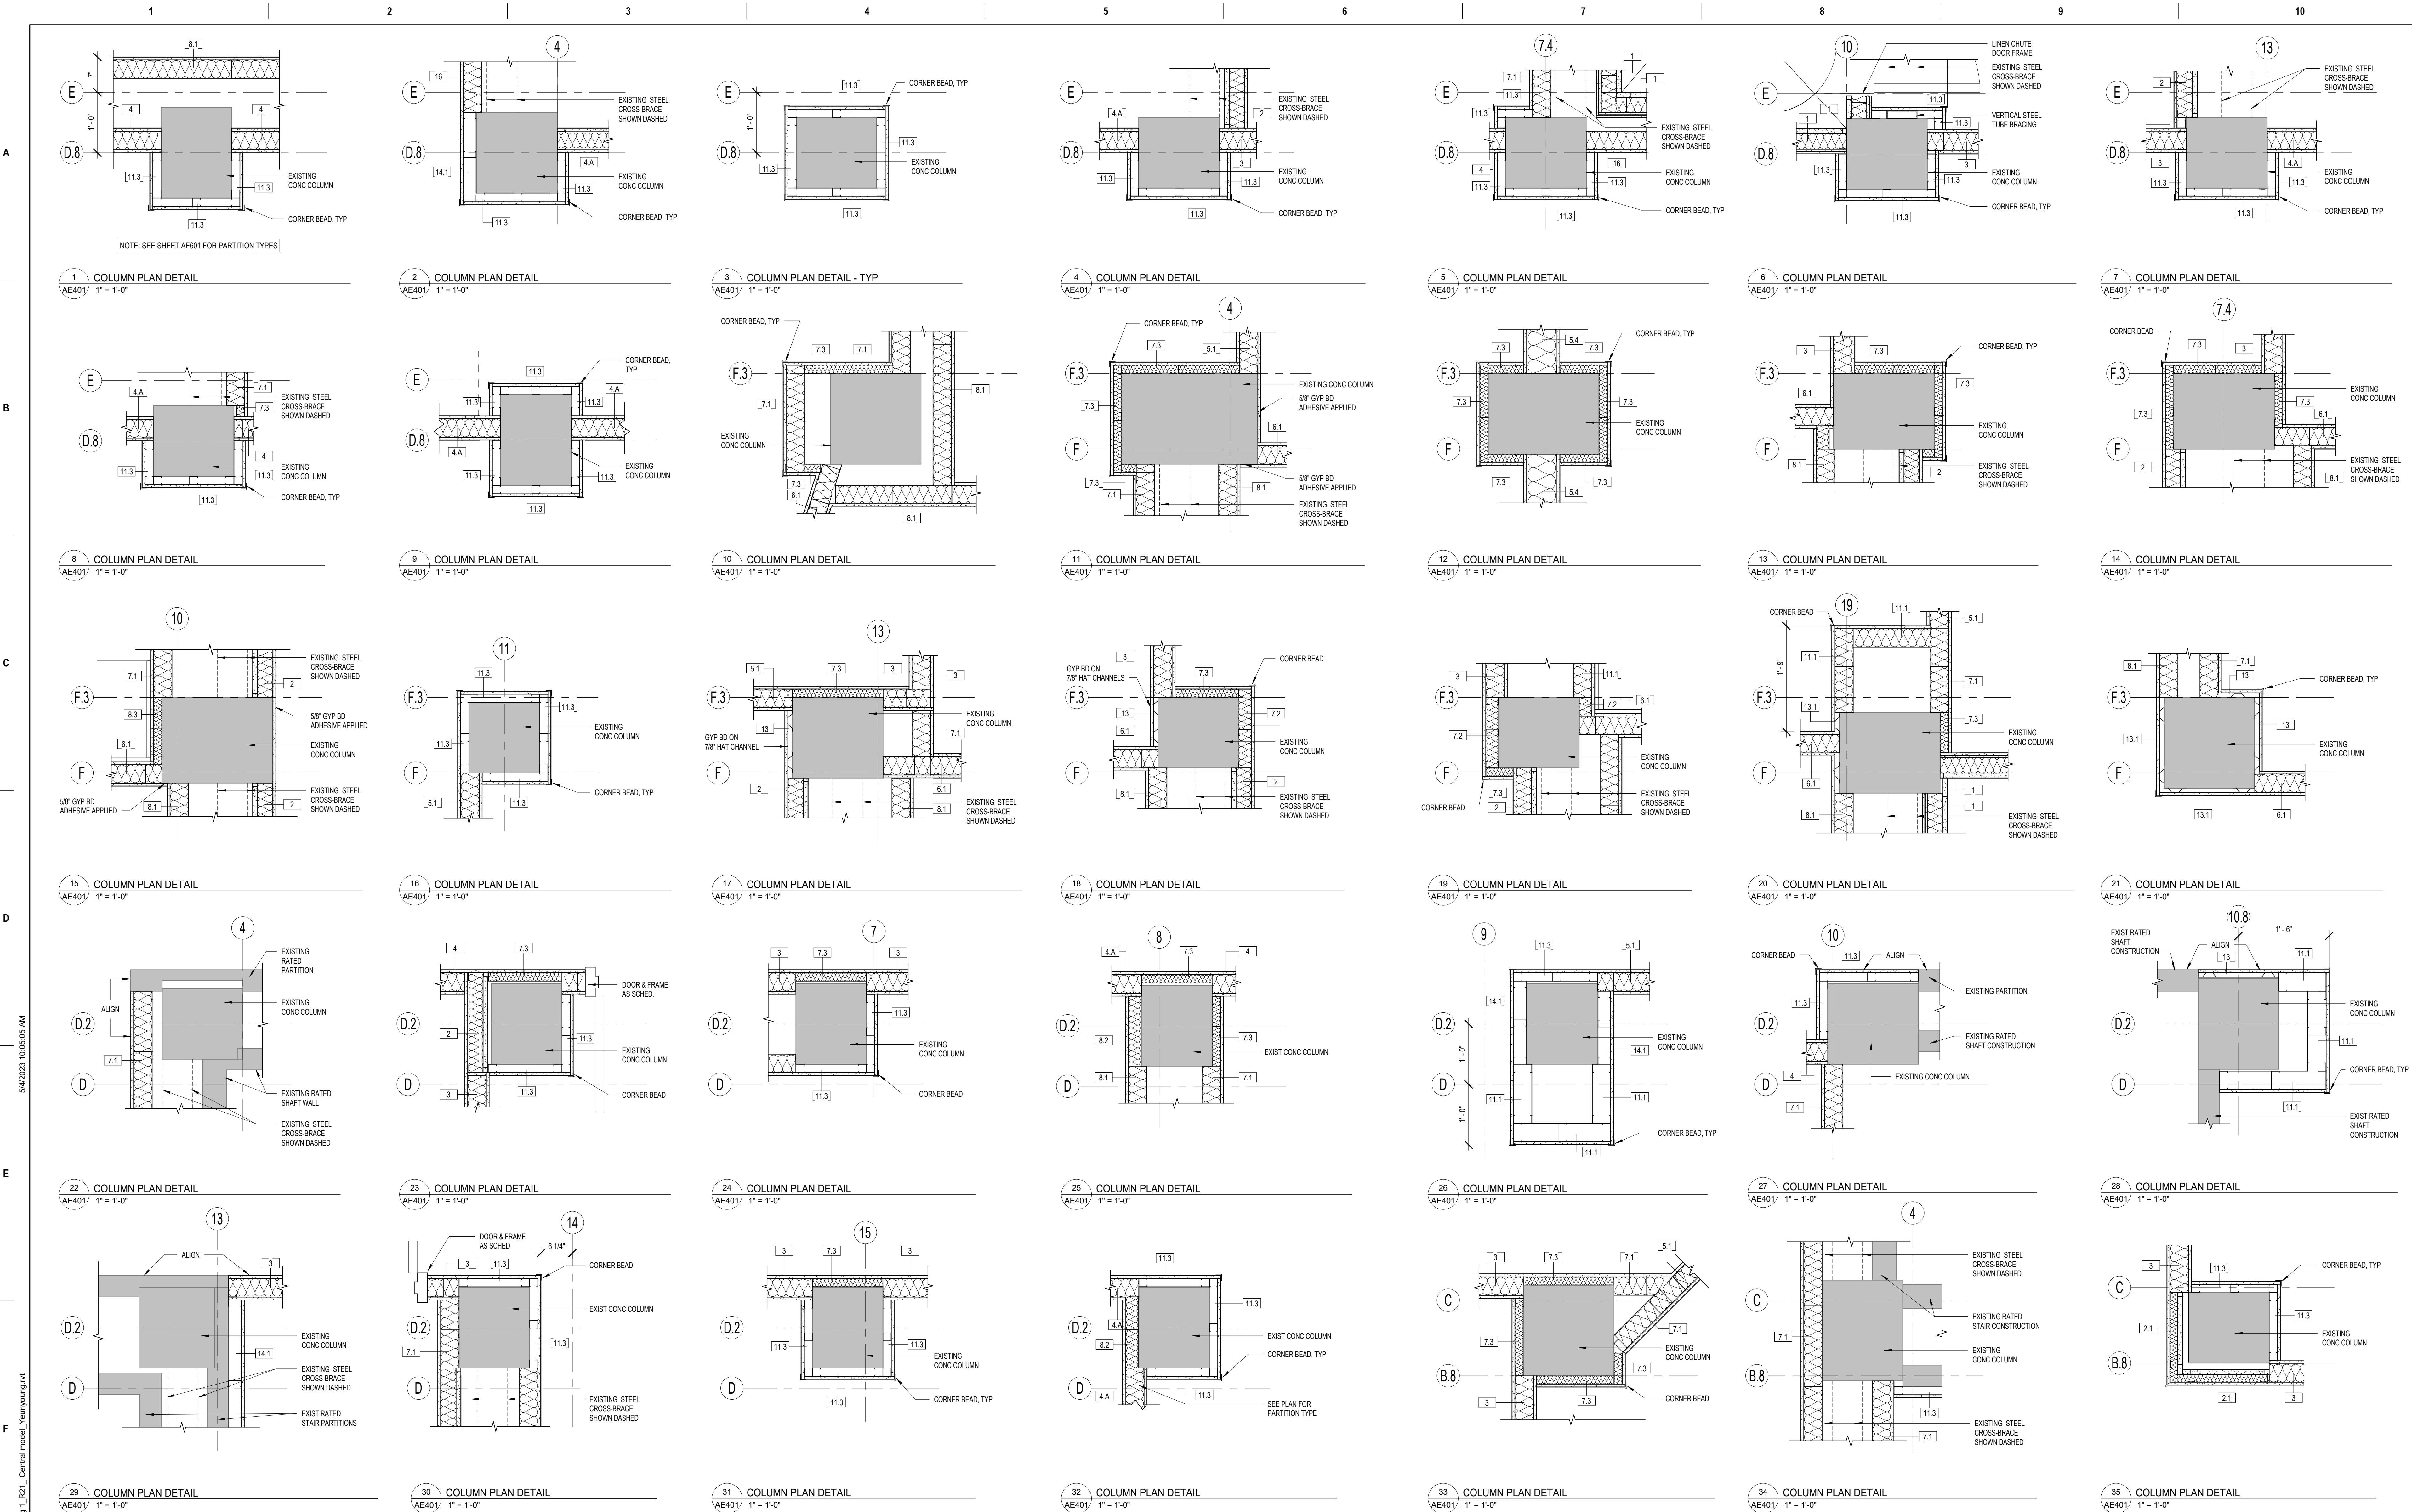

BID DOCUMENTS

--	--	

A

B

C

D

E

F

A

B

C


D

E


F

3/19/2023 10:32:25 AM


C:\Users\pjd\Documents\15950 - VAHC-Bldg Building 1_R21_Central.mxd_Yeunyoung.nst

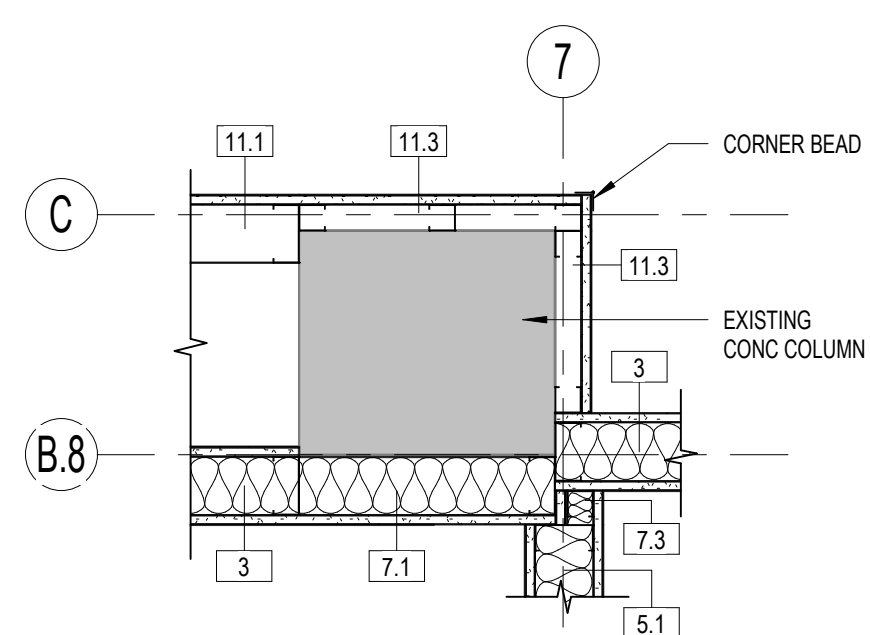


1 COLUMN PLAN DETAIL
1" = 1'-0"

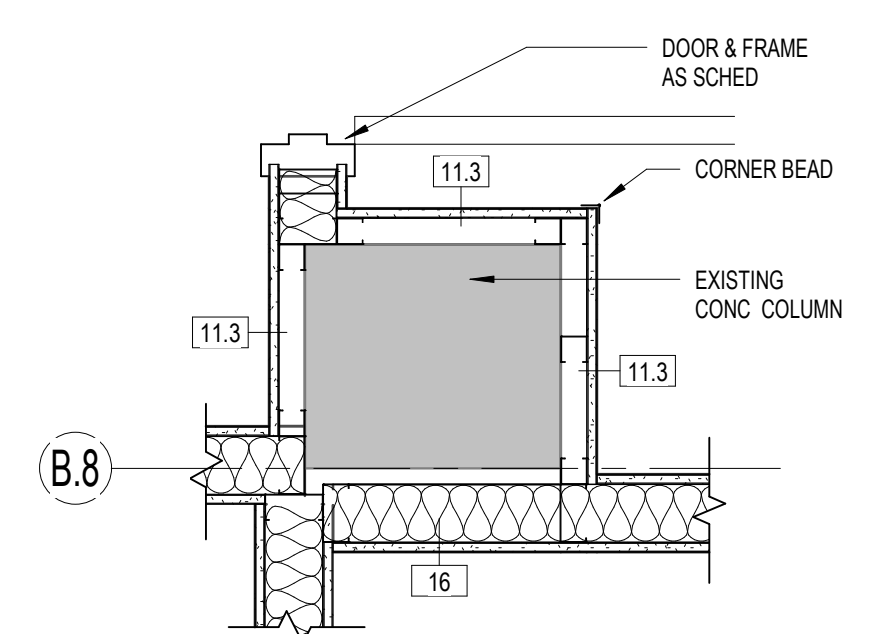


8 COLUMN PLAN DETAIL
1" = 1'-0"

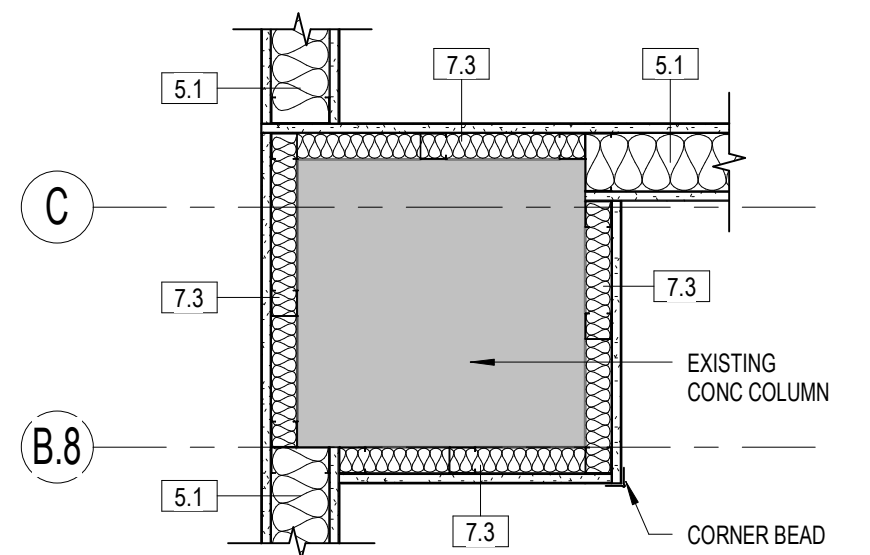


15 COLUMN PLAN DETAIL
1" = 1'-0"

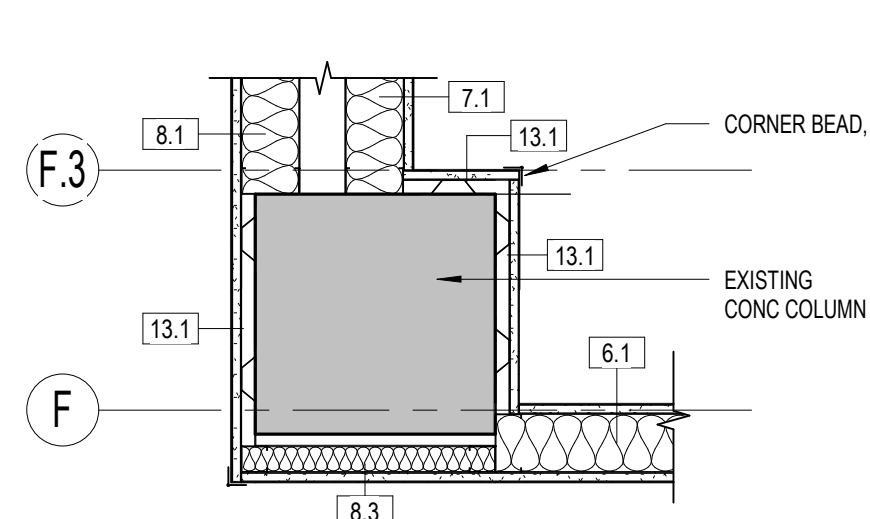


22 COLUMN PLAN DETAIL
1" = 1'-0"

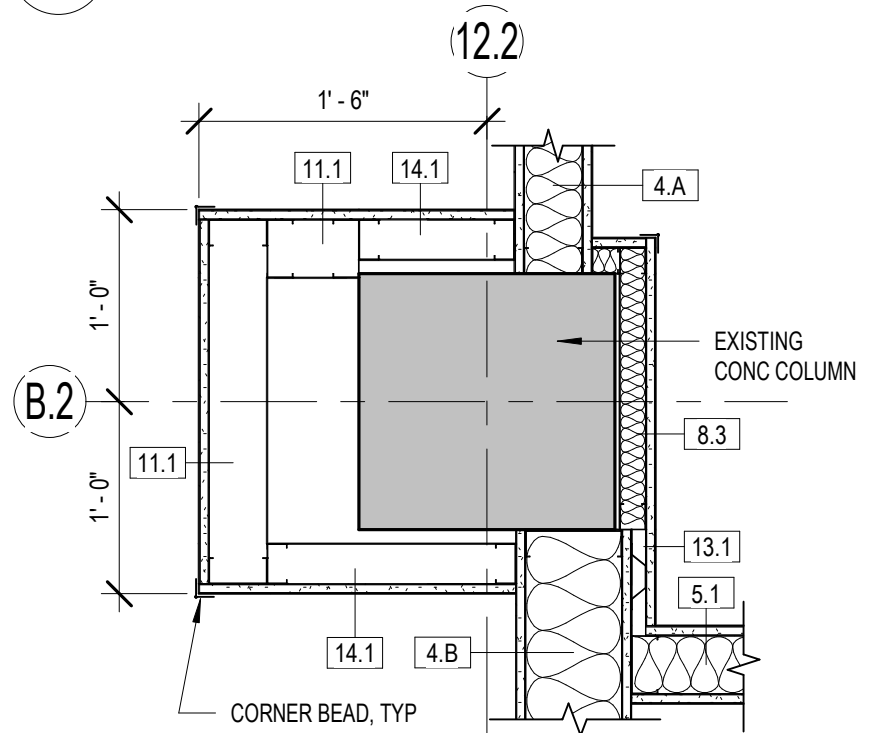


29 COLUMN PLAN DETAIL
1" = 1'-0"

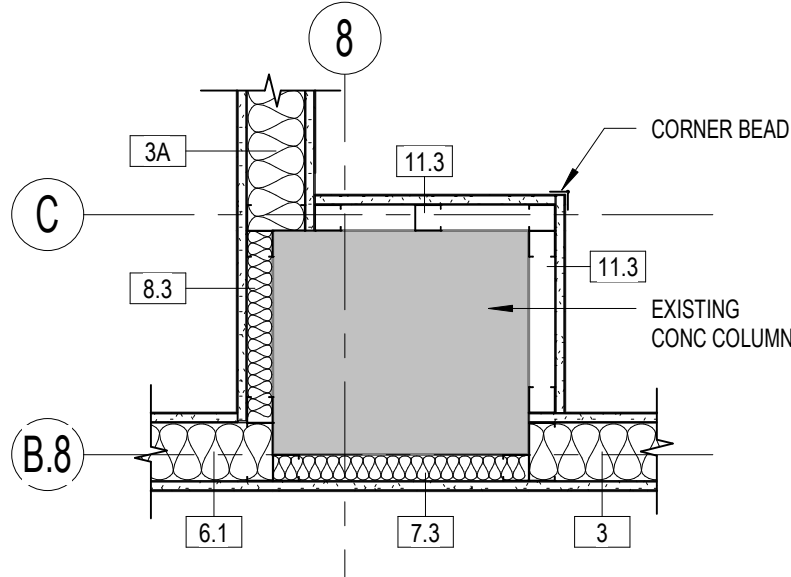


2 COLUMN PLAN DETAIL
1" = 1'-0"

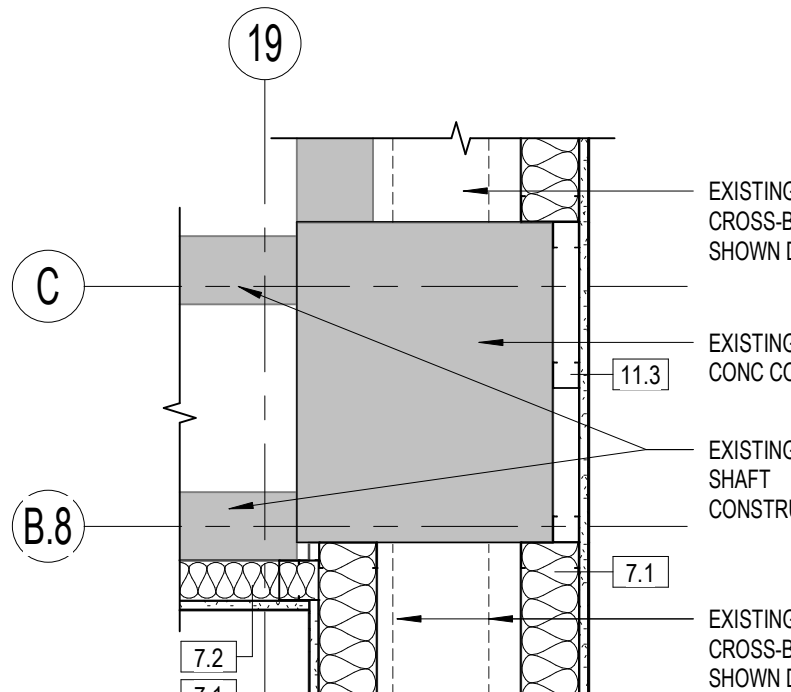


9 COLUMN PLAN DETAIL
1" = 1'-0"

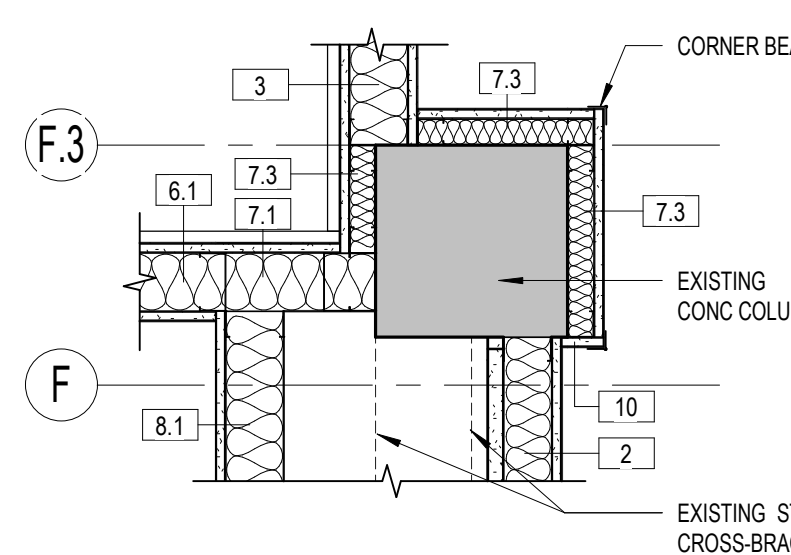


16 COLUMN PLAN DETAIL
1" = 1'-0"

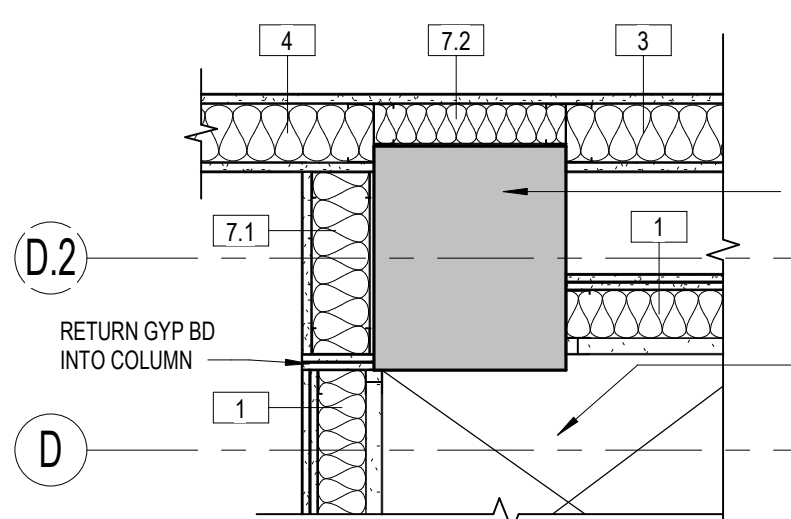


23 COLUMN PLAN DETAIL
1" = 1'-0"

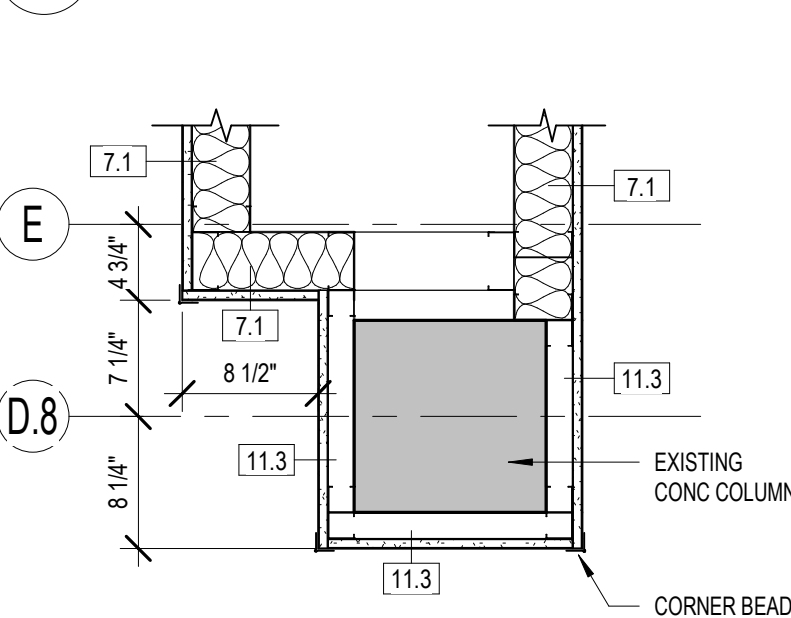


30 COLUMN PLAN DETAIL
1" = 1'-0"

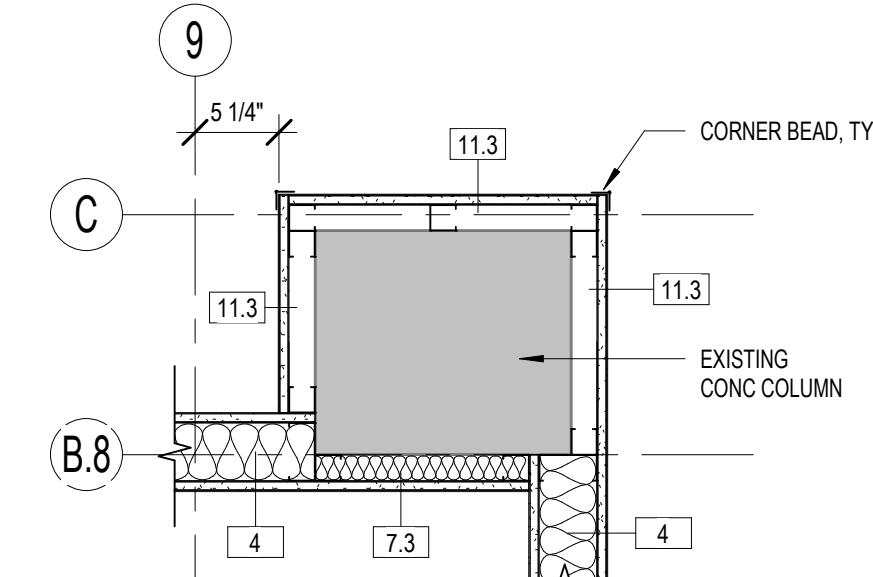


3 COLUMN PLAN DETAIL
1" = 1'-0"

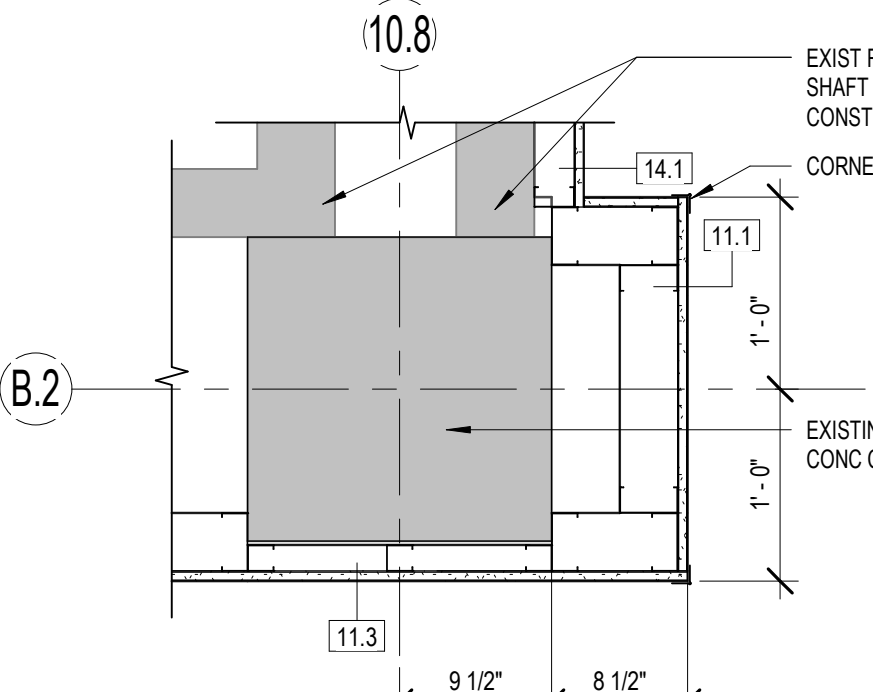


10 COLUMN PLAN DETAIL
1" = 1'-0"

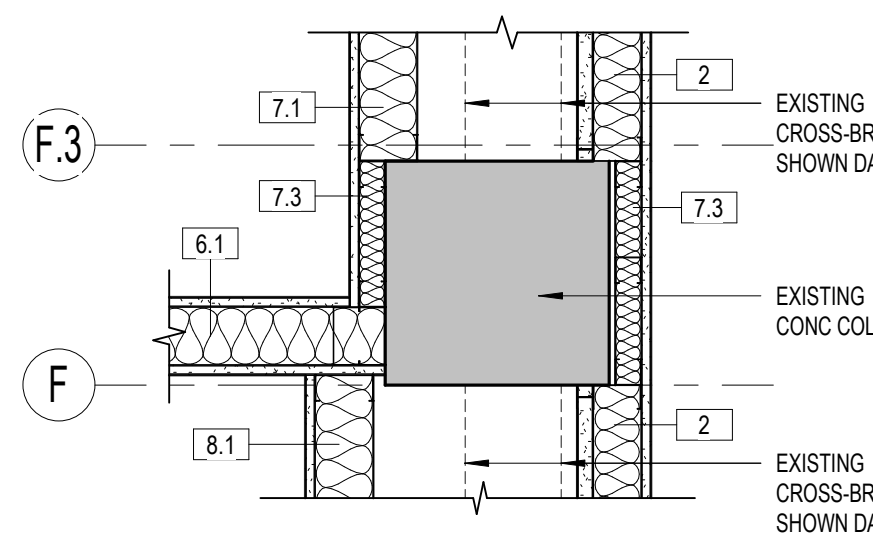


17 COLUMN PLAN DETAIL
1" = 1'-0"

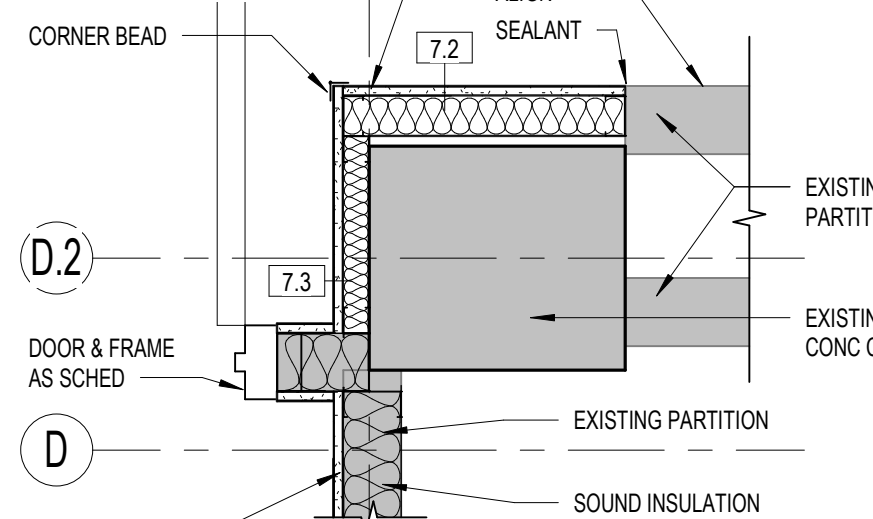


24 COLUMN PLAN DETAIL
1" = 1'-0"

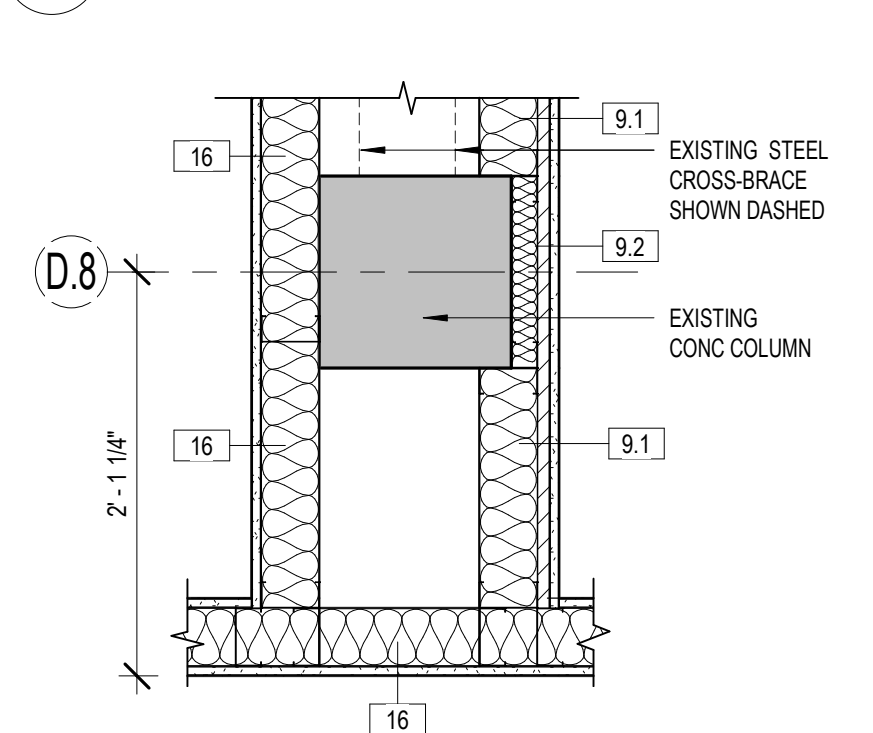


31 COLUMN PLAN DETAIL
1" = 1'-0"

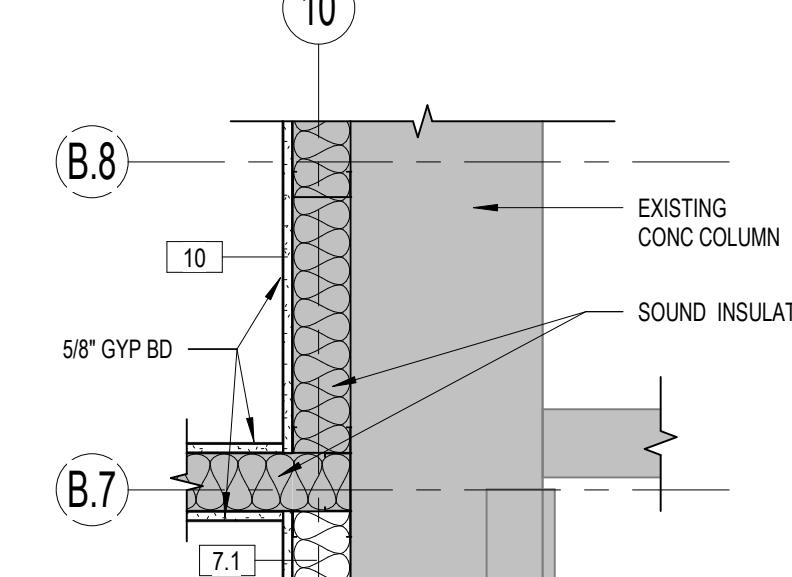


4 COLUMN PLAN DETAIL
1" = 1'-0"

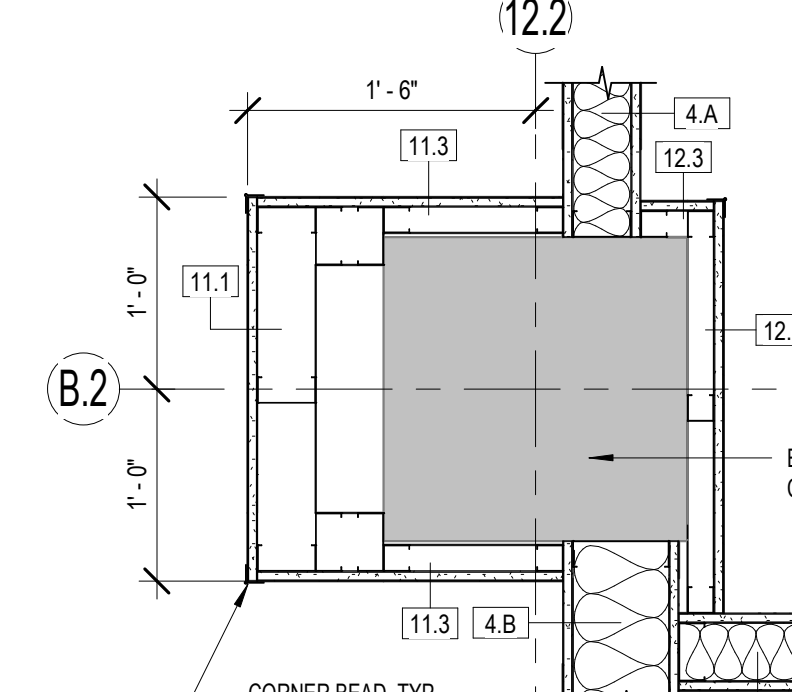


11 COLUMN PLAN DETAIL
1" = 1'-0"

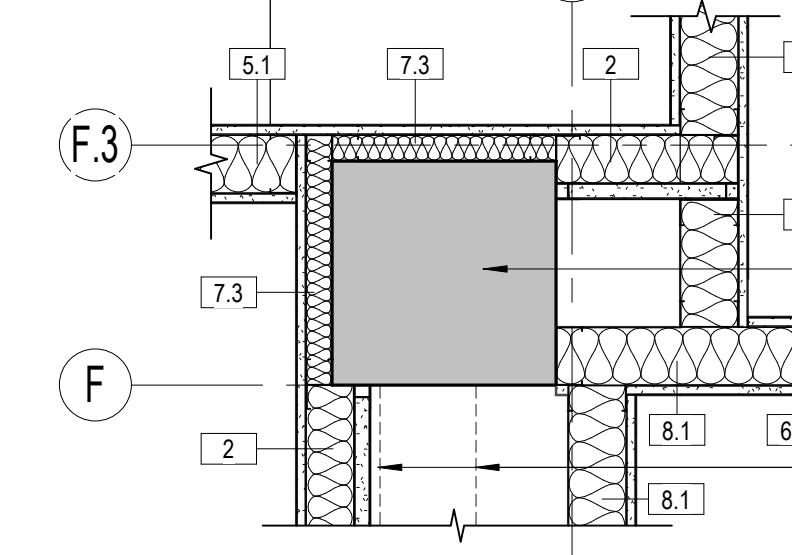


18 COLUMN PLAN DETAIL
1" = 1'-0"

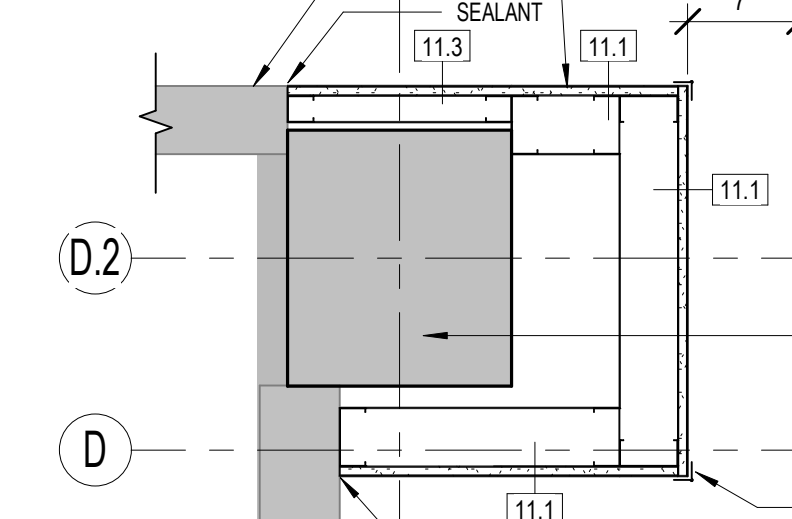


25 COLUMN PLAN DETAIL
1" = 1'-0"

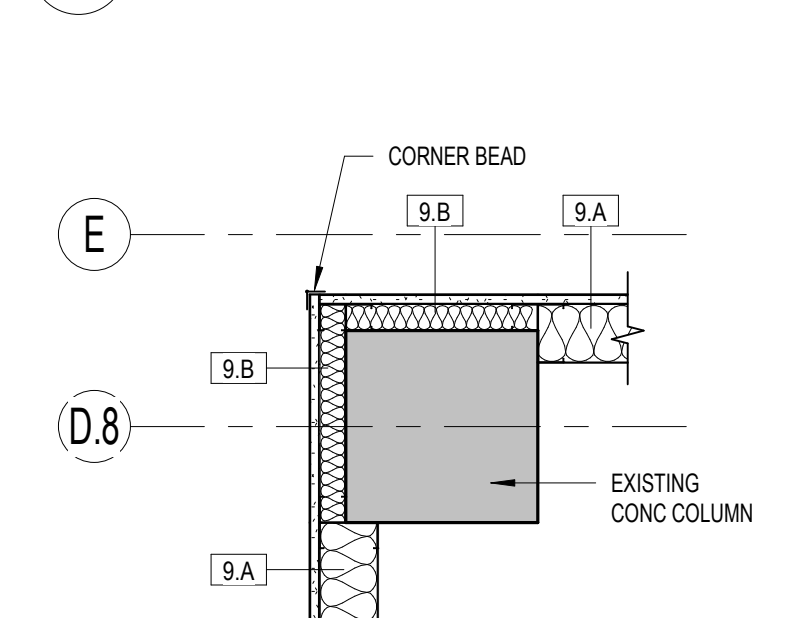


32 COLUMN PLAN DETAIL
1" = 1'-0"

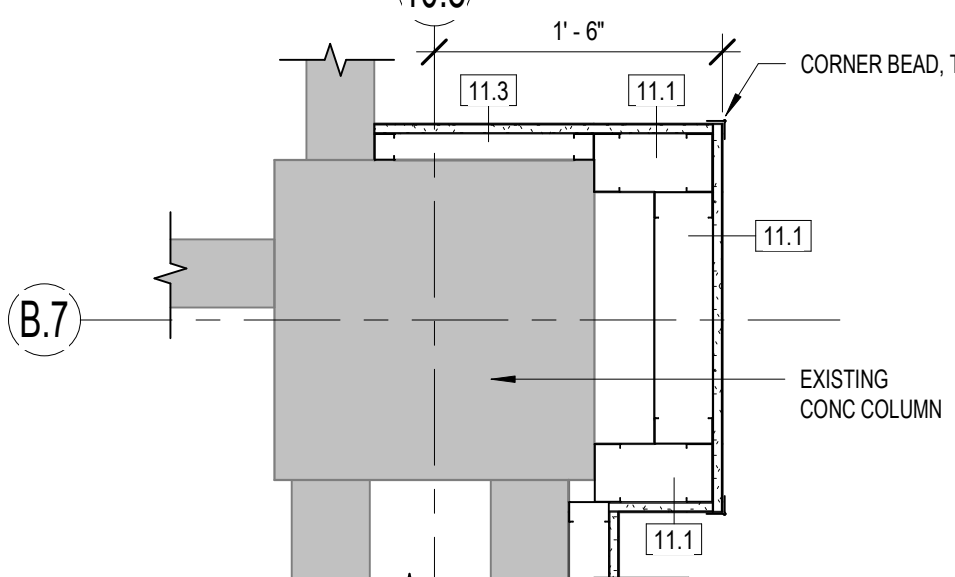


5 COLUMN PLAN DETAIL
1" = 1'-0"

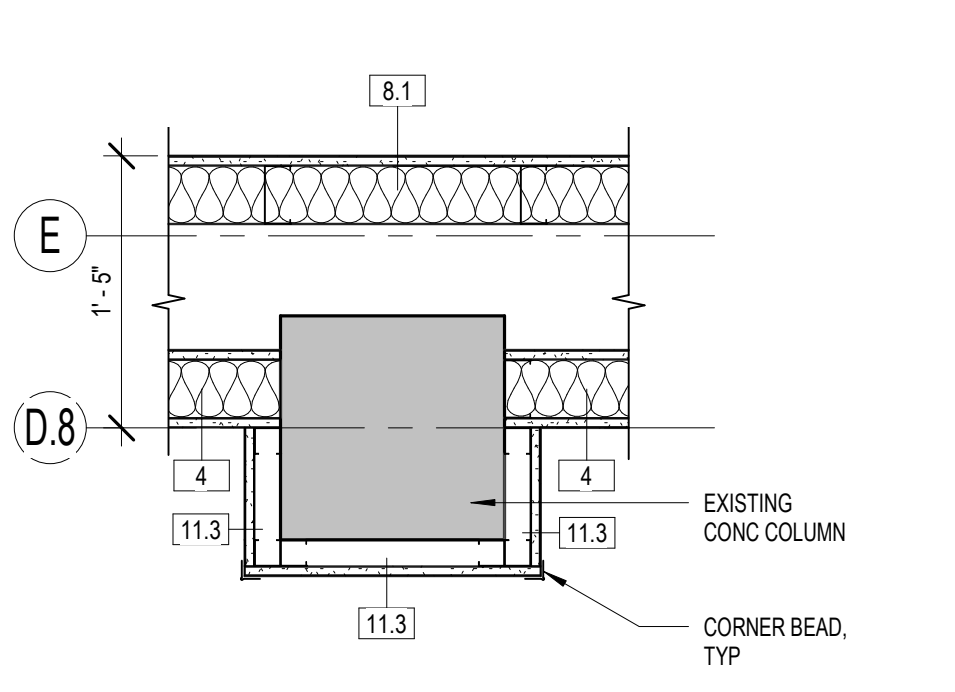


12 COLUMN PLAN DETAIL
1" = 1'-0"

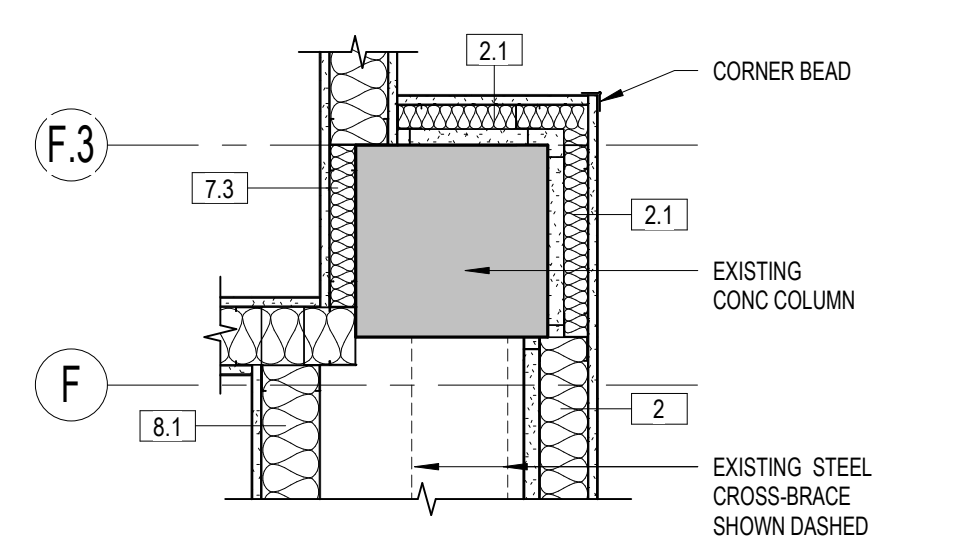


19 COLUMN PLAN DETAIL
1" = 1'-0"

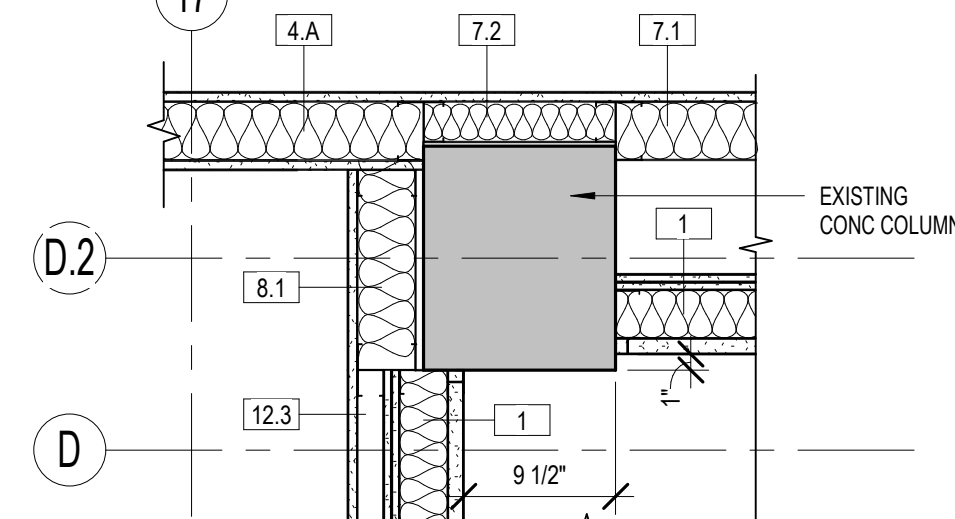


26 COLUMN PLAN DETAIL
1" = 1'-0"

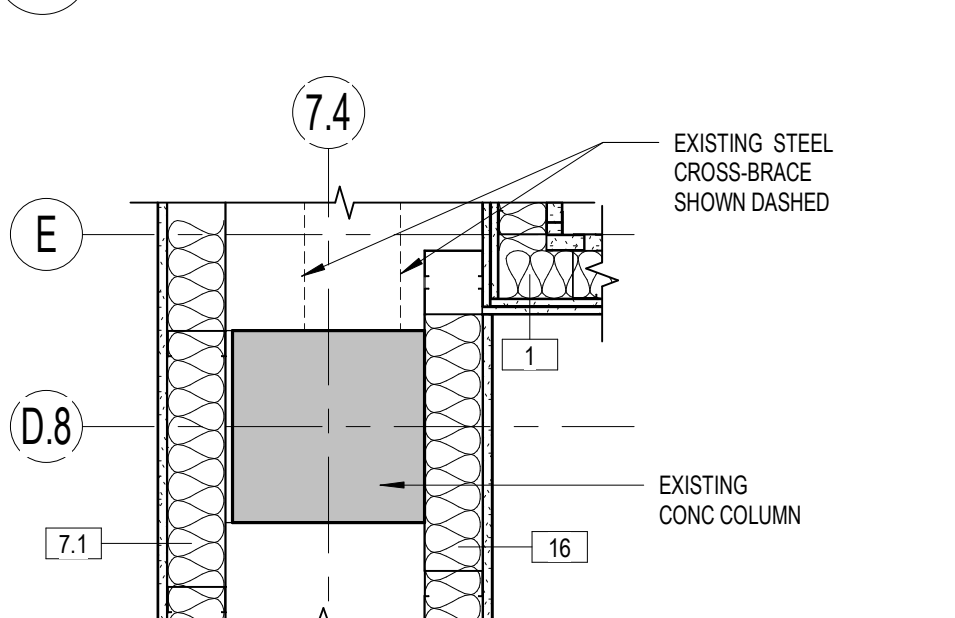


33 COLUMN PLAN DETAIL
1" = 1'-0"

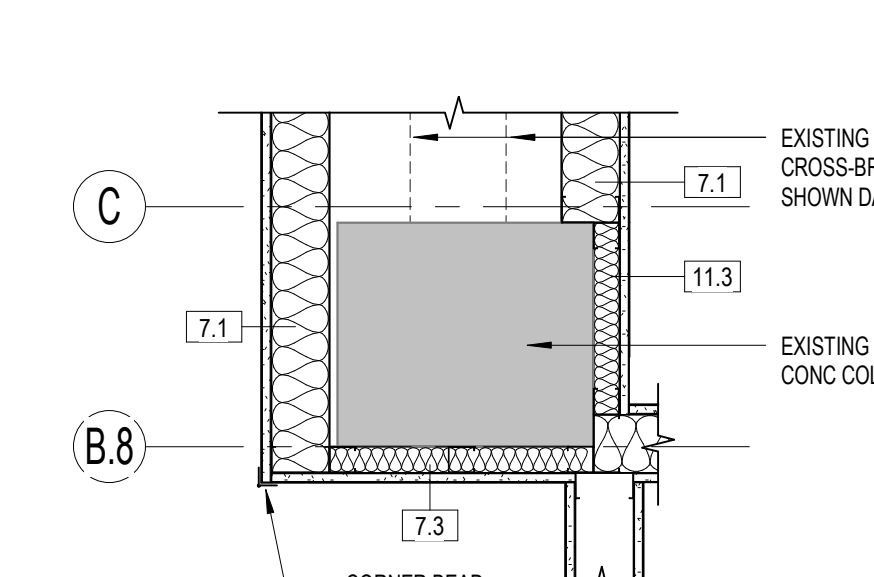


6 COLUMN PLAN DETAIL
1" = 1'-0"

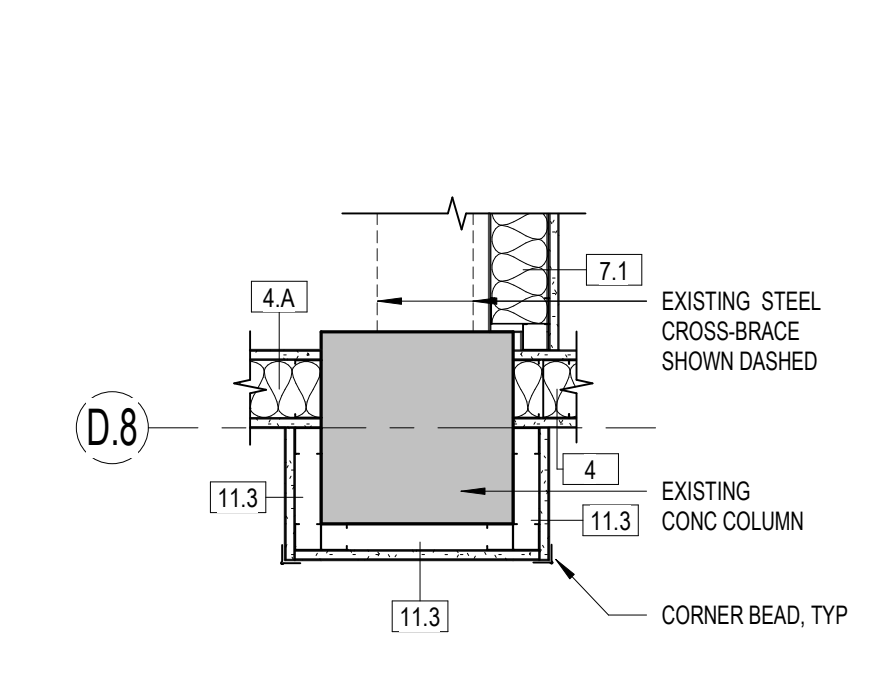


13 COLUMN PLAN DETAIL
1" = 1'-0"

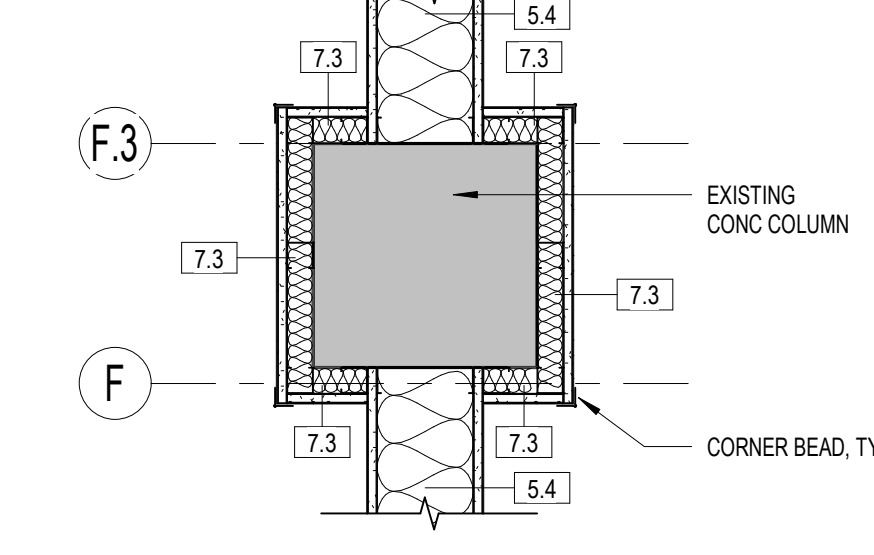


20 COLUMN PLAN DETAIL
1" = 1'-0"

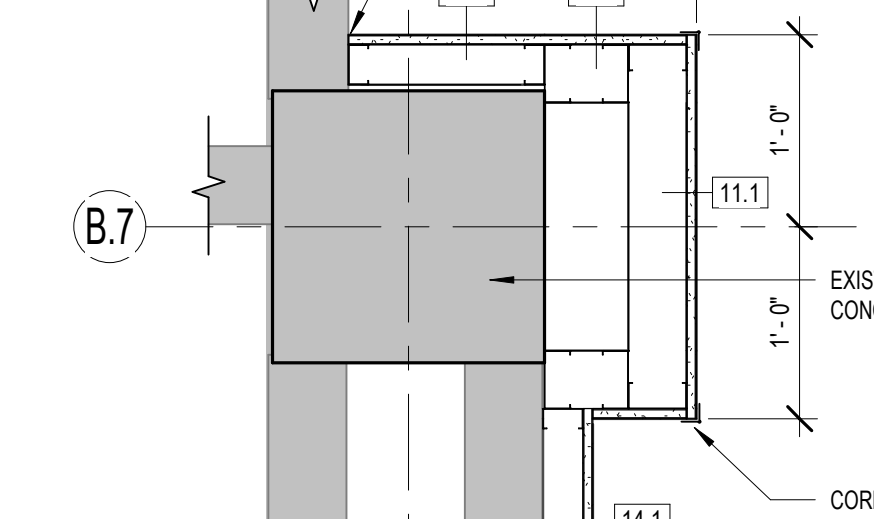


27 COLUMN PLAN DETAIL
1" = 1'-0"

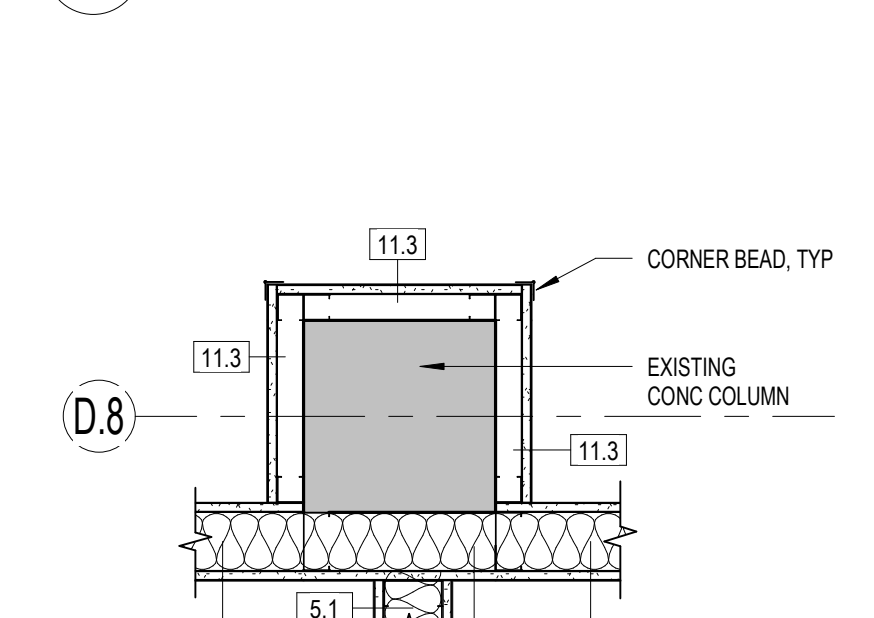


34 COLUMN PLAN DETAIL
1" = 1'-0"

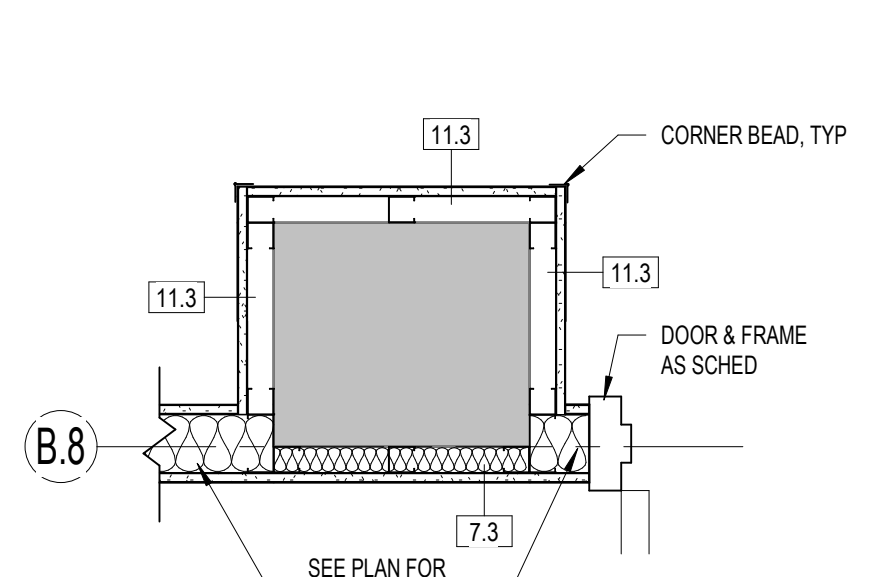


7 COLUMN PLAN DETAIL
1" = 1'-0"

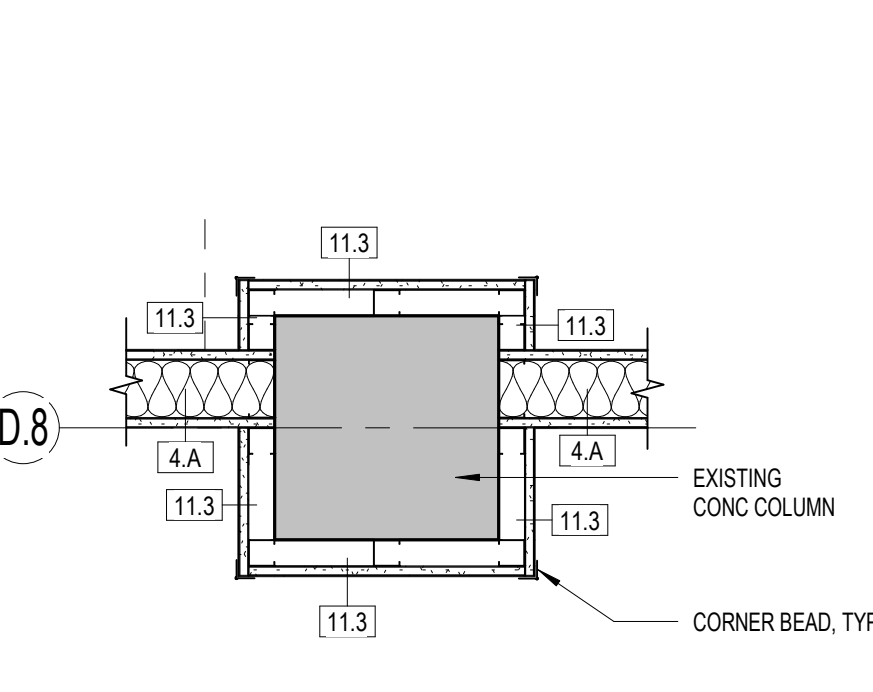


14 COLUMN PLAN DETAIL
1" = 1'-0"

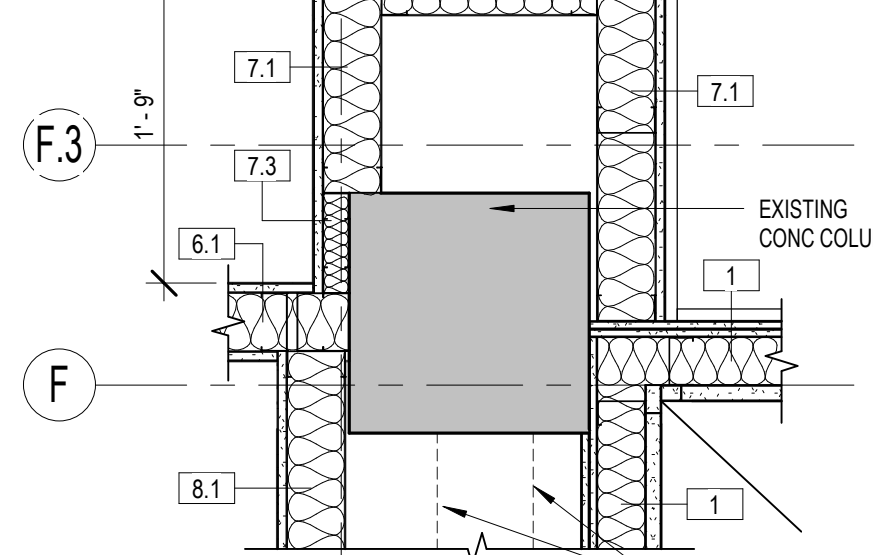

21 COLUMN PLAN DETAIL
1" = 1'-0"

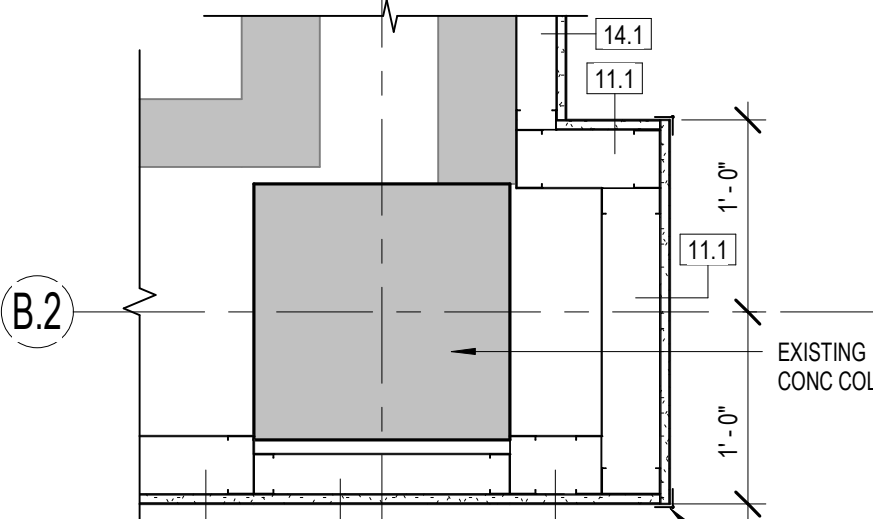

28 COLUMN PLAN DETAIL
1" = 1'-0"

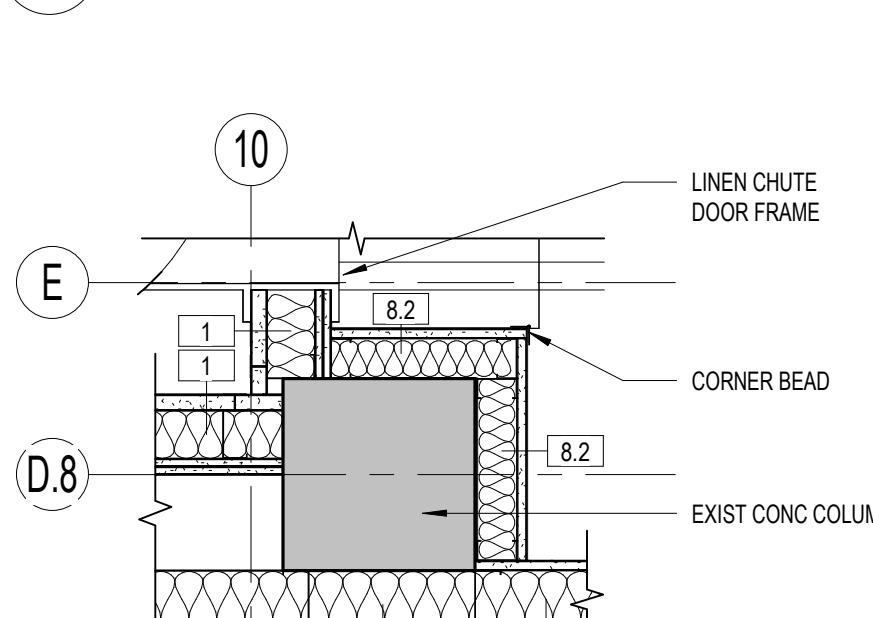


35 COLUMN PLAN DETAIL
1" = 1'-0"

BID DOCUMENTS

NO.	REVISIONS	DATE

CONSULTANT

ARCHITECT/ENGINEER OF RECORD
THOMAS OLESAK, ARCHITECT
MS Lic # 5505
1050 HOYT AVE WEST ST PAUL, MN 55117
952-451-0460

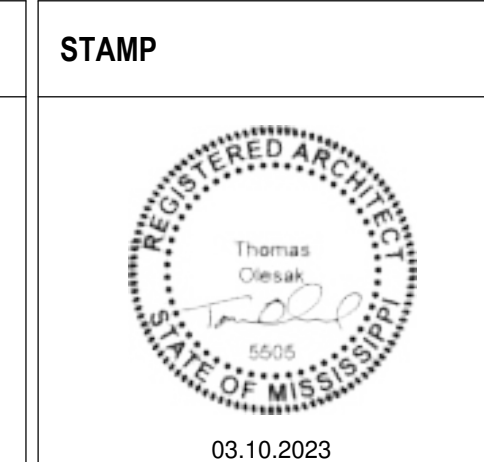


Office of Construction and Facilities Management
U.S. Department of Veterans Affairs

Drawing Title
PLAN DETAILS
Approved:

Phase
CONSTRUCTION DOCUMENTS
FULLY SPRINKLERED


Project Title RENOVATE BUILDING 1	Project Number 520-317X
Location BILOXI, MISSISSIPPI	Building Number 1
Issue Date 03/10/2023	Drawing Number AE402
Checked LA	Drawn CD, PC
Dwg. 93 of 238	

C:\Users\pjd\Documents\15950 - VAHC-Bldg Building 1_R21 - Central model_Yunyoung.nxd 3/19/2025 10:32:33 AM

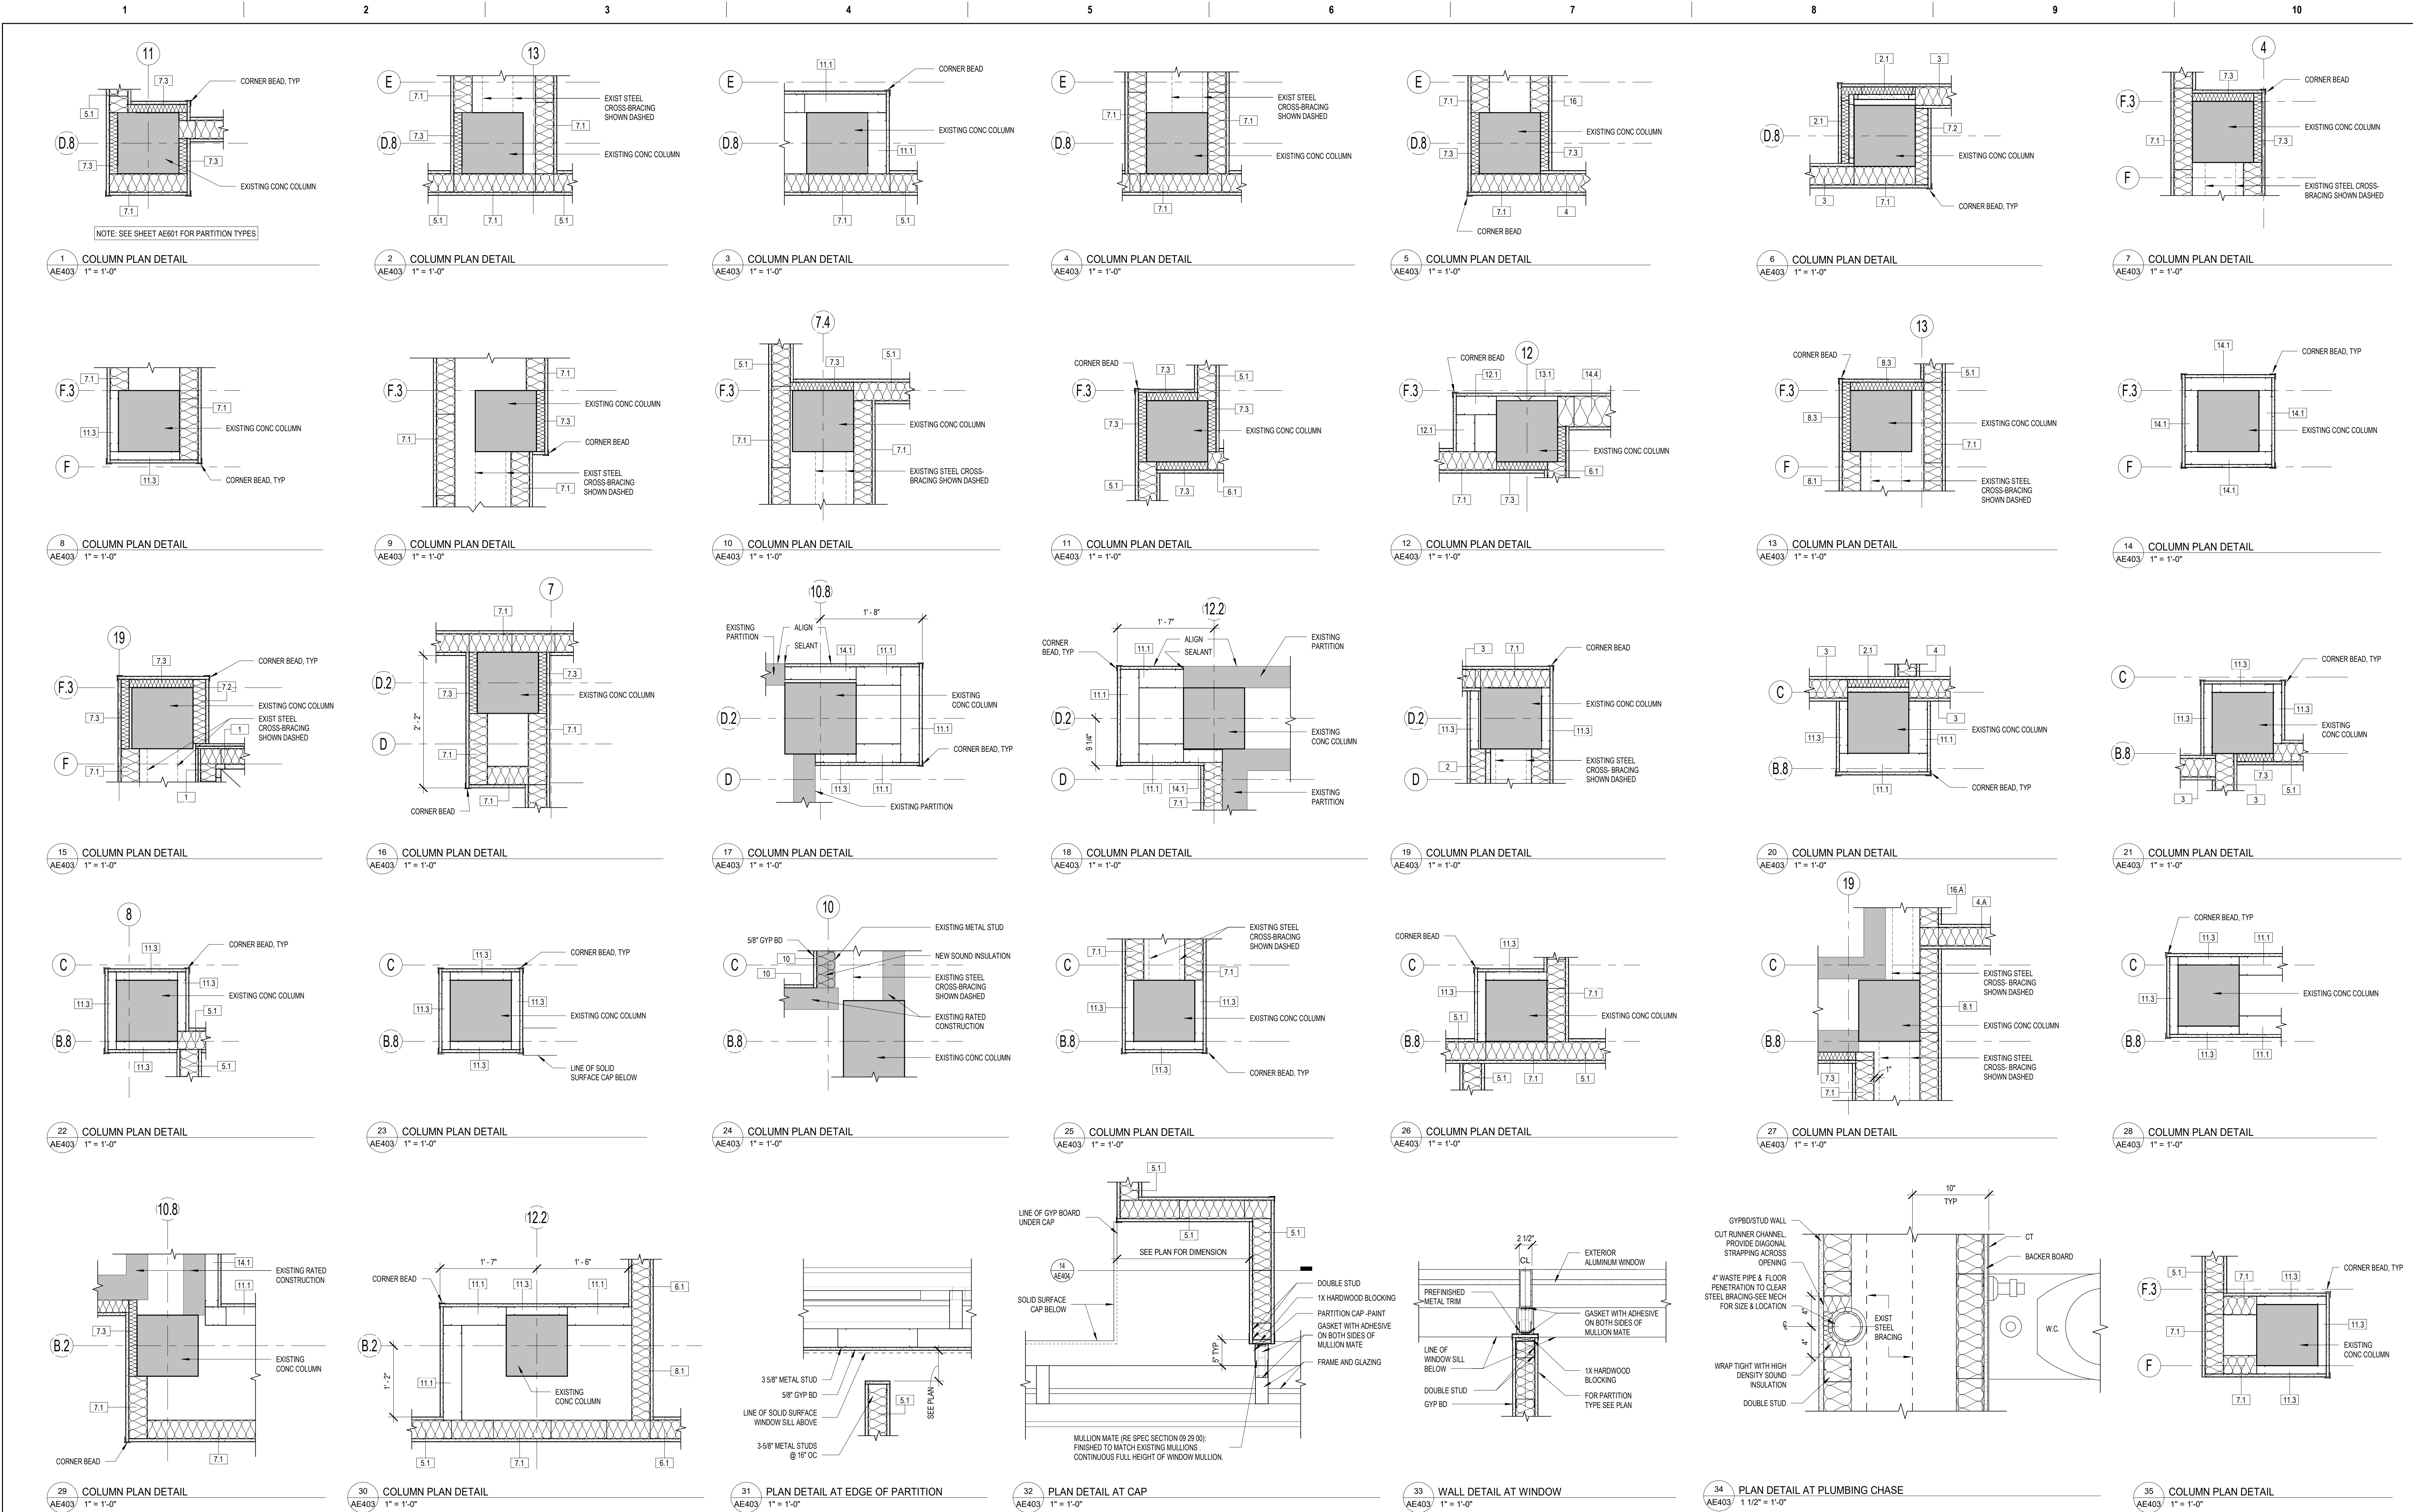

BID DOCUMENTS

			CONSULTANT	ARCHITECT/ENGINEER OF RECORD	STAMP	Office of Construction and Facilities Management	Drawing Title PLAN DETAILS	Phase CONSTRUCTION DOCUMENTS	Project Title RENOVATE BUILDING 1	Project Number 520-317X
				THOMAS OLESAK, ARCHITECT		U.S. Department of Veterans Affairs	Approved:	FULLY SPRINKLERED	Location BILOXI, MISSISSIPPI	Building Number 1
			MS Lic # 5505	Issue Date 03/10/2023						Drawing Number AE403
			1050 HOYT AVE WEST ST PAUL, MN 55117 952-451-0460	Checked LA						Dwg. 94 of 238

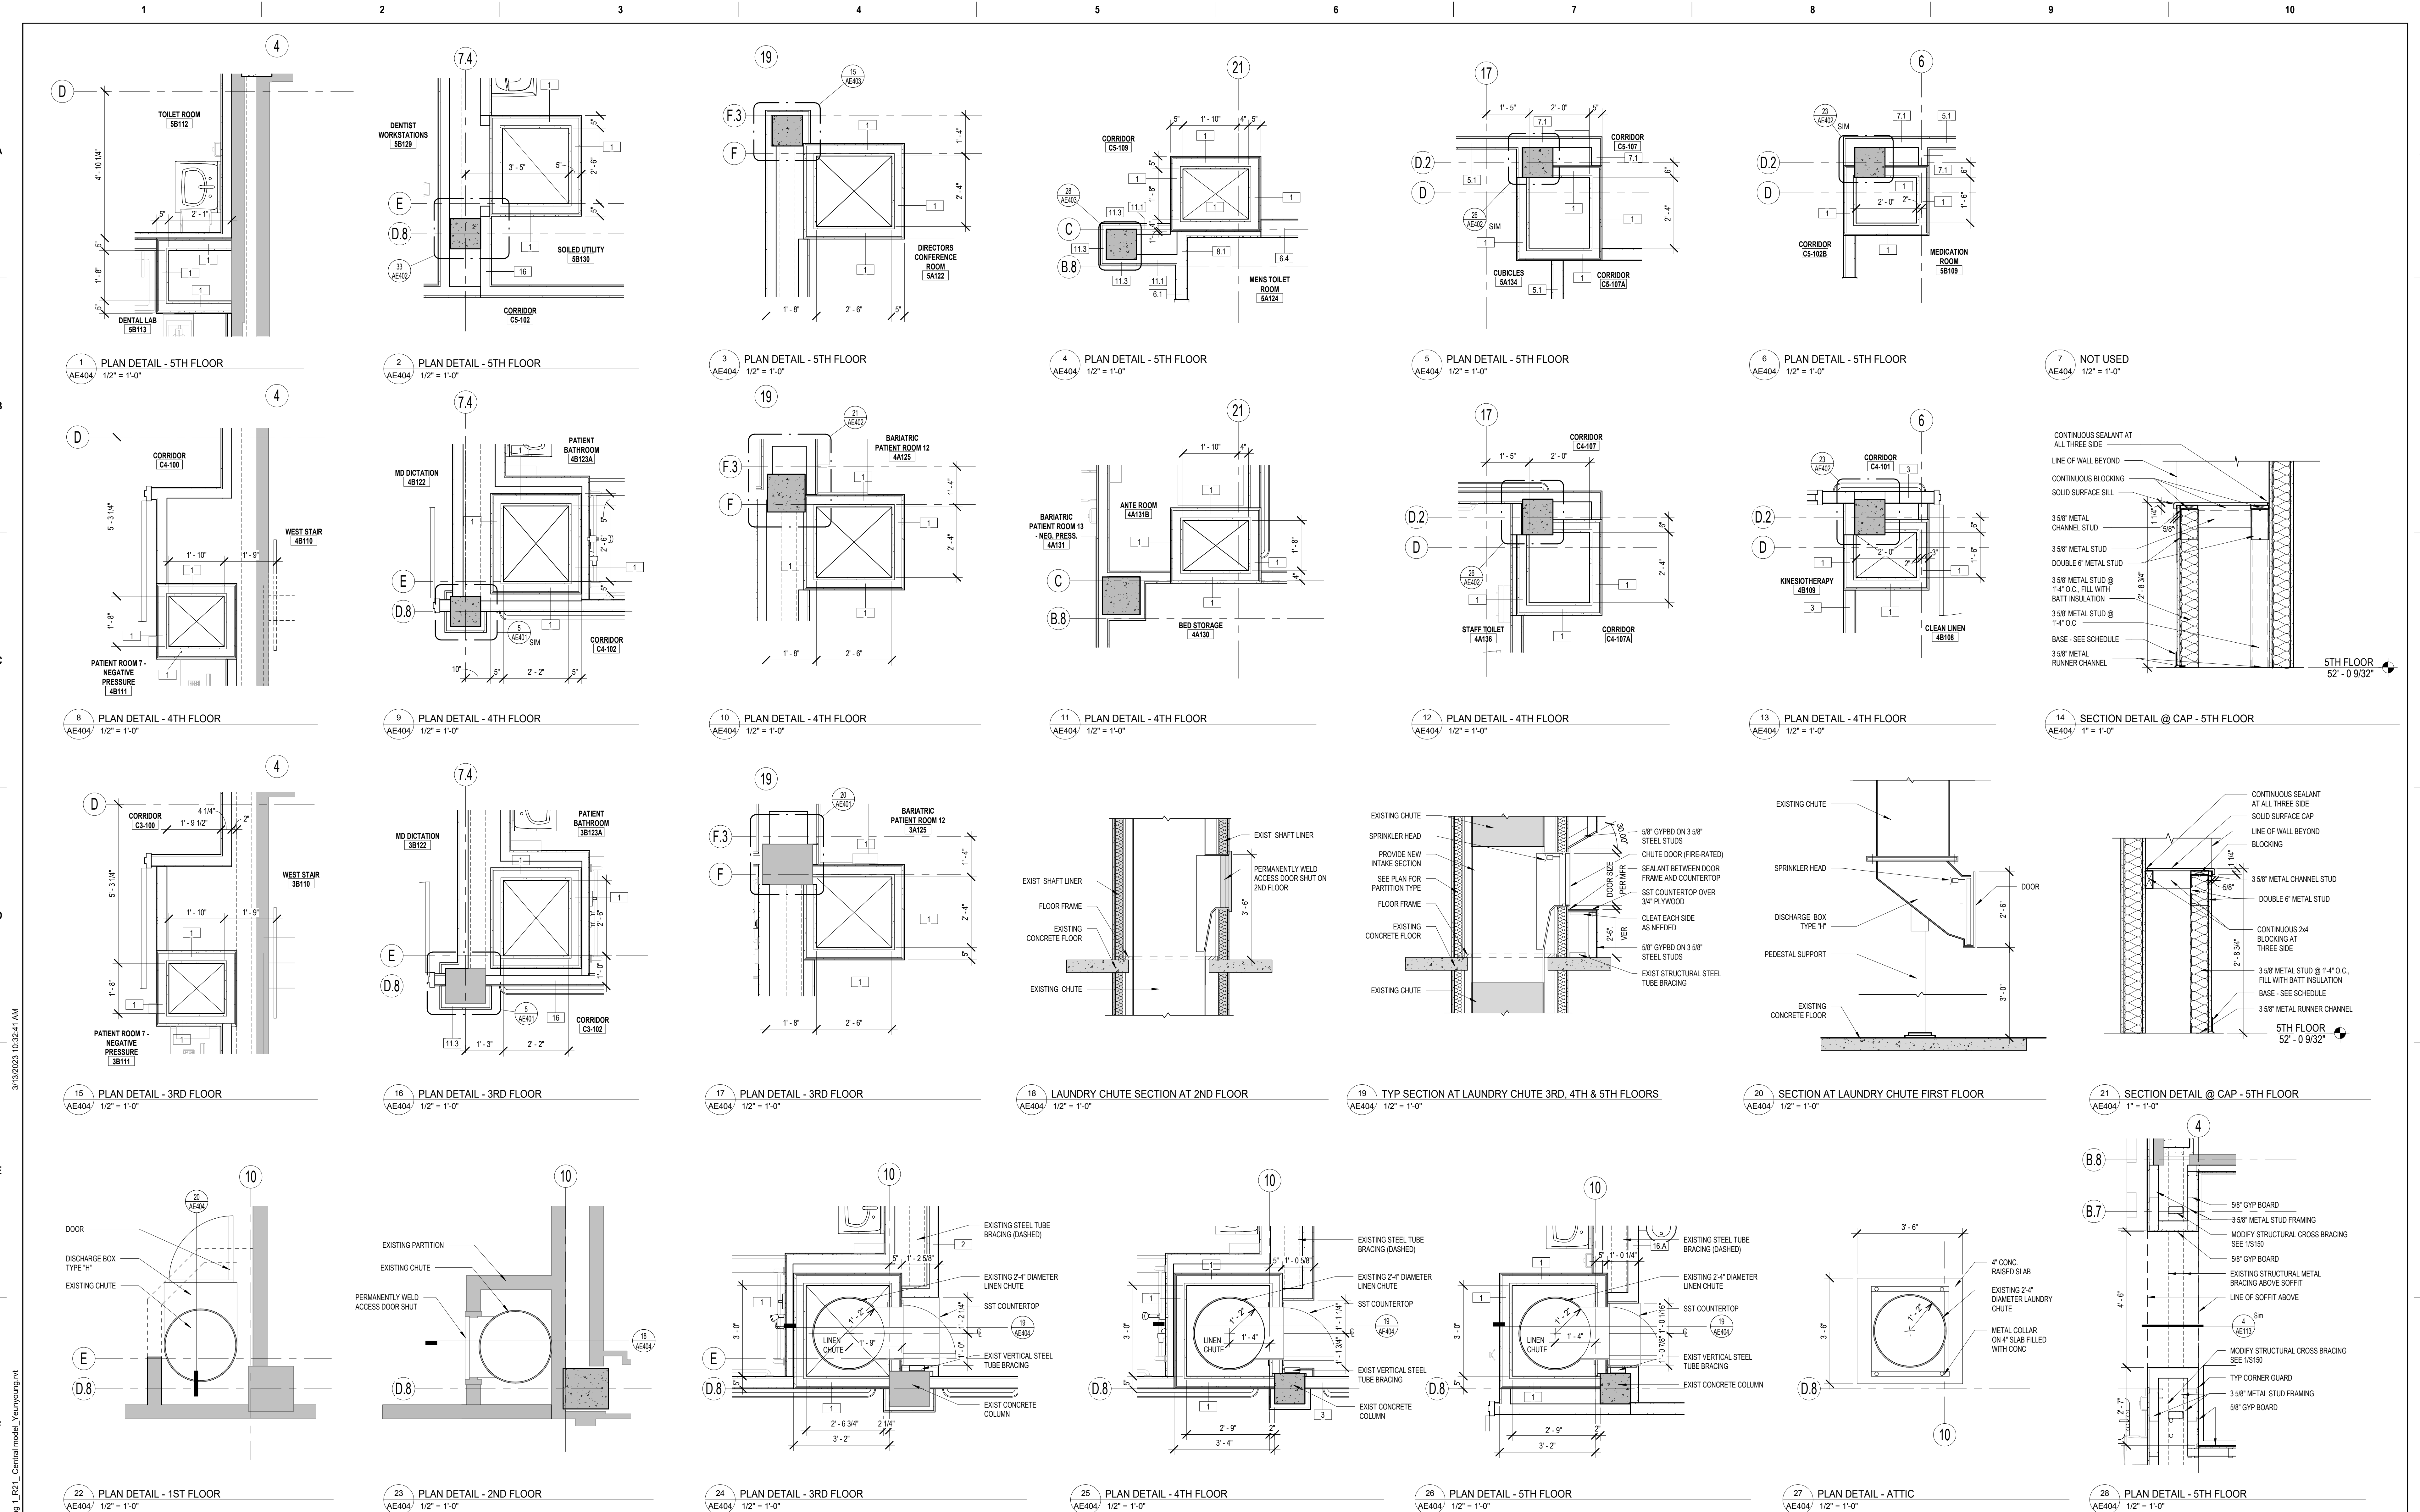

BID DOCUMENTS

NO.	REVISIONS	DATE

CONSULTANT

ARCHITECT/ENGINEER OF RECORD
THOMAS OLESAK, ARCHITECT
MS Lic # 5505
1050 HOYT AVE WEST ST PAUL, MN 55117
952-451-0460

STAMP
REGISTERED ARCHITECT
Thomas Olesak
STATE OF MISSISSIPPI
03.10.2023

Office of Construction and Facilities Management
U.S. Department of Veterans Affairs

Drawing Title
PLAN AND SECTION DETAILS
Approved:

Phase
CONSTRUCTION DOCUMENTS
FULLY SPRINKLERED

Project Title
RENOVATE BUILDING 1
Location
BILOXI, MISSISSIPPI
Issue Date
03/10/2023
Checked
LA
Drawn
CD, PC

Project Number
520-317X
Building Number
1
Drawing Number
AE404
Dwg. 95 of 238

A

B

C


D

E


F

5/26/2023 11:12:24 AM


C:\Users\pjd\Documents\15950 - VAAC-Bldg Building 1_R21 - Central.mxd_Yunyoung.nxd

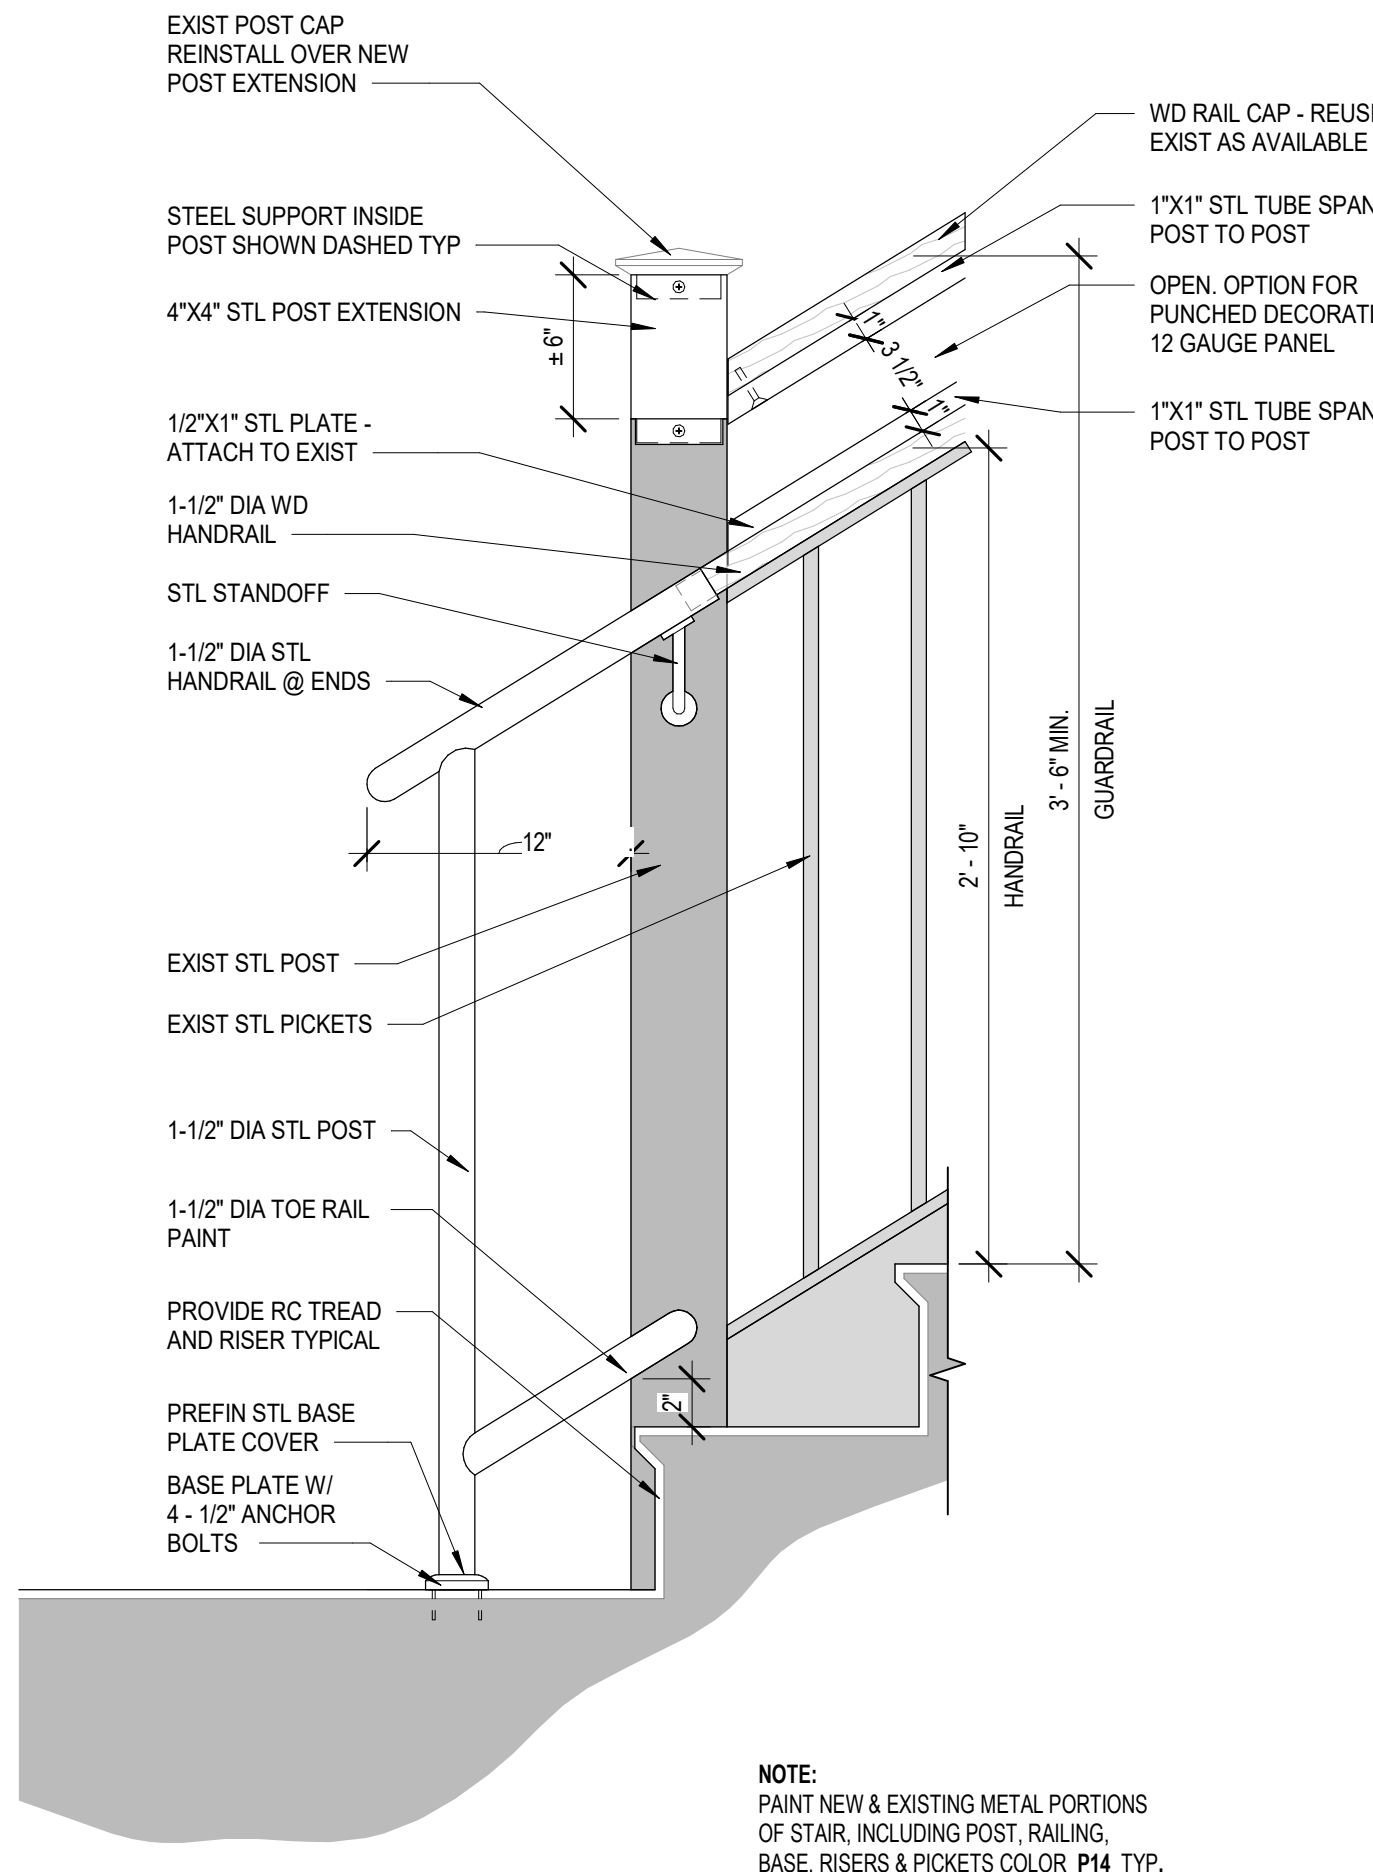


1 TYP STAIR LANDING DETAIL
AE501/ 1 1/2" = 1'-0"

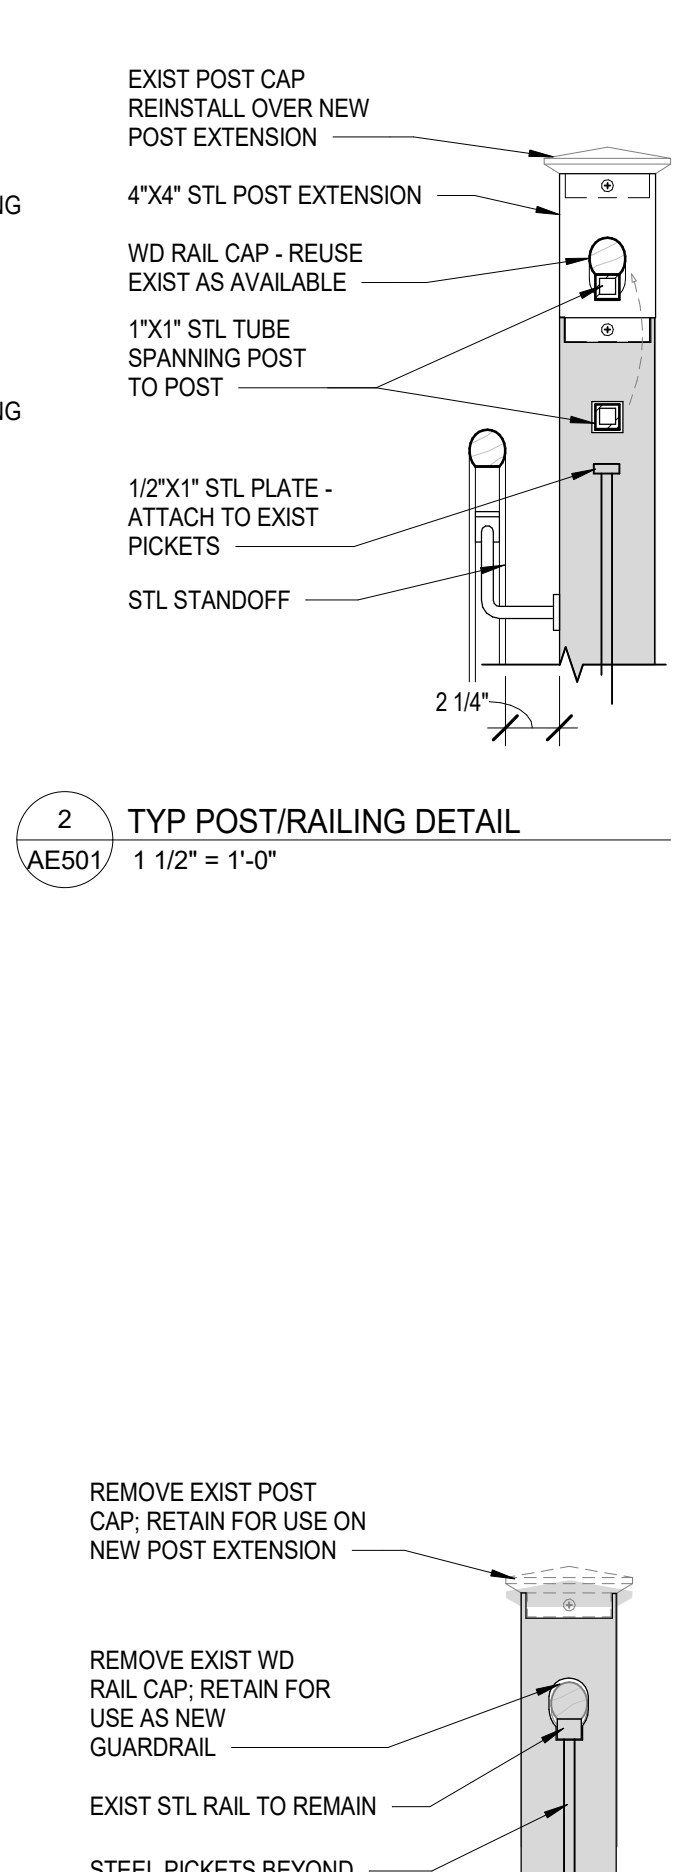


2 TYP POST/RAILING DETAIL
AE501/ 1 1/2" = 1'-0"

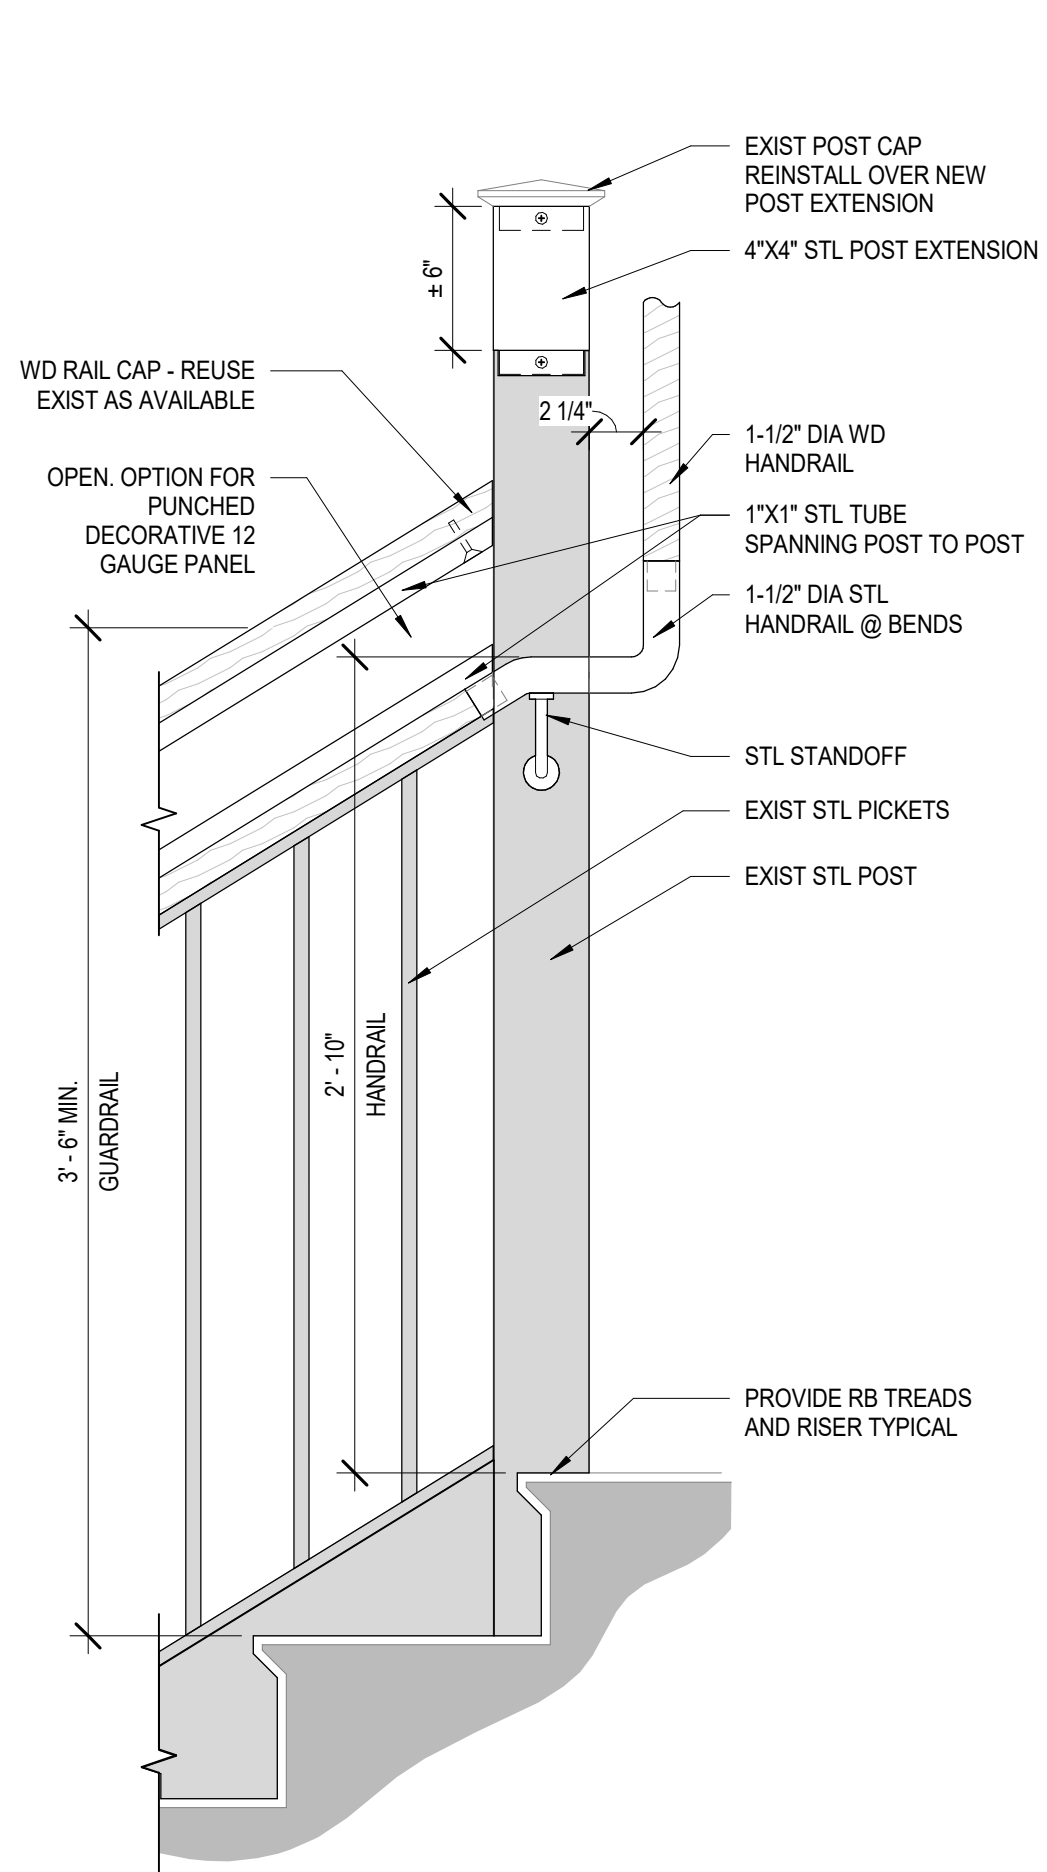


4 TYP STAIR RAIL DETAIL
AE501/ 1 1/2" = 1'-0"

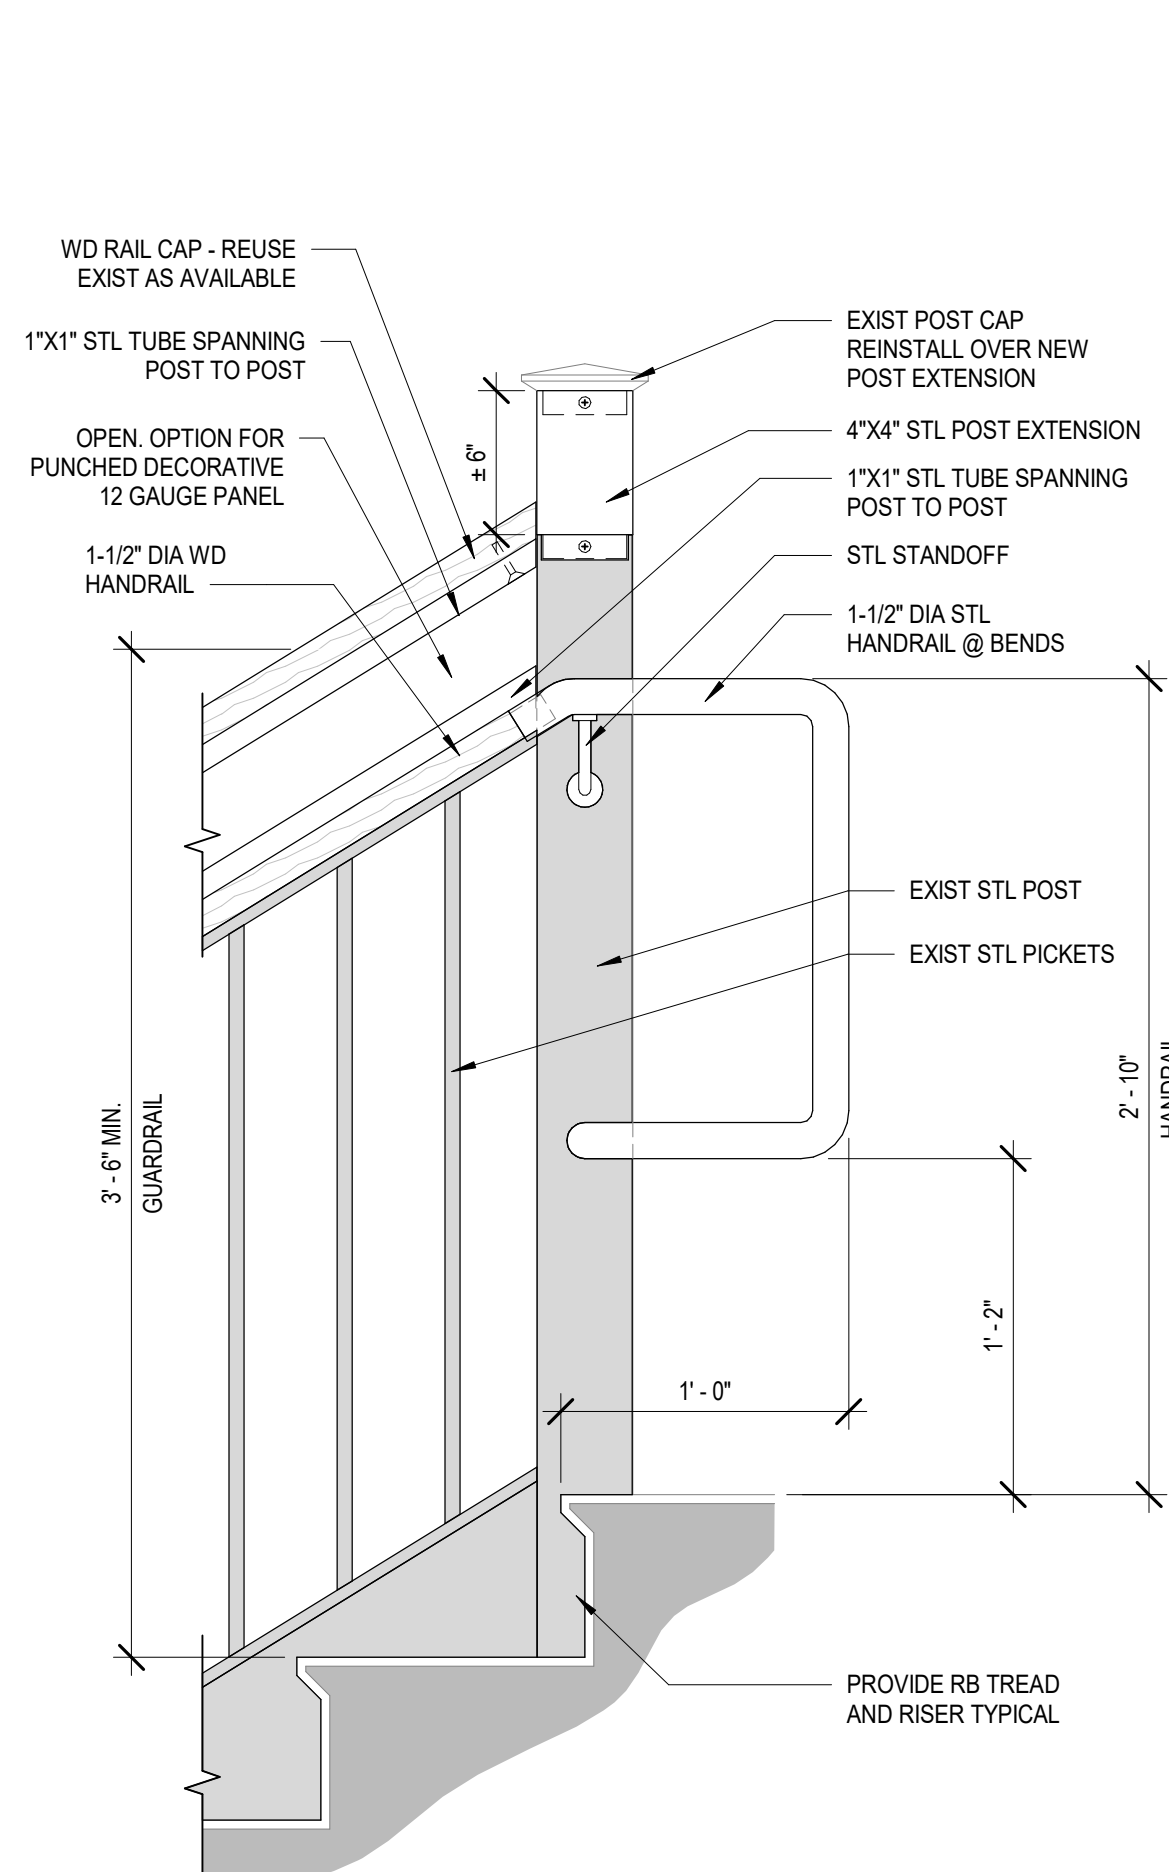


5 TYP STAIR RAIL DETAIL
AE501/ 1 1/2" = 1'-0"

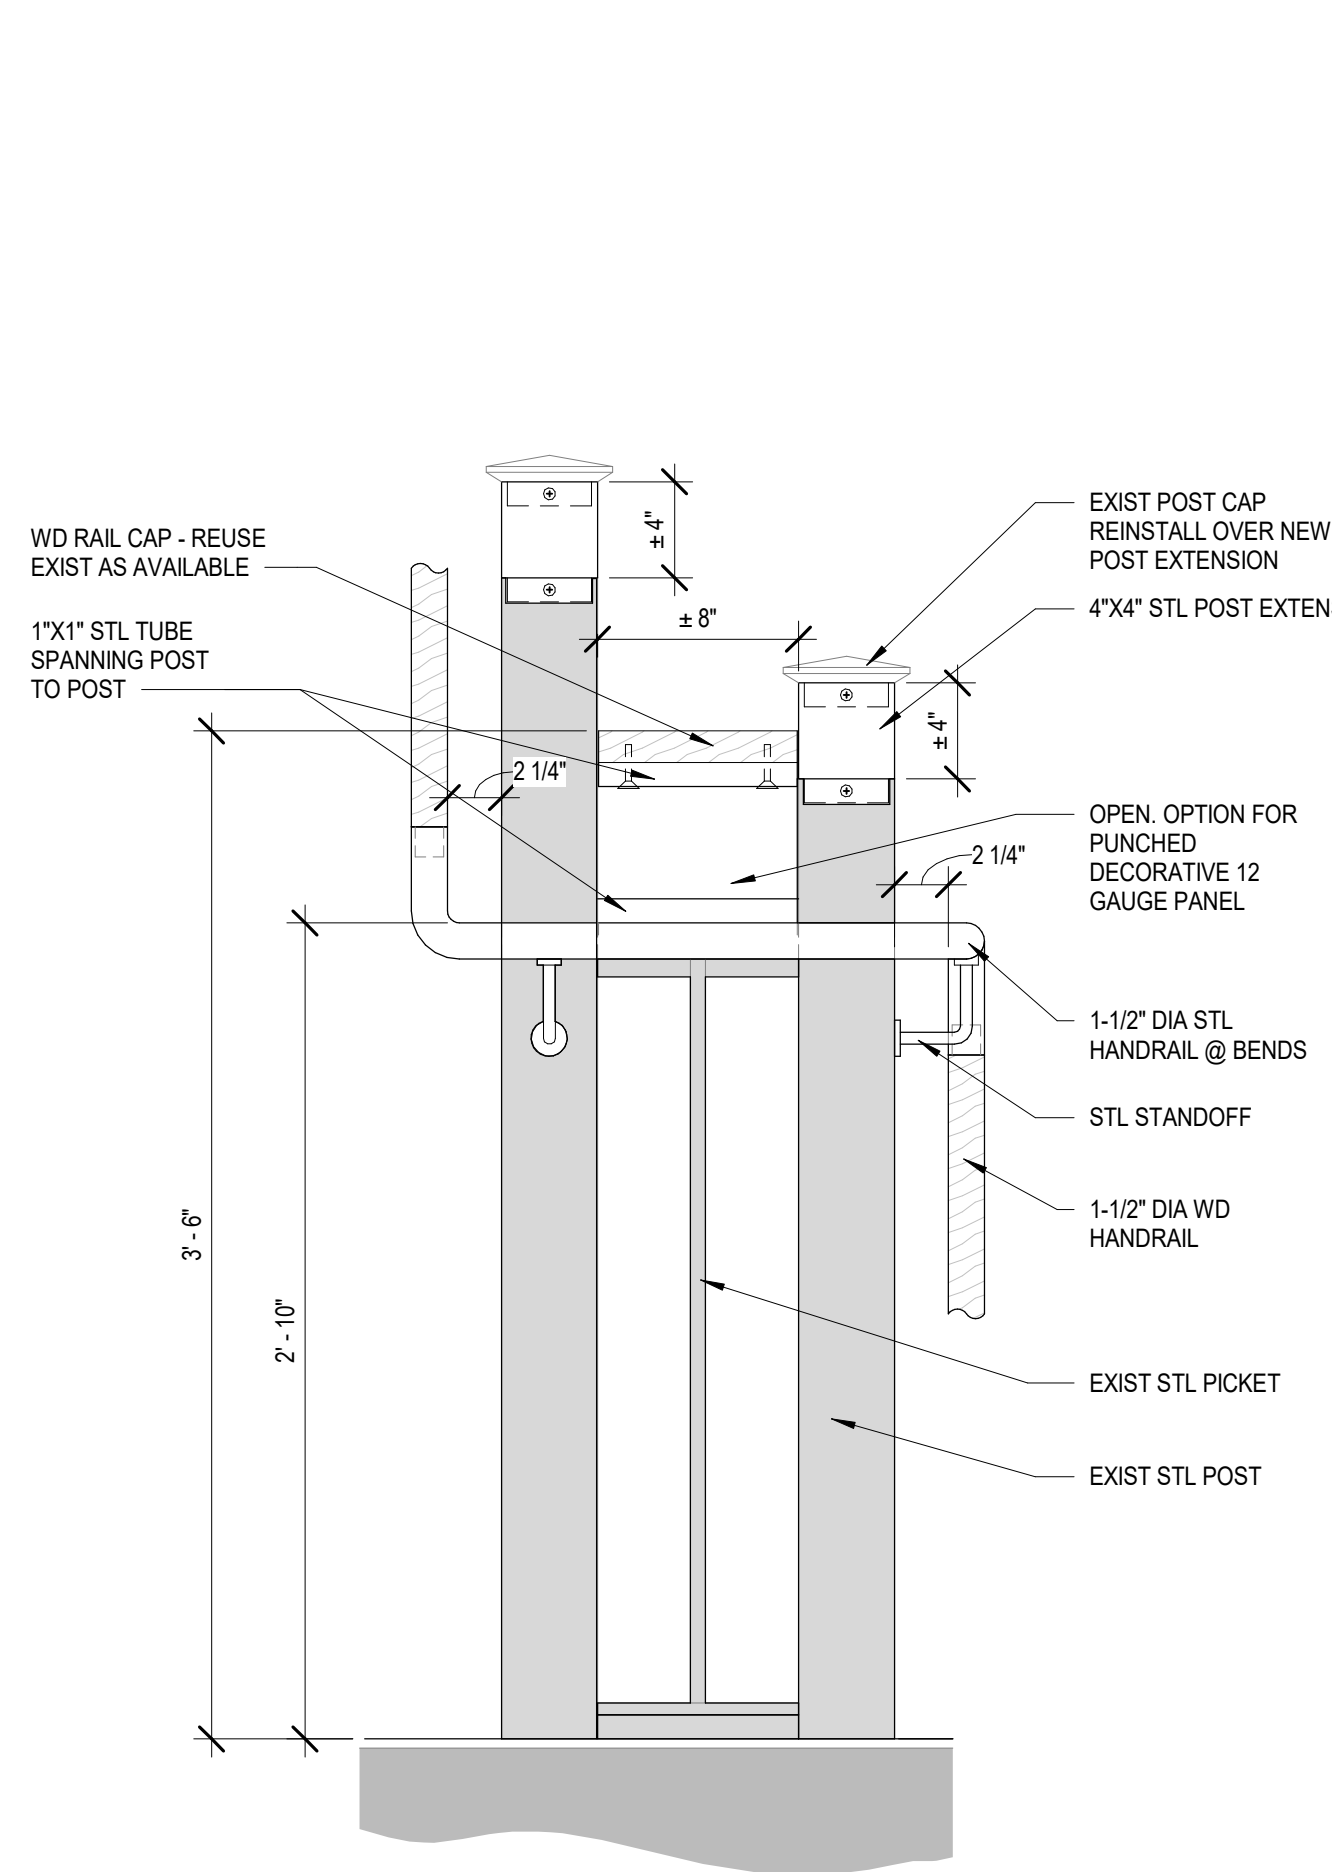


6 TYP STAIR RAIL DETAIL
AE501/ 1 1/2" = 1'-0"

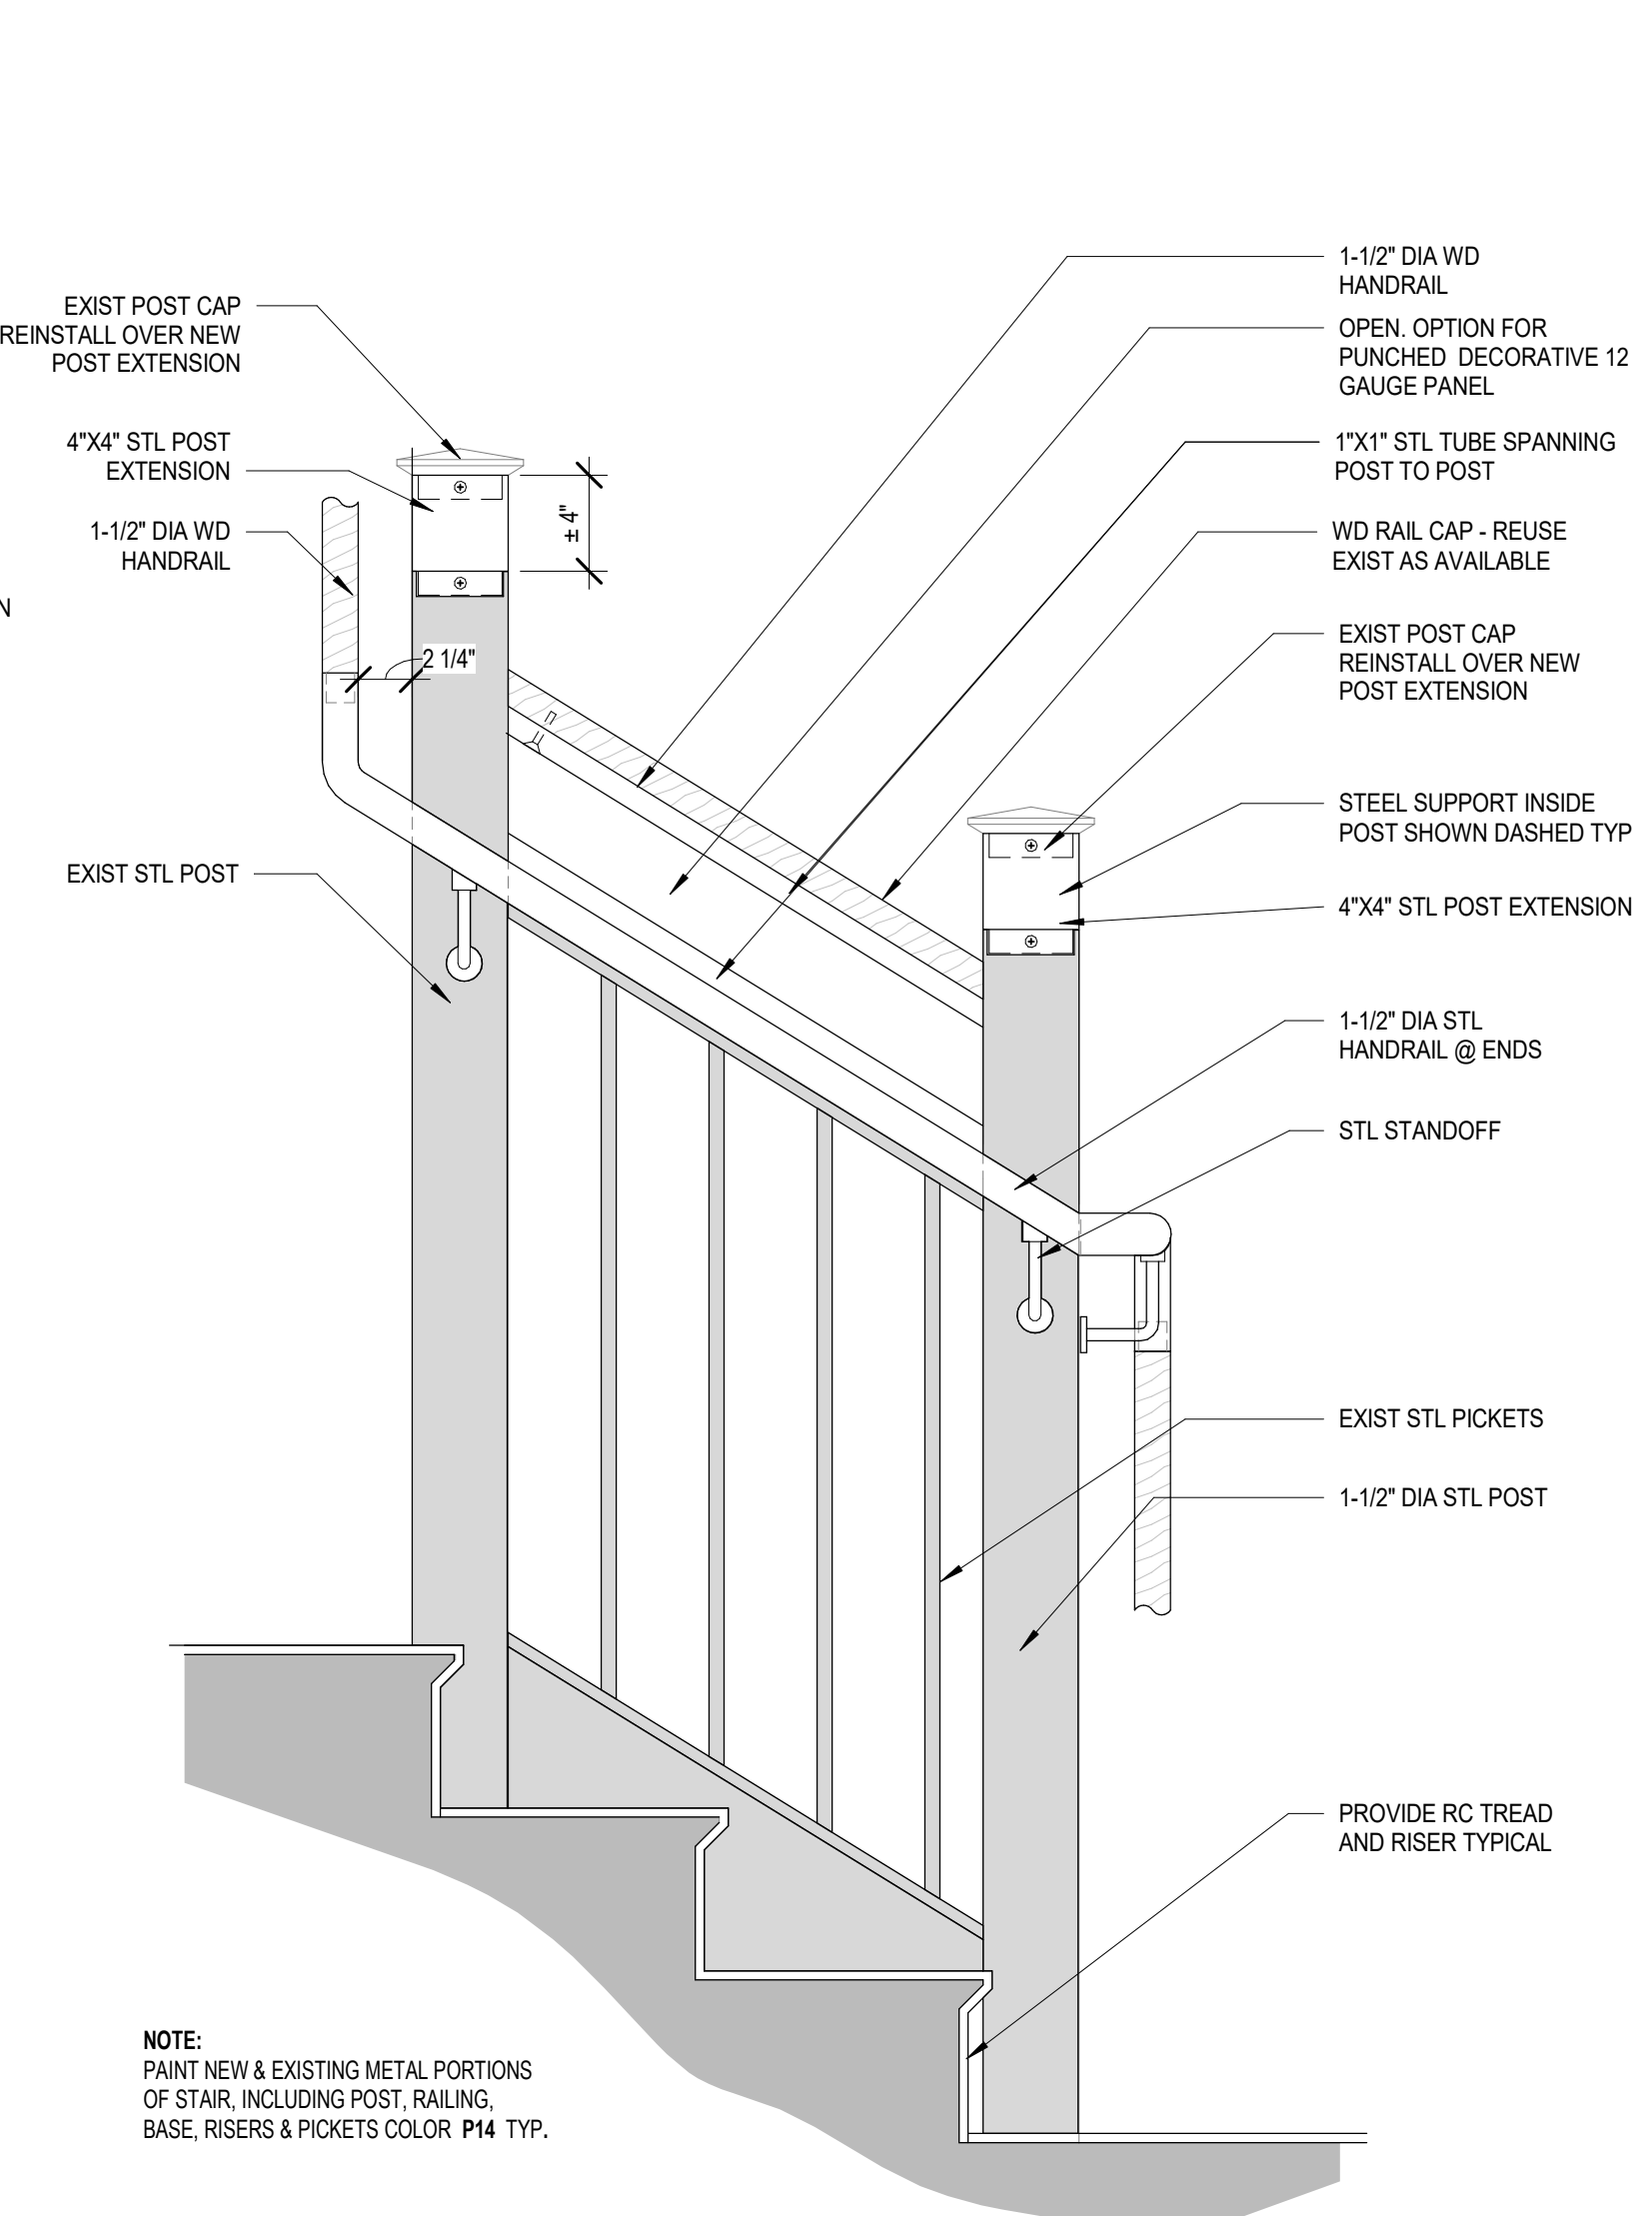



7 TYP STAIR LANDING DETAIL
AE501/ 1 1/2" = 1'-0"

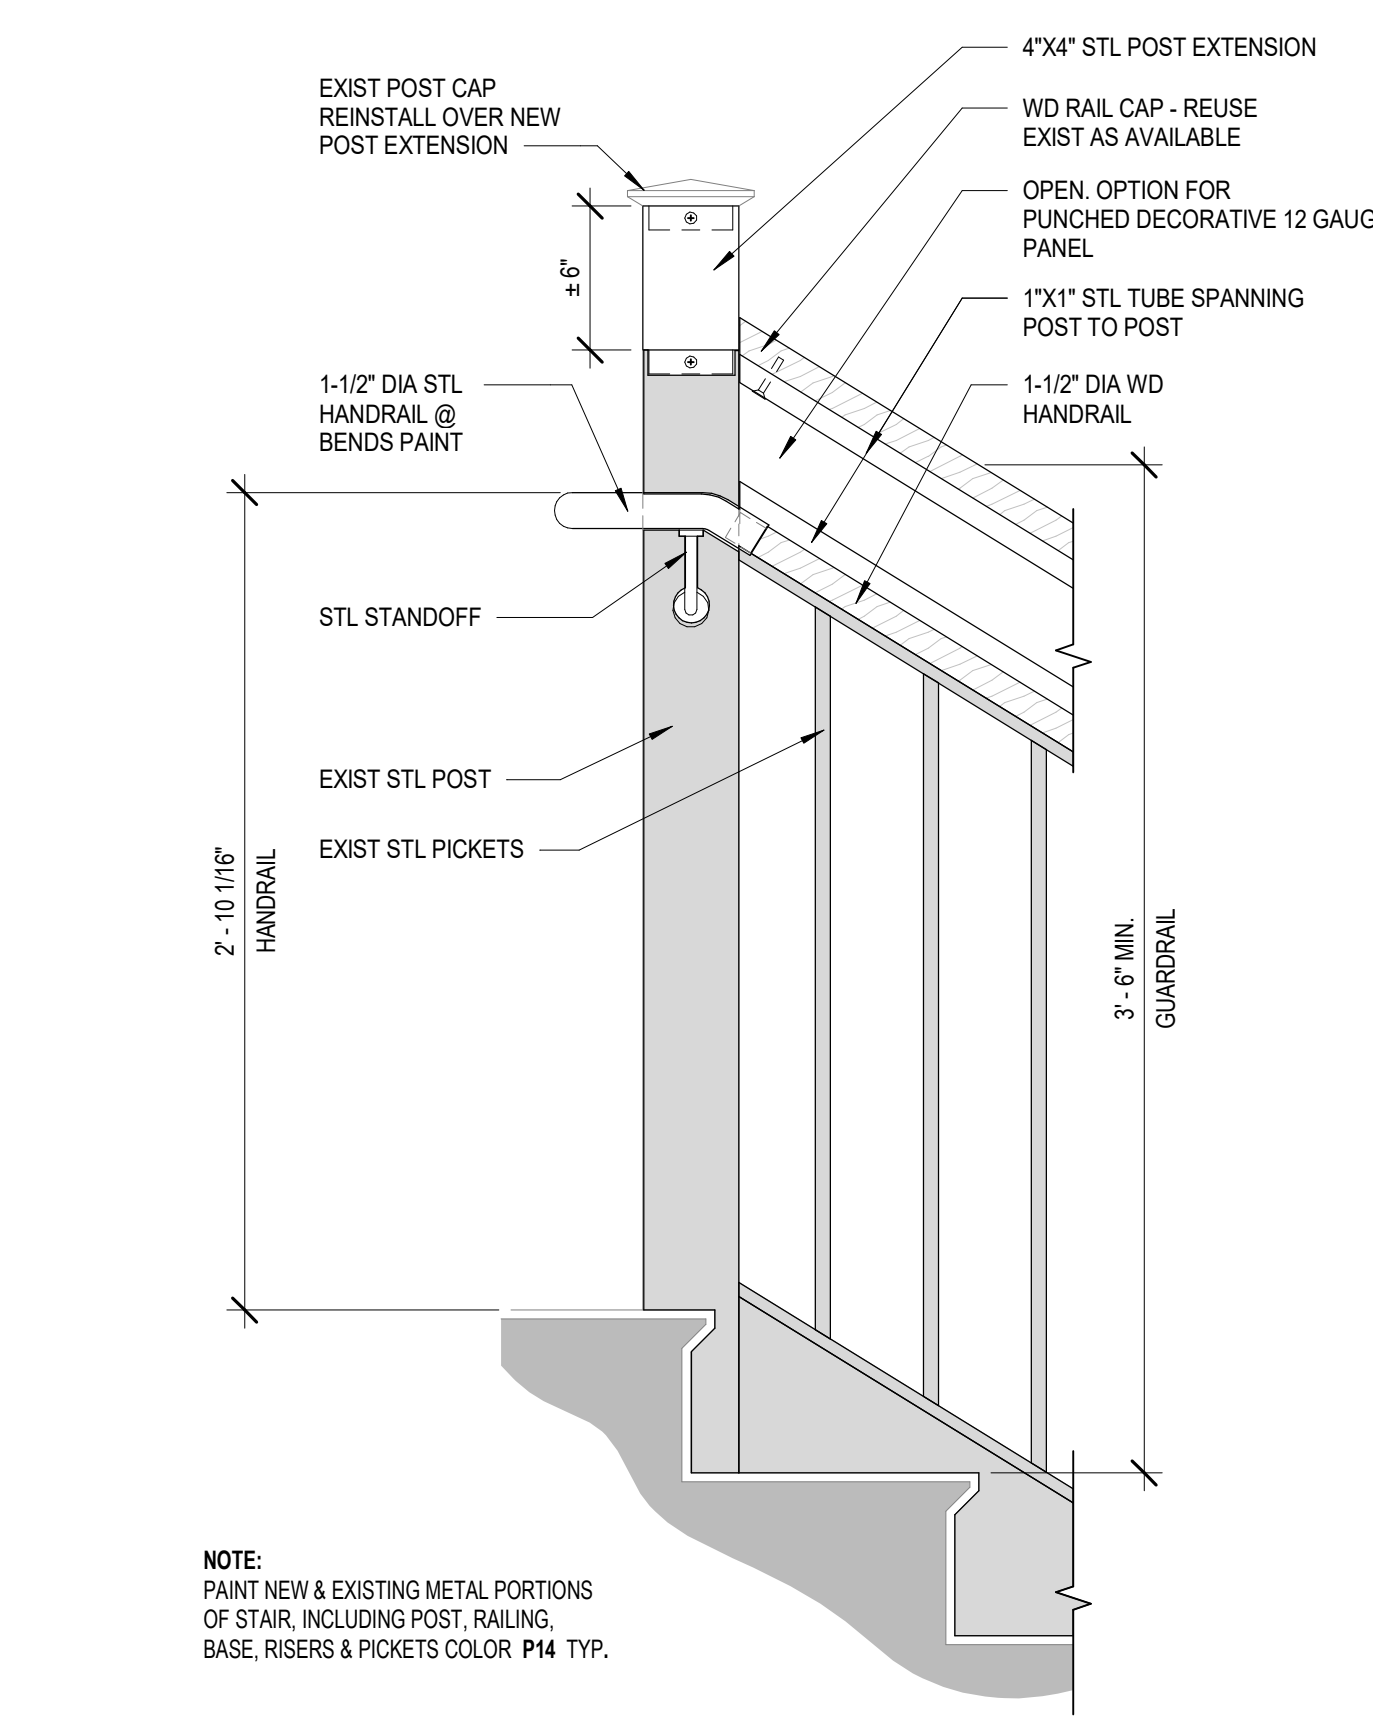

8 TYP STAIR RAIL DETAIL
AE501/ 1 1/2" = 1'-0"

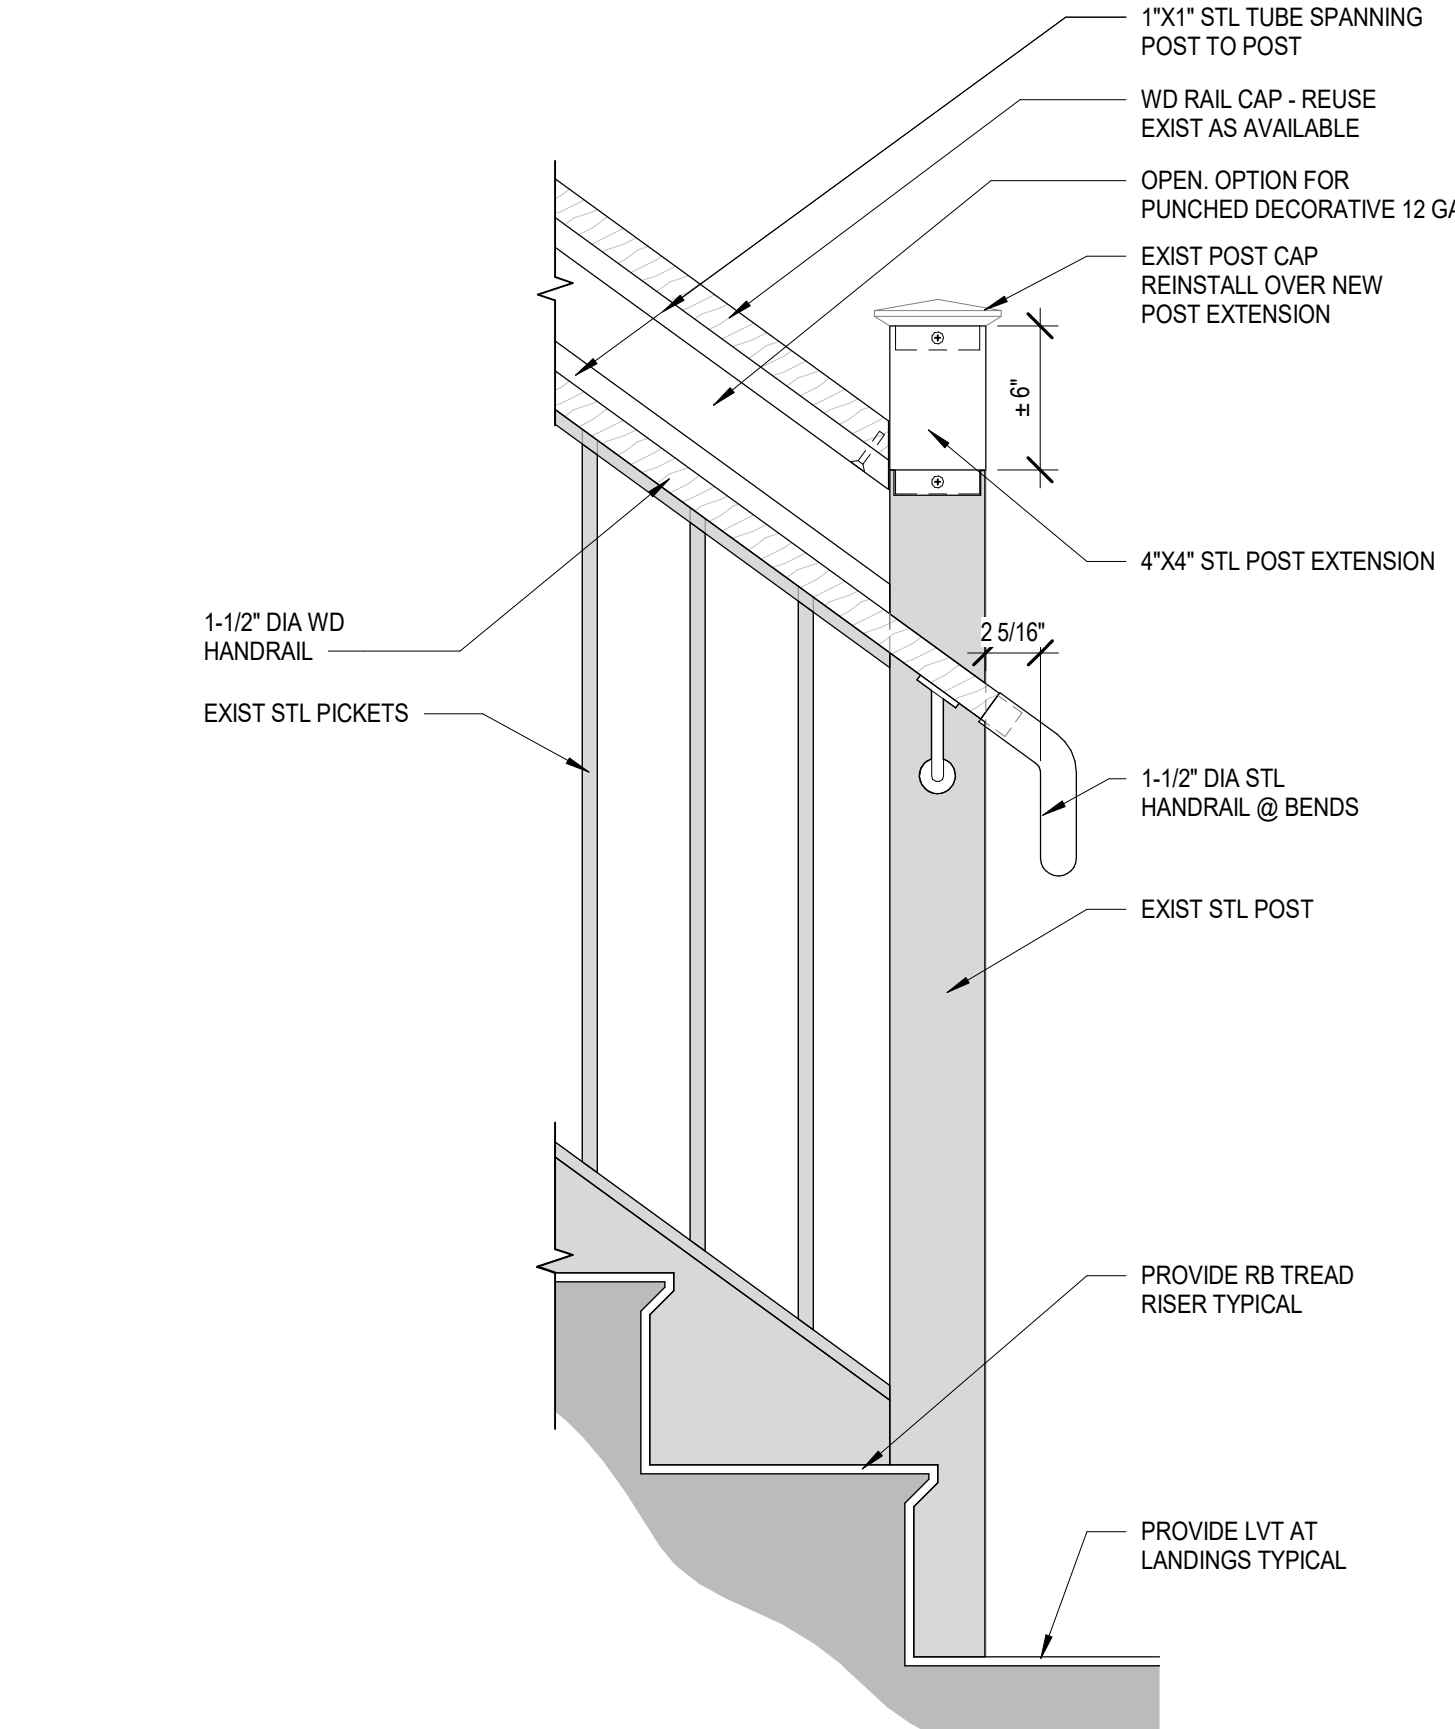


9 TYP STAIR RAIL DETAIL
AE501/ 1 1/2" = 1'-0"

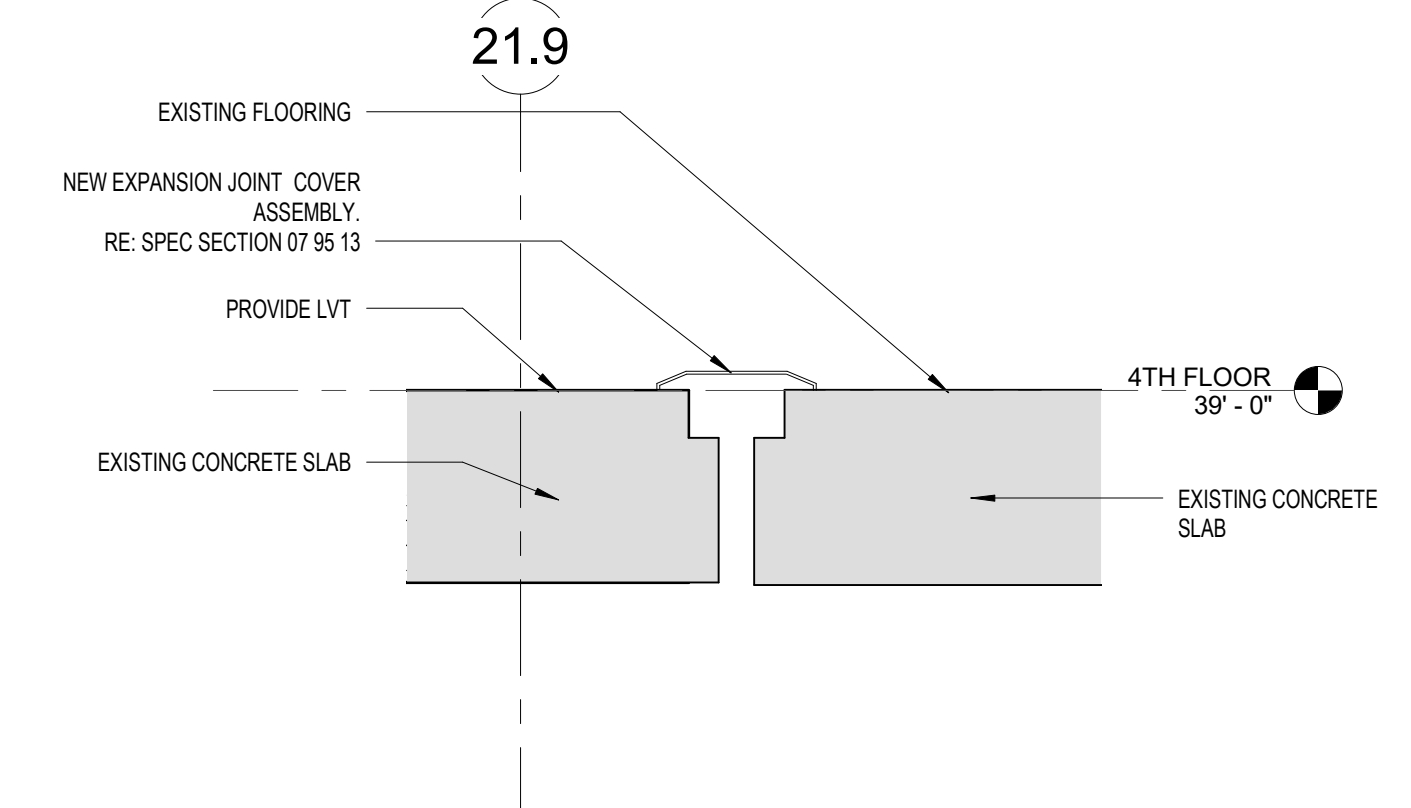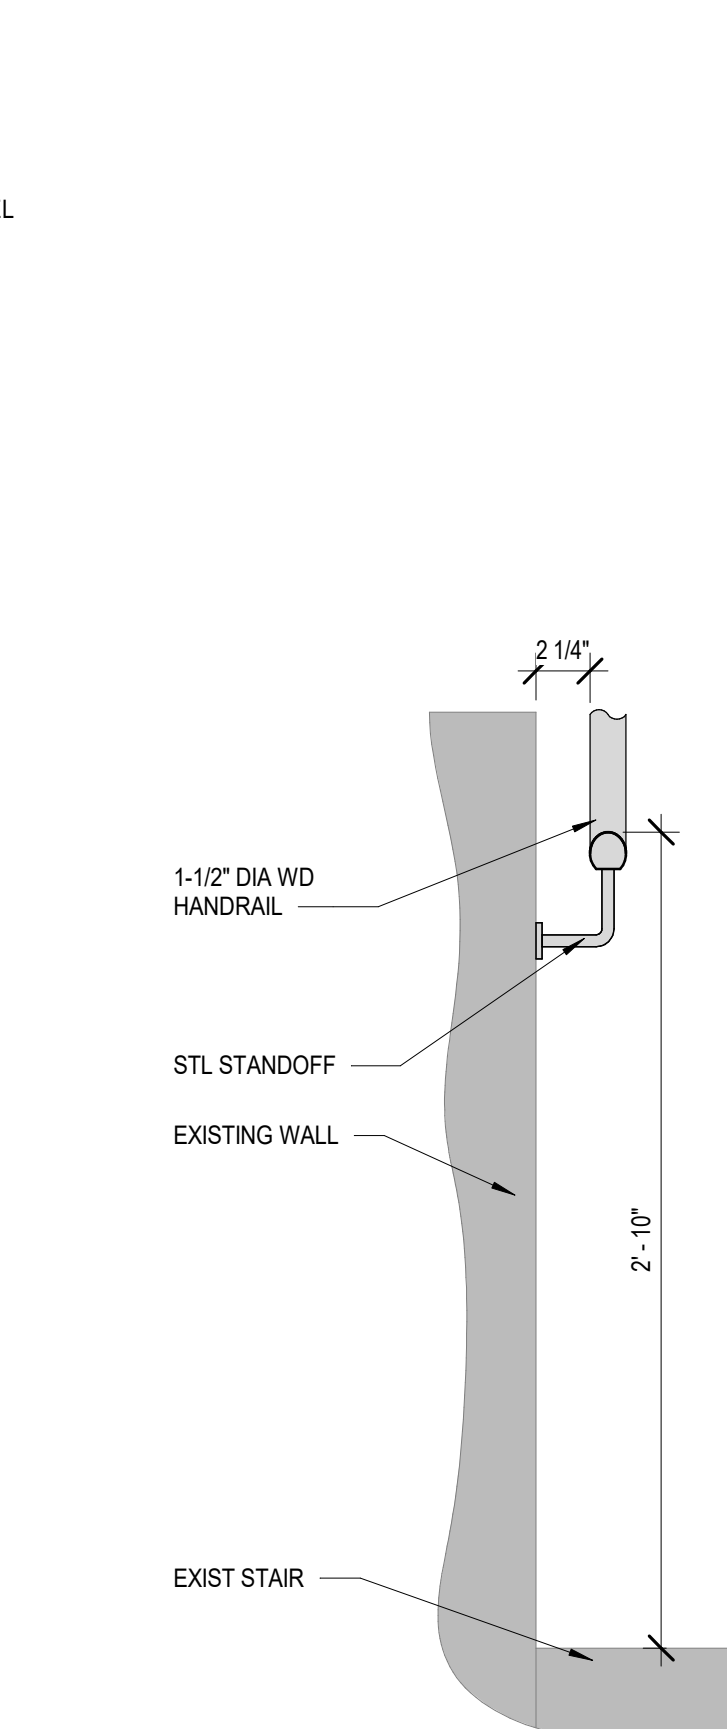

NO.	REVISIONS	DATE

CONSULTANT

ARCHITECT/ENGINEER OF RECORD
THOMAS OLESAK, ARCHITECT
MS Lic # 5505
1050 HOYT AVE WEST ST PAUL, MN 55117
952-451-0460

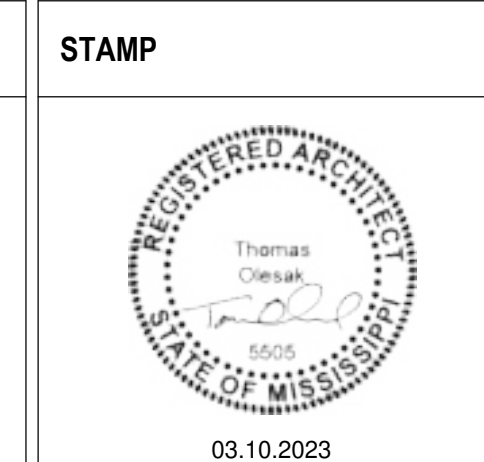

Office of Construction and Facilities Management
VA U.S. Department of Veterans Affairs


Drawing Title
STAIR SECTION DETAILS
Approved:

Phase
CONSTRUCTION DOCUMENTS
FULLY SPRINKLERED

Project Title RENOVATE BUILDING 1	Project Number 520-317X
Location BILOXI, MISSISSIPPI	Building Number 1
Issue Date 03/10/2023	Checked LA
Drawn CD	Drawing Number AE501
Dwg. 96 of 238	


BID DOCUMENTS

A

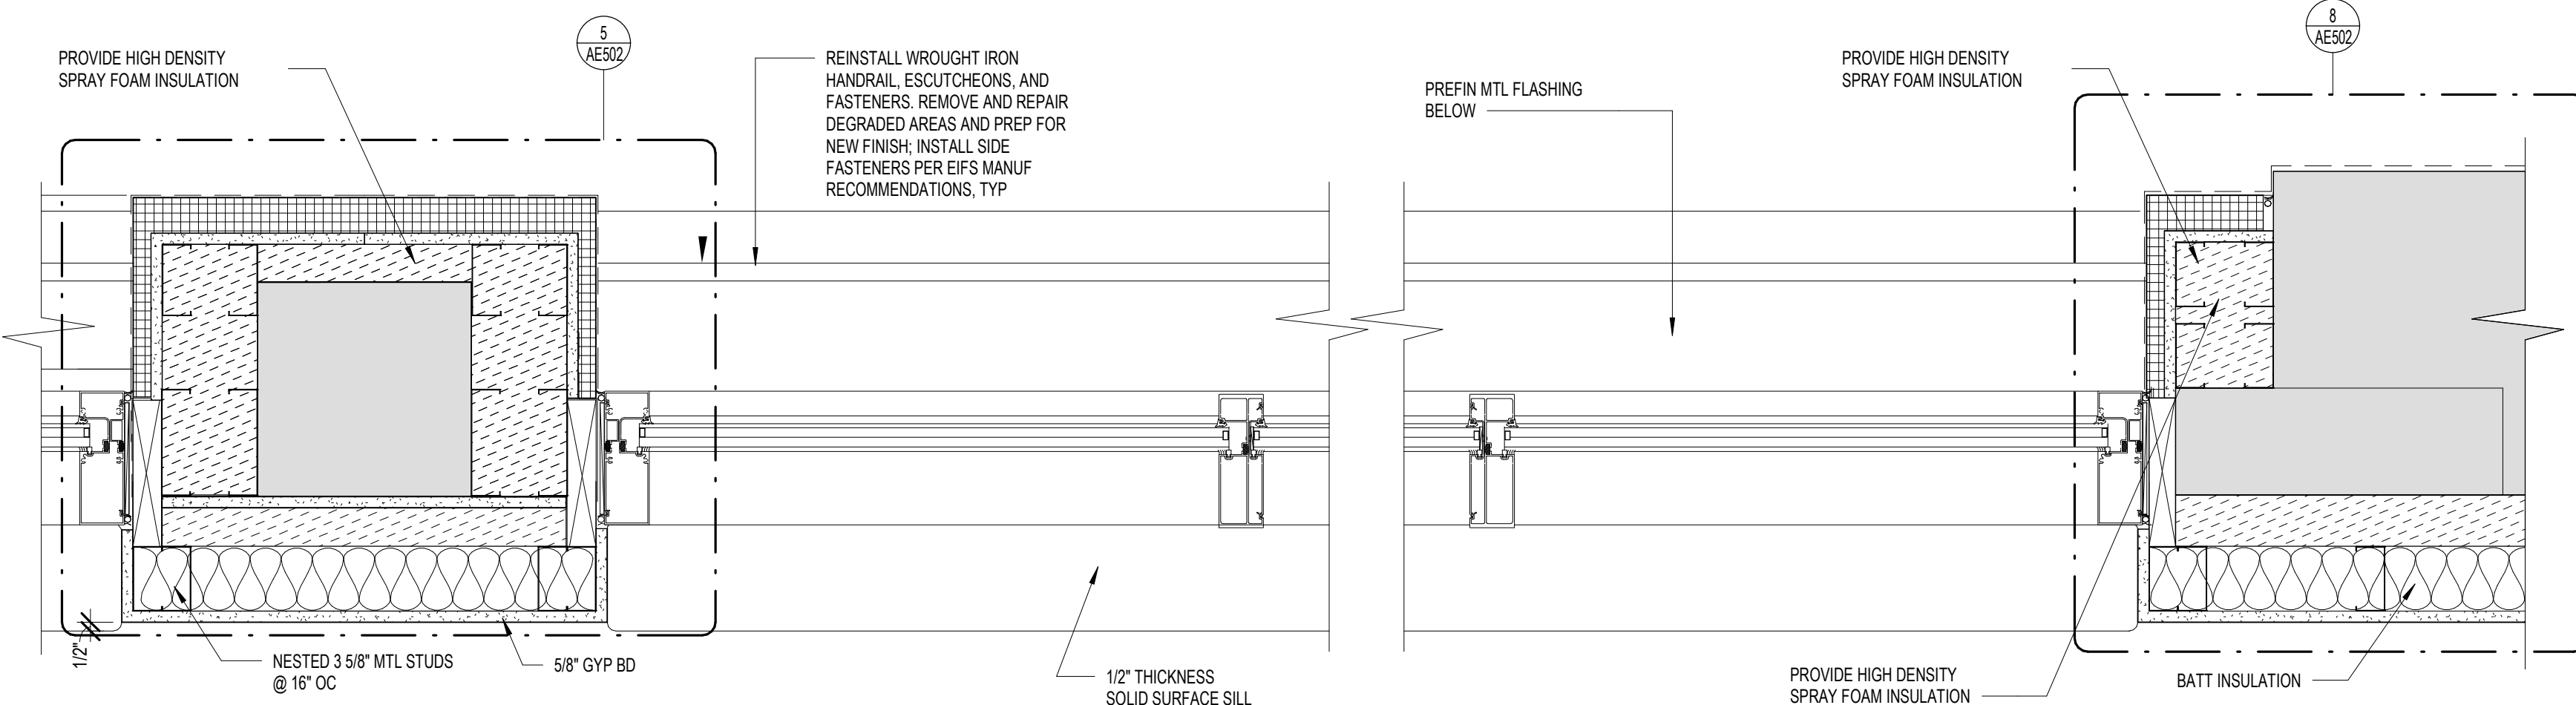

1 TYPICAL CURTAINWALL DETAIL - 3RD & 4TH FLOOR
AE502 1 1/2" = 1'-0"


B

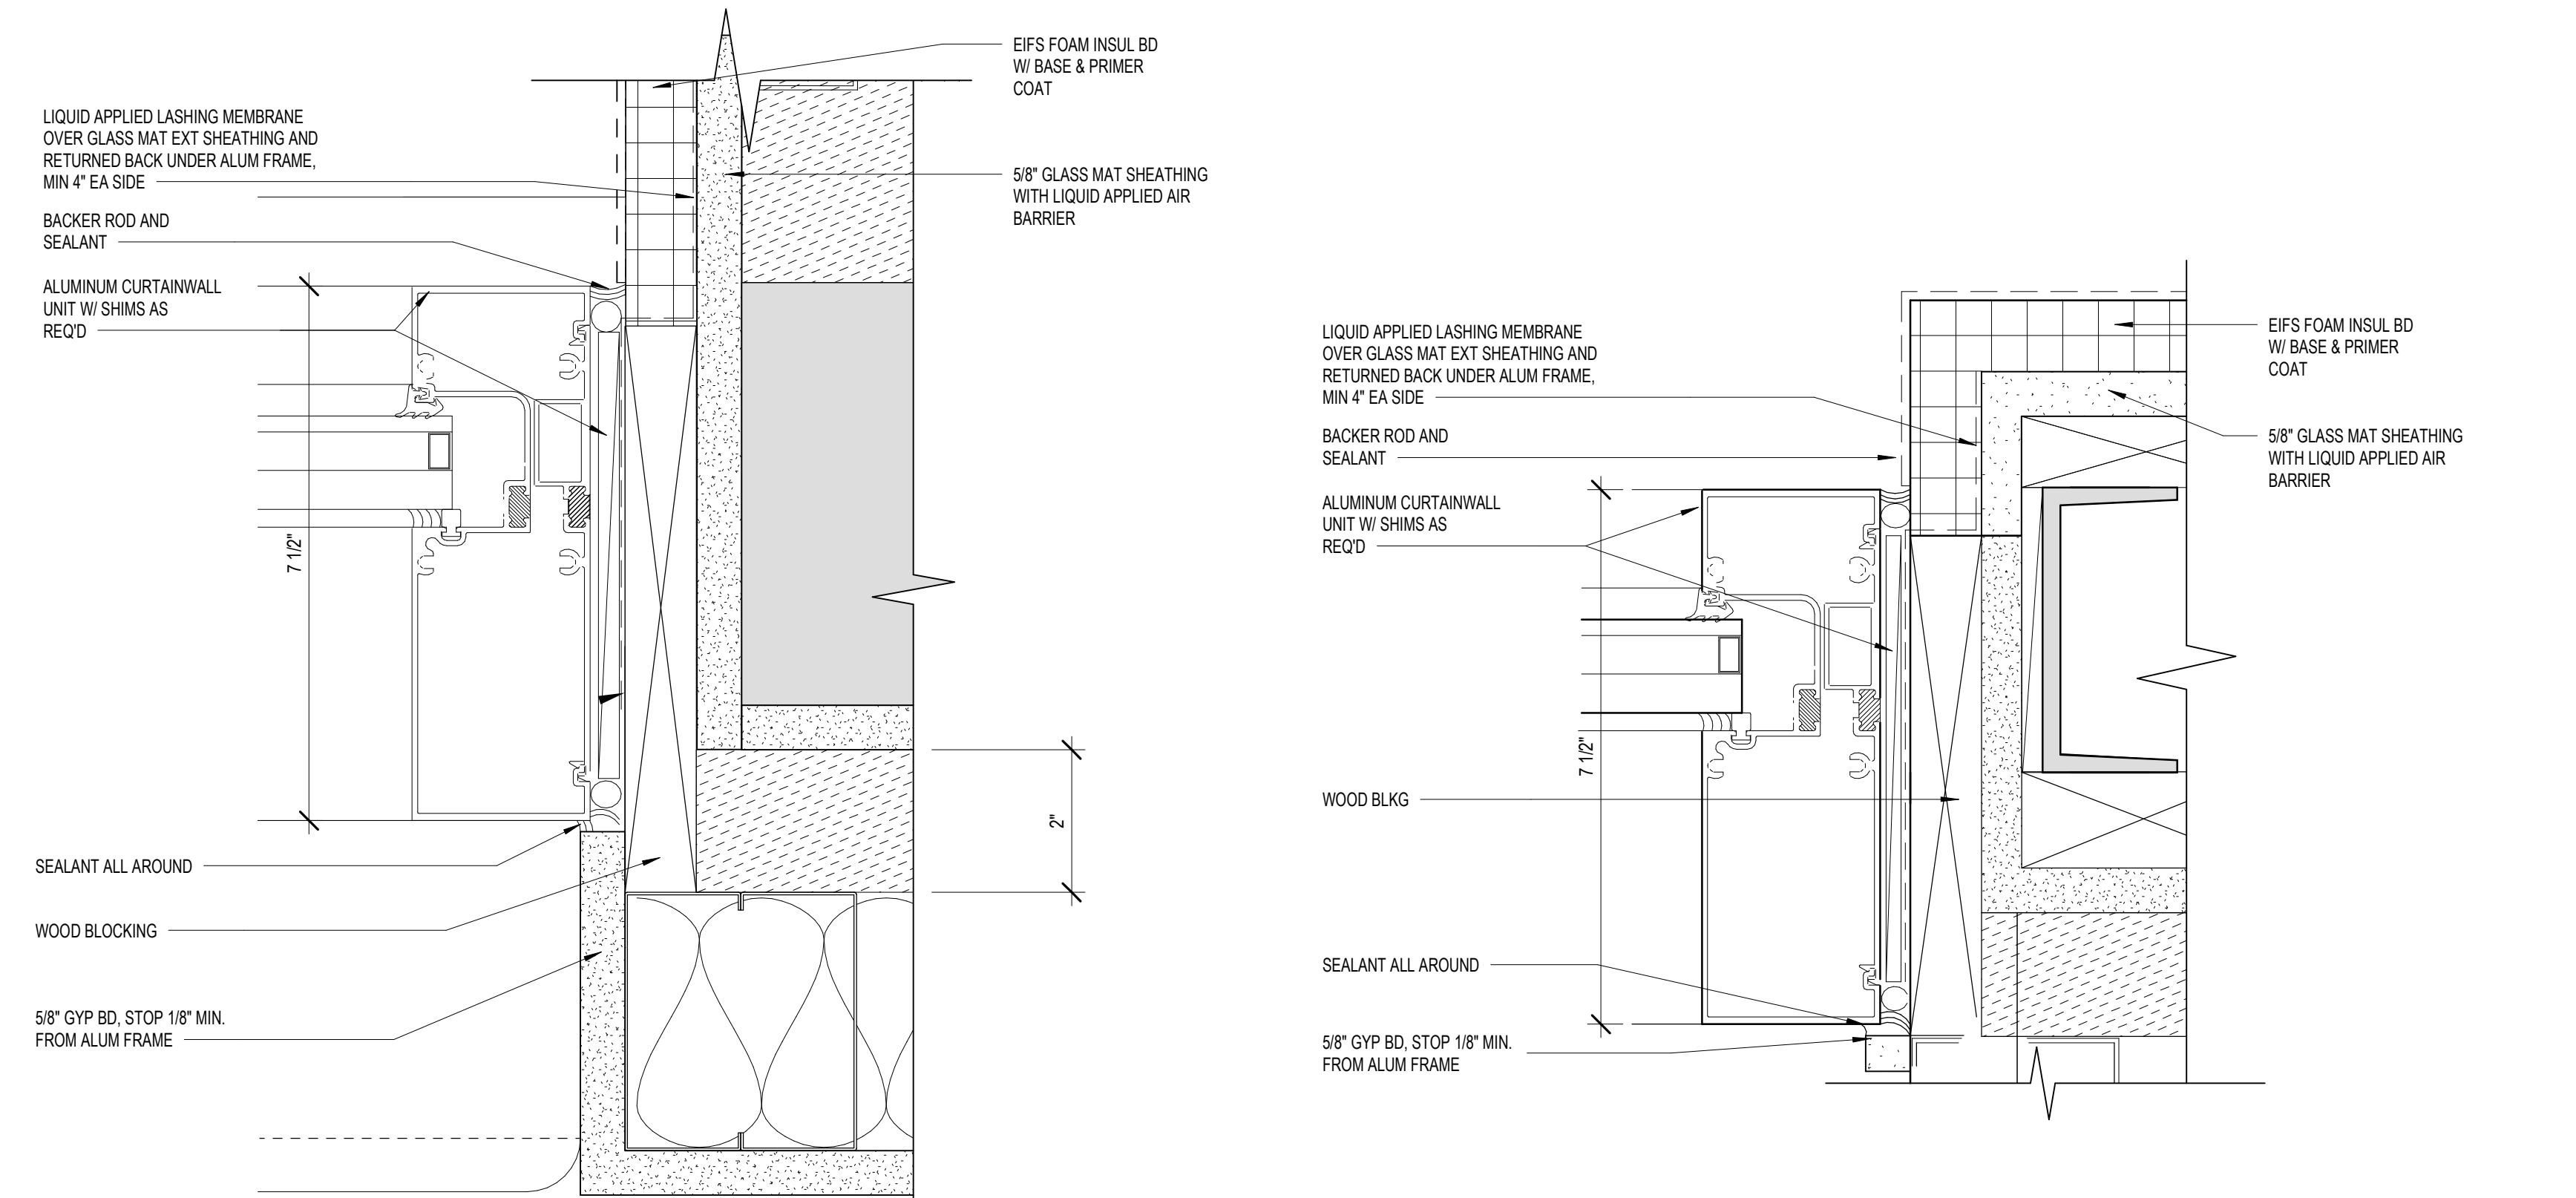

3 WINDOW JAMB & CONC COLUMN
AE502 6" = 1'-0"


4 WINDOW JAMB @ STL COLUMN
AE502 6" = 1'-0"

D

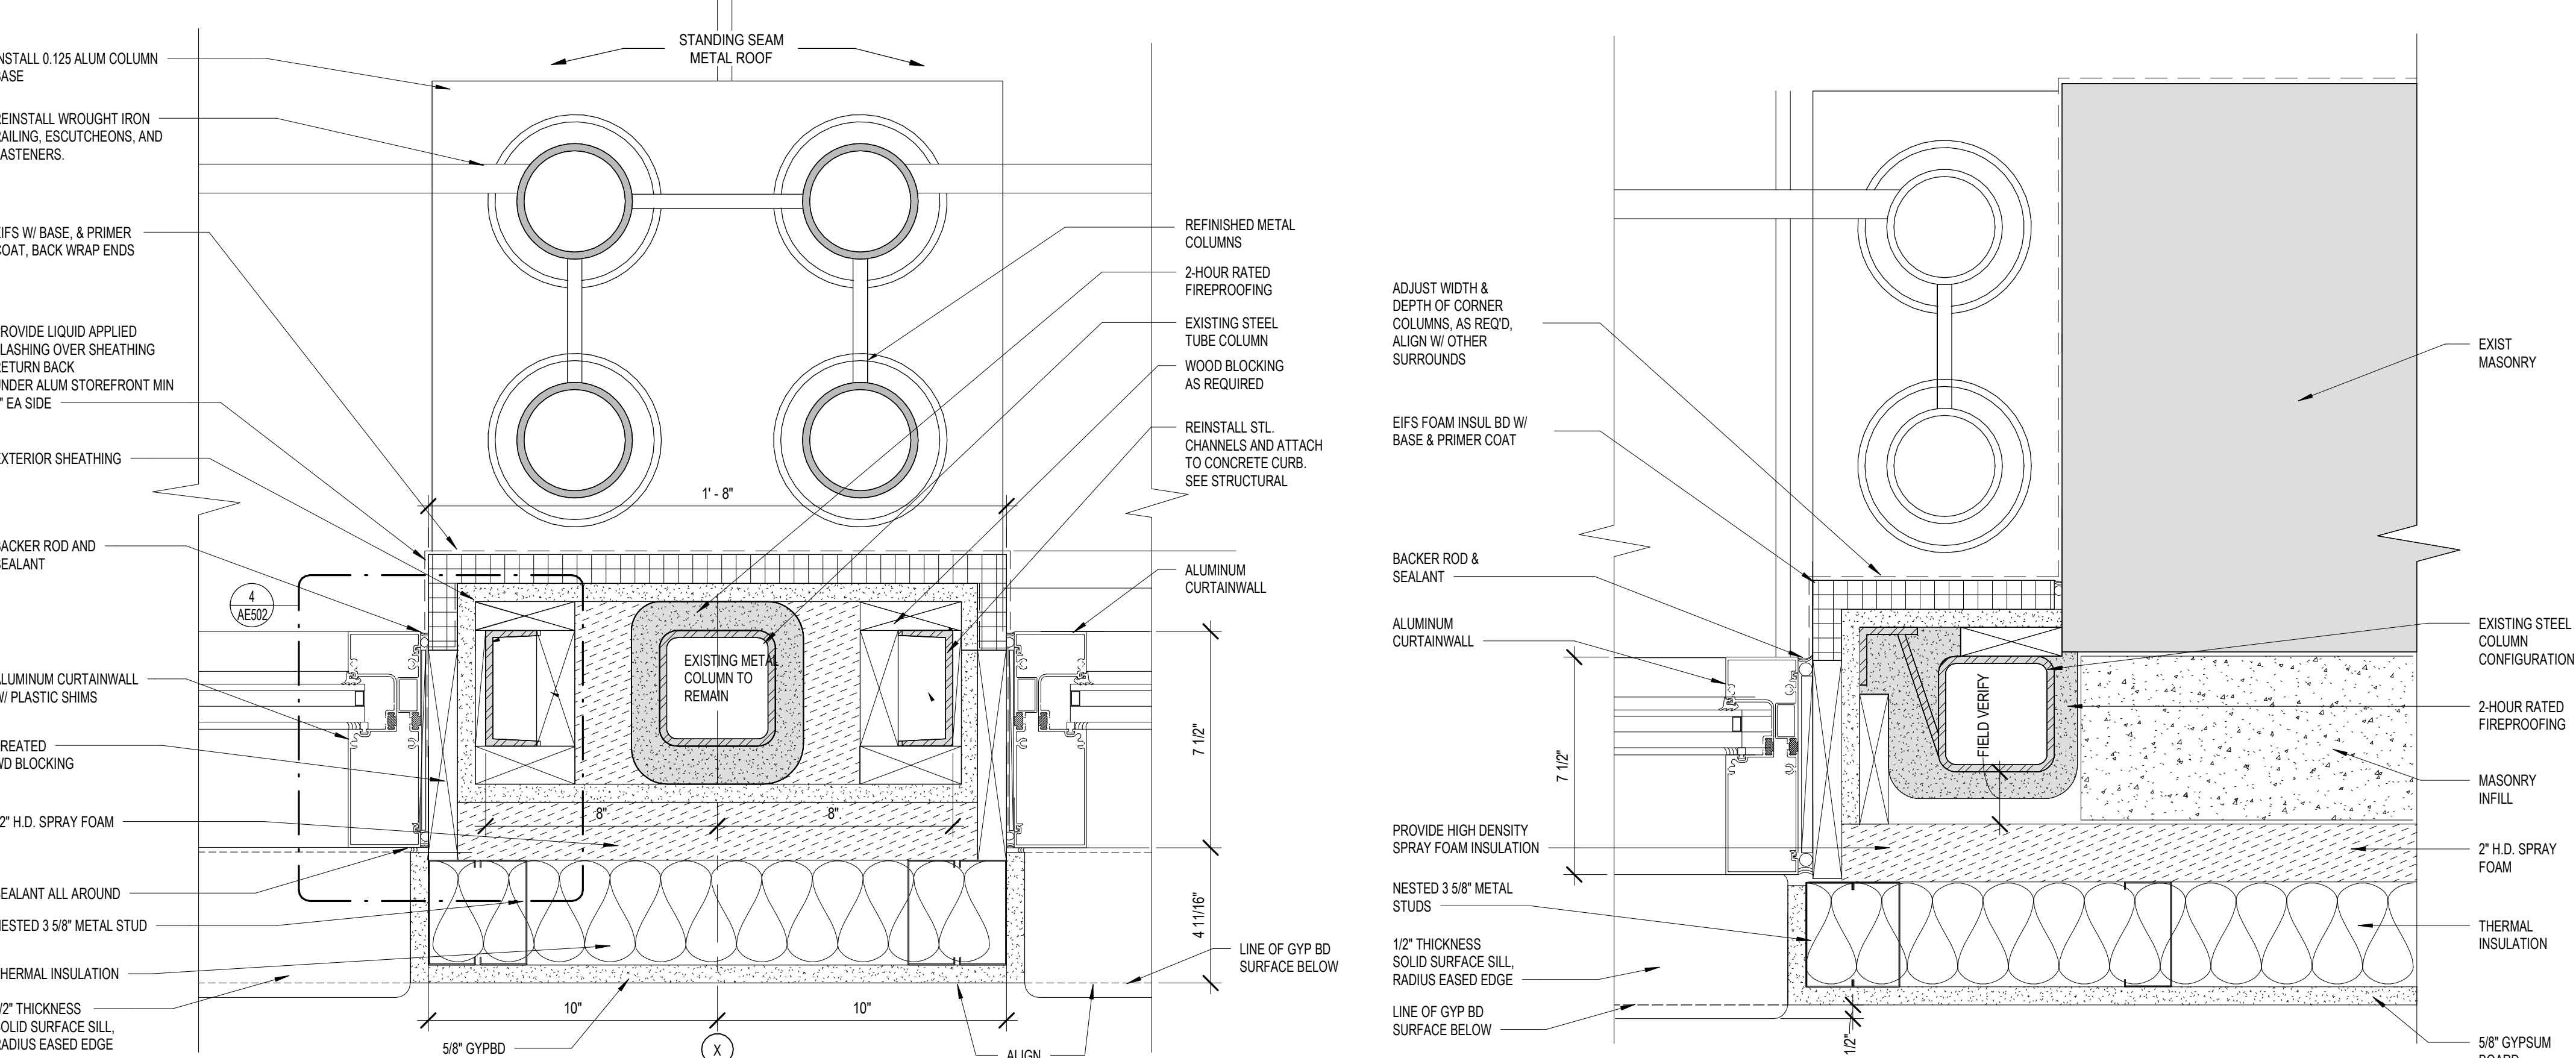


6 COLUMN DETAIL - 5TH FLOOR
AE502 3" = 1'-0"


7 END CONDITION - 5TH FLOOR
AE502 3" = 1'-0"

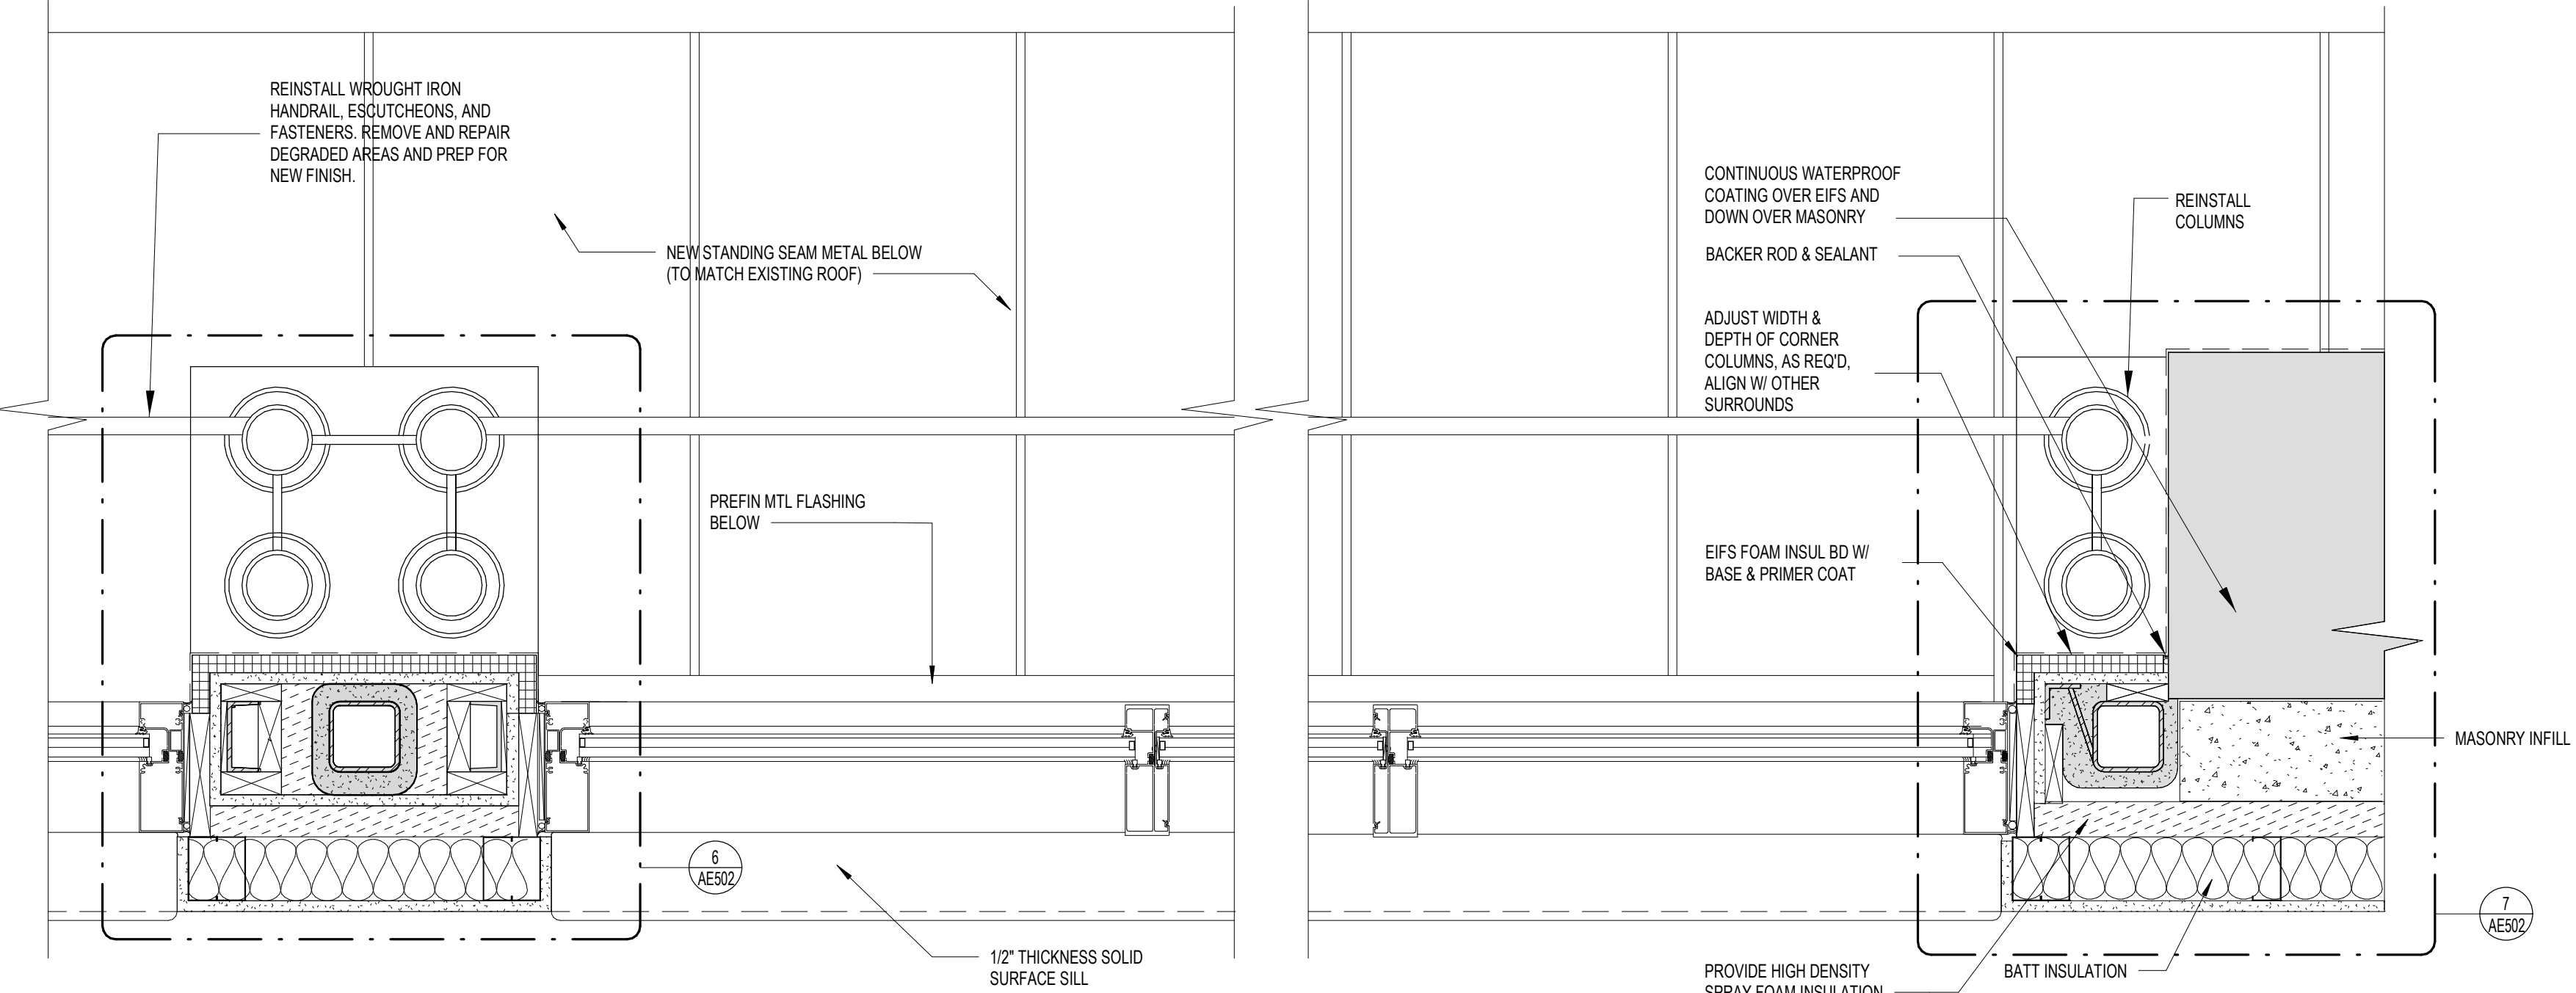

2 TYPICAL CURTAINWALL DETAIL - 5TH FLOOR
AE502 1 1/2" = 1'-0"

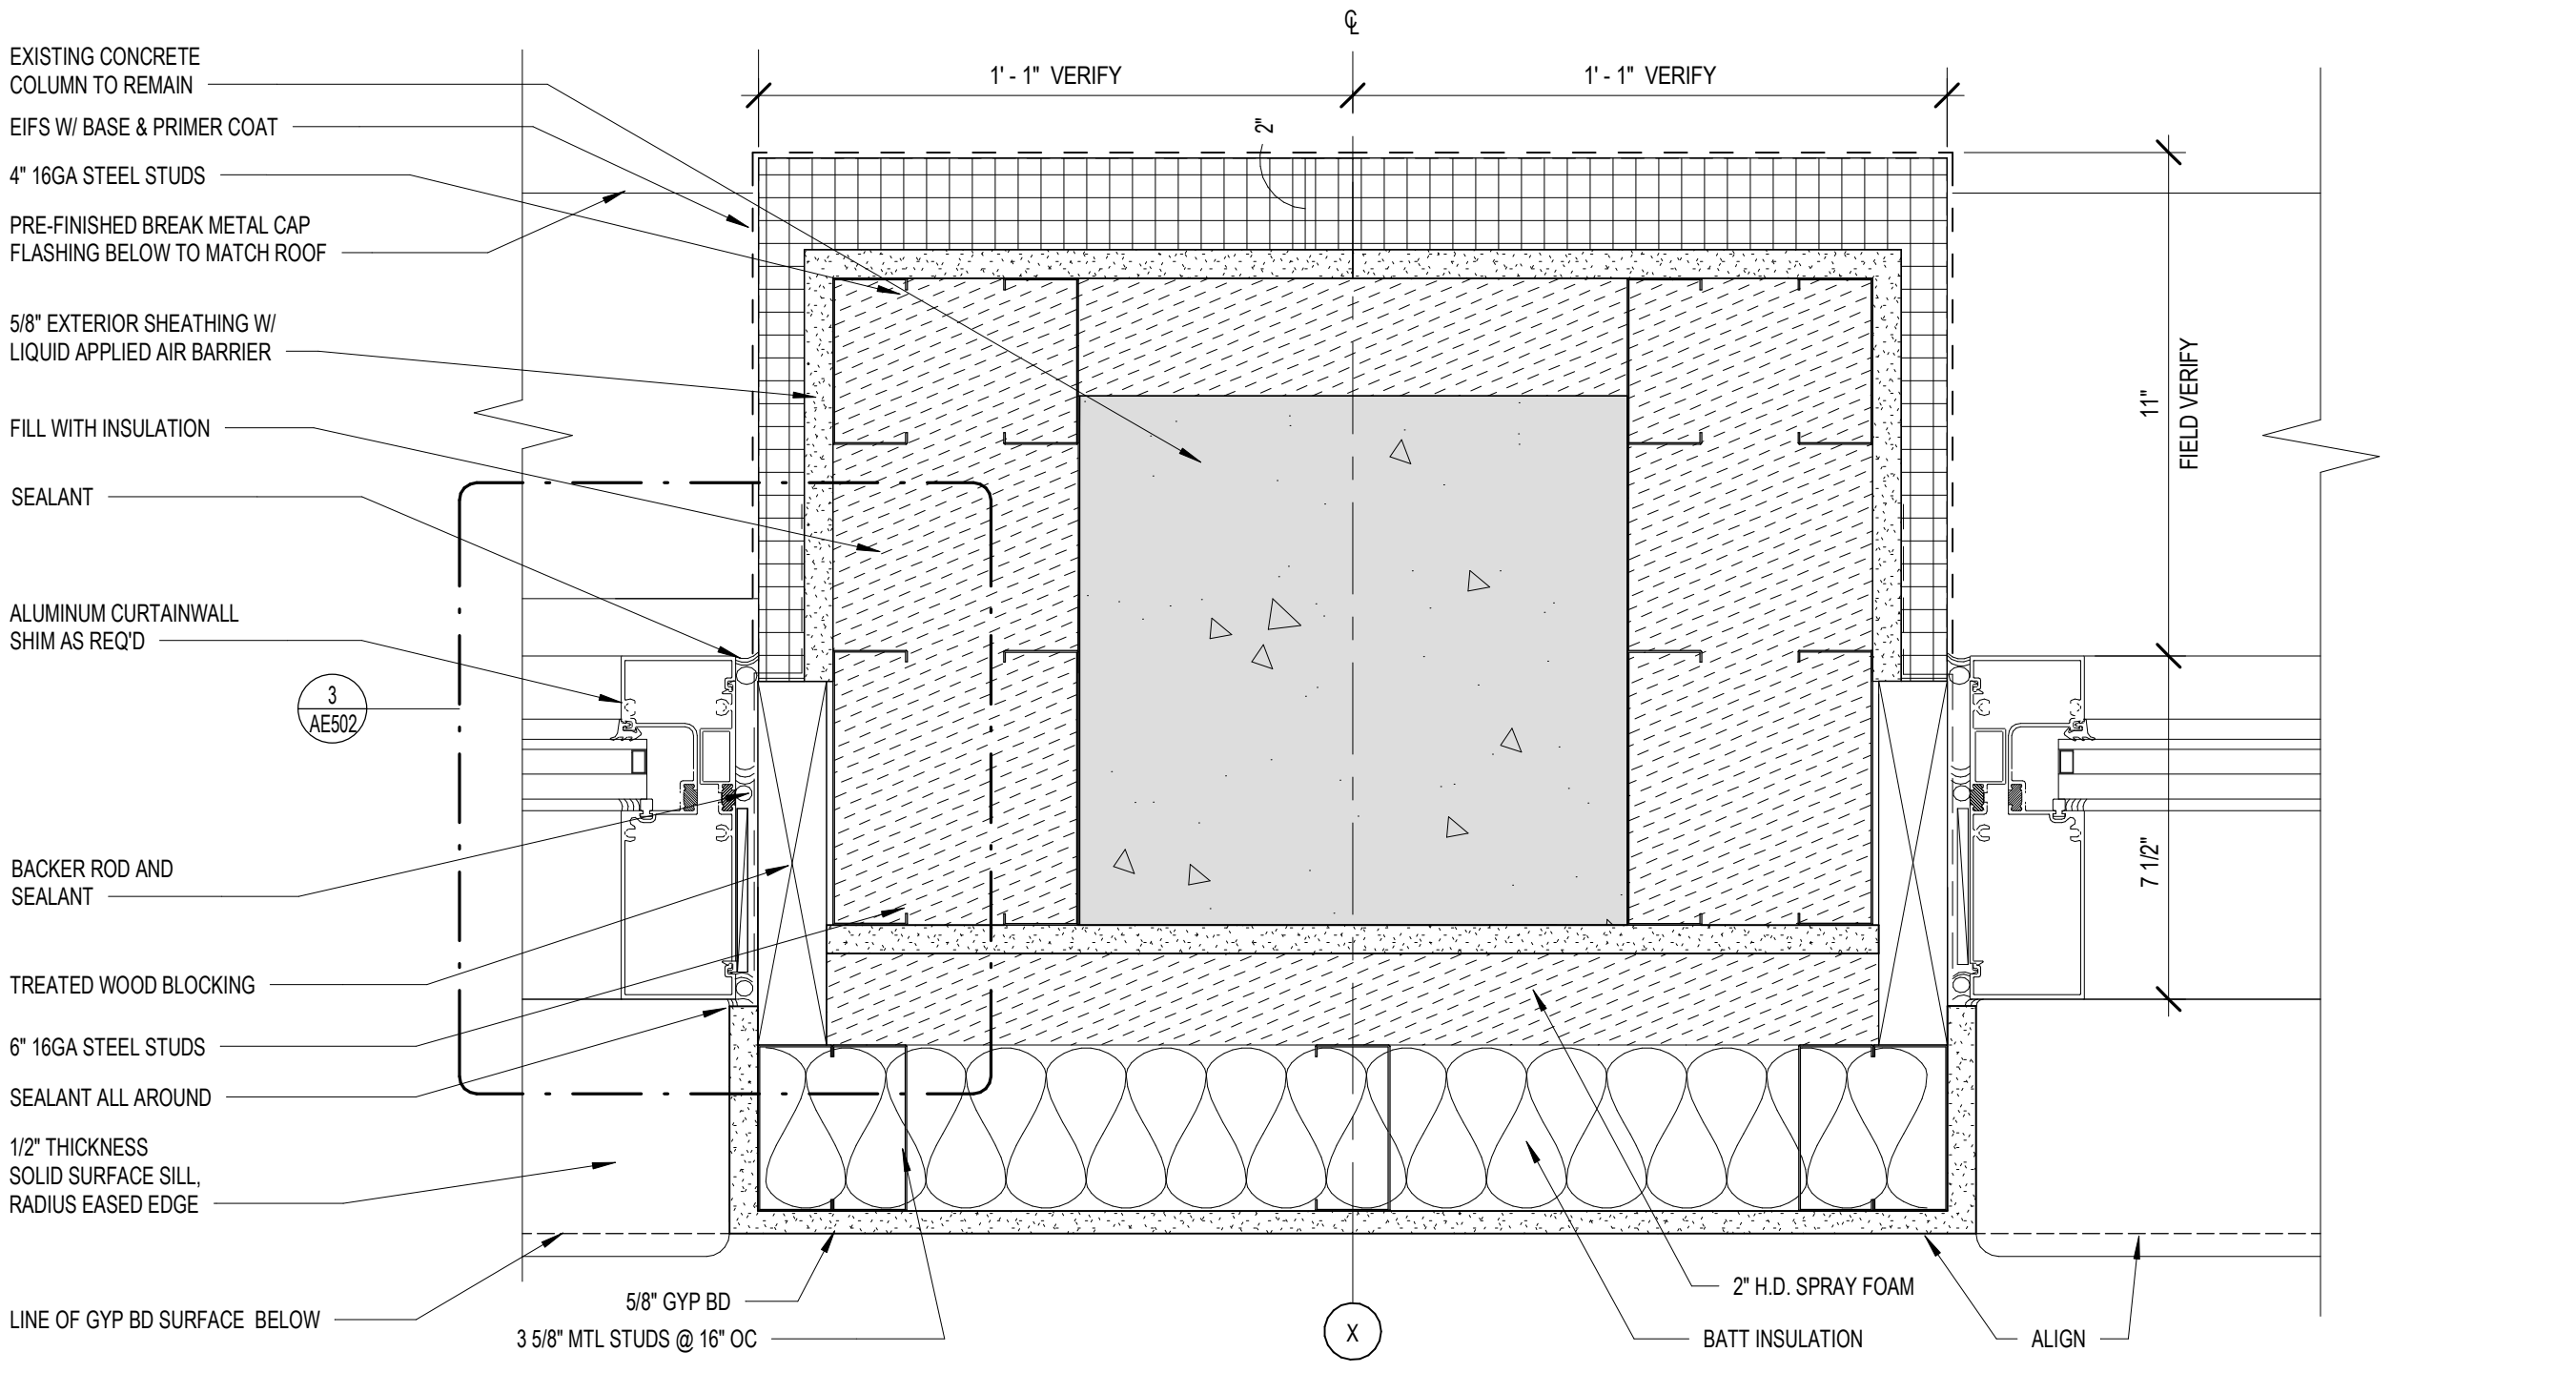

5 TYP (CONCRETE) COLUMN DETAIL - 3RD & 4TH FLOORS
AE502 3" = 1'-0"

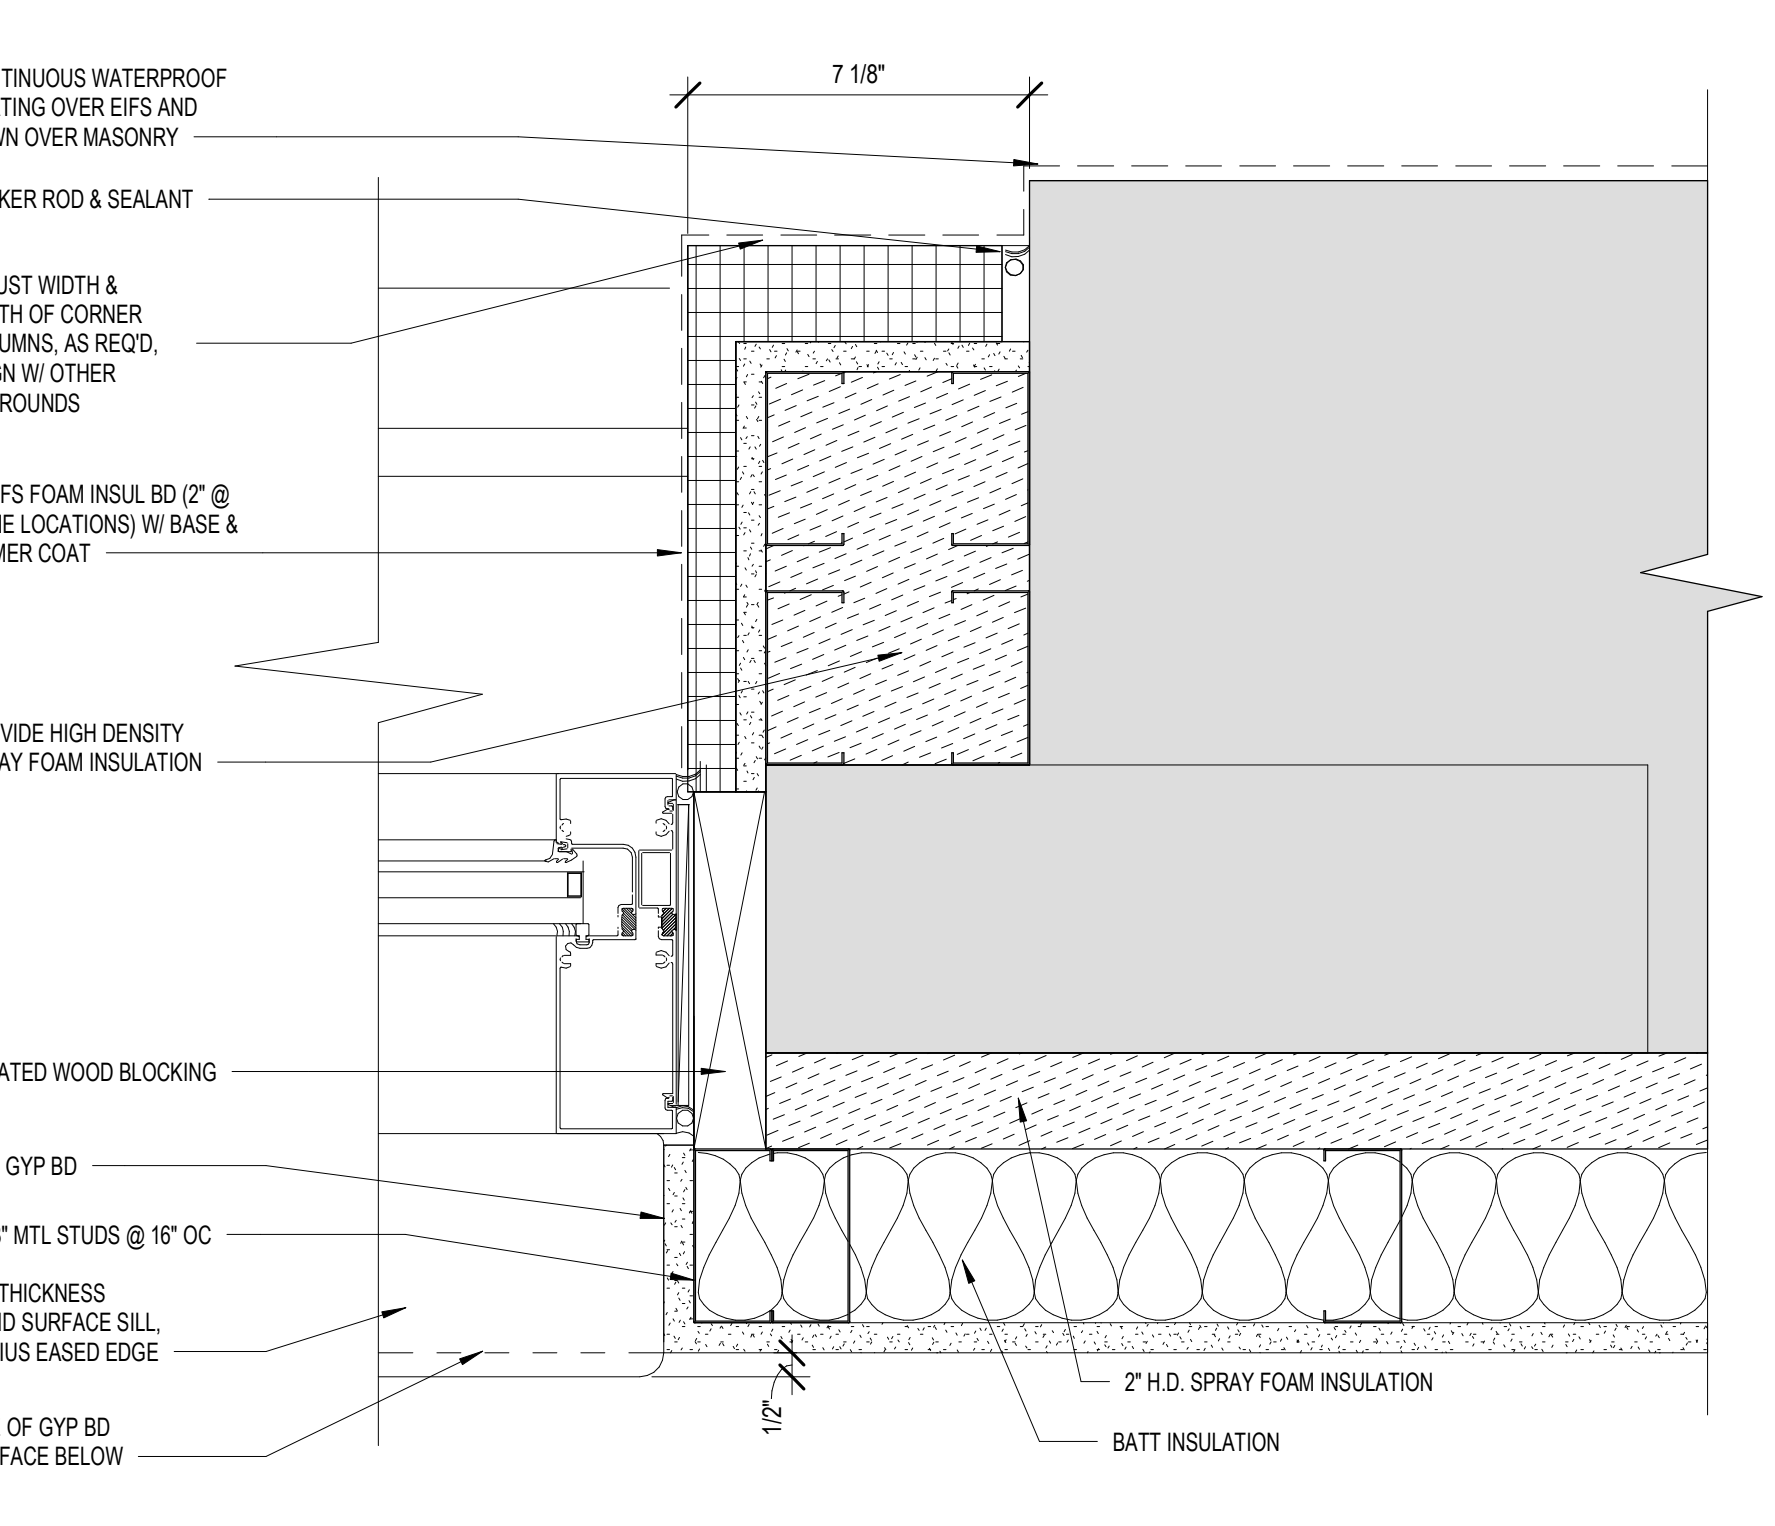

8 END CONDITION - 3RD & 4TH FLOOR
AE502 3" = 1'-0"

- NOTE**
- EXCEPT AS DESCRIBED IN THE ENLARGED DETAILS THIS SHEET, THIS DETAIL IS TYPICAL FOR ALL STOREFRONT WINDOW LOCATIONS ON THE 3RD AND 4TH FLOORS.
 - EXISTING STRUCTURAL COLUMNS AT PERIMETER OF BUILDING 1 ARE CONCRETE AT 3RD AND 4TH FLOORS AND STEEL PIPE COLUMNS AT 5TH FLOOR. STEEL COLUMNS HAVE CHANNEL AND ANGLE SUPERSTRUCTURE.
 - DIMENSIONS BETWEEN COLUMNS VARY BASED ON LOCATION IN BUILDING. SEE WINDOW TYPES FOR SIZE REQUIREMENTS BETWEEN COLUMNS/BLOCKING. CONTRACTOR TO VERIFY IN FIELD.
 - CONDITIONS SHOWN ARE THE SAME AT 3RD AND 4TH FLOORS EXCEPT EXISTING STRUCTURAL COLUMNS DIFFER.
 - COORDINATE W/ NEW BUILD OUT SET FOR CONNECTION TO 2 1/2" MTL STUDS AT INTERIOR OF BUILDING.
 - SEE DETAILS ON SHEETS AE502-AE503 FOR ADDITIONAL INFORMATION.
 - PROVIDE LIQUID APPLIED AIR BARRIER OVER ALL GLASS MAT SHEATHING

BID DOCUMENTS

CONSULTANT		ARCHITECT/ENGINEER OF RECORD		STAMP		Office of Construction and Facilities Management		Phase		Project Title		Project Number	
		THOMAS OLESAK, ARCHITECT		Thomas Olesak 03.10.2023		U.S. Department of Veterans Affairs		CONSTRUCTION DOCUMENTS		RENOVATE BUILDING 1		520-317X	
		MS Lic # 5505						FULLY SPRINKLERED		Location		Building Number	
		1050 HOYT AVE WEST ST PAUL, MN 55117								BILOXI, MISSISSIPPI		1	
		952-451-0460								Issue Date		Drawing Number	
										03/10/2023		AE502	
										Checked		Dwg. 97 of 238	
										LA			
										Drawn			
										CD, MS			

A

B

C


D

E


F

2/26/2019 9:26:08 AM


C:\Users\jcd\Documents\15950 - VAAC-Bldg Building_1_R172_Central model - 10-9-18_Yeanyoung.rvt

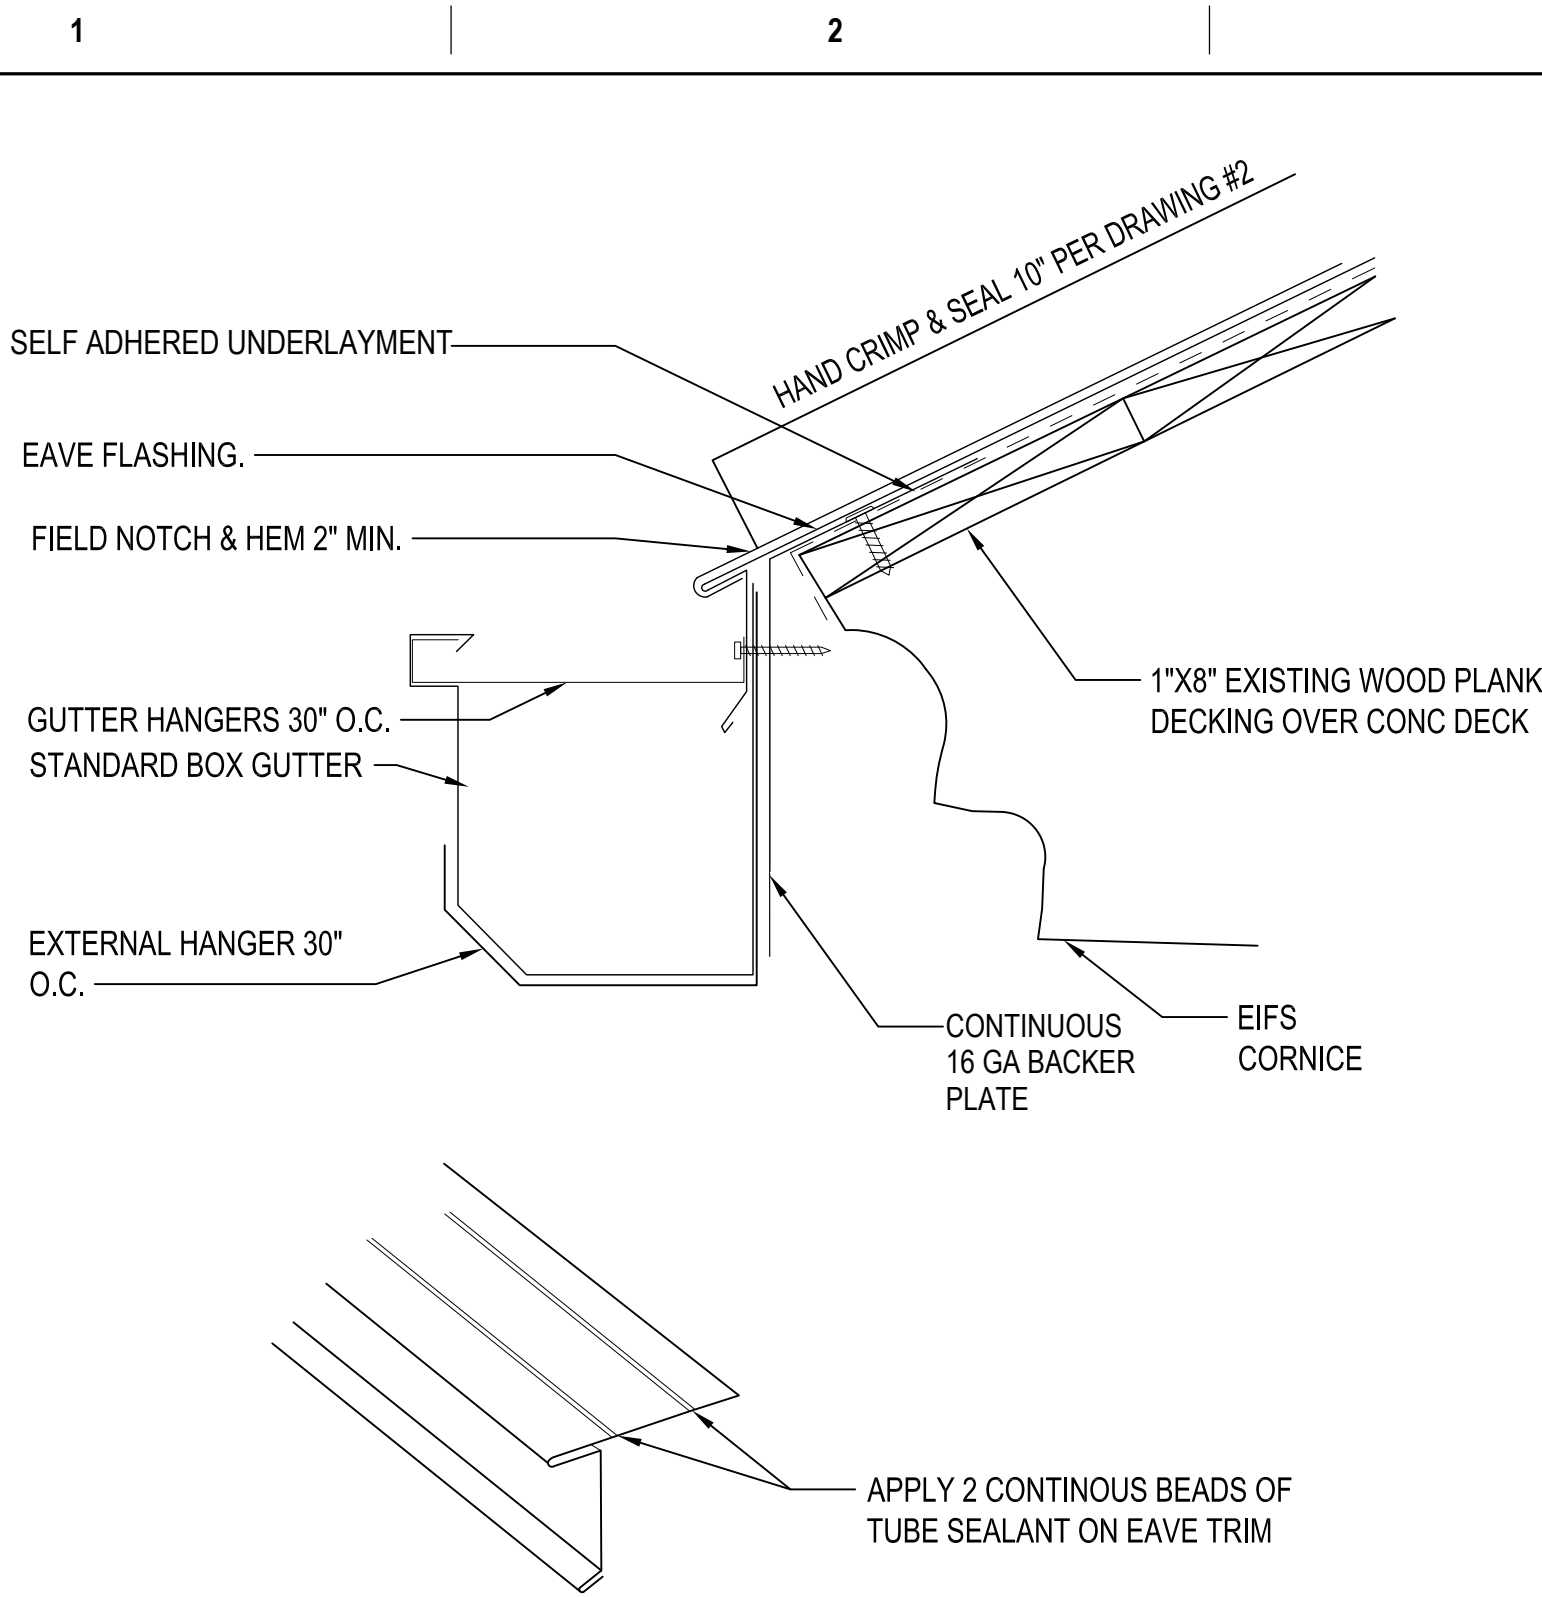


1 GUTTER DETAIL
AE503 SCALE: 1-1/2"=1'-0"

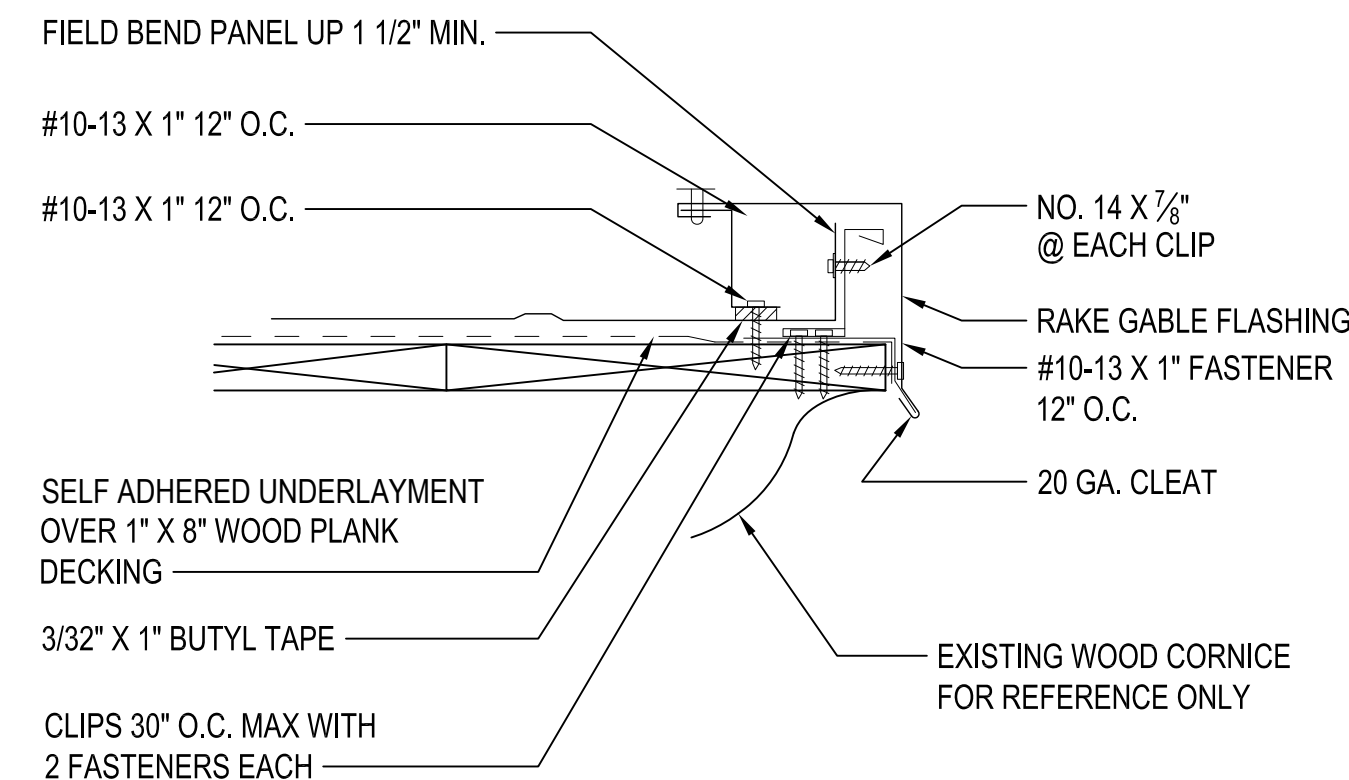


2 RAKE EDGE DETAIL
AE503 SCALE: 1-1/2"=1'-0"

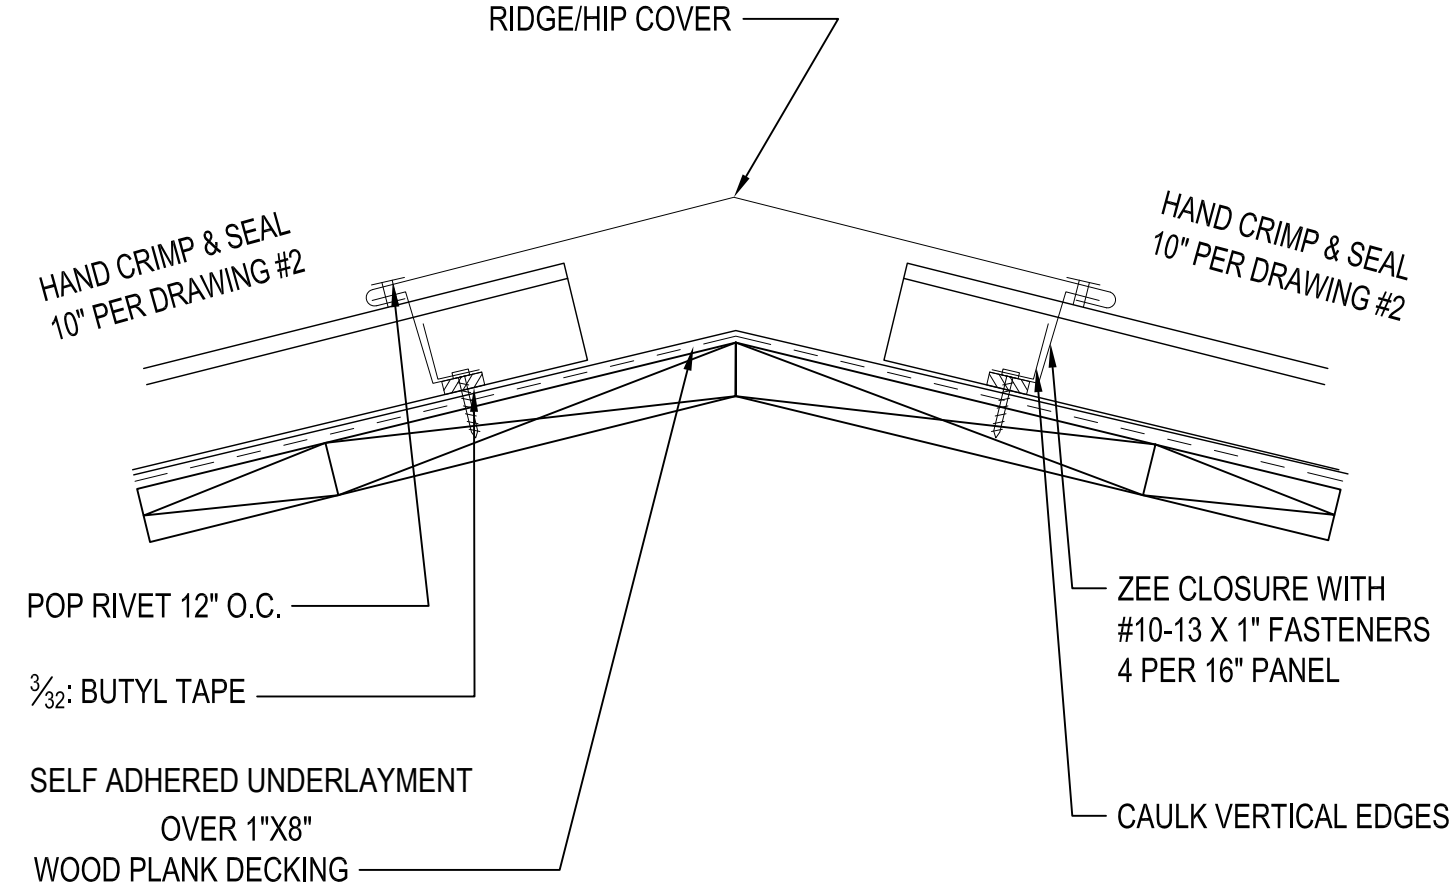


3 RIDGE DETAIL
AE503 SCALE: 1-1/2"=1'-0"

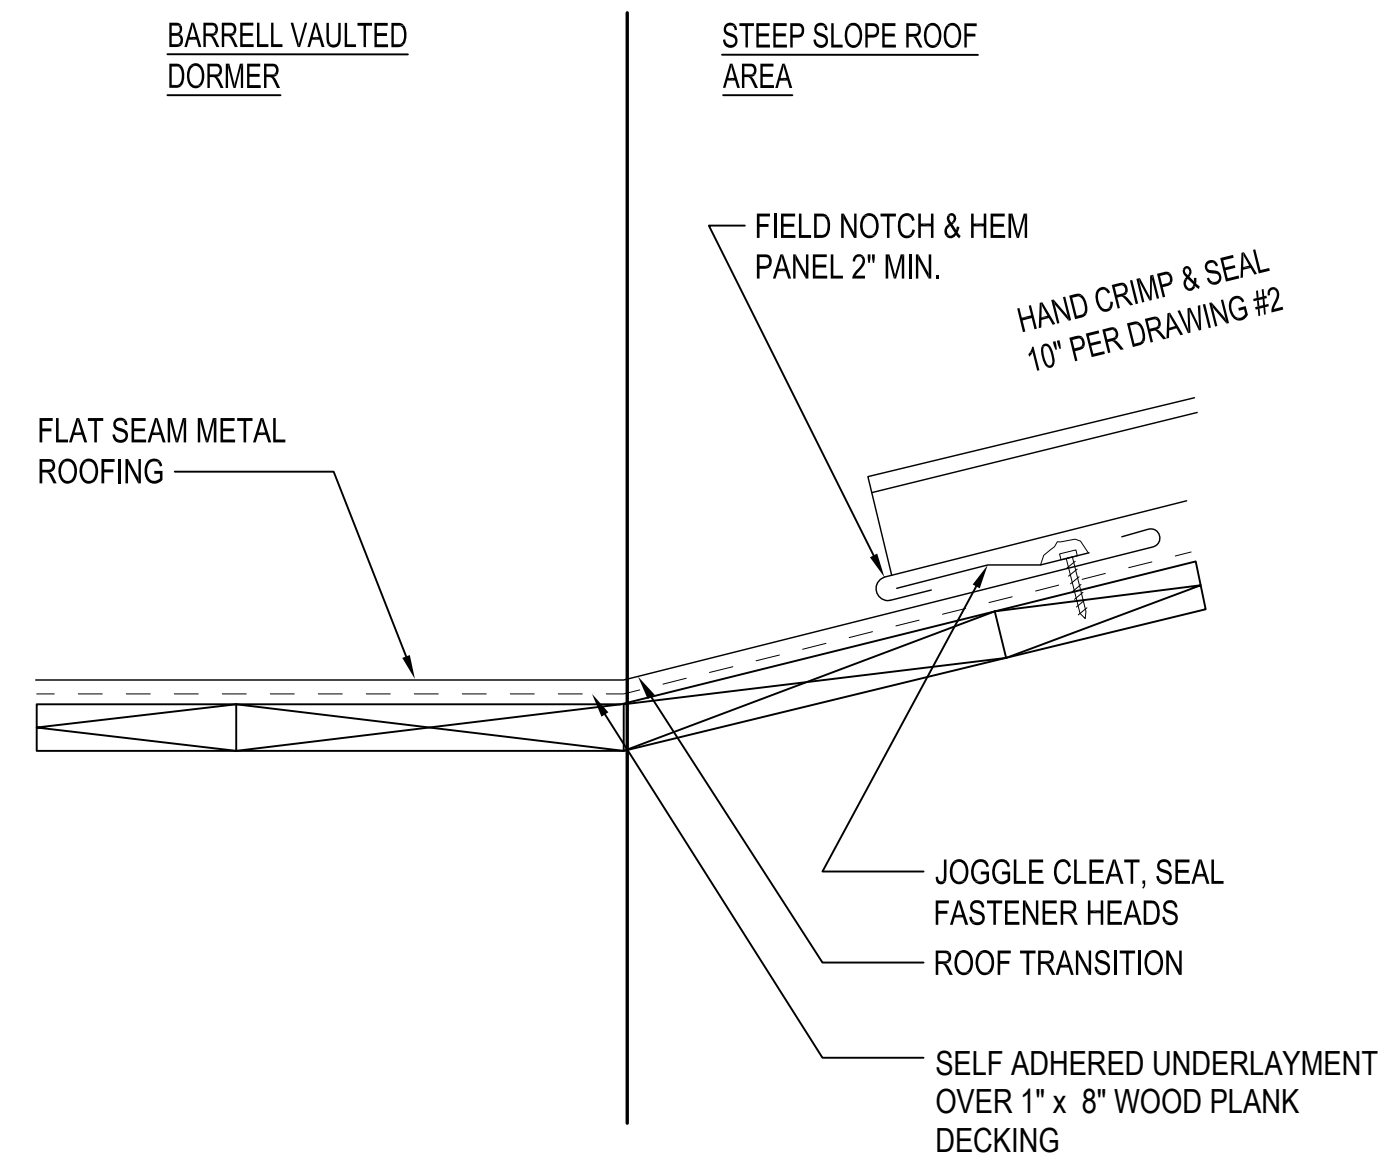


4 TRANSITION ROOF DETAIL
AE503 SCALE: 1-1/2"=1'-0"

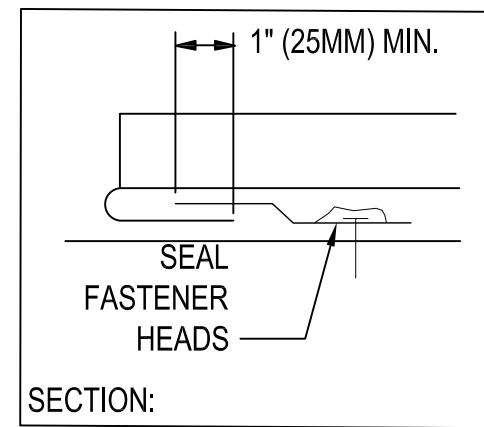


SECTION:

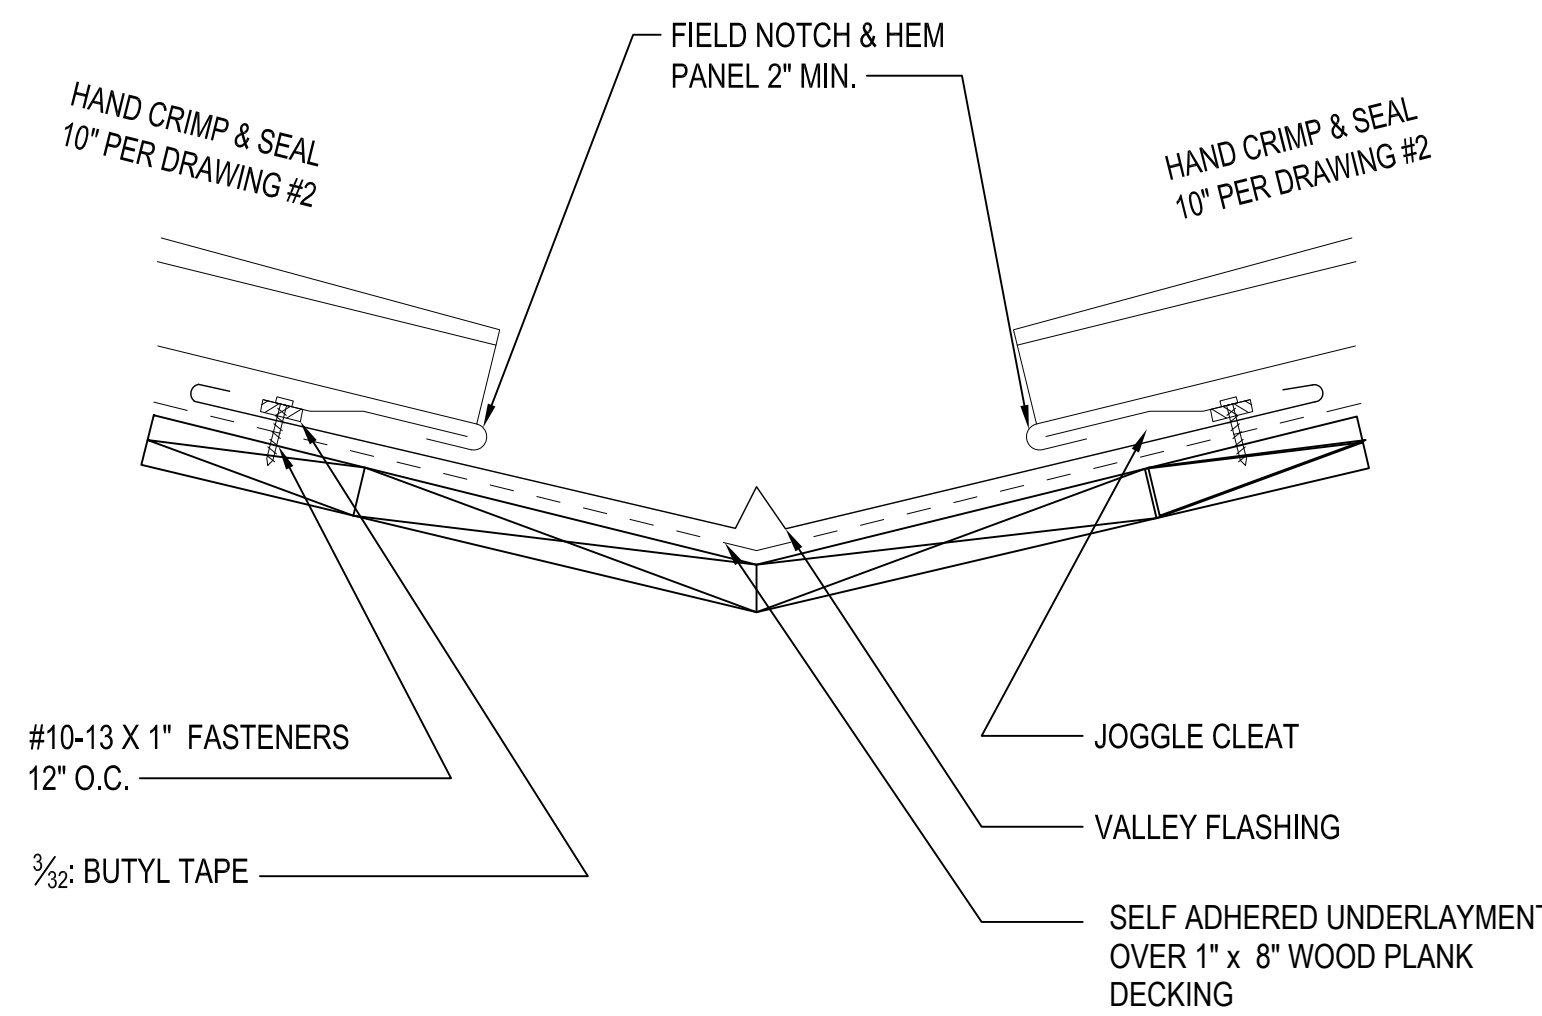


5 VALLEY DETAIL
AE503 SCALE: 1-1/2"=1'-0"

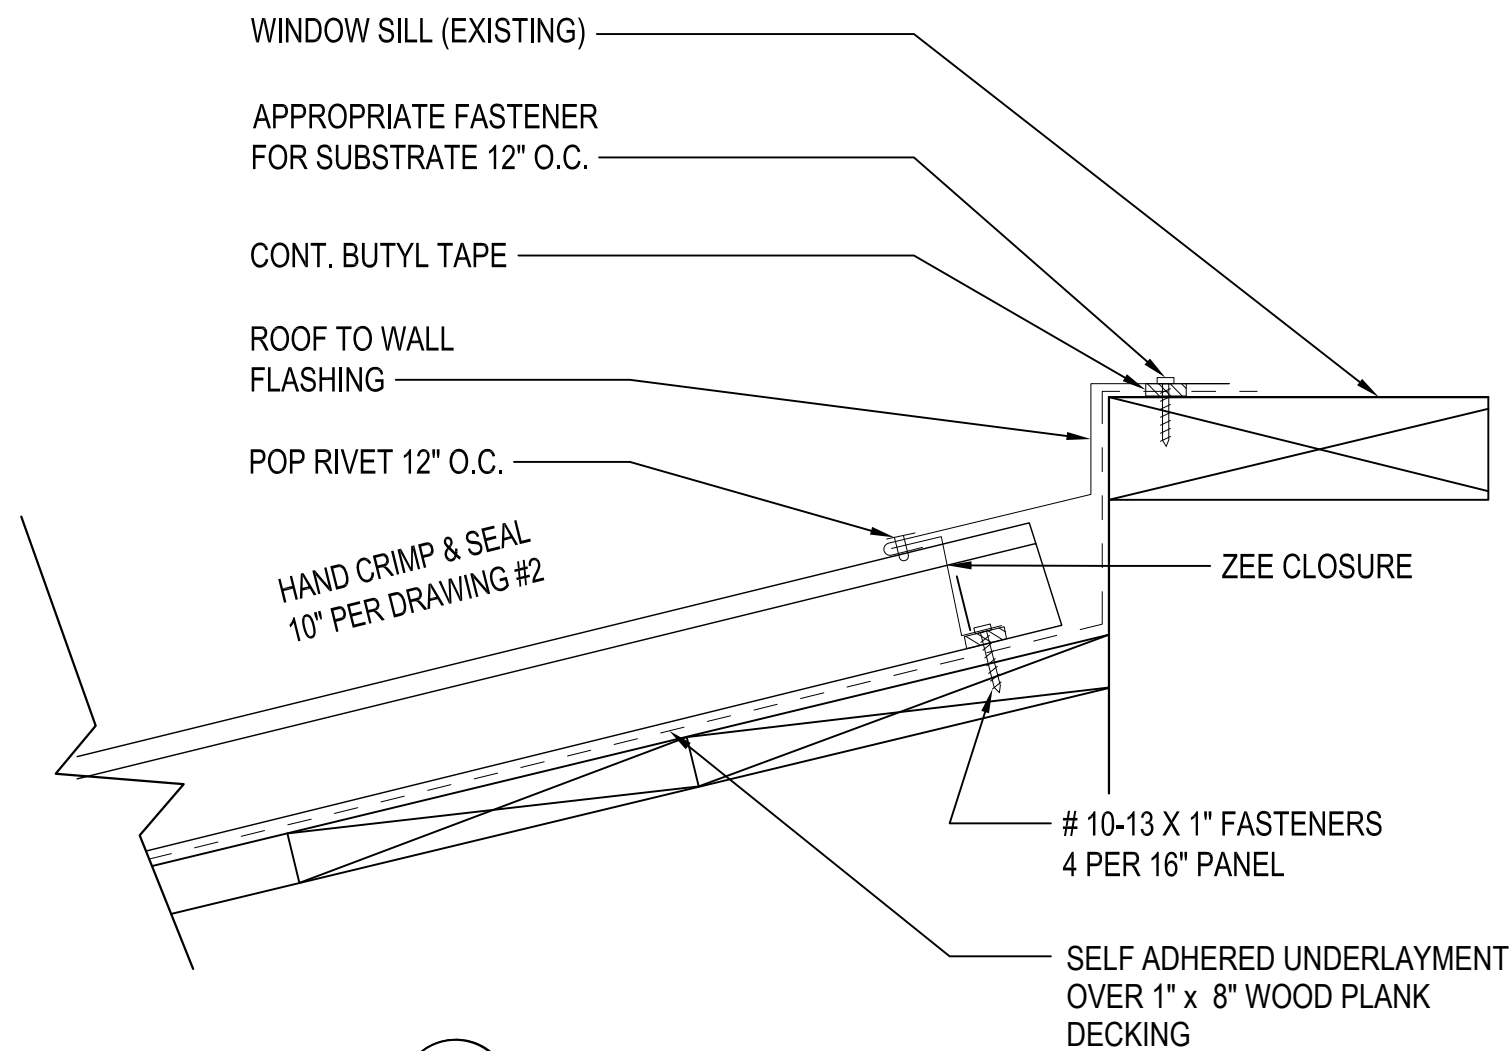


6 TRANSITION DETAIL
AE503 SCALE: 1-1/2"=1'-0"

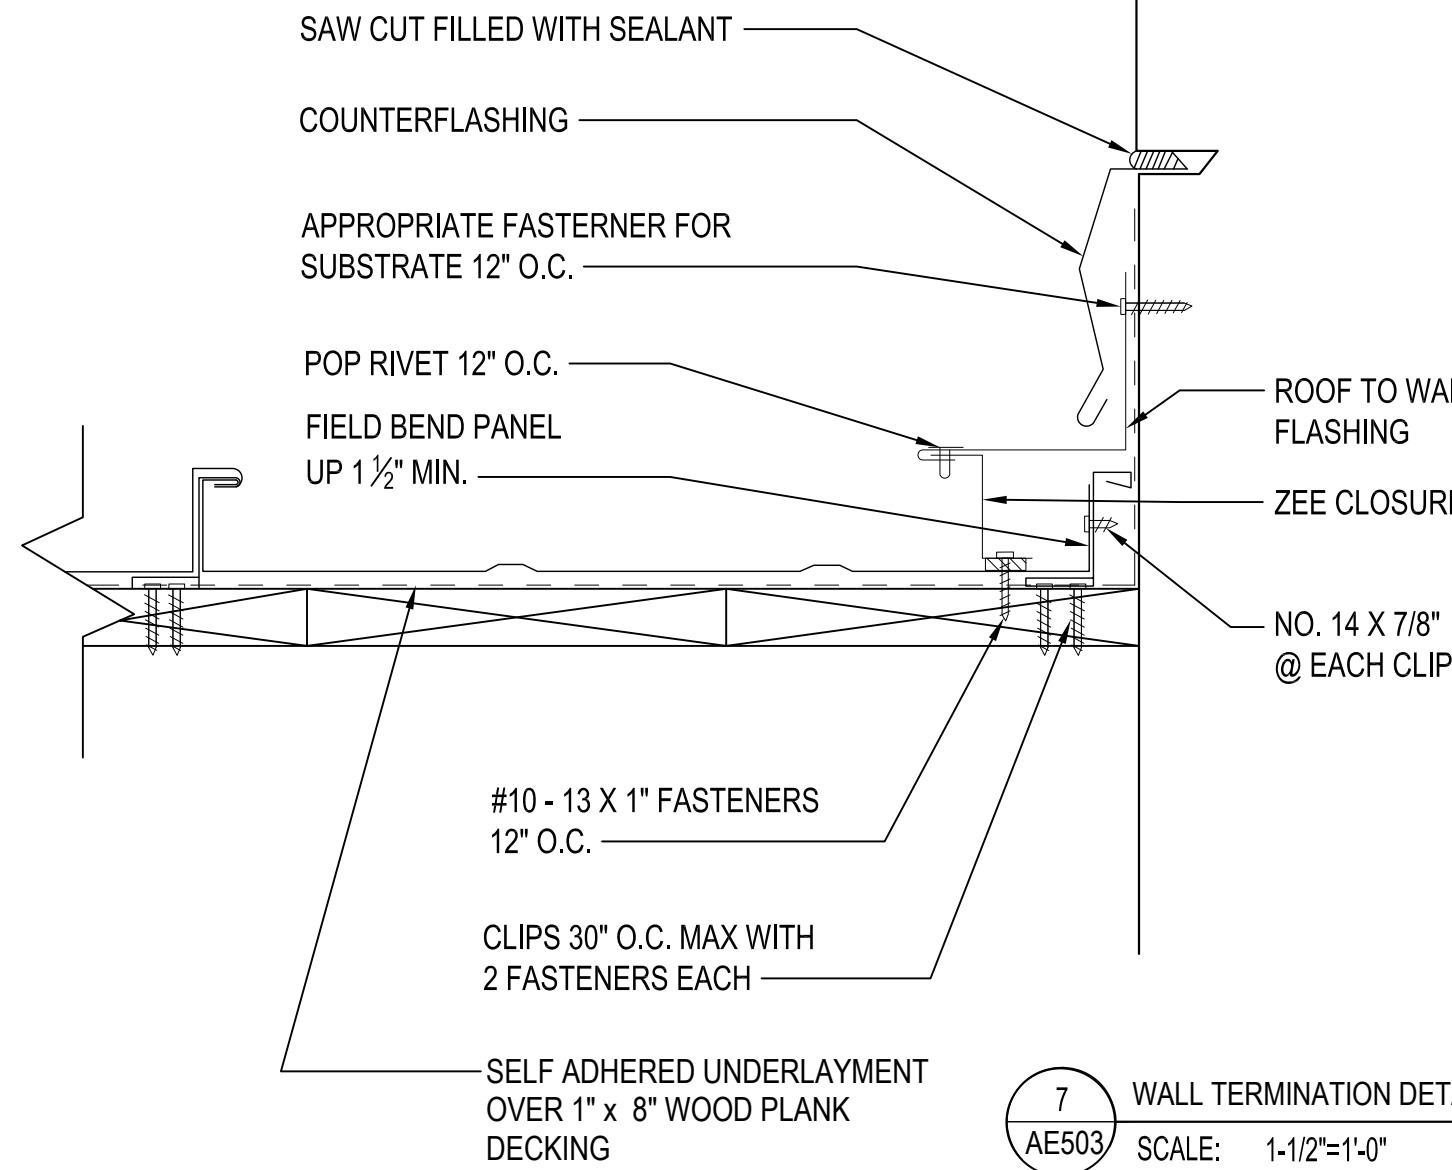


7 WALL TERMINATION DETAIL
AE503 SCALE: 1-1/2"=1'-0"

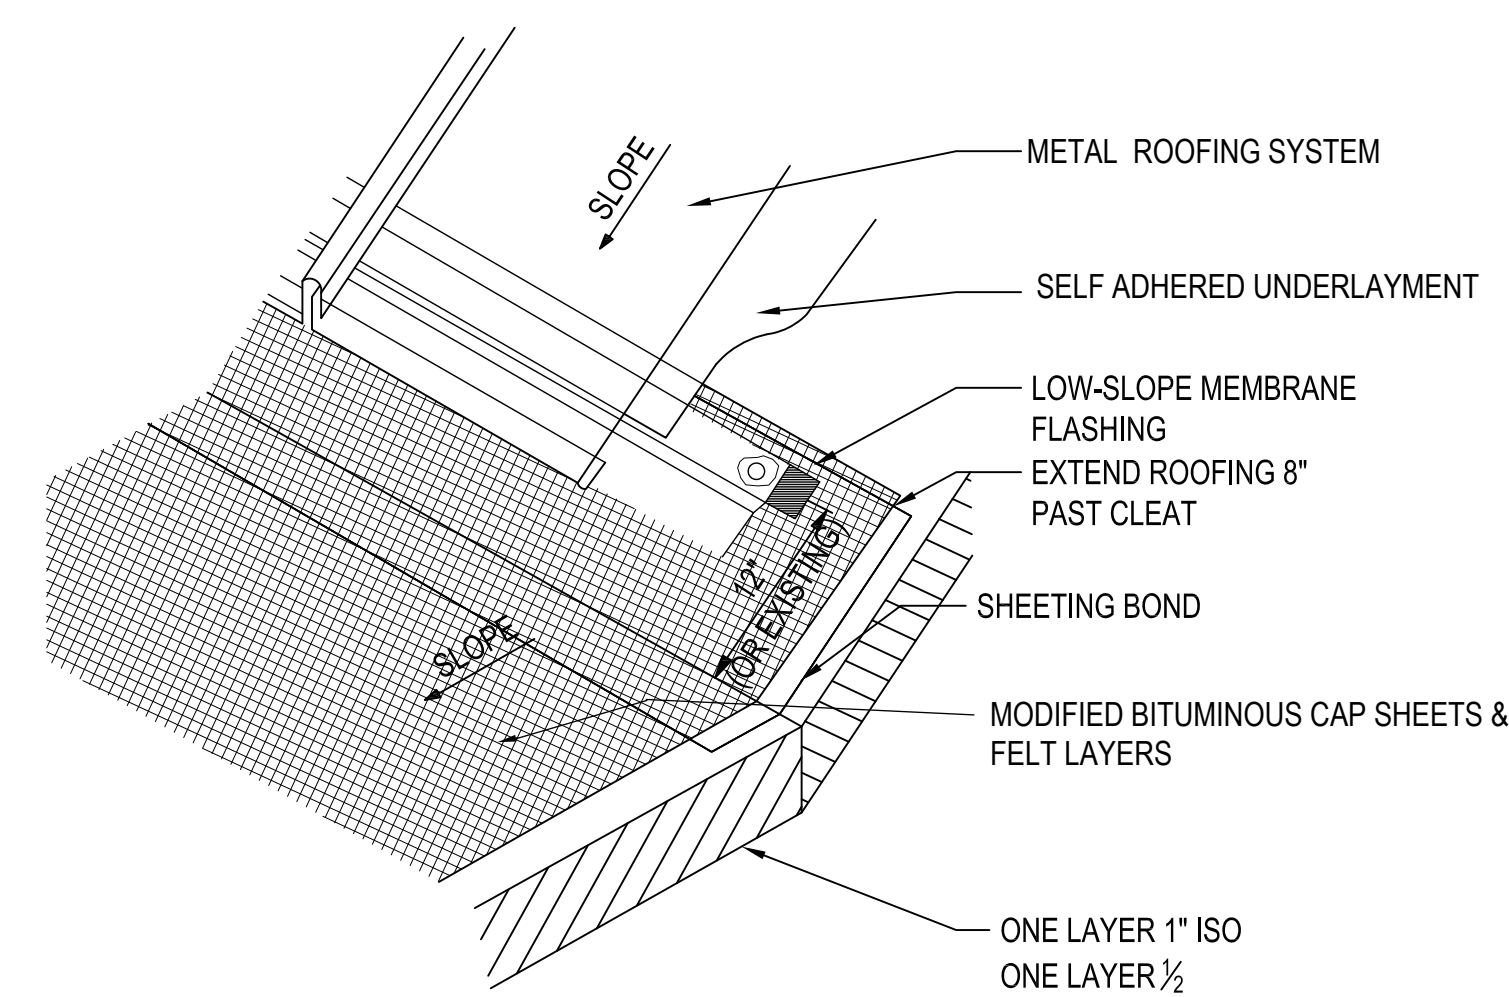


8 TRANSITION ROOF DETAIL
AE503 SCALE: 1-1/2"=1'-0"

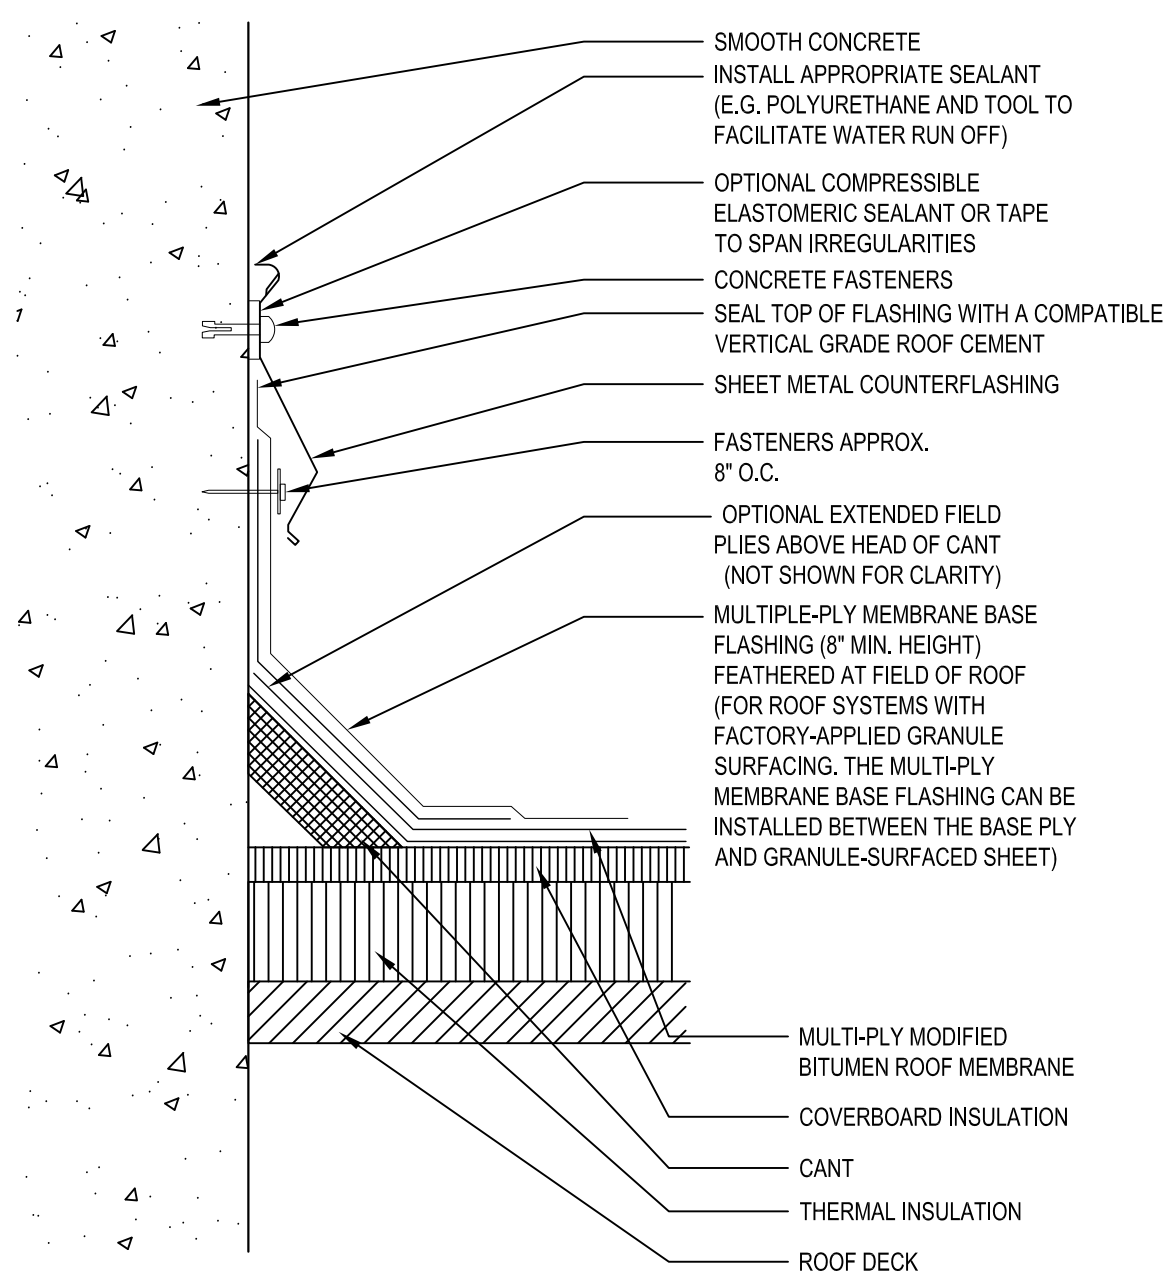

9 WALL TERMINATION DETAIL
AE503 SCALE: 1-1/2"=1'-0"

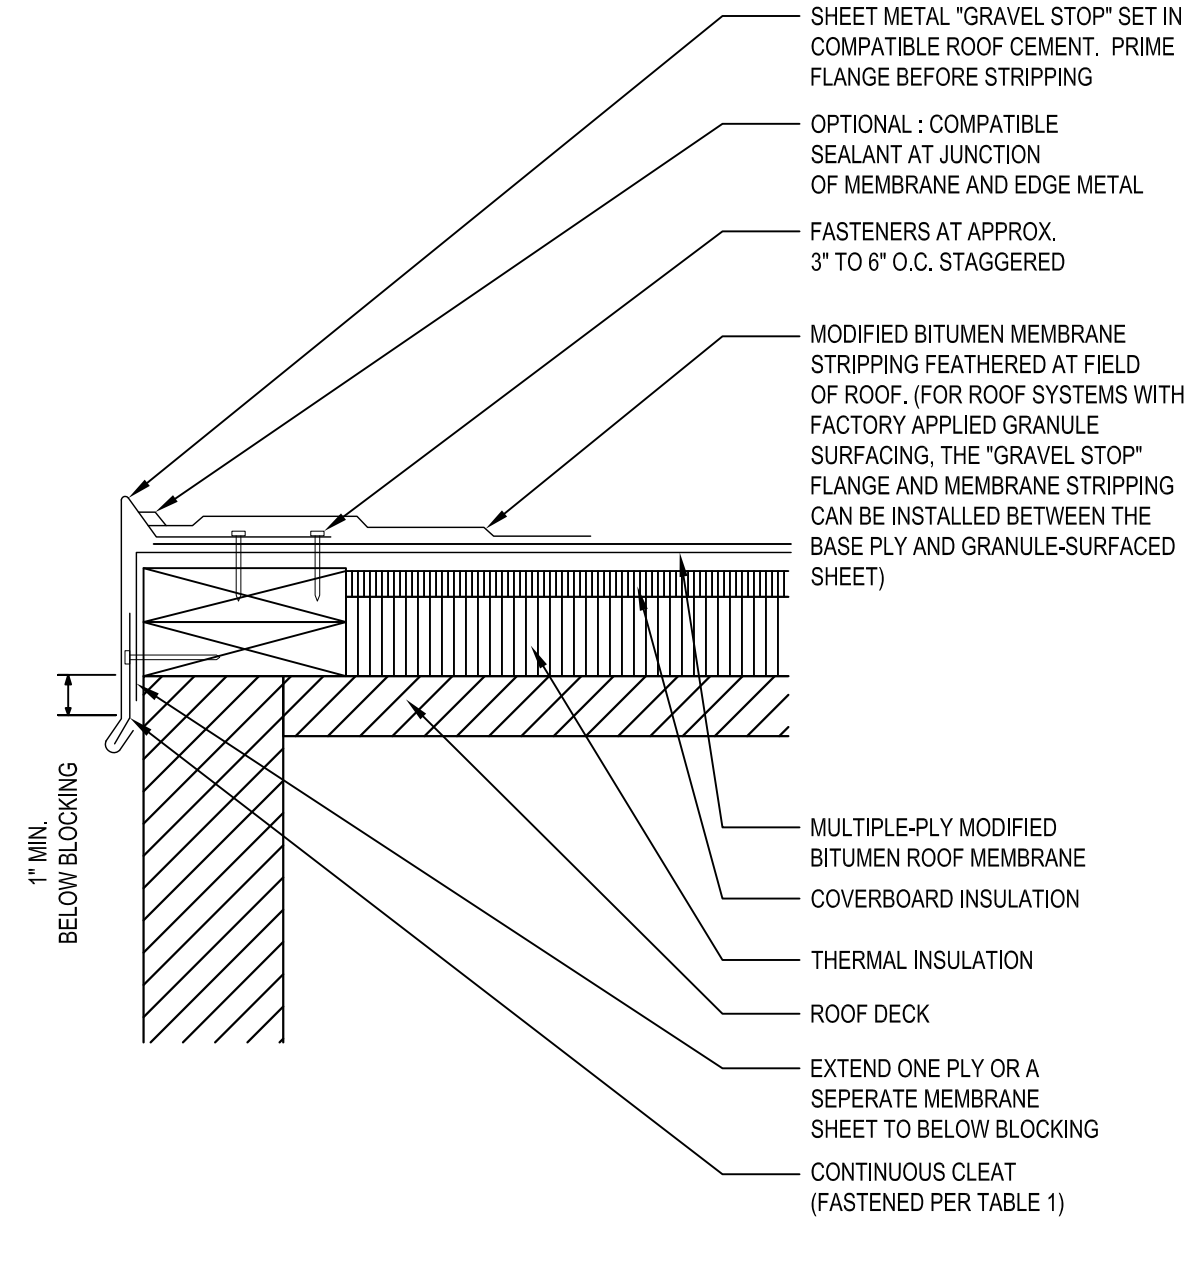

10 EDGE GUARD DETAIL
AE503 SCALE: 1-1/2"=1'-0"

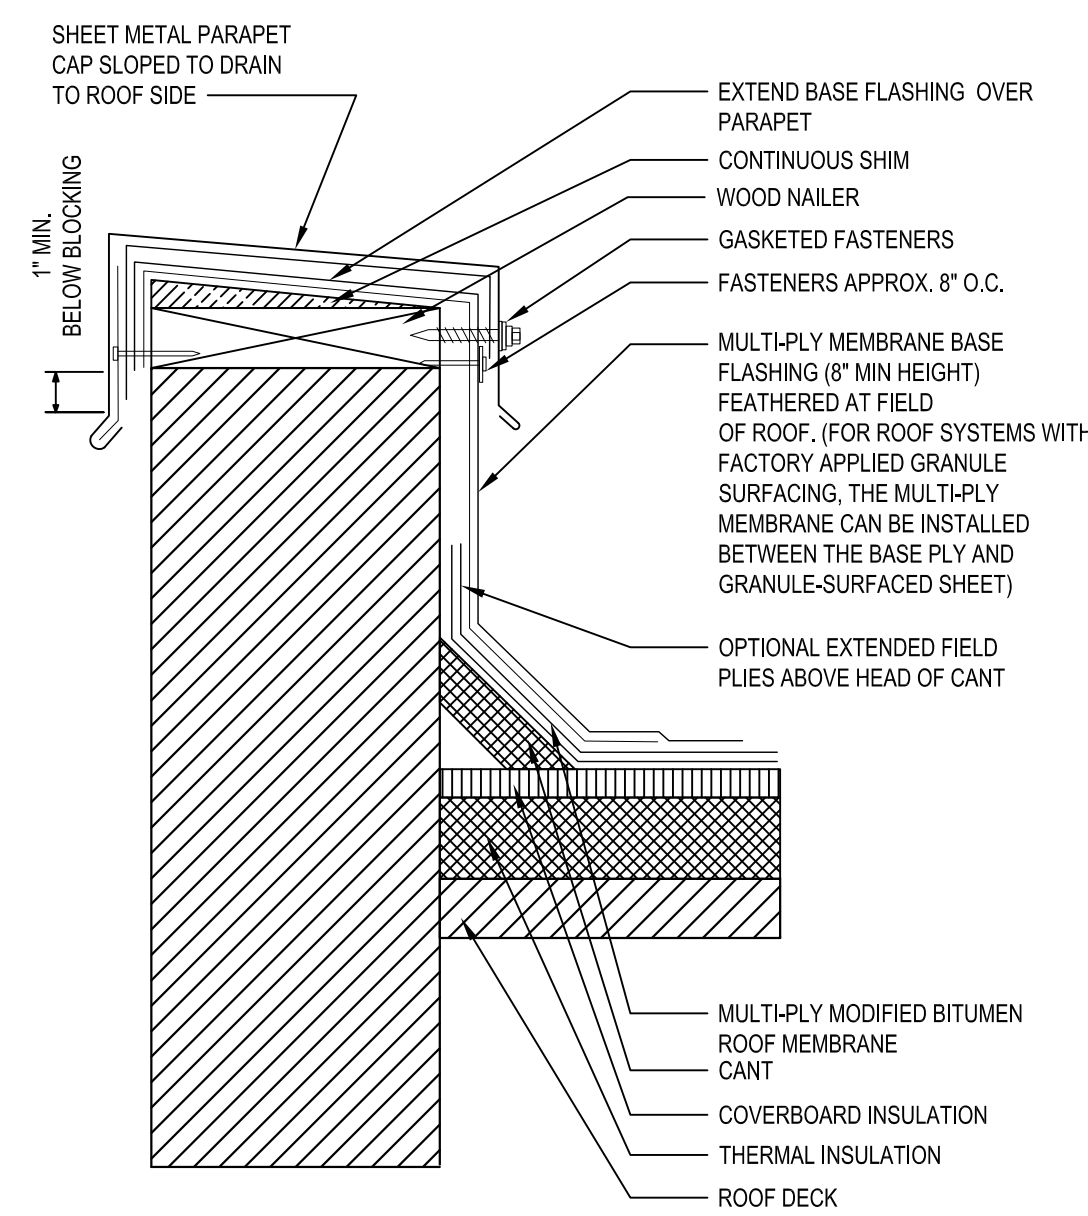

11 PARAPET CAP DETAIL
AE503 SCALE: 1-1/2"=1'-0"

NOTE: THESE ARE STANDARD DETAILS. SEE ENLARGED SECTION FOR ADDITIONAL INFORMATION. SECTION REQUIREMENTS TAKE PRECEDENT OVER THESE TYPICAL DETAILS.

BID DOCUMENTS

Revisions:	Date:

CONSULTANT


ARCHITECT/ENGINEER OF RECORD
THOMAS OLESAK, ARCHITECT
MS Lic # 5505
1050 HOYT AVE WEST ST PAUL, MN 55117
952-451-0460

STAMP
03.10.2023

Office of Construction and Facilities Management
U.S. Department of Veterans Affairs
Drawing Title
ROOF DETAILS
Approved:

Phase
CONSTRUCTION DOCUMENTS
FULLY SPRINKLERED

Project Title
RENOVATE BUILDING 1
Project Number
520-317X
Building Number
1
Drawing Number
AE503
Dwg. 98 of 238
Location
BILOXI, MISSISSIPPI
Issue Date
03/10/2023
Checked
LA
Drawn
CD

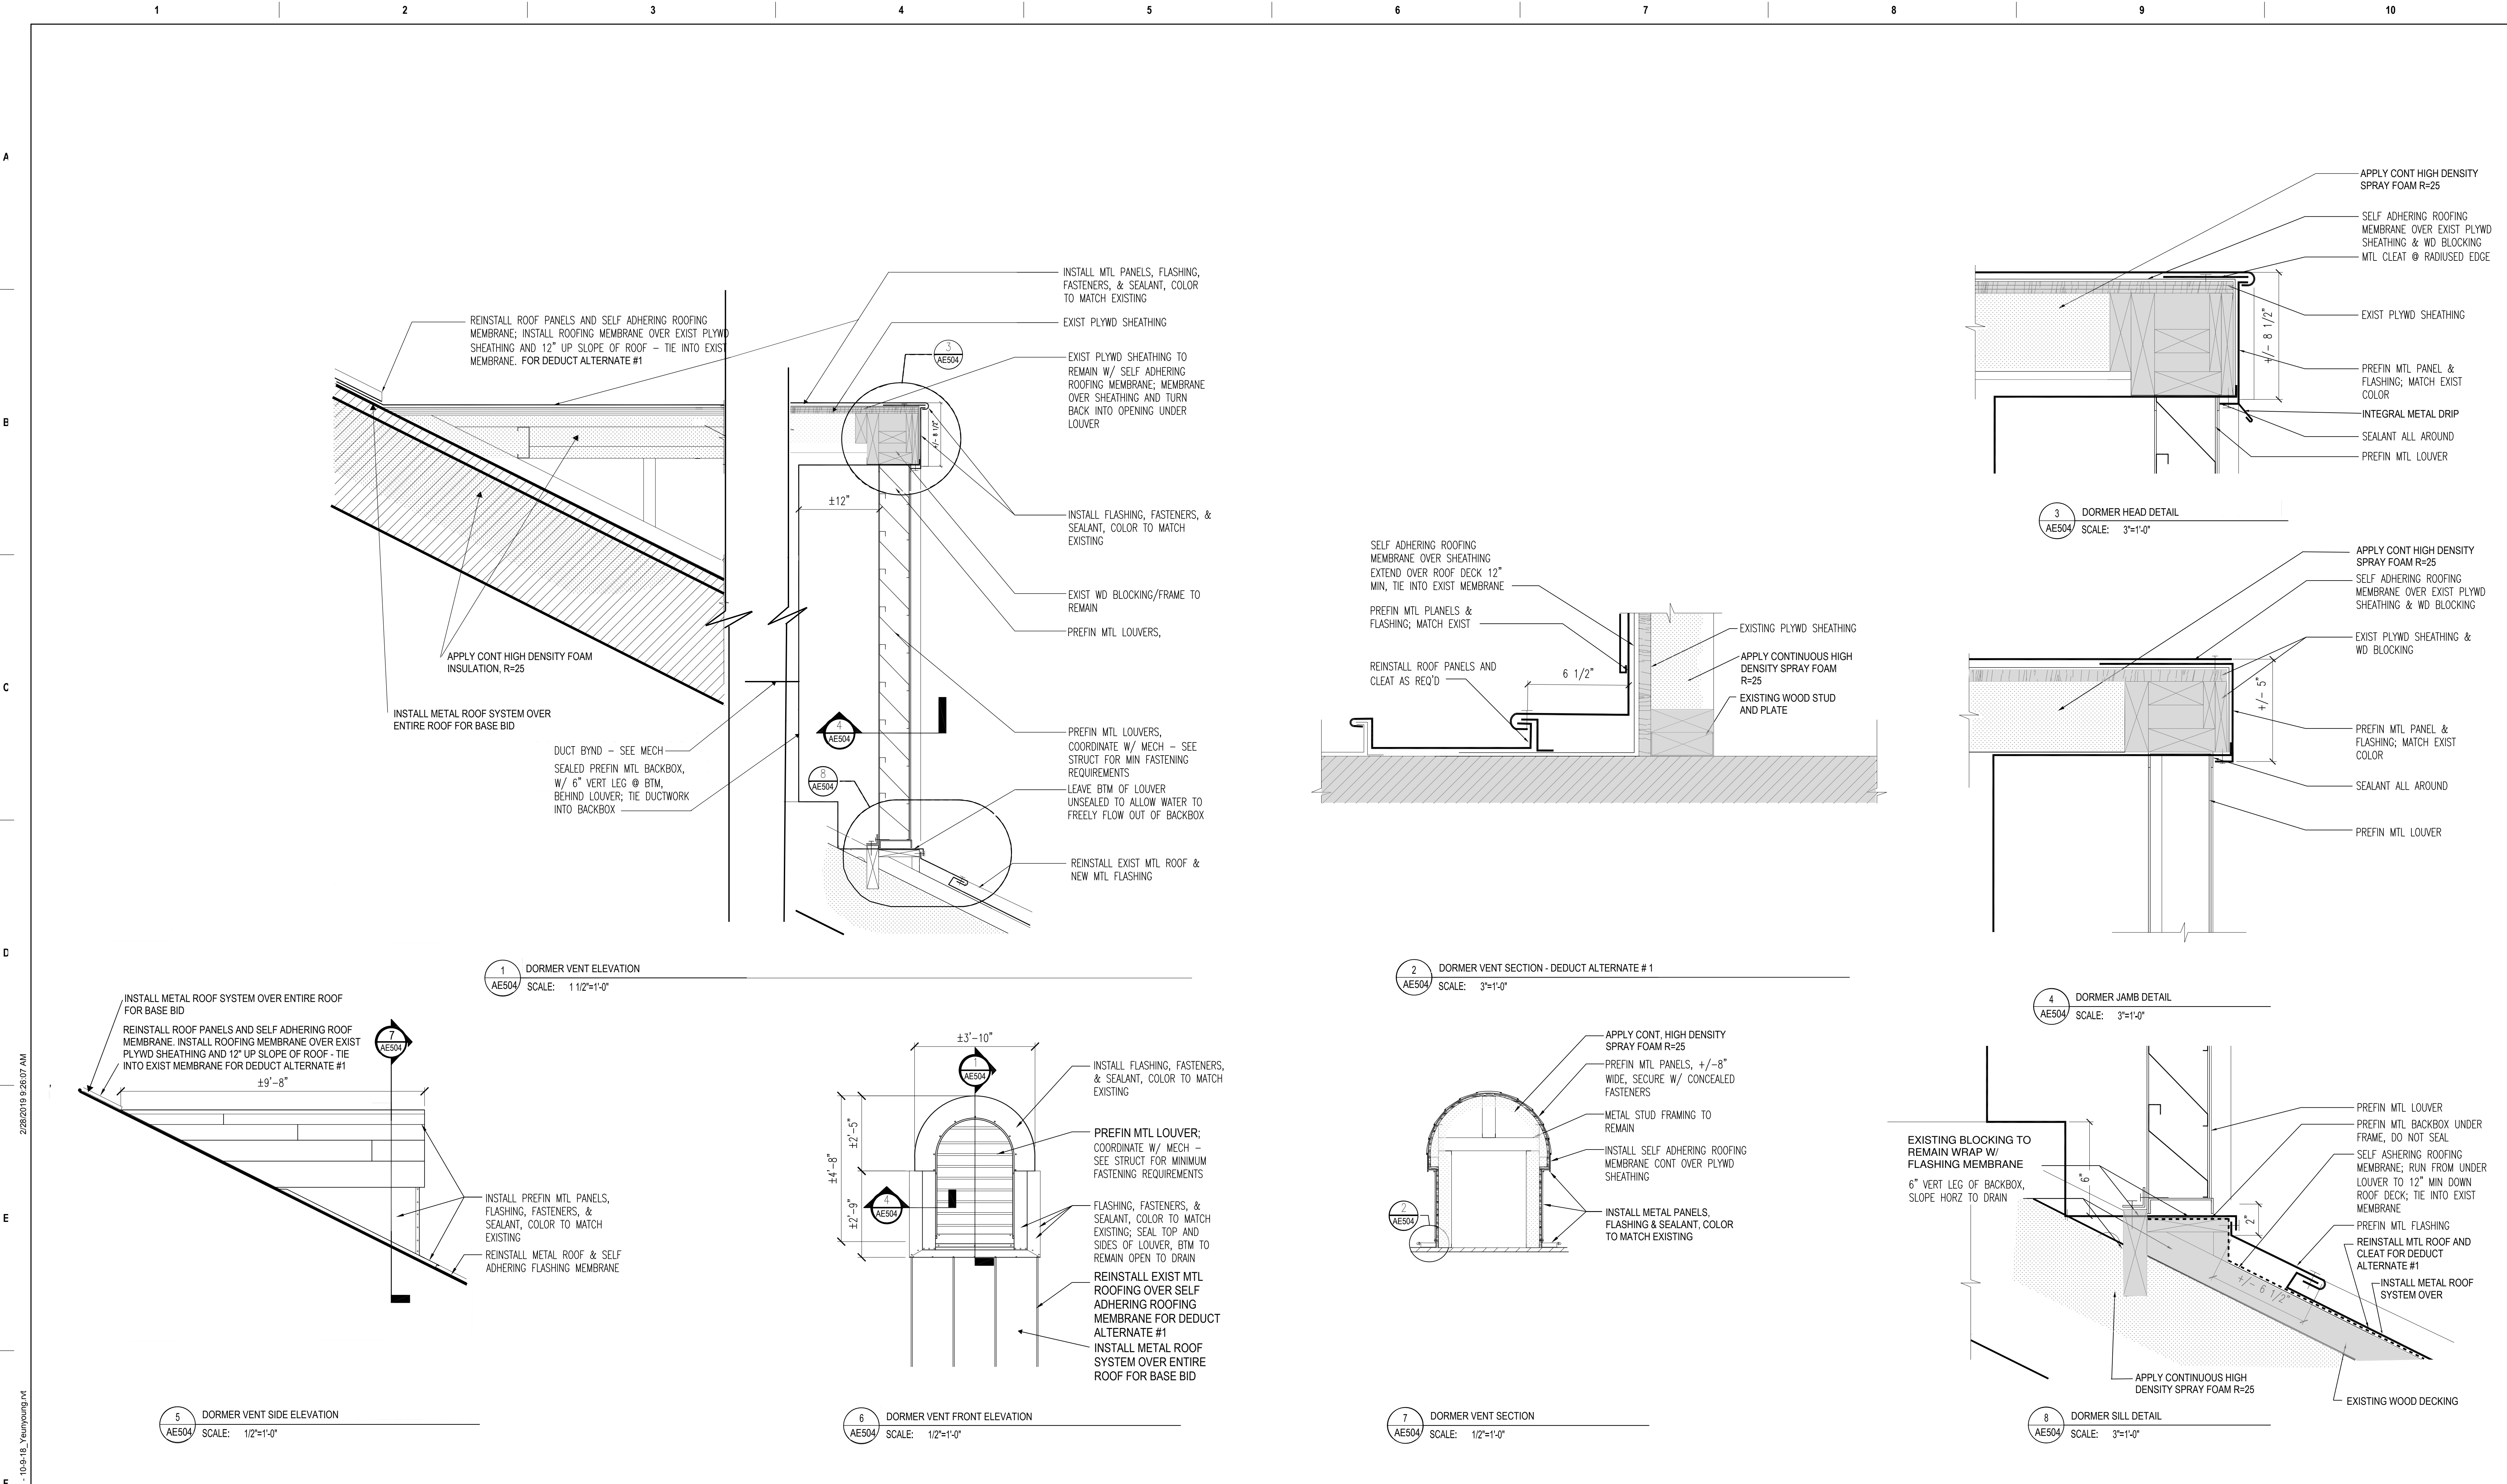

BID DOCUMENTS


Revisions: Date:	CONSULTANT	ARCHITECT/ENGINEER OF RECORD THOMAS OLESAK, ARCHITECT MS Lic # 5505 1050 HOYT AVE WEST ST PAUL, MN 55117 952-451-0460	STAMP 03.10.2023	Office of Construction and Facilities Management VA U.S. Department of Veterans Affairs	Drawing Title DORMER DETAILS Approved:	Phase CONSTRUCTION DOCUMENTS FULLY SPRINKLERED	Project Title RENOVATE BUILDING 1		Project Number 520-317X
							Location BILOXI, MISSISSIPPI		Building Number 1
							Issue Date 03/10/2023	Checked LA	Drawn CD
							Dwg. 99 of 238		Drawing Number AE504



Dwg.	100	01	230
------	-----	----	-----


[illegible]

Project Title RENOVATE BUILDING 1			Project Number 520-317X	
			Building Number 1	
Location BILOXI, MISSISSIPPI			Drawing Number AE511	
Issue Date 03/10/2023	Checked LA	Drawn CD	Dwg. 100 of 238	

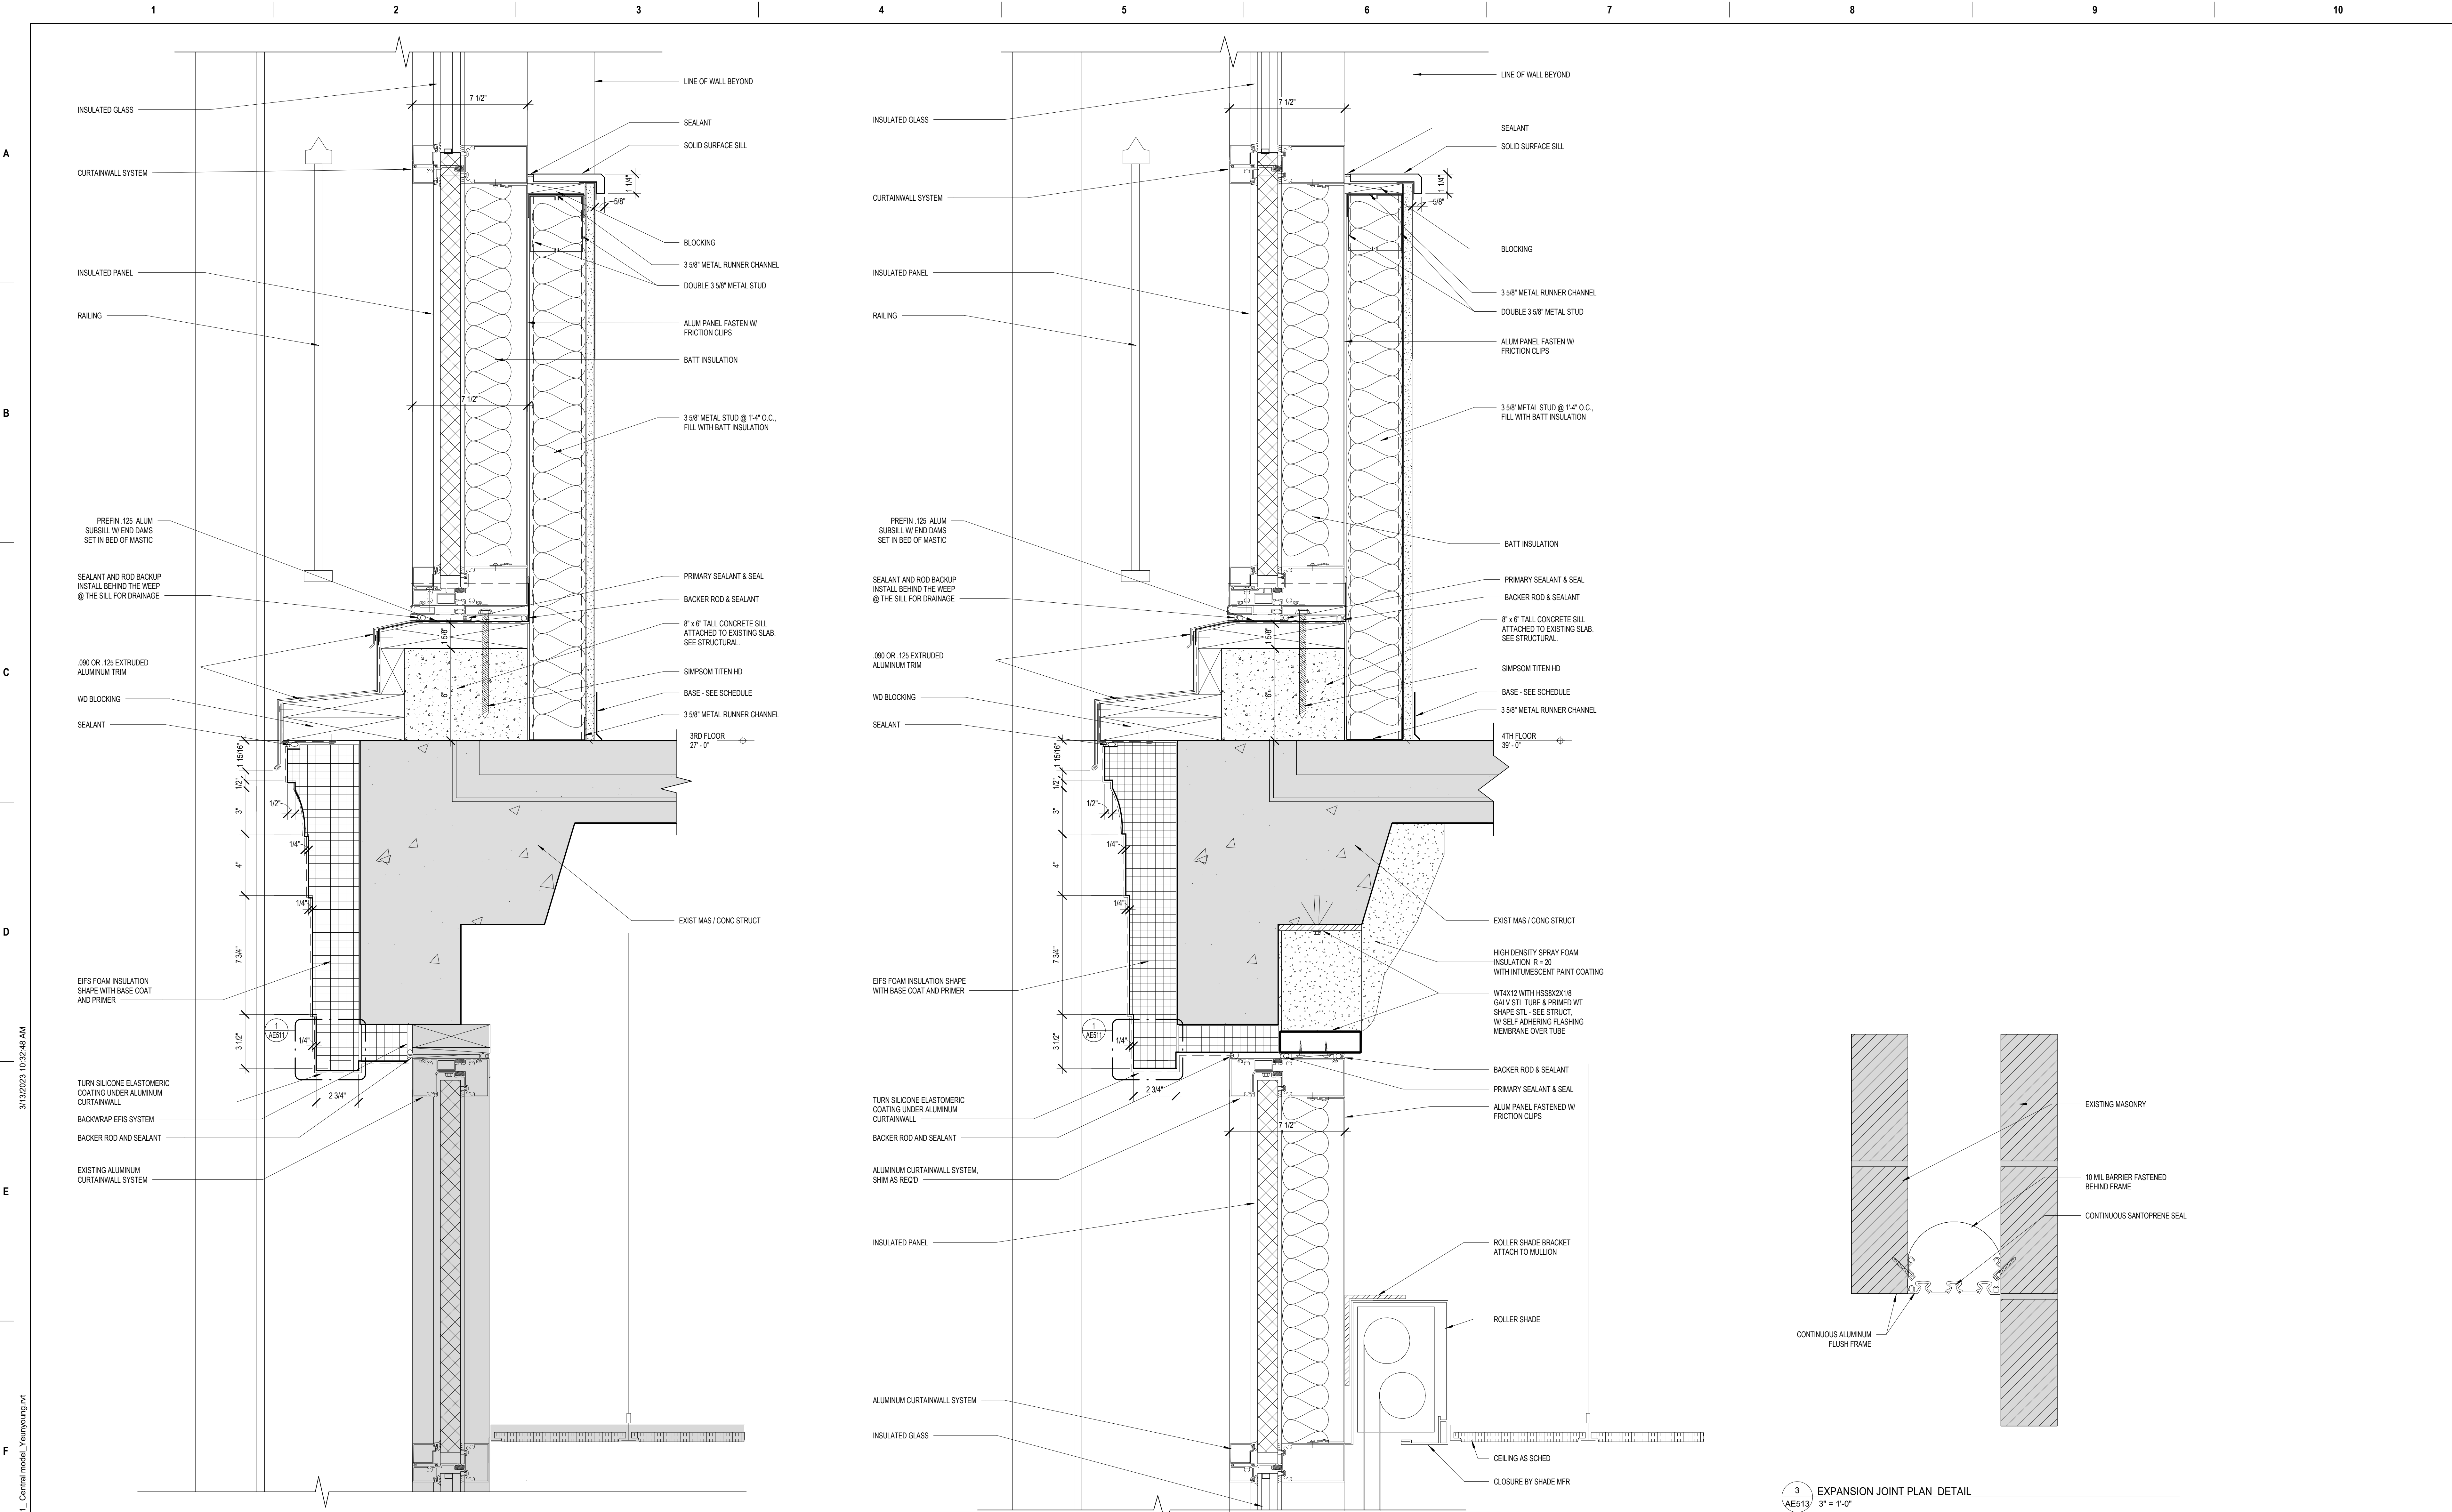


FOR ADDITIONAL NOTES AND INFORMATION SEE S408			FOR ADDITIONAL NOTES AND INFORMATION SEE S408			FOR ADDITIONAL NOTES AND INFORMATION SEE S408		
1 PARTIAL CURTAINWALL SECTION - ALTERNATE. AE513 3" = 1'-0"			2 PARTIAL CURTAINWALL SECTION - ALTERNATE AE513 3" = 1'-0"			3 EXPANSION JOINT PLAN DETAIL AE513 3" = 1'-0"		
CONSULTANT			ARCHITECT/ENGINEER OF RECORD			Drawing Title WALL DETAILS		
THOMAS OLESAC, ARCHITECT			THOMAS OLESAC, ARCHITECT			Office of Construction and Facilities Management		
MS Lic # 5505			MS Lic # 5505			U.S. Department of Veterans Affairs		
1050 HOYT AVE WEST ST PAUL, MN 55117			1050 HOYT AVE WEST ST PAUL, MN 55117			U.S. Department of Veterans Affairs		
952-451-0460			952-451-0460			U.S. Department of Veterans Affairs		
STAMP			STAMP			STAMP		
03.10.2023			03.10.2023			03.10.2023		
Approved:			Approved:			Approved:		
Phase			Phase			Phase		
CONSTRUCTION DOCUMENTS			CONSTRUCTION DOCUMENTS			CONSTRUCTION DOCUMENTS		
FULLY SPRINKLERED			FULLY SPRINKLERED			FULLY SPRINKLERED		
Project Title			Project Title			Project Title		
RENOVATE BUILDING 1			RENOVATE BUILDING 1			RENOVATE BUILDING 1		
Location			Location			Location		
BILOXI, MISSISSIPPI			BILOXI, MISSISSIPPI			BILOXI, MISSISSIPPI		
Issue Date			Issue Date			Issue Date		
03/10/2023			03/10/2023			03/10/2023		
Checked			Checked			Checked		
LA			LA			LA		
Drawn			Drawn			Drawn		
CD			CD			CD		
Project Number			Project Number			Project Number		
520-317X			520-317X			520-317X		
Building Number			Building Number			Building Number		
1			1			1		
Drawing Number			Drawing Number			Drawing Number		
AE513			AE513			AE513		
Dwg. 102 of 238			Dwg. 102 of 238			Dwg. 102 of 238		


A

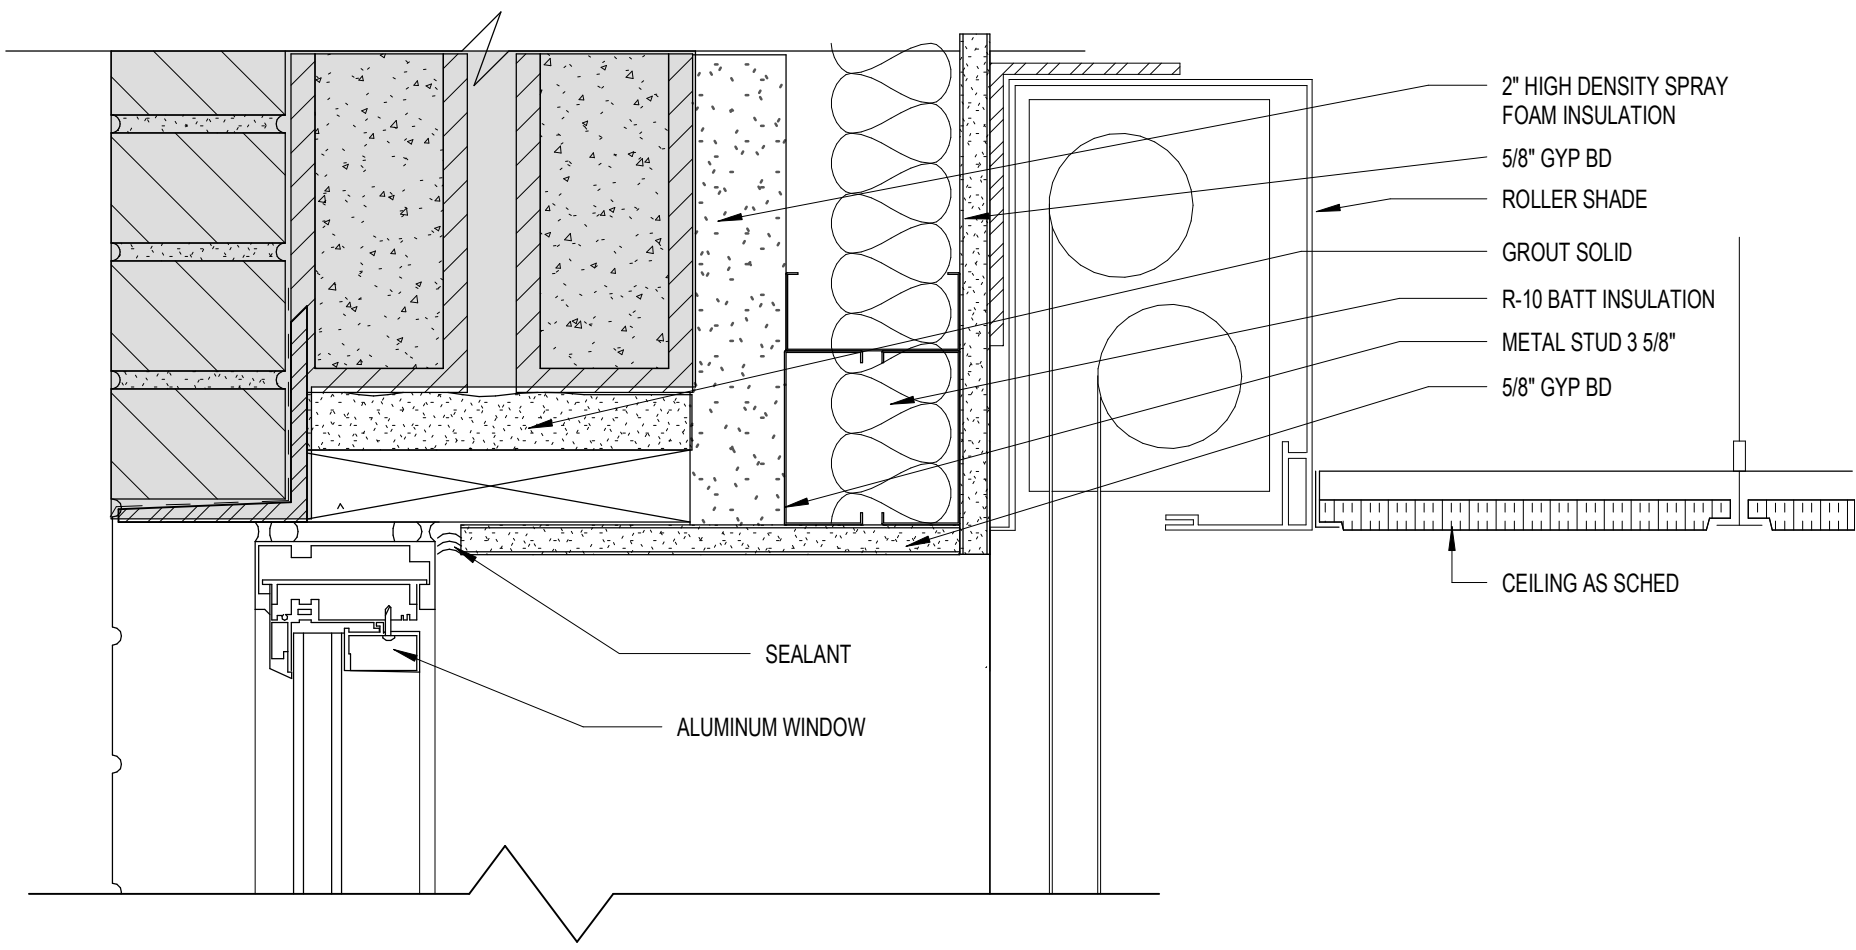

1 ALUMINUM WINDOW HEAD DETAIL
AE514 3" = 1'-0"

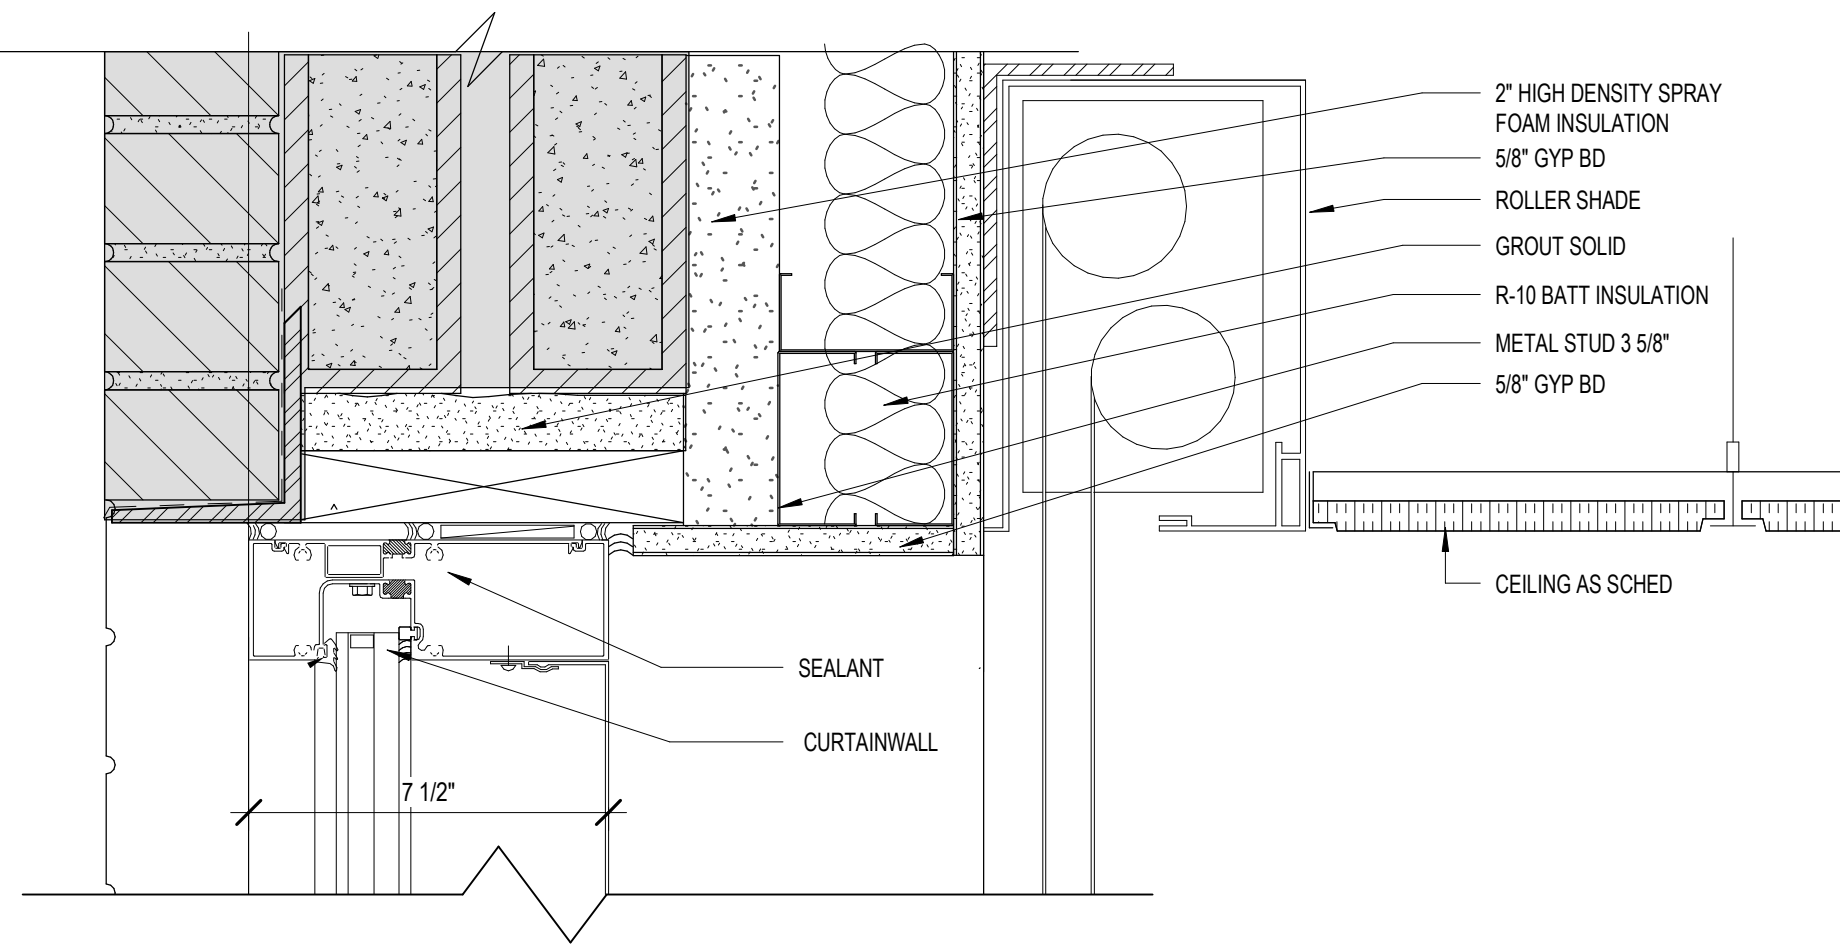


5 CURTAINWALL HEAD DETAIL
AE514 3" = 1'-0"

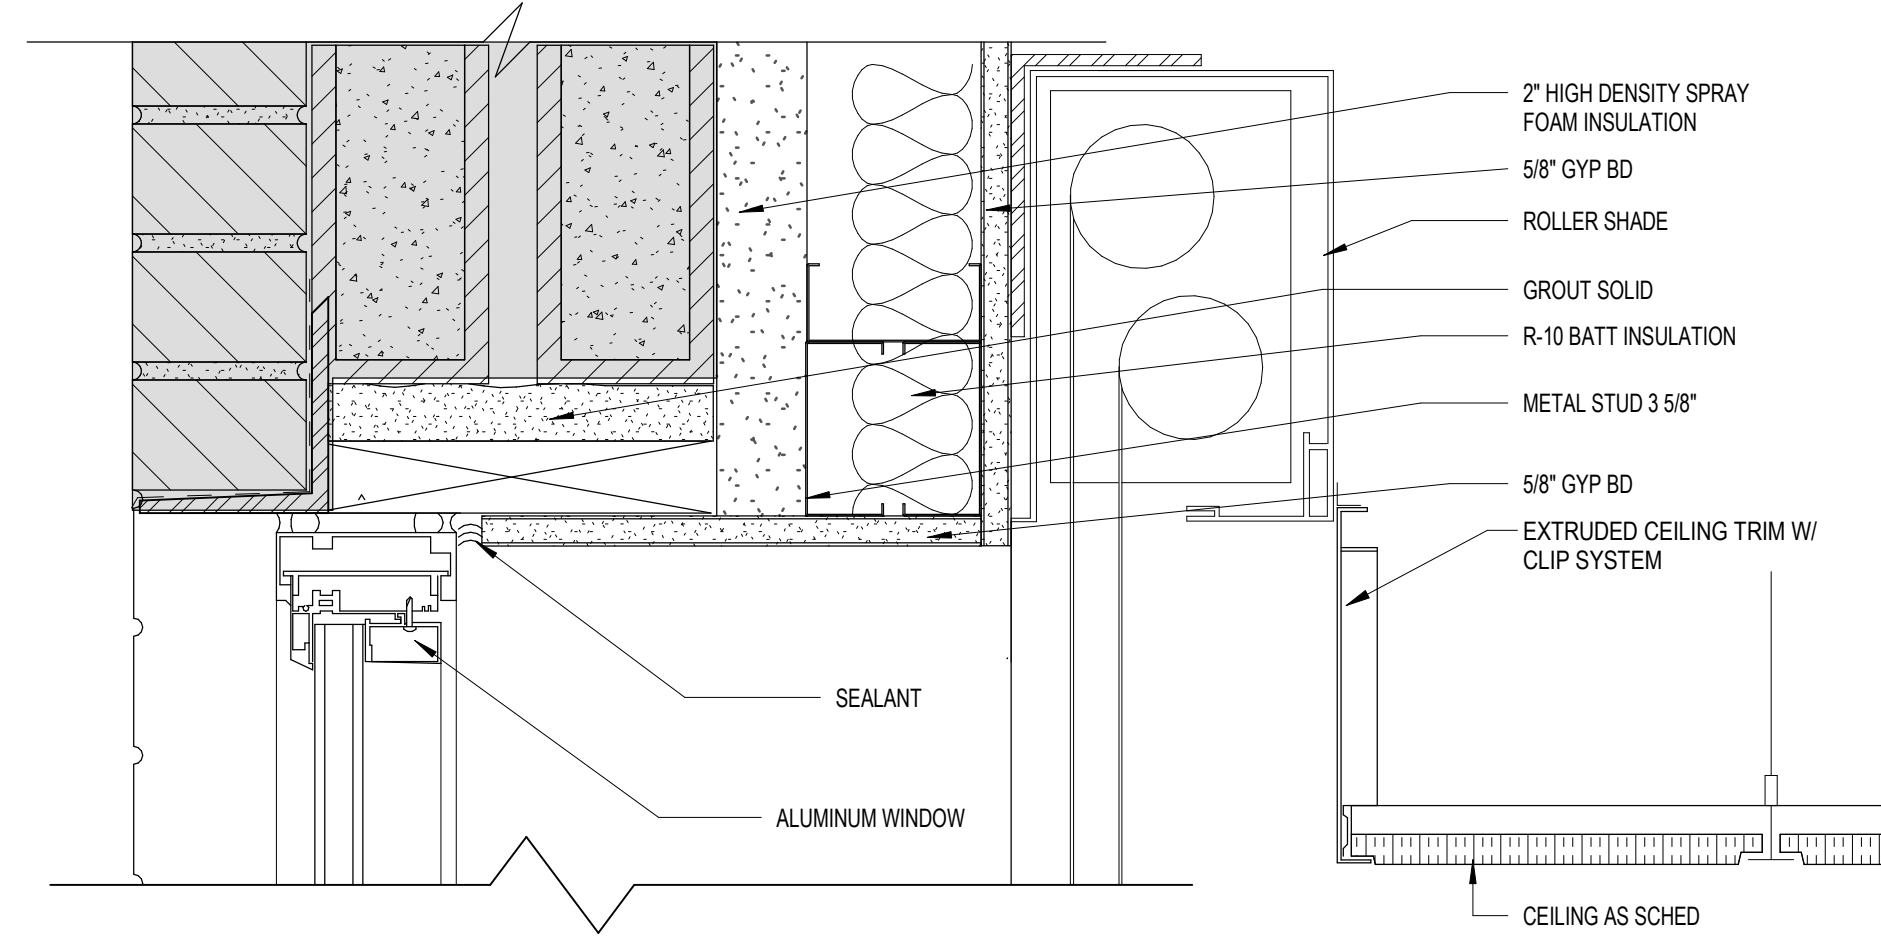


9 WINDOW HEAD
AE514 3" = 1'-0"


B

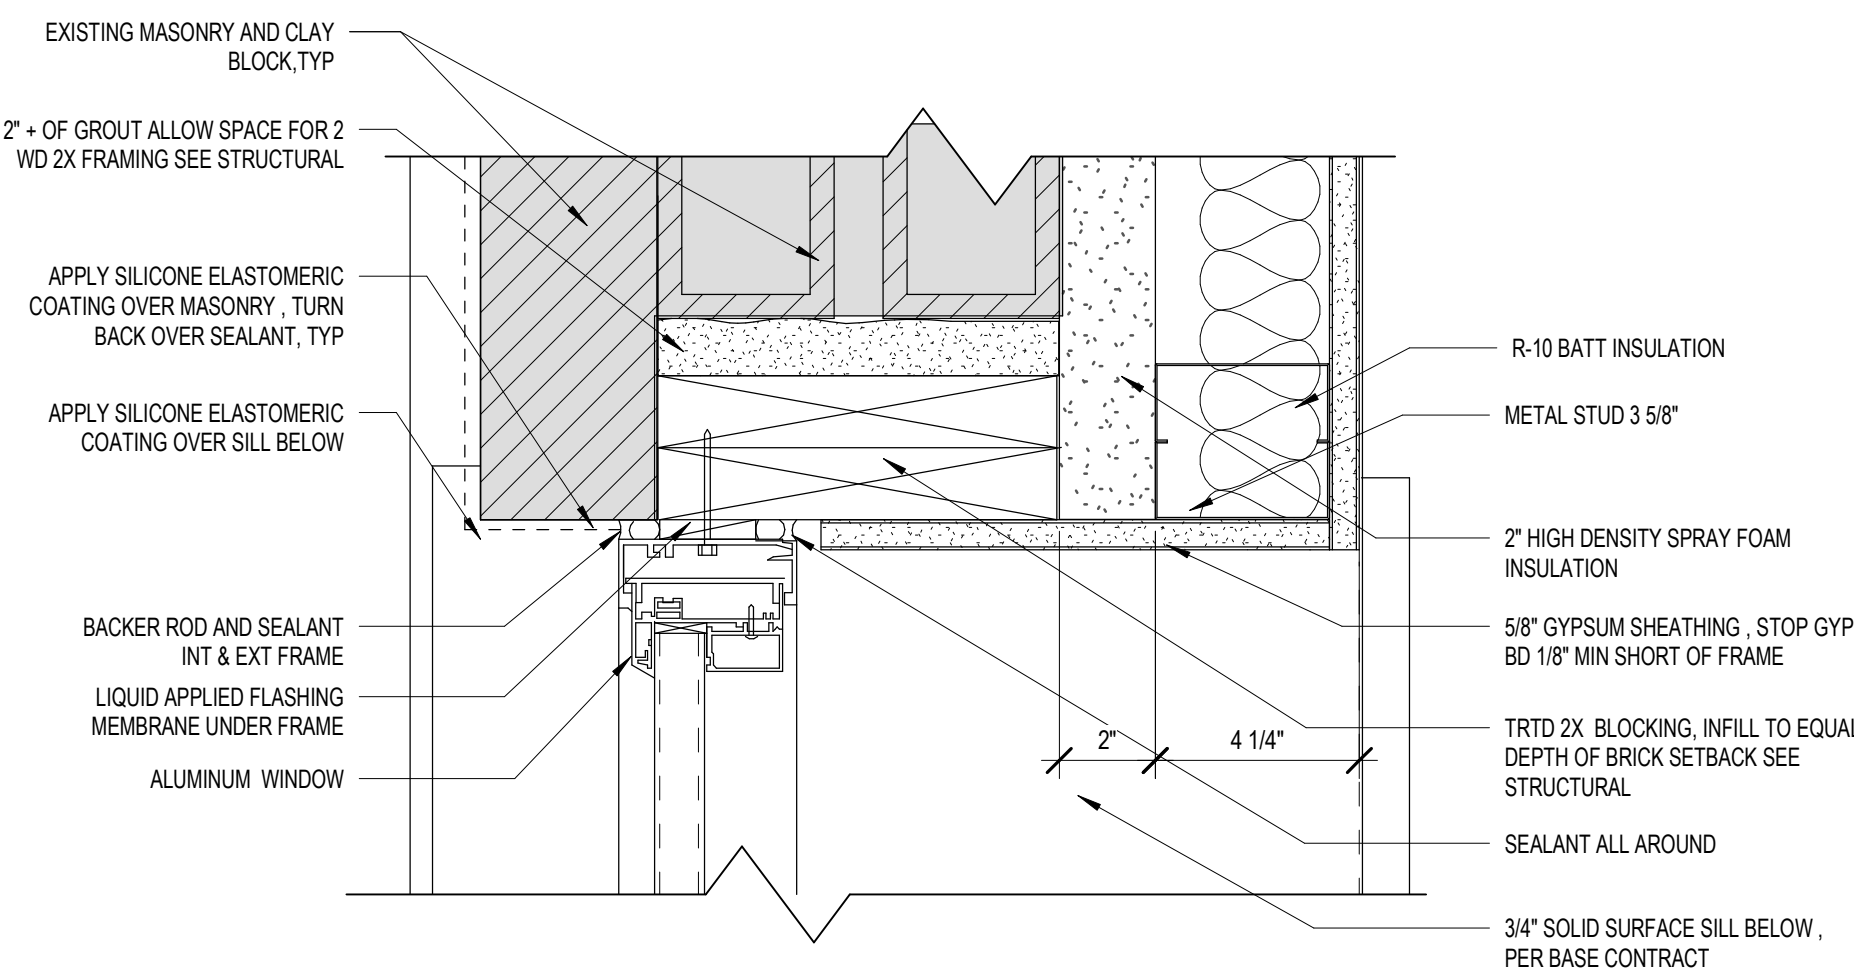

2 ALUMINUM WINDOW JAMB DETAIL
AE514 3" = 1'-0"

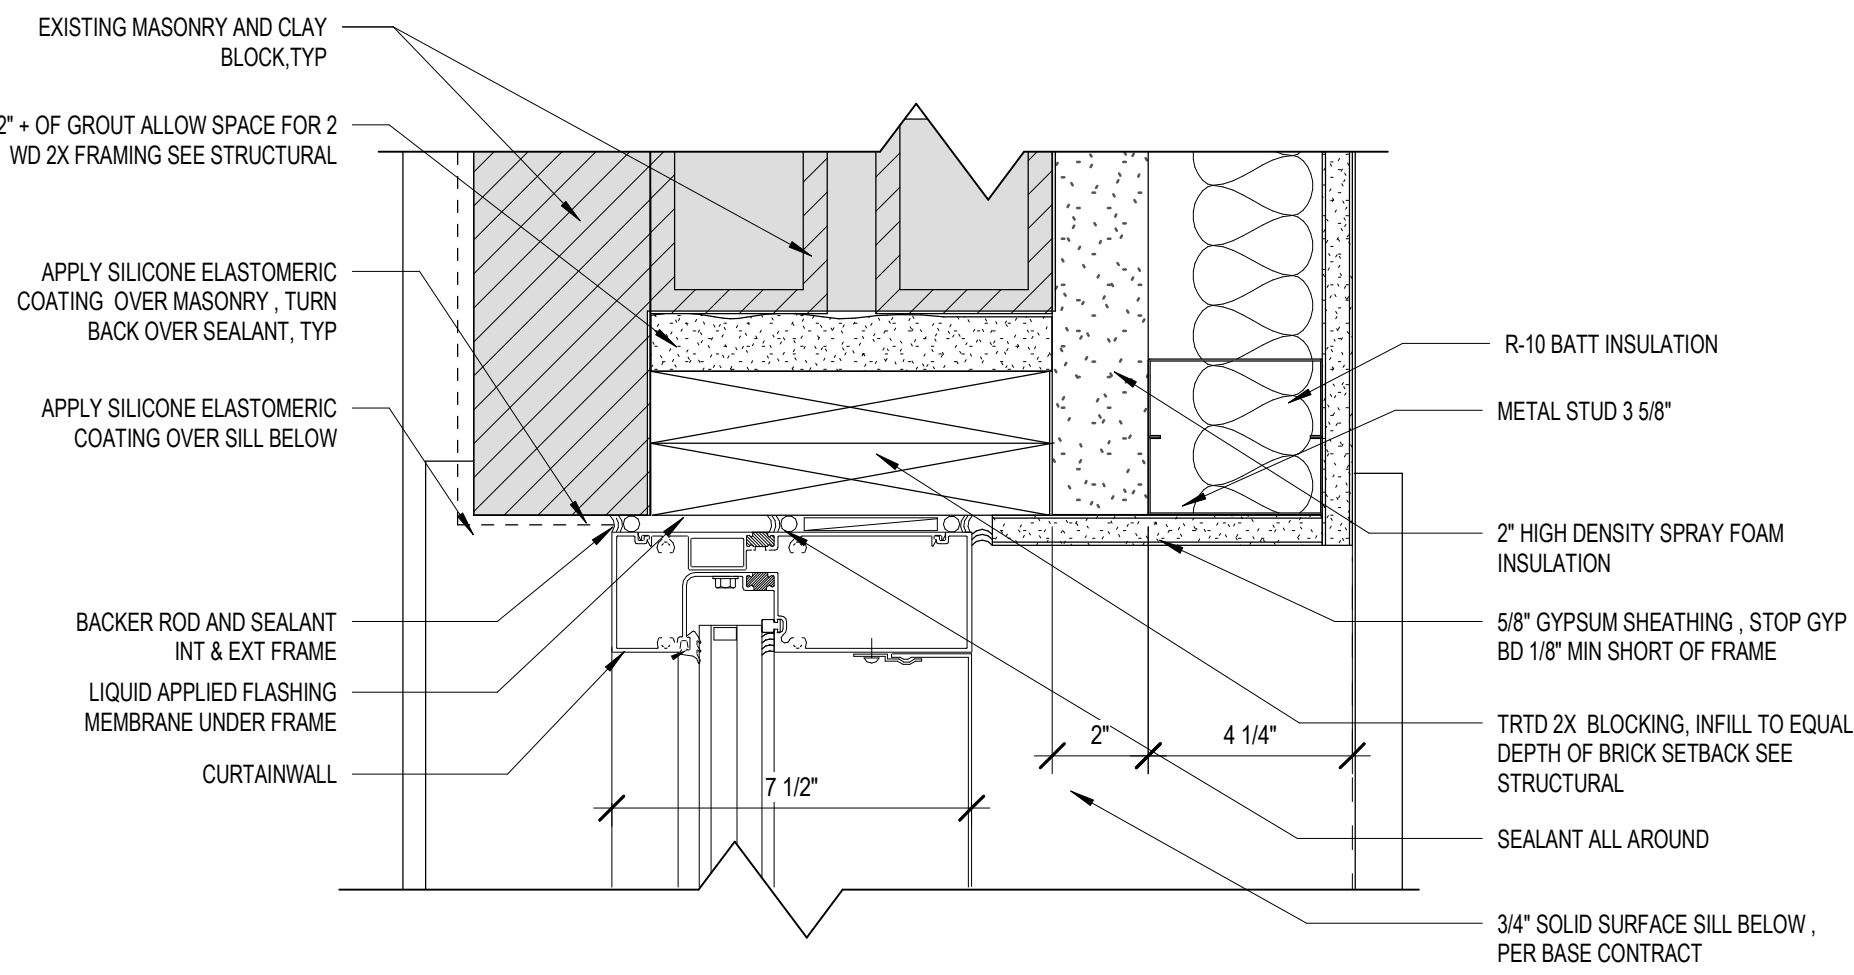


6 CURTAINWALL JAMB DETAIL
AE514 3" = 1'-0"

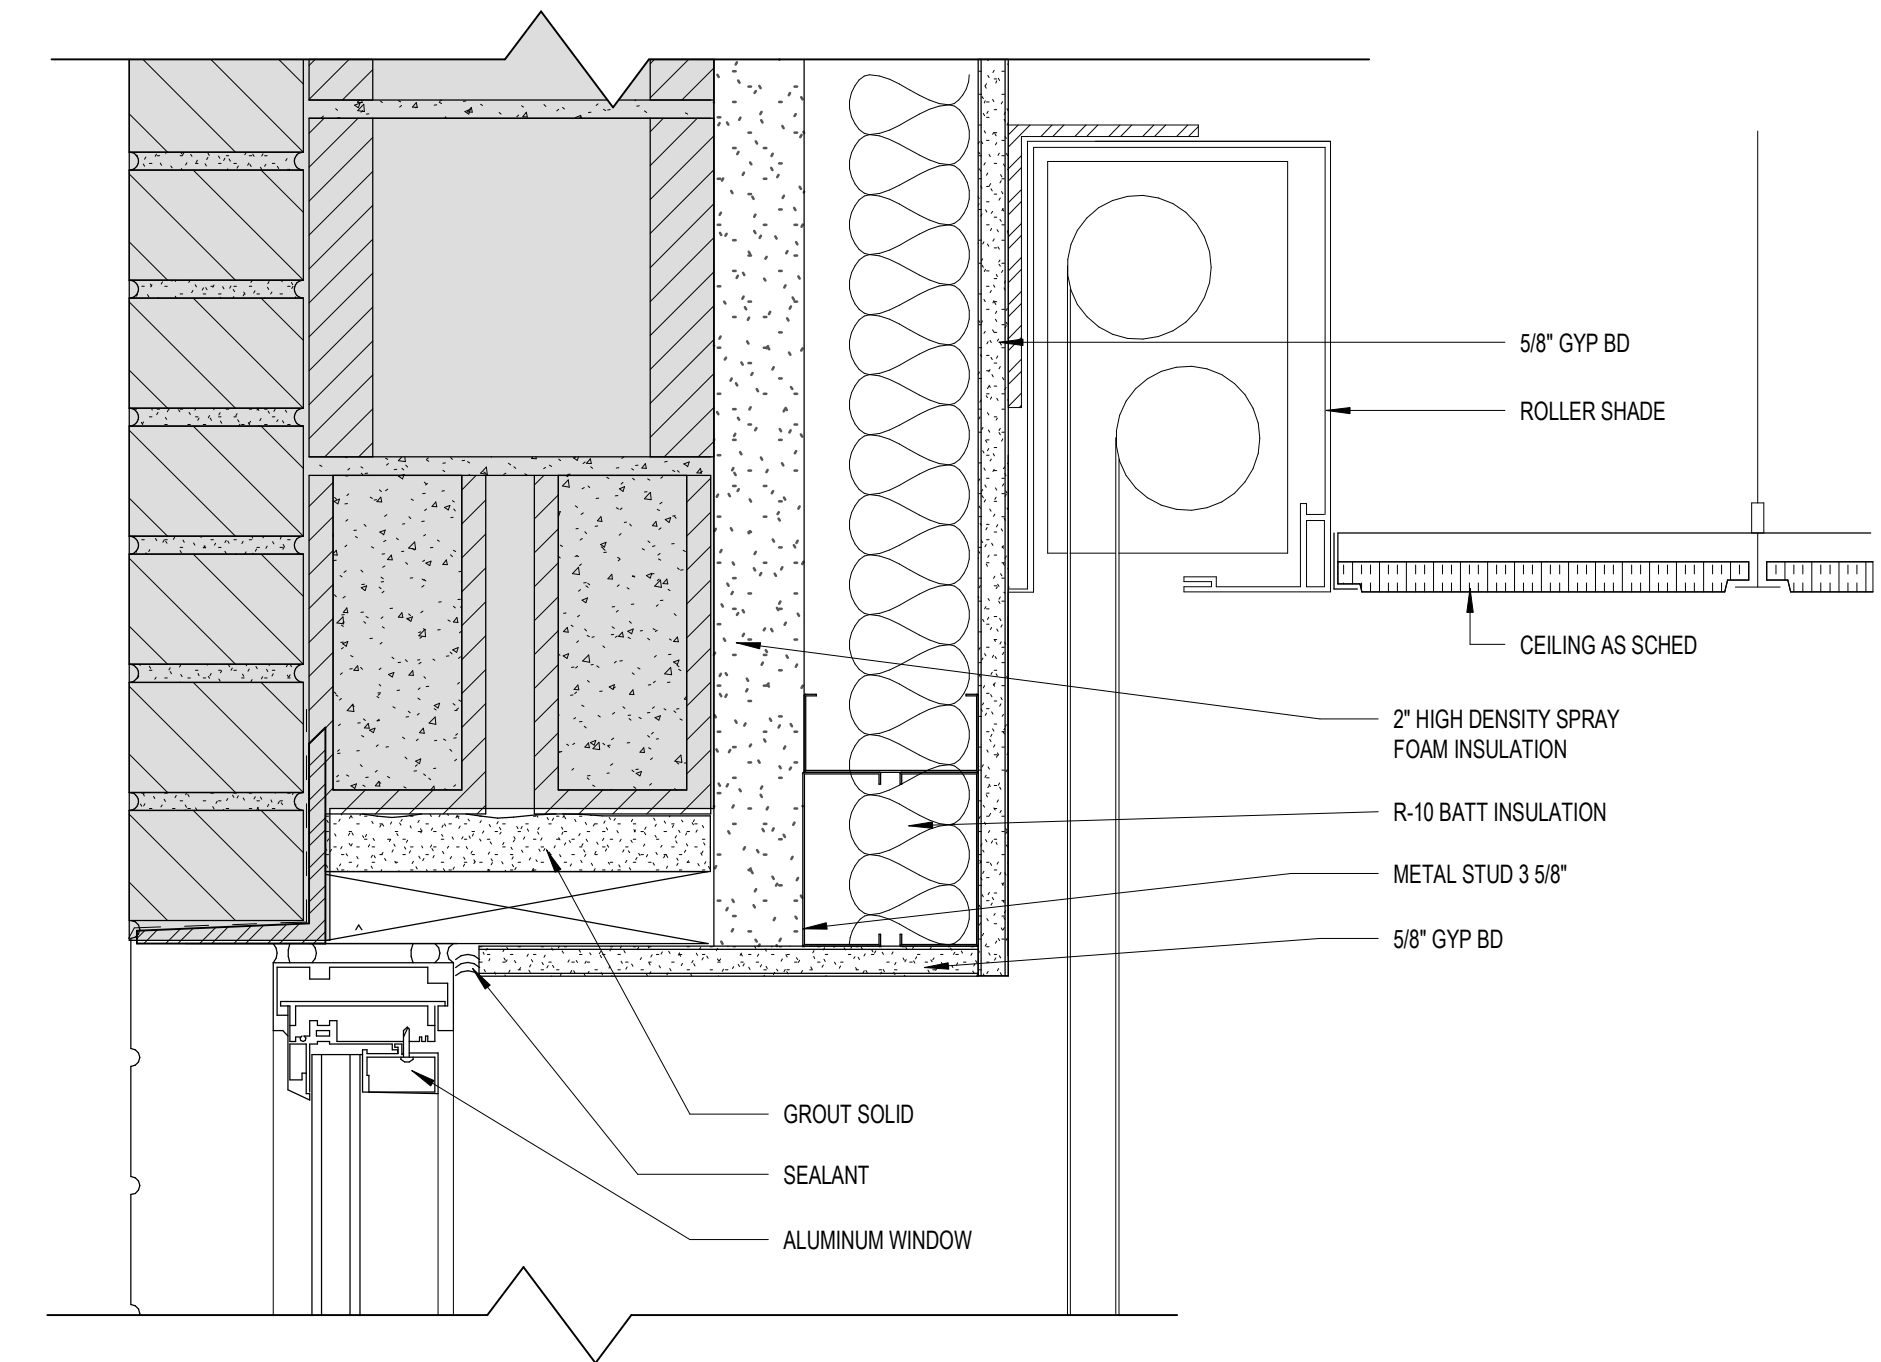


10 ALUMINUM WINDOW HEAD DETAIL
AE514 3" = 1'-0"


D

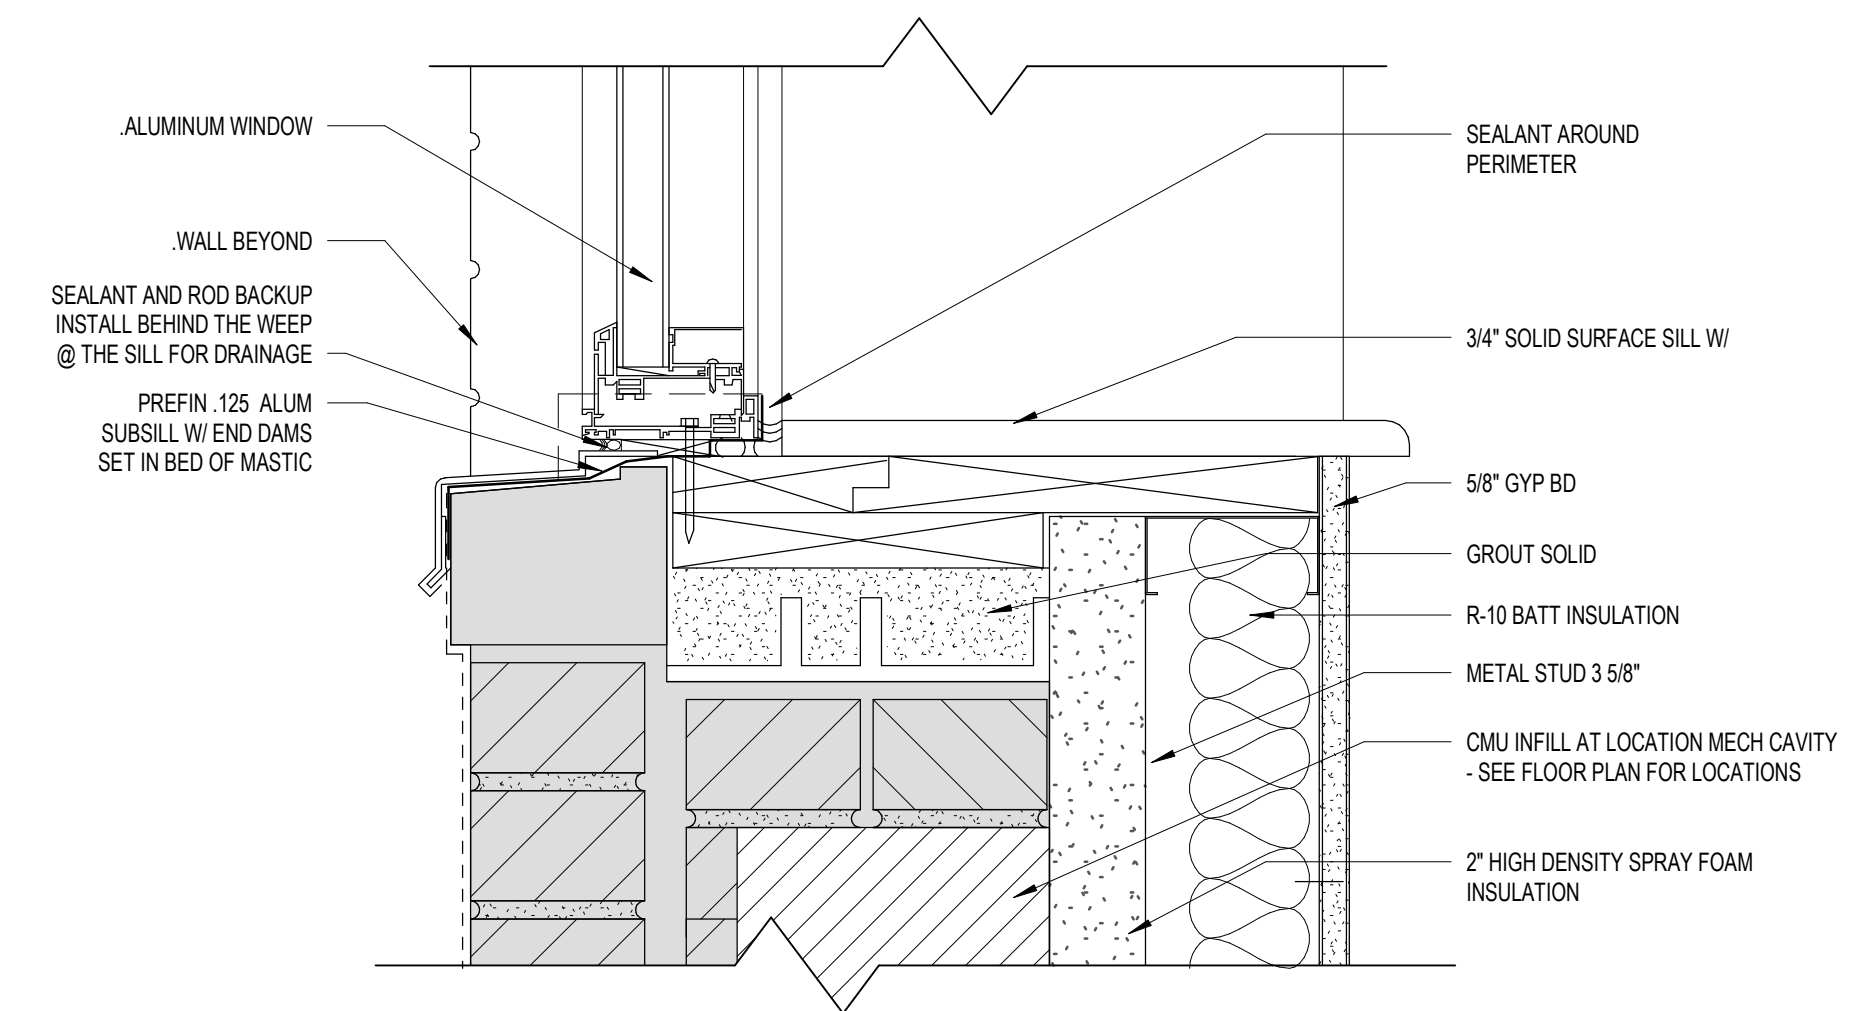

3 ALUMINUM WINDOW SILL DETAIL
AE514 3" = 1'-0"

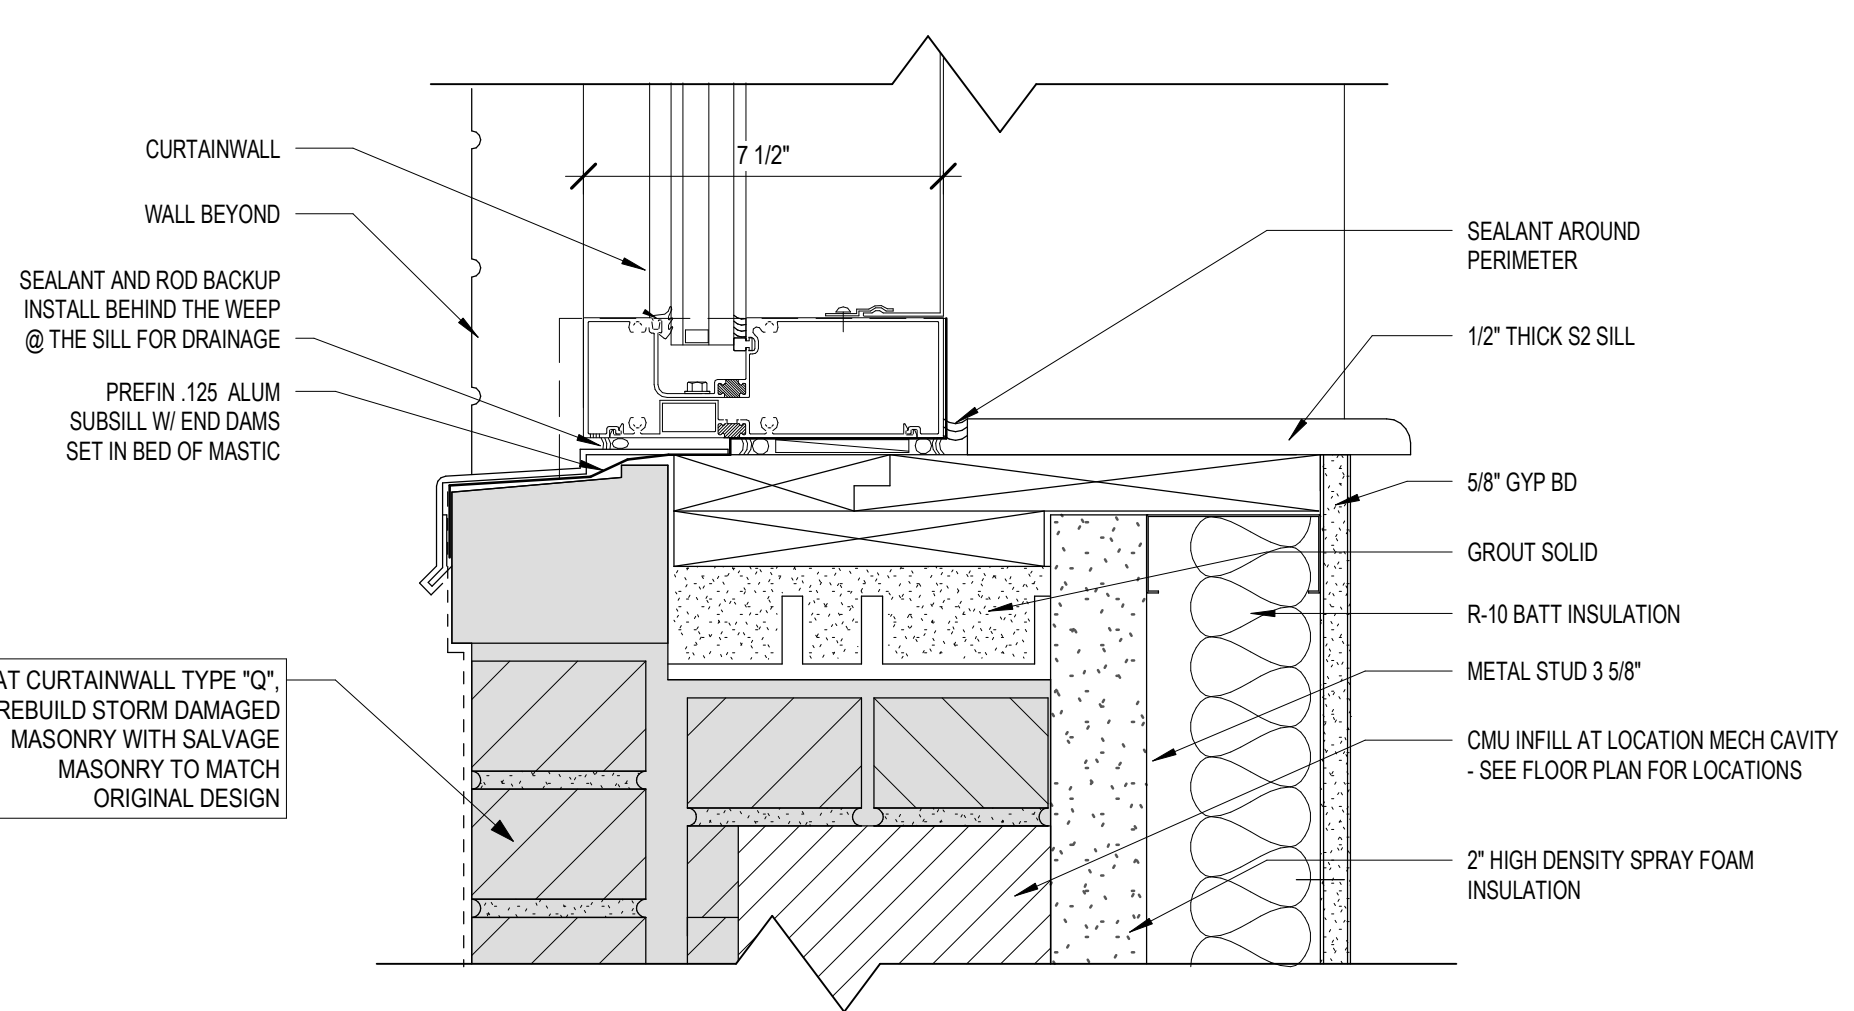


7 CURTAINWALL SILL DETAIL
AE514 3" = 1'-0"

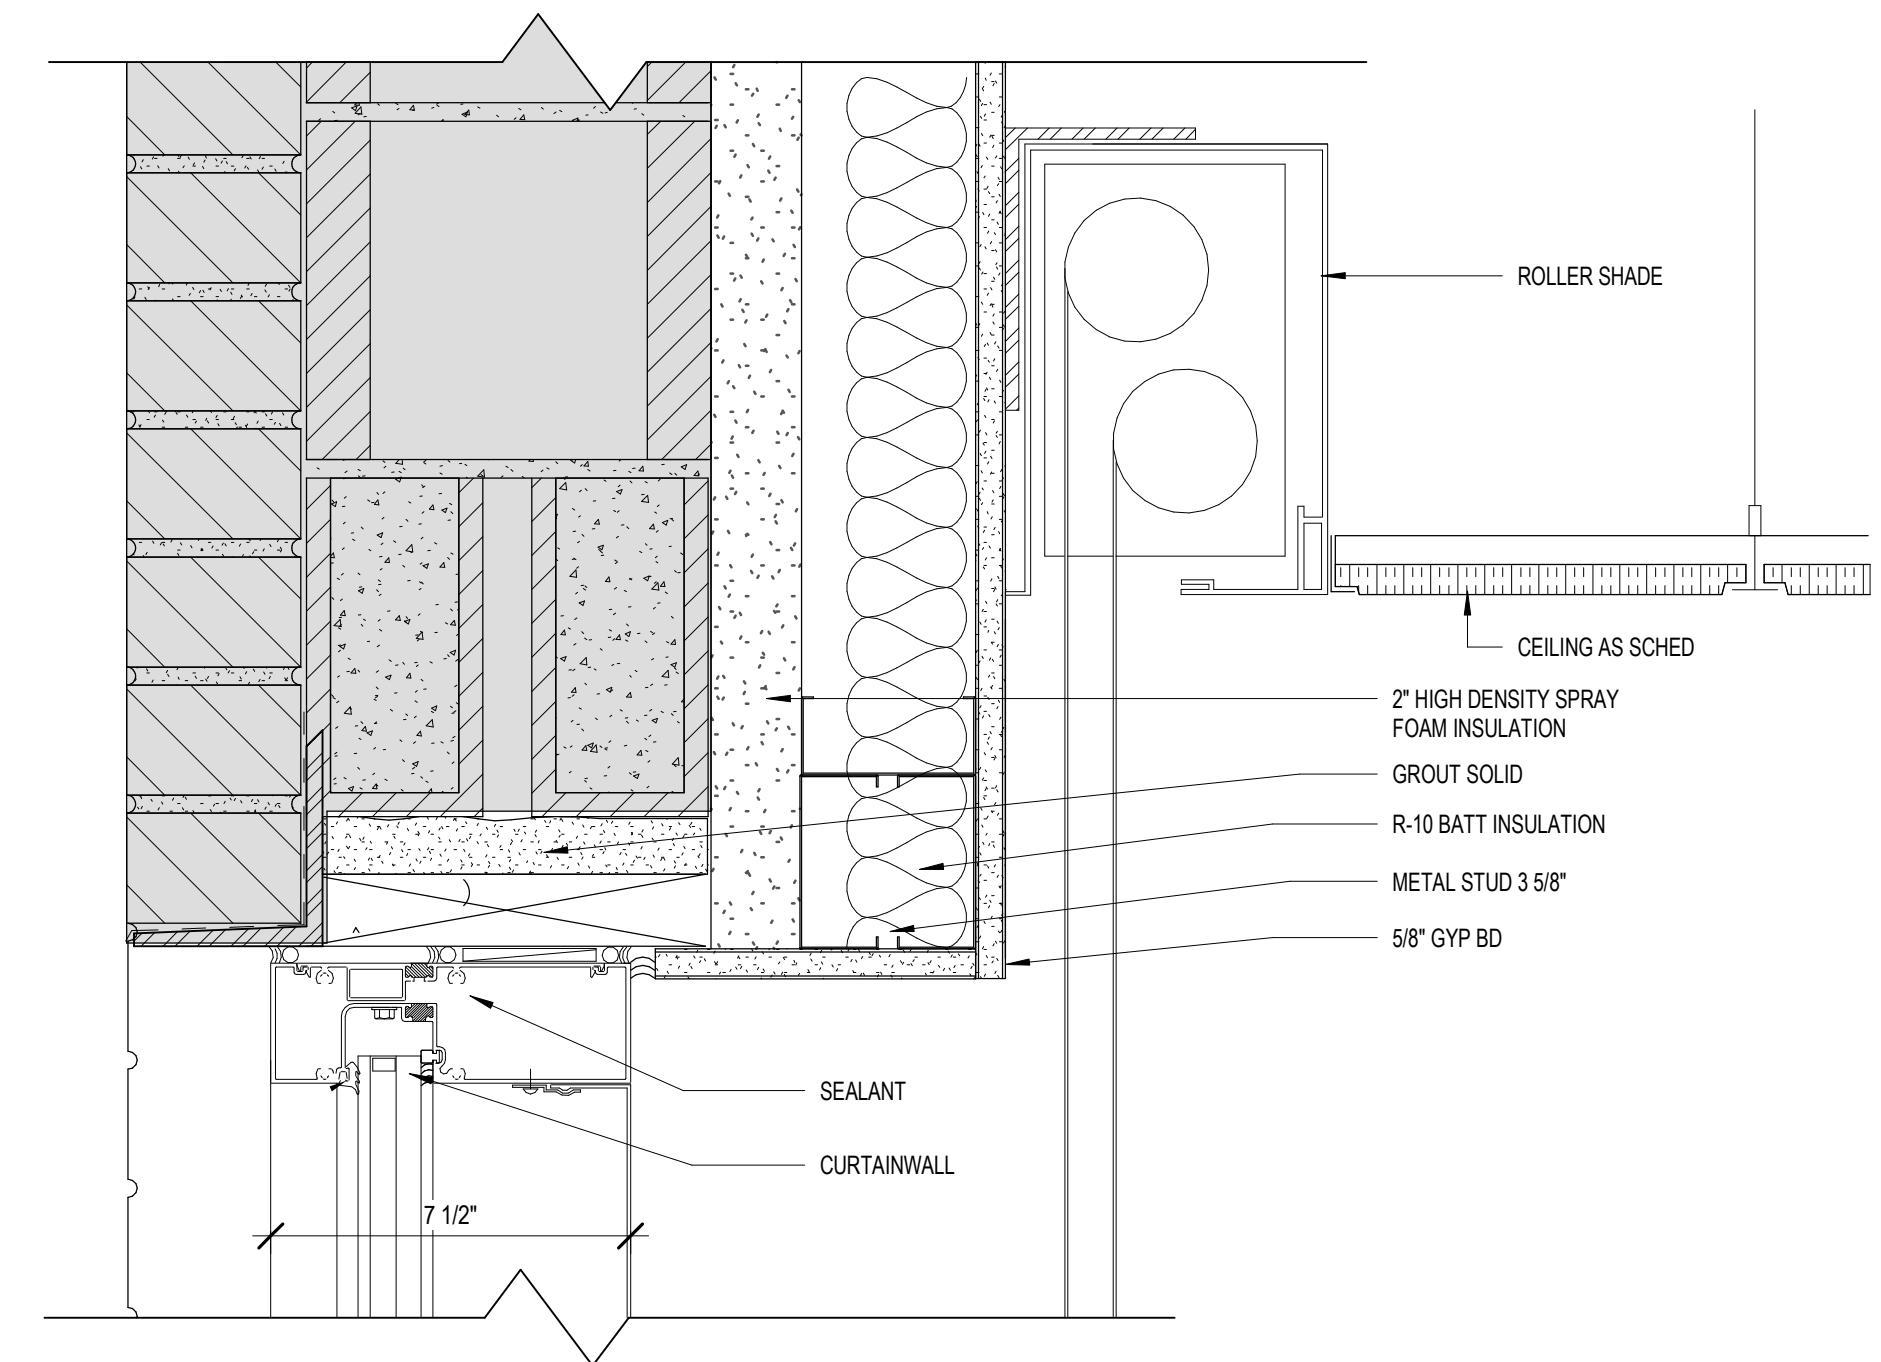


11 CURTAINWALL HEAD DETAIL
AE514 3" = 1'-0"

F

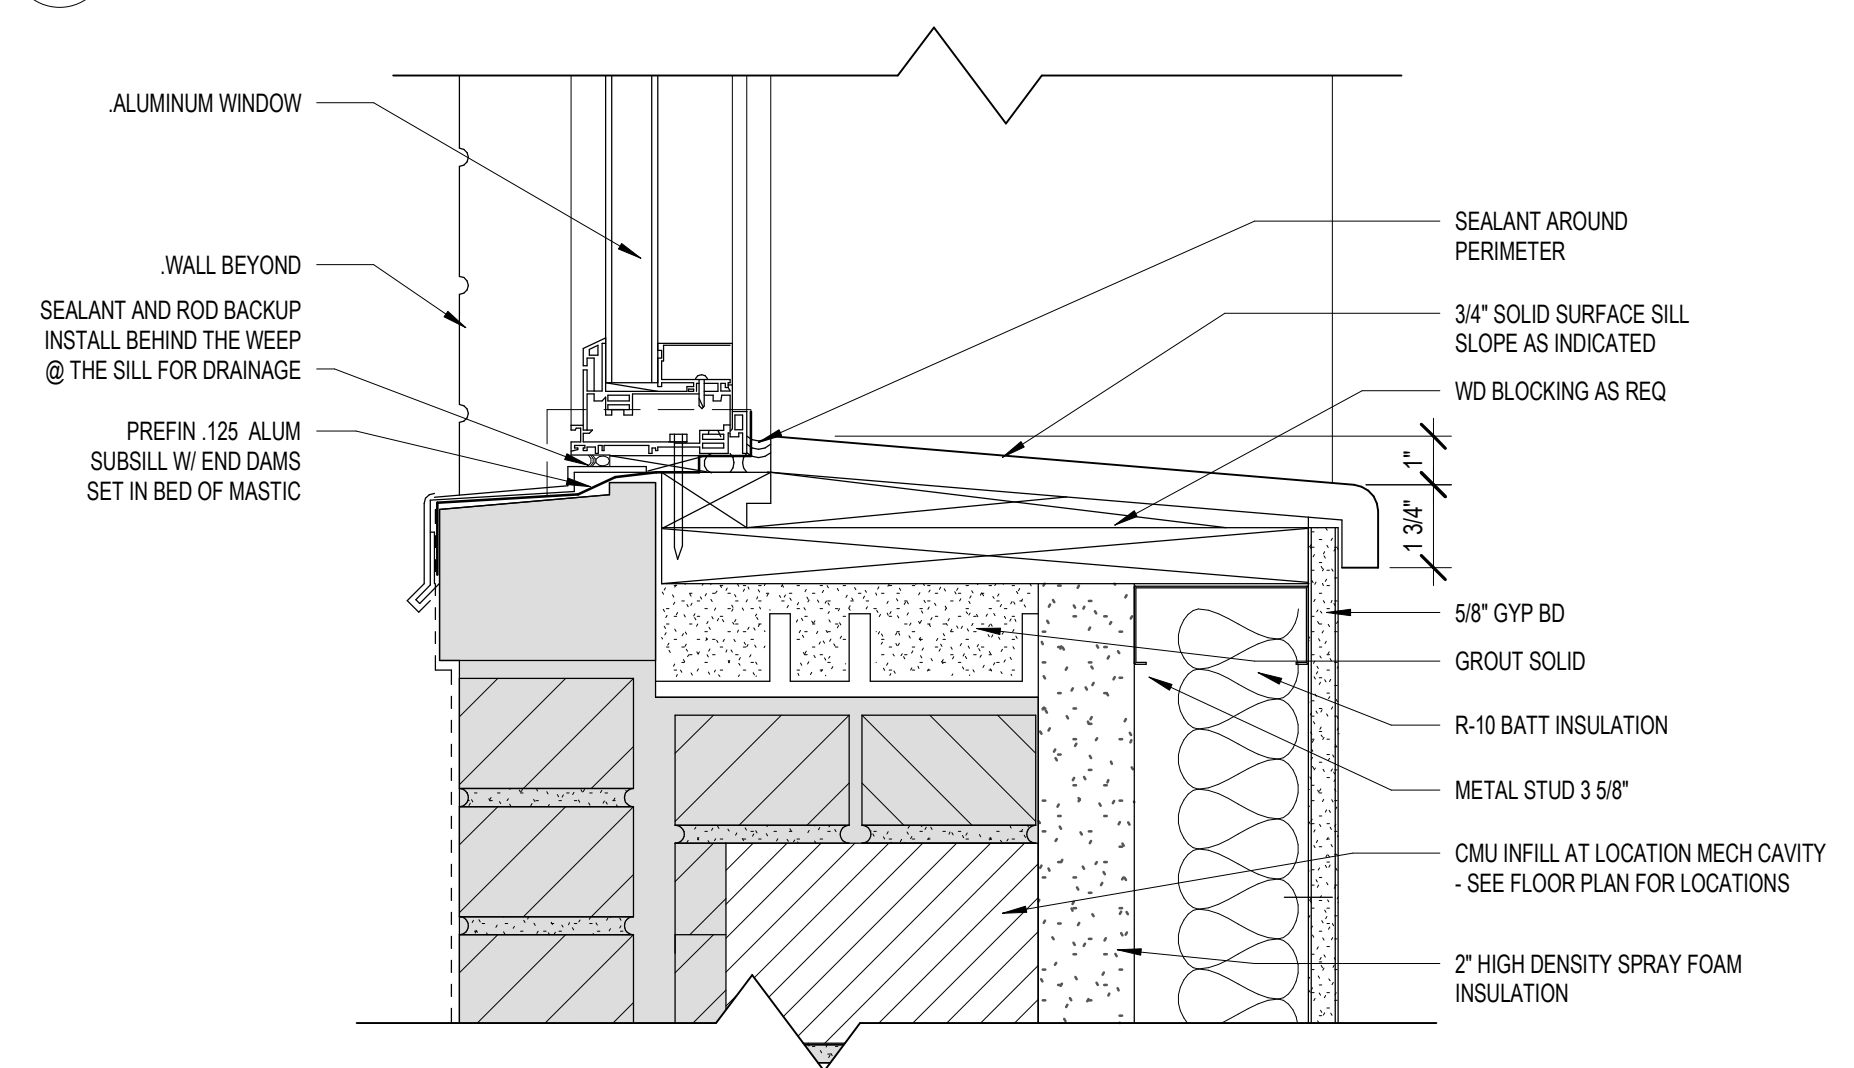

4 ALUMINUM WINDOW SILL DETAIL
AE514 3" = 1'-0"

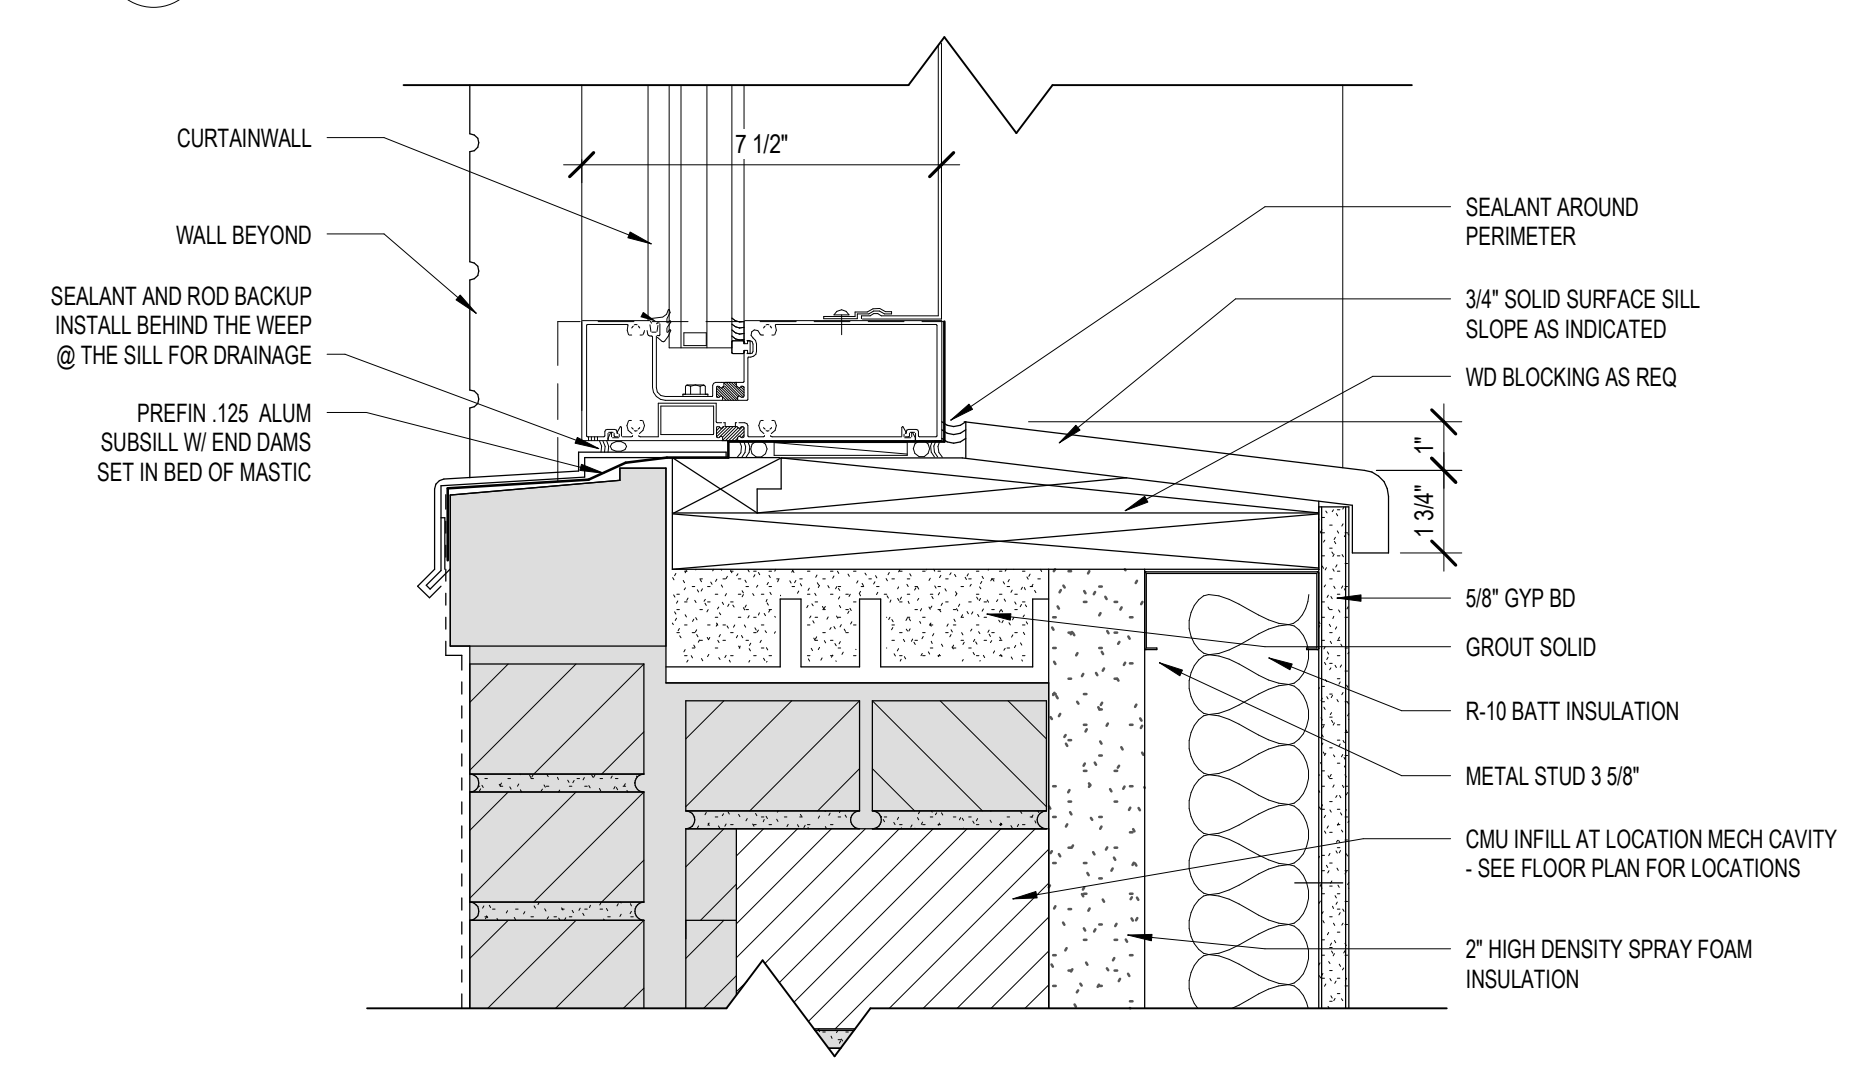

8 CURTAINWALL SILL DETAIL
AE514 3" = 1'-0"

F

C:\Users\pdp\Documents\15950 - VAHC-Bldg Building 1_R21 - Central.mxd_Yunyoung.nxd

BID DOCUMENTS

NO.	REVISIONS	DATE

CONSULTANT

ARCHITECT/ENGINEER OF RECORD

THOMAS OLESAK, ARCHITECT
MS Lic # 5505

1050 HOYT AVE WEST ST PAUL, MN 55117
952-451-0460

STAMP



Office of
Construction
and Facilities
Management



U.S. Department
of Veterans
Affairs

Drawing Title
WINDOW AND CURTAINWALL
DETAILS

Approved:

Phase

CONSTRUCTION
DOCUMENTS

FULLY SPRINKLERED

Project Title

RENOVATE BUILDING 1

Location

BILOXI, MISSISSIPPI

Issue Date

03/10/2023

Checked

LA

Drawn

CD

Project Number

520-317X

Building Number

1

Drawing Number


AE514

Dwg. 103 of 238


3/13/2023 10:32:32 AM
C:\Users\pjd\Documents\15950 - VAHC-Bldg Building 1_R21 - Central model_Yunyoung.nxd
VA FORM 08 - 6231

1 2 3 4 5 6 7 8 9 10

A
B
C
D
E
F

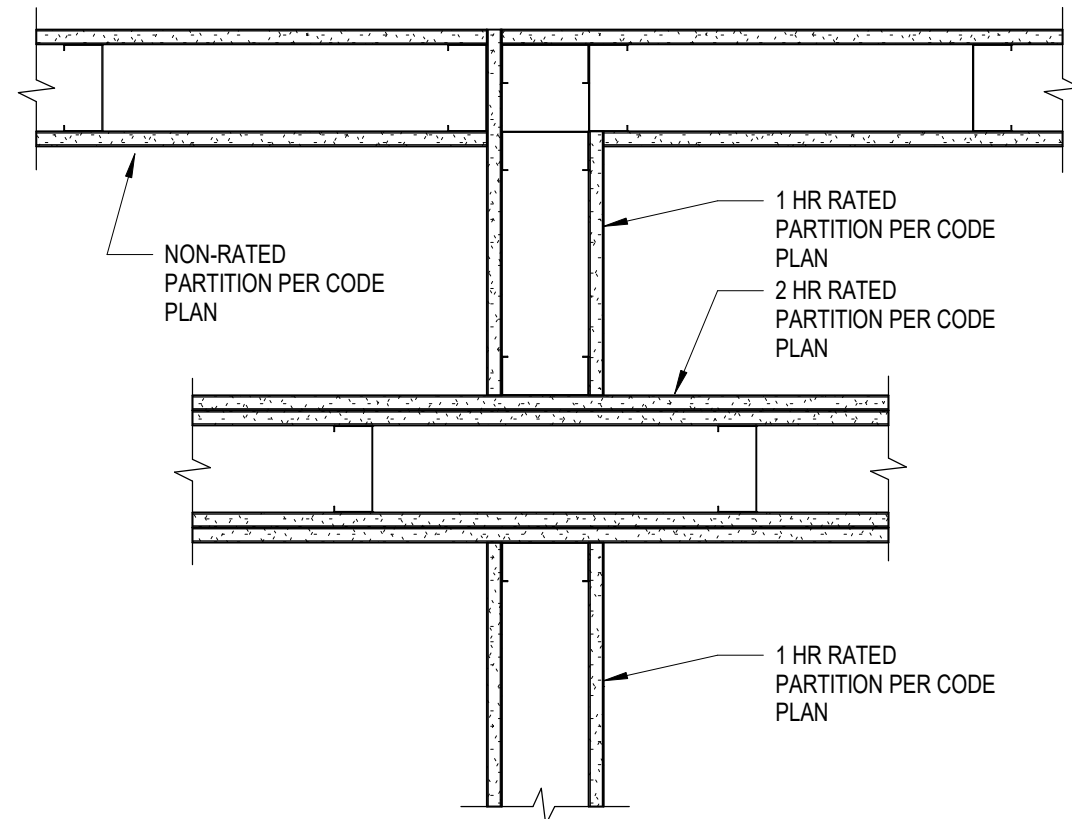


CONTROL JOINT NOTES
1. PROVIDE CONTROL JOINTS IN PARTITIONS WHERE INDICATED ON PLANS AND/OR INTERIOR ELEVATIONS, AT END INTERSECTION WITH CONCOMU WALLS, INTERSECTION WITH EXISTING PARTITIONS.
2. PROVIDE CONTROL JOINTS IN UNINTERRUPTED LONG EXPANSES OF GYP AT 30'-0" OC MAX. WITH EACH SIDE OF PARTITION CONSIDERED SEPARATELY.
3. CONTROL JOINT LOCATIONS SHALL BE FIELD VERIFIED BY ARCHITECT.

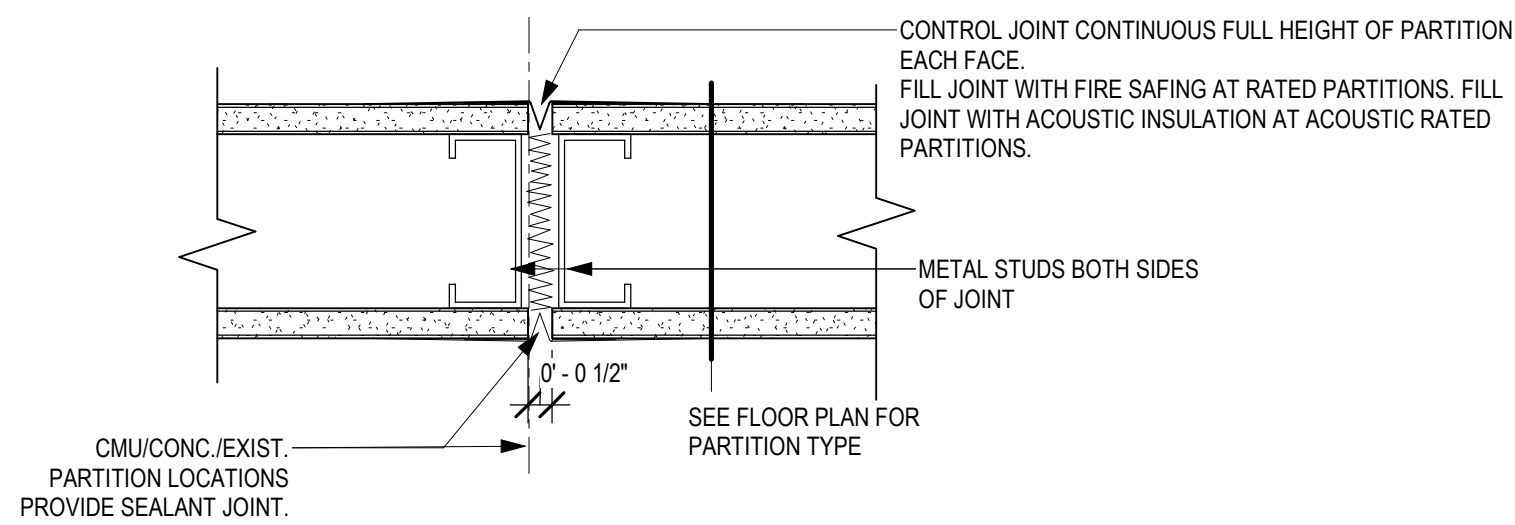

1 GUIDELINE - RATED WALL INTERSECTION
AE600/ 1 1/2" = 1'-0"

2 GYPSUM BOARD CONTROL JOINT
AE600/ 3" = 1'-0"

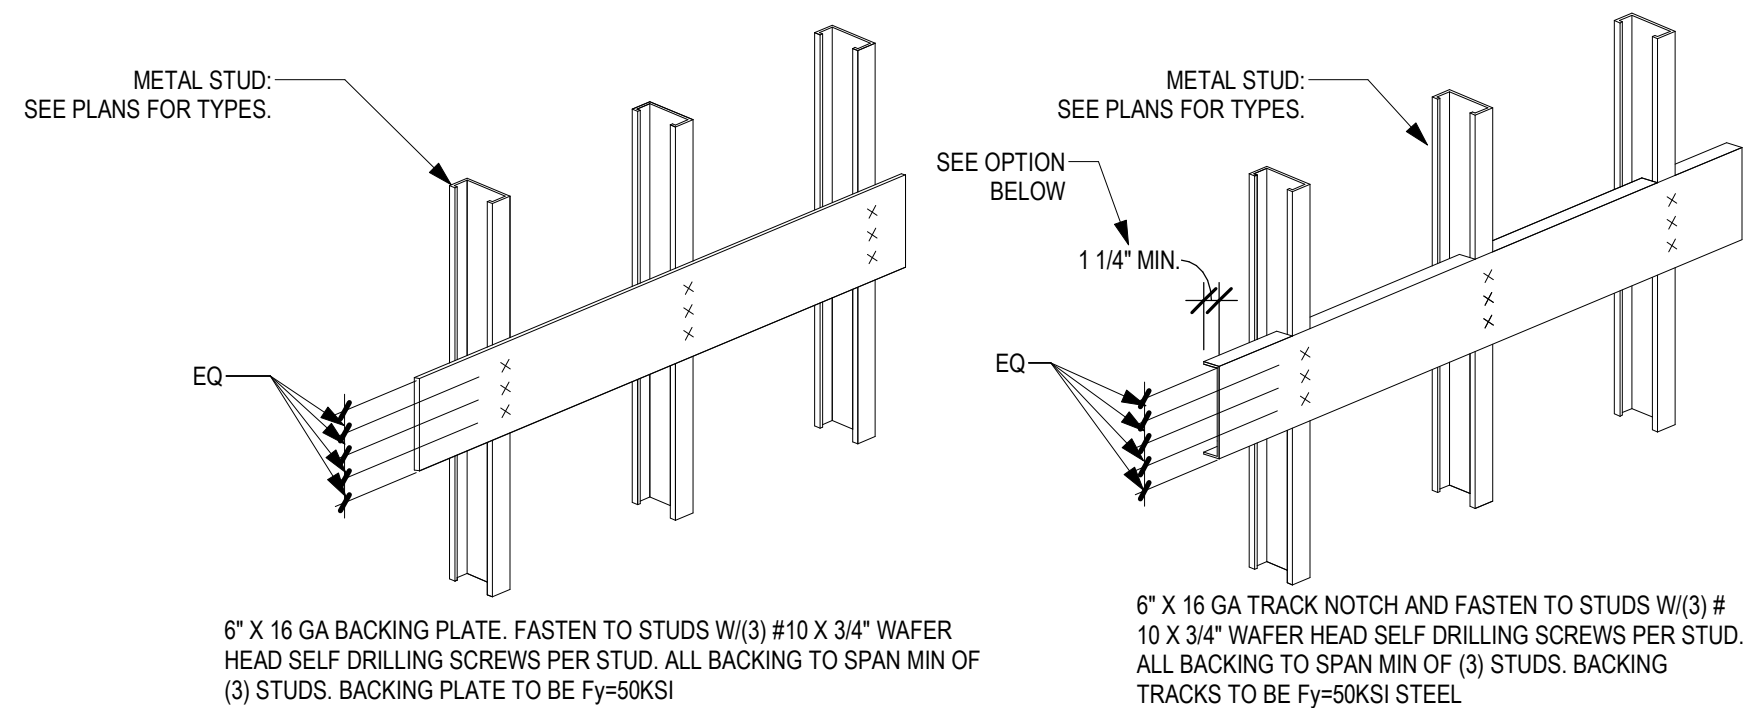


A PLATE BACKING: USE FOR FOLLOWING ITEMS

1. FLOOR MOUNTED BASE CABINETS.
2. WALL MOUNTED DISPENSERS AND HARDWARE WEIGHTING LESS THAN 20 LBS.
3. MIRRORS
4. BACKING AT THE BOTTOM OF WALL HUNG CABINETS LESS THAN 15" IN DEPTH.

B TRACK BACKING: USE FOR FOLLOWING ITEMS



1. HANDRAILS (UP TO 250#)
2. FLOOR MOUNTED CABINETS GREATER THAN 3' - 0" IN HEIGHT.
3. WALL HUNG CABINETS GREATER THAN 15" IN DEPTH AND AT THE TOP OF WALL HUNG CABINETS LESS THAN 15" IN DEPTH.

C ALTERNATE TO **B**

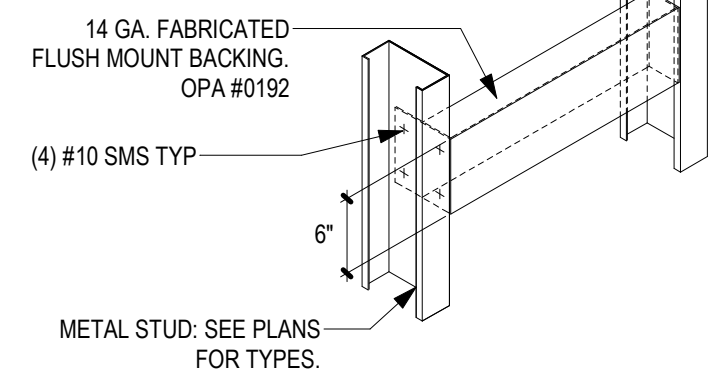

SEE BACKING PLATE TYPE B FOR ADDITIONAL NOTES.


D ALTERNATE TO **B**

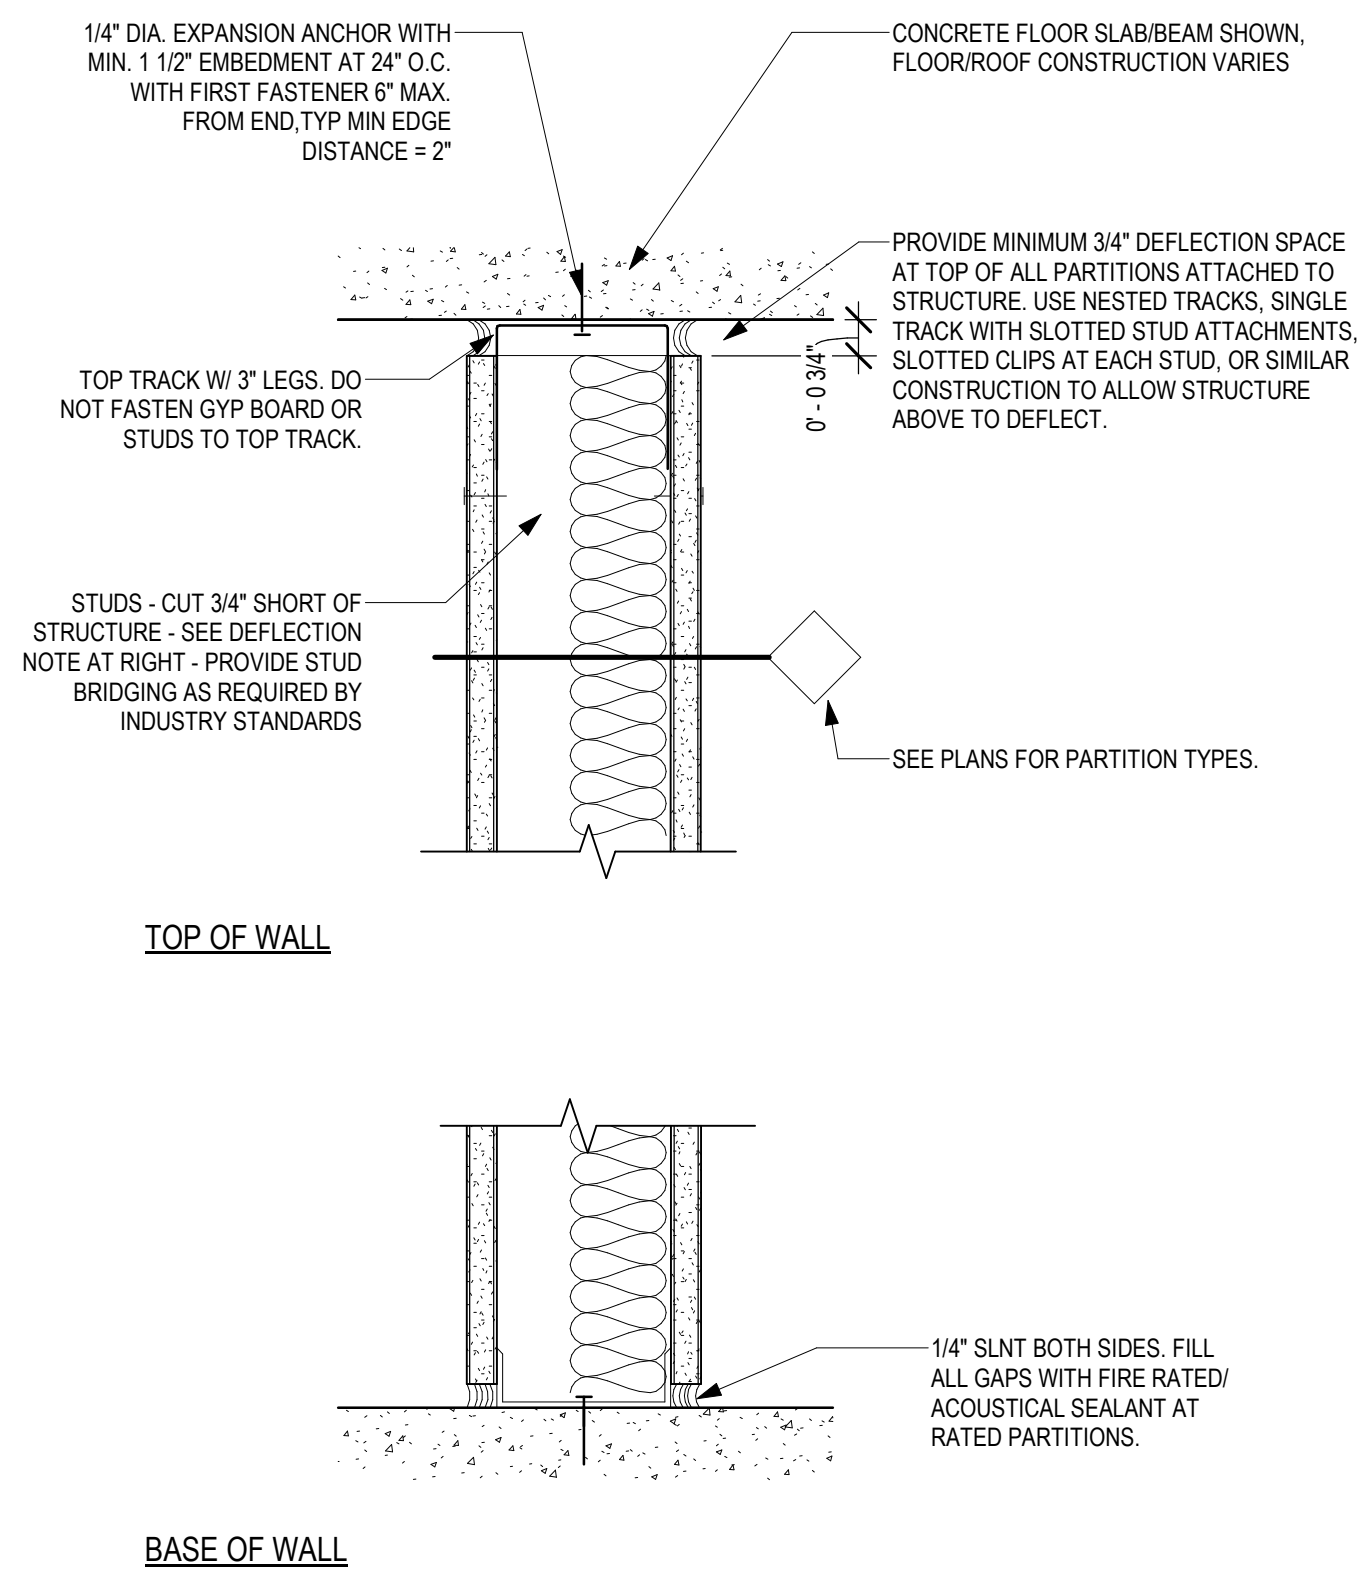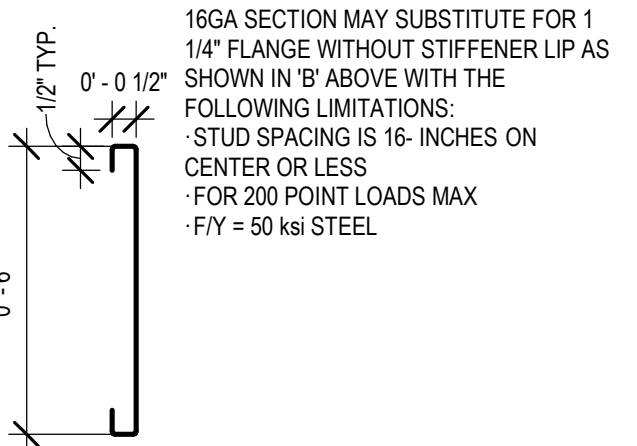


BASE OF WALL

3 PARTITION BLOCKING-BACKING TYPES
AE600/ 3" = 1'-0"

4 PARTITION DEFLECTION JOINT & FLOOR CLOSURE
AE600/ 3" = 1'-0"

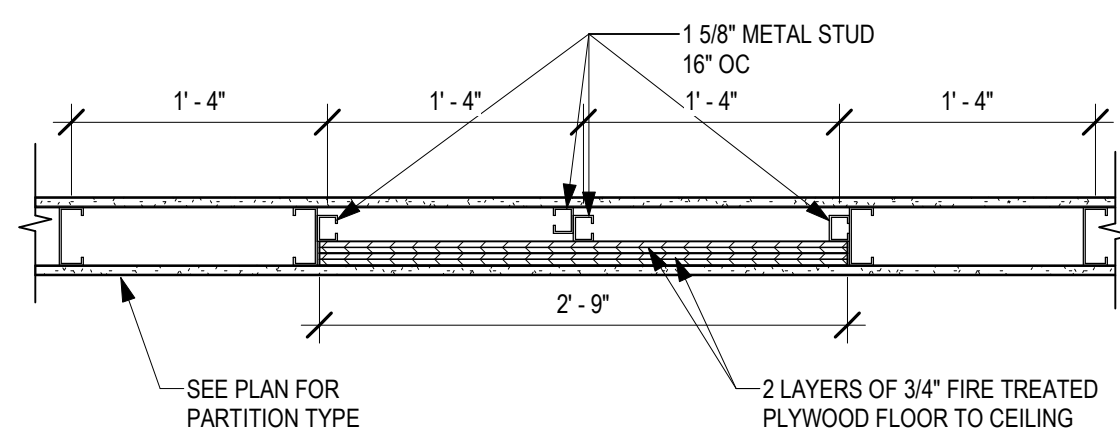

6 PARTITION DETAIL AT IN-WALL BLOCKING AT XRAY UNIT
AE600/ 1" = 1'-0"

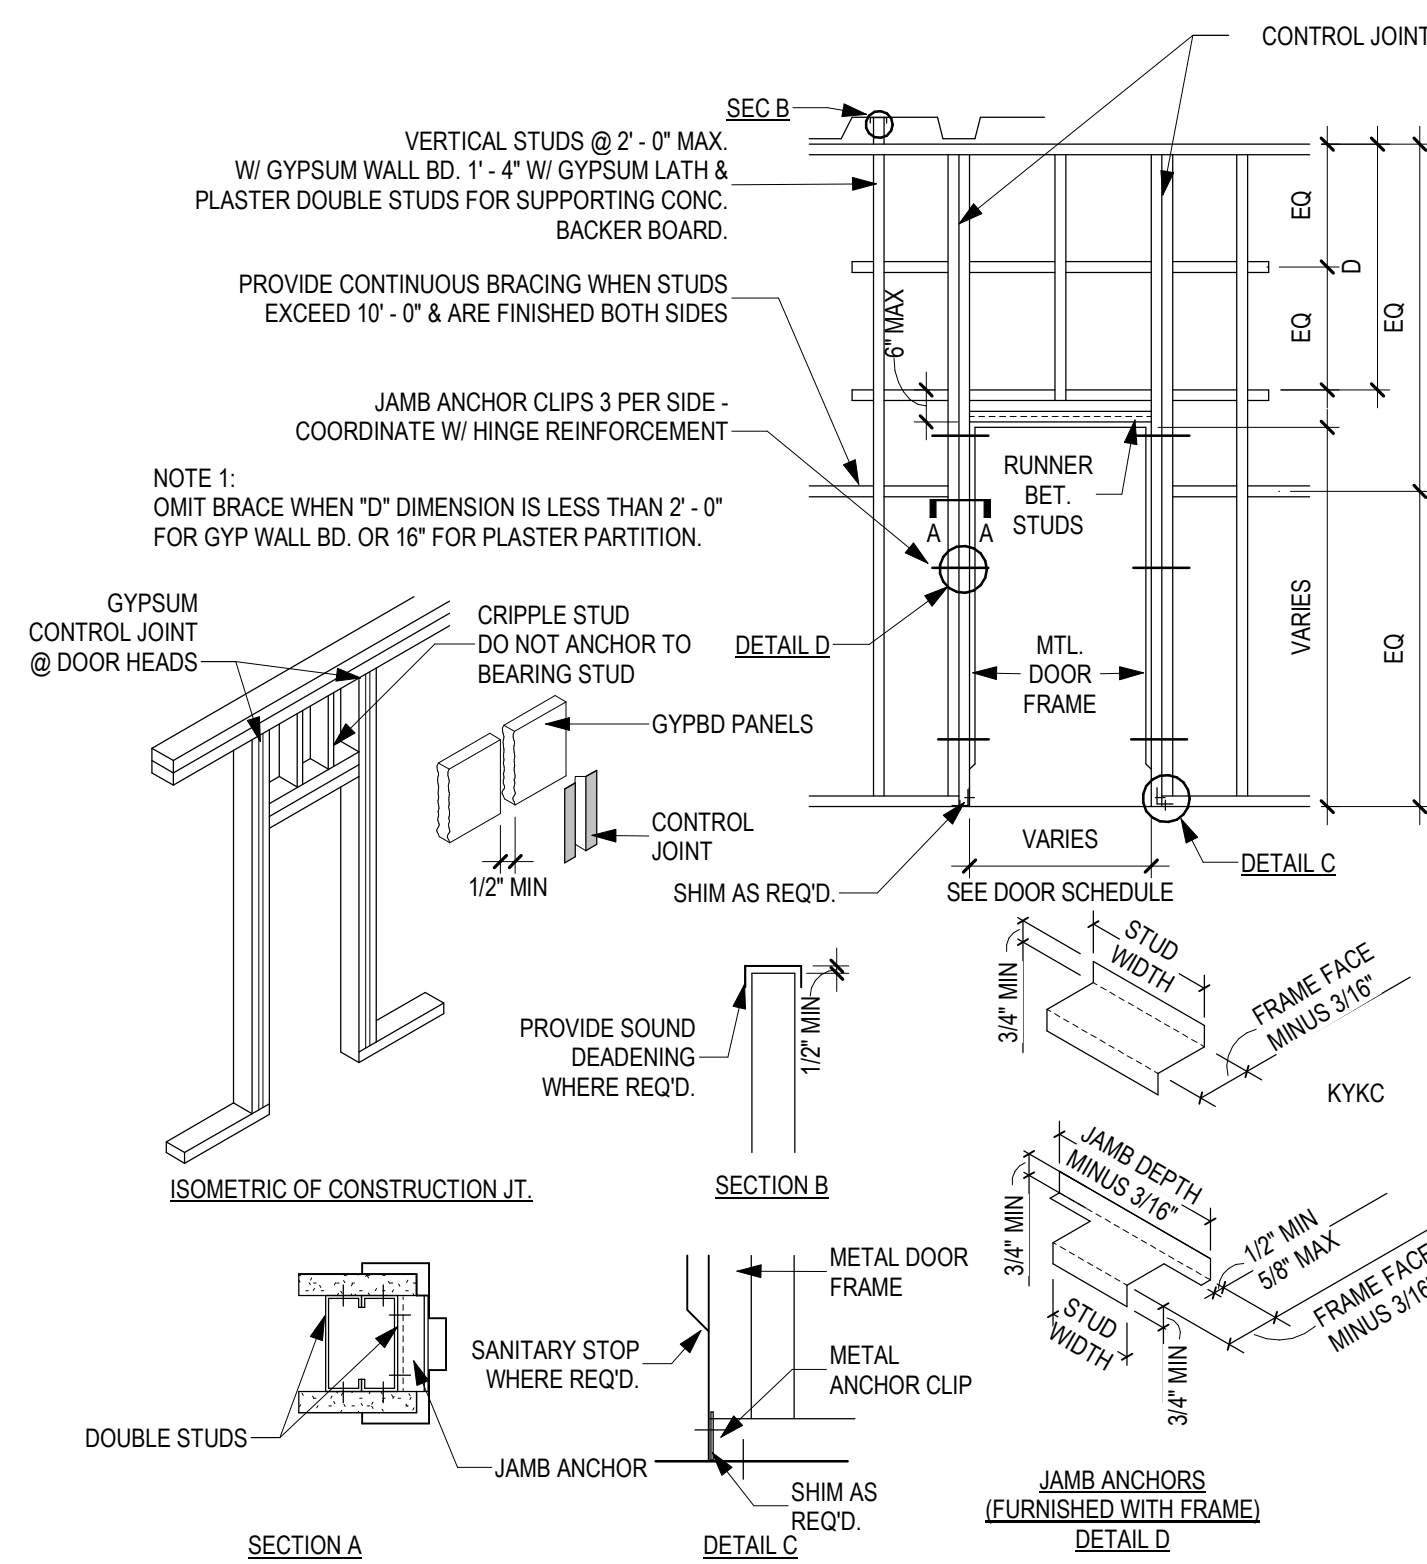

5 TYPICAL PARTITION CONTROL JOINT FRAMING AT DOORS
AE600/ 1 1/2" = 1'-0"

NO.	REVISIONS	DATE

CONSULTANT

ARCHITECT/ENGINEER OF RECORD
THOMAS OLESAC, ARCHITECT
MS Lic # 5505
1050 HOYT AVE WEST ST PAUL, MN 55117
952-451-0460

STAMP
Thomas Olesac
03.10.2023

Office of
Construction
and Facilities
Management
VA U.S. Department
of Veterans
Affairs

Drawing Title
INTERIOR PARTITION DETAILS
Approved:

Phase
**CONSTRUCTION
DOCUMENTS**
FULLY SPRINKLERED

Project Title RENOVATE BUILDING 1		Project Number 520-317X	
Location BILOXI, MISSISSIPPI		Building Number 1	
Issue Date 03/10/2023	Checked Checker	Drawn Author	Drawing Number AE600
			Dwg. 104 of 238

BID DOCUMENTS

A

B

C


D

E

F


DOOR & FRAME SCHEDULE - 3RD FLOOR																	
OPENING	SINGLE / PAIR	DOOR					FRAME					FIRE RATING	HARDWARE	REMARKS			
		WIDTH	HEIGHT	THICKNESS	MATERIAL	TYPE	GLAZING	TYPE	MATERIAL	DETAILS							
										HEAD	JAMB				SILL		
3A101	S	3'-8"	7'-0"	0'-1 3/4"	WD	3	GL-7	F-1	HM	3/AE811	4/AE811		90	5.0	B, G, P		
3A102	S	3'-0"	7'-0"	0'-1 3/4"	WD	1		F-1	HM	1/AE811	2/AE811			31.0	B, E, P		
3A103	S	3'-0"	7'-0"	0'-1 3/4"	WD	1		F-1	HM	1/AE811	2/AE811			31.0	B, E, P		
3A104	S	3'-0"	7'-0"	0'-1 3/4"	WD	1		F-1	HM	1/AE811	2/AE811			31.0	B, E, P		
3A106	S	3'-0"	7'-0"	0'-1 3/4"	WD	3	GL-1	F-1	HM	1/AE811	2/AE811			33.0	P		
3A110	S	3'-8"	7'-0"	0'-1 3/4"	WD	1		F-1	HM	1/AE811	2/AE811		45	10.0	B, P		
3A111	S	3'-0"	7'-0"	0'-1 3/4"	WD	1		F-1	HM	1/AE811	2/AE811		45	11.0	B, P		
3A112	S	3'-0"	7'-0"	0'-1 3/4"	WD	1		F-1	HM	1/AE811	2/AE811		27.0	A, P			
3A114	S	3'-0"	7'-0"	0'-1 3/4"	WD	1		F-1	HM	1/AE811	2/AE811		15.0	B, F, P			
3A115	S	3'-0"	7'-0"	0'-1 3/4"	WD	2	GL-1	F-1	HM	1/AE811	2/AE811		34.0	B, P			
3A117	S	4'-0"	7'-0"	0'-1 3/4"	WD	1		F-1	HM	1/AE811	2/AE811		37.0				
3A117A	S	4'-0"	8'-5"	0'-1 3/4"	WD	1		F-2	HM	1/AE811	2/AE811		38.0	C, H			
3A118	S	4'-0"	7'-0"	0'-1 3/4"	WD	1		F-1	HM	1/AE811	2/AE811		37.0				
3A118A	S	4'-0"	8'-5"	0'-1 3/4"	WD	1		F-2	HM	1/AE811	2/AE811		38.0	C, H			
3A120	S	3'-0"	7'-0"	0'-1 3/4"	WD	1	GL-11	F-6	HM	1/AE811	2/AE811		27.0	A			
3A121	S	3'-8"	7'-0"	0'-1 3/4"	WD	3	GL-7	F-1	HM	1/AE811	2/AE811		45	9.0	B, P		
3A122	S	4'-0"	7'-0"	0'-1 3/4"	WD	1		F-1	HM	1/AE811	2/AE811		37.0	P			
3A122A	S	4'-0"	8'-5"	0'-1 3/4"	WD	1		F-2	HM	1/AE811	2/AE811		38.0	C, H			
3A123	S	4'-0"	7'-0"	0'-1 3/4"	WD	1		F-1	HM	1/AE811	2/AE811		37.0	P			
3A123A	S	4'-0"	8'-5"	0'-1 3/4"	WD	1		F-2	HM	1/AE811	2/AE811		38.0	C, H			
3A125	P	6'-0"	7'-0"	0'-1 3/4"	WD	8		F-4	HM	1/AE811	2/AE811		24.0	B			
3A125A	S	4'-0"	8'-5"	0'-1 3/4"	WD	1		F-2	HM	1/AE811	2/AE811		38.0	C, H			
3A127	S	3'-0"	7'-0"	0'-1 3/4"	WD	1		F-1	HM	1/AE811	2/AE811		9.0	B			
3A128	S	3'-0"	7'-0"	0'-1 3/4"	WD	3	GL-1	F-1	HM	1/AE811	2/AE811		33.0				
3A130	S	3'-0"	7'-0"	0'-1 3/4"	WD	3	GL-1	F-1	HM	1/AE811	2/AE811		25.0	P			
3A131	P	6'-0"	7'-0"	0'-1 3/4"	WD	8		F-4	HM	1/AE811	2/AE811		24.0	B			
3A131A	S	4'-0"	8'-5"	0'-1 3/4"	WD	1		F-2	HM	1/AE811	2/AE811		38.0	C, H			
3A131B	S	3'-0"	7'-0"	0'-1 3/4"	WD	2	GL-1	F-1	HM	1/AE811	2/AE811		37.0				
3A131C	S	3'-0"	7'-0"	0'-1 3/4"	WD	2	GL-1	F-1	HM	1/AE811	2/AE811		36.0	P			
3A133	S	3'-8"	7'-0"	0'-1 3/4"	WD	3	GL-7	F-1	HM	3/AE811	4/AE811		90	5.0	B, G, P		
3A134	S	3'-0"	7'-0"	0'-1 3/4"	WD	1	GL-11	F-6	HM	1/AE811	2/AE811		35.0				
3A134A	S	3'-0"	7'-0"	0'-1 3/4"	WD	1		F-1	HM	1/AE811	2/AE811		30.0	B, A, P			
3A135	S	3'-0"	7'-0"	0'-1 3/4"	WD	1		F-1	HM	1/AE811	2/AE811		30.0	B, A, P			
3A136	S	3'-0"	7'-0"	0'-1 3/4"	WD	1		F-1	HM	1/AE811	2/AE811		21.0	B, P			
3A138	S	3'-0"	7'-0"	0'-1 3/4"	WD	3	GL-1	F-1	HM	1/AE811	2/AE811		22.1	B, P			
3A139	S	3'-0"	7'-0"	0'-1 3/4"	WD	1		F-1	HM	1/AE811	2/AE811		21.0	B, P			
3A140	S	3'-0"	7'-0"	0'-1 3/4"	WD	1		F-1	HM	1/AE811	2/AE811		45	3.0	F, P		
3A141A	S	3'-0"	7'-0"	0'-1 3/4"	WD	3	GL-1	F-1	HM	1/AE811	2/AE811		18.0	B, P			
3A141B	S	3'-0"	7'-0"	0'-1 3/4"	WD	3	GL-1	F-1	HM	1/AE811	2/AE811		19.0	B, P			
3A142	S	3'-8"	7'-0"	0'-1 3/4"	WD	1		F-1	HM	1/AE811	2/AE811		45	10.0	B, P		
3B101	S	3'-0"	7'-0"	0'-1 3/4"	WD	1		F-1	HM	1/AE811	2/AE811		4.0	B, G, P			
3B103	S	3'-0"	7'-0"	0'-1 3/4"	WD	1	GL-11	F-6	HM	1/AE811	2/AE811		35.0				
3B104	S	3'-8"	7'-0"	0'-1 3/4"	WD	1		F-1	HM	1/AE811	2/AE811		45	7.0	B, P		
3B105	P	5'-0"	7'-0"	0'-1 3/4"	WD	4		F-4	HM	1/AE811	2/AE811		23.0	P			
3B106	S	3'-8"	7'-0"	0'-1 3/4"	WD	1		F-1	HM	1/AE811	2/AE811		9.0	B, P			
3B107	S	3'-8"	7'-0"	0'-1 3/4"	WD	1		F-1	HM	1/AE811	2/AE811		45	8.0	B, P		
3B108	S	3'-8"	7'-0"	0'-1 3/4"	WD	1		F-1	HM	1/AE811	2/AE811		45	10.0	B, P		
3B109	S	3'-0"	7'-0"	0'-1 3/4"	WD	1	GL-11	F-6	HM	1/AE811	2/AE811		35.0				
3B110	S	3'-8"	7'-0"	0'-1 3/4"	WD	3	GL-1	F-1	HM	3/AE811	4/AE811		90	5.0	B, G, P		
3B111	S	4'-0"	7'-0"	0'-1 3/4"	WD	1		F-1	HM	1/AE811	2/AE811		37.0	P			
3B111A	S	4'-0"	8'-5"	0'-1 3/4"	WD	1		F-2	HM	1/AE811	2/AE811		38.0	C, H			
3B111B	S	3'-0"	7'-0"	0'-1 3/4"	WD	2	GL-1	F-1	HM	1/AE811	2/AE811		37.0	P			
3B111C	S	3'-0"	7'-0"	0'-1 3/4"	WD	2	GL-1	F-1	HM	1/AE811	2/AE811		36.0	P			
3B113	S	3'-8"	7'-0"	0'-1 3/4"	WD	3	GL-1	F-1	HM	1/AE811	2/AE811		45	27.0	A, P		
3B114	S	4'-0"	7'-0"	0'-1 3/4"	WD	1		F-1	HM	1/AE811	2/AE811		37.0				
3B114A	S	4'-0"	8'-5"	0'-1 3/4"	WD	1		F-2	HM	1/AE811	2/AE811		38.0	C, H			
3B116	S	4'-0"	7'-0"	0'-1 3/4"	WD	1		F-1	HM	1/AE811	2/AE811		37.0				
3B116A	S	4'-0"	8'-5"	0'-1 3/4"	WD	1		F-2	HM	1/AE811	2/AE811		38.0	C, H			
3B118	S	4'-0"	7'-0"	0'-1 3/4"	WD	1		F-1	HM	1/AE811	2/AE811		37.0				
3B118A	S	4'-0"	8'-5"	0'-1 3/4"	WD	1		F-2	HM	1/AE811	2/AE811		38.0	C, H			
3B119	S	4'-0"	7'-0"	0'-1 3/4"	WD	1		F-1	HM	1/AE811	2/AE811		37.0				
3B119A	S	4'-0"	8'-5"	0'-1 3/4"	WD	1		F-2	HM	1/AE811	2/AE811		38.0	C, H			
3B121	S	3'-0"	7'-0"	0'-1 3/4"	WD	3	GL-7	F-1	HM	1/AE811	2/AE811		45	9.0	B, P		
3B122	S	3'-0"	7'-0"	0'-1 3/4"	WD	1	GL-11	F-6	HM	1/AE811	2/AE811		27.0	A			
3B123	S	4'-0"	7'-0"	0'-1 3/4"	WD	1		F-1	HM	1/AE811	2/AE811		37.0				
3B123A	S	4'-0"	8'-5"	0'-1 3/4"	WD	1		F-2	HM	1/AE811	2/AE811		38.0	C, H			
3B124	S	4'-0"	7'-0"	0'-1 3/4"	WD	1		F-1	HM	1/AE811	2/AE811		37.0				
3B124A	S	4'-0"	8'-5"	0'-1 3/4"	WD	1		F-2	HM	1/AE811	2/AE811		38.0	C, H			
C3-106	P	7'-6"	7'-0"	0'-1 3/4"	EXISTING	5	GL-7	F-5	HM	5/AE811	6/AE811		20	2.0	B, D, P		
C3-109	P	7'-6"	7'-0"	0'-1 3/4"	EXISTING	EXISTING	EXISTING	EXISTING	EXISTING	--	--	--	20	2.0	M, O		

DOOR & FRAME SCHEDULE - 4TH FLOOR																
OPENING	SINGLE / PAIR	DOOR						FRAME						FIRE RATING	HARDWARE	REMARKS
		WIDTH	HEIGHT	THICKNESS	MATERIAL	TYPE	GLAZING	TYPE	MATERIAL	DETAILS						
										HEAD	JAMB	SILL				
4A101	S	3'-8"	7'-0"	0'-1 3/4"	WD	3	GL-7	F-1	HM	3/AE511	2/AE511		90	5.0	B, G, P	
4A102	S	3'-0"	7'-0"	0'-1 3/4"	WD	1	F-1	F-1	HM	1/AE511	2/AE511			31.0	B, E, P	
4A103	S	3'-0"	7'-0"	0'-1 3/4"	WD	1		F-1	HM	1/AE511	2/AE511			31.0	B, E, P	
4A104	S	3'-0"	7'-0"	0'-1 3/4"	WD	1		F-1	HM	1/AE511	2/AE511			31.0	B, E, P	
4A106	S	3'-0"	7'-0"	0'-1 3/4"	WD	3	GL-1	F-1	HM	1/AE511	2/AE511			33.0	P	
4A110	S	3'-8"	7'-0"	0'-1 3/4"	WD	1		F-1	HM	1/AE511	2/AE511		45	10.0	B, P	
4A111	S	3'-0"	7'-0"	0'-1 3/4"	WD	1		F-1	HM	3/AE511	1/AE511		45	11.0	B, P	
4A112	S	3'-0"	7'-0"	0'-1 3/4"	WD	1		F-1	HM	1/AE511	2/AE511			27.0	A, P	
4A114	S	3'-0"	7'-0"	0'-1 3/4"	WD	1		F-1	HM	1/AE511	2/AE511			15.0	B, E, P	
4A115	S	3'-0"	7'-0"	0'-1 3/4"	WD	2	GL-1	F-1	HM	1/AE511	2/AE511			34.0	B, P	
4A117	S	4'-0"	7'-0"	0'-1 3/4"	WD	1		F-1	HM	1/AE511	2/AE511			37.0		
4A117A	S	4'-0"	8'-5"	0'-1 3/4"	WD	1		F-2	HM	1/AE511	2/AE511			38.0	C, H	
4A118	S	4'-0"	7'-0"	0'-1 3/4"	WD	1		F-1	HM	1/AE511	2/AE511					
4A118A	S	4'-0"	8'-5"	0'-1 3/4"	WD	1		F-2	HM	1/AE511	2/AE511			38.0	C, H	
4A120	S	3'-0"	7'-0"	0'-1 3/4"	WD	1	GL-11	F-6	HM	1/AE511	2/AE511			27.0	A	
4A121	S	3'-8"	7'-0"	0'-1 3/4"	WD	3	GL-7	F-1	HM	1/AE511	2/AE511		45	9.0	B, P	
4A122	S	4'-0"	7'-0"	0'-1 3/4"	WD	1		F-1	HM	1/AE511	2/AE511			37.0		
4A122A	S	4'-0"	8'-5"	0'-1 3/4"	WD	1		F-2	HM	1/AE511	2/AE511			38.0	C, H	
4A123	S	4'-0"	7'-0"	0'-1 3/4"	WD	1		F-1	HM	1/AE511	2/AE511			37.0		
4A123A	S	4'-0"	8'-5"	0'-1 3/4"	WD	1		F-2	HM	1/AE511	2/AE511			38.0	C, H	
4A125	P	6'-0"	7'-0"	0'-1 3/4"	WD	8		F-4	HM	1/AE511	2/AE511			24.0	B	
4A125A	S	4'-0"	8'-5"	0'-1 3/4"	WD	1		F-2	HM	1/AE511	2/AE511			38.0	C, H	
4A127	S	3'-8"	7'-0"	0'-1 3/4"	WD	1		F-1	HM	1/AE511	2/AE511			9.0	B	
4A128	S	3'-0"	7'-0"	0'-1 3/4"	WD	3	GL-1	F-1	HM	1/AE511	2/AE511			33.0		
4A130	S	6'-0"	7'-0"	0'-1 3/4"	WD	3	GL-1	F-1	HM	1/AE511	2/AE511		45	35.0	P	
4A131	P	6'-0"	7'-0"	0'-1 3/4"	WD	8		F-4	HM	1/AE511	2/AE511			24.0	B	
4A131A	S	4'-0"	8'-5"	0'-1 3/4"	WD	1		F-2	HM	1/AE511	2/AE511			38.0	C, H	
4A131B	S	3'-0"	7'-0"	0'-1 3/4"	WD	2	GL-1	F-1	HM	1/AE511	2/AE511			36.0		
4A131C	S	3'-0"	7'-0"	0'-1 3/4"	WD	2	GL-1	F-1	HM	1/AE511	2/AE511			37.0	P	
4A133	S	3'-0"	7'-0"	0'-1 3/4"	WD	3	GL-7	F-1	HM	3/AE511	1/AE511		90	5.0	B, G, P	
4A134	S	3'-0"	7'-0"	0'-1 3/4"	WD	1	GL-11	F-6	HM	1/AE511	2/AE511			35.0		
4A134A	S	3'-0"	7'-0"	0'-1 3/4"	WD	1		F-1	HM	1/AE511	2/AE511			30.0	R, A, P	
4A135	S	3'-0"	7'-0"	0'-1 3/4"	WD	1		F-1	HM	1/AE511	2/AE511			30.0	B, A, P	
4A136	S	3'-0"	7'-0"	0'-1 3/4"	WD	1		F-1	HM	1/AE511	2/AE511			30.0	B, A, P	
4A137	S	3'-0"	7'-0"	0'-1 3/4"	WD	1		F-1	HM	1/AE511	2/AE511			21.0	B, P	
4A138	S	3'-0"	7'-0"	0'-1 3/4"	WD	3	GL-1	F-1	HM	1/AE511	2/AE511			22.1	B, P	
4A139	S	3'-0"	7'-0"	0'-1 3/4"	WD	1		F-1	HM	1/AE511	2/AE511			21.0	B, P	
4A140	S	3'-0"	7'-0"	0'-1 3/4"	WD	1		F-1	HM	1/AE511	2/AE511		45	3.0	F, P	
4A141A	S	3'-0"	7'-0"	0'-1 3/4"	WD	3	GL-1	F-1	HM	1/AE511	2/AE511			18.0	B, P	
4A141B	S	3'-0"	7'-0"	0'-1 3/4"	WD	3	GL-1	F-1	HM	1/AE511	2/AE511			19.0	B, P	
4A142	S	3'-8"	7'-0"	0'-1 3/4"	WD	1		F-1	HM	1/AE511	2/AE511		45	10.0	B, P	
4B100A	P	5'-0"	7'-0"	0'-1 3/4"	WD	4		F-4	HM	1/AE511	2/AE511				B	
4B101	S	3'-0"	7'-0"	0'-1 3/4"	WD	1		F-1	HM	1/AE511	2/AE511			4.0	B, G, P	
4B103	S	3'-0"	7'-0"	0'-1 3/4"	WD	1	GL-11	F-6	HM	1/AE511	2/AE511			35.0		
4B104	S	3'-0"	7'-0"	0'-1 3/4"	WD	1		F-1	HM	1/AE511	2/AE511		45	7.0	B, P	
4B105	P	5'-0"	7'-0"	0'-1 3/4"	WD	4		F-4	HM	1/AE511	2/AE511		45	23.0	P	
4B106	S	3'-8"	7'-0"	0'-1 3/4"	WD	1		F-1	HM	1/AE511	2/AE511			9.0	B, P	
4B107	S	3'-8"	7'-0"	0'-1 3/4"	WD	1		F-1	HM	1/AE511	2/AE511		45	8.0	B, P	
4B108	S	3'-8"	7'-0"	0'-1 3/4"	WD	1		F-1	HM	1/AE511	2/AE511		45	10.0	B, P	
4B109	S	3'-0"	7'-0"	0'-1 3/4"	WD	1	GL-11	F-6	HM	1/AE511	2/AE511			35.0		
4B110	S	3'-8"	7'-0"	0'-1 3/4"	WD	3	GL-7	F-1	HM	3/AE511	1/AE511		90	5.0	B, G, P	
4B111	S	4'-0"	7'-0"	0'-1 3/4"	WD	1		F-1	HM	1/AE511	2/AE511			37.0	P	
4B111A	S	4'-0"	8'-5"	0'-1 3/4"	WD	1		F-2	HM	1/AE511	2/AE511			38.0	C, H	
4B111B	S	3'-0"	7'-0"	0'-1 3/4"	WD	2	GL-1	F-1	HM	1/AE512	2/AE512			37.0		
4B111C	S	3'-0"	7'-0"	0'-1 3/4"	WD	2	GL-1	F-1	HM	1/AE511	2/AE511			36.0	P	
4B113	S	3'-8"	7'-0"	0'-1 3/4"	WD	3	GL-1	F-1	HM	1/AE511	2/AE511			27.0	A, P	
4B114	S	4'-0"	7'-0"	0'-1 3/4"	WD	1		F-1	HM	1/AE511	2/AE511			37.0		
4B114A	S	4'-0"	8'-5"	0'-1 3/4"	WD	1		F-2	HM	1/AE511	2/AE511			38.0	C, H	
4B116	S	4'-0"	7'-0"	0'-1 3/4"	WD	1		F-1	HM	1/AE511	2/AE511			37.0		
4B116A	S	4'-0"	8'-5"	0'-1 3/4"	WD	1		F-2	HM	1/AE511	2/AE511			38.0	C, H	
4B118	S	4'-0"	7'-0"	0'-1 3/4"	WD	1		F-1	HM	1/AE511	2/AE511			37.0		
4B118A	S	4'-0"	8'-5"	0'-1 3/4"	WD	1		F-2	HM	1/AE511	2/AE511			38.0	C, H	
4B119	S	4'-0"	7'-0"	0'-1 3/4"	WD	1		F-1	HM	1/AE511	2/AE511			37.0		
4B119A	S	4'-0"	8'-5"	0'-1 3/4"	WD	1		F-2	HM	1/AE511	2/AE511			38.0	C, H	
4B121	S	3'-8"	7'-0"	0'-1 3/4"	WD	3	GL-7	F-1	HM	1/AE511	2/AE511		45	9.0	B, P	
4B122	S	3'-0"	7'-0"	0'-1 3/4"	WD	1	GL-11	F-6	HM	1/AE511	2/AE511			27.0	A	
4B123	S	4'-0"	7'-0"	0'-1 3/4"	WD	1		F-1	HM	1/AE511	2/AE511			37.0		
4B123A	S	4'-0"	8'-5"	0'-1 3/4"	WD	1		F-2	HM	1/AE511	2/AE511			38.0	C, H	
4B124	S	4'-0"	7'-0"	0'-1 3/4"	WD	1		F-1	HM	1/AE511	2/AE511			37.0		
4B124A	S	4'-0"	8'-5"	0'-1 3/4"	WD	1		F-2	HM	1/AE511	2/AE511			38.0	C, H	
CA-106	P	2'-0"	7'-0"	0'-1 3/4"	WD	5	GL-7	F-2	HM	5/AE511	6/AE511		20	2.0	R, D, P	
CA-109	P	7'-8"	7'-0"	0'-1 3/4"	EXISTING	EXISTING	EXISTING	EXISTING						2.0	M, O	

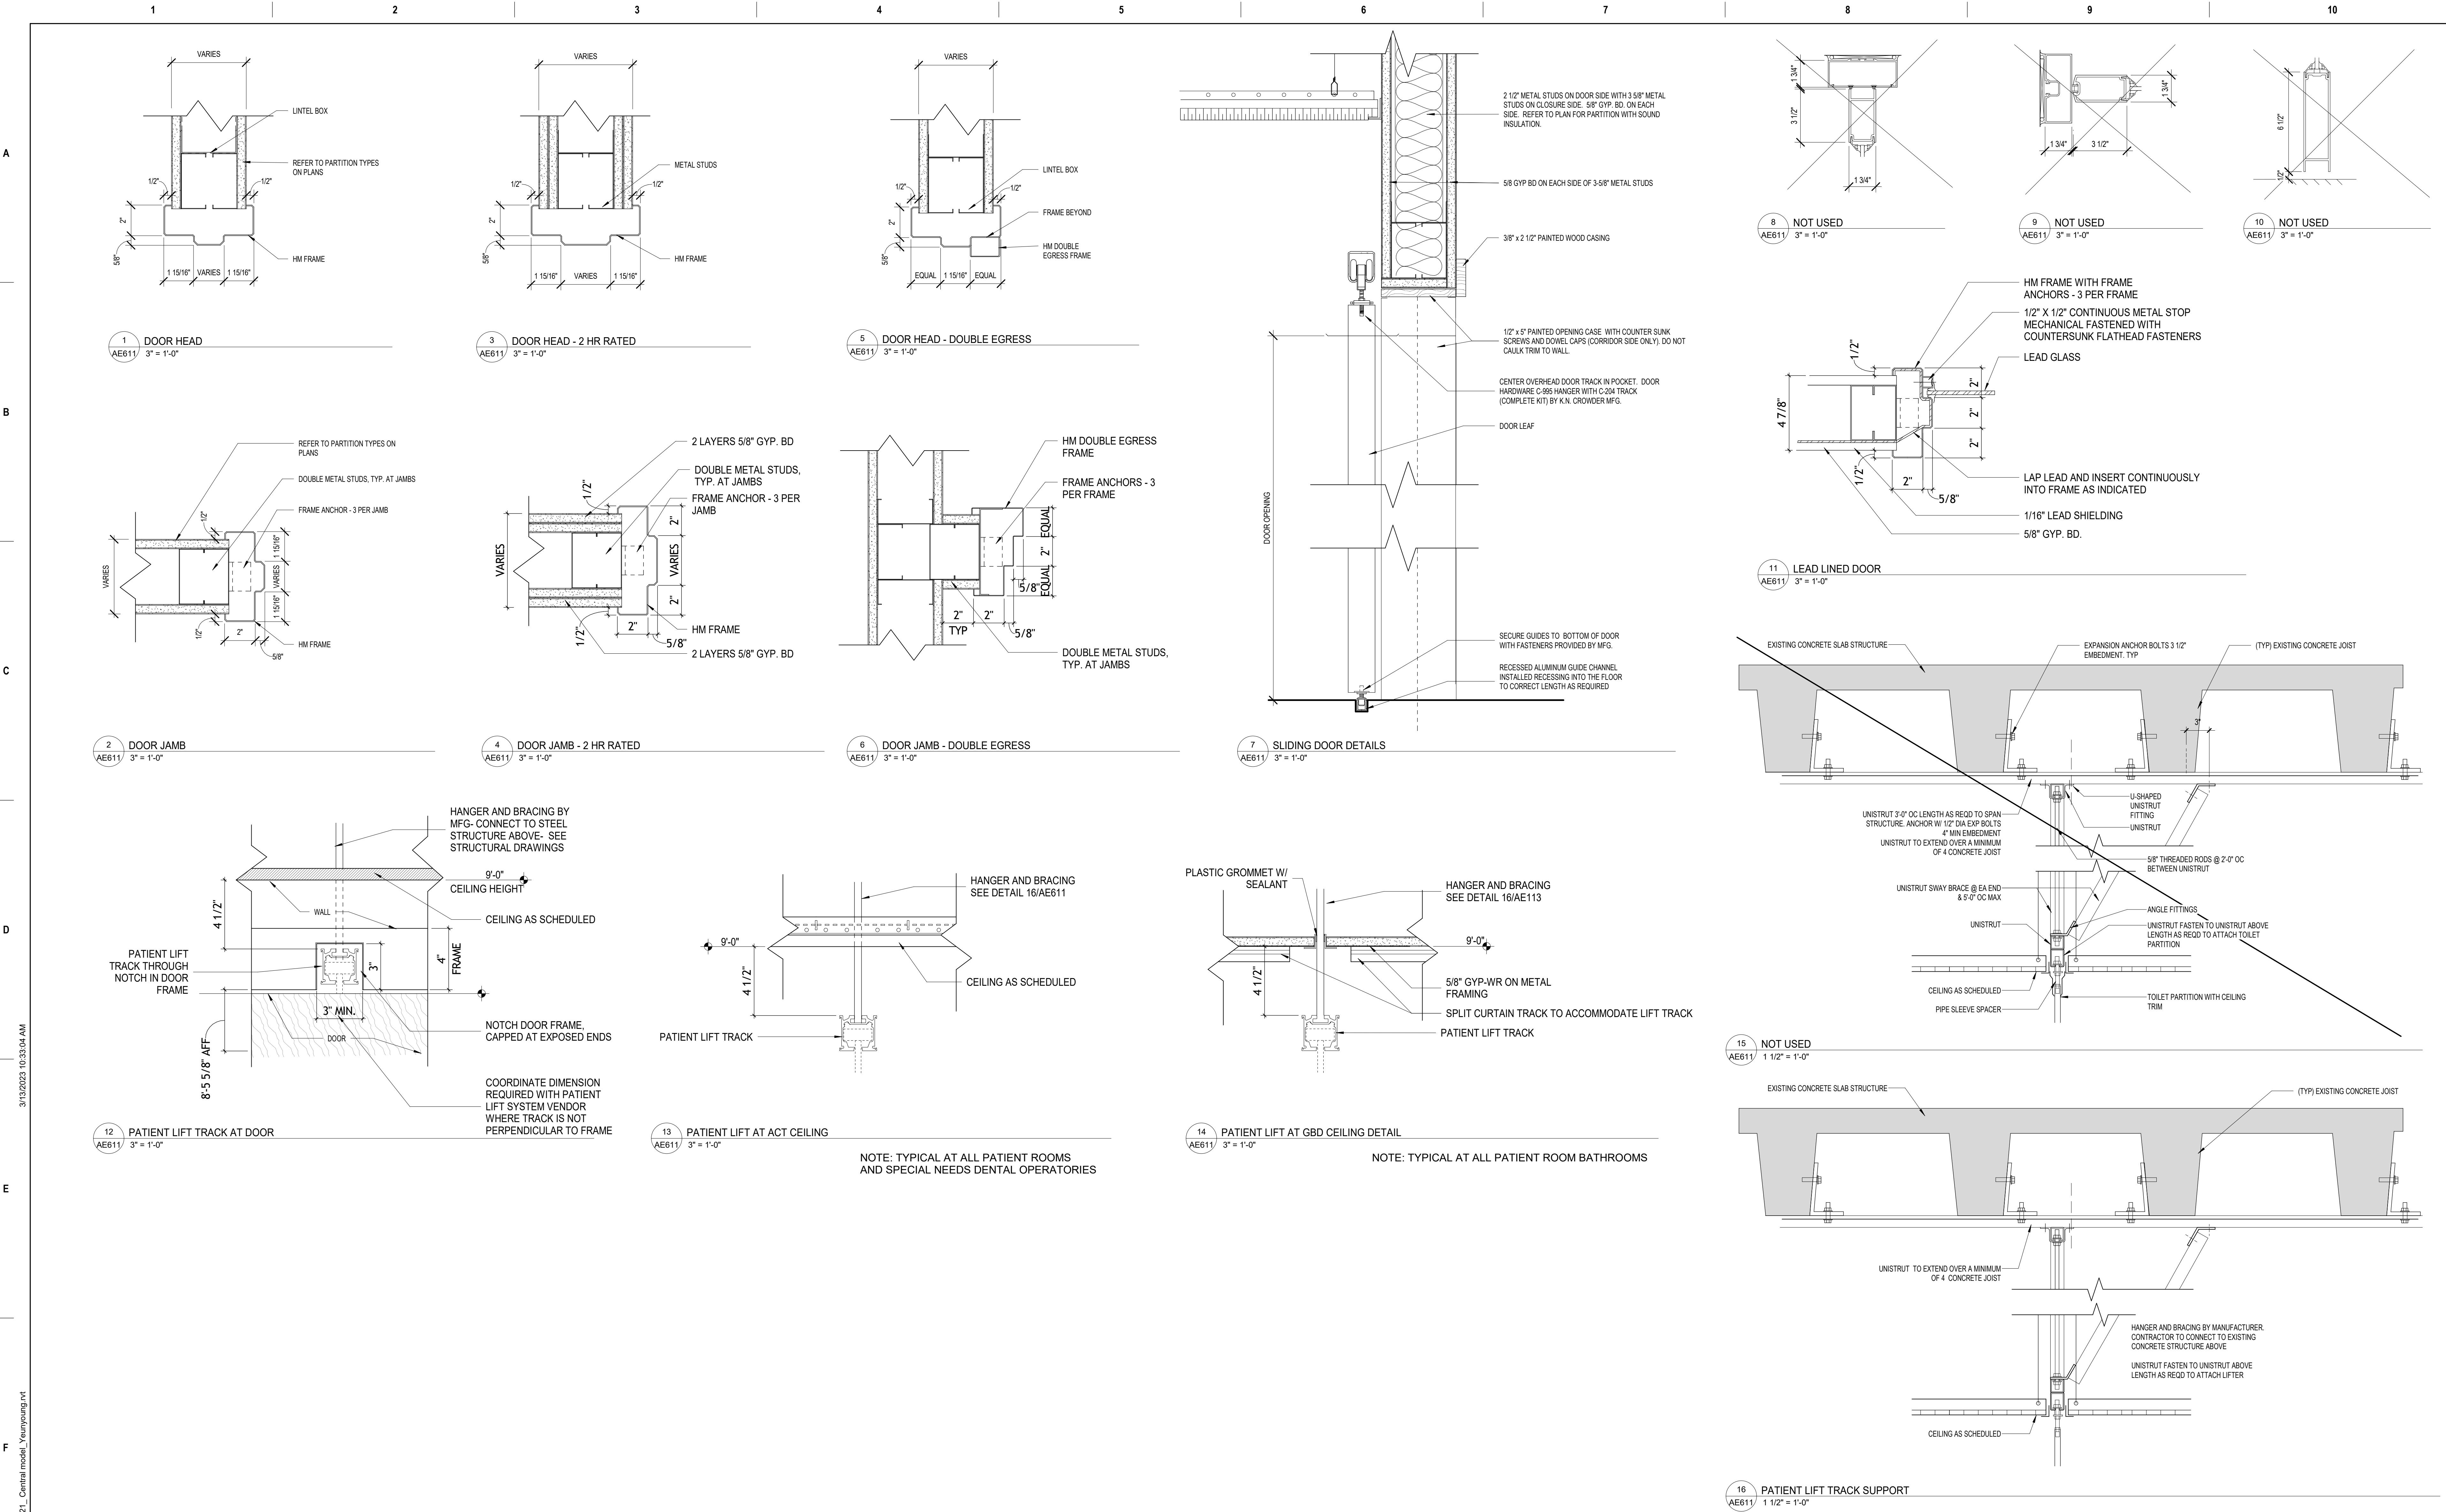


C:\Users\pdel\Documents\15090 - VANC-Blow-Building

CONSULTANT										ARCHITECT/ENGINEER OF RECORD										STAMP										Office of Construction and Facilities Management										Drawing Title										Phase										Project Title										Project Number	
										THOMAS OLESAK, ARCHITECT																				U.S. Department of Veterans Affairs										DOOR DETAILS										CONSTRUCTION DOCUMENTS										RENOVATE BUILDING 1										520-317X	
										MS Lic # 5505	Building Number	
										1050 HOYT AVE WEST ST PAUL, MN 55117	1																														Drawing Number	
										952-451-0460	AE611	

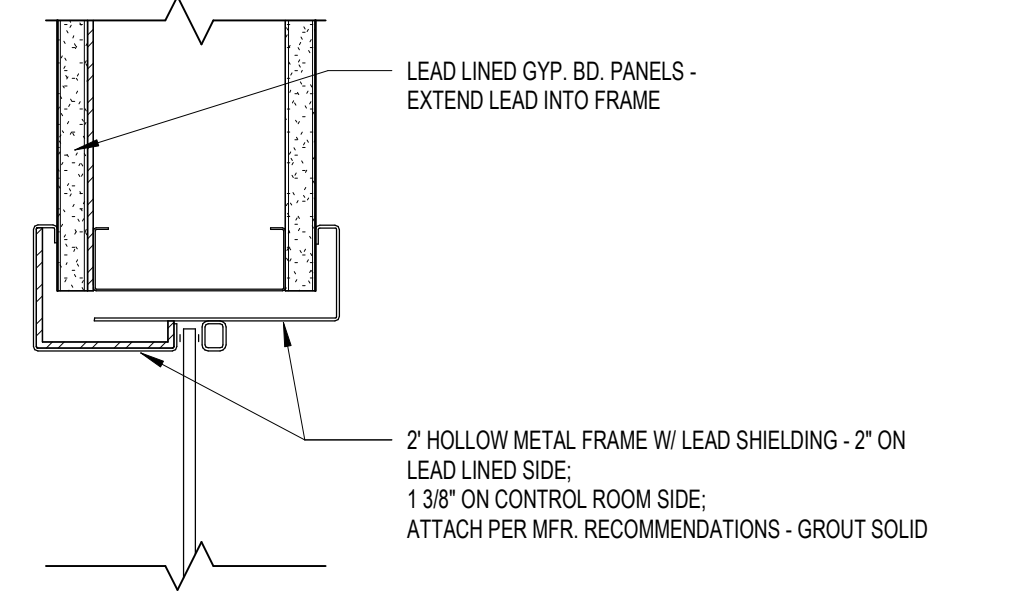

6	WINDOW HEAD - LEAD GLAZING
AE612	3" = 1'-0"

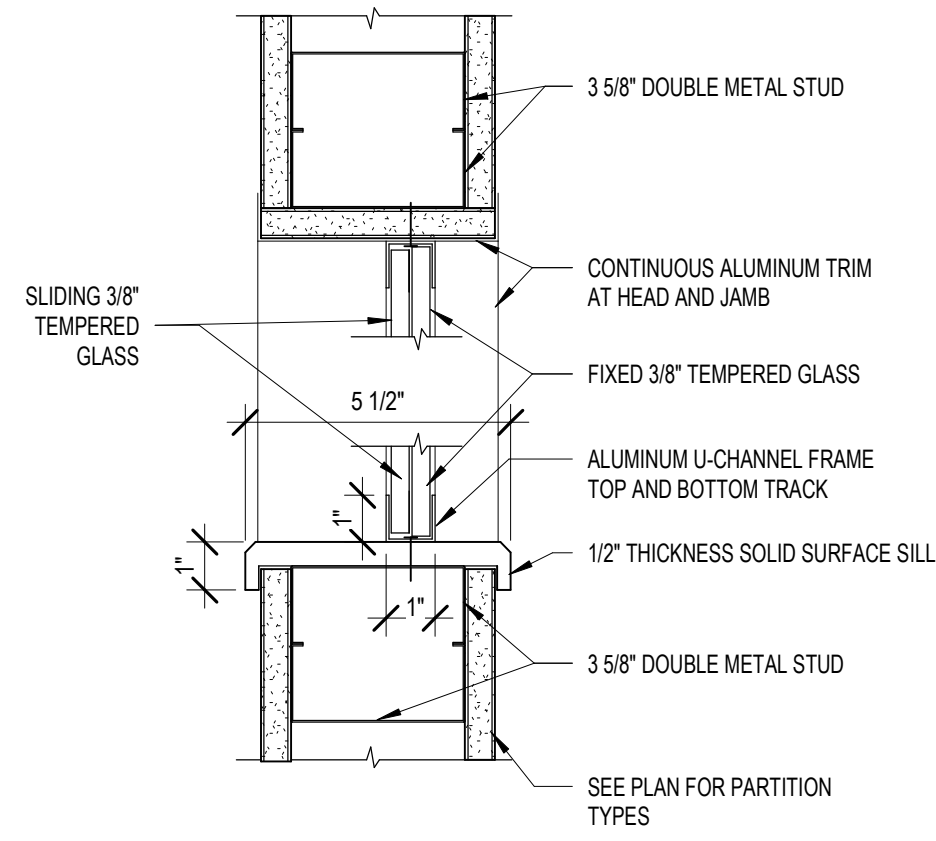

8 TRANSACTION WINDOW DETAIL
AE612 3" = 1'-0"

CONSULTANT	ARCHITECT/ENGINEER OF RECORD	STAMP	Office of Construction and Facilities Management VA U.S. Department of Veterans Affairs	Drawing Title DOOR AND WINDOW DETAILS Approved:	Project Title RENOVATE BUILDING 1	Project Number 520-317X Building Number 1
	THOMAS OLESAK, ARCHITECT MS Lic # 5505 1050 HOYT AVE WEST ST PAUL, MN 55117 952-451-0460			Drawing Title CONSTRUCTION DOCUMENTS FULLY SPRINKLERED	Location BILOXI, MISSISSIPPI Issue Date 03/10/2023 Checked LA Drawn PC	Drawing Number AE612 Dwg. 109 of 238

A

B

C

D

E

F

3/19/2025 10:35:38 AM

C:\Users\pjd\Documents\15959 - VAHC-Bldg Building 1_R21 - Central.mxd_Yunyoung not



1 3rd Floor Equipment Plan
QH101 1/8" = 1'-0"



EQUIPMENT SCHEDULE - 3RD FLOOR				
JSN	Description	ACTIVATED BY	QUANTITY	COMMENTS
A1066	MIRROR, FLOAT GLASS, WITH SS FRAME, 18 X 36	CC	19	
A4255	IV STAND, ADJUSTABLE	VV	13	
A4995	TABLE, DIAPER CHANGING, WALL MOUNTED	CC	2	
A5075	DISPENSER, HAND SOAP	VV	38	
A5077	HAND SANITIZER DISPENSER	VV	20	
A5080	DISPENSER, PAPER TOWEL	VV	38	
A5090	SANITARY NAPKIN DISPOSAL	VV	17	
A5106	WASTE DISPOSAL UNIT, SHARPS	VV	16	
A5107	GLOVE DISPENSER RACK	VV	44	
A5109A	GRAB BAR, SS, 18"	CC	13	
A5109B	GRAB BAR, 1 1/4" DIA, SS, 24"	CC	15	
A5109C	GRAB BAR, 1 1/4" DIA, SS, 30"	CC	2	
A5109D	GRAB BAR, 1 1/4" DIA, SS, 36"	CC	36	
A5109E	HORIZONTAL GRAB BAR, 42"	CC	19	
A5109F	HORIZONTAL GRAB BAR, 48"	CC	5	
A5109G	VERTICAL GRAB BAR, 1 1/4" DIA, SS, 18"	CC	29	
A5110A	SWING UP GRAB BAR	CC	14	
A5110B	SWING UP GRAB BAR W/TOILET PAPER DISPENSER	CC	3	
A5135	SHELF, UTILITY W/PO/BROOM HOLDERS, SS, SURFACE MOUNTED	CC	2	
A5145	HOOK, GARMENT, DOUBLE, SS, SURFACE MOUNTED	CC	20	
A5160	STAINLESS STEEL SHELF - 12" x 4"	CC	13	
A5170	ROD, SHOWER CURTAIN 1 1/4" DIAMETER, STRAIGHT	CC	1	
A5202	TOILET PAPER DISPENSER	VV	18	
A5210	BRACKET, TELEVISION, WALLMOUNTED W/ADJUSTABLE ARM	CC	13	

EQUIPMENT SCHEDULE - 3RD FLOOR				
JSN	Description	ACTIVATED BY	QUANTITY	COMMENTS
A5212	BRACKET, TELEVISION, WALL MOUNT WITH TILT	CC	1	
A7010A	BED, PATIENT, ELECTRONIC	VV	11	
A7010B	BARIATRIC PATIENT BED	VV	2	
F2010	STEP ON TRASH CAN	VV	2	
F2310	RACK, PAMPHLET, WALL MOUNTED	VV	1	
K1552	COFFEE BREWER, AUTO	VV	3	
K4665	OVEN, MICROWAVE	VV	2	
M0506	TV, FLAT SCREEN, 43"	VV	13	
M1801	COMPUTER AND MONITOR	VV	31	
M2025	RACK, STORAGE CYLINDER, GAS	VV	1	
M3070	HAMPER, LINEN, MOBILE, WILD	VV	2	
M3150B	AUTOMATED STORAGE/DISPENSING UNIT(OMNICELL) - 3 CELL	VV	1	
M4116	VITAL SIGNS MONITOR (WELSH ALLYN CVSM)	VV	15	
M7040	OVERBED TABLE	VV	13	
M13150	AUTOMATED STORAGE/DISPENSING UNIT (CLEAN LINEN)	VV	3	
R4650	ICE MAKER, COUNTER-TOP	VV	1	
R6200	REFRIGERATOR, UNDERCOUNTER, 5 CU. FT	VV	1	
R7250	REFRIGERATOR/FREEZER, 20 CU. FT.	VV	2	
U0002	PDI WIPE DISPENSER	VV	1	
U0003	FEMININE HYGIENE DISPENSER, SURFACE MOUNT	CC	6	

EQUIPMENT ABBREVIATIONS	
CC	CONTRACTOR FURNISHED & INSTALLED
VV	VA FURNISHED & INSTALLED
VC	VA FURNISHED & CONTRACTOR INSTALLED

NOTE: SEE SHEET QH104 MASTER EQUIPMENT SCHEDULE FOR ADDITIONAL INFORMATION

BID DOCUMENTS

NO.	REVISIONS	DATE

CONSULTANT

ARCHITECT/ENGINEER OF RECORD
THOMAS OLESAC, ARCHITECT
MS Lic # 5505
1050 HOYT AVE WEST ST PAUL, MN 55117
952-451-0460

STAMP
03.10.2023

Office of Construction and Facilities Management
VA U.S. Department of Veterans Affairs

Drawing Title
3RD FLOOR EQUIPMENT PLAN
Approved:

Phase
CONSTRUCTION DOCUMENTS
FULLY SPRINKLERED

Project Title
RENOVATE BUILDING 1
Location
BILOXI, MISSISSIPPI
Issue Date
03/10/2023
Checked
LA
Drawn
MP
Project Number
520-317X
Building Number
1
Drawing Number
QH101
Dwg. 110 of 238



1 4th Floor Equipment Plan
QH102
1/8" = 1'-0"

EQUIPMENT SCHEDULE - 4TH FLOOR				
JSN	Description	ACTIVATED BY	QUANTITY	COMMENTS
		CC	13	VENDOR PROVIDED
A1066	MIRROR, FLOAT GLASS, WITH SS FRAME, 18 X 36	CC	20	
A4255	IV STAND, ADJUSTABLE	VV	13	
A4995	TABLE, DIAPER CHANGING, WALL MOUNTED	CC	3	
A5075	DISPENSER, HAND SOAP	VV	39	
A5077	HAND SANITIZER DISPENSER	VV	15	
A5080	DISPENSER, PAPER TOWEL	VV	36	
A5090	SANITARY NAPKIN DISPOSAL	VV	18	
A5106	WASTE DISPOSAL UNIT, SHARPS	VV	16	
A5107	GLOVE DISPENSER RACK	VV	41	
A5109A	GRAB BAR, SS, 18"	CC	13	
A5109B	GRAB BAR, 1 1/4" DIA, SS, 24"	CC	17	
A5109C	GRAB BAR, 1 1/4" DIA, SS, 30"	CC	2	
A5109D	GRAB BAR, 1 1/4" DIA, SS, 36"	CC	40	
A5109E	HORIZONTAL GRAB BAR, 42"	CC	23	
A5109F	HORIZONTAL GRAB BAR, 48"	CC	4	
A5109G	VERTICAL GRAB BAR, 1 1/4" DIA, SS, 18"	CC	30	
A5110A	SWING UP GRAB BAR	CC	11	
A5135	SHELF, UTILITY WIMPOBROOM HOLDERS, SS, SURFACE MOUNTED	CC	2	
A5145	HOOK, GARMENT, DOUBLE, SS, SURFACE MOUNTED	CC	20	
A5160	STAINLESS STEEL SHELF - 12" x 4"	CC	13	
A5170	ROD, SHOWER CURTAIN 1 1/4" DIAMETER, STRAIGHT	CC	2	

EQUIPMENT SCHEDULE - 4TH FLOOR				
JSN	Description	ACTIVATED BY	QUANTITY	COMMENTS
A5202	TOILET PAPER DISPENSER	VV	19	
A5210	BRACKET, TELEVISION, WALLMOUNTED W/ADJUSTABLE ARM	CC	13	
A5212	BRACKET, TELEVISION, WALL MOUNT WITH TILT	CC	1	
A7010A	BED, PATIENT, ELECTRONIC	VV	11	
A7010B	BARIATRIC PATIENT BED	VV	2	
F2010	STEP ON TRASH CAN	VV	2	
F2310	RACK, PAMPHLET, WALL MOUNTED	VV	1	
K1552	COFFEE BREWER, AUTO	VV	1	
K4665	OVEN, MICROWAVE	VV	1	
M0506	TV, FLAT SCREEN, 43"	VV	13	
M1801	COMPUTER AND MONITOR	VV	26	
M2025	RACK, STORAGE CYLINDER, GAS	VV	1	
M3070	HAMPER, LINEN, MOBILE, W/ILID	VV	2	
M3150B	AUTOMATED STORAGE/DISPENSING UNIT(OMNICELL) - 3 CELL	VV	1	
M4116	VITAL SIGNS MONITOR (WELSH ALLYN CVSM)	VV	13	
M7040	OVERBED TABLE	VV	13	
M13150	AUTOMATED STORAGE/DISPENSING UNIT (CLEAN LINEN)	VV	3	
R4650	ICE MAKER, COUNTER-TOP	VV	1	
R6200	REFRIGERATOR, UNDERCOUNTER, 5 CU. FT	VV	1	
R7250	REFRIGERATOR/FREEZER, 20 CU. FT.	VV	2	
U0002	PDI WIPE DISPENSER	VV	1	
U0003	FEMININE HYGIENE DISPENSER, SURFACE MOUNT	CC	3	

EQUIPMENT ABBREVIATIONS	
CC:	CONTRACTOR FURNISHED & INSTALLED
VV:	VA FURNISHED & INSTALLED
VC:	VA FURNISHED & CONTRACTOR INSTALLED

NOTE: SEE SHEET QH104 MASTER EQUIPMENT SCHEDULE FOR ADDITIONAL INFORMATION

BID DOCUMENTS

NO.	REVISIONS	DATE

CONSULTANT

ARCHITECT/ENGINEER OF RECORD
THOMAS OLESAC, ARCHITECT
MS Lic # 5505
1050 HOYT AVE WEST ST PAUL, MN 55117
952-451-0460

STAMP

Office of Construction and Facilities Management

Drawing Title
4TH FLOOR EQUIPMENT PLAN
Approved:

Phase
CONSTRUCTION DOCUMENTS
FULLY SPRINKLERED

Project Title
RENOVATE BUILDING 1

Location
BILOXI, MISSISSIPPI

Issue Date
03/10/2023


Checked
LA

Drawn
MP

Project Number
520-317X
Building Number
1

Drawing Number
QH102

Dwg. 111 of 238

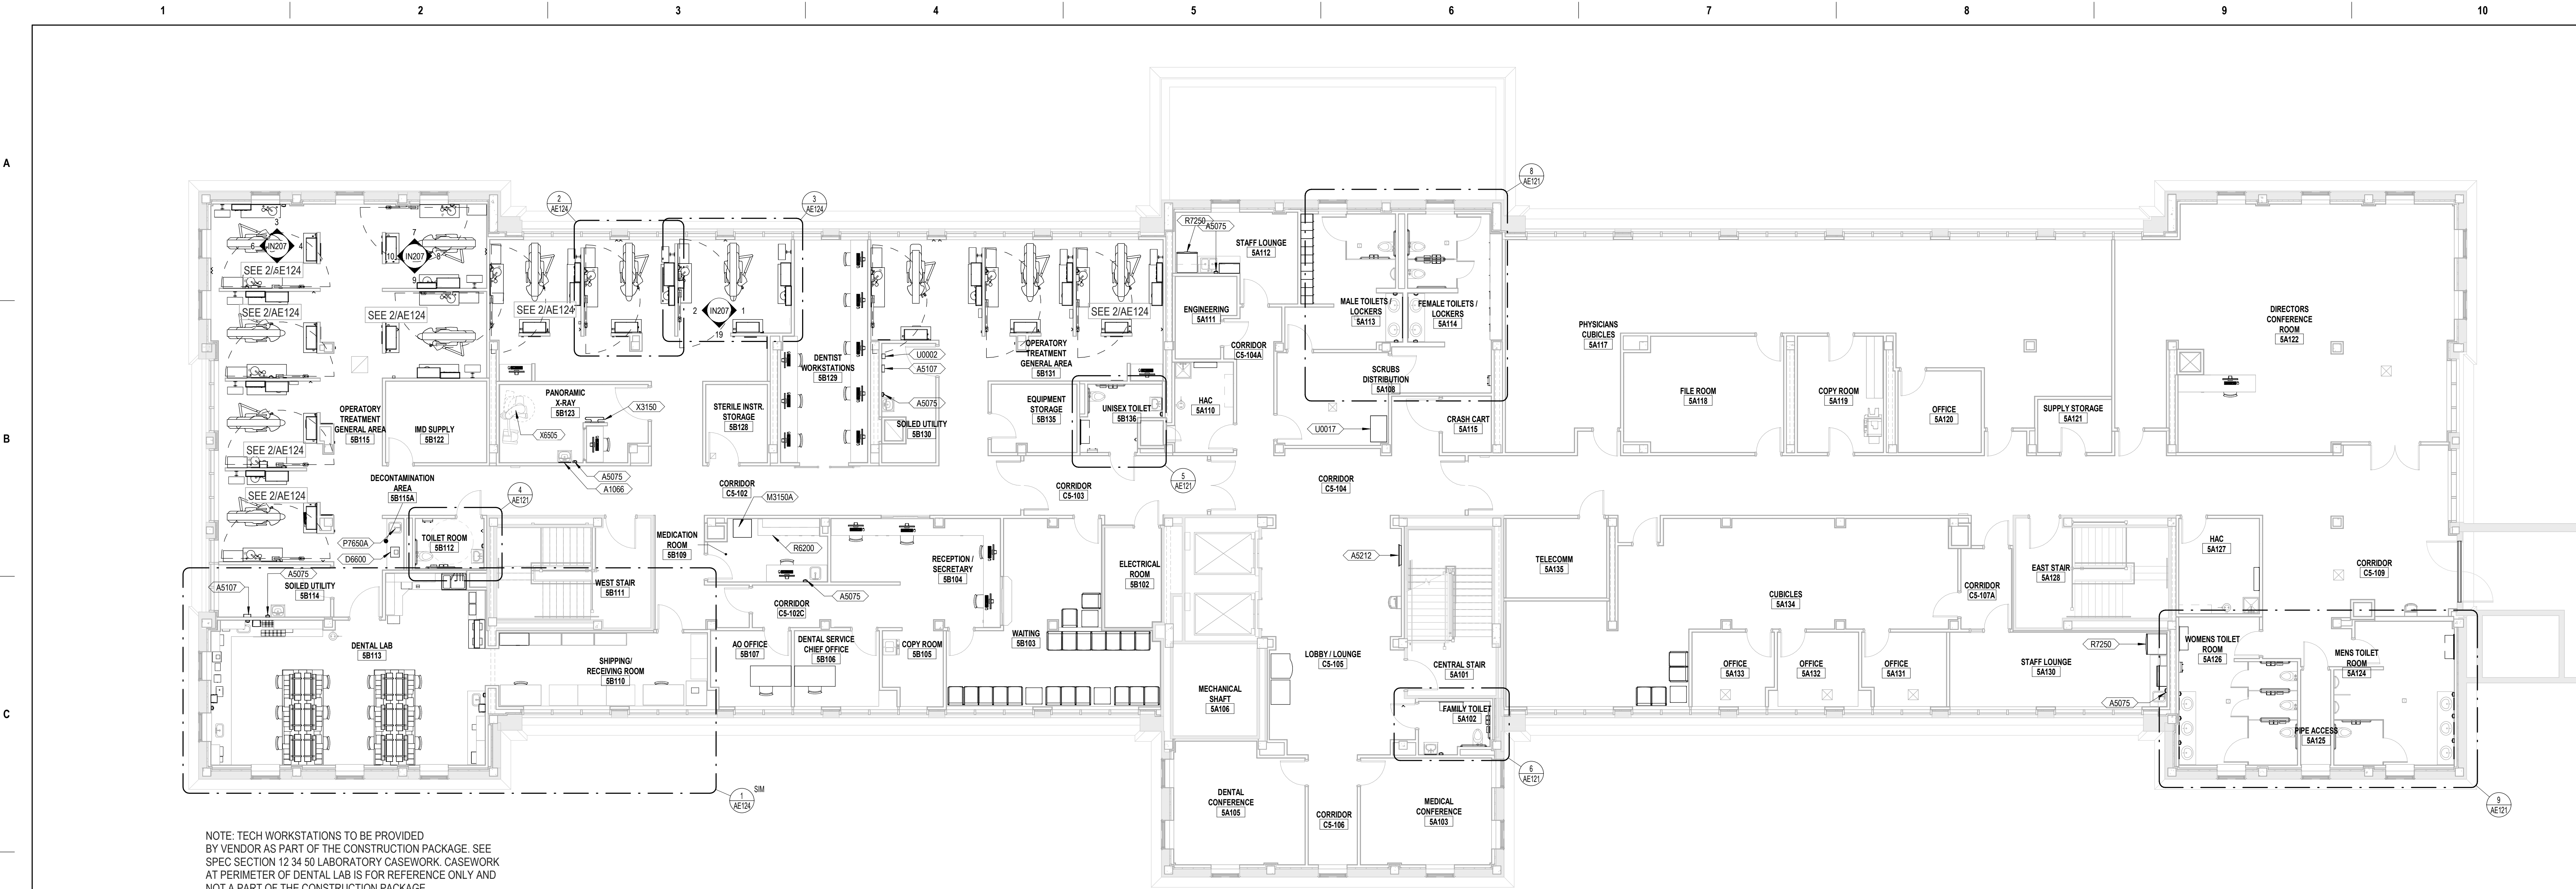

NOTE: TECH WORKSTATIONS TO BE PROVIDED BY VENDOR AS PART OF THE CONSTRUCTION PACKAGE. SEE SPEC SECTION 12 34 50 LABORATORY CASEWORK, CASEWORK AT PERIMETER OF DENTAL LAB IS FOR REFERENCE ONLY AND NOT A PART OF THE CONSTRUCTION PACKAGE.

1 5th Floor Equipment Plan
1/8" = 1'-0"

EQUIPMENT SCHEDULE - 5TH FLOOR				
JSN	Description	ACTIVATED BY	QUANTITY	COMMENTS
A1012	TELEPHONE, WALL MOUNTED	VV	13	
A1066	MIRROR, FLOAT GLASS, WITH SS FRAME, 18 X 36	CC	24	
A1070	MIRROR, FLOAT GLASS, WITH SS FRAME, 60 X 36	CC	2	
A4995	TABLE, DIAPER CHANGING, WALL MOUNTED	CC	4	
A5075	DISPENSER, HAND SOAP	VV	46	
A5077	HAND SANITIZER DISPENSER	VV	20	
A5080	DISPENSER, PAPER TOWEL	VV	34	
A5090	SANITARY NAPKIN DISPOSAL	VV	8	
A5106	WASTE DISPOSAL UNIT, SHARPS	VV	14	
A5107	GLOVE DISPENSER RACK	VV	26	
A5109D	GRAB BAR, 1 1/4" DIA, SS, 36"	CC	7	
A5109E	HORIZONTAL GRAB BAR, 42"	CC	13	
A5135	SHELF, UTILITY W/IMPOBROOM HOLDERS, SS, SURFACE MOUNTED	CC	2	
A5145	HOOK, GARMENT, DOUBLE, SS, SURFACE MOUNTED	CC	19	
A5202	TOILET PAPER DISPENSER	VV	10	
A5212	BRACKET, TELEVISION, WALL MOUNT WITH TILT	CC	1	
D0670	CONSOLE, TREATMENT UNIT, DENTAL OPERATORY	CC	12	SEE SPEC SECTION 12 35 70.74
D0680	CONSOLE, ACCESSORY/SIDE DENTAL OPERATORY	CC	24	SEE SPEC SECTION 12 35 70.74
D0682	3 GLOVE DISPENSING CABINET, DENTAL OPERATORY	CC	12	SEE SPEC SECTION 12 35 70.74
D0685	STORAGE CABINET, DENTAL OPERATORY - 34 INCH WIDE	CC	23	SEE SPEC SECTION 12 35 70.74
D0685B	STORAGE CABINET, FULL HEIGHT, 2 DOORS, LOCKABLE DENTAL	CC	12	SEE SPEC SECTION 12 35 70.74
D0755	TANK ASSEMBLY, BOILOUT - CURING, DOUBLE	CC	1	SEE SPEC SECTION 12 34 50, SEE EP103 & PL106 MEP FOR CONNECTIONS
D2520	MOBILE STORAGE CABINET	CC	12	SEE SPEC SECTION 12 35 70.74
D3320	CHAIR, DENTAL OPERATING	CC	12	SEE SPEC SECTION 11 74 00
D3565	RESIN CURING UNIT, VISABLE LIGHT	VV	8	
D4100	CLEANER, STEAM, DENTAL	VV	1	
D4260	HANDPIECE, LABORATORY, DENTAL, ELECTRIC	VV	8	
D4320	PRESS, FLASK, HYDRAULIC, SINGLE FLASK	VV	2	

EQUIPMENT SCHEDULE - 5TH FLOOR				
JSN	Description	ACTIVATED BY	QUANTITY	COMMENTS
D4560	ENGINE, DENTAL BENCH, ELECTRIC	VV	8	
D4590	CHISEL, DENTAL, PNEUMATIC	VV	2	
D6600	MIXER/INVESTOR, WITH VACUUM	VV	2	
D6650	FROMER, VACUUM, W/MOTOR, VACUUM PUMP, HEATER	VV	1	
D8250	DELIVERY SYSTEM, DENTAL OPERATORY WITH ASST INSTRUMENTATION	CC	12	SEE SPEC SECTION 11 74 00
D8530	DENTAL POLISHER	VV	1	
D8850	AMALGAMATOR, DENTAL	VV	11	
D8950	VIBRATOR, DENTAL, HEAVY DUTY	VV	2	
D9015	MICROFINISHER, DENTAL, COUNTER MOUNTED	VV	1	
D9035	DRIVER, MODEL INDEXING PINS	VV	1	
D9050	TRIMMER, MODEL, DENTAL 0.25 HP	VV	2	
DX001	PRESSURE POT 8 QUART	VV	2	
DX002	DENTAL WORK BENCH, 23" DEPTH	VC	14	SEE SPEC SECTION 12 34 50
DX003	AIR HOSE X6 + ACCESSORIES	VV	12	
DX004	SAND SHELL XL	VV	1	
DX005	WAXING UNIT	VV	12	
DX006	TOUCH O MATIC BUN BURNER NATURAL GAS #77-0	VV	12	
DX007	AIR PURIFIER 301F	VV	1	
DX008	SAND VAC GRAY	VV	2	
DX009	ATLAS UPPER FLASK W/REAR GUIDE PIN #44U	VV	20	
DX010	ATLAS LOWER FLASK W/REAR GUIDE PIN #44L	VV	20	
DX011	COMPRESS FLASKS F2	VV	12	
DX012	RELINER JIG 2 POST	VV	8	
DX013	IMPULSE HEAT SEALER	VV	1	
DX014	FLAMMABLE CABINET	VV	1	
DX016	ARTICULATOR MOUNTING PLATE	VV	40	
DX017	HANAU WIDE - VUE ARTICULATOR HANAU ARCON 183-2	VV	12	
DX018	WHIP MIX MODEL 2240 ARTICULATOR W/SERIES 200 FRAME	VV	12	
DX019	CURING UNIT	VV	2	

EQUIPMENT SCHEDULE - 5TH FLOOR				
JSN	Description	ACTIVATED BY	QUANTITY	COMMENTS
DX020	DENTAL MOLDING VIBRATOR	VV	1	
DX021	FUME HOOD	CC	1	SEE SPEC SECTION 23 38 13
DX023	DENTAL LAB CASEWORK	VC	1	SEE SPEC SECTION 12 34 50
K4665	OVEN, MICROWAVE	VV	2	
M1801	COMPUTER AND MONITOR	VV	18	
M1801A	LAPTOP COMPUTER	VV	11	
M1803	COMPUTER WORKSTATION, WALL MOUNTED	CC	12	
M3150A	AUTOMATED STORAGE/DISPENSING UNIT(OMNICELL) - 1 CELL	VV	1	
P7650	TRAP, PLASTER, SMALL	CC	3	
P7650A	TRAP, PLASTER SMALL	CC	1	SEE MEP
R6200	REFRIGERATOR, UNDERCOUNTER, 5 CU. FT	VV	1	
R7250	REFRIGERATOR/FREEZER, 20 CU. FT.	VV	2	
U0002	PDI WIPE DISPENSER	VV	1	
U0003	FEMININE HYGIENE DISPENSER, SURFACE MOUNT	CC	4	
U0017	SCRUBX MACHINE	VV	1	
X3150	RACK, APRON & GLOVE, WALL MOUNT	VV	1	
X6505	RADIOGRAPHIC UNIT, DENTAL PANOGRAPHIC	VV	1	
X6600	RADIOGRAPHIC XRAY UNIT (PLANMECA PRO-X)	VV	12	
X6610	SENSOR, DENTAL IMAGING SYSTEM (PLANMECA PRO-X)	VV	12	
X6620	EXPOSURE SWITCH - DENTAL XRAY (PLANMECA PRO-X)	VV	12	

EQUIPMENT ABBREVIATIONS

CC: CONTRACTOR FURNISHED & INSTALLED
VV: VA FURNISHED & INSTALLED
VC: VA FURNISHED & CONTRACTOR INSTALLED

NOTE: SEE SHEET QH104 MASTER EQUIPMENT SCHEDULE FOR ADDITIONAL INFORMATION

BID DOCUMENTS

NO.	REVISIONS	DATE

CONSULTANT

ARCHITECT/ENGINEER OF RECORD
THOMAS OLESACK, ARCHITECT
MS Lic # 5505
1050 HOYT AVE WEST ST PAUL, MN 55117
952-451-0460

STAMP
REGISTERED ARCHITECT
Thomas Olesack
2005
STATE OF MISSISSIPPI
03.10.2023

Office of Construction and Facilities Management
VA U.S. Department of Veterans Affairs

Drawing Title
5TH FLOOR EQUIPMENT PLAN
Approved:

Phase
CONSTRUCTION DOCUMENTS
FULLY SPRINKLERED

Project Title
RENOVATE BUILDING 1
Location
BILOXI, MISSISSIPPI
Issue Date
03/10/2023
Checked
LA
Drawn
MP

Project Number
520-317X
Building Number
1
Drawing Number
QH103
Dwg. 112 of 238

A

B

C

D

E

F

5/4/2023 10:22:40 AM

C:\Users\pjd\Documents\15959 - VAMC-Bloor Building 1_R21 - Central.mxd_Yunyoung.nt

EQUIPMENT SCHEDULE				
JSN	Description	ACTIVATED BY	QUANTITY	COMMENTS
A1012	TELEPHONE, WALL MOUNTED	VV	13	
A1066	MIRROR, FLOAT GLASS, WITH SS FRAME, 18 X 36	CC	63	
A1070	MIRROR, FLOAT GLASS, WITH SS FRAME, 60 X 36	CC	2	
A4255	IV STAND, ADJUSTABLE	VV	26	
A4995	TABLE, DIAPER CHANGING, WALL MOUNTED	CC	10	
A5075	DISPENSER, HAND SOAP	VV	123	
A5077	HAND SANITIZER DISPENSER	VV	55	
A5080	DISPENSER, PAPER TOWEL	VV	112	
A5090	SANITARY NAPKIN DISPOSAL	VV	43	
A5106	WASTE DISPOSAL UNIT, SHARPS	VV	46	
A5107	GLOVE DISPENSER RACK	VV	111	
A5109A	GRAB BAR, SS, 18"	CC	26	
A5109B	GRAB BAR, 1 1/4" DIA, SS, 24"	CC	32	
A5109C	GRAB BAR, 1 1/4" DIA, SS, 30"	CC	4	
A5109D	GRAB BAR, 1 1/4" DIA, SS, 36"	CC	83	
A5109E	HORIZONTAL GRAB BAR, 42"	CC	55	
A5109F	HORIZONTAL GRAB BAR, 48"	CC	9	
A5109G	VERTICAL GRAB BAR, 1 1/4" DIA, SS, 18"	CC	59	
A5110A	SWING UP GRAB BAR	CC	27	
A5110B	SWING UP GRAB BAR W/TOILET PAPER DISPENSER	CC	5	
A5135	SHELF, UTILITY W/MPOBROOM HOLDERS, SS, SURFACE MOUNTED	CC	6	
A5145	HOOK, GARMENT, DOUBLE, SS, SURFACE MOUNTED	CC	59	
A5160	STAINLESS STEEL SHELF - 12" x 4"	CC	26	
A5170	ROD, SHOWER CURTAIN 1 1/4" DIAMETER, STRAIGHT	CC	3	
A5202	TOILET PAPER DISPENSER	VV	47	
A5210	BRACKET, TELEVISION, WALLMOUTNED W/ADJUSTABLE ARM	CC	26	
A5212	BRACKET, TELEVISION, WALL MOUNT WITH TILT	CC	3	
A7010A	BED, PATIENT, ELECTRONIC	VV	22	
A7010B	BARIATRIC PATIENT BED	VV	4	
D0670	CONSOLE, TREATMENT UNIT, DENTAL OPERATORY	CC	12	SEE SPEC SECTION 12 35 70.74
D0680	CONSOLE, ACCESSORY/SIDE DENTAL OPERATORY	CC	24	SEE SPEC SECTION 12 35 70.74
D0682	3 GLOVE DISPENSING CABINET, DENTAL OPERATORY	CC	12	SEE SPEC SECTION 12 35 70.74
D0685	STORAGE CABINET, DENTAL OPERATORY - 34 INCH WIDE	CC	23	SEE SPEC SECTION 12 35 70.74
D0685B	STORAGE CABINET, FULL HEIGHT, 2 DOORS, LOCKABLE DENTAL	CC	12	SEE SPEC SECTION 12 35 70.74
D0755	TANK ASSEMBLY, BOILOUT - CURING, DOUBLE	CC	1	SEE SPEC SECTION 12 34 50, SEE EP103 & PL106 MEP FOR CONNECTIONS
D2520	MOBILE STORAGE CABINET	CC	12	SEE SPEC SECTION 12 35 70.74
D3320	CHAIR, DENTAL OPERATNG	CC	12	SEE SPEC SECTION 11 74 00
D3665	RESIN CURING UNIT, VISABLE LIGHT	VV	8	
D4100	CLEANER, STEAM, DENTAL	VV	1	
D4260	HANDPIECE, LABORATORY, DENTAL, ELECTRIC	VV	8	
D4320	PRESS, FLASK, HYDRAULIC, SINGLE FLASK	VV	2	
D4560	ENGINE, DENTAL BENCH, ELECTRIC	VV	8	
D4590	CHISEL, DENTAL, PNEUMATIC	VV	2	
D6600	MIXER/INVESTOR , WITH VACUUM	VV	2	
D6650	FROMER, VACCUM, W/MOTOR, VACCUM PUMP, HEATER	VV	1	
D8250	DELIVERY SYSTEM, DENTAL OPERATORY WITH ASST INSTRUMENTATION	CC	12	SEE SPEC SECTION 11 74 00
D8530	DENTAL POLISHER	VV	1	
D8850	AMALGAMATOR, DENTAL	VV	11	
D8950	VIBRATOR, DENTAL, HEAVY DUTY	VV	2	
D9015	MICROFINISHER, DENTAL, COUNTER MOUNTED	VV	1	
D9035	DRIVER, MODEL INDEXING PINS	VV	1	

EQUIPMENT SCHEDULE				
JSN	Description	ACTIVATED BY	QUANTITY	COMMENTS
D9050	TRIMMER, MODEL, DENTAL 0.25 HP	VV	2	
DX001	PRESSURE POT 8 QUART	VV	2	
DX002	DENTAL WORK BENCH, 23" DEPTH	VC	14	SEE SPEC SECTION 12 34 50
DX003	AIR HOSE X6 + ACCESSORIES	VV	12	
DX004	SAND SHELL XL	VV	1	
DX005	WAXING UNIT	VV	12	
DX006	TOUCH O MATIC BUN BURNER NATURAL GAS #77-0	VV	12	
DX007	AIR PURIFUER 301F	VV	1	
DX008	SAND VAC GRAY	VV	2	
DX009	ATLAS UPPER FLASK W/REAR GUIDE PIN #44U	VV	20	
DX010	ATLAS LOWER FLASK W/REAR GUIDE PIN #44L	VV	20	
DX011	COMPRESS FLASKS F2	VV	12	
DX012	RELINE JIG 2 POST	VV	8	
DX013	IMPULSE HEAT SEALER	VV	1	
DX014	FLAMMABLE CABINET	VV	1	
DX016	ARTICULATOR MOUNTING PLATE	VV	40	
DX017	HANAU WIDE - VUE ARTICULATOR HANAU ARCON 183-2	VV	12	
DX018	WHIP MIX MODEL 2240 ARTICULATOR W/SERIES 200 FRAME	VV	12	
DX019	CURING UNIT	VV	2	
DX020	DENTAL MOLDING VIBRATOR	VV	1	
DX021	FUME HOOD	CC	1	SEE SPEC SECTION 23 38 13
DX023	DENTAL LAB CASEWORK	VC	1	SEE SPEC SECTION 12 34 50
F2010	STEP ON TRASH CAN	VV	4	
F2310	RACK, PAMPHLET, WALL MOUNTED	VV	2	
K1552	COFFEE BREWER, AUTO	VV	4	
K4665	OVEN, MICROWAVE	VV	5	
M0506	TV, FLAT SCREEN, 43"	VV	26	
M1801	COMPUTER AND MONITOR	VV	75	
M1801A	LAPTOP COMPUTER	VV	11	
M1803	COMPUTER WORKSTATION, WALL MOUNTED	CC	12	
M2025	RACK, STORAGE CYLINDER, GAS	VV	2	
M3070	HAMPER, LINEN, MOBILE, W/LID	VV	4	
M3150A	AUTOMATED STORAGE/DISPENSING UNIT(OMNICELL) - 1 CELL	VV	1	
M3150B	AUTOMATED STORAGE/DISPENSING UNIT(OMNICELL) - 3 CELL	VV	2	
M4116	VITAL SIGNS MONITOR (WELSH ALLYN CVSM)	VV	28	
M7040	OVERBED TABLE	VV	26	
M13150	AUTOMATED STORAGE/DISPENSING UNIT (CLEAN LINEN)	VV	6	
P7650	TRAP, PLASTER, SMALL	CC	3	
P7650A	TRAP, PLASTER SMALL	CC	1	SEE MEP
R4650	ICE MAKER, COUNTER-TOP	VV	2	
R6200	REFRIGERATOR, UNDERCOUNTER, 5 CU. FT	VV	3	
R7250	REFRIGERATOR/FREEZER, 20 CU. FT.	VV	6	
U0002	PDI WIPE DISPENSER	VV	3	
U0003	FEMININE HYGIENE DISPENSER, SURFACE MOUNT	CC	13	
U0017	SCRUBX MACHINE	VV	1	
X3150	RACK, APRON & GLOVE, WALL MOUNT	VV	1	
X6505	RADIOGRAPHIC UNIT, DENTAL PANOGRAPHIC	VV	1	
X6600	RADIOGRAPHIC XRAY UNIT (PLANMECA PRO-X)	VV	12	
X6610	SENSOR, DENTAL IMAGING SYSTEM (PLANMECA PRO-X)	VV	12	
X6620	EXPOSURE SWITCH - DENTAL XRAY (PLANMECA PRO-X)	VV	12	

EQUIPMENT ABBREVIATIONS	
CC:	CONTRACTOR FURNISHED & INSTALLED
VV:	VA FURNISHED & INSTALLED
VC:	VA FURNISHED & CONTRACTOR INSTALLED

A

B

C

D

E

F

BID DOCUMENTS

<table><tr><td></td><td></td><td></td></tr><tr><td></td><td></td><td></td></tr><tr><td></td><td></td><td></td></tr><tr><td></td><td></td><td></td></tr><tr><td></td><td></td><td></td></tr><tr><td></td><td></td><td></td></tr><tr><td>NO.</td><td>REVISIONS</td><td>DATE</td></tr></table>																					NO.	REVISIONS	DATE	CONSULTANT		ARCHITECT/ENGINEER OF RECORD		STAMP	Office of Construction and Facilities Management		Drawing Title	Phase	Project Title		Project Number	
NO.	REVISIONS	DATE																																		
					THOMAS OLESAK, ARCHITECT			VA U.S. Department of Veterans Affairs		EQUIPMENT SCHEDULE	CONSTRUCTION DOCUMENTS	RENOVATE BUILDING 1	520-317X		Building Number 1																					
					MS Lic # 5505								Location		Drawing Number																					
					1050 HOYT AVE WEST ST PAUL, MN 55117 952-451-0460								BILOXI, MISSISSIPPI		QH104																					
										Approved:	FULLY SPRINKLERED		Issue Date		Checked	Drawn	Dwg. 113 of 238																			
													03/10/2023		LA	MP																				