




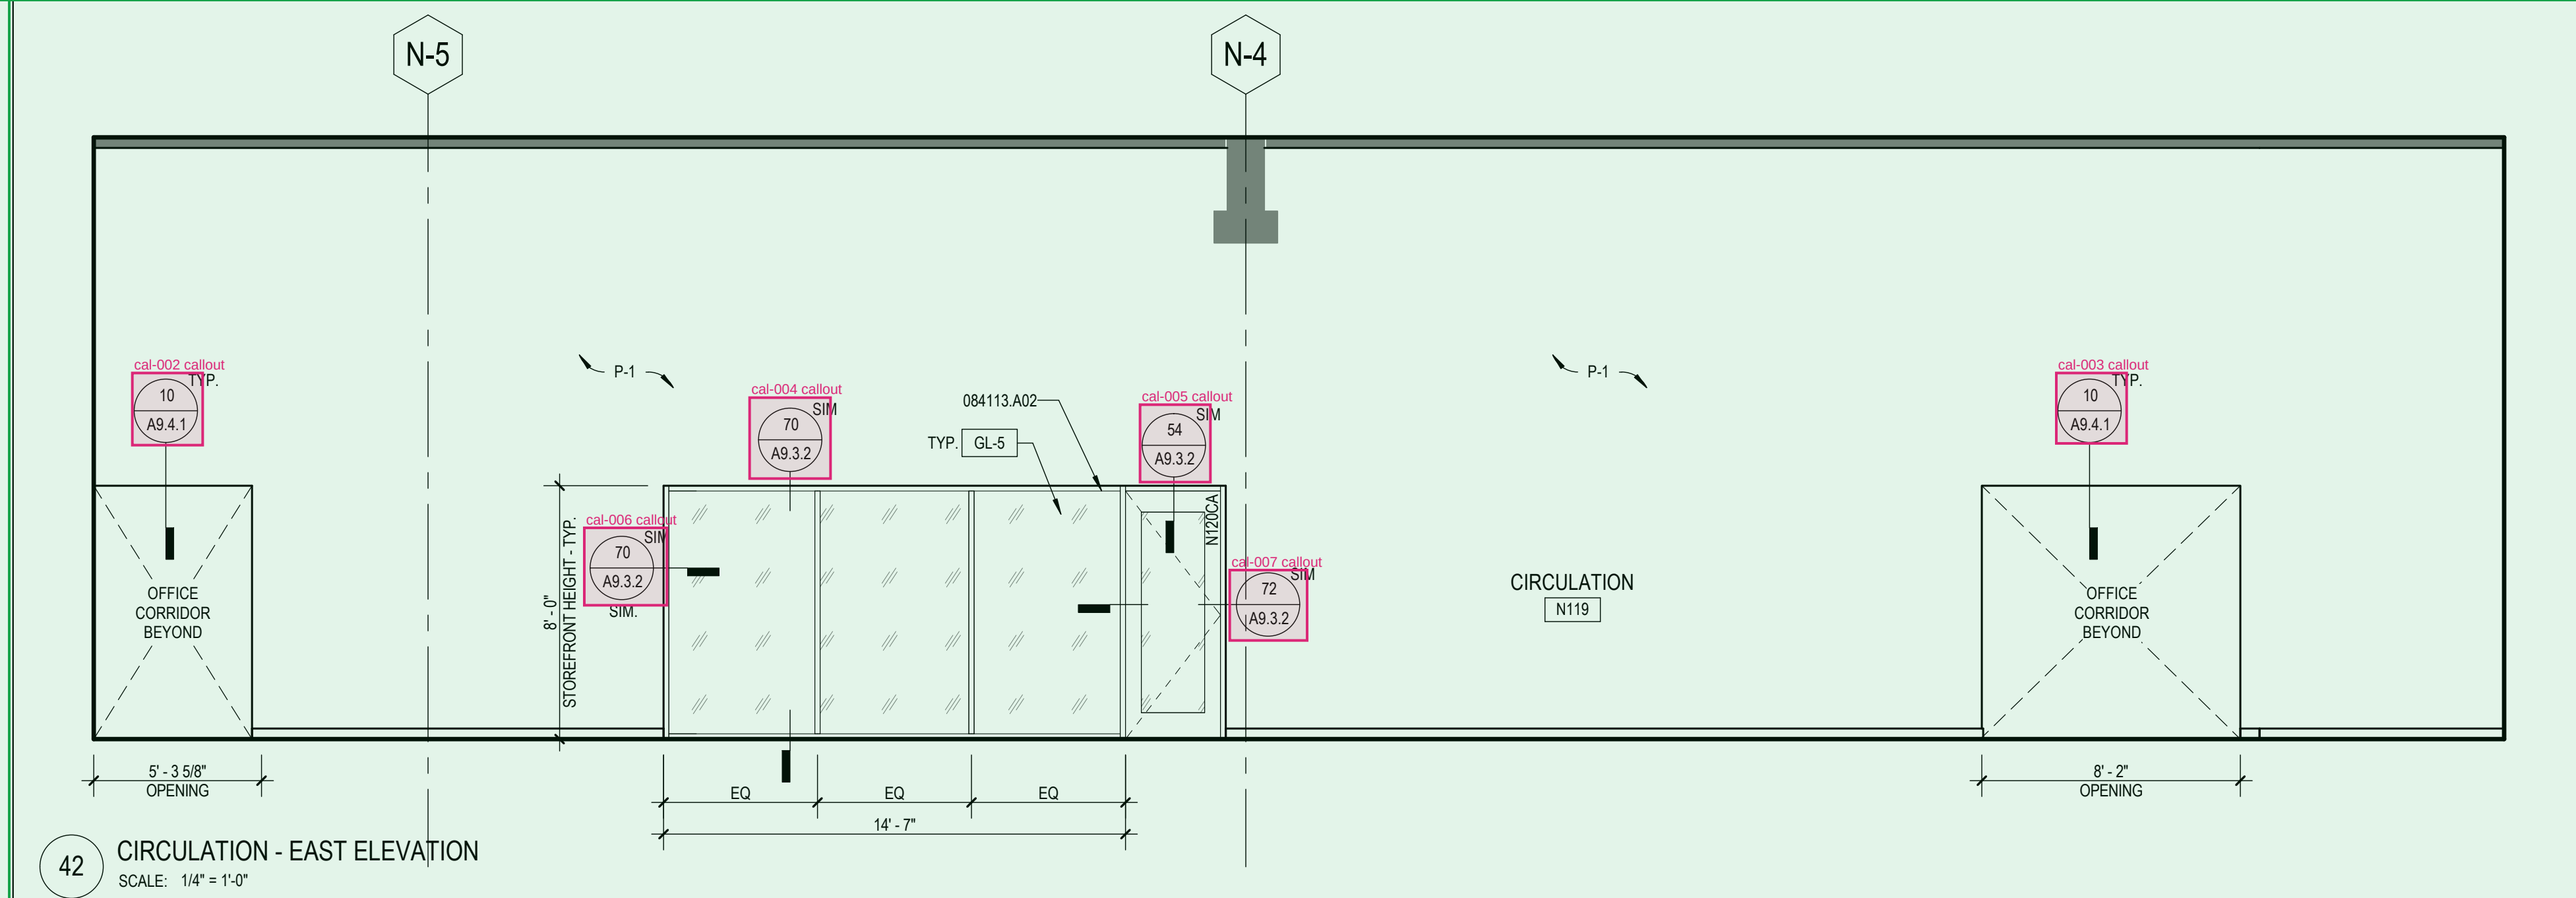

42 CIRCULATION - EAST ELEVATION
SCALE: 1/4" = 1'-0"

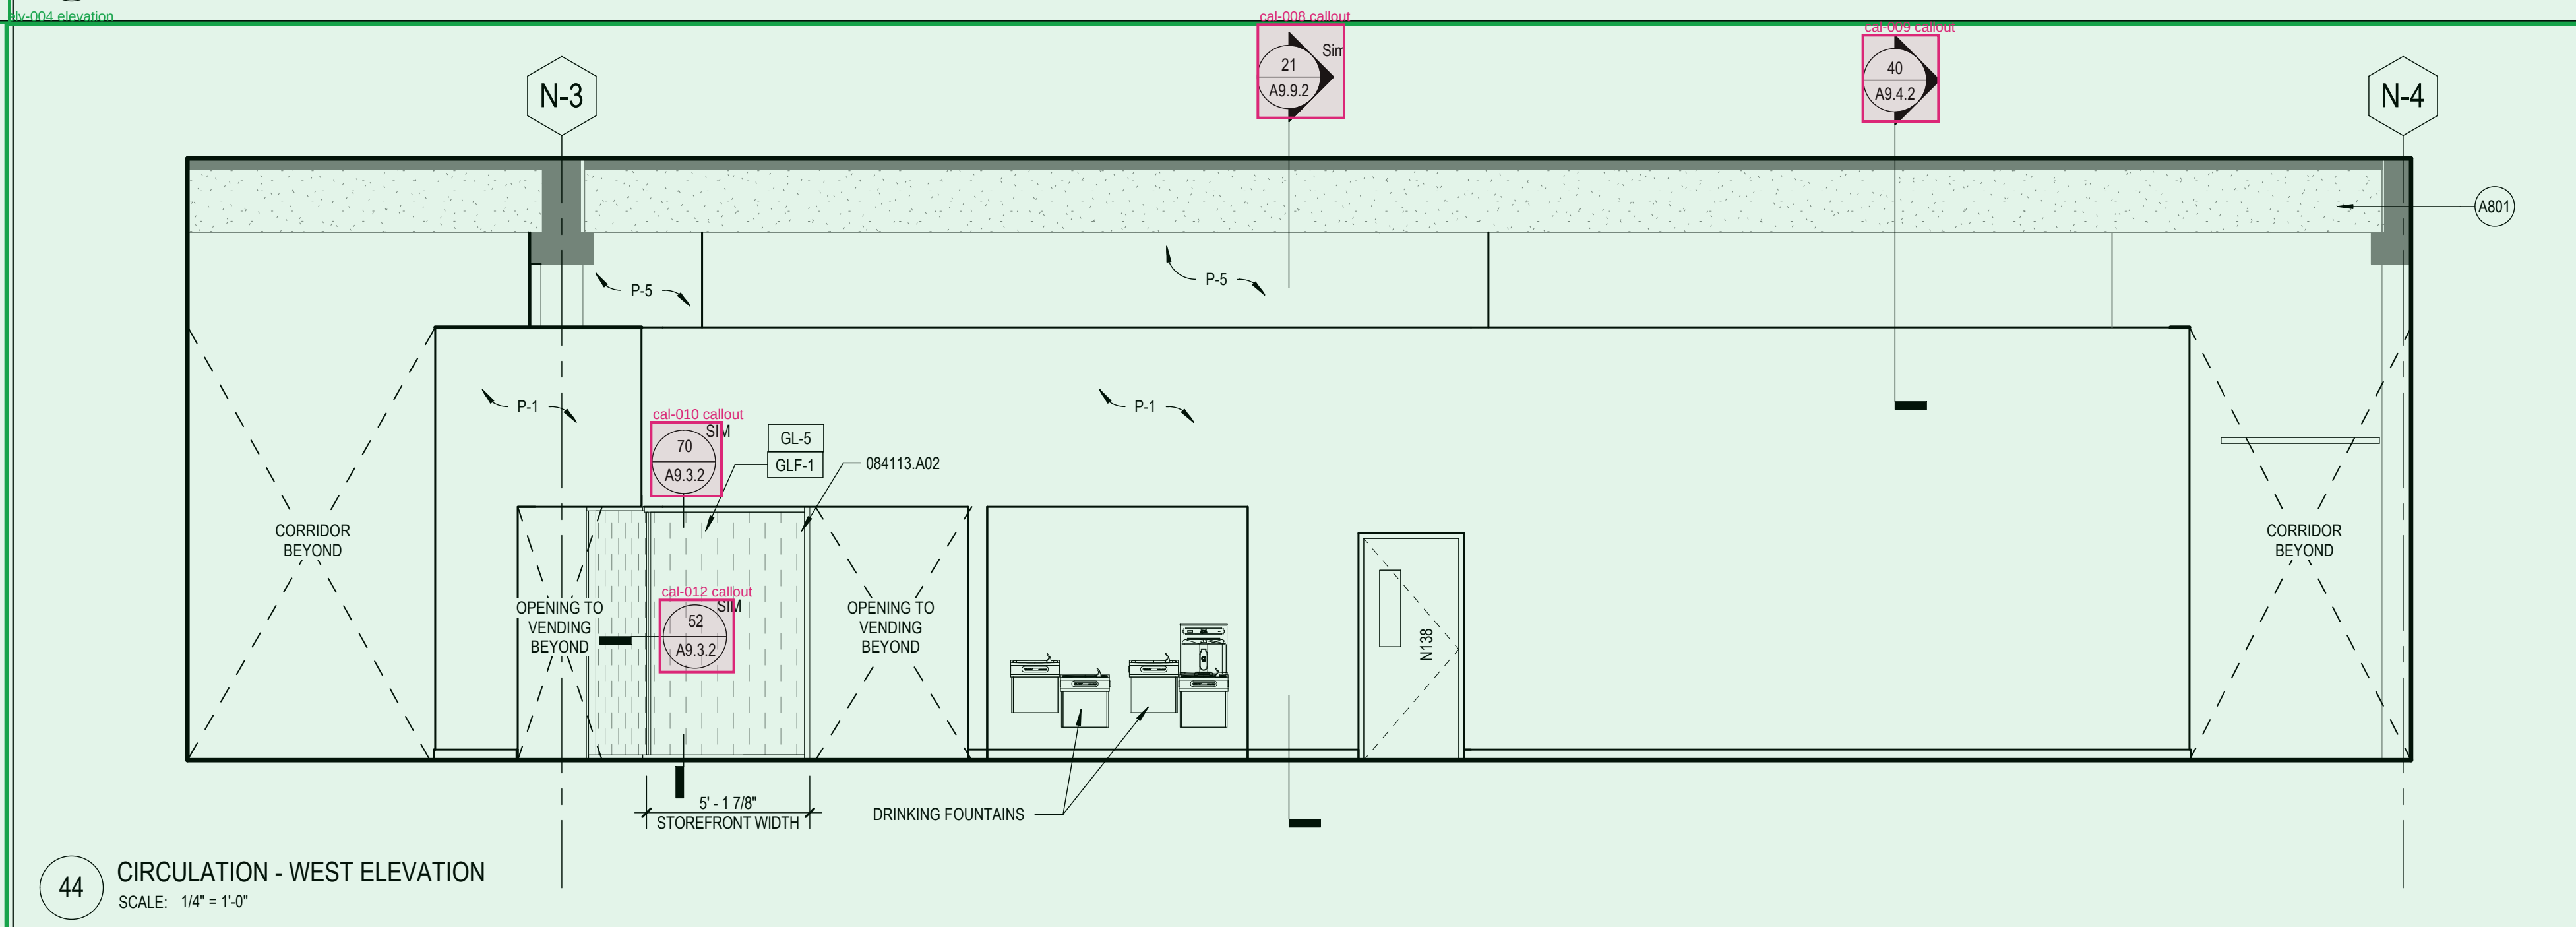

44 CIRCULATION - WEST ELEVATION
SCALE: 1/4" = 1'-0"

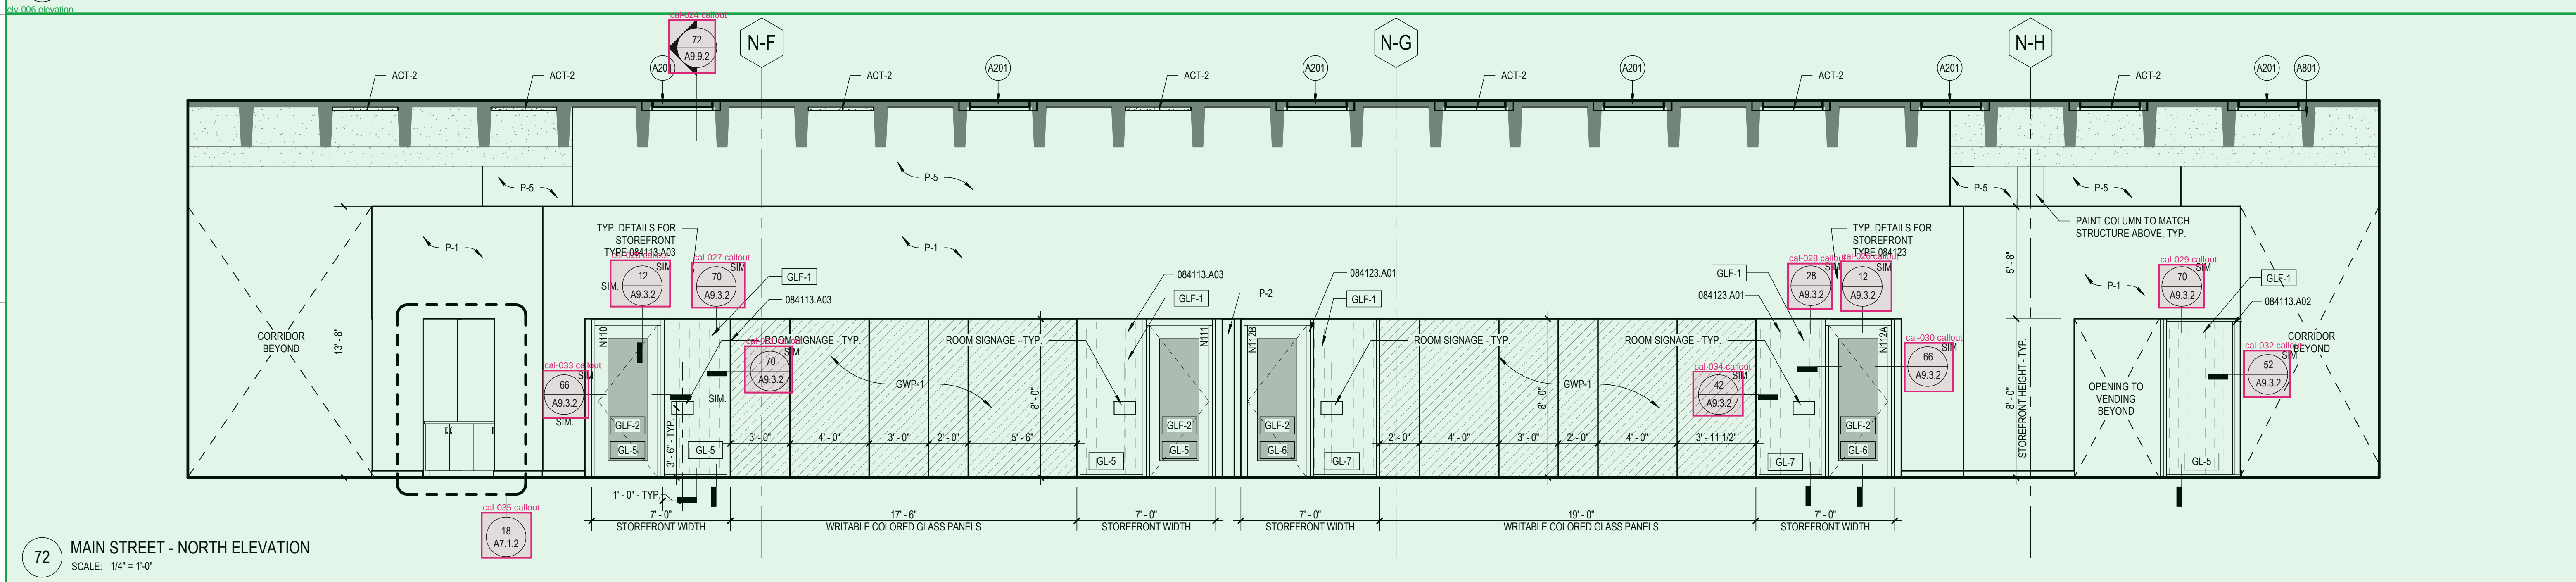

72 MAIN STREET - NORTH ELEVATION
SCALE: 1/4" = 1'-0"

3650 NORTH NEVADA AVE
COLORADO SPRINGS, CO, 80907

- A. REFER TO THE A.O.X SERIES SHEETS FOR ARCHITECTURAL GENERAL NOTES, DRAWING, REFERENCE AND MATERIAL SYMBOLS, ABBREVIATIONS, AS WELL AS DIMENSIONING CONVENTIONS USED ON THIS SHEET.
- B. REFER TO AND COORDINATE WITH MECHANICAL, PLUMBING AND ELECTRICAL FOR ADDITIONAL INFORMATION NOT SHOWN ON THIS SHEET.
- C. THE PURPOSE OF THE DRAWINGS ON THIS SHEET IS TO ILLUSTRATE THE OVERALL CONFIGURATION OF ALL ITEMS OF ALL TRADES OCCURRING ON THE INTERIOR ELEVATIONS. LOCATIONS OF ELEMENTS SHOWN ON ELECTRICAL, MECHANICAL, AND PLUMBING DRAWINGS ARE SCHEMATIC AND THE DIMENSIONS SHOWN HERE TAKE PRECEDENCE.
- D. REFER TO THE A.O.X SERIES SHEETS FOR TYPICAL MOUNTING HEIGHTS FOR DIMENSIONS NOT SHOWN ON THIS SHEET.
- E. REFER TO THE "AF" SERIES SHEETS FOR INTERIOR FINISH INFORMATION.
- F. SOLE PRODUCT OR MANUFACTURER/SOURCE: WHERE A SINGLE PRODUCT OR MANUFACTURER/SOURCE IS NAMED, IT IS SUBJECT TO CHANGE WITH REQUIREMENTS. COMPATIBLE PRODUCTS WILL BE CONSIDERED.

MARTIN/MARTIN, INC.
STRUCTURAL ENGINEER
12499 WEST COLFAX AVENUE
LAKEWOOD, CO, 80215
303-431-6100

05/04/2021

TYPES SHOWN ON ELEVATIONS, AND IN THE "GLASS TYPES" COLUMNS UNDER THE "OPENING" AND "FRAME" COLUMNS OF THE DOOR SCHEDULE.

SOLE PRODUCT OR MANUFACTURER/SOURCE: WHERE A SINGLE PRODUCT OR MANUFACTURER/SOURCE IS NAMED, SUBJECT TO COMPLIANCE WITH REQUIREMENTS, COMPARABLE PRODUCTS WILL BE CONSIDERED.



- | | |
|-----|--|
| GL1 | 1" INSULATED GLAZING UNIT - CLEAR TEMPERED LOW-IR LOCATION: INTERIOR GLAZING ENTRY VESTIBULE
BASIS OF DESIGN:
MANUFACTURER: VITRO
TYPE: SOLARBAN ACUTY |
| GL2 | TYPE: 1" INSULATED GLAZING UNIT - CLEAR LOW-IR LOCATION: EXTERIOR STOREFRONT
BASIS OF DESIGN:
MANUFACTURER: VITRO
TYPE: SOLARBAN 90 CLEAR |
| GL3 | 1" INSULATED GLAZING UNIT - CLEAR TEMPERED LOW-IR LOCATION: EXTERIOR STOREFRONT
BASIS OF DESIGN:
MANUFACTURER: VITRO
TYPE: SOLARBAN 90 CLEAR |
| GL4 | 1" INSULATED GLAZING UNIT - SPANDREL TEMPERED LOCATION: EXTERIOR STOREFRONT
BASIS OF DESIGN:
MANUFACTURER: VITRO
TYPE: SOLARBAN ACUTY
SPANDREL COLOR: #3-0770 WARM GRAY |
| GL5 | 3/8" CLEAR GLASS - TEMPERED
LOCATION: INTERIOR WINDOWS AND DOORS, UNRATED |
| GL6 | 5/16" FIRE-RATED GLASS
LOCATION: INTERIOR FIRE-RATED GLASS DOORS
RATING: 45-MIN |
| GL7 | 3/4" FIRE-RATED GLASS
LOCATION: INTERIOR FIRE-RATED WINDOWS
RATING: 45-MIN |

12654.00





three inches = one foot
one and one half inches = one foot
one inch = one foot
three quarters inch = one foot
one half inch = one foot
three eighths inch = one foot
one quarter inch = one foot
one eighth inch = one foot

FINISH SCHEDULE					FINISH SPECIFICATIONS				
NO.	ROOM	FLOORS		WALLS	WELDED SHEET VINYL		VINYL COMPOSITION TILE		PLASTIC LAMINATE
		WVS/VCT	P		WVS/VCT	P	WVS/VCT	P	
100	WAITING	1	1	1	1	1	1	1	1
101	DRESS	1	1	1	1	1	1	1	1
102	ADA DRESS	1	1	1	1	1	1	1	1
103	CLEAN	1	1	1	1	1	1	1	1
104	SOILED	1	1	1	1	1	1	1	1
105	CONTROL ROOM	1	1	1	1	1	1	1	1
106	SUB-WAITING	1	1	1	1	1	1	1	1
107	MRI SCAN ROOM	1	1	1	1	1	1	1	1
108	EQUIP. ROOM	1	1	1	1	1	1	1	1
109	CL	1	1	1	1	1	1	1	1
110	CL	1	1	1	1	1	1	1	1






WELDED SHEET VINYL		VINYL COMPOSITION TILE		PLASTIC LAMINATE	
WVS-1	MANF: JONHONSON COLOR: WALNUT STREET W/ INTERGLAZE BASE	VCT-1	MANF: JONHONSON COLOR: LUNAR BLUE 51932	PL-1	MANF: WILSONART COLOR: ASIAN SAND - 752K-18
WVS-2	MANF: JONHONSON COLOR: LUNAR BLUE 51932	VCT-2	MANF: JONHONSON COLOR: LUNAR BLUE 51932	PL-2	MANF: WILSONART COLOR: PASADENA OAK - 785K-38
VINYL WALL BASE		CEILING GRID		WOOD DOORS	
VB-1	MANF: JONHONSON PRODUCT: 4" COVE BASE COLOR: WINDSOR BLUE 518	CG-1	2X2 - MATCH CT ROOM	WD-1	CLEAR RED OAK
PAINT		WALL PROTECTION		WOOD PROTECTION	
P-1	MANF: SHERWIN WILLIAMS PRODUCT: EGG SHELL COLOR: SAND DUNE 59966	WP-1	MANF: JONHONSON PRODUCT: 4" CORNER GUARDS COLOR: PONT BLUE 018 LOCATION: OUTSIDE CORNERS	WP-1	MANF: JONHONSON PRODUCT: 4" CORNER GUARDS COLOR: PONT BLUE 018 LOCATION: OUTSIDE CORNERS
P-2	MANF: SHERWIN WILLIAMS PRODUCT: SEMI-GLOSS COLOR: SAND DUNE 59966	WP-2	MANF: JONHONSON PRODUCT: 4" CORNER GUARDS COLOR: PONT BLUE 018 LOCATION: OUTSIDE CORNERS	WP-2	MANF: JONHONSON PRODUCT: 4" CORNER GUARDS COLOR: PONT BLUE 018 LOCATION: OUTSIDE CORNERS
SOLID SURFACE		WOOD DOORS		WOOD PROTECTION	
SS-1	MANF: CORIAN COLOR: PLATINUM	WD-1	CLEAR RED OAK	WP-1	MANF: JONHONSON PRODUCT: 4" CORNER GUARDS COLOR: PONT BLUE 018 LOCATION: OUTSIDE CORNERS

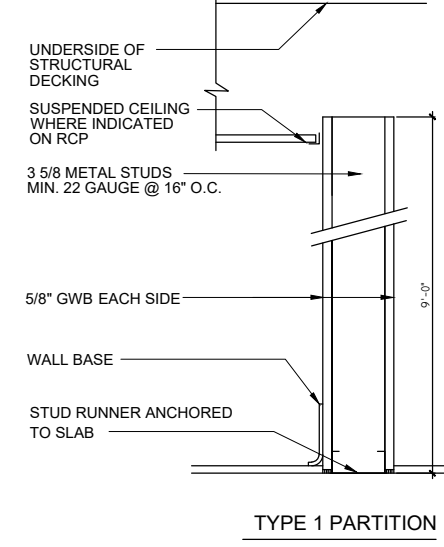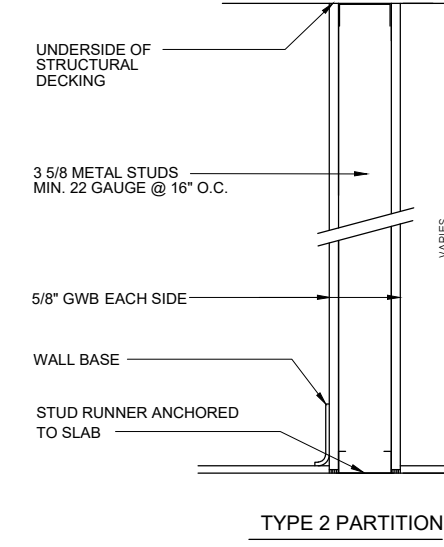PARTITION TYPES	
	
	
ALL NEW WALLS PARTITION TYPE #1 UNLESS OTHER WISE NOTED	



INTERIOR DOOR SCHEDULE						
NO.	LOCATION	TYPE	DESCRIPTION	SIZE	FINISH	HARDWARE
1	WAITING - 100	4	HINGED DOUBLE	6'-0" x 7'-0" x 1 3/4"	STAINED	1
2	DRESS - 101	1	HINGED SINGLE	3'-0" x 7'-0" x 1 3/4"	STAINED	3
3	DRESS - 102	1	HINGED SINGLE	3'-0" x 7'-0" x 1 3/4"	STAINED	3
4	CLEAN - 103	3	HINGED DOUBLE	3'-0" x 7'-0" x 1 3/4"	STAINED	4
5	SOILED - 104	3	HINGED DOUBLE	3'-0" x 7'-0" x 1 3/4"	STAINED	4
6	WAITING - 100	1	HINGED DOUBLE	3'-0" x 7'-0" x 1 3/4"	STAINED	1
7	CL - 109	3	HINGED DOUBLE	3'-0" x 7'-0" x 1 3/4"	STAINED	5
8	CONTROL ROOM - 105	1	HINGED SINGLE	3'-0" x 7'-0" x 1 3/4"	STAINED	6
9	CONTROL ROOM - 105	1	HINGED SINGLE	3'-0" x 7'-0" x 1 3/4"	STAINED	2
10	MRI SCAN ROOM - 107	2	HINGED SINGLE	4'-0" x 7'-0" x 1 3/4"	PL-2	2
11	EQUIP. ROOM - 108	1	HINGED SINGLE	3'-0" x 7'-0" x 1 3/4"	STAINED	1
12	CL - 110	3	HINGED DOUBLE	3'-0" x 7'-0" x 1 3/4"	STAINED	5

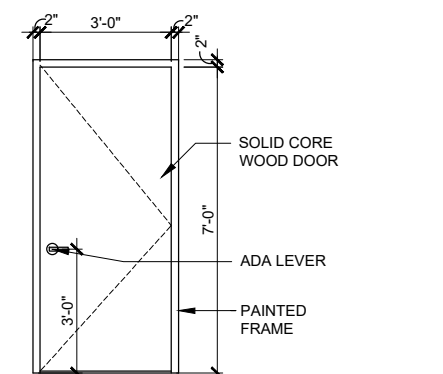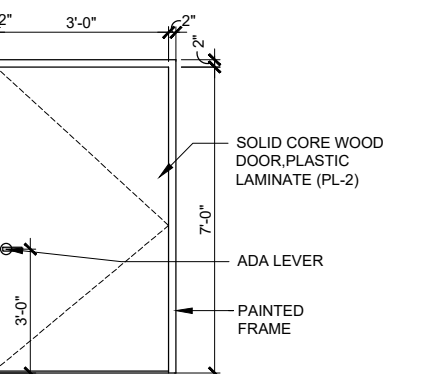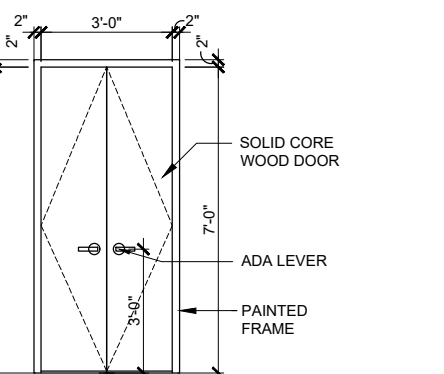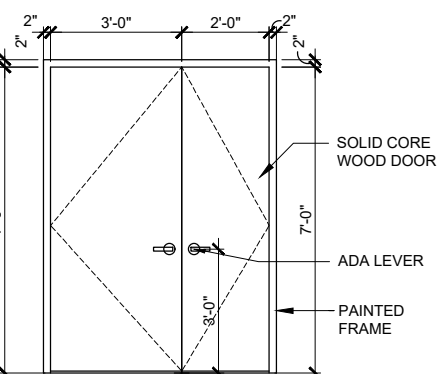
INTERIOR DOOR TYPES	
	

HARDWARE SPECIFICATIONS		HARDWARE SCHEDULE	
BUTT HINGES STANLEY FBB199 4 1/2" x 4 1/2" (A) INTERIOR DOORS USED (B) EXTERIOR DOORS WHICH ARE DEFINED AS DOORS EXPOSED TO THE ELEMENTS SHALL BE US32D.		HW SET #1 3 PAIR 1 1 2 1	
LOCKSETS AND LATCHSETS YALE CAMEL - CRI LEVER HARDWARE - COORDINATE FINISH WITH BUILDING MANAGEMENT		BUTT HINGES LATCHSET DUMMY LEVER SET CLOSERS FLUSH BOLT	
STOPS STOPS #436 AND #407 AS MANUFACTURED BY IVES OR APPROVED EQUAL. PROVIDE ONE FOR EACH INTERIOR DOOR.		HW SET #2 - 1 1	
MISCELLANEOUS ITEMS (1) SILENCERS OLIVIA-JOHNSON QJ84 THREE PAIRS PER EACH SINGLE DOOR, TWO EACH PER PAIR OF DOORS SHALL BE FURNISHED.		HW SET #3 1 1/2 PAIR 1 1	
NOTES: 1. ALL DOORS MUST OPEN TO A FULL 90 DEGREES UNLESS OTHERWISE NOTED. 2. ALL HARDWARE TO BE ADA COMPLIANT. 3. OWNER TO SELECTION FINISHES.		HW SET #4 1 1/2 PAIR 1 1	
		HW SET #5 3 1/2 PAIR 2 2	

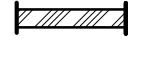 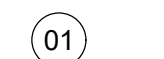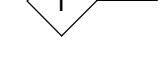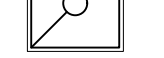
PLAN/CEILING SYMBOLS	
D - DEMOLISH E - EXISTING R - RELOCATED N - NEW	
	WALL TO BE REMOVED
	EXIST WALL, TO REMAIN
	NEW WALL
	SHIELDING WALL
	DOOR NUMBER
	PARTITION TYPE
	2' X 2' LAY-IN FIXTURE

DESIGN/BUILDER:		ARCHITECT/ENGINEERS:	
Deerfield Construction Group 610 Professional Drive, Suite 210 Gaithersburg, Maryland 20879 (301)947-4701		Nicholas Lucarelli Architects, LLC 6723 Whittier Avenue Suite 414 Mclean, VA 22101 Tel: (703) 790-9606	
D2 Engineering, LLC 18310 Montgomery Village Ave Suite 520 Gaithersburg, MD 20879 Tel: (301) 208-9575 Fax: (301) 208-9405		PROPERTY OF THE UNITED STATES GOVERNMENT FOR OFFICIAL USE ONLY DO NOT REMOVE THIS NOTICE. PROPERLY DESTROY DOCUMENTS WHEN NO LONGER NEEDED.	
For review and approval Revisions:		Date	

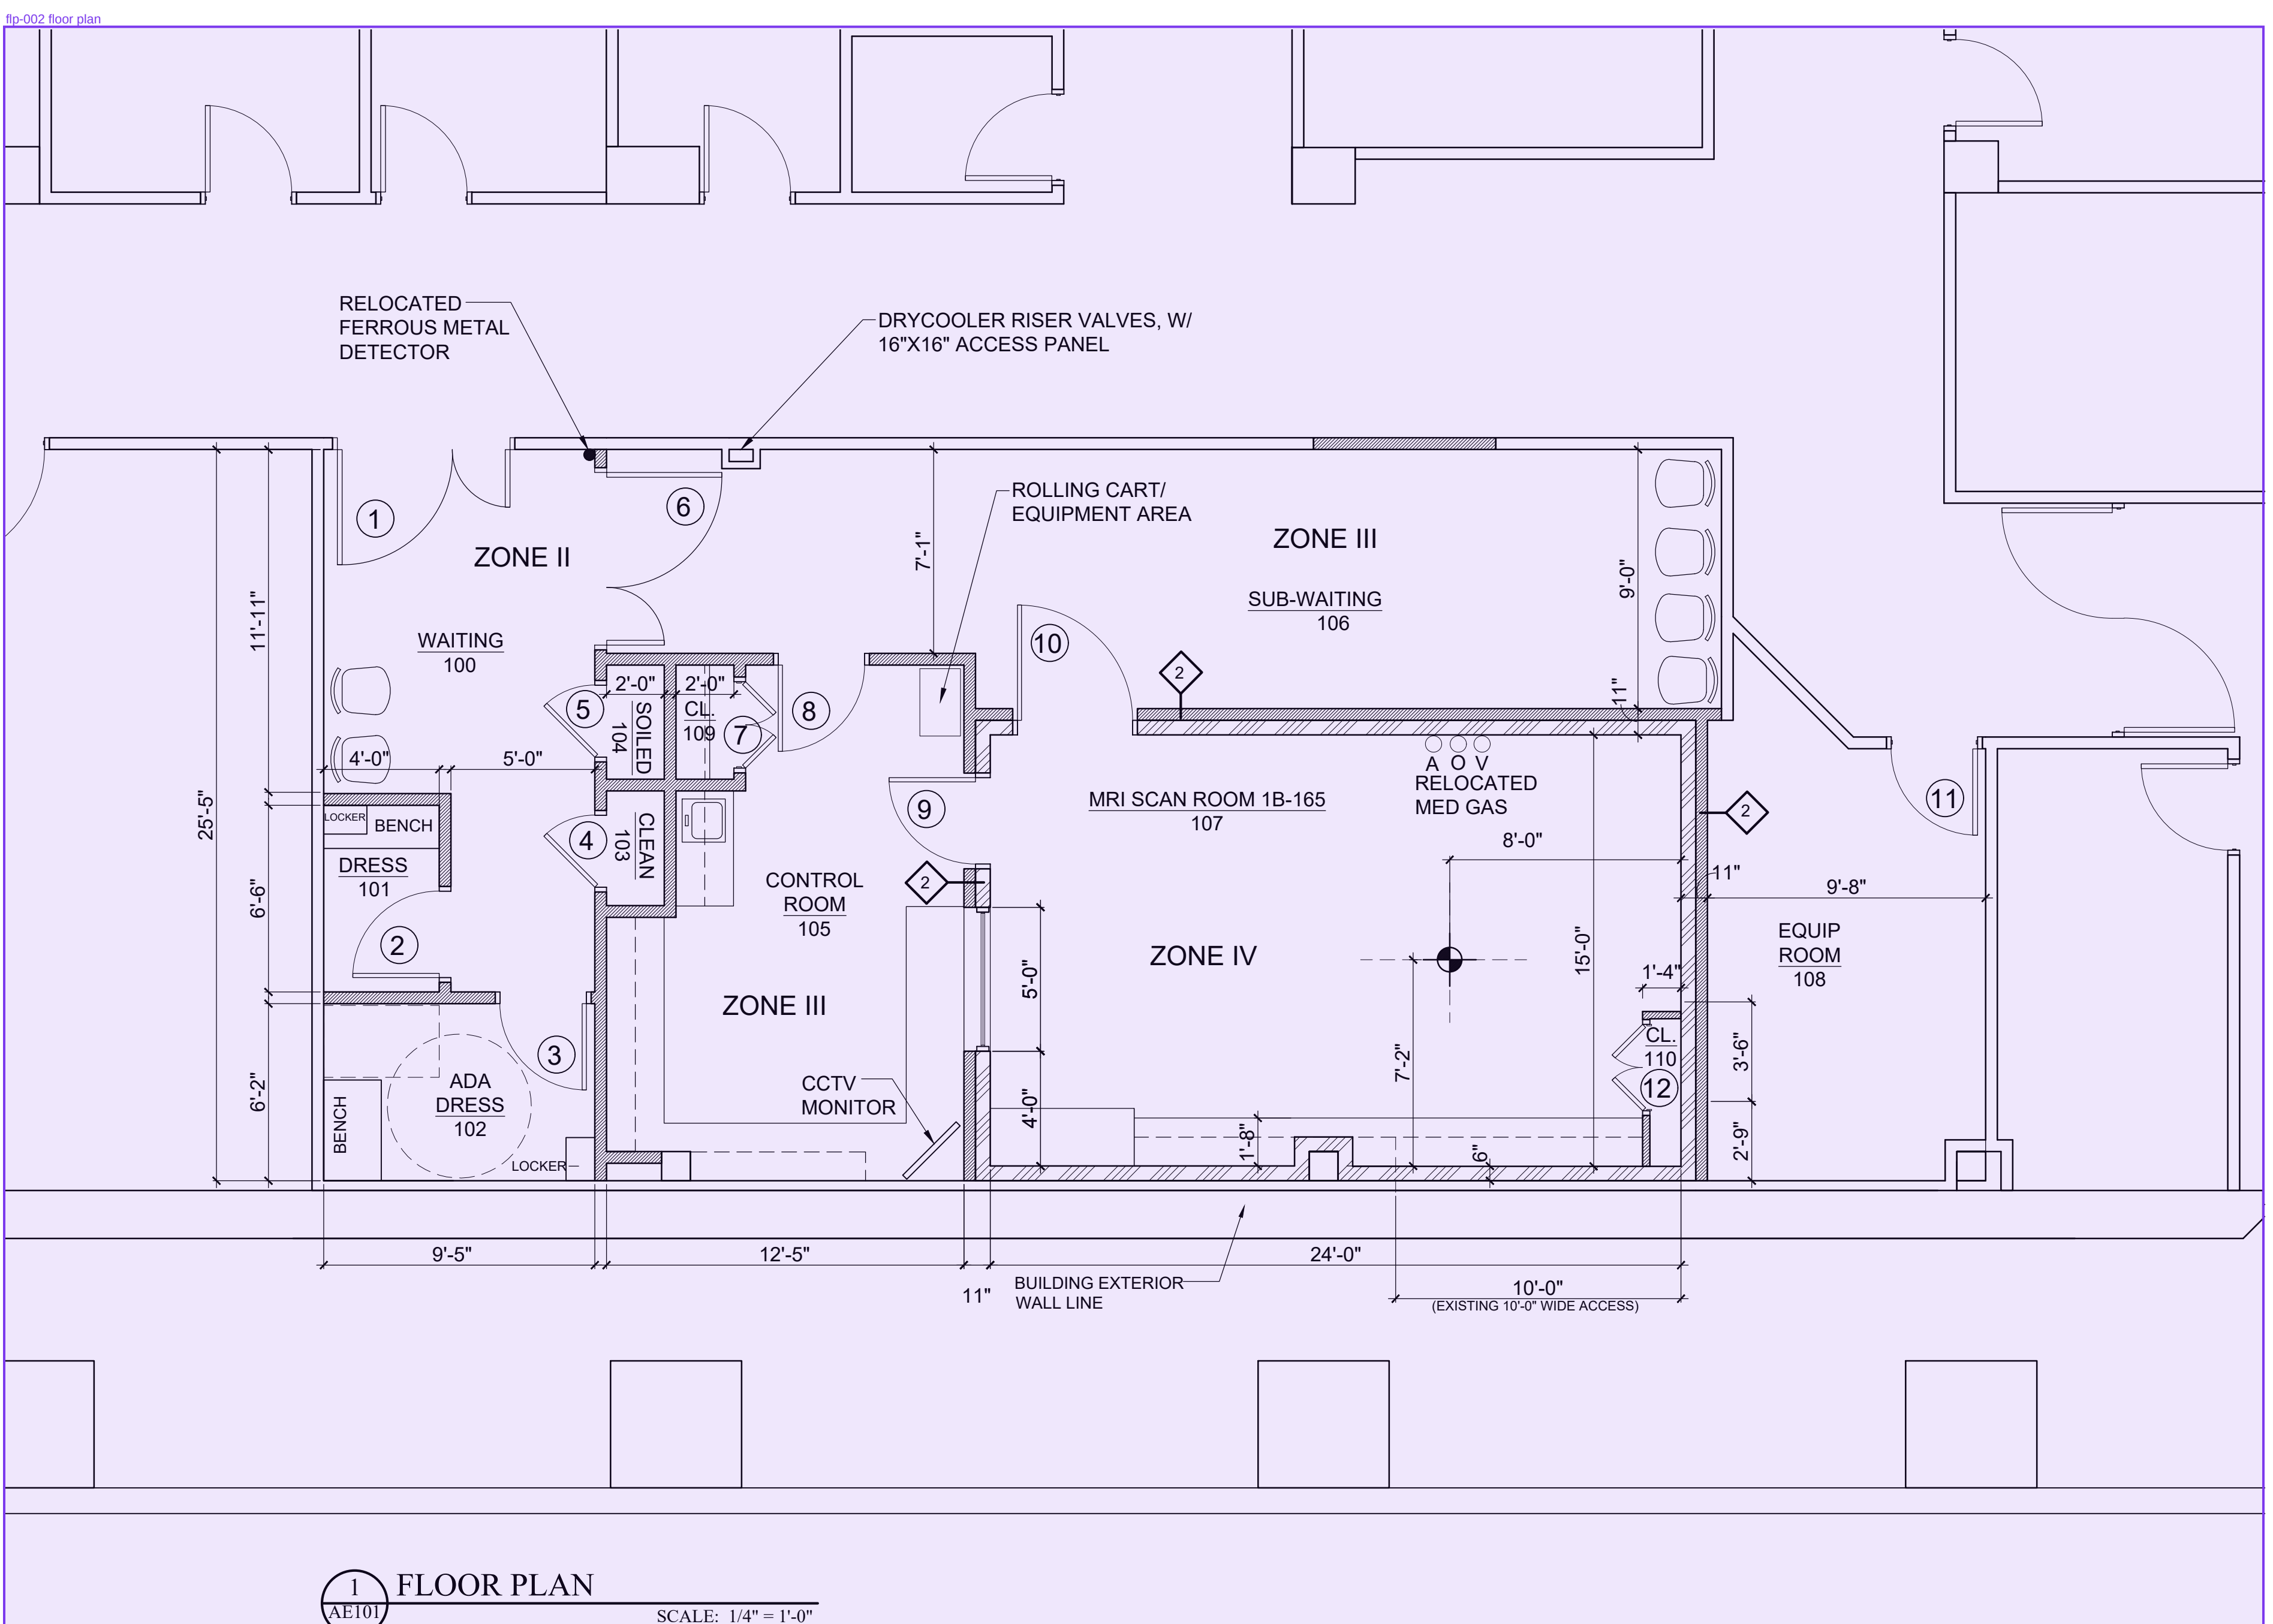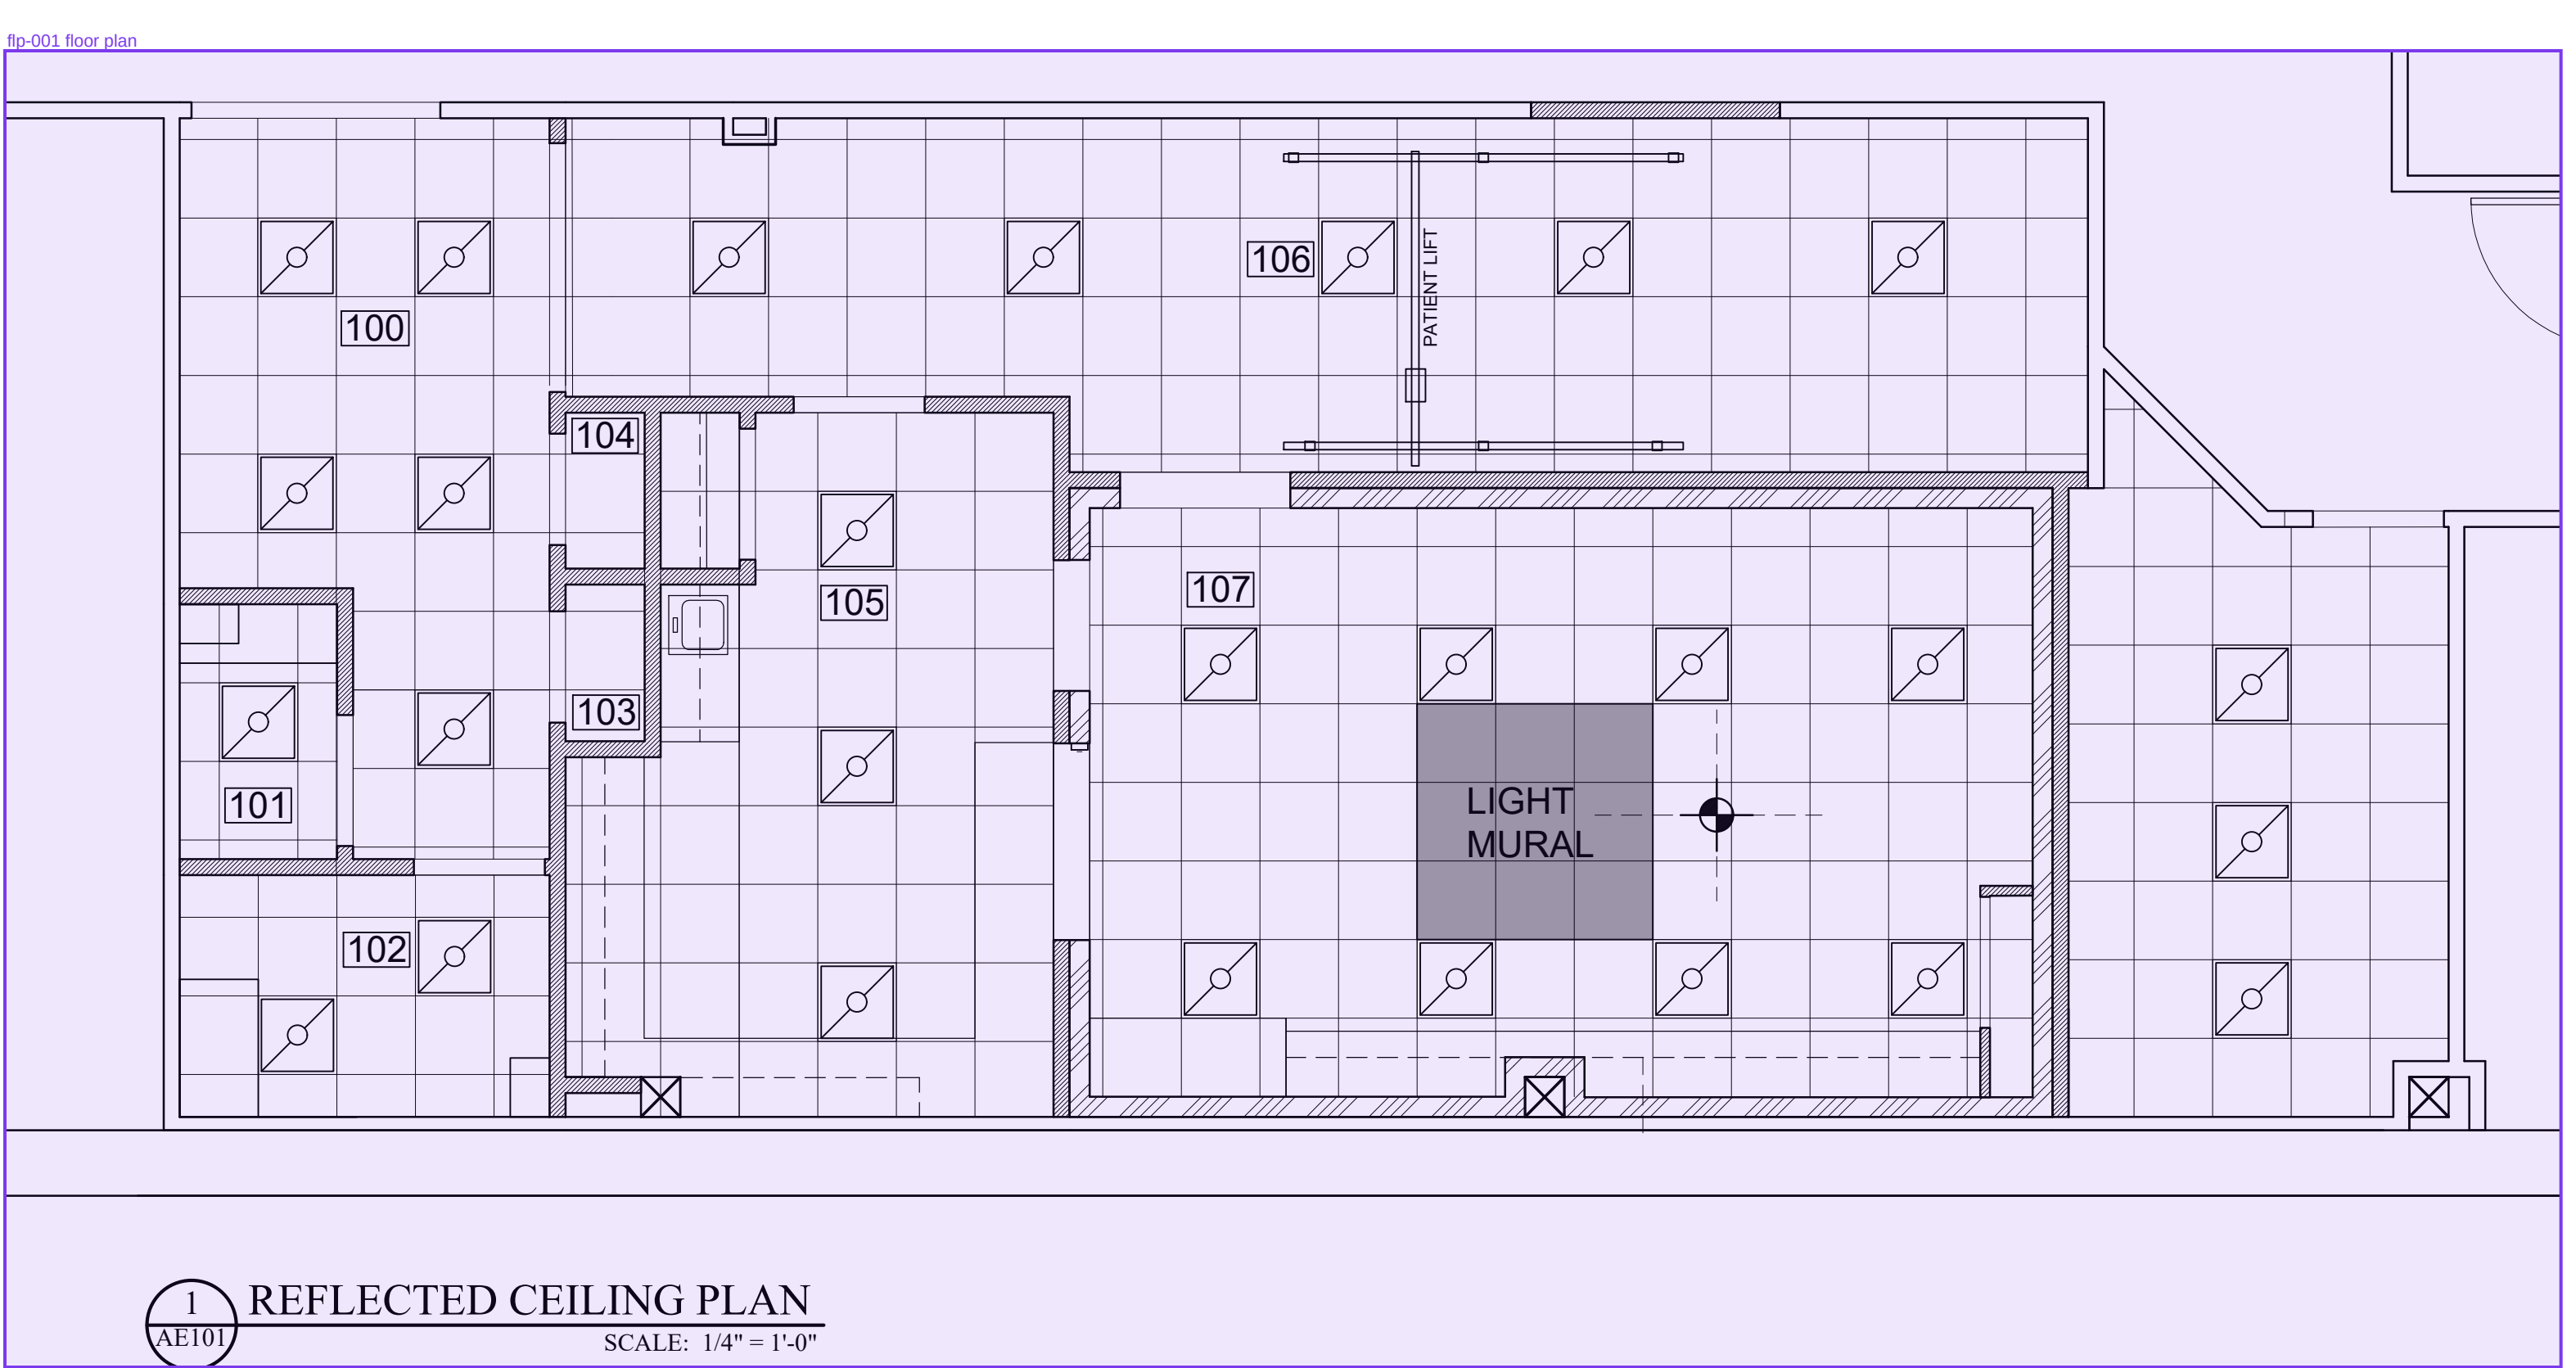

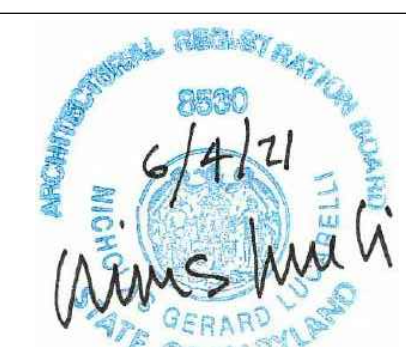DESIGN/BUILDER:		ARCHITECT/ENGINEERS:		Stamp/Seal	Drawing Title	Project Title	Project Number
Deerfield Construction Group 610 Professional Drive, Suite 210 Gaithersburg, Maryland 20879 (301)947-4701		Nicholas Lucarelli Architects, LLC 6723 Whittier Avenue Suite 414 Mclean, VA 22101 Tel: (703) 790-9606			FLOOR PLAN, REFLECTED CEILING PLAN & SCHEDULES	VA BALTIMORE MEDICAL CENTER ROOM 1B-165	PROJECT #
For review and approval Revisions:		Date		Approved: Project Director		Location 10 NORTH GREENE STREET, BALTIMORE, MD 21201	Building Number
						Date 6.2.2021	Checked
						Drawn	AE101

flp-003 floor plan

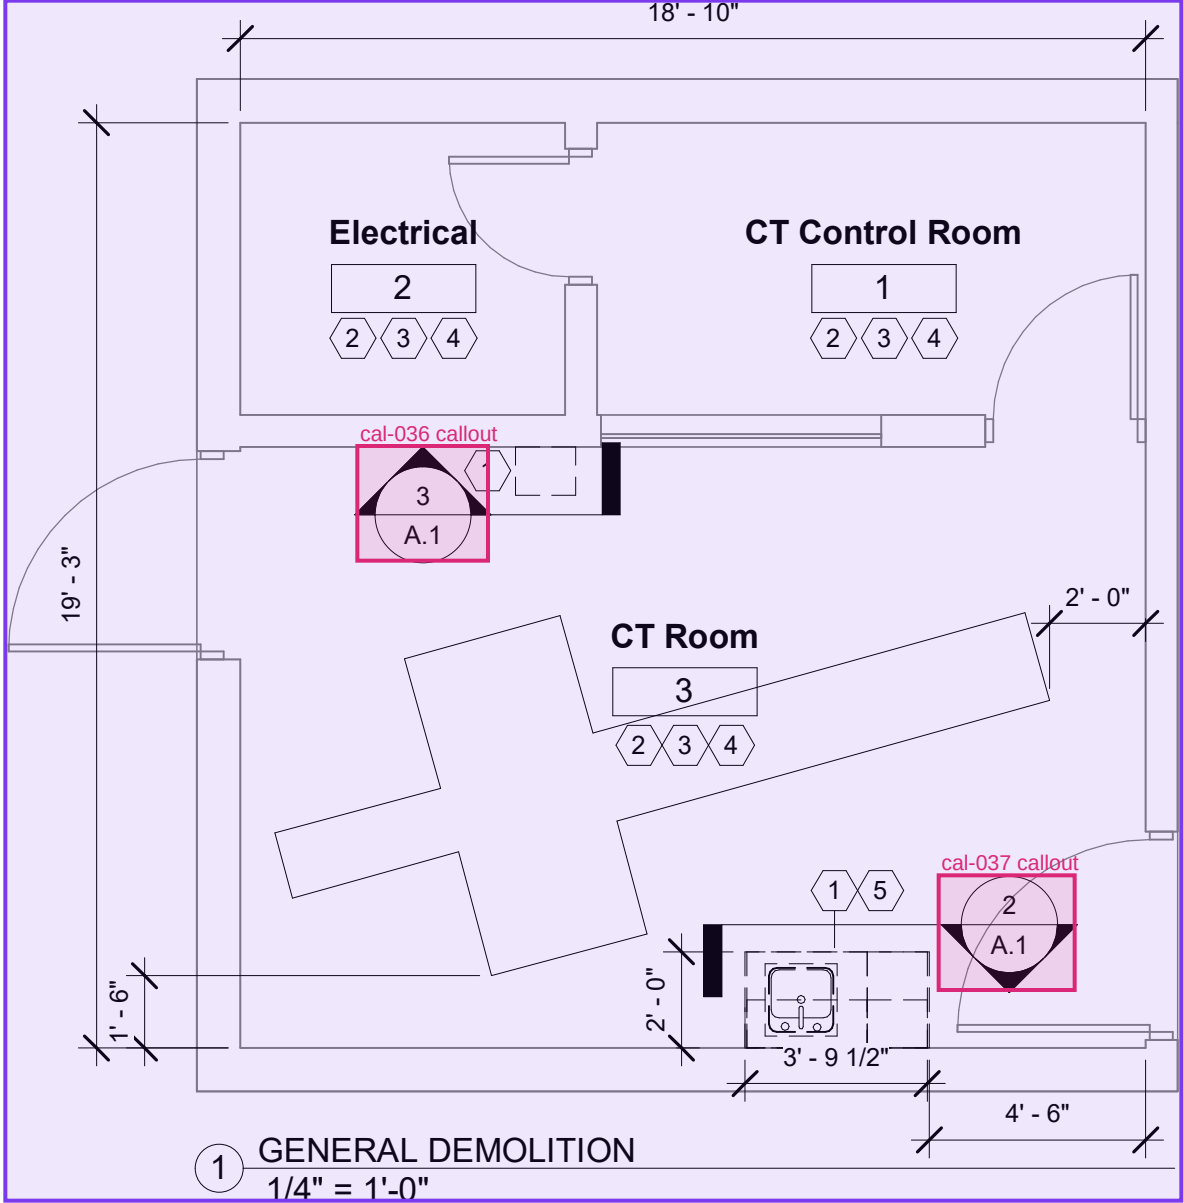


MASTER KEYNOTE

Note Number	Note Content
1	Demolition Existing Cabinets as Per Base Bid
2	Demolish Existing VCT Flooring & Rubber Wall Base
3	Demolish Existing 2'x4' Ceiling Tile
4	Demolish Existing Ceiling Grid
5	Demolish Existing PVC Sewer Line 1' Below Floor & Cap. Demolish Water Line & Cap Above Ceiling Grid.


General Notes:

1. The contractor shall demolish throughout the following: flooring, ceiling tile, and ceiling grid. See SOW

elv-007 elevation

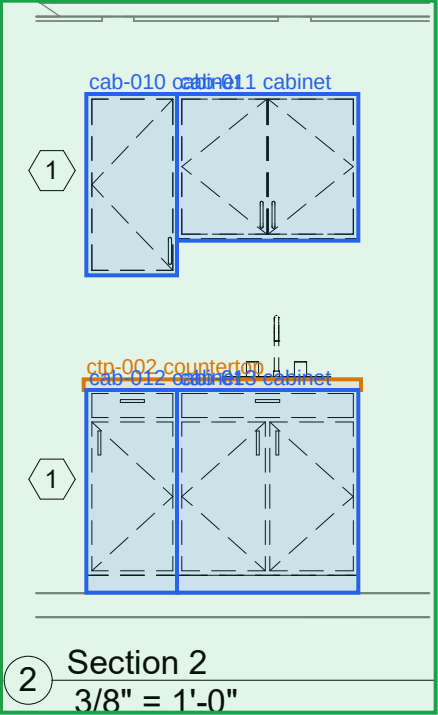

elv-008 elevation

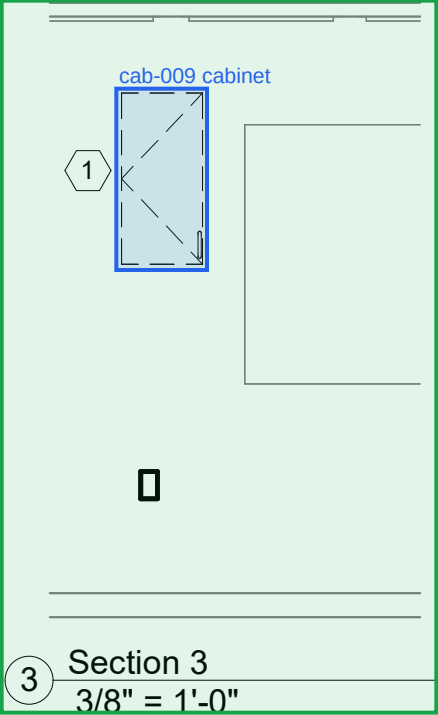

GREAT PLAINS AREA INDIAN HEALTH SERVICE
OFFICE OF ENVIRONMENTAL
HEALTH & ENGINEERING

DIVISION OF FACILITIES MANAGEMENT
115 4TH AVENUE SE, RM 309
ABERDEEN, SD 57401
(605) 226-7451 FAX (605) 226-7580

www.ihs.gov



Quentin N. Burdick
Memorial Health Facility

Replace RTU &
Cabinetry - CT Area

CONTRACT NO:	
TASK ORDER NO:	
PROJECT NUMBER:	GP22TM300H10
DATE:	08/26/2025
DRAWN BY:	Taylor Strand
CHECKED BY:	Brad Weekley
LAST REVISION DATE:	

GENERAL DEMOLITION

A.1

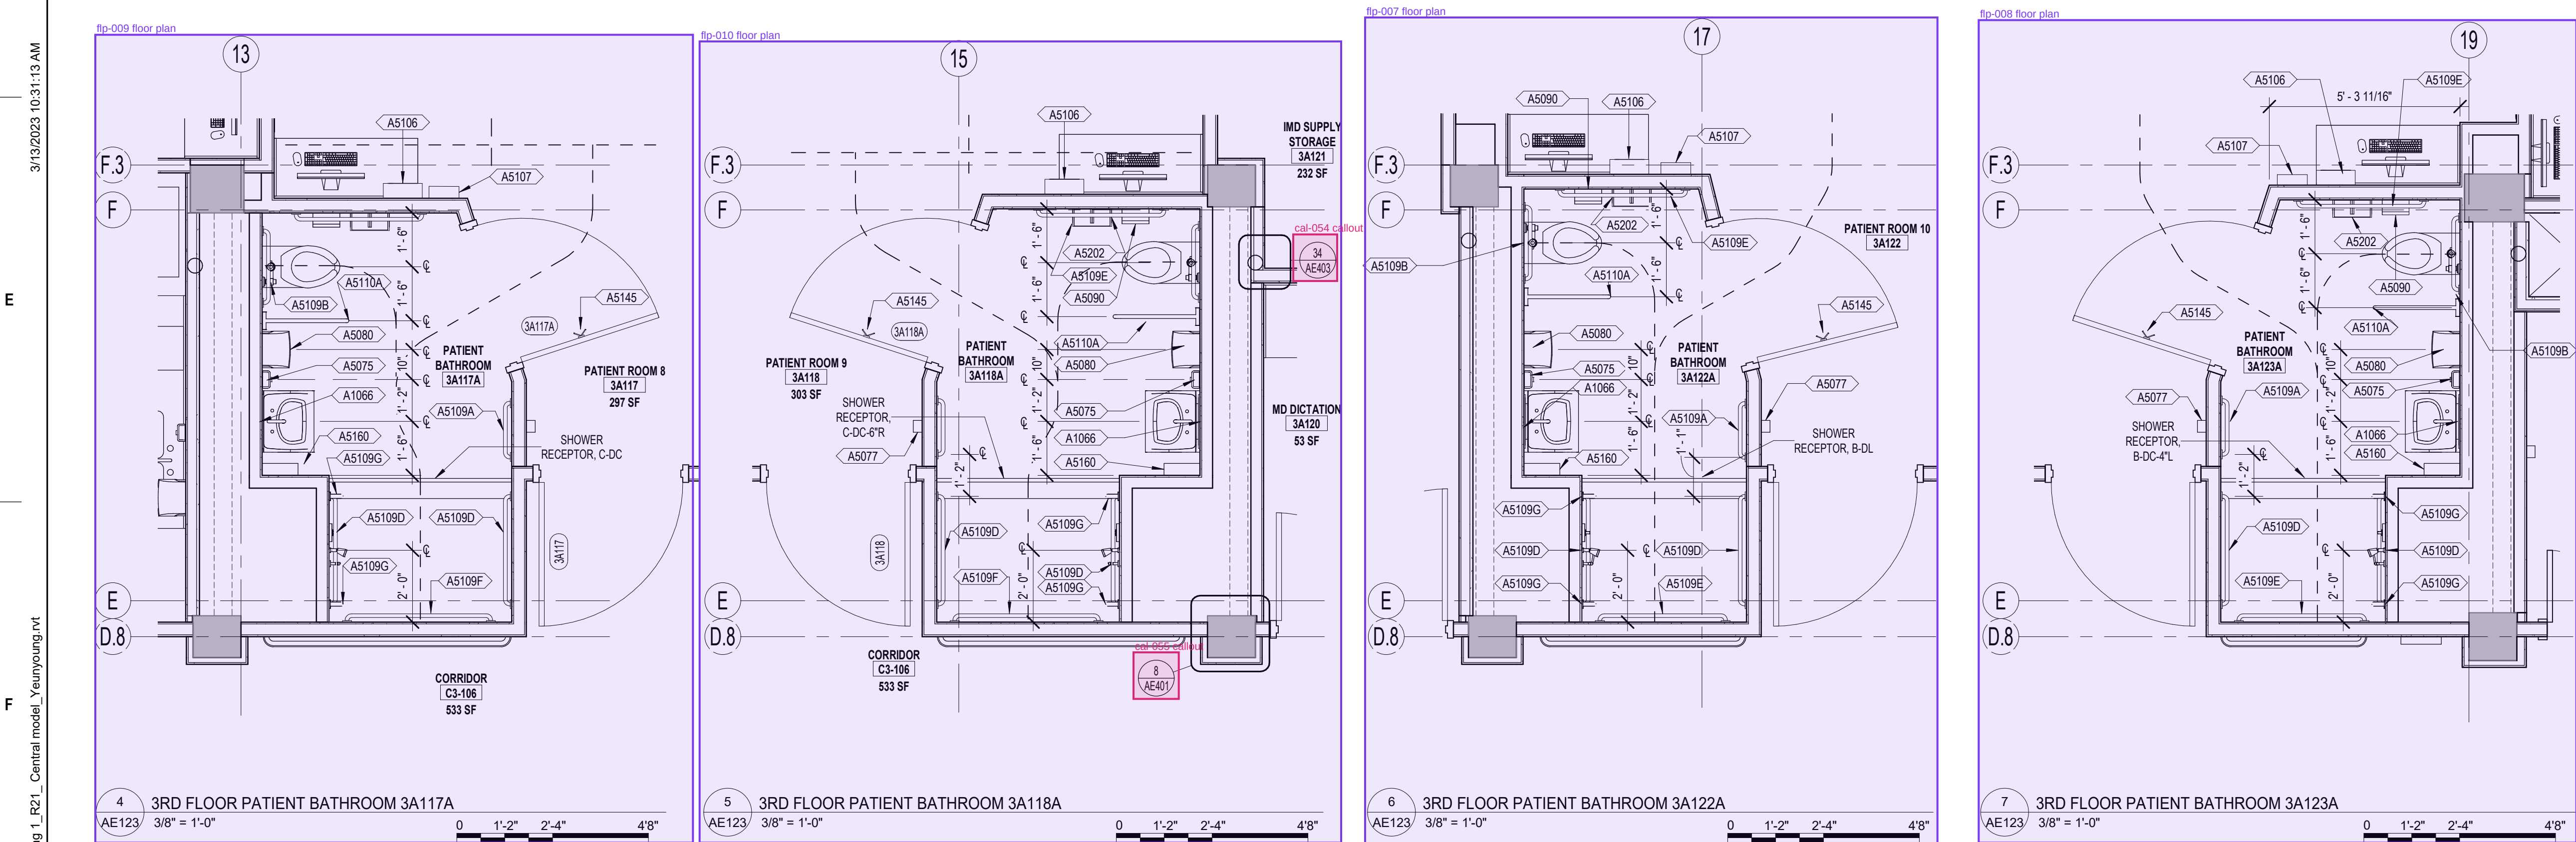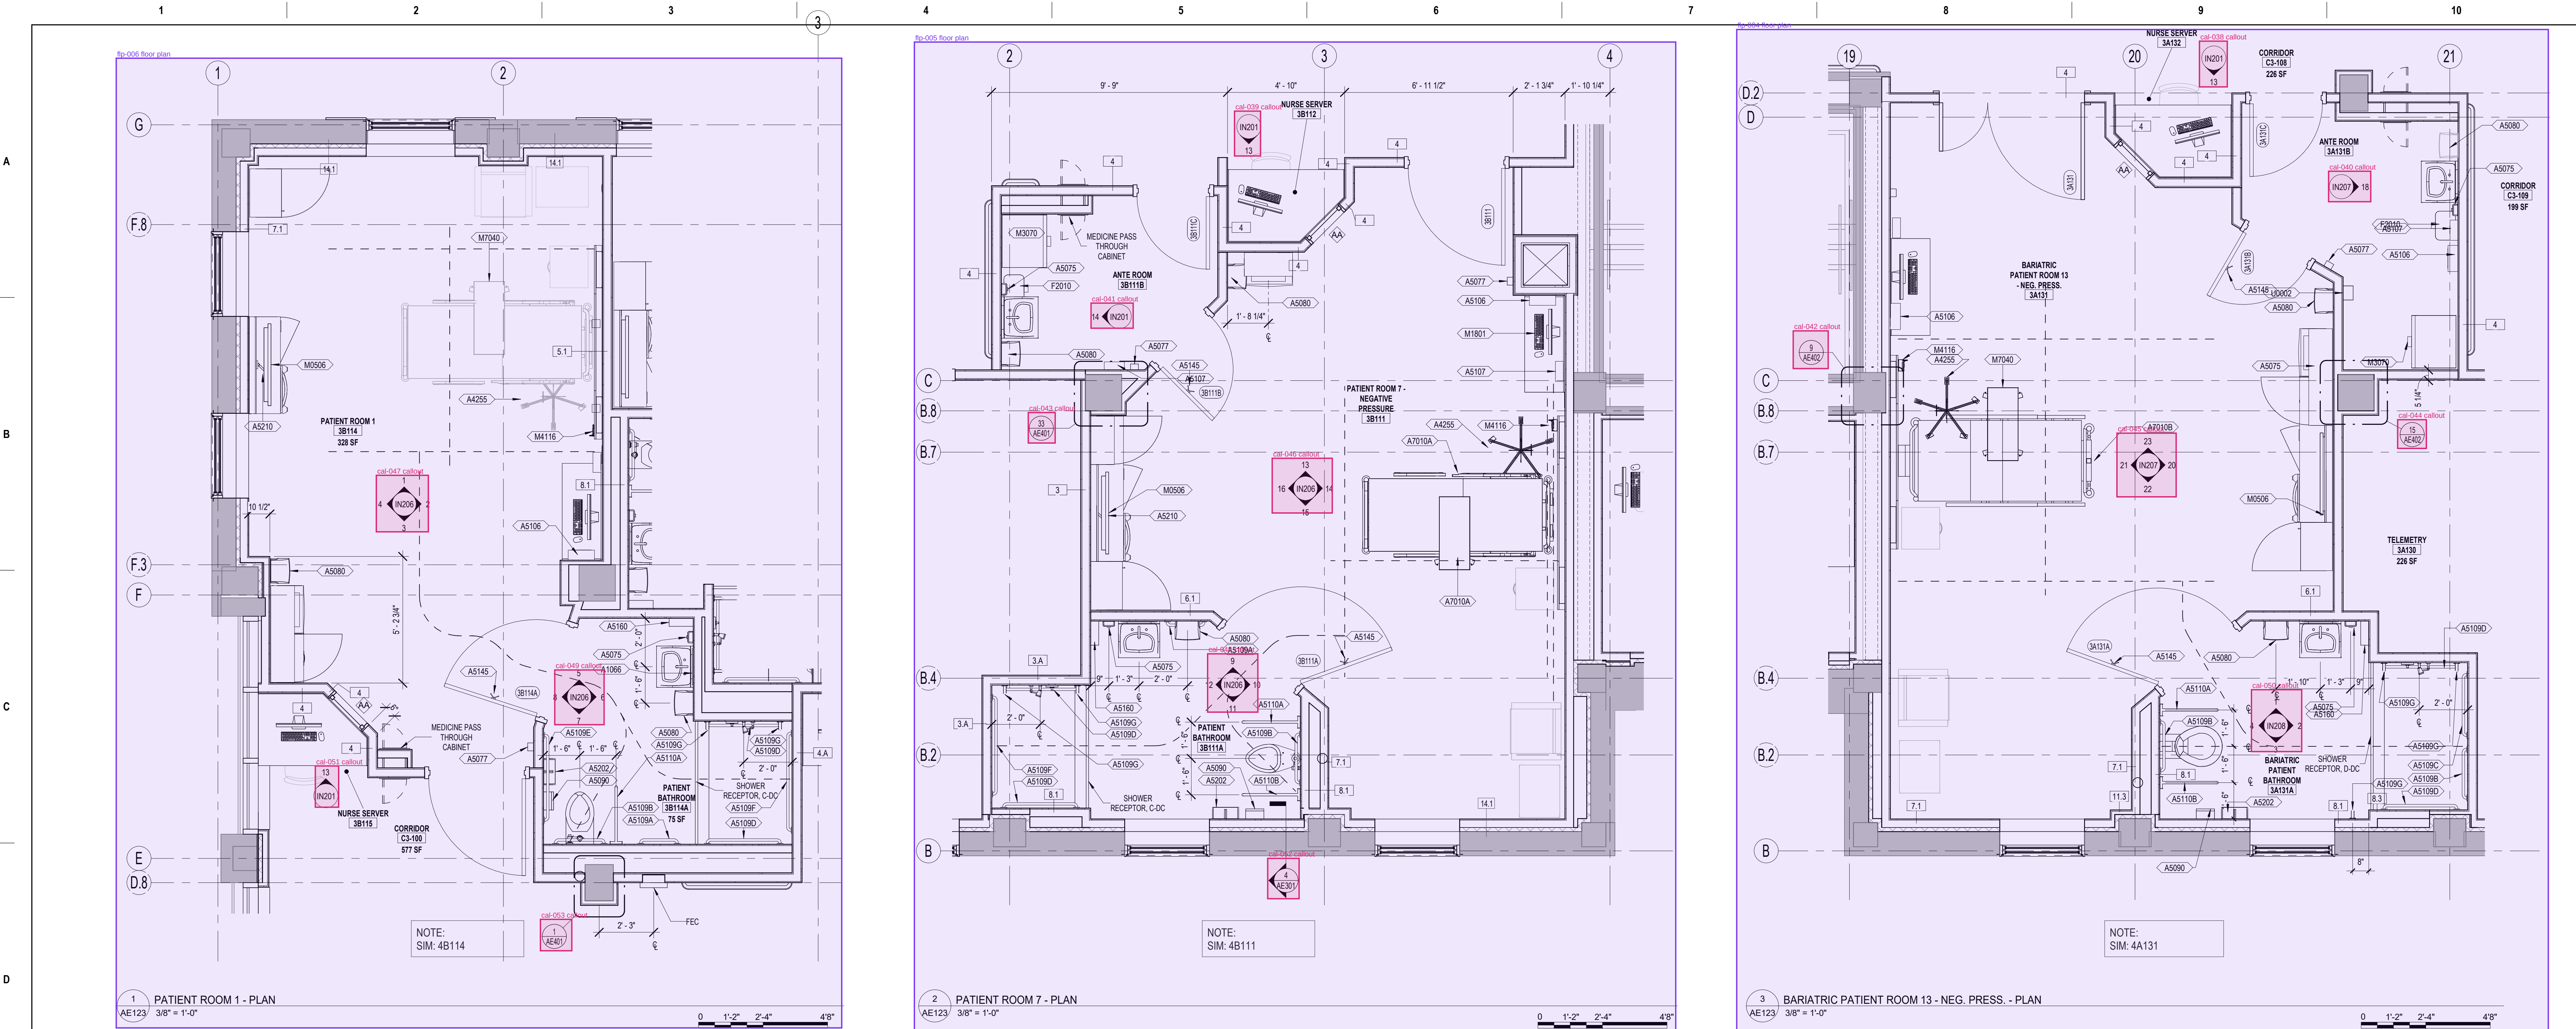

EQUIPMENT SCHEDULE - SHEET AE123		
JSN	DESCRIPTION	ACTIVATED BY
A1066	MIRROR, FLOAT GLASS, WITH SS FRAME, 18 X 36	CC
A5075	DISPENSER, HAND SOAP	VV
A5077	HAND SANITIZER DISPENSER	VV
A5080	DISPENSER, PAPER TOWEL	VV
A5090	SANITARY NAPKIN DISPOSAL	VV
A5106	WASTE DISPOSAL UNIT, SHARPS	VV
A5107	GLOVE DISPENSER RACK	VV
A5109A	GRAB BAR, SS, 18"	CC
A5109B	GRAB BAR, 1 1/4" DIA, SS, 24"	CC
A5109D	GRAB BAR, 1 1/4" DIA, SS, 36"	CC
A5109E	HORIZONTAL GRAB BAR, 42"	CC
A5109F	HORIZONTAL GRAB BAR, 48"	CC
A5109G	VERTICAL GRAB BAR, 1 1/4" DIA, SS, 18"	CC
A5110A	SWING UP GRAB BAR	CC
A5110B	SWING UP GRAB BAR W/TOILET PAPER DISPENSER	CC
A5145	HOOK, GARMENT, DOUBLE, SS, SURFACE MOUNTED	CC
A5160	STAINLESS STEEL SHELF - 12" x 4"	CC
A5202	TOILET PAPER DISPENSER	VV
A7010A	BED, PATIENT, ELECTRONIC	VV
M0506	TV, FLAT SCREEN, 43"	VV
M1801	COMPUTER AND MONITOR	VV
M4116	VITAL SIGNS MONITOR (WELSH ALLYN CVSM)	VV
U0002	PDI WIPE DISPENSER	VV

RESTROOM ACCESSORY NOTES	
1. SEE SHEET G101 FOR SHOWER RECEPTOR TYPES.	
2. MOUNT WASTE RECEPTACLE TO MEET ABAS. MOUNT HIGHEST OPERABLE PART OF CONTROLS, DISPENSERS, RECEPTACLES AND OTHER OPERABLE EQUIPMENT BETWEEN 15" - 48" ABOVE FINISH FLOOR.	
3. ATTACH MIRROR PER MANUFACTURER STANDARD, CENTER MIRROR ON LAVATORY(S) BELOW.	
4. ROBE HOOKS (A5145) TO BE MOUNTED ON TOILET SIDE OF DOOR, 48" FROM ABOVE FINISH FLOOR TO CENTER.	
5. FIELD VERIFY MOUNTING HEIGHTS WITH RESIDENT ENGINEER BEFORE INSTALLATION.	
6. PROVIDE & INSTALL PRE-JOINED (PLASTIC COVER) INSULATION FOR ALL EXPOSED PIPING, MEETING ALL APPLICABLE ABA REQUIREMENTS.	

RESTROOM ACCESSORY GENERAL NOTES	
A. MOUNTING HEIGHTS REFERENCED ON SHEET G101. VERIFY ALL MOUNTING HEIGHTS WITH CODES AND MANUFACTURER RECOMMENDATIONS.	
B. ABA TOILET PARTITION DOOR MUST BE 34" MINIMUM CLEAR OPENING.	
C. WHERE DIMENSIONS ARE INDICATED ON PLAN AS "CLEAR", THE DIMENSIONS ARE TAKEN FROM FACE OF FINISHED WALL MATERIAL TO FACE OF FINISHED WALL MATERIAL.	
D. SEE SHEET Q104 FOR EQUIPMENT SCHEDULE.	

EQUIPMENT ABBREVIATIONS	
CC:	CONTRACTOR FURNISHED & INSTALLED
VV:	VA FURNISHED & INSTALLED
VC:	VA FURNISHED & CONTRACTOR INSTALLED

NO.

REVISIONS

DATE

CONSULTANT

ARCHITECT/ENGINEER OF RECORD

THOMAS OLESAC, ARCHITECT

MS Lic # 5505

1050 HOYT AVE WEST ST PAUL, MN 55117

952-451-0460

STAMP

REGISTERED ARCHITECT

Thomas Olesac

STATE OF MISSISSIPPI

03.10.2023

Office of Construction and Facilities Management

U.S. Department of Veterans Affairs

Drawing Title

ENLARGED FLOOR PLANS

Approved:

Phase

CONSTRUCTION DOCUMENTS

FULLY SPRINKLERED

Project Title

RENOVATE BUILDING 1

Location

BILOXI, MISSISSIPPI

Issue Date

03/10/2023

Checked

LA

Drawn

CD,PC

Project Number

520-317X

Drawing Number

1

Drawing Number

AE123

Dwg. 79 of 238

A

B

C

D

E

F

A












B

C

D

E

F

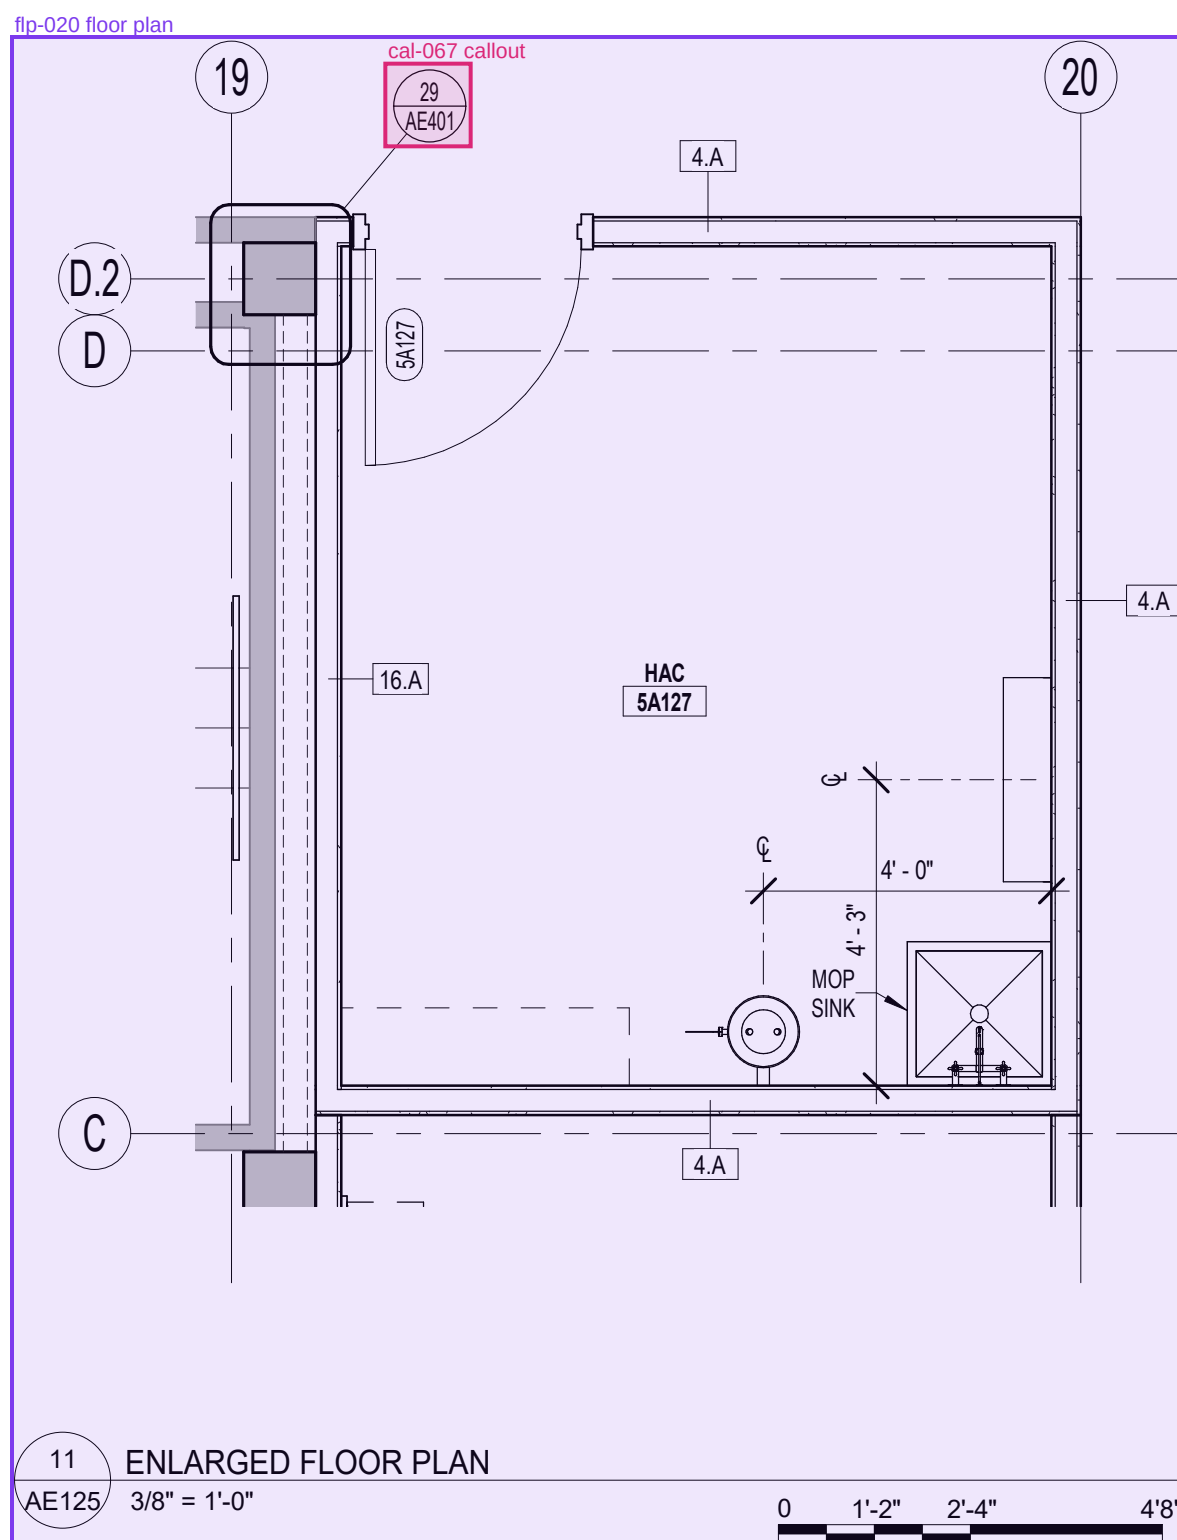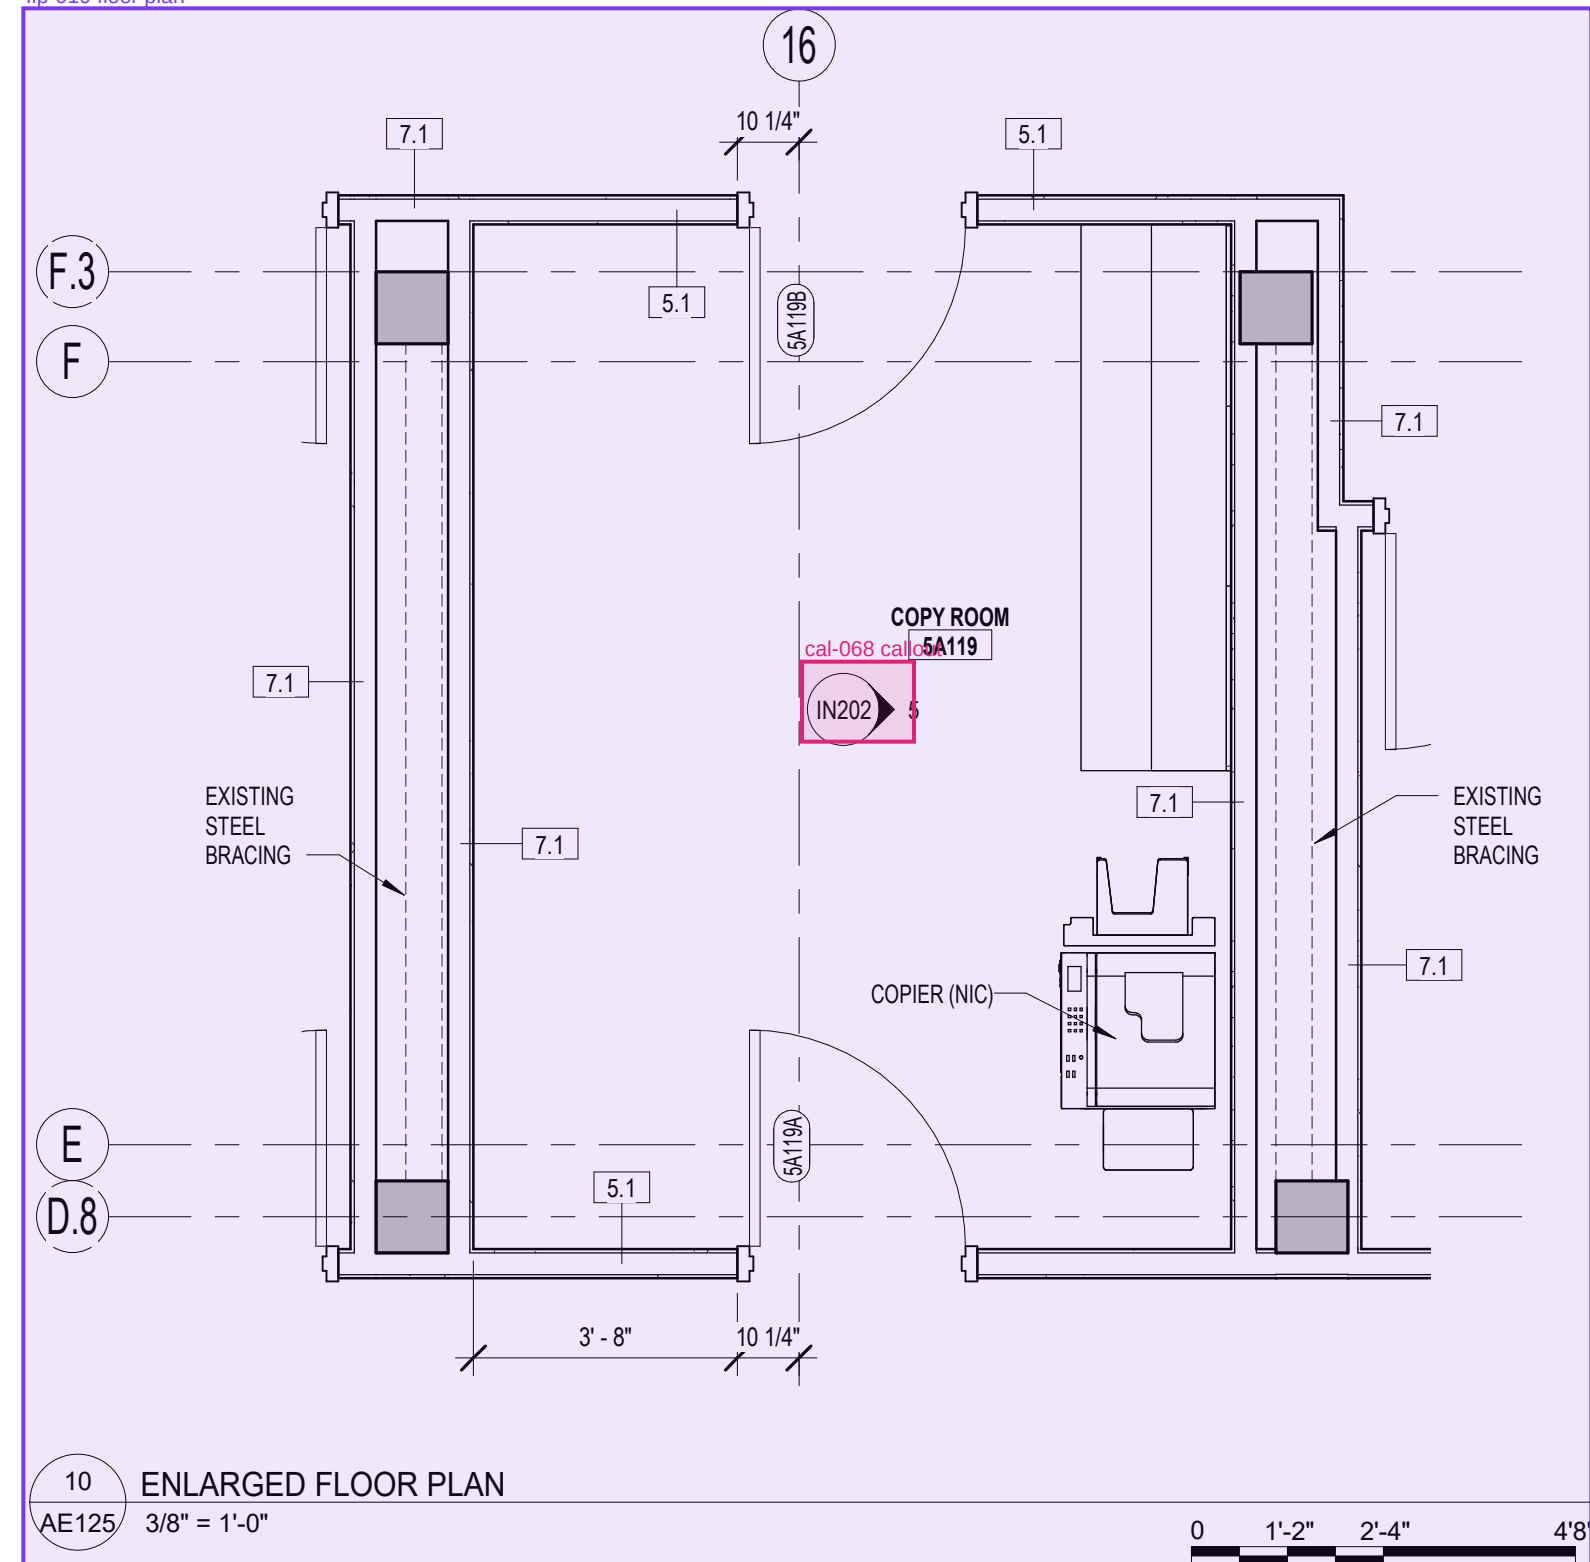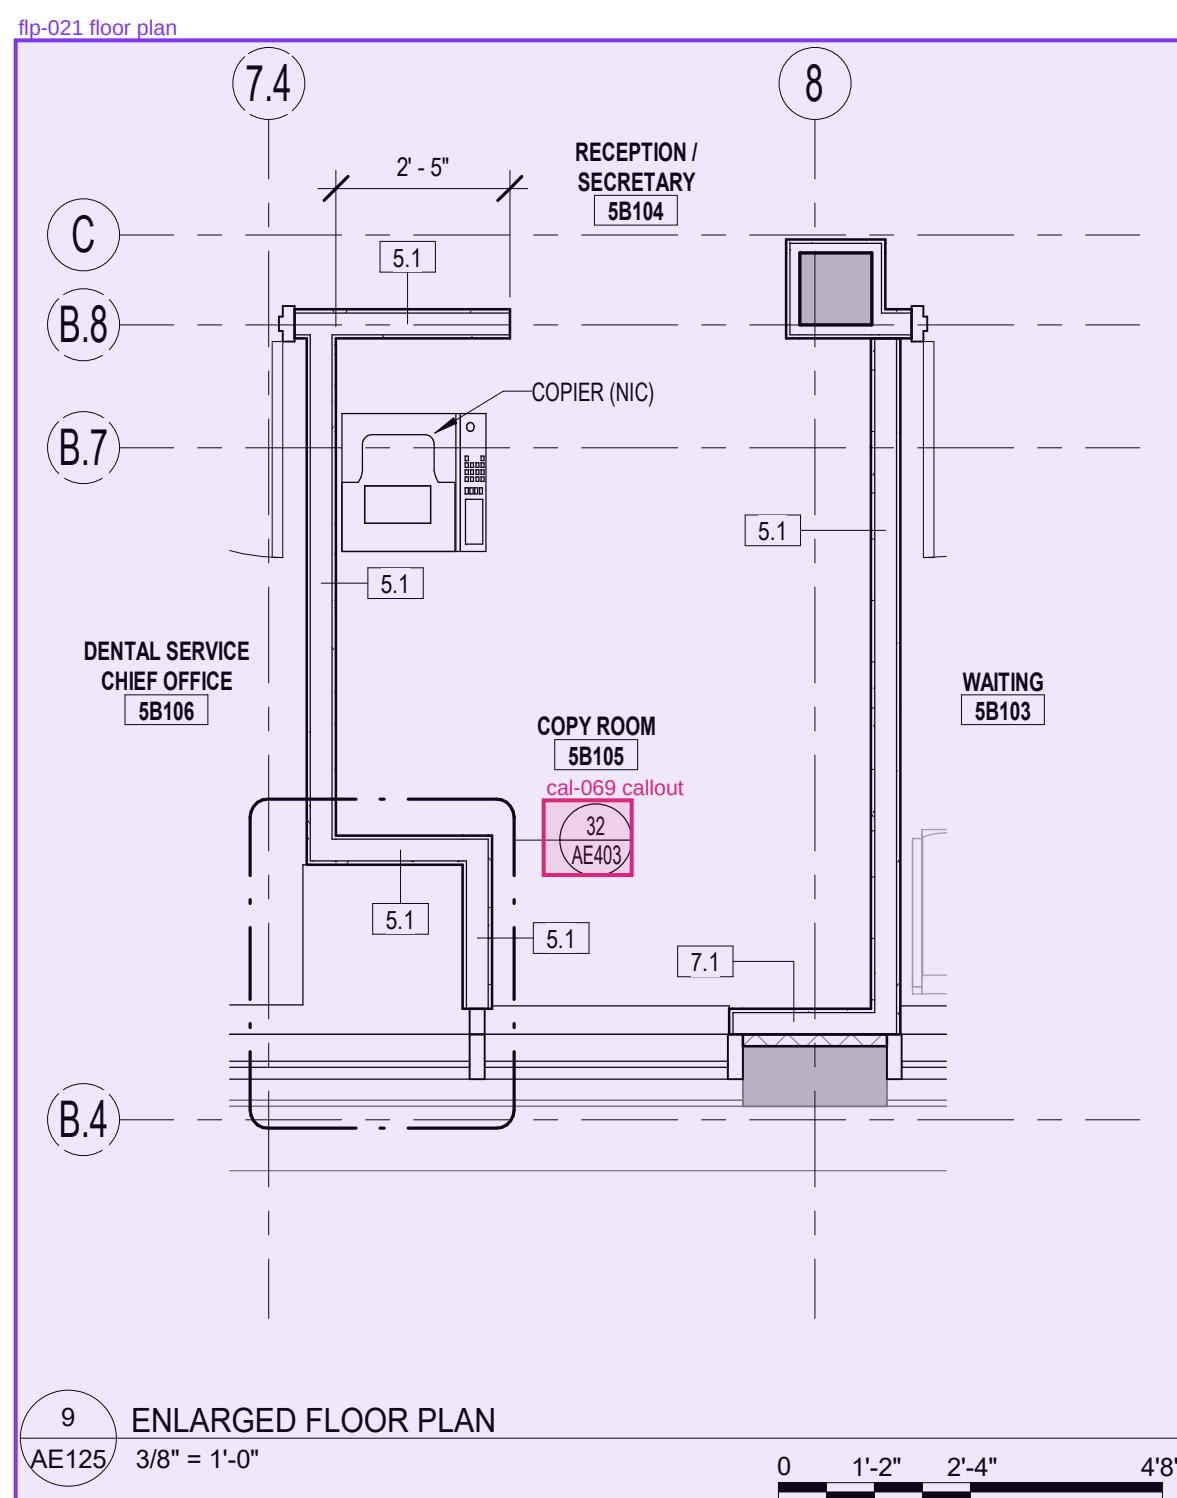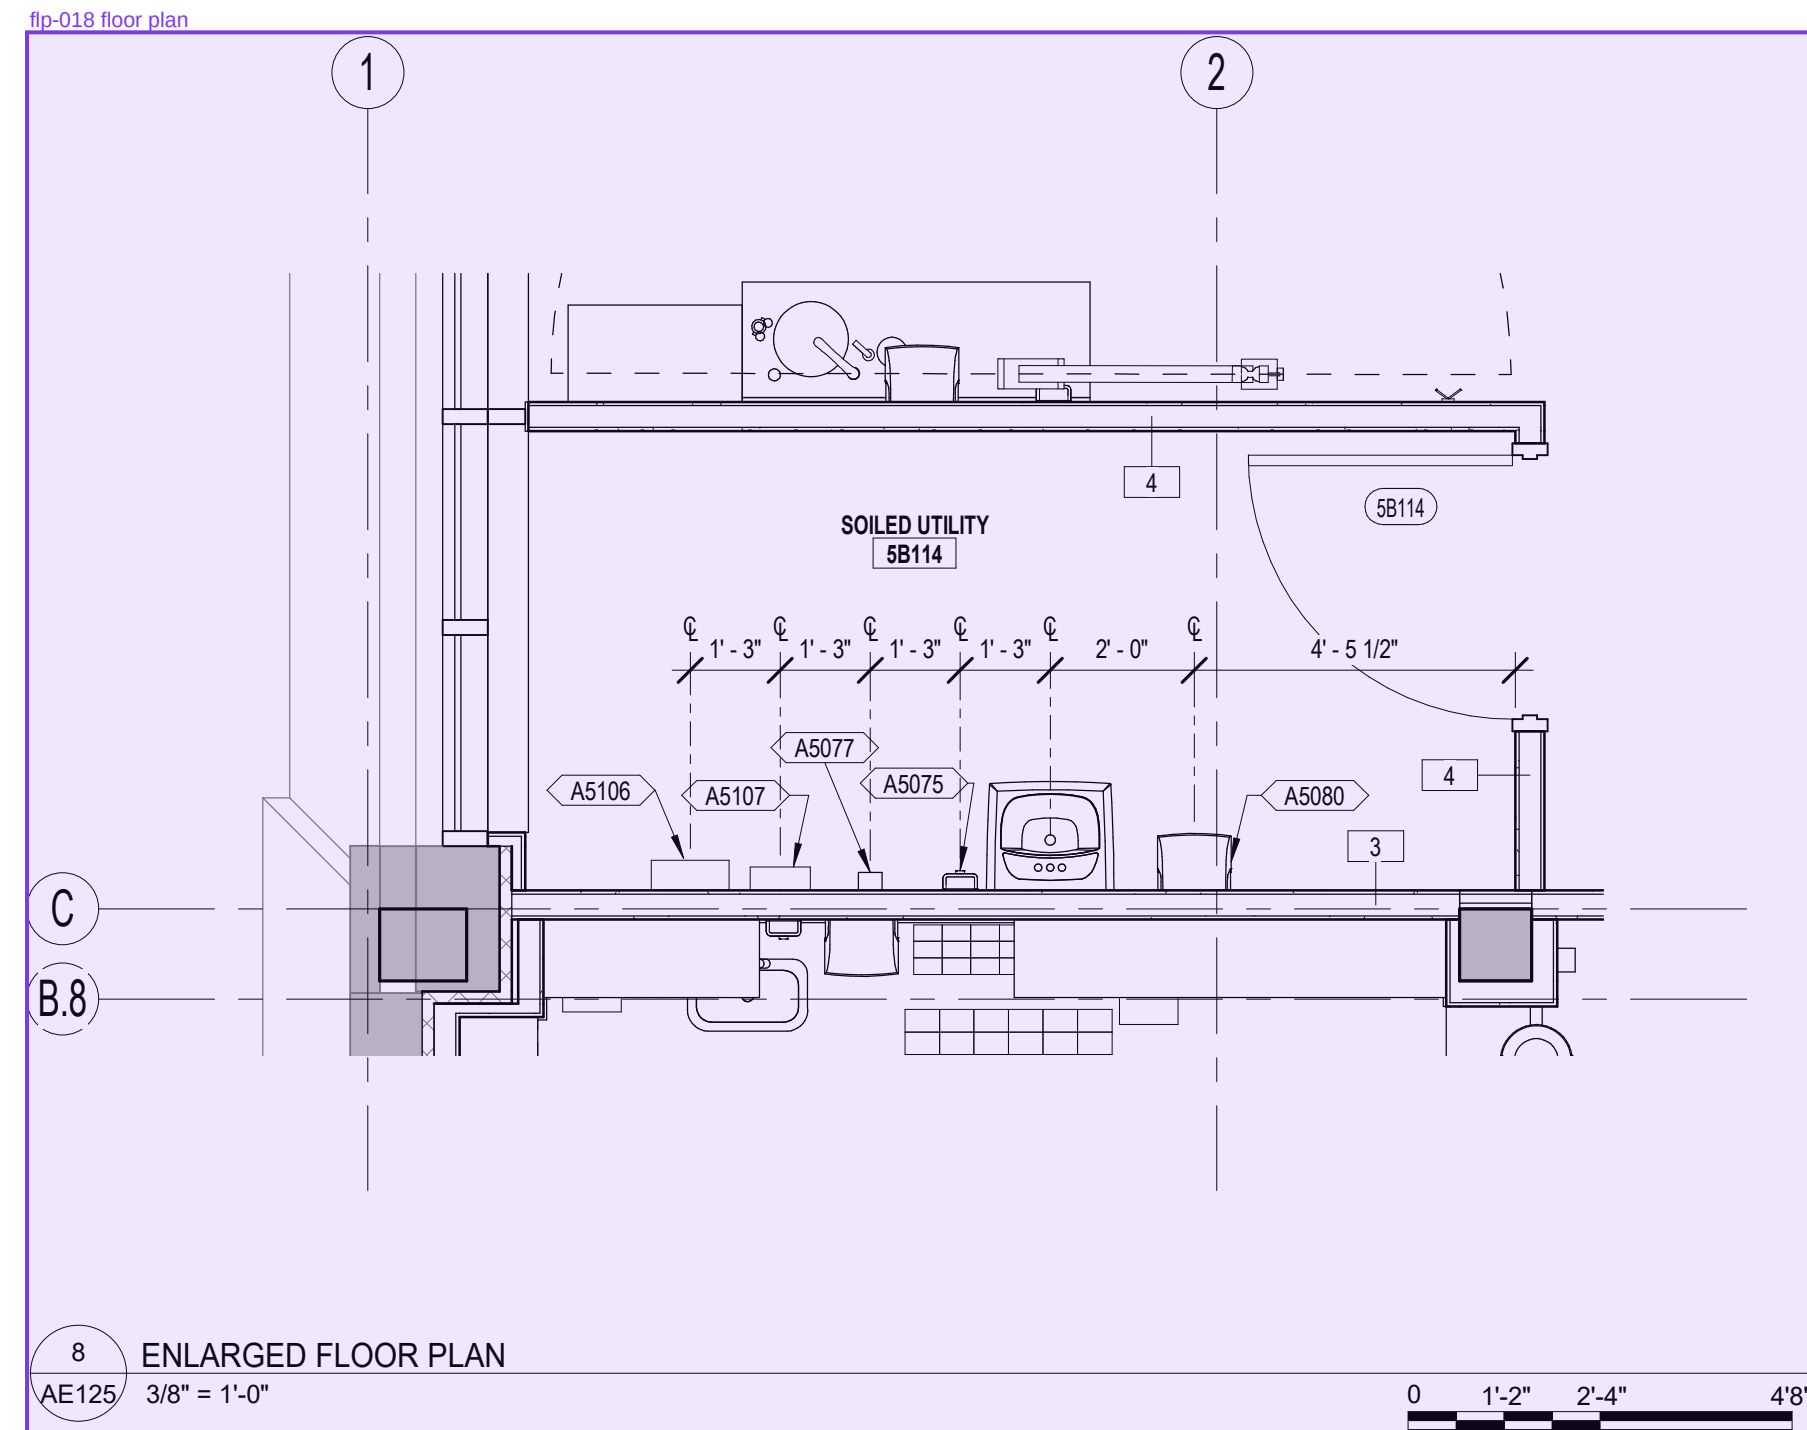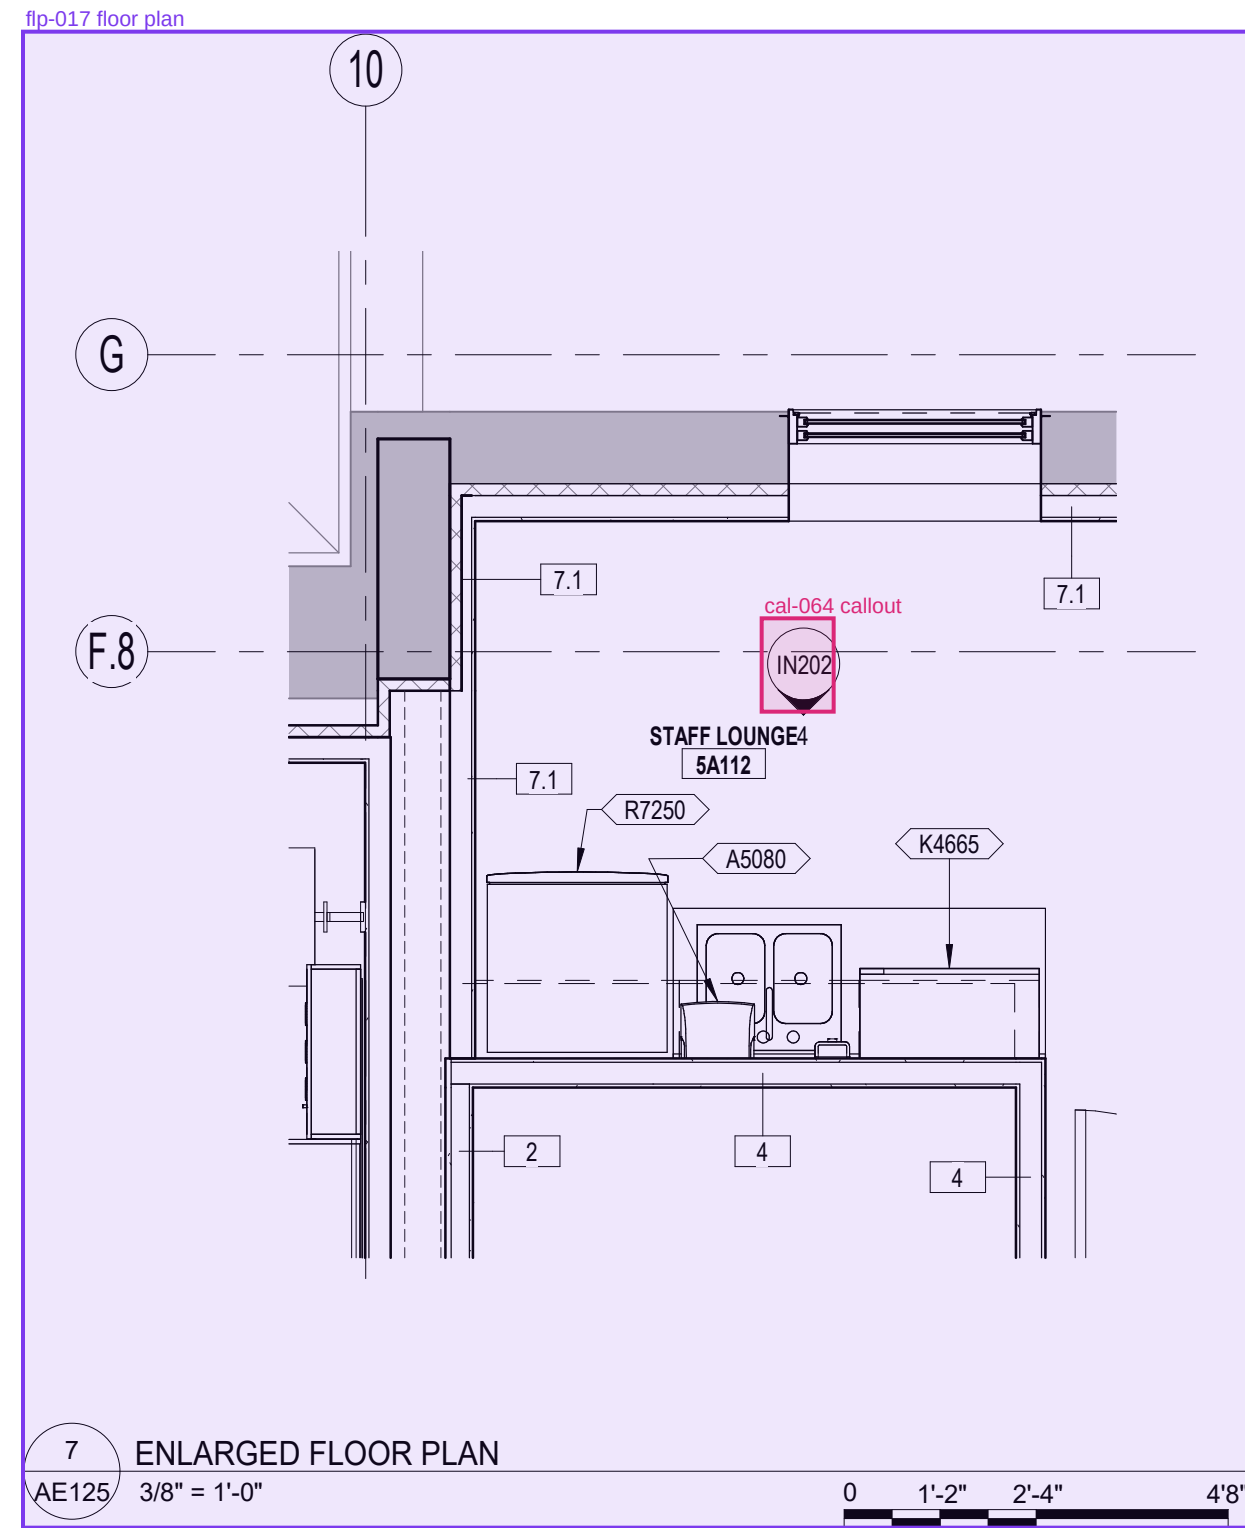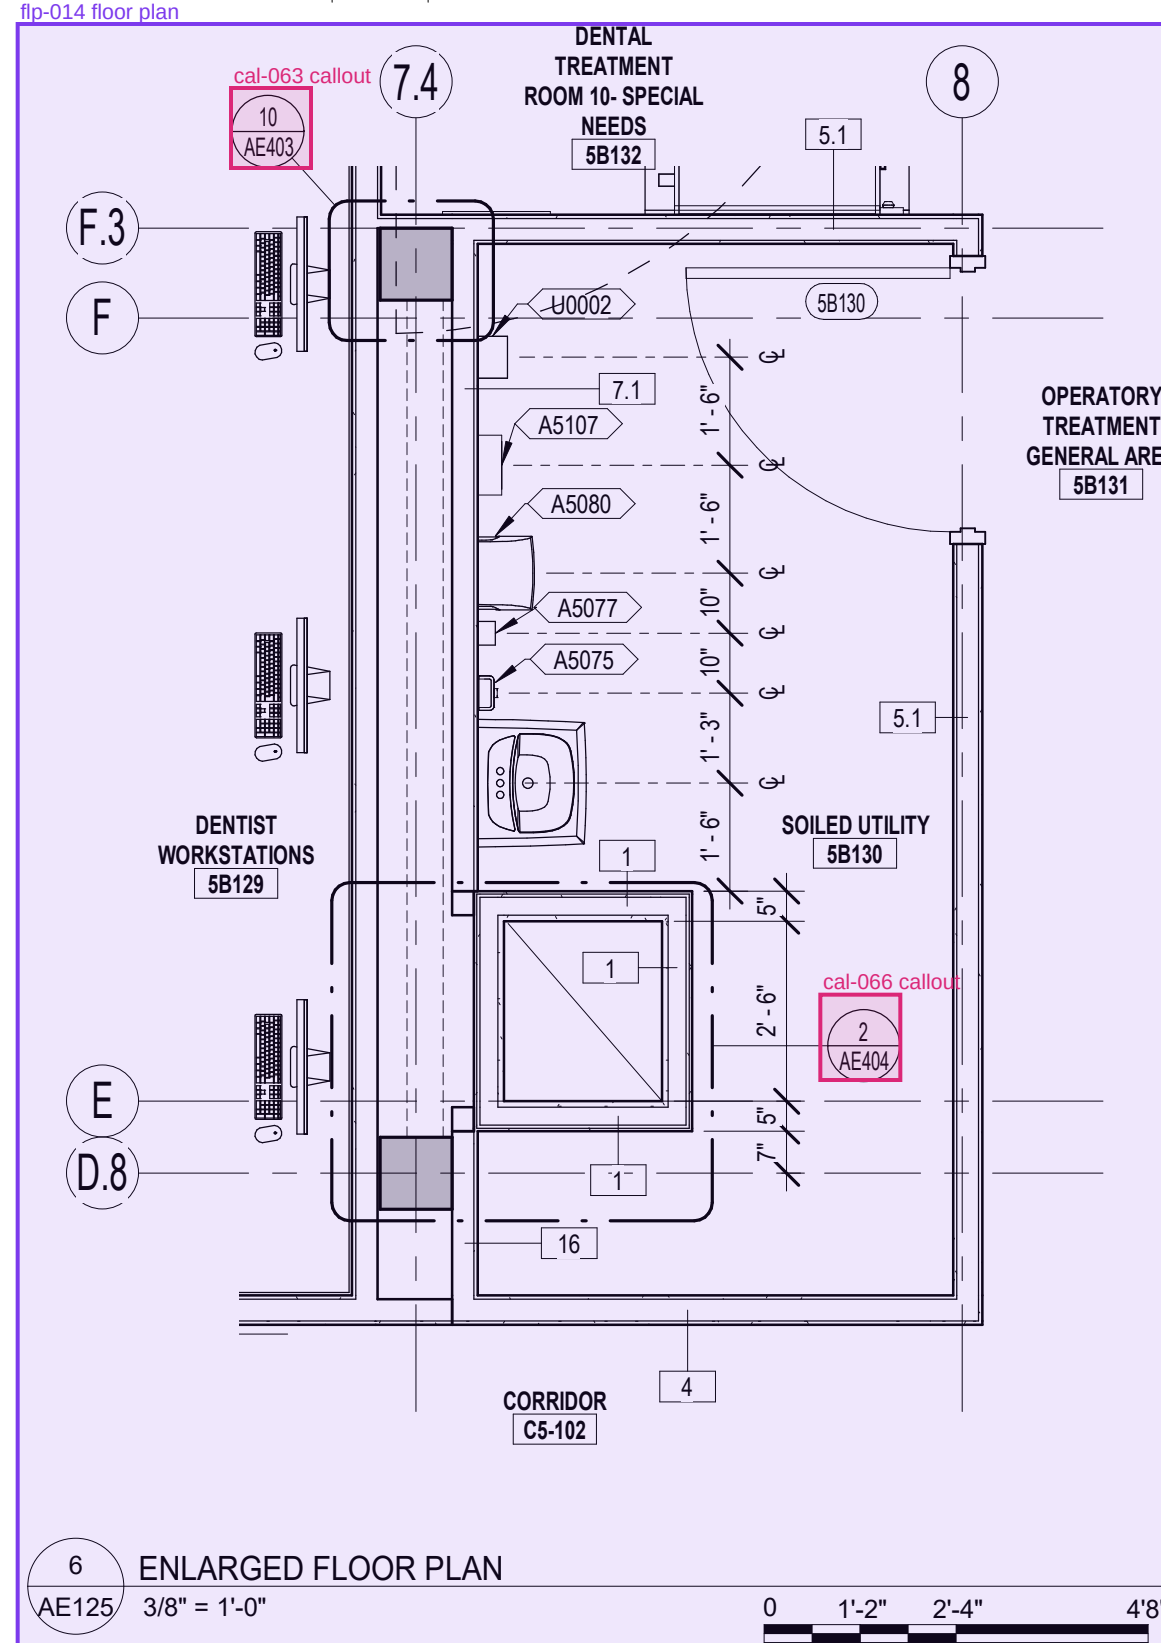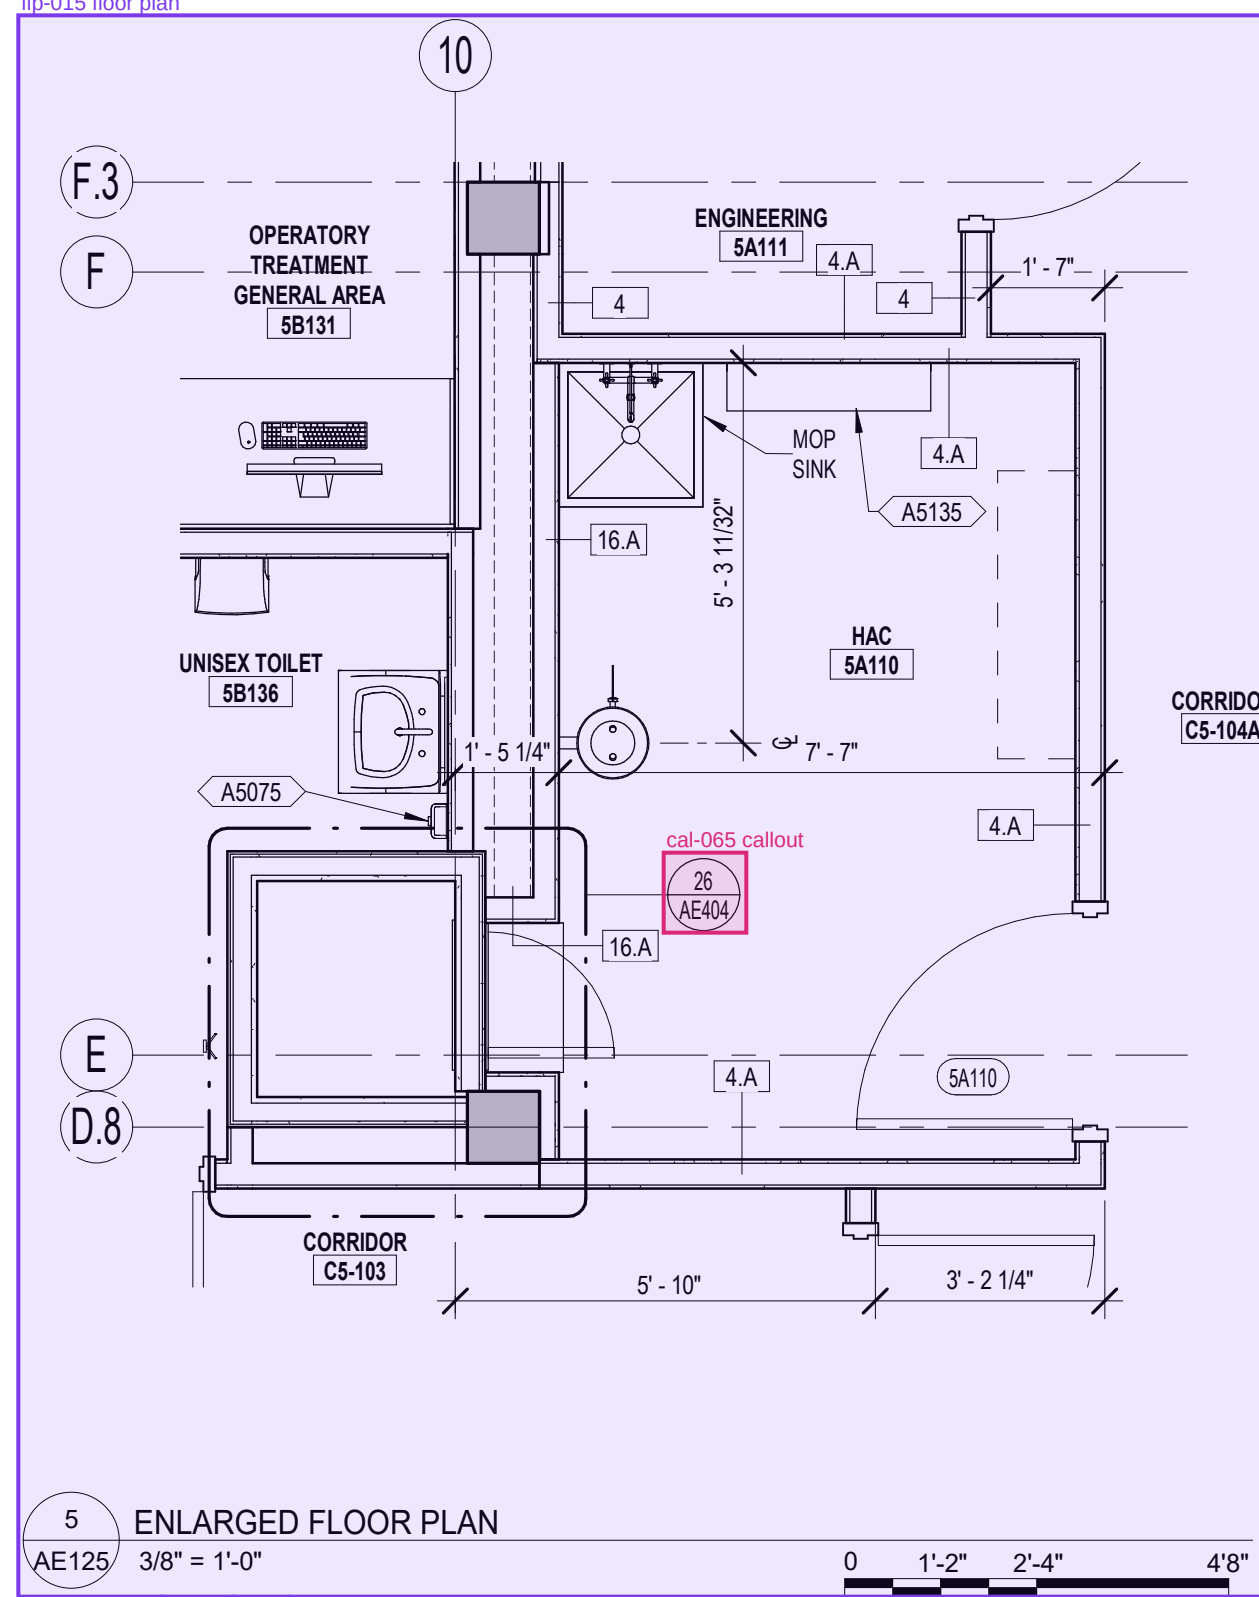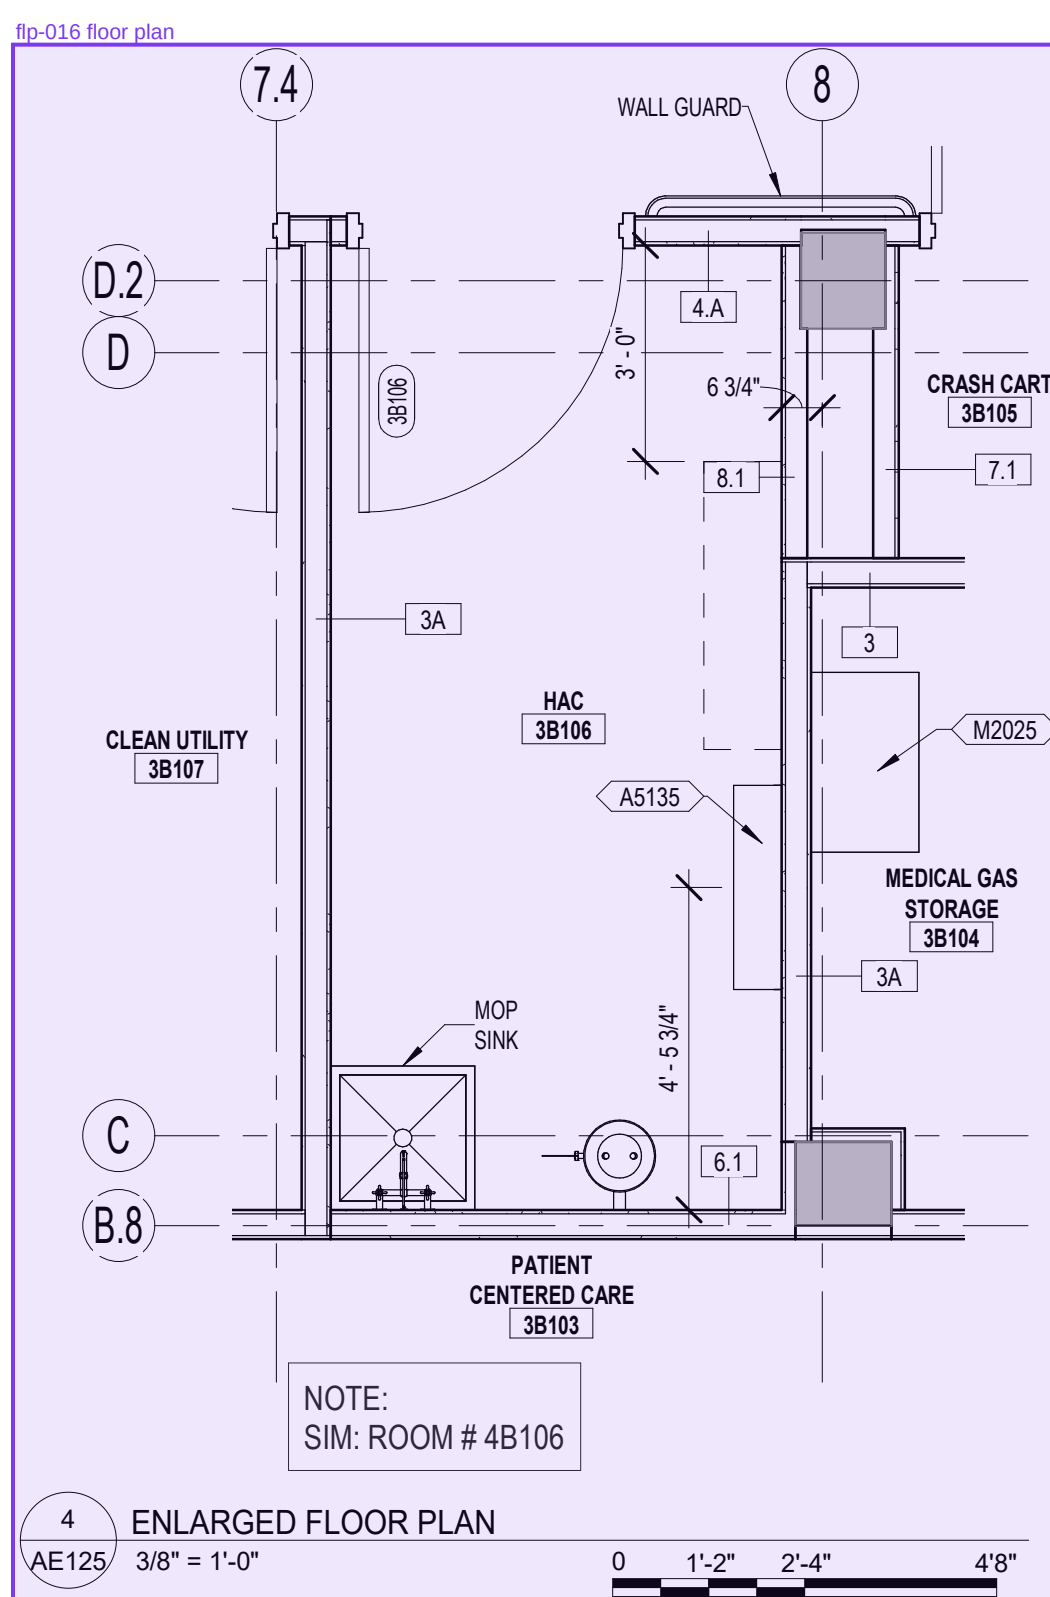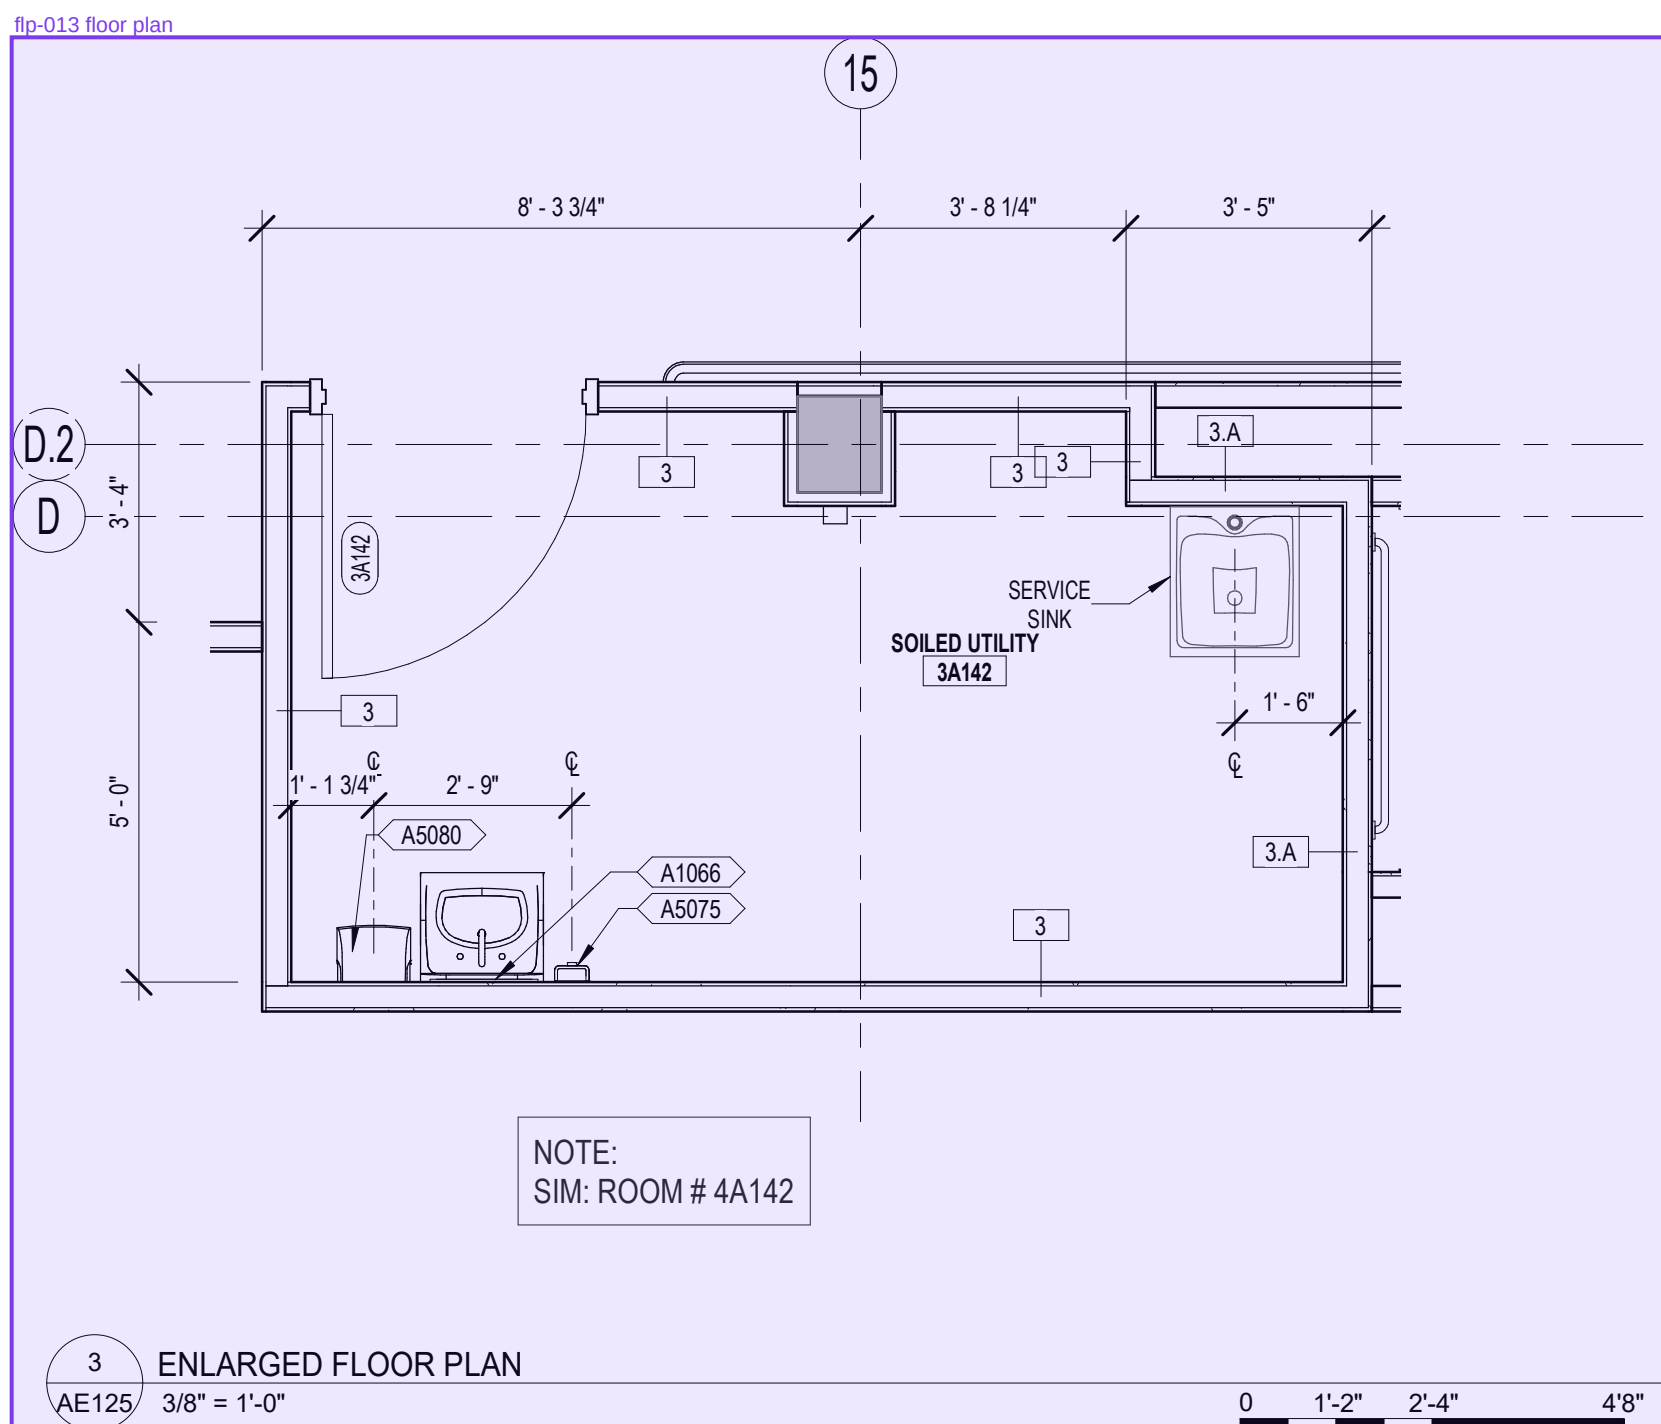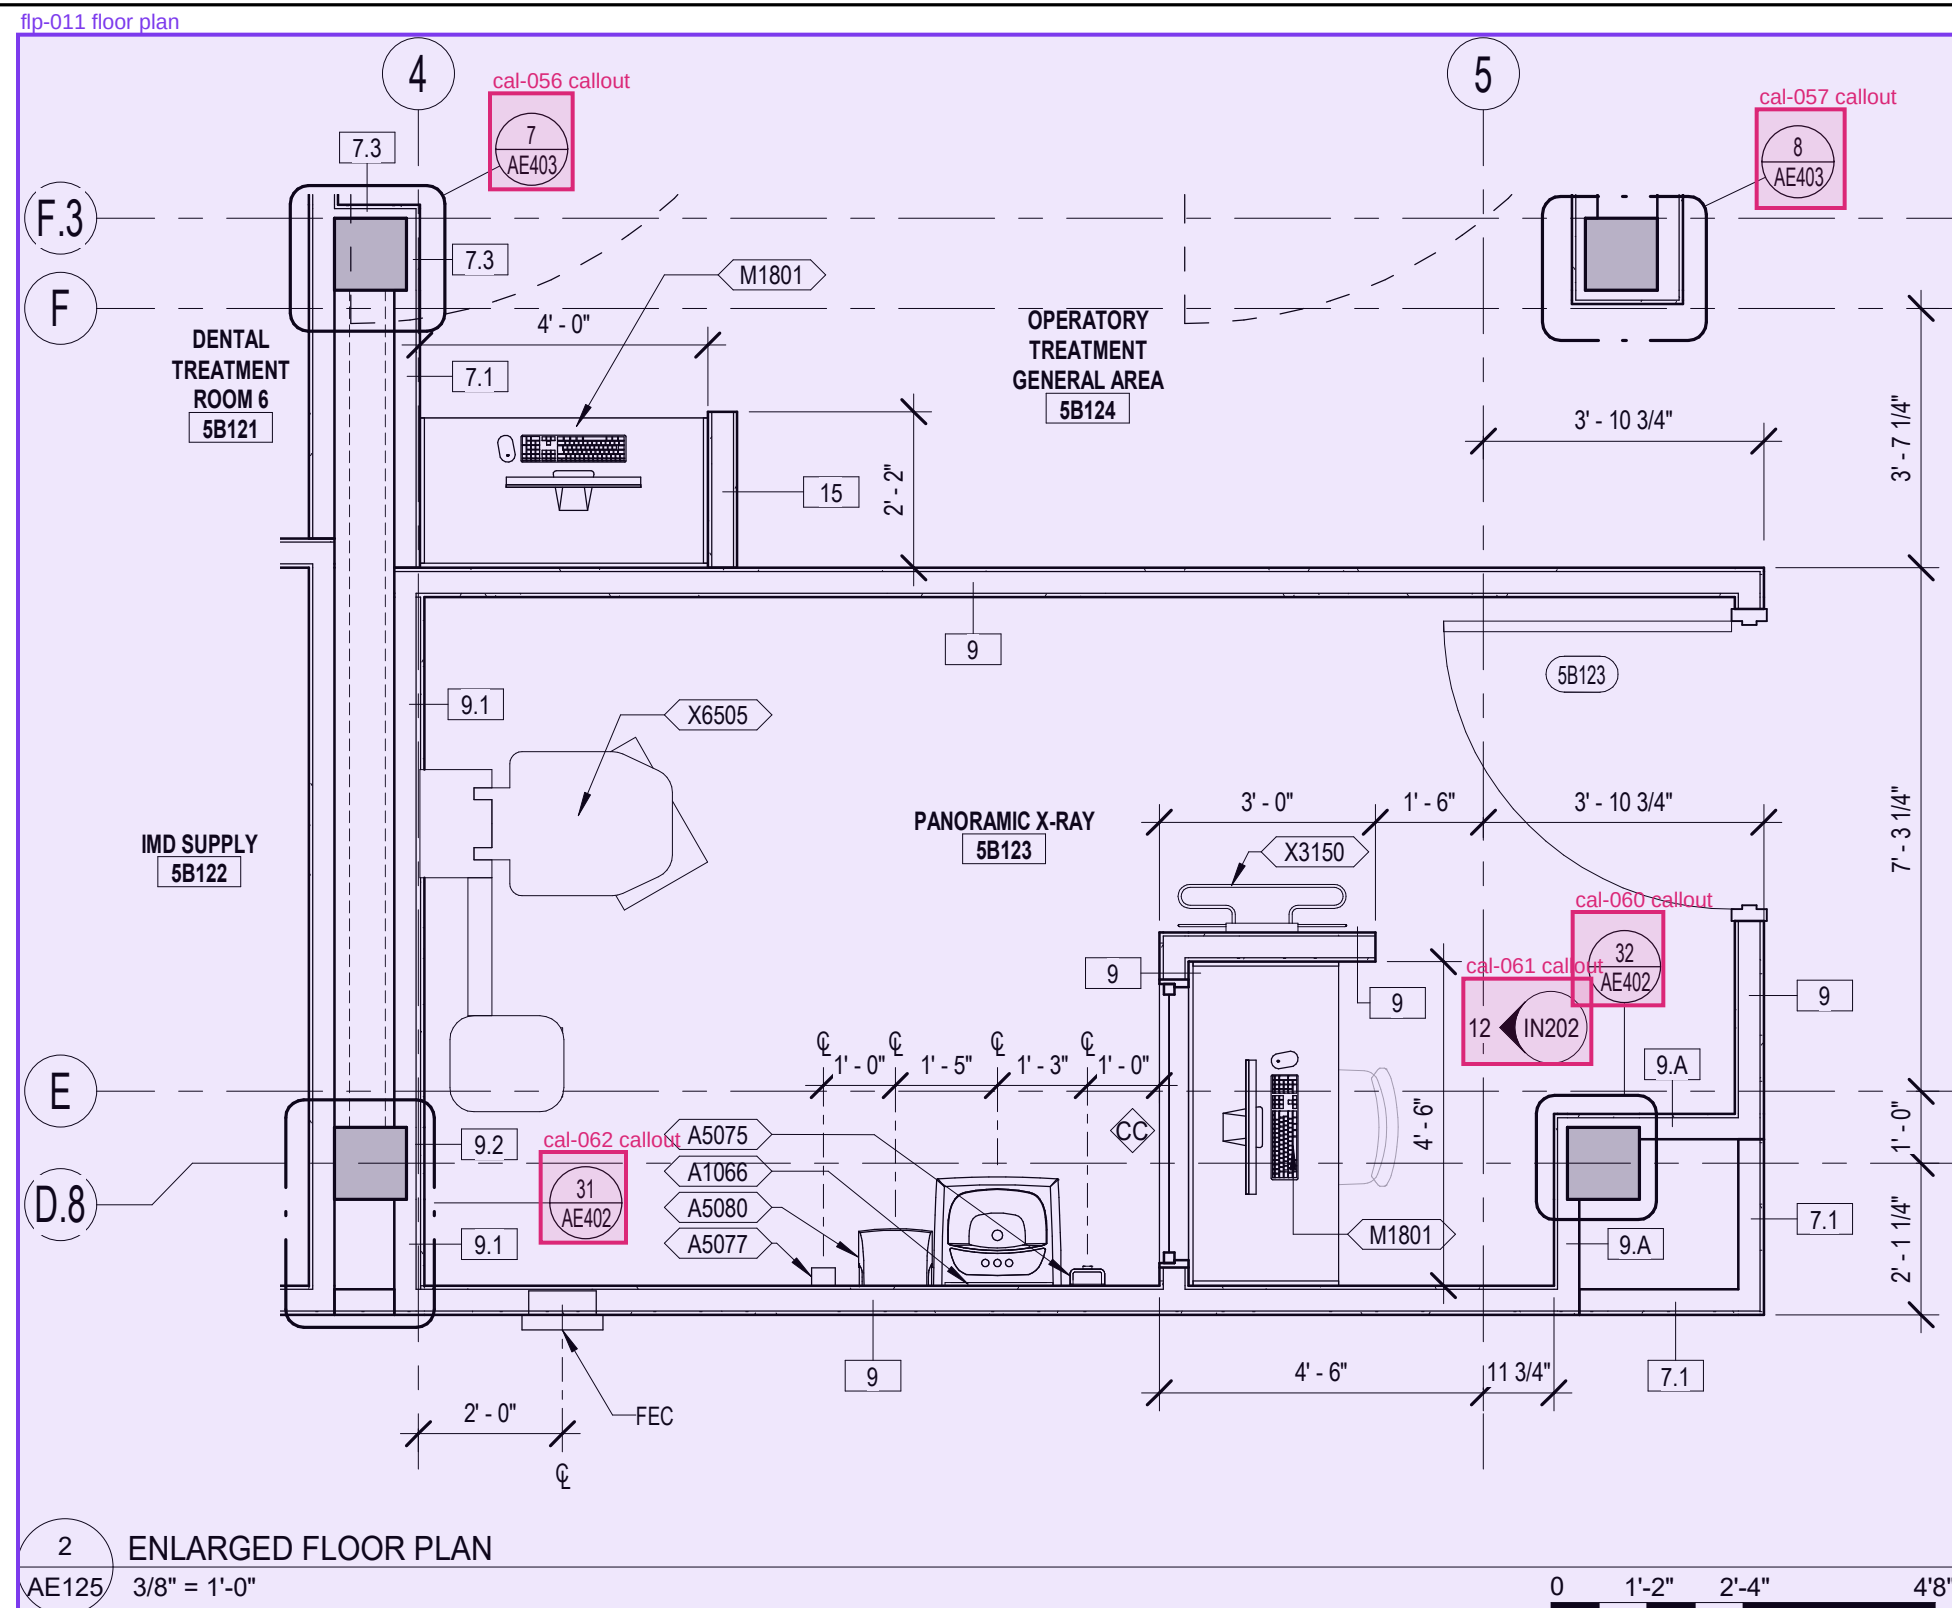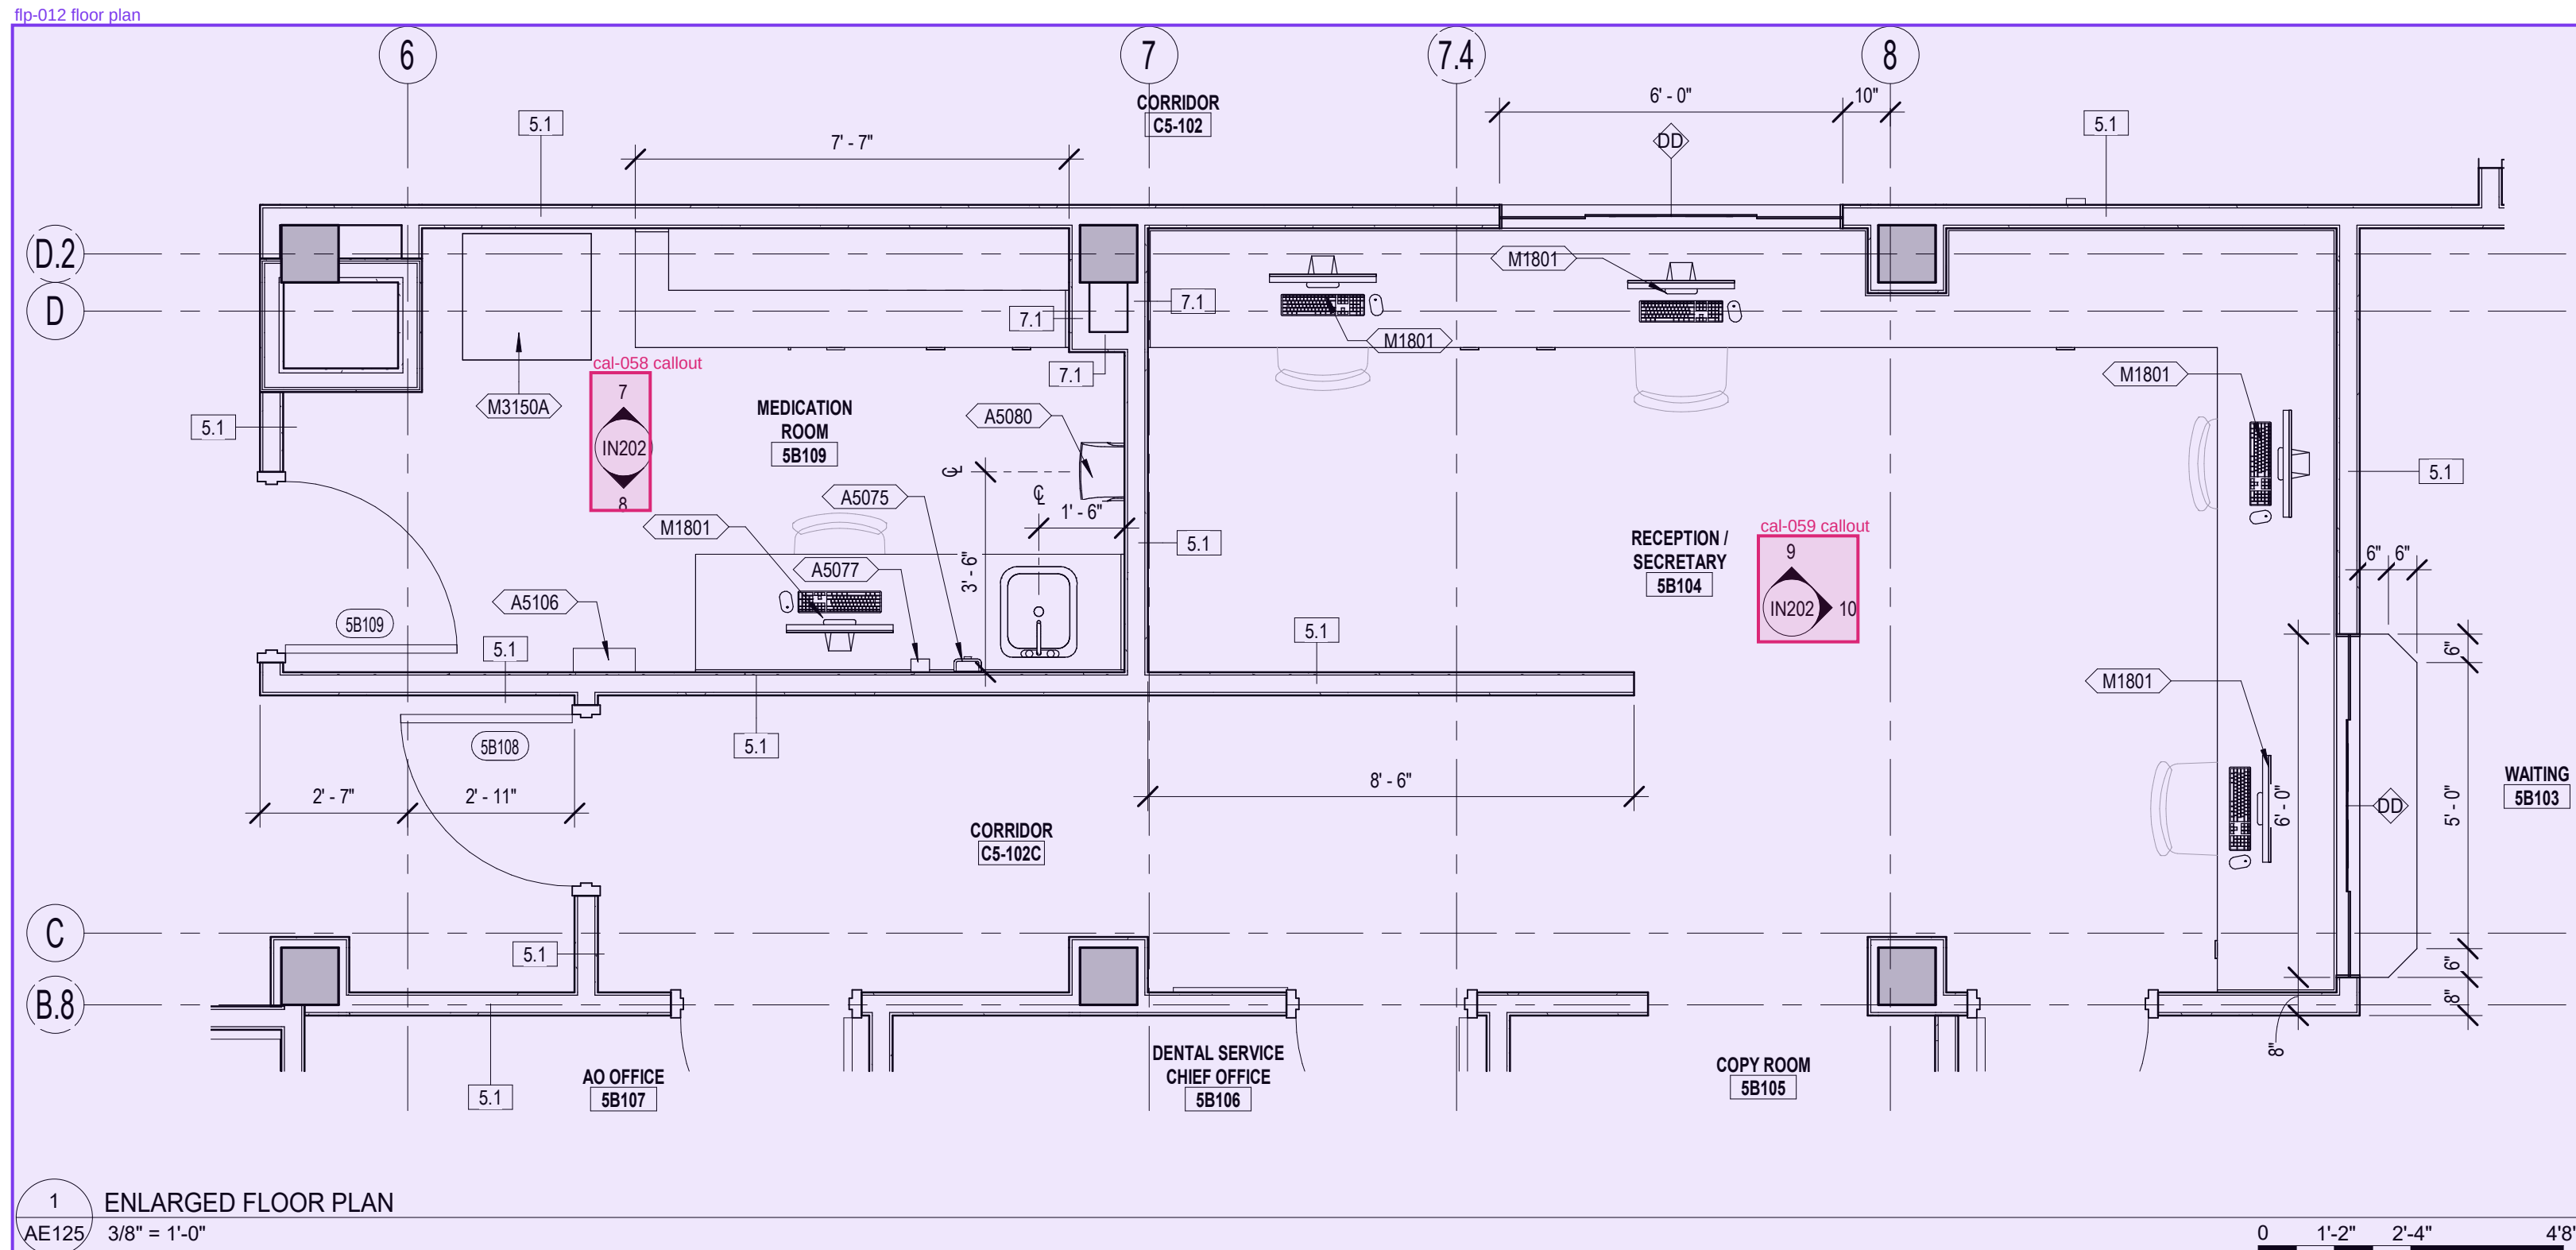

EQUIPMENT SCHEDULE - SHEET AE125		
JSN	DESCRIPTION	ACTIVATED BY
A1066	MIRROR, FLOAT GLASS, WITH SS FRAME, 18 X 36	CC
A5075	DISPENSER, HAND SOAP	VV
A5077	HAND SANITIZER DISPENSER	VV
A5080	DISPENSER, PAPER TOWEL	VV
A5106	WASTE DISPOSAL UNIT, SHARPS	VV
A5107	GLOVE DISPENSER RACK	VV
A5135	SHELF, UTILITY W/MPD/BROOM HOLDERS, SS, SURFACE MOUNTED	CC
K4665	OVEN, MICROWAVE	VV
M1801	COMPUTER AND MONITOR	VV
M2025	RACK, STORAGE CYLINDER, GAS	VV
M3150A	AUTOMATED STORAGE/DISPENSING UNIT(OMNICELL) - 1 CELL	VV
R6200	REFRIGERATOR, UNDERCOUNTER, 5 CU. FT	VV
R7250	REFRIGERATOR/FREEZER, 20 CU. FT.	VV
U0002	PDI WIPE DISPENSER	VV
X3150	RACK, APRON & GLOVE, WALL MOUNT	VV
X6505	RADIOGRAPHIC UNIT, DENTAL PANOGRAPHIC	VV

EQUIPMENT ABBREVIATIONS

CC:	CONTRACTOR FURNISHED & INSTALLED
VV:	VA FURNISHED & INSTALLED
VC:	VA FURNISHED & CONTRACTOR INSTALLED

RESTROOM ACCESSORY NOTES

- SEE SHEET G101 FOR SHOWER RECEPTOR TYPES.
- MOUNT WASTE RECEPTACLE TO MEET ABAS. MOUNT HIGHEST OPERABLE PART OF CONTROLS, DISPENSERS, RECEPTACLES AND OTHER OPERABLE EQUIPMENT BETWEEN 15'-48" ABOVE FINISH FLOOR.
- ATTACH MIRROR PER MANUFACTURER STANDARD; CENTER MIRROR ON LAVATORY(S) BELOW.
- ROBE HOOKS (A5145) TO BE MOUNTED ON TOILET SIDE OF DOOR, 48" FROM ABOVE FINISH FLOOR TO CENTER.
- FIELD VERIFY MOUNTING HEIGHTS WITH RESIDENT ENGINEER BEFORE INSTALLATION.
- PROVIDE & INSTALL PRE-JOINED (PLASTIC COVER) INSULATION FOR ALL EXPOSED PIPING, MEETING ALL APPLICABLE ABA REQUIREMENTS.

RESTROOM ACCESSORY GENERAL NOTES

- A. MOUNTING HEIGHTS REFERENCED ON SHEET G101. VERIFY ALL MOUNTING HEIGHTS WITH CODES AND MANUFACTURER RECOMMENDATIONS.
- B. ABA TOILET PARTITION DOOR MUST BE 34" MINIMUM CLEAR OPENING.
- C. WHERE DIMENSIONS ARE INDICATED ON PLAN AS "CLEAR", THE DIMENSIONS ARE TAKEN FROM FACE OF FINISHED WALL MATERIAL TO FACE OF FINISHED WALL MATERIAL.
- D. SEE SHEET QH104 FOR EQUIPMENT SCHEDULE.

BID DOCUMENTS

NO.	REVISIONS	DATE

CONSULTANT

ARCHITECT/ENGINEER OF RECORD

THOMAS OLESAC, ARCHITECT
MS Lic # 5505

1050 HOYT AVE WEST ST PAUL, MN 55117
952-451-0460

STAMP



Office of
Construction
and Facilities
Management



U.S. Department
of Veterans
Affairs

Drawing Title
ENLARGED FLOOR PLANS

Approved:

Phase
CONSTRUCTION
DOCUMENTS

FULLY SPRINKLERED

Project Title
RENOVATE BUILDING 1

Location
BILOXI, MISSISSIPPI

Issue Date
03/10/2023

Checked
LA


Drawn
CD,PC

Project Number
520-317X

Building Number
1

Drawing Number
AE125

Dwg. 81 of 238

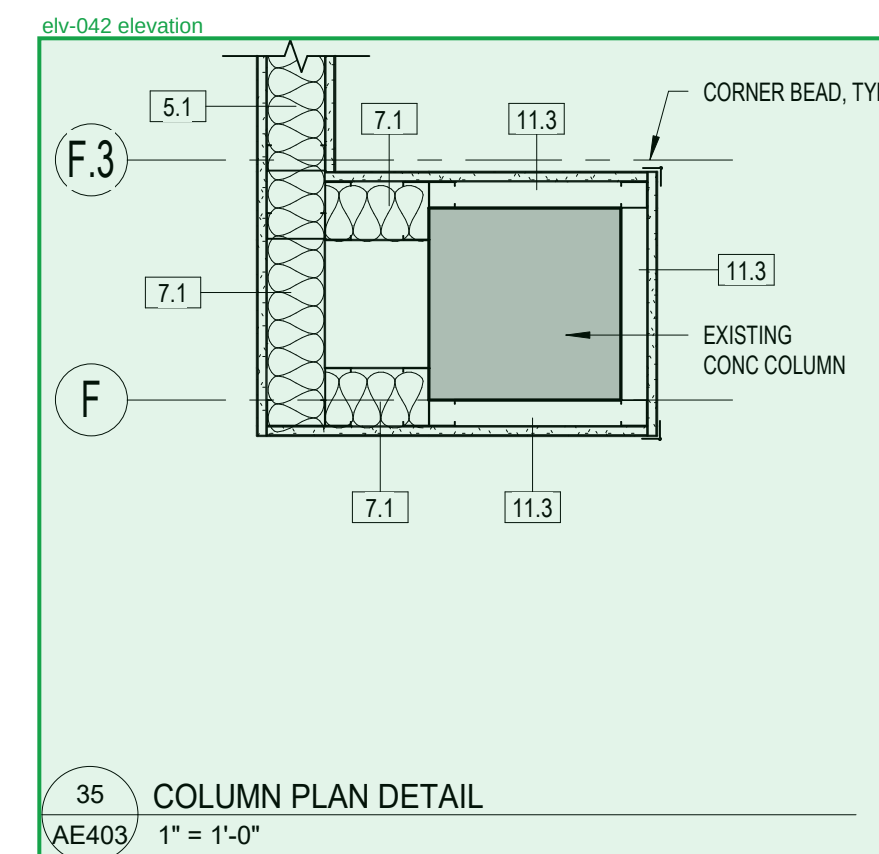

Dwg. 94 of 238

- 1. DASHED LINE INDICATES NEW WALL BELOW, REFER TO ARCHITECTURAL DRAWINGS FOR MORE INFORMATION. REFER TO SHEET SF105 FOR WALL FRAMING INFORMATION, INCLUDING ADDITIONAL FRAMING AND CONNECTION REQUIREMENTS FOR WALLS SUPPORTING EQUIPMENT OR CABINETS.
- 2. REFER TO ARCH FOR LOCATIONS OF ALL NEW SUSPENDED CEILINGS AND SOFFITS/SOFTT WALLS. APPROXIMATE LOCATIONS OF SUSPENDED SOFFIT WALLS ARE SHOWN ON PLANS, REFER TO DETAIL E6/S502 FOR TYPICAL SUSPENDED SOFFIT WALL FRAMING. DO NOT TIE TOP HUNG SOFFITS INTO INTERIOR WALLS, PROVIDE SLIP JOINT AND JOINTS IN FINISH MATERIALS TO ALLOW DIFFERENTIAL VERTICAL MOVEMENT BETWEEN INTERSTITIAL FRAMING SUPPORTED SOFFITS/CEILING AND SLAB SUPPORTED INTERIOR WALLS.
- 3. REFER TO SPECIFICATIONS FOR INSTALLATION REQUIREMENTS PER APPLICABLE ASTM STANDARDS FOR ALL SUSPENDED CEILING SYSTEMS. REFER TO ARCHITECTURAL DRAWINGS FOR LOCATIONS/EXTENTS AND TYPES OF ALL SUSPENDED CEILINGS.
- 4. PATIENT LIFT SYSTEM SUSPENDED BELOW, REFER TO ARCHITECTURAL DRAWINGS FOR EXACT CONFIGURATION. REFER TO DETAIL E7/S501 AND F6/S502 FOR TYPICAL SUPPORT DETAIL TO EXISTING STRUCTURE.
- 5. BOOM ARM EQUIPMENT MOUNT SYSTEM SUSPENDED BELOW, REFER TO ARCHITECTURAL DRAWINGS FOR EXACT CONFIGURATION. REFER TO DETAIL F1/S501 FOR TYPICAL SUPPORT DETAIL TO EXISTING STRUCTURE. REFER TO SUPPLIER FOR MOUNTING PLATE HEIGHT.
- 6. EXISTING CHASE OPENING IN STRUCTURE, ALL OPENINGS EXISTING UNLESS NOTED OTHERWISE, TYPICAL.
- 7. PROVIDE STEEL FRAME SUPPORT REPAIR TO EXISTING JOIST PREVIOUSLY CUT WITHOUT PROPER STRUCTURAL BRACING. REFER TO F4/S502.
- 8. ENLARGE EXISTING MEP OPENING TO ACCOMMODATE NEW DUCT SIZE, REFER TO MECHANICAL FOR MORE INFORMATION, REFER TO F4/S502 FOR FRAMING SUPPORT TO BE INSTALLED PRIOR TO CUTTING JOIST.
- 9. NEW MEP OPENING TO ACCOMMODATE EXHAUST FAN AT LOW ROOF, REFER TO MECHANICAL FOR MORE INFORMATION, REFER TO F4/S502 FOR FRAMING SUPPORT TO BE INSTALLED PRIOR TO CUTTING JOIST.
- 10. NEW OPENING IN STRUCTURE. REFER TO KEYNOTES FOR WORK REQUIRED PRIOR TO CUTTING NEW OPENING.
- 11. NEW STAIR FRAMING SUPPORT POSTS ABOVE LOW ROOF, REFER TO SHEET SF107 FOR MORE INFORMATION.

GENERAL NOTES

- A. FIRST FLOOR TOP OF STRUCTURE ELEVATION = 922'-4". ALL ELEVATIONS ARE BASED ON THIS DATUM UNLESS NOTED OTHERWISE, AS INDICATED ON AS-BUILT DRAWINGS OF ORIGINAL STRUCTURE.
- B. REFER TO SHEET S001 AND S002 FOR GENERAL NOTES.
- C. REFER TO PLUMBING DRAWINGS FOR LOCATION OF FLOOR DRAINS AND SLOPED SLABS, ADJUST SLOPE TO DRAIN LOCATION TO ENSURE DRAIN PENETRATION DOES NOT CLASH WITH EXISTING PAN JOISTS. GPP SCANNING IS REQUIRED TO ENSURE NO DAMAGE OCCURS TO EXISTING STRUCTURE, DOES NOT GRIND FLOOR SLAB OR OTHERWISE DISTURB FOR INSTALLATION OF SLOPED SLABS. ALL SLOPED SLABS REQUIRE FLOOR OVERLAY TO ACHIEVE SLOPE.
- D. VERIFY ALL WALL OPENING AND INTERIOR WALL DIMENSIONS AND LOCATIONS WITH ARCHITECTURAL DRAWINGS. VERIFY EXACT LOCATIONS AND DIMENSIONS WITH ARCHITECTURAL DRAWINGS WHERE NOT SPECIFICALLY NOTED ON THIS SHEET.
- E. VERIFY ALL DIMENSIONS IN THE FIELD PRIOR TO FABRICATION OF STRUCTURAL ITEMS. EXISTING PORTION OF PLANS ARE FROM LIMITED FIELD OBSERVATIONS AND AS-BUILT STRUCTURAL DRAWING REVIEW, WHICH MAY OR MAY NOT REFLECT THE EXACT AS-BUILT CONDITIONS. THE CONTRACTOR SHALL BE RESPONSIBLE FOR COORDINATING FIELD SURVEY WORK ON THE PLANS AND WHAT EXISTS IN THE FIELD, CONTACT THE COR TO DETERMINE WHAT SHOULD BE DONE TO MATCH EXISTING CONDITIONS AS REQUIRED. BEGINNINGS OF CONSTRUCTION MEANS ACCEPTANCE OF EXISTING CONDITIONS. REFER TO GENERAL NOTES.
- F. REFER TO E6/S501 FOR HOUSEKEEPING OR EQUIPMENT MOUNTING PADS. REFER TO ARCH AND MEP DRAWINGS FOR SLOPED AND LOCATION ON PADS.
- G. REFER TO SHEET S803 FOR TYPICAL LIGHT CASE FRAMING DETAILS. REFER TO ARCHITECTURAL AND MEP DRAWINGS FOR ADDITIONAL COORDINATION OF EQUIPMENT AND CABINETS SHOWN TO BE MOUNTED TO WALLS NOT SPECIFICALLY SHOWN ON THIS PLAN. THE CONTRACTOR SHALL BE RESPONSIBLE FOR COORDINATING WALL FRAMING PER DETAILS ON SHEET S503 FOR FRAMING OF WALLS AT LOCATIONS WHERE ADDITIONAL EQUIPMENT AND CABINETS S' LBS AND GREATER ARE TO BE MOUNTED UNDER THIS CONTRACT. ARCHITECTURAL LAYOUT SUPERCEDES ITEMS LOCATED ON THIS PLAN.
- H. ONLY THOSE PORTIONS OF THE EXISTING STRUCTURE ARE SHOWN WHERE PERTINENT TO THE LOCATIONS OF SUPPORT FRAMING MODIFICATION OR ADDITION. DRAWINGS SHALL BE USED FOR LAYOUT RELATIVE TO THE EXISTING STRUCTURE. HOWEVER FIELD VERIFICATION OF FRAMING LOCATIONS IS REQUIRED BEFORE INSTALLATION OF ANY NEW FRAMING.
- I. CONTRACTOR SHALL PROVIDE GROUND PENETRATING RADAR OR OTHER MEANS OF SLAB REINFORCING LOCATION AND MARK SUCH LOCATIONS SO THAT NO EXISTING REINFORCING IS DAMAGED DURING INSTALLATION OF ANY NEW FASTENERS (POWER ACTUATED FASTENERS, SCREWS, BOLTS OR OTHER CONNECTORS), FLOOR SINKS DRAINS OR OTHER MEP SLAB REPAIRS TO TOP OF EXISTING REINFORCED FLOOR SLAB. ANY DAMAGED REINFORCING WILL REQUIRE STRUCTURAL REPAIRS AT THE CONTRACTORS EXPENSE.

1st floor plan showing structural elements, MEP equipment, and annotations.

EXISTING PAN JOIST STRUCTURAL SYSTEM:
10" DEEP CONCRETE JOISTS x 5" WIDE WITH
20" TYPICAL PAN WIDTH. EXISTING SLAB IS 2
1/2" THICK REINFORCED CONCRETE.

**EXISTING T.O. STRUCTURE
ELEVATION = 983'-8"**

SUSPENDED LIFT/EQUIPMENT/MEP NOTE:
REFER TO F6/S502 FOR ANCHORAGE AND
INSTALLATION DETAILS FOR ALL SUSPENDED
EQUIPMENT INSTALLATIONS.

CONTRACTOR DEMO NOTE:
REFER TO ARCHITECTURAL AND MEP
DRAWINGS FOR ALL LOCATIONS AND SIZES
OF PENETRATIONS THROUGH THE FLOOR
SLAB. NOT ALL PENETRATIONS ARE SHOWN
ON THESE DRAWINGS. SHIFT LOCATIONS TO
AVOID EXISTING FLOOR STRUCTURE, DRILL
THROUGH FLOOR SLAB ONLY. REFER TO
GENERAL NOTE I.

Annotations include:
- F4 S502 (SUSPENDED LIFT/EQUIPMENT/MEP)
- F4 S502 (SUSPENDED LIFT/EQUIPMENT/MEP)
- C4 S501 (SUSPENDED LIFT/EQUIPMENT/MEP)
- HSS 4x4x1/4 COL.
- 3'-0"

Grid lines: 10, 9, 8, 7, 6, 5, 4, 3, 2, 1 (horizontal); A, B, C, D, E, F (vertical).

Dimensions: 22'-1 1/2", 21'-4", 15'-7 1/2", 20'-6 1/2", 20'-0", 20'-0", 20'-0", 18'-6 1/2", 20'-7", 21'-5", 20'-0", 20'-6 1/2".

F1 **ROOF FRAMING FRAMING PLAN**
3/16" = 1'-0"

FULLY SPRINKLED

--	--	

